■ 청주시 건축 조례

제35조(일조 등의 확보를 위한 건축물의 높이제한)

① 영 제86조제1항에 따라 전용주거지역이나 일반주거지역에서 일조 등의 확보를 위하여 건축물의 각 부분을 정북방향의 인접대지경계선으로부터 띄어야 하는 거리는 다음 각 호와 같다.

1. 높이 9미터 이하인 부분: 인접대지경계선으로부터 1.5미터 이상
2. 높이 9미터를 초과하는 부분: 인접대지경계선으로부터 해당 건축물 각 부분 높이의 2분의 1이상

② 영 제86조제3항 각 호 외의 부분 단서에서 "건축조례로 정하는 거리"란 1.5미터로 한다.

③ 영 제86조제3항제2호가목 및 나목에 따라 같은 대지에서 두 동(棟) 이상의 건축물이 서로 마주보고 있는 경우에 건축물 각 부분 사이의 거리는 다음 각 호의 거리 이상을 띄어야 한다.


1. 채광을 위한 창문 등이 있는 벽면으로부터 직각방향으로 건축물 각 부분 높이의 1.0배 (도시형 생활주택의 경우에는 0.5배)이상
2. 제1호에도 불구하고 서로 마주보는 건축물 중 높은 건축물(높은 건축물을 중심으로 마주보는 두 동의 축이 시계방향으로 정동에서 정서 방향인 경우만 해당 한다)의 주된 개구부(거실과 주된 침실이 있는 부분의 개구부를 말한다)의 방향이 낮은 건축물을 향하는 경우에는 10미터 이상으로서 낮은 건축물 각 부분의 높이의 1.0배 (도시형생활주택 포함) 이상으로 한다.

■ 층별 높이 기준

층 수	필로티내부 건축물 설치(101동,104동,105동,107동)				1층 전체 필로티 적용 건축물(102동,103동,106동,108동)			
	팬트하우스 인 경우		팬트하우스 아닌 경우		팬트하우스 인 경우		팬트하우스 아닌 경우	
	(1H)	(H/2)	(1H)	(H/2)	(1H)	(H/2)	(1H)	(H/2)
15층	43,500	21,750	43,300	21,650	40,000	20,000	39,800	19,900
16층	46,300	23,150	46,100	23,050	42,800	21,400	42,600	21,300
17층	49,100	24,550	48,900	24,450	45,600	22,800	45,400	22,700
18층	51,900	25,950	51,700	25,850	48,400	24,200	48,200	24,100
19층	54,700	27,350	54,500	27,250	51,200	25,600	51,000	25,500
20층	57,500	28,750	57,300	28,650	54,000	27,000	53,800	26,900
21층	60,300	30,150	60,100	30,050	56,800	28,400	56,600	28,300
22층	63,100	31,550	62,900	31,450	59,600	29,800	59,400	29,700
23층	65,900	32,950	65,700	32,850	62,400	31,200	62,200	31,100
24층	68,700	34,350	68,500	34,250	65,200	32,600	65,000	32,500
25층	71,500	35,750	71,300	35,650	68,000	34,000	67,800	33,900
26층	74,300	37,150	74,100	37,050	70,800	35,400	70,600	35,300
27층	77,100	38,550	76,900	38,450	73,600	36,800	73,400	36,700
28층	79,900	39,950	79,700	39,850	76,400	38,200	76,200	38,100
29층	82,700	41,350	82,500	41,250	79,200	39,600	79,000	39,500

■ 건축물 높이 산정 기준

구 분	높이 산출 기준 건축한계선(부대복리시설3M) 대지경계선(구역계) 건축한계선(6M)
필로티 내부 건축물 설치	- 높이 = 3.5m + { (층수 - 3) × 기준층고 } + 3.00m + 3.00m + 0.40m - 층고 : 1층(3.00m), 기준층(2.80m), 최상층아래층(3.00m), 최상층(3.00m) - 1층 GL +0.50m - 파라펫 높이 : 0.40m
1층 전체 필로티 적용 건축물	- 높이 = { (층수 - 3) × 기준층고 } + 3.00m + 3.00m + 0.40m - 층고 : 기준층 (2.80m), 최상층아래층 (3.00m), 최상층 (3.00m) - 파라펫 높이 : 0.40m

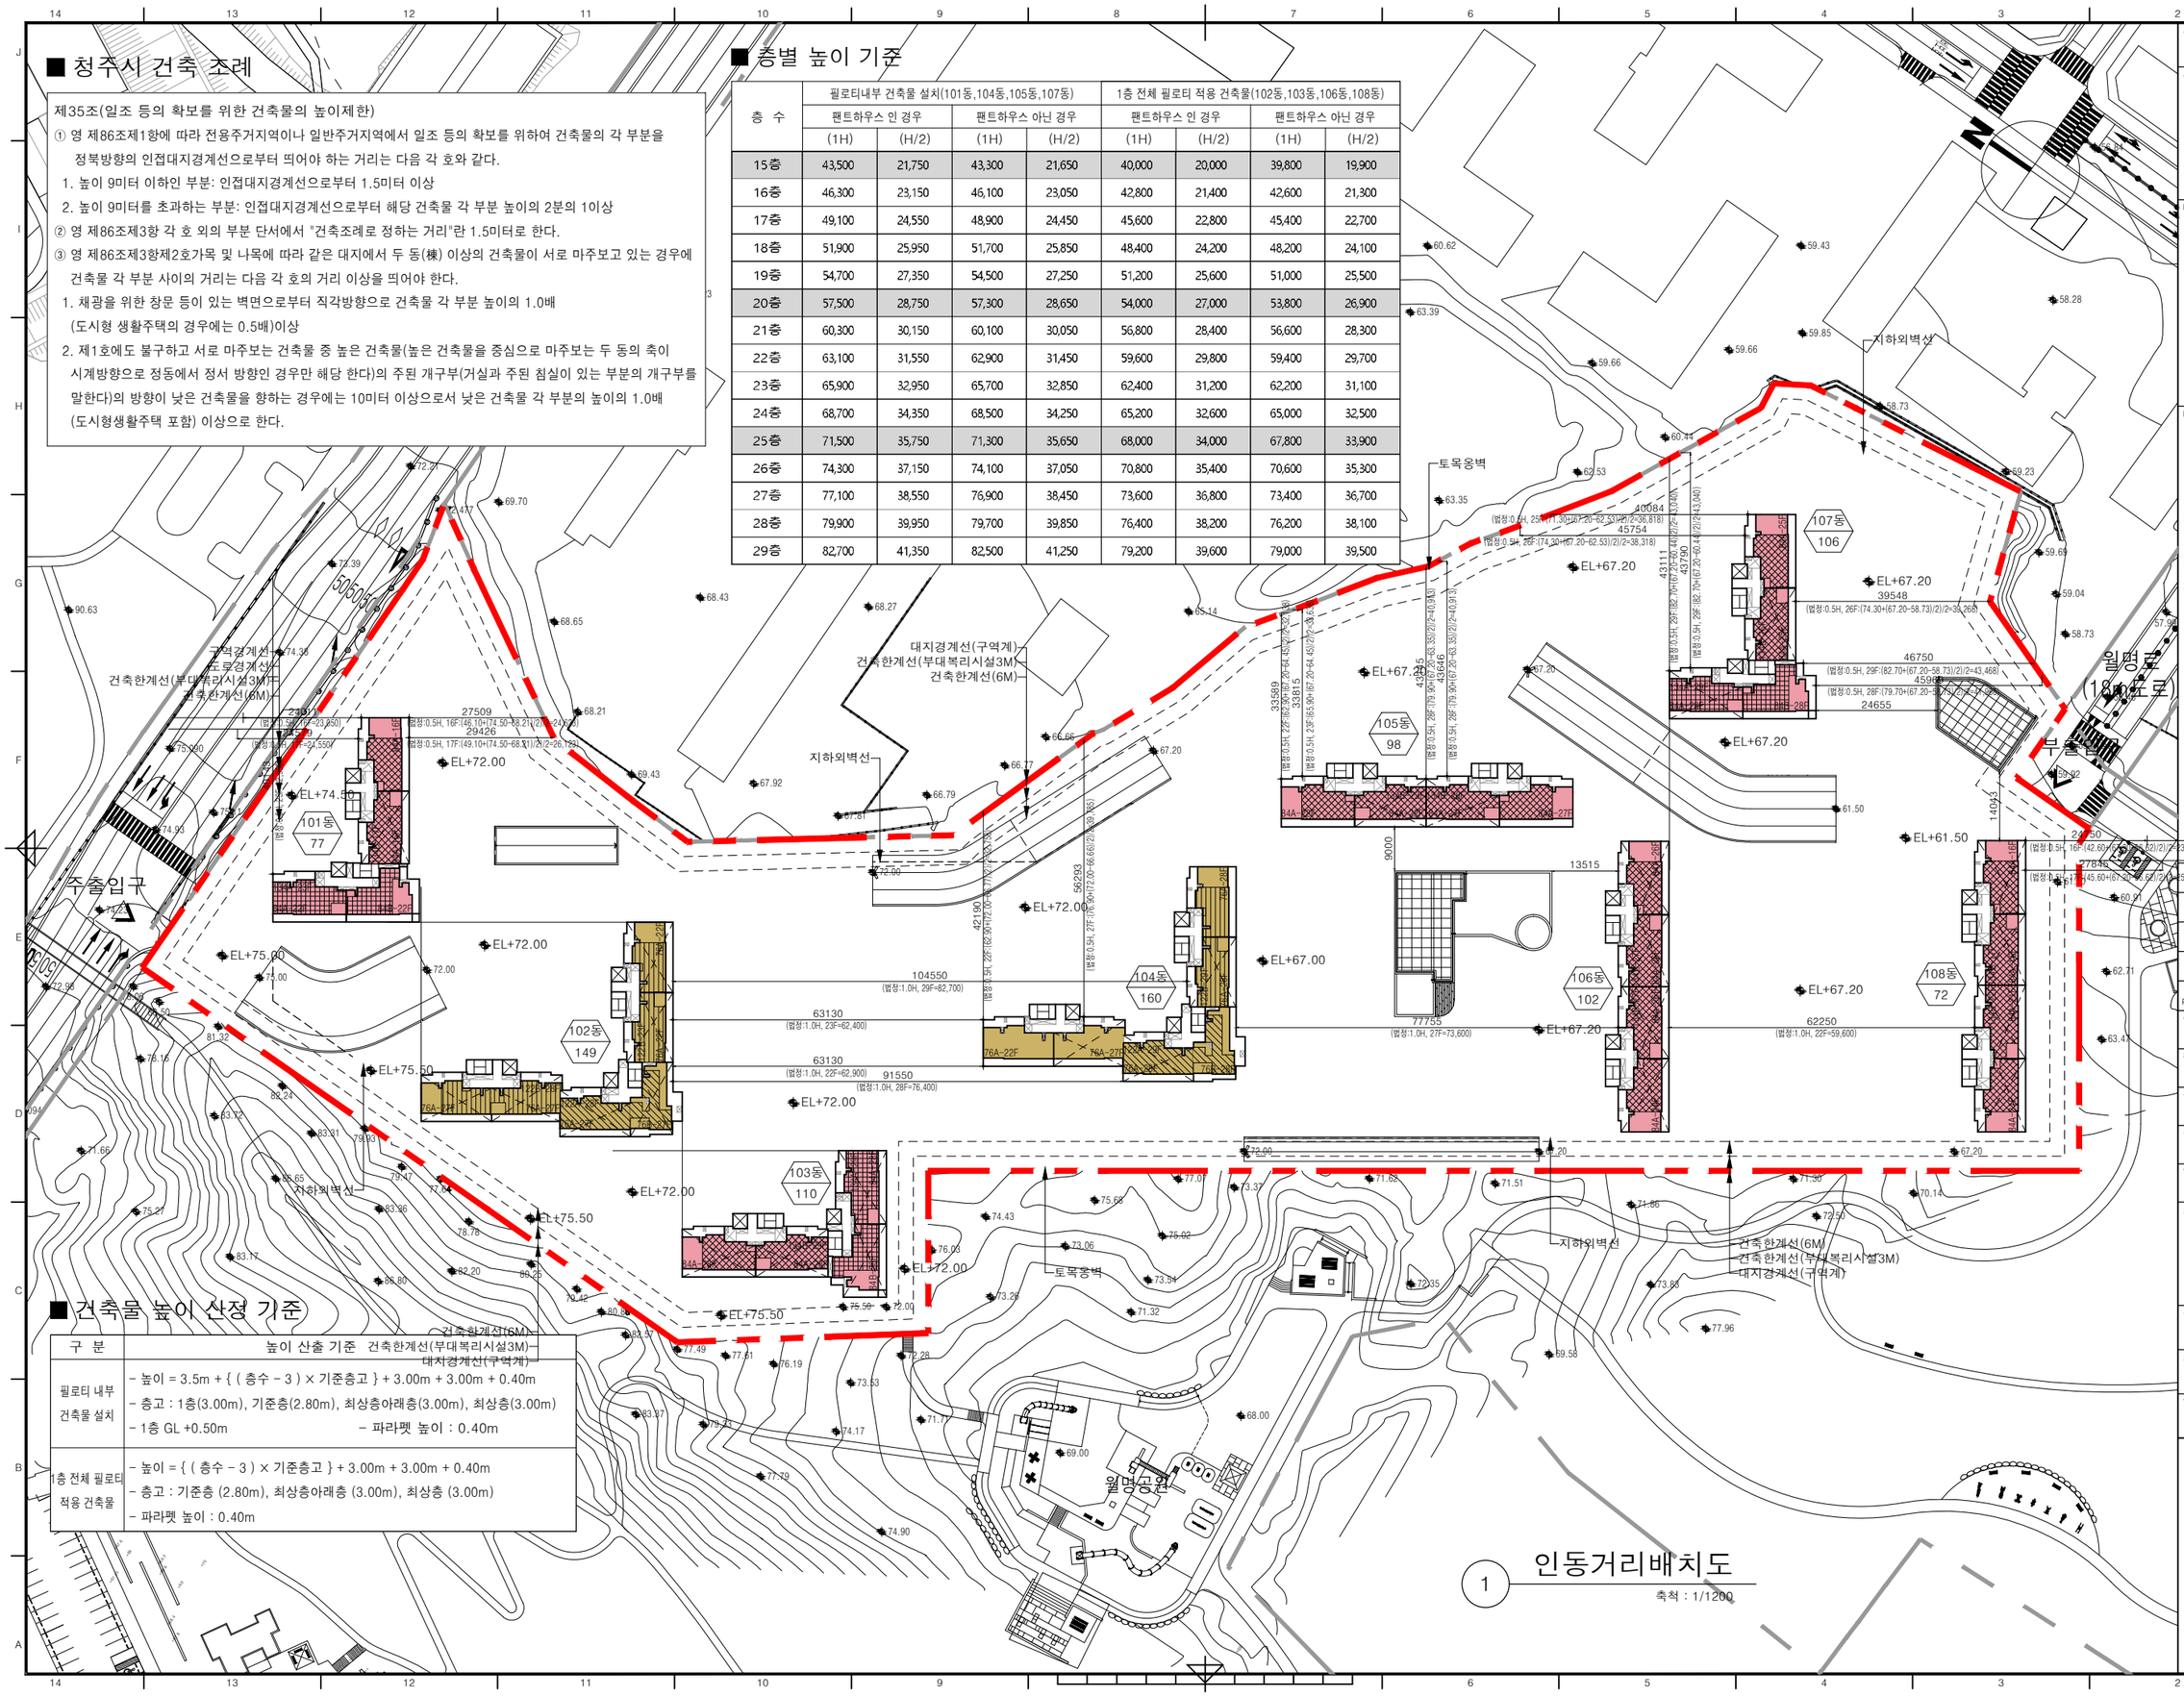

1 인동거리배치도

축척 : 1/1200

사업번호 PROJECT NO.

사업명 PROJECT TITLE

청주 월명근린공원 조성 및 공동주택 신축공사

KEY PLAN

NOTE

1. TBM2 = EL:67.312(토목도면 참조)

수정번호 REV. NO.	일 자 DATE	내 용 DESCRIPTION	승 인 CHKD
1	23.08	1차 검수용 도서	

설계 DESIGNED BY

검토 CHECKED BY

심사 SUMMITED BY

승인 APPROVED BY 이승준 이진수

일자 DATE 2023. 09.

도면명 DRAWING TITLE

인동거리배치도

축 척 SCALE A1: 1/600 A3: 1/1200

도면번호 DRAWING NO. AG-109

일련번호 SHEET NO. 1 REV. NO.

HAUD (주)하우드현지니어링 종합건축사사무소
Architects, Planners & Engineers
TEL. 02 2148 4493, SEOUL, KOREA

JH 건축사사무소 진 한
Architecture & Engineering
서울시 송파구 법원로11길7 현대지식산업센터C 921호
TEL : 02) 415-3785/6 FAX : 02) 415-3787
E-MAIL : jinhangood@empal.com