


■ 범 례

건 축 한 계 선	공 공 조 경
차량출입허용구간	중저층구간(10층이하)
직 각 배 치 구 간	탑상형 배치구간
전 면 공 지	통 경 축 구 간

■ 인동거리 산출표

층 수	* 아파트 높이 산정식	인동거리 (1H)	인동거리 (0.8H)	도로사선 (H/1.5)	정북일조 (H/2)	채광부일조 (H/2)
9층	0.6+(2.7X 9)+0.23=25.13 0.8+(2.7X 9)+0.23=25.33	25.13 25.33	20.10 20.26	16.75 16.94	12.56 12.66	12.56 12.66
10층	0.6+(2.7X10)+0.23=27.83	27.83	22.26	18.55	13.91	13.91
11층	0.6+(2.7X11)+0.23=30.53 0.8+(2.7X11)+0.23=30.73	30.53 30.73	24.42 24.58	20.35 20.48	15.26 15.36	15.26 15.36
12층	0.6+(2.7X12)+0.23=33.23	33.23	26.58	22.15	16.61	16.61
13층	0.6+(2.7X13)+0.23=35.93	35.93	28.74	23.95	17.96	17.96
14층	0.6+(2.7X14)+0.23=38.63	38.63	30.90	25.75	19.31	19.31
15층	0.6+(2.7X15)+0.23=41.33	41.33	33.06	27.55	20.66	20.66
16층	0.6+(2.7X16)+0.23=44.03	44.03	35.22	29.35	22.01	22.01
17층	0.6+(2.7X17)+0.23=46.73	46.73	37.38	31.15	23.36	23.36
18층	0.6+(2.7X18)+0.23=49.43	49.43	39.54	32.95	24.71	24.71
19층	0.6+(2.7X19)+0.23=52.13	52.13	41.70	34.75	26.06	26.06
20층	0.6+(2.7X20)+0.23=54.83	54.83	43.86	36.55	27.41	27.41

* 지붕 형태 : 경사지붕
* 1층 FL = GL + 0.6M(0.8M:계단실형/1201,1202,1203동)
* 층고 : 2.7 M
* 기준층고+0.23 M(난간높이)
* 이격거리 표기 예 = 계획 이격거리 / <법정> 계산식 및 이격거리

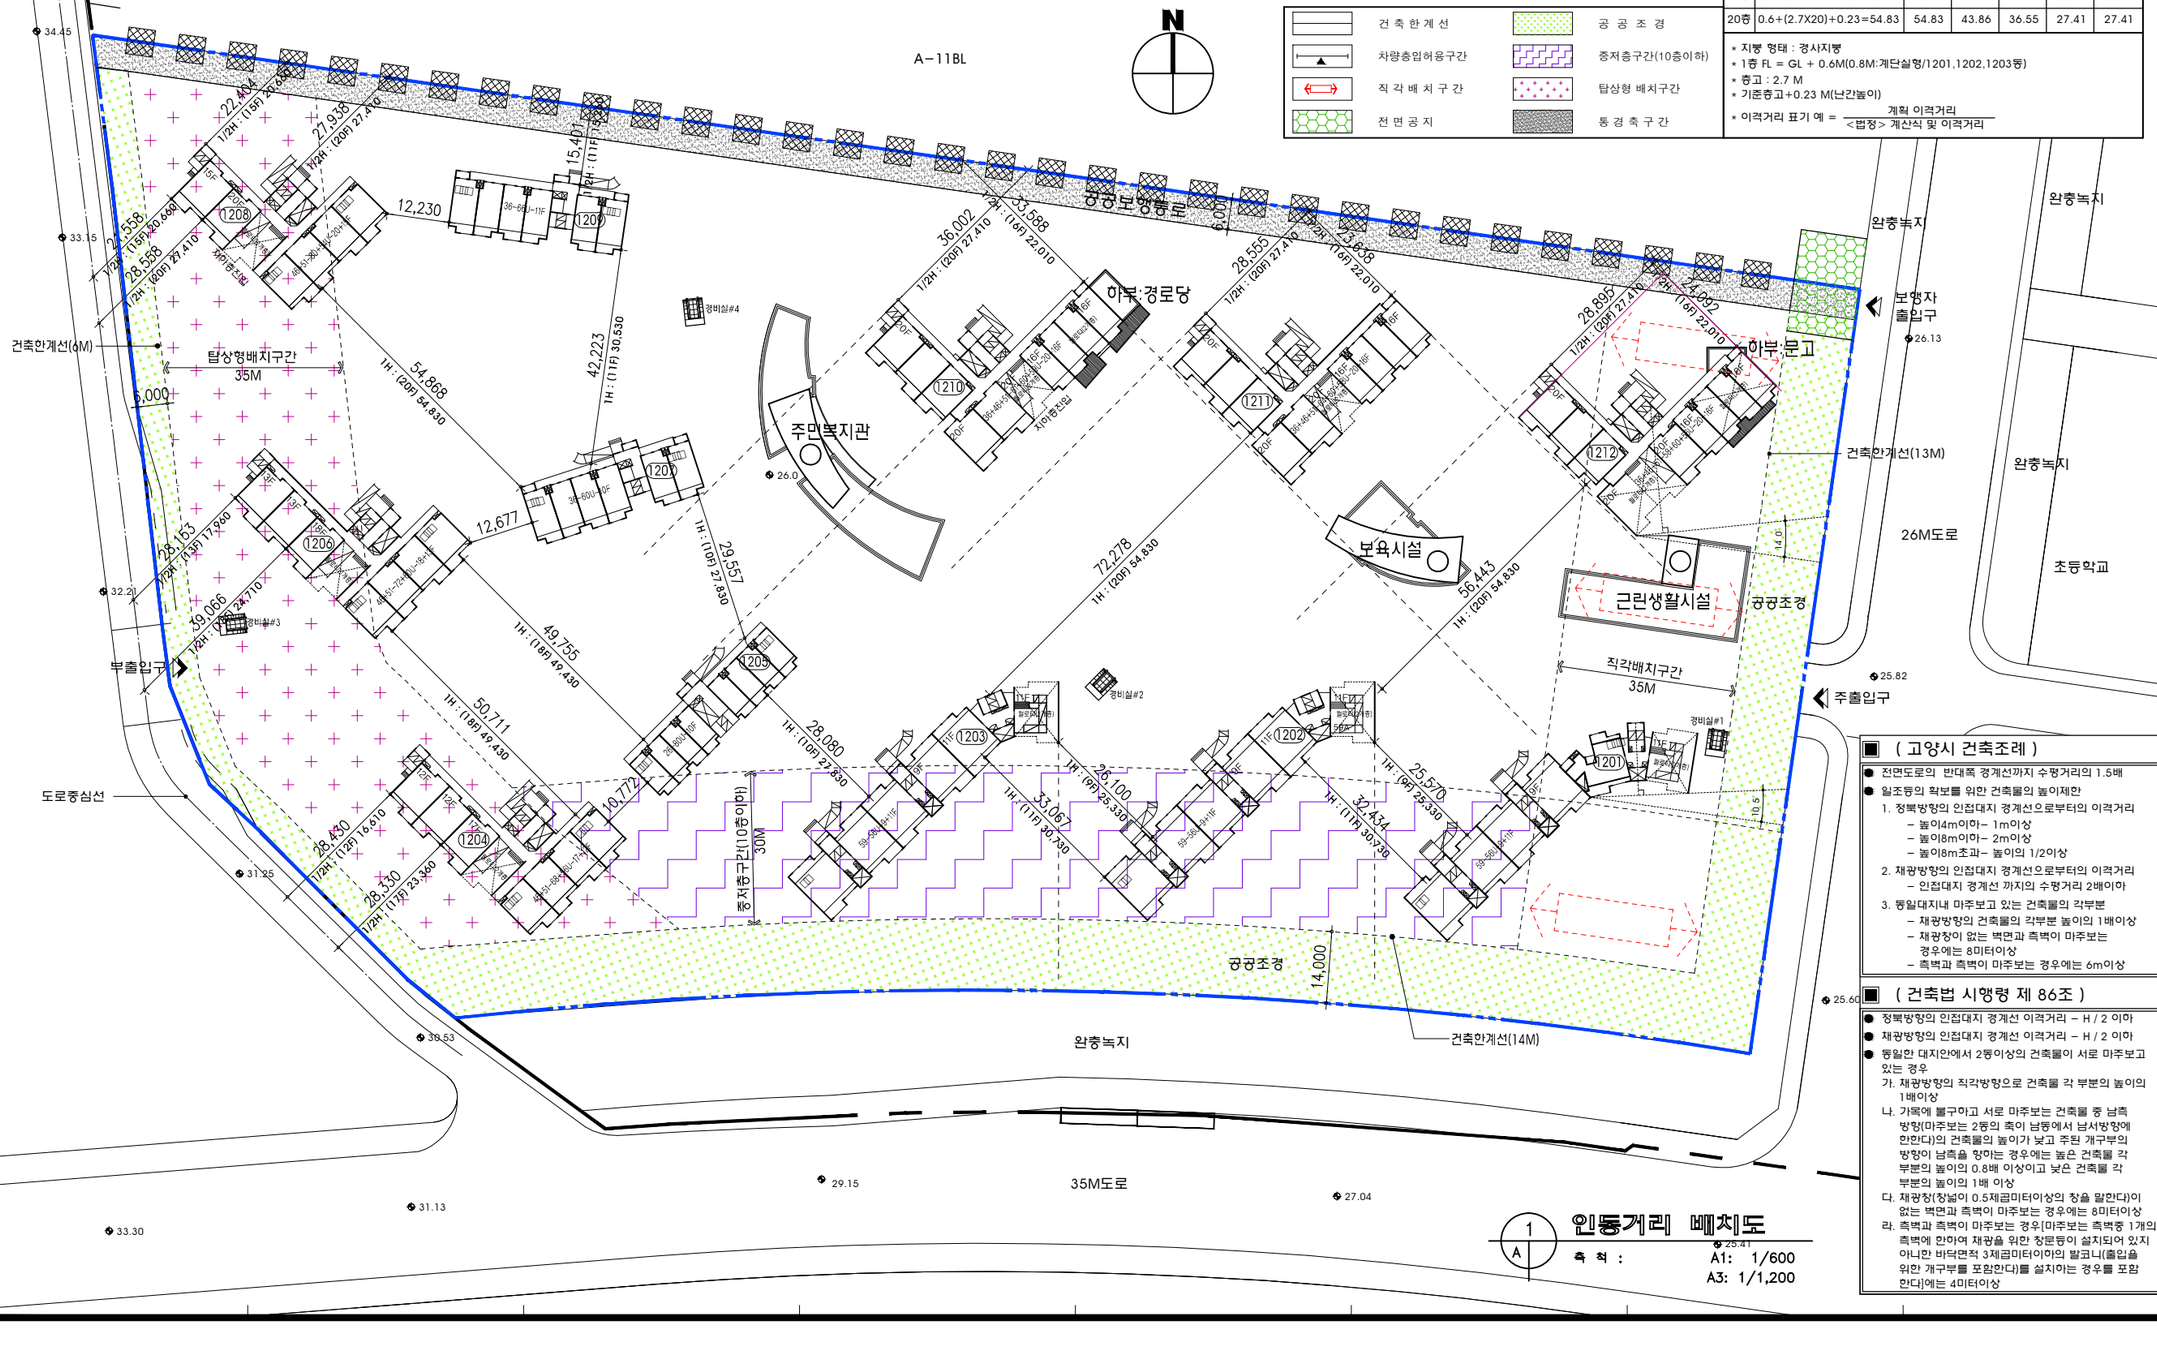

■ (고양시 건축조례)

- 전면도로의 반대쪽 경계선까지 수평거리의 1.5배
- 일조등의 확보를 위한 건축물의 높이제한
  1. 정북방향의 인접대지 경계선으로부터의 이격거리
     - 높이4m이하- 1m이상
     - 높이8m이하- 2m이상
     - 높이8m초과- 높이의 1/2이상
  2. 채광방향의 인접대지 경계선으로부터의 이격거리
     - 인접대지 경계선 까지의 수평거리 2배이하
  3. 동일대지내 마주보고 있는 건축물의 각부분
     - 채광방향의 건축물의 각부분 높이의 1배이상
     - 채광창이 없는 벽면과 측벽이 마주보는 경우에는 8미터이상
     - 측벽과 측벽이 마주보는 경우에는 6m이상

■ (건축법 시행령 제 86조)

- 정북방향의 인접대지 경계선 이격거리 - H / 2 이하
- 채광방향의 인접대지 경계선 이격거리 - H / 2 이하
- 동일한 대지안에서 2동이상의 건축물이 서로 마주보고 있는 경우
  가. 채광방향의 직각방향으로 건축물 각 부분의 높이의 1배이상
  나. 가목에 불구하고 서로 마주보는 건축물 중 남측방향(마주보는 2동의 축이 남동에서 남서방향에 한한다)의 건축물의 높이가 낮고 주된 개구부의 방향이 남측을 향하는 경우에는 높은 건축물 각 부분의 높이의 0.8배 이상이고 낮은 건축물 각 부분의 높이의 1배 이상
  다. 채광창(창넓이 0.5제곱미터이상의 창을 말한다)이 없는 벽면과 측벽이 마주보는 경우에는 8미터이상
  라. 측벽과 측벽이 마주보는 경우[마주보는 측벽중 1개의 측벽에 한하여 채광을 위한 창문등이 설치되어 있지 아니한 바닥면적 3제곱미터이하의 발코니(출입을 위한 개구부를 포함한다)를 설치하는 경우를 포함한다]에는 4미터이상

1 / A

인동거리 배치도

축 척 : A1: 1/600, A3: 1/1,200

LH

설계명 PROJECT TITLE

고양 삼송지구 A-12블록 공동주택 건설공사

주 기 NOTE

당초(사업승인안)

설 계 변 경
DESCRIPTION OF REVISION

일자	설계	검토	심사	승인

설계사무소명 DRAWING OFFICE NAME

(주)하우드종합건축사사무소

책임건축(기술)사 ARCHITECT NAME

이 승 준

참여기술자
대표전화 : 02-2140-4400
소장 정호혁 : 02-2140-4475
부장 이승훈 : 02-2140-4432
과장 박민수 : 02-2140-4732
과장 박건옥 : 02-2140-4749

축 척 SCALE	
A1	1 / 600
A3	1 / 1200

일 자 DATE

2007. 10.

설계번호 PROJECT NO.

도면화일명 DWG. FILE NAME

도면번호 SHEET NO.

AA - 006

도면명 SUBJECT TITLE

인동거리배치도
(사업승인안)