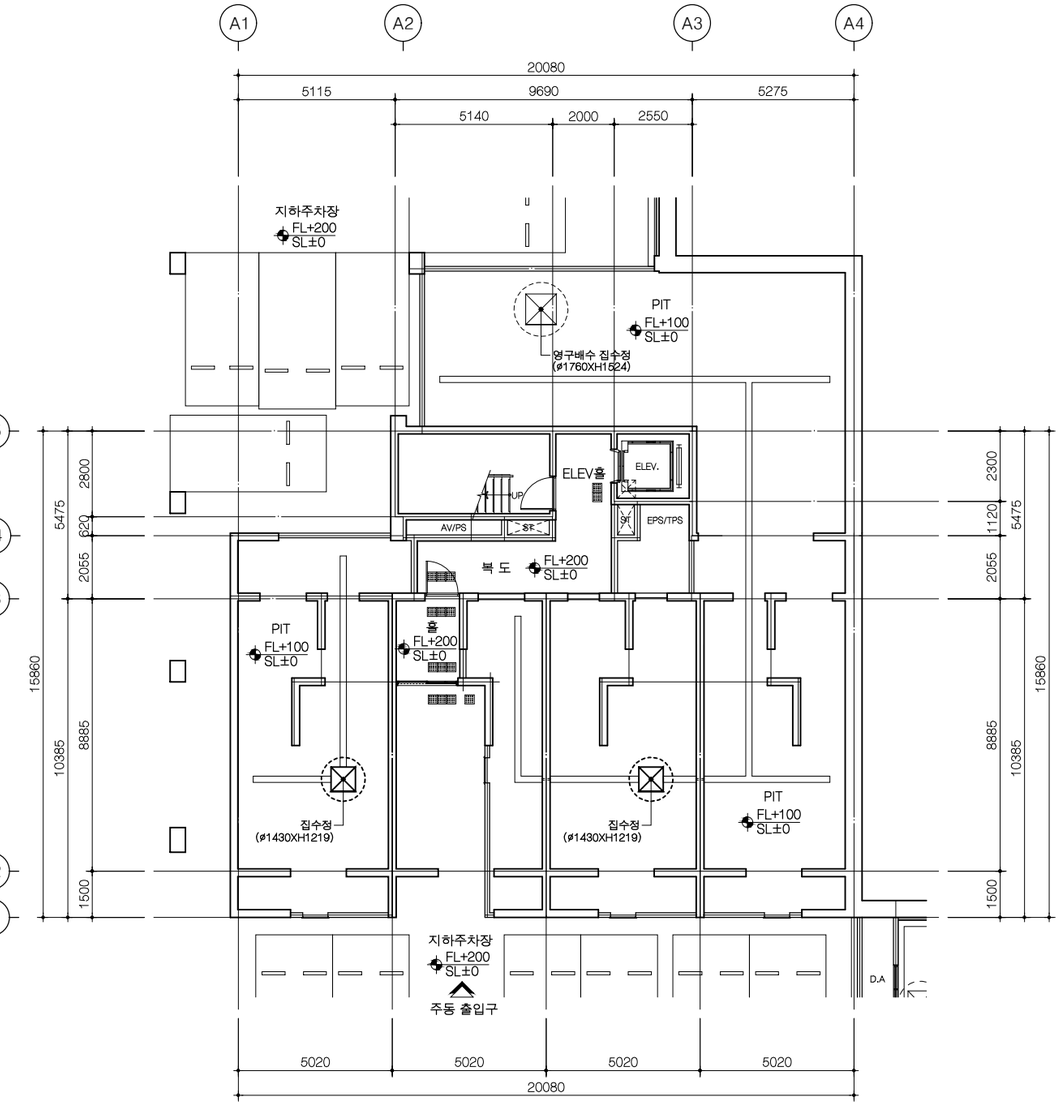

1 A 101동 지하3층 평면도

축척 = 1/100

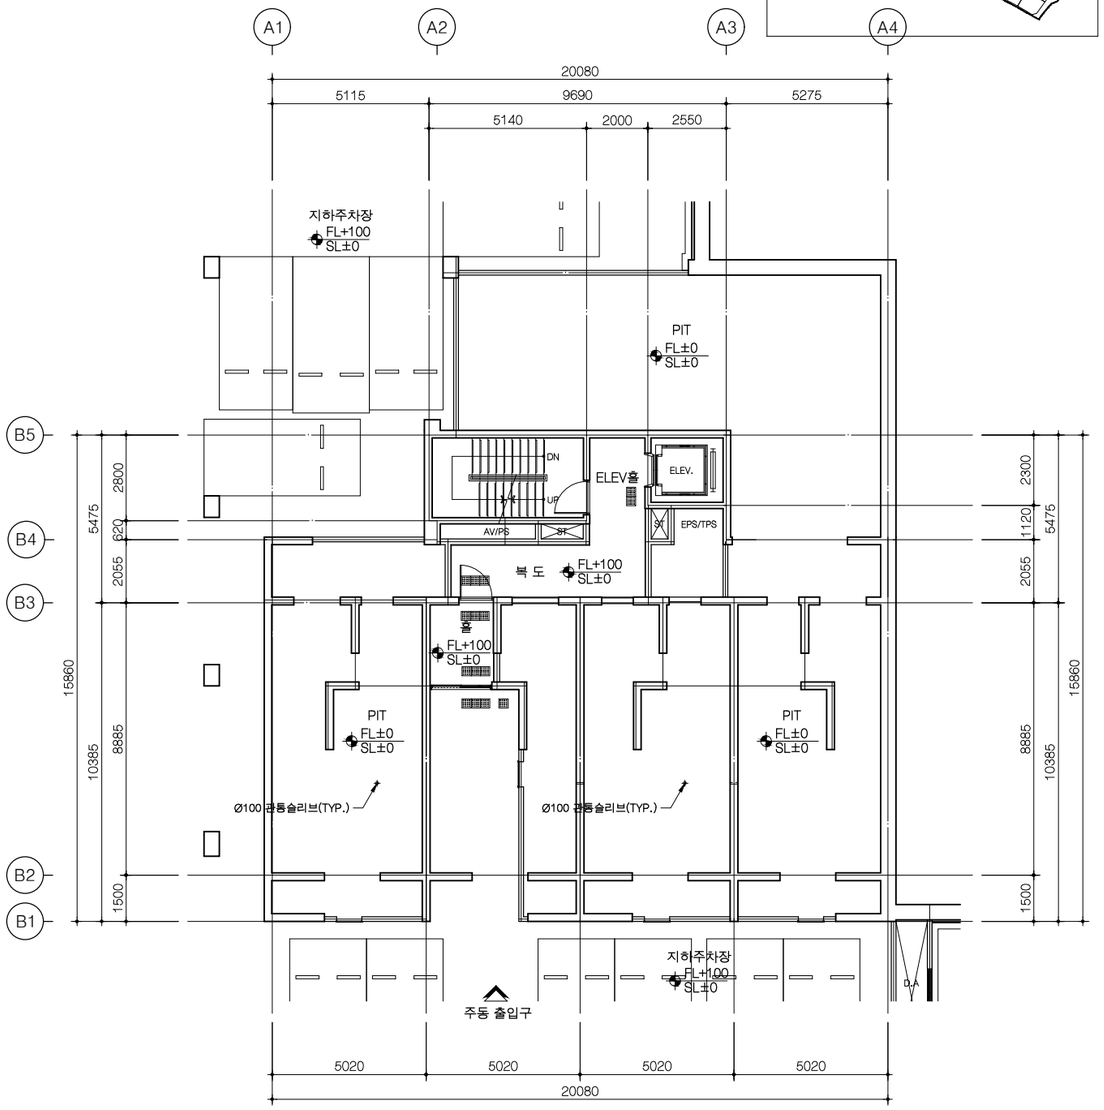

2 A 101동 지하2층 평면도

축척 = 1/100

사업번호 PROJECT NO.

사업명 PROJECT TITLE

수색4재정비촉진구역
주택재개발 정비사업

KEY MXP

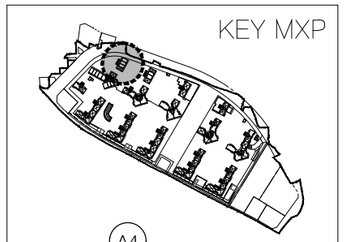

KEY PLAN

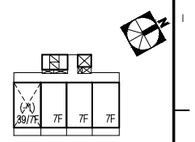

NOTE

1. 지하층 무근 콘크리트는 실시공시 THK80~120 범위로 변동이 있을수 있음.(SLOPE)
2. ELEV홀에 면한부위는 1.0B 조적쌓기임.
3. 지하주차장의 블록쌓기 기준은 높이가 3.6m이하인 경우 4인치 보강블록쌓기가 기준임 (단, 5.4m이하는 6인치쌓기, 5.4m초과는 8인치쌓기가 기준임)
4. ELEV.PIT 집수정은 (600X600X600)임.
5. 주차장 내의 창호는 주차장 창호도 참조.
6. 주차장 집수정 및 영구배수 집수정의 크기 및 위치는 지하주차장 평면도를 참조 할 것.
   ⊠: 주차장 집수정(ø1430XH1219)
   ⊠: 영구배수 집수정(ø1760XH1524)
   ⊗: 아파트 집수정(ø1430XH1219)

********** 지하3층 바닥LEVEL
B3SL±0 = B3FL±0 = EL+15.85
**** 지하2층 바닥LEVEL
B2SL±0 = B2FL±0 = EL+19.30

수정번호 REV. NO.	일 자 DATE	내 용 DESCRIPTION	승 인 CHKD
△			
△			
△			
△			

설계 DESIGNED BY

검토 CHECKED BY
최 진 규

심사 SUMMITED BY
정 호 혁

승인 APPROVED BY
이 승 준

일자 DATE
2019.08

도면명 DRAWING TITLE
101동
지하3층 및 지하2층 평면도

축 척 SCALE
A1: 1/100
A3: 1/200

도면번호 DRAWING NO.
A-301

일련번호 SHEET NO.

△ REV. NO.

HAUD
(주)하우드엔지니어링
종합건축사사무소
Architects, Planners & Engineers
TEL. 02-2140-4400, SEOUL, KOREA

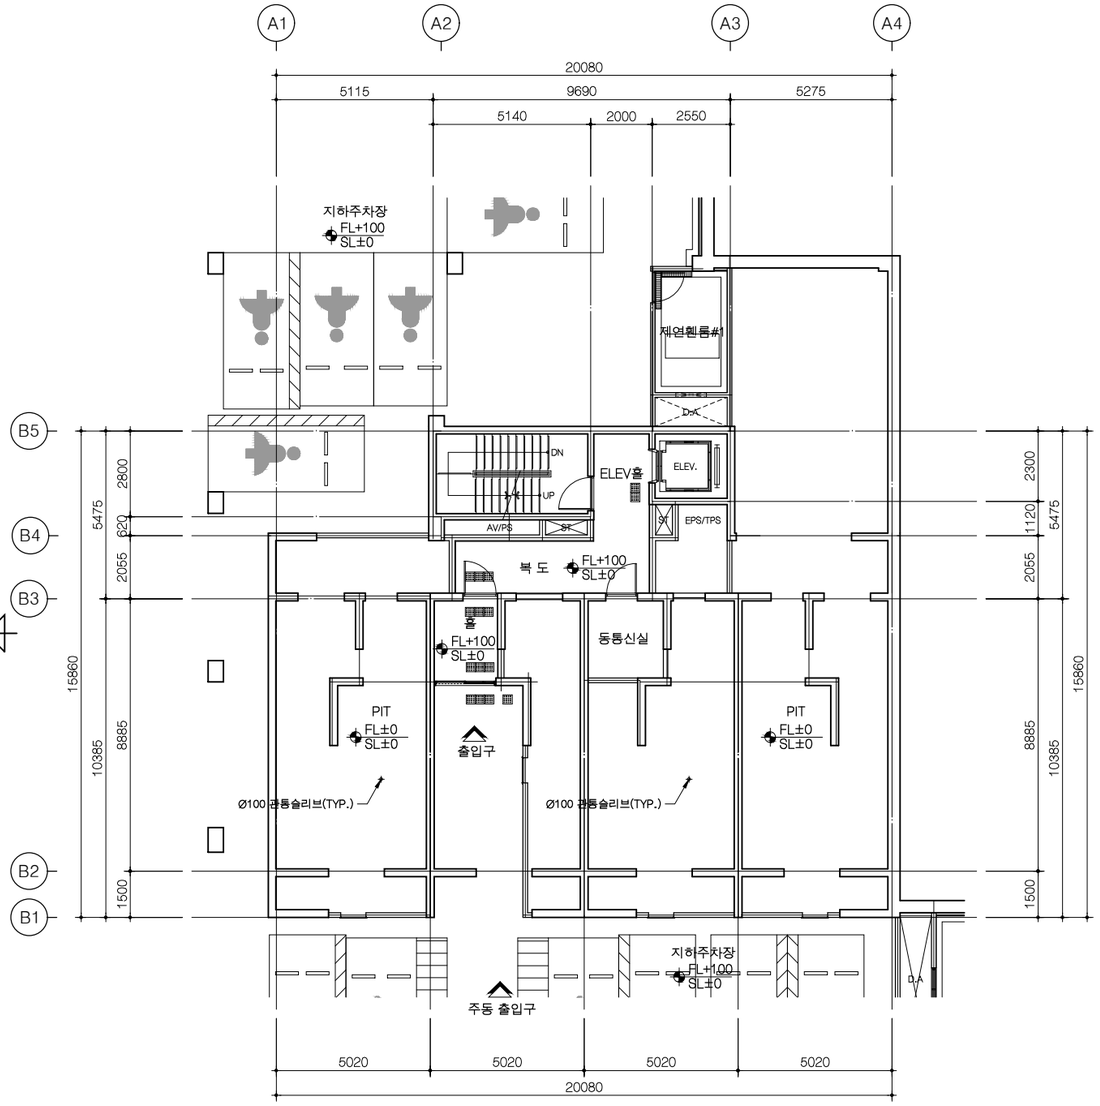

1 A 101동 지하1층 평면도

축척 = 1/100

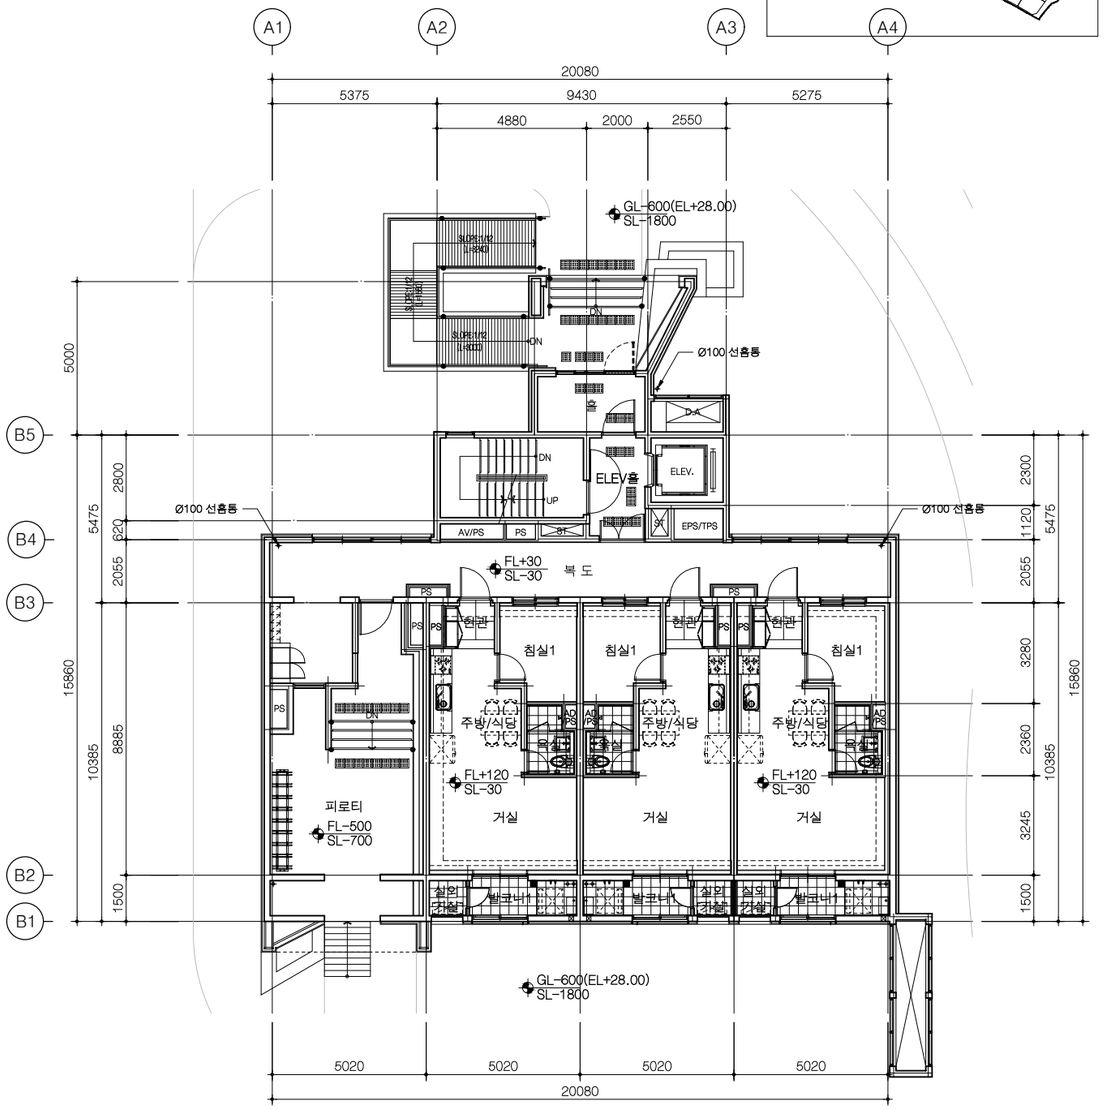

2 A 101동 1층 평면도

축척 = 1/100

KEY MXP

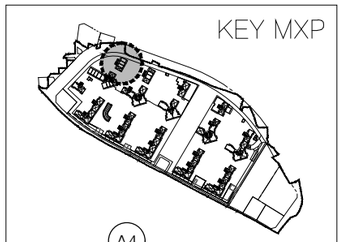

사업번호 PROJECT NO.

사업명 PROJECT TITLE

수색4재정비촉진구역
주택재개발 정비사업

KEY PLAN

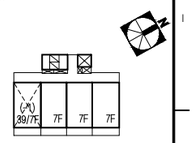

NOTE

1. 본 도면은 발코니 확장전를 기준으로 작성됨.
2. 지붕층 난간의 형태와 설치 위치는 안전성과 입면디자인을 고려하여 변경 가능함.
3. 지붕의 재료, 형태, 구조는 실시공 시 변경 될 수 있음.
4. 지붕 및 옥탑 구조물의 형태와 구조는 실시공 시 변경될 수 있음.
5. 옥상 출눈의 간격은 실시공 시 변경될 수 있음.
6. 옥상 출눈 몸에 실란트 시공되지 않음
7. 지하주차장의 ELEV홀에 면한부위는 1.0B 조적쌓기임.
8. 지하주차장의 블록쌓기 기준은 높이가 3.8m이하인 경우 4인치 보강블록쌓기가 기준임 (단, 5.4m이하는 6인치쌓기, 5.4m초과는 8인치쌓기가 기준임)
9. 주차장 내의 창호는 주차장 창호도 참조.
10. 우편물 수취함 설치 위치는 변경될 수 있음

• 지하1층 바닥LEVEL
B1SL±0 = B1FL±0 = EL+23.00
1층 바닥LEVEL
1SL±0 = 1FL±0 = GL±0 = EL+28.60
GL-600 = EL+28.00(토목도면 참조)

수정번호 REV. NO.	일 자 DATE	내 용 DESCRIPTION	승 인 CHKD
△			
△			
△			
△			

설계 DESIGNED BY

검토 CHECKED BY
최 진 규

심사 SUMMITED BY
정 호 혁

승인 APPROVED BY
이 승 준

일자 DATE
2019.08

도면명 DRAWING TITLE
101동
지하1층 및 1층 평면도

축 척 SCALE
A1: 1/100
A3: 1/200

도면번호 DRAWING NO.
A-302

일련번호 SHEET NO.

△ REV. NO.

HAUD
(주)하우드엔지니어링
종합건축사사무소
Architects, Planners & Engineers
TEL. 02 2140 4400, SEOUL, KOREA

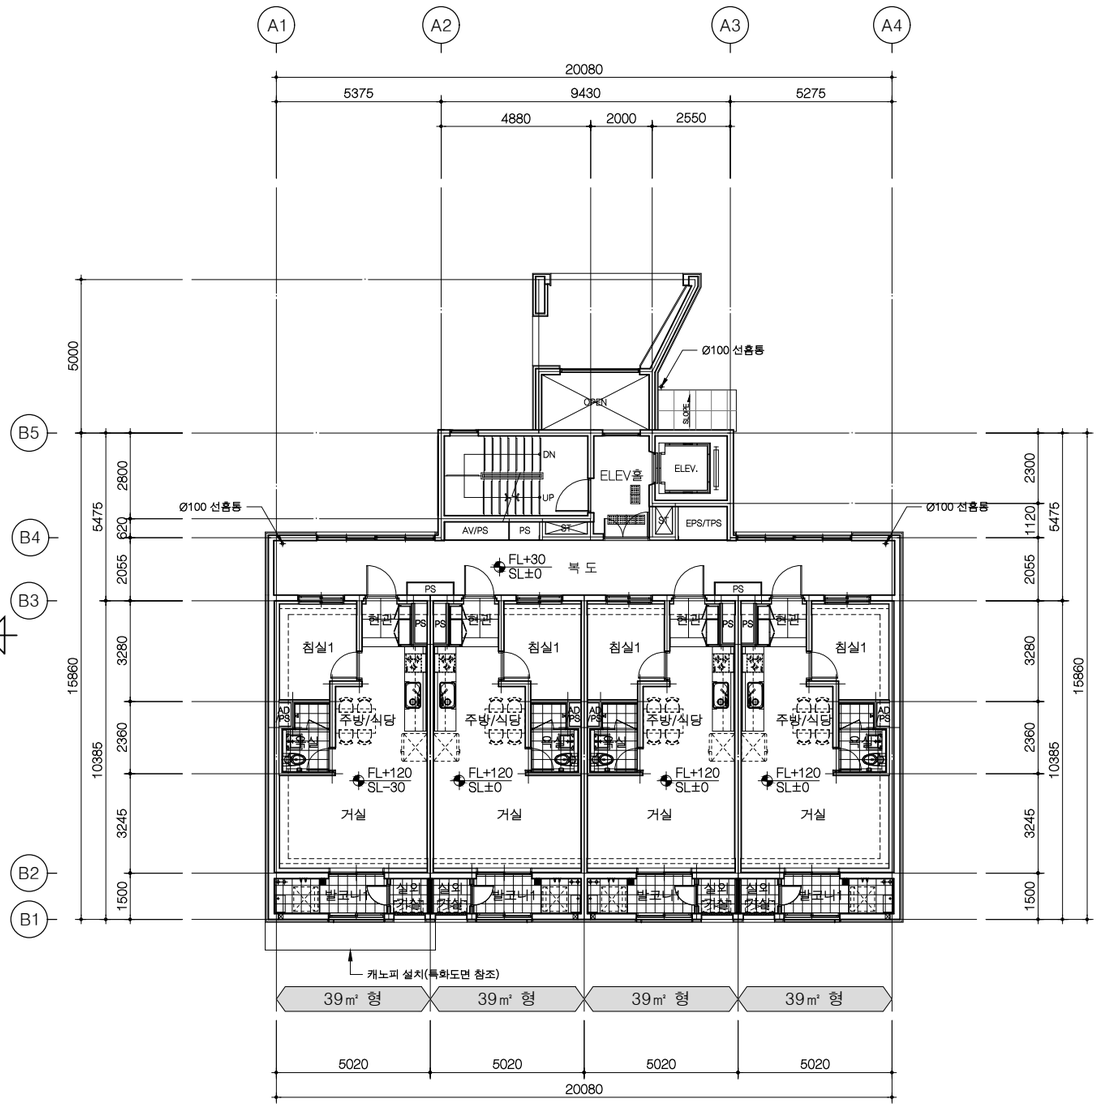

1 A 101동 2층 평면도

축척 = 1/100

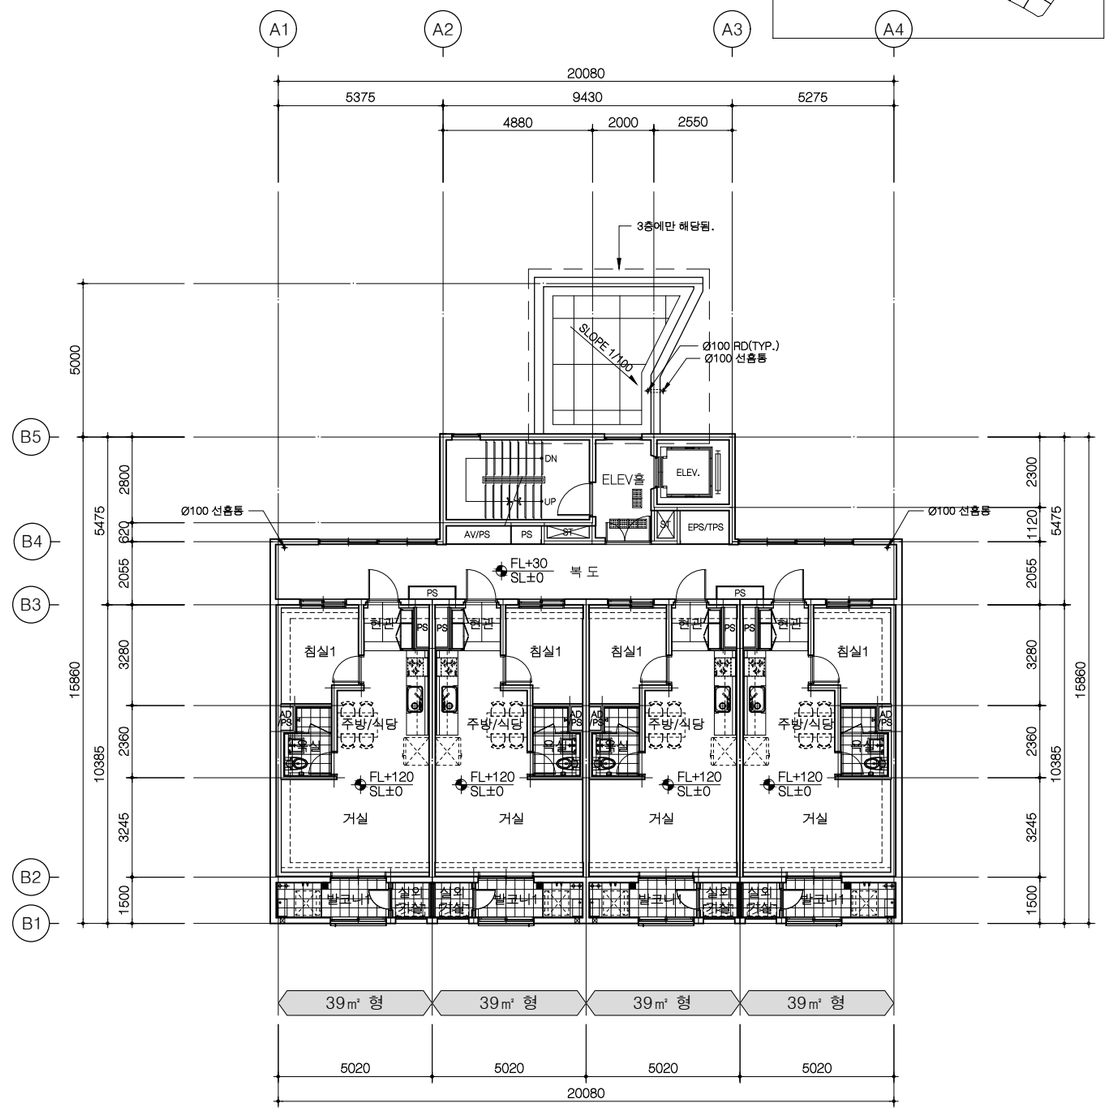

2 A 101동 3~7층 평면도

축척 = 1/100

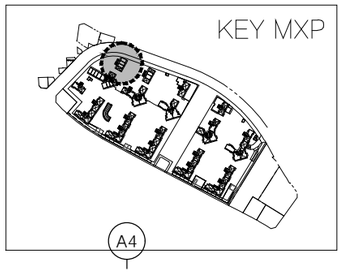

사업번호 PROJECT NO.

사업명 PROJECT TITLE

수색4재정비촉진구역
주택재개발 정비사업

KEY PLAN

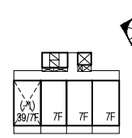

NOTE

1. 본 도면은 발코니 확장전를 기준으로 작성됨.
2. 지붕층 난간의 형태와 설치 위치는 안전성과 입면디자인을 고려하여 변경 가능함.
3. 지붕의 재료, 형태, 구조는 실시공 시 변경 될 수 있음.
4. 지붕 및 옥탑 구조물의 형태와 구조는 실시공 시 변경될 수 있음.
5. 옥상 출눈의 간격은 실시공 시 변경될 수 있음.
6. 옥상 출눈 틈에 실란트 시공되지 않음
7. 우편물 수취함 설치 위치는 변경될 수 있음

2층 바닥LEVEL
2SL±0 = 2FL±0 = EL+31.80

수정번호 REV. NO.	일 자 DATE	내 용 DESCRIPTION	승 인 CHKD
△			
△			
△			
△			

설계 DESIGNED BY

검토 CHECKED BY
최 진 규

심사 SUMMITED BY
정 호 혁

승인 APPROVED BY
이 승 준

일자 DATE
2019.08

도면명 DRAWING TITLE
101동
2층 및 3~7층 평면도

축 척 SCALE
A1: 1/100
A3: 1/200

도면번호 DRAWING NO.
A-303

일련번호 SHEET NO.

△ REV. NO.

HAUD
(주)하우드엔지니어링
종합건축사사무소
Architects, Planners & Engineers
TEL. 02 2140 4400, SEOUL, KOREA

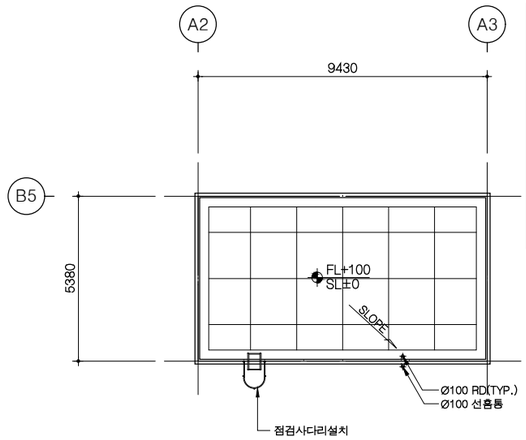

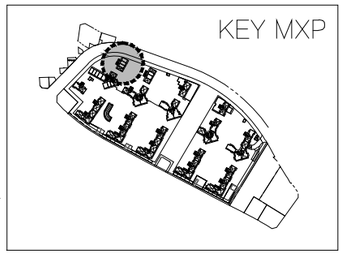

3 A 101동 옥탑지붕 평면도

축척 = 1/100

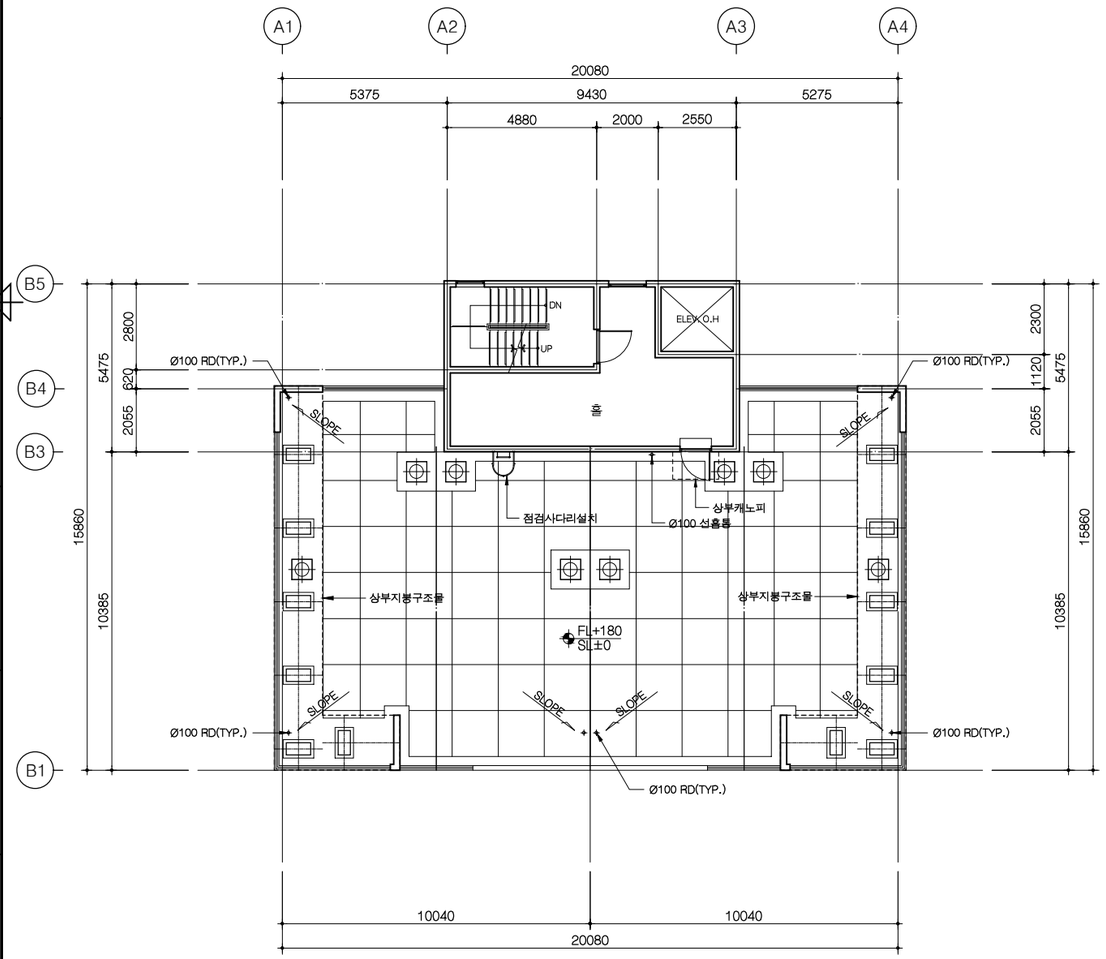

1 A 101동 지붕 평면도

축척 = 1/100

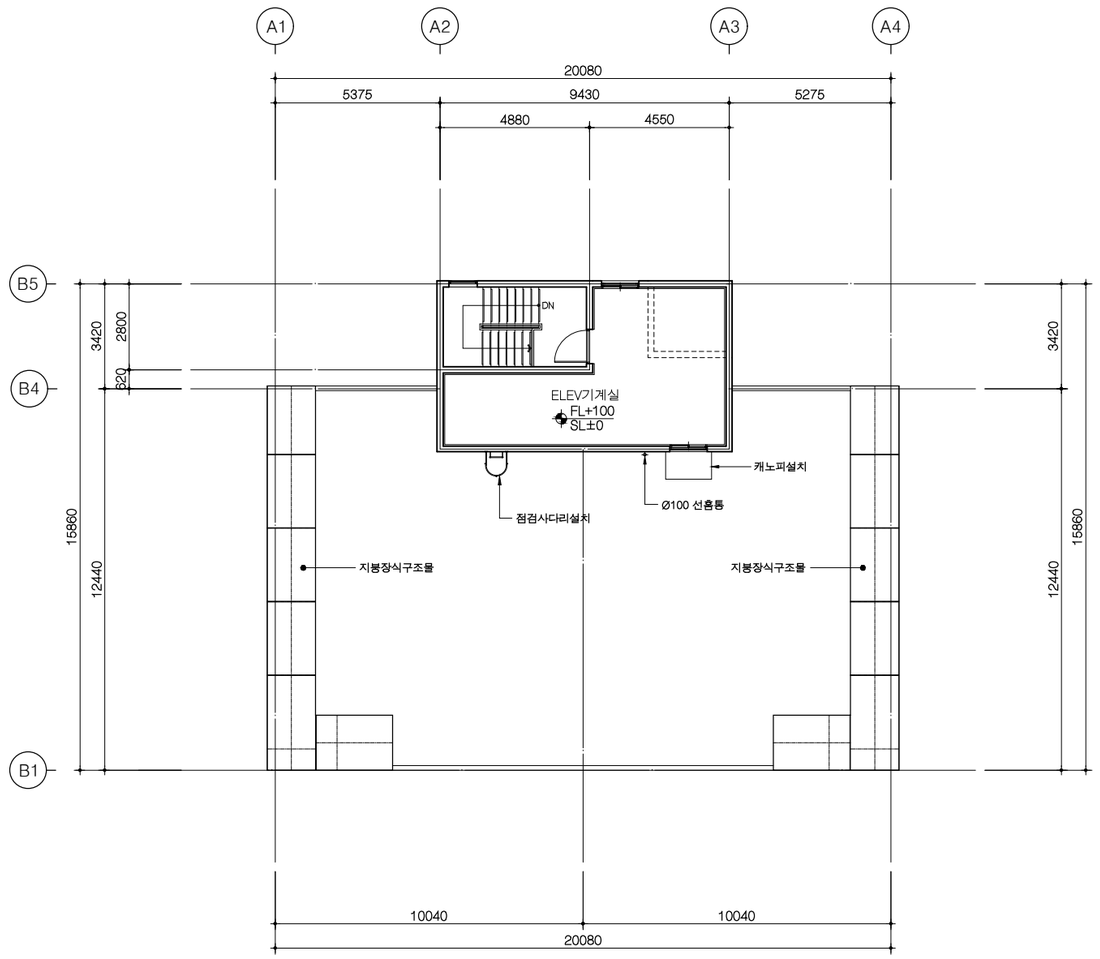

2 A 101동 옥탑층 평면도

축척 = 1/100

사업번호 PROJECT NO.

사업명 PROJECT TITLE

수색4재정비촉진구역
주택재개발 정비사업

KEY PLAN

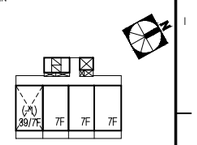

NOTE

1. 지붕바닥
   ① EXP. JOINT: 3000 X 3000
2. 본 평면도는 발코니확장전을 기준으로 작성됨
3. 재료마감은 실내,외 재료마감표 참조
4. 지붕 난간형태/설치위치는 안전성과 입면을 고려하여 실시공시 변경될 수 있음
5. 지붕재료 및 형태,구조는 실시공시 변경될수 있음
6. 지붕(옥탑지붕)의 배수드레인,청소용고리, 베기탑,점검사다리(점검구) 등의 설치위치/개소는 실시공시 변경될 수 있음
7. 옥상 상부구조물은 PC구조물 임.
8. 정화조 배기는 기계도서 참조

수정번호 REV. NO.	일 자 DATE	내 용 DESCRIPTION	승 인 CHKD
△			
△			
△			
△			

설계 DESIGNED BY

검토 CHECKED BY
최 진 규

심사 SUMMITED BY
정 호 혁

승인 APPROVED BY
이 승 준

일자 DATE
2019.08

도면명 DRAWING TITLE
101동
지붕,옥탑층 및
옥탑지붕 평면도

축 척 SCALE
A1: 1/100
A3: 1/200

도면번호 DRAWING NO.
A-304

일련번호 SHEET NO. △ REV. NO.

HAUD
(주)하우드엔지니어링
종합건축사사무소
Architects, Planners & Engineers
TEL. 02 2143 4400, SEOUL, KOREA

1 A 101동 정면도

축척 = 1/150

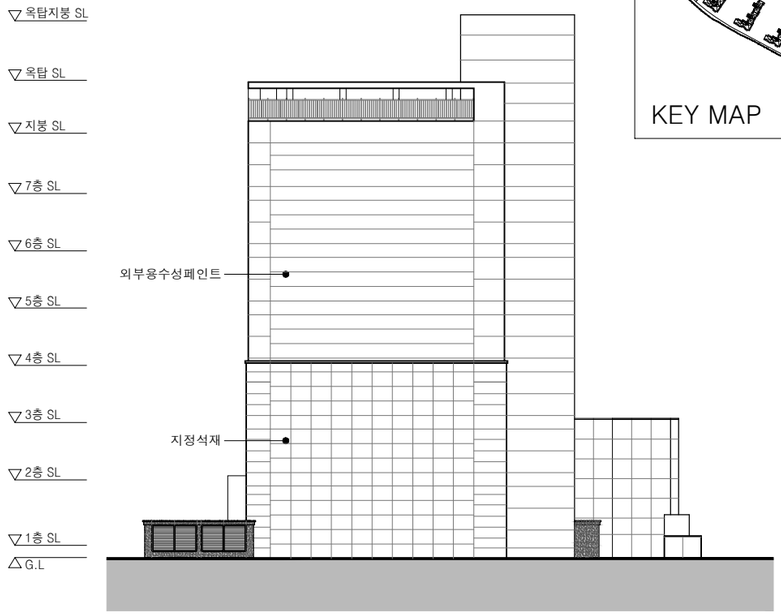

2 A 101동 우측면도

축척 = 1/150

3 A 101동 배면도

축척 = 1/150

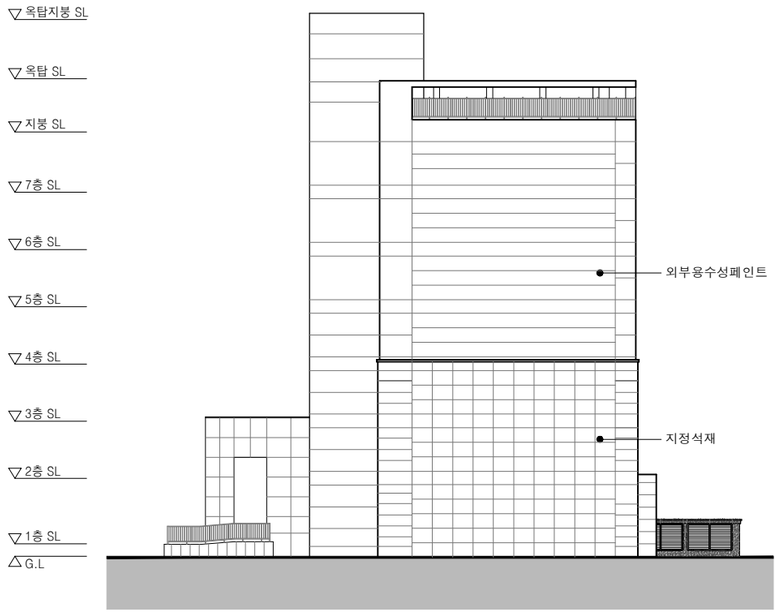

4 A 101동 좌측면도

축척 = 1/150

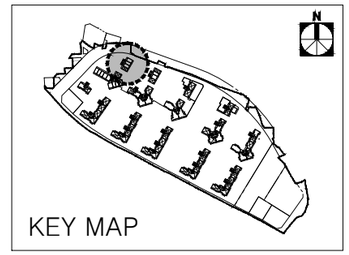

사업번호 PROJECT NO.

사업명 PROJECT TITLE

수색4재정비촉진구역
주택재개발 정비사업

KEY PLAN

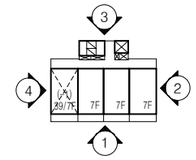

NOTE

1. 1층 바닥 LEVEL
   1SL±0 = 1FL±0 = GL±0 = EL+28.60
2. 지붕 난간의 형태 및 설치위치는 안전성과 입면디자인을 고려하여 변경가능함.
3. 지붕의 재료, 형태, 구조는 실시공시 변경될 수 있음.
4. 지붕 및 옥탑구조물의 형태와 구조는 실시공시 변경될 수 있음.
5. 외벽 및 측벽 문양은 실시공시 변경될 수 있음
6. 입면의 줄눈 및 마감선은 실시공시 변경될 수 있음.
7. 저층부 석재마감 및 입면 마감 색상, 재료에 대한 모든 기준은 특화도면을 우선 적용함.

수정번호 REV. NO.	일 자 DATE	내 용 DESCRIPTION	승 인 CHKD
△			
△			
△			
△			

설계 DESIGNED BY

검토 CHECKED BY
최 진 규

심사 SUMMITED BY
정 호 혁

승인 APPROVED BY
이 승 준

일자 DATE
2019.08

도면명 DRAWING TITLE

101동 정면도,우측면도
배면도,좌측면도

축 척 SCALE
A1: 1/150
A3: 1/300

도면번호 DRAWING NO.
A-305

일련번호 SHEET NO.

△ REV. NO.

HAUD
㈜하우드엔지니어링
종합건축사사무소
Architects, Planners & Engineers
TEL. 02 2148 4400, SEOUL, KOREA

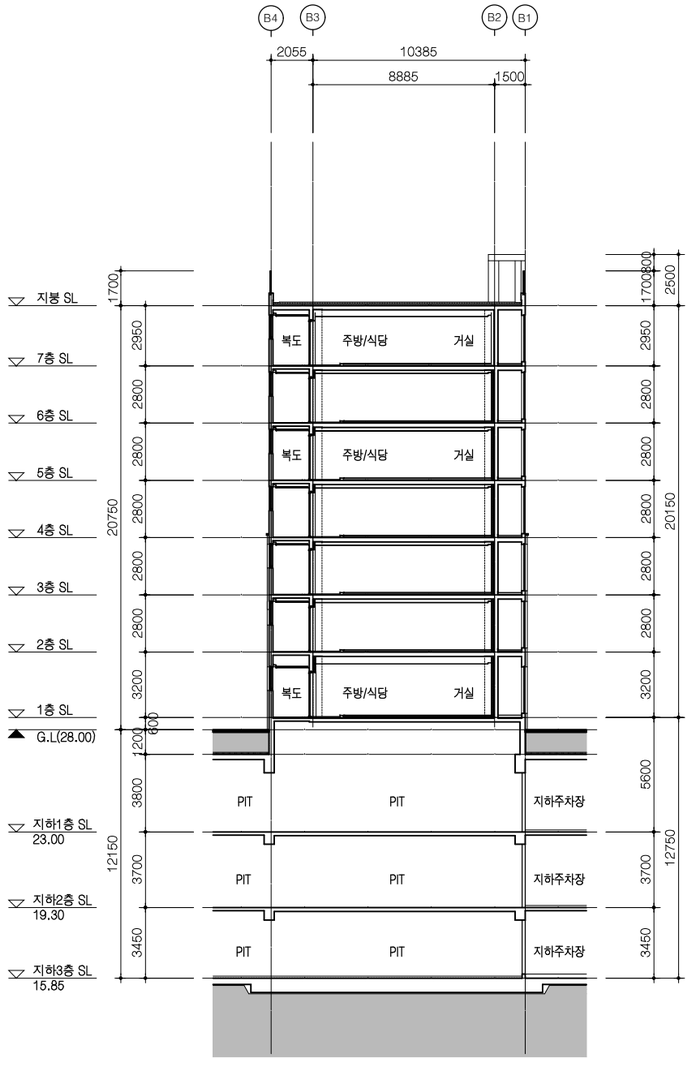

1 A 101동 종단면도

축척 = 1/150

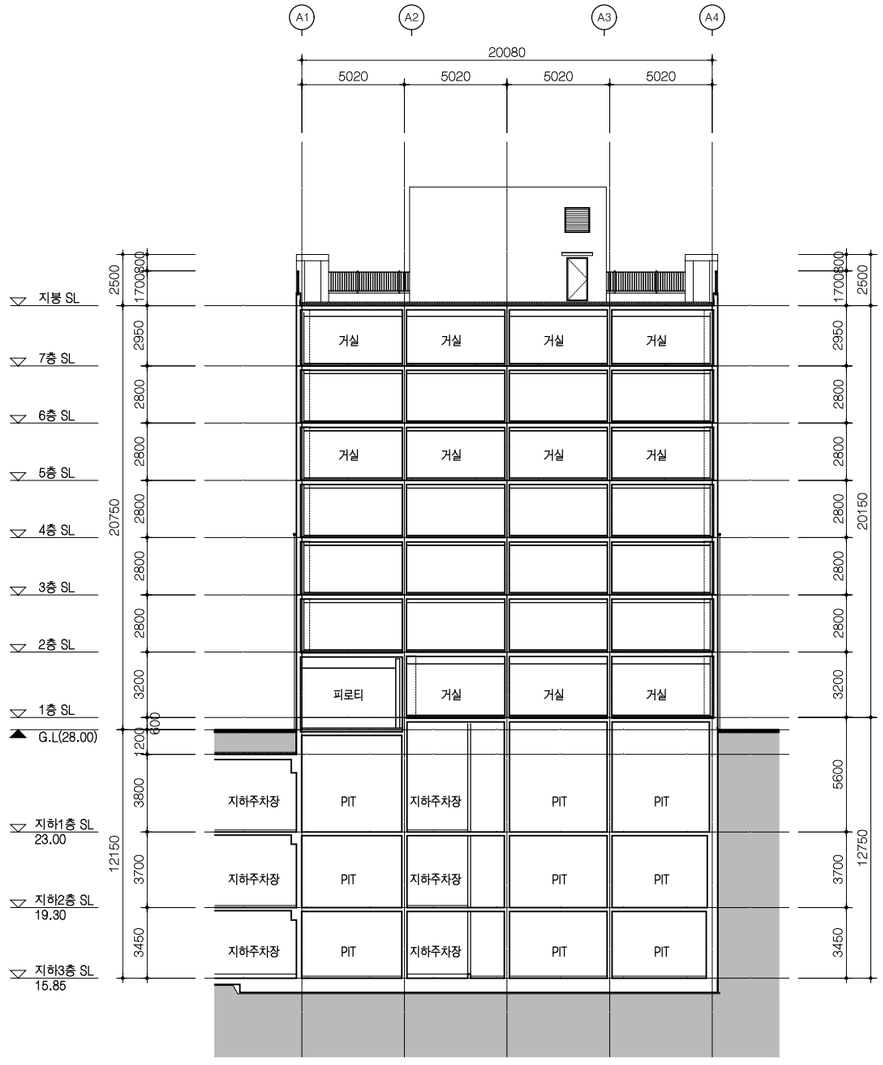

2 A 101동 횡단면도

축척 = 1/150

사업번호 PROJECT NO.

사업명 PROJECT TITLE

수색4재정비촉진구역
주택재개발 정비사업

KEY PLAN

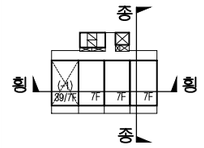

NOTE

수정번호 REV. NO.	일 자 DATE	내 용 DESCRIPTION	승 인 CHKD

설계 DESIGNED BY

검토 CHECKED BY
최 진 규

심사 SUMMITED BY
정 호 혁

승인 APPROVED BY
이 승 준

일자 DATE
2019.08

도면명 DRAWING TITLE
101동 종,횡단면도

축 척 SCALE
A1: 1/150
A3: 1/300

도면번호 DRAWING NO.
A-306

일련번호 SHEET NO.

REV. NO.

HAUD
㈜하우드엔지니어링
종합건축사사무소
Architects, Planners & Engineers
TEL. 02 2140 4400, SEOUL, KOREA

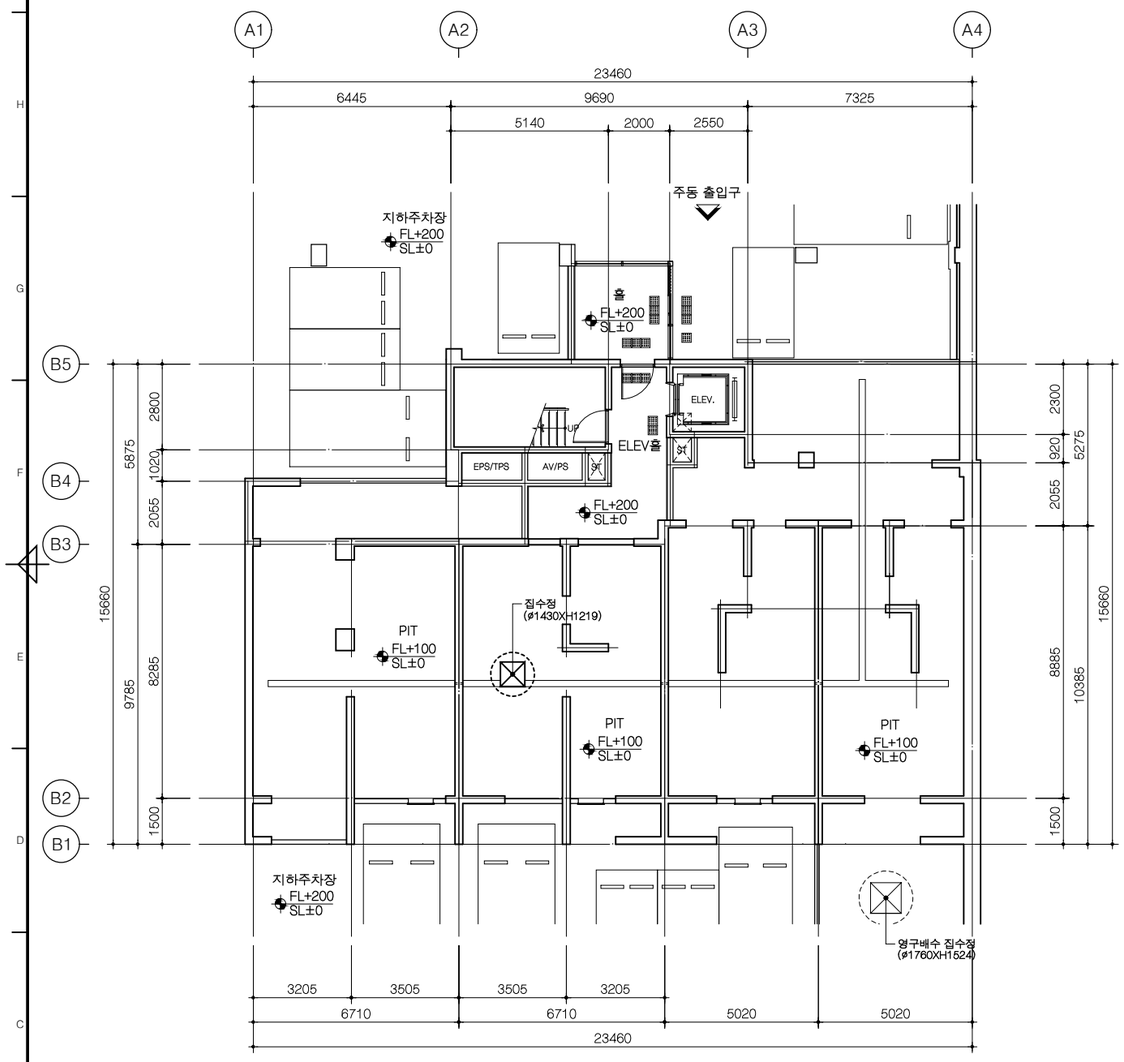

1 A 102동 지하3층 평면도

축척 = 1/100

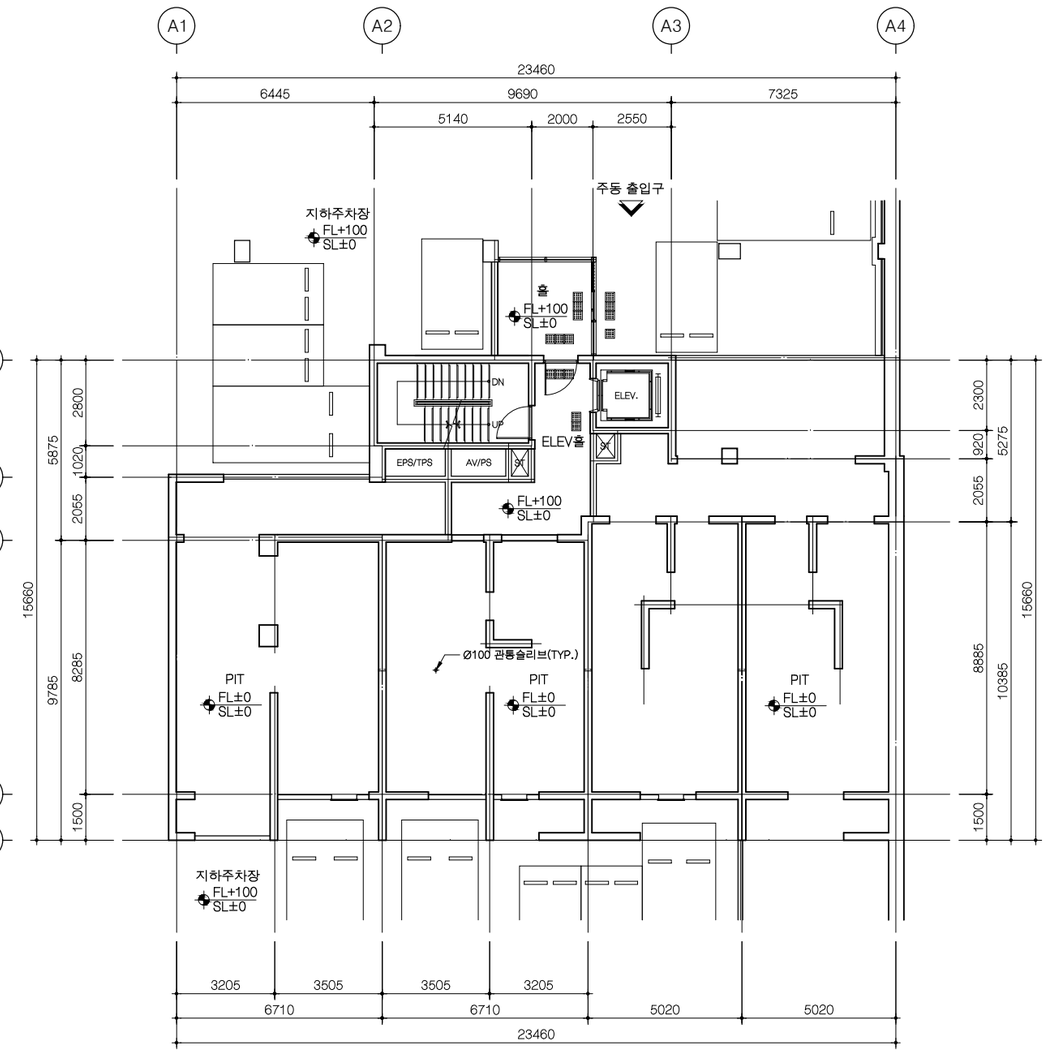

2 A 102동 지하2층 평면도

축척 = 1/100

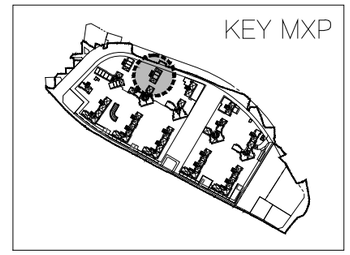

사업번호 PROJECT NO.

사업명 PROJECT TITLE

수색4재정비촉진구역
주택재개발 정비사업

KEY PLAN

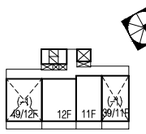

NOTE

1. 지하층 무근 콘크리트는 실시공시
   THK80~120 범위로 변동이
   있을수 있음.(SLOPE)
2. ELEV홀에 면한부위는 1.0B 조적쌓기임.
3. 지하주차장의 블록쌓기 기준은
   높이가 3.6m이하인 경우 4인치
   보강블록쌓기가 기준임
   (단, 5.4m이하는 6인치쌓기,
   5.4m초과는 8인치쌓기가 기준임)
4. ELEV.PIT 집수정은 (600X600X600)임.
5. 주차장 내의 창호는 주차장 창호도 참조.
6. 주차장 집수정 및 영구배수 집수정의
   크기 및 위치는 지하주차장 평면도를
   참조 할 것.
   ⊠: 주차장 집수정(ø1430XH1219)
   ⊠: 영구배수 집수정(ø1760XH1524)
   ⊠: 아파트 집수정(ø1430XH1219)

********** 지하3층 바닥LEVEL
B3SL±0 = B3FL±0 = EL+15.85
**** 지하2층 바닥LEVEL
B2SL±0 = B2FL±0 = EL+19.30

수정번호 REV. NO.	일 자 DATE	내 용 DESCRIPTION	승 인 CHKD
△			
△			
△			
△			

설계 DESIGNED BY

검토 CHECKED BY
최 진 규

심사 SUMMITED BY
정 호 혁

승인 APPROVED BY
이 승 준

일자 DATE
2019.08

도면명 DRAWING TITLE

102동
지하3층 및 지하2층 평면도

축 척 SCALE
A1: 1/100
A3: 1/200

도면번호 DRAWING NO.
A-311

일련번호 SHEET NO. △ REV. NO.

HAUD
(주)하우드엔지니어링
종합건축사사무소
Architects, Planners & Engineers
TEL. 02 2140 4400, SEOUL, KOREA

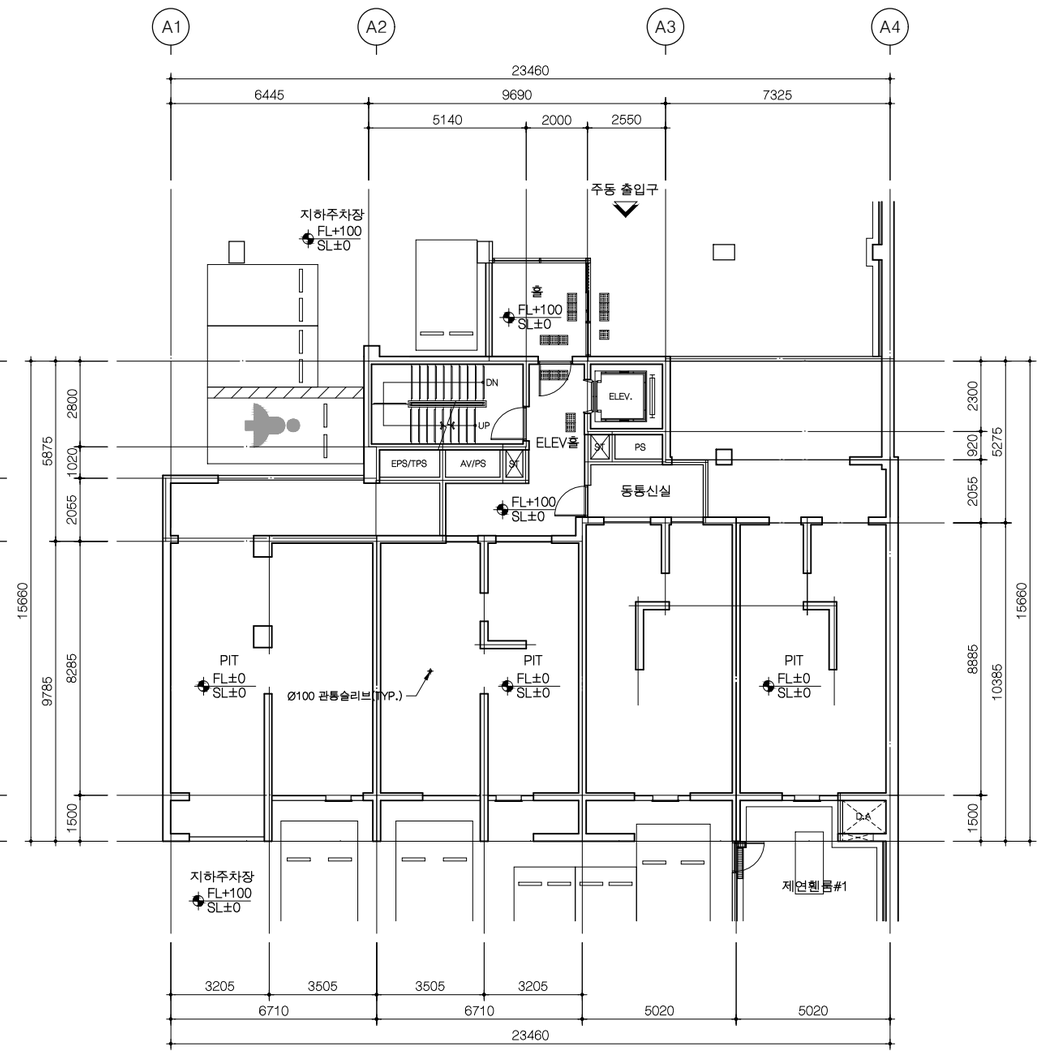

1 A 102동 지하1층 평면도

축척 = 1/100

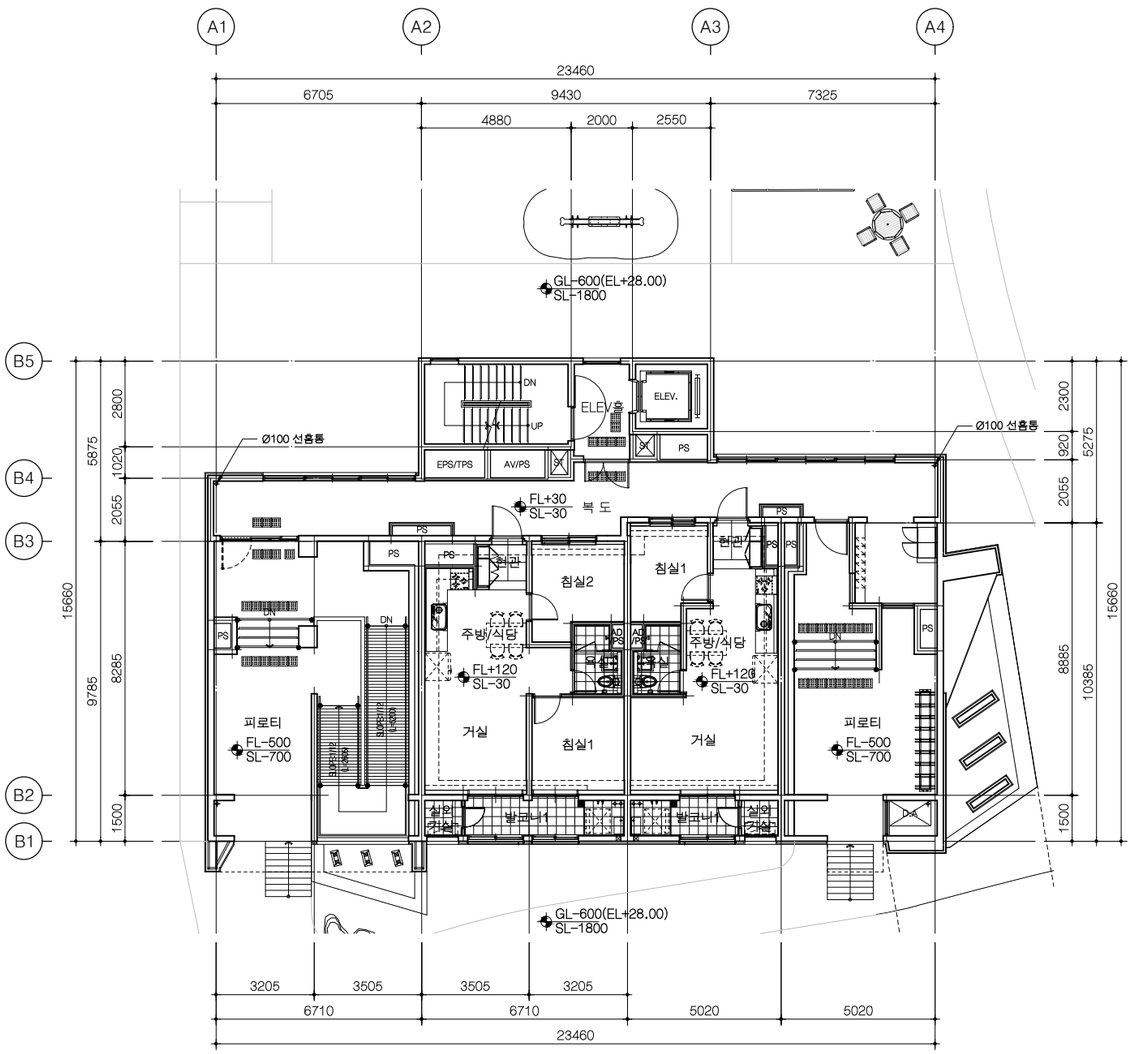

2 A 102동 1층 평면도

축척 = 1/100

KEY MXP

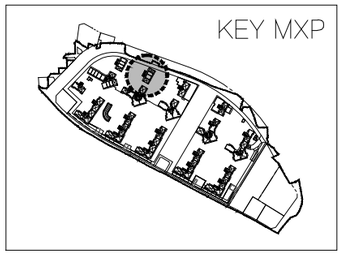

사업번호 PROJECT NO.

사업명 PROJECT TITLE

수색4재정비촉진구역
주택재개발 정비사업

KEY PLAN

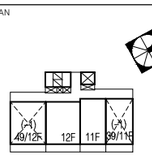

NOTE

1. 본 도면은 발코니 확장전를 기준으로 작성됨.
2. 지붕층 난간의 형태와 설치 위치는 안전성과 입면디자인을 고려하여 변경 가능함.
3. 지붕의 재료, 형태, 구조는 실시공 시 변경 될 수 있음.
4. 지붕 및 옥탑 구조물의 형태와 구조는 실시공 시 변경될 수 있음.
5. 옥상 출눈의 간격은 실시공 시 변경될 수 있음.
6. 옥상 출눈 틈에 실란트 시공되지 않음
7. 지하주차장의 ELEV홀에 면한부위는 1.0B 조적쌓기임.
8. 지하주차장의 블록쌓기 기준은 높이가 3.8m이하인 경우 4인치 보강블록쌓기가 기준임 (단, 5.4m이하는 6인치쌓기, 5.4m초과는 8인치쌓기가 기준임)
9. 주차장 내의 창호는 주차장 창호도 참조.
10. 우편물 수취함 설치 위치는 변경될 수 있음

• 지하1층 바닥LEVEL
B1SL±0 = B1FL±0 = EL+23.00
1층 바닥LEVEL
1SL±0 = 1FL±0 = GL±0 = EL+28.60
GL-600 = EL+28.00(토목도면 참조)

수정번호 REV. NO.	일 자 DATE	내 용 DESCRIPTION	승 인 CHKD
△			
△			
△			
△			

설계 DESIGNED BY

검토 CHECKED BY
최 진 규

심사 SUMMITED BY
정 호 혁

승인 APPROVED BY
이 승 준

일자 DATE
2019.08

도면명 DRAWING TITLE
102동
지하1층 및 1층 평면도

축 척 SCALE
A1: 1/100
A3: 1/200

도면번호 DRAWING NO.
A-312

일련번호 SHEET NO.

△ REV. NO.

HAUD
(주)하우드랜지니어링
종합건축사사무소
Architects, Planners & Engineers
TEL. 02 2140 4400, SEOUL, KOREA

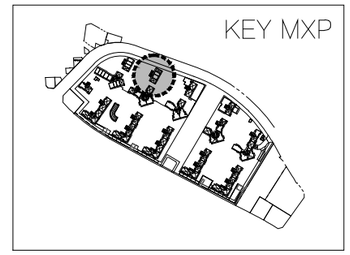

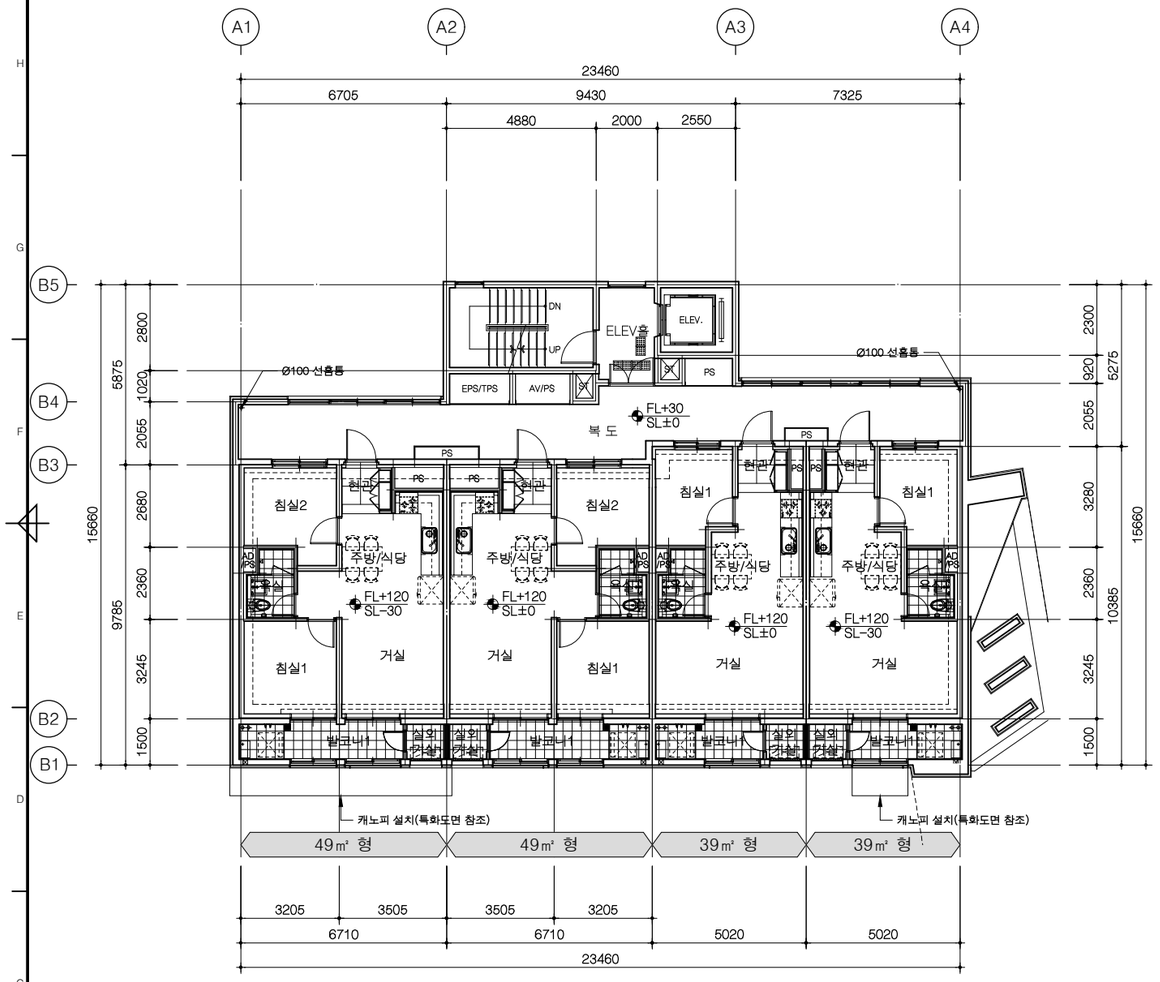

1 A 102동 2층 평면도

축척 = 1/100

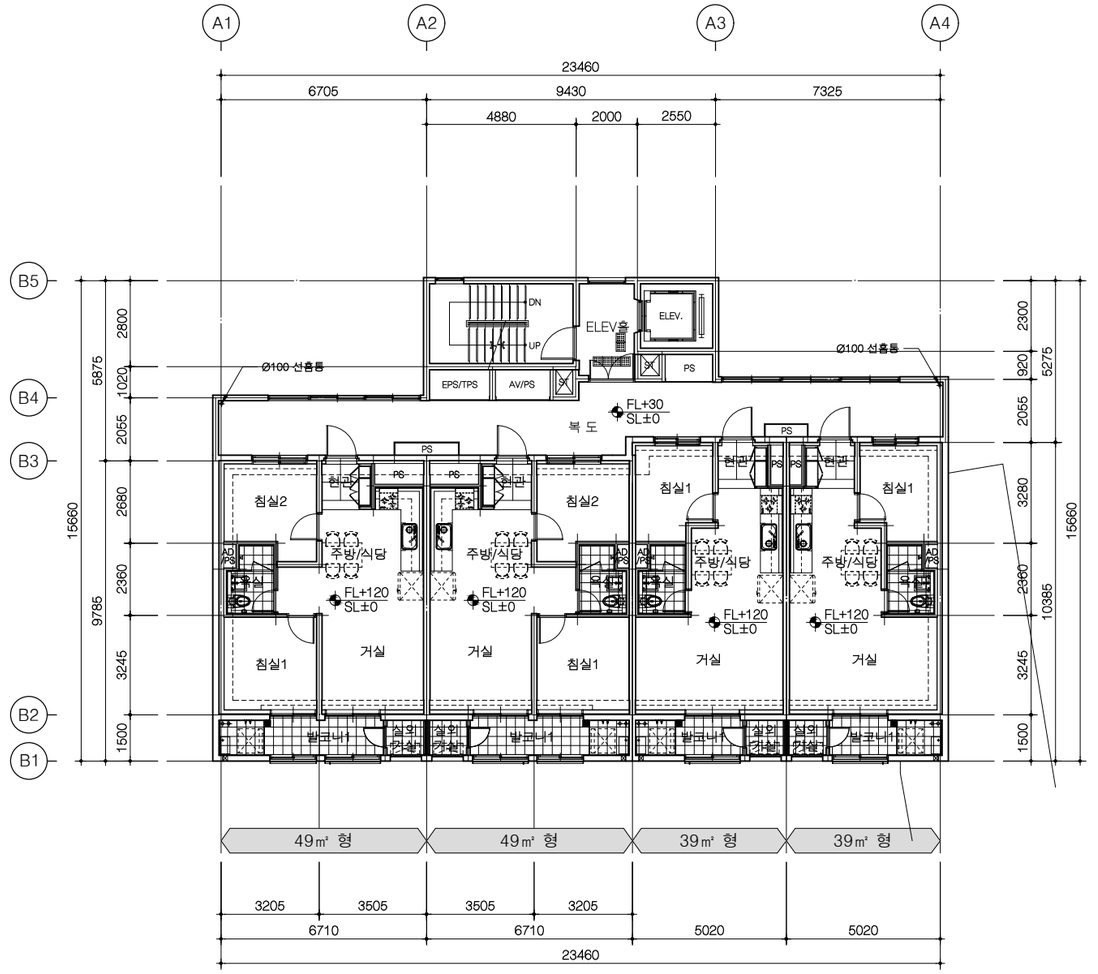

2 A 102동 3~11층 평면도

축척 = 1/100

사업번호 PROJECT NO.

사업명 PROJECT TITLE

수색4재정비촉진구역
주택재개발 정비사업

KEY PLAN

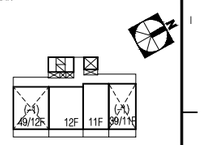

NOTE

1. 본 도면은 발코니 확장전를 기준으로 작성됨.
2. 지붕층 난간의 형태와 설치 위치는 안전성과 입면디자인을 고려하여 변경 가능함.
3. 지붕의 재료, 형태, 구조는 실시공 시 변경 될 수 있음.
4. 지붕 및 옥탑 구조물의 형태와 구조는 실시공 시 변경될 수 있음.
5. 옥상 줄눈의 간격은 실시공 시 변경될 수 있음.
6. 옥상 줄눈 틈에 실란트 시공되지 않음
7. 우편물 수취함 설치 위치는 변경될 수 있음

2층 바닥LEVEL
2SL±0 = 2FL±0 = EL+31.80

수정번호 REV. NO.	일 자 DATE	내 용 DESCRIPTION	승 인 CHKD
△			
△			
△			
△			

설계 DESIGNED BY

검토 CHECKED BY
최 진 규

심사 SUMMITED BY
정 호 혁

승인 APPROVED BY
이 승 준

일자 DATE
2019.08

도면명 DRAWING TITLE
102동
2층 및 3~11층 평면도

축 척 SCALE
A1: 1/100
A3: 1/200

도면번호 DRAWING NO.
A-313

일련번호 SHEET NO. △ REV. NO.

HAUD
(주)하우드엔지니어링
종합건축사사무소
Architects, Planners & Engineers
TEL. 02 2149 4400, SEOUL, KOREA

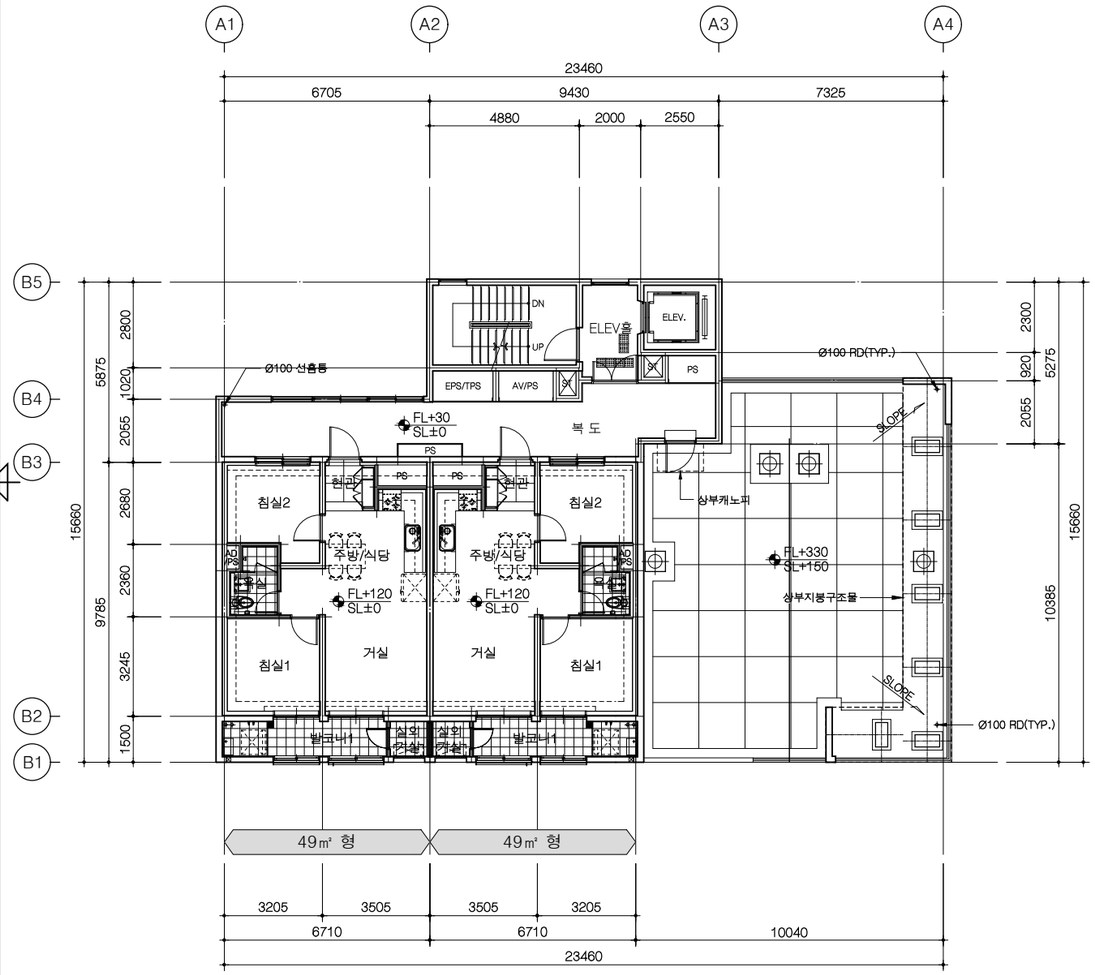

1 A 102동 12층 평면도

축척 = 1/100

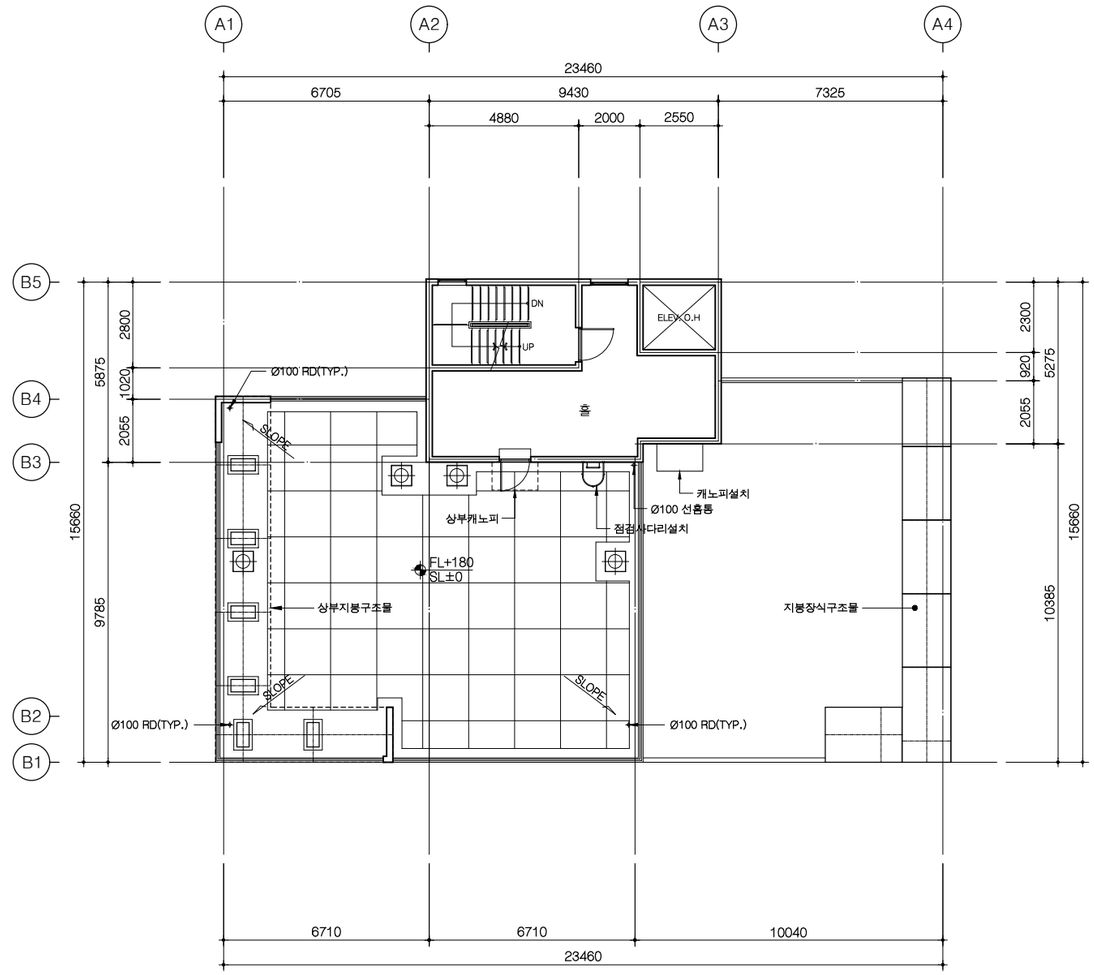

2 A 102동 지붕 평면도

축척 = 1/100

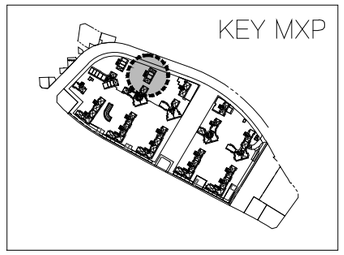

사업번호 PROJECT NO.

사업명 PROJECT TITLE

수색4재정비촉진구역
주택재개발 정비사업

KEY PLAN

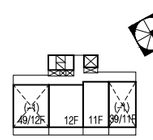

NOTE

1. 본 도면은 발코니 확장전를 기준으로 작성됨.
2. 지붕층 난간의 형태와 설치 위치는 안전성과 입면디자인을 고려하여 변경 가능함.
3. 지붕의 재료, 형태, 구조는 실시공 시 변경 될 수 있음.
4. 지붕 및 옥탑 구조물의 형태와 구조는 실시공 시 변경될 수 있음.
5. 옥상 출눈의 간격은 실시공 시 변경될 수 있음.
6. 옥상 출눈 틈에 실란트 시공되지 않음
7. 우편물 수취함 설치 위치는 변경될 수 있음

수정번호 REV. NO.	일 자 DATE	내 용 DESCRIPTION	승 인 CHKD
△			
△			
△			
△			

설계 DESIGNED BY

검토 CHECKED BY
최 진 규

심사 SUMMITED BY
정 호 혁

승인 APPROVED BY
이 승 준

일자 DATE
2019.08

도면명 DRAWING TITLE
102동
12층 및 지붕 평면도

축 척 SCALE
A1: 1/100
A3: 1/200

도면번호 DRAWING NO.
A-314

일련번호 SHEET NO.

△ REV. NO.

HAUD
(주)하우드엔지니어링
종합건축사사무소
Architects, Planners & Engineers
TEL. 02 3143 4400, SEOUL, KOREA

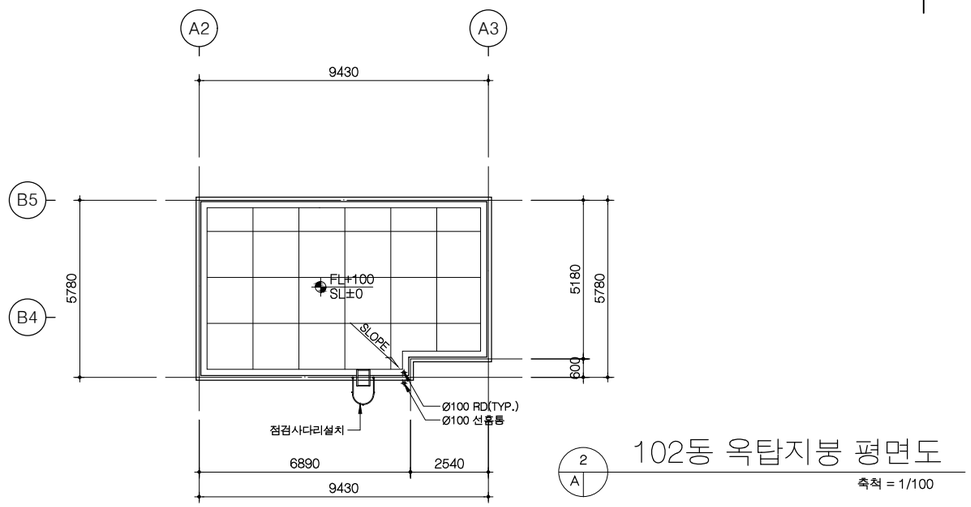

2 A 102동 옥탑지붕 평면도

축척 = 1/100

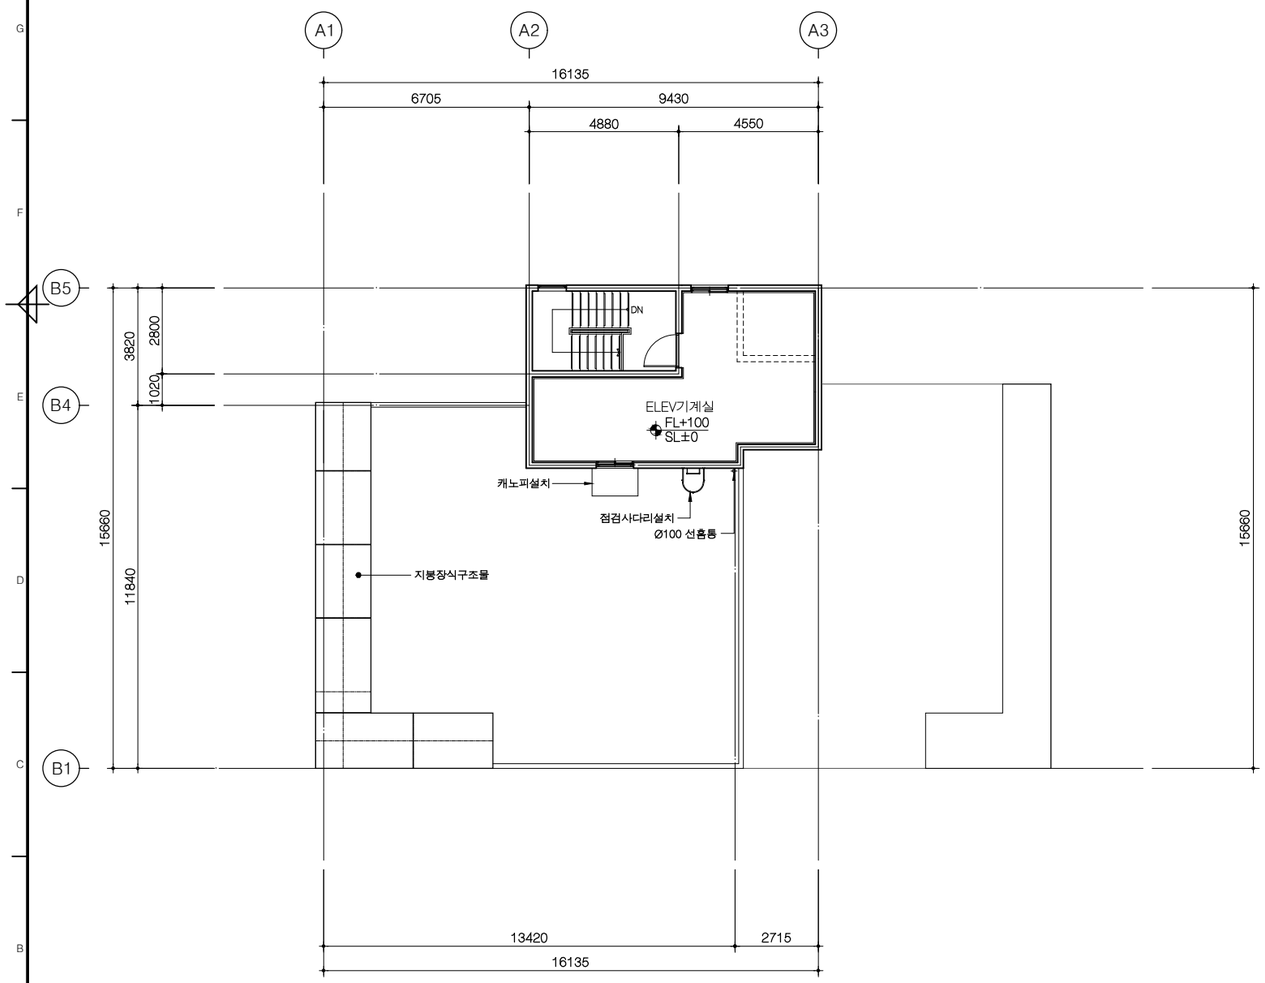

1 A 102동 옥탑층 평면도

축척 = 1/100

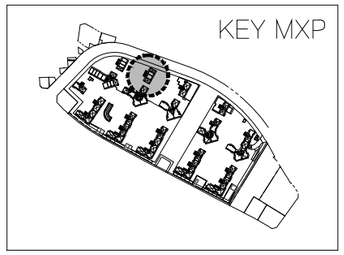

사업번호 PROJECT NO.

사업명 PROJECT TITLE

수색4재정비촉진구역
주택재개발 정비사업

KEY PLAN

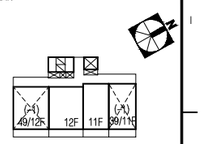

NOTE

1. 지붕바닥
   ① EXP. JOINT: 3000 X 3000
2. 본 평면도는 발코니확장전을 기준으로 작성됨
3. 재료마감은 실내,외 재료마감표 참조
4. 지붕 난간형태/설치위치는 안전성과 입면을 고려하여 실시공시 변경될 수 있음
5. 지붕재료 및 형태,구조는 실시공시 변경될수 있음
6. 지붕(옥탑지붕)의 배수드레인,창소용고리, 베기탑,점검사다리(점검구) 등의 설치위치/개소는 실시공시 변경될 수 있음
7. 옥상 상부구조물은 PC구조물 임.
8. 정화조 배기는 기계도서 참조

수정번호 REV. NO.	일 자 DATE	내 용 DESCRIPTION	승 인 CHKD
△			
△			
△			
△			

설계 DESIGNED BY

검토 CHECKED BY
최 진 규

심사 SUMMITED BY
정 호 혁

승인 APPROVED BY
이 승 준

일자 DATE
2019.08

도면명 DRAWING TITLE

102동
옥탑층 및 옥탑지붕 평면도

축 척 SCALE
A1: 1/100
A3: 1/200

도면번호 DRAWING NO.
A-315

일련번호 SHEET NO.

REV. NO. △

HAUD
㈜하우드엔지니어링
종합건축사사무소
Architects, Planners & Engineers
TEL. 02 2143 4400, SEOUL, KOREA

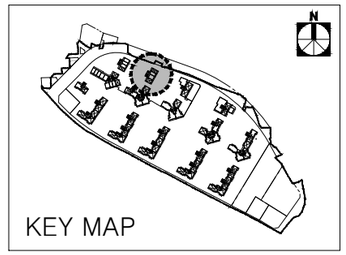

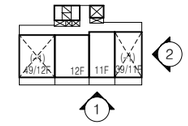

NOTE

1. 1층 바닥 LEVEL
   1SL±0 = 1FL±0 = GL±0 = EL+28.60
2. 지붕 난간의 형태 및 설치위치는 안전성과 입면디자인을 고려하여 변경가능함.
3. 지붕의 재료, 형태, 구조는 실시공시 변경될 수 있음.
4. 지붕 및 옥탑구조물의 형태와 구조는 실시공시 변경될 수 있음.
5. 외벽 및 측벽 문양은 실시공시 변경될 수 있음
6. 입면의 줄눈 및 마감선은 실시공시 변경될 수 있음.
7. 저층부 석재마감 및 입면 마감 색상, 재료에 대한 모든 기준은 특화도면을 우선 적용함.

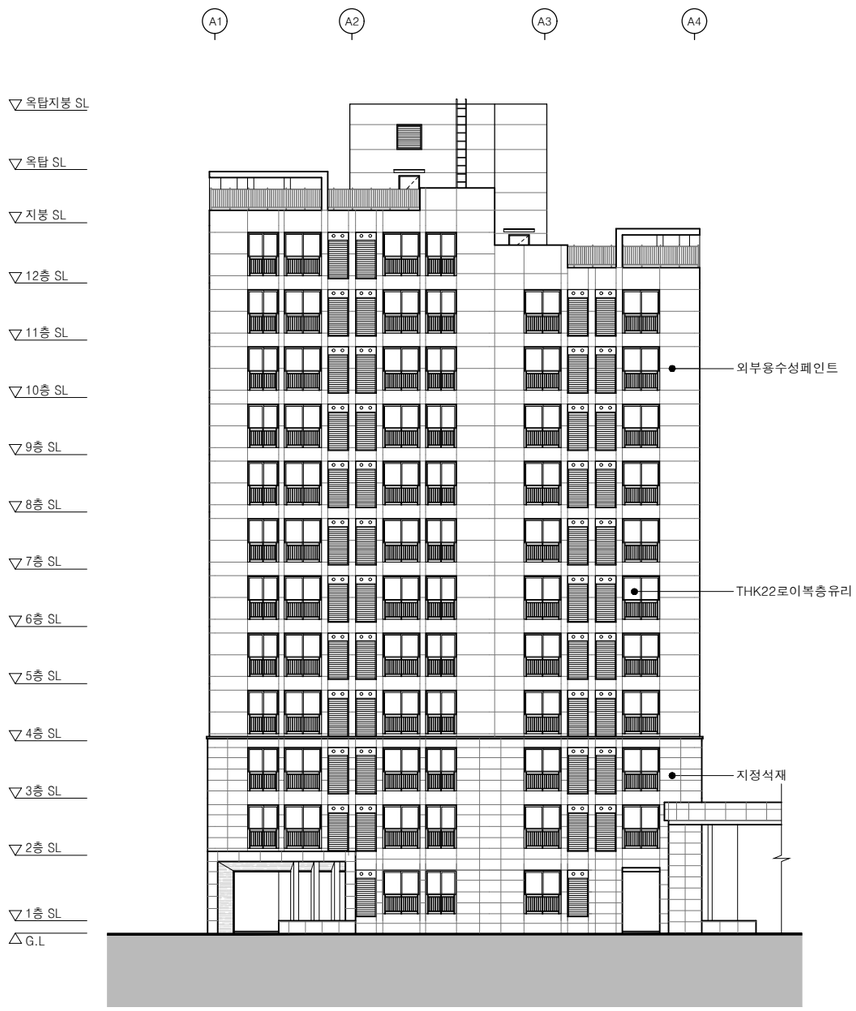

1 A 102동 정면도

축척 = 1/150

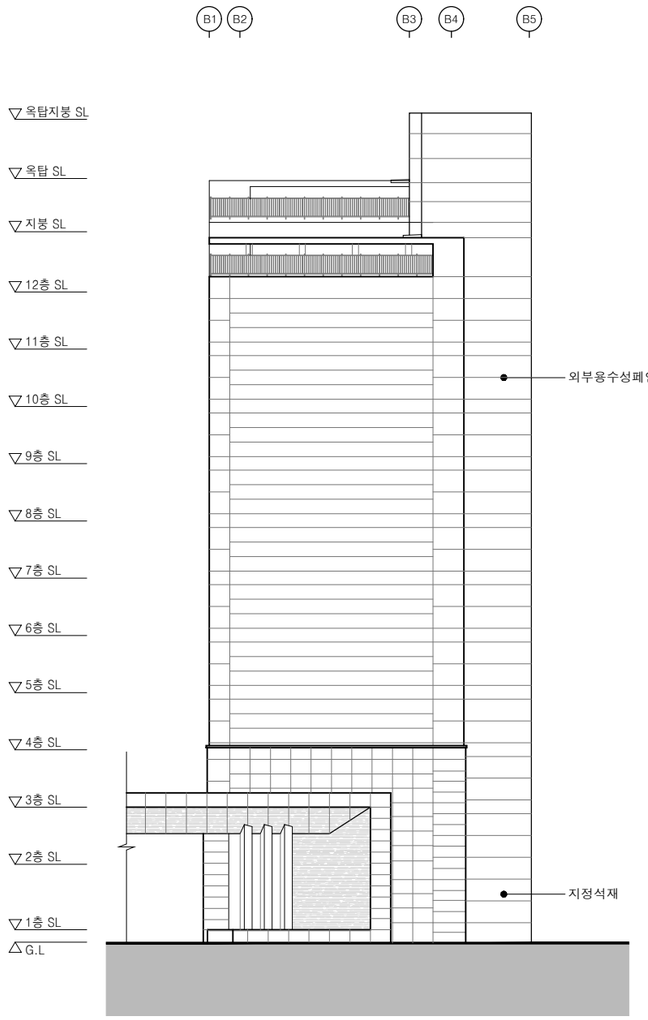

2 A 102동 우측면도

축척 = 1/150

수정번호 REV. NO.	일 자 DATE	내 용 DESCRIPTION	승 인 CHKD
△			
△			
△			
△			

사업번호 PROJECT NO.

사업명 PROJECT TITLE

수색4재정비촉진구역
주택재개발 정비사업

설계 DESIGNED BY

검토 CHECKED BY
최 진 규

심사 SUMMITED BY
정 호 혁

승인 APPROVED BY
이 승 준

일자 DATE
2019.08

도면명 DRAWING TITLE
102동 정면도,우측면도

축 척 SCALE
A1: 1/150
A3: 1/300

도면번호 DRAWING NO.
A-316

일련번호 SHEET NO.

△ REV. NO.

HAUD
㈜하우드엔지니어링
종합건축사사무소
Architects, Planners & Engineers
TEL. 02-2149 4400, SEOUL, KOREA

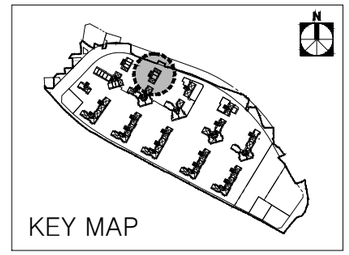

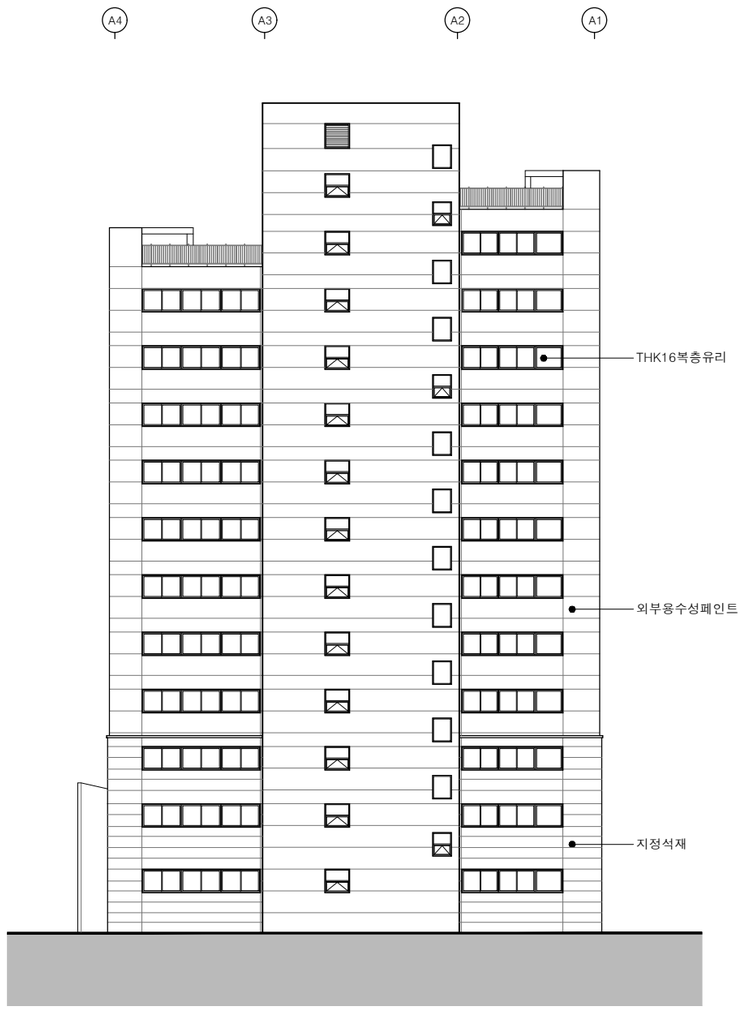

1 A 102동 배면도

축척 = 1/150

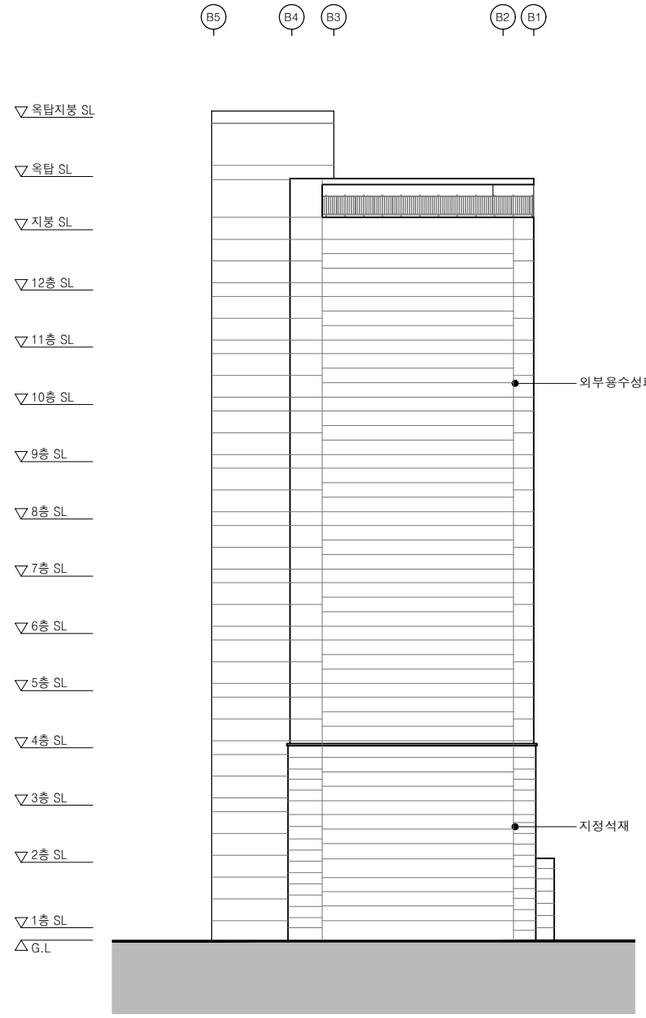

2 A 102동 좌측면도

축척 = 1/150

사업번호 PROJECT NO.

사업명 PROJECT TITLE

수색4재정비촉진구역
주택재개발 정비사업

KEY PLAN

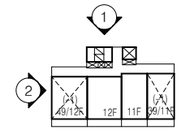

NOTE

1. 1층 바닥 LEVEL
   1SL±0 = 1FL±0 = GL±0 = EL+28.60
2. 지붕 난간의 형태 및 설치위치는 안전성과 입면디자인을 고려하여 변경가능함.
3. 지붕의 재료, 형태, 구조는 실시공시 변경될 수 있음.
4. 지붕 및 옥탑구조물의 형태와 구조는 실시공시 변경될 수 있음.
5. 외벽 및 측벽 문양은 실시공시 변경될 수 있음
6. 입면의 줄눈 및 마감선은 실시공시 변경될 수 있음.
7. 저층부 석재마감 및 입면 마감 색상, 재료에 대한 모든 기준은 특화도면을 우선 적용함.

수정번호 REV. NO.	일 자 DATE	내 용 DESCRIPTION	승 인 CHKD
△			
△			
△			
△			

설계 DESIGNED BY

검토 CHECKED BY
최 진 규

심사 SUMMITED BY
정 호 혁

승인 APPROVED BY
이 승 준

일자 DATE
2019.08

도면명 DRAWING TITLE
102동 배면도,좌측면도

축 척 SCALE
A1: 1/150
A3: 1/300

도면번호 DRAWING NO.
A-317

일련번호 SHEET NO.

△ REV. NO.

HAUD
㈜하우드엔지니어링
종합건축사사무소
Architects, Planners & Engineers
TEL. 02 2140 4400, SEOUL, KOREA

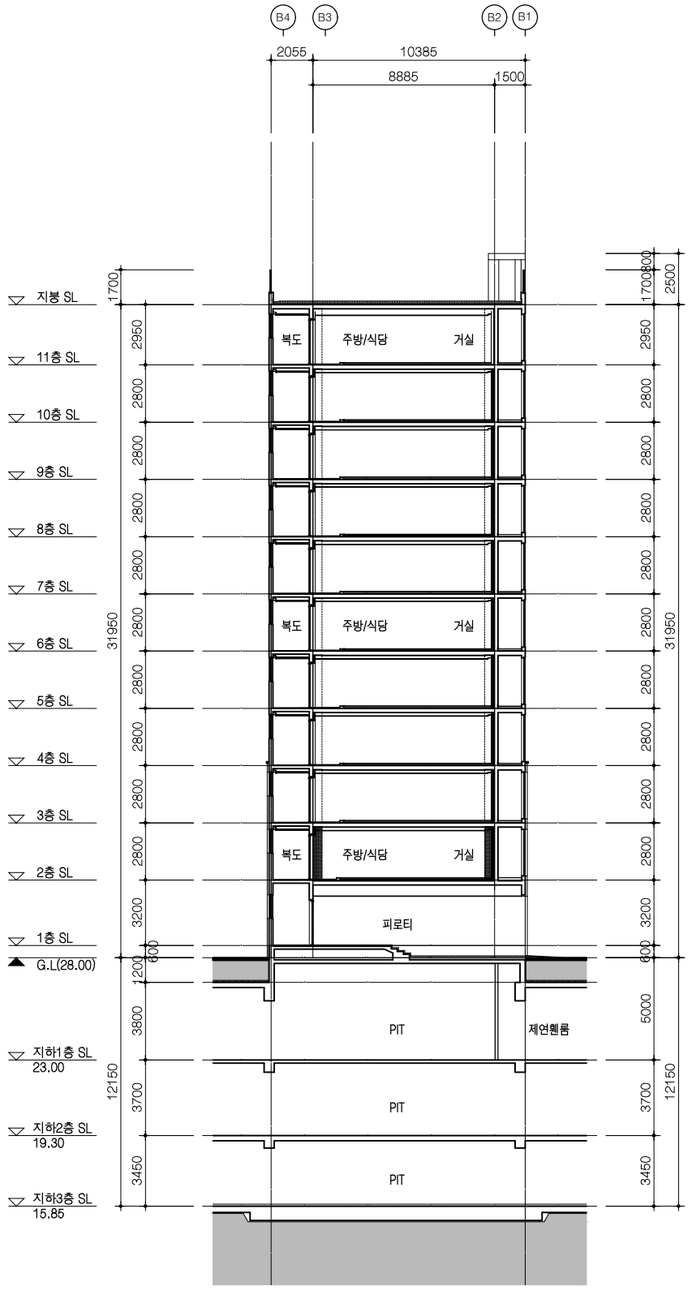

1 A 102동 종단면도

축척 = 1/150

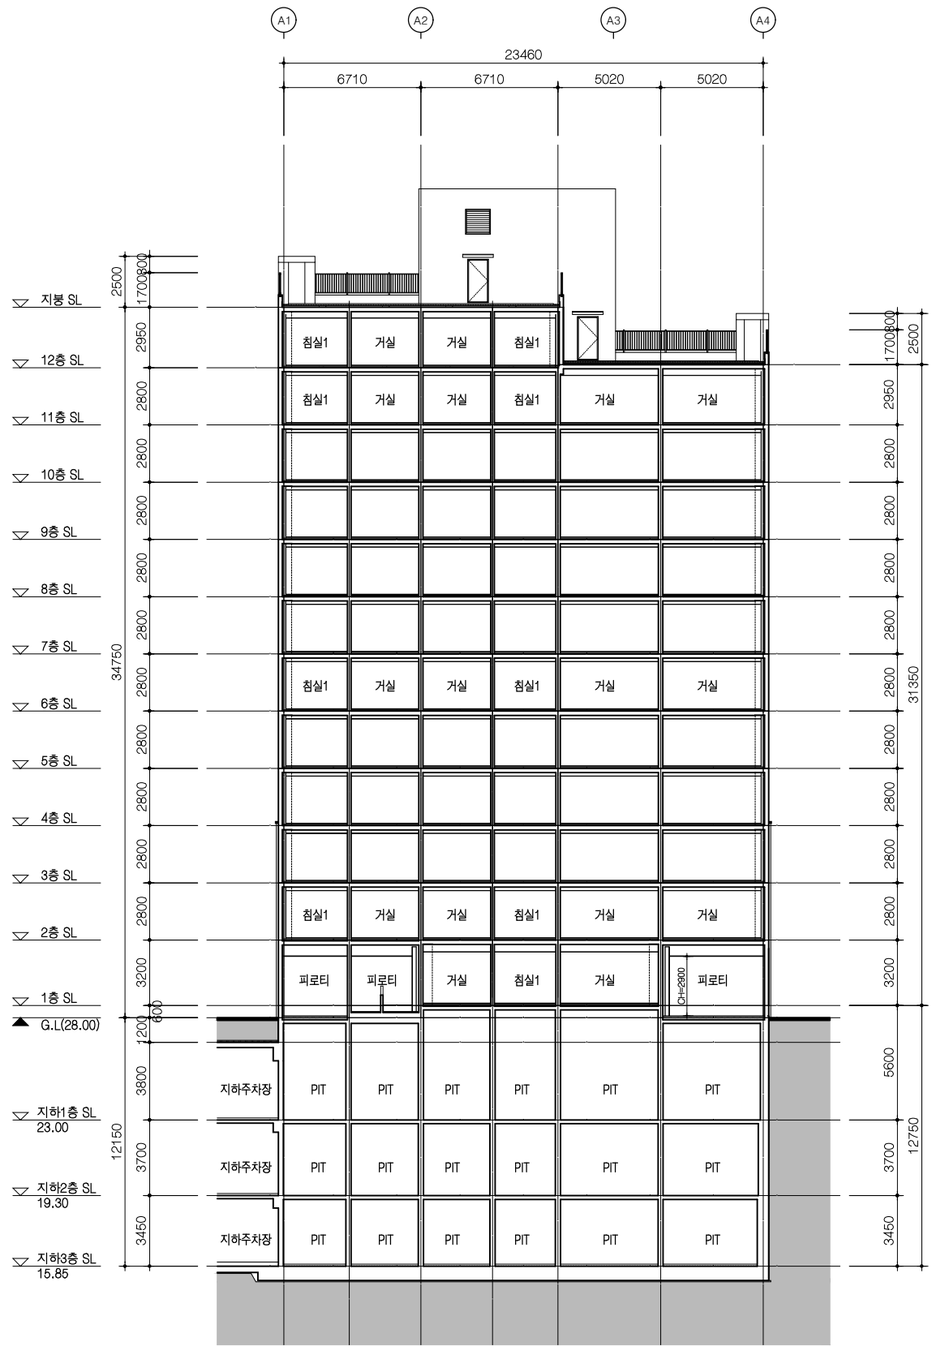

2 A 102동 횡단면도

축척 = 1/150

사업번호 PROJECT NO.

사업명 PROJECT TITLE

수색4재정비촉진구역
주택재개발 정비사업

KEY PLAN

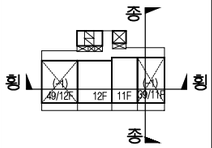

NOTE

수정번호 REV. NO.	일 자 DATE	내 용 DESCRIPTION	승 인 CHKD
△			
△			
△			
△			

설계 DESIGNED BY

검토 CHECKED BY
최 진 규

심사 SUMMITED BY
정 호 혁

승인 APPROVED BY
이 승 준

일자 DATE
2019.08

도면명 DRAWING TITLE
102동 종,횡단면도

축 척 SCALE
A1: 1/150
A3: 1/300

도면번호 DRAWING NO.
A-318

일련번호 SHEET NO. △ REV. NO.

HAUD
(주)하우드엔지니어링
종합건축사사무소
Architects, Planners & Engineers
TEL. 02 2140 4400, SEOUL, KOREA

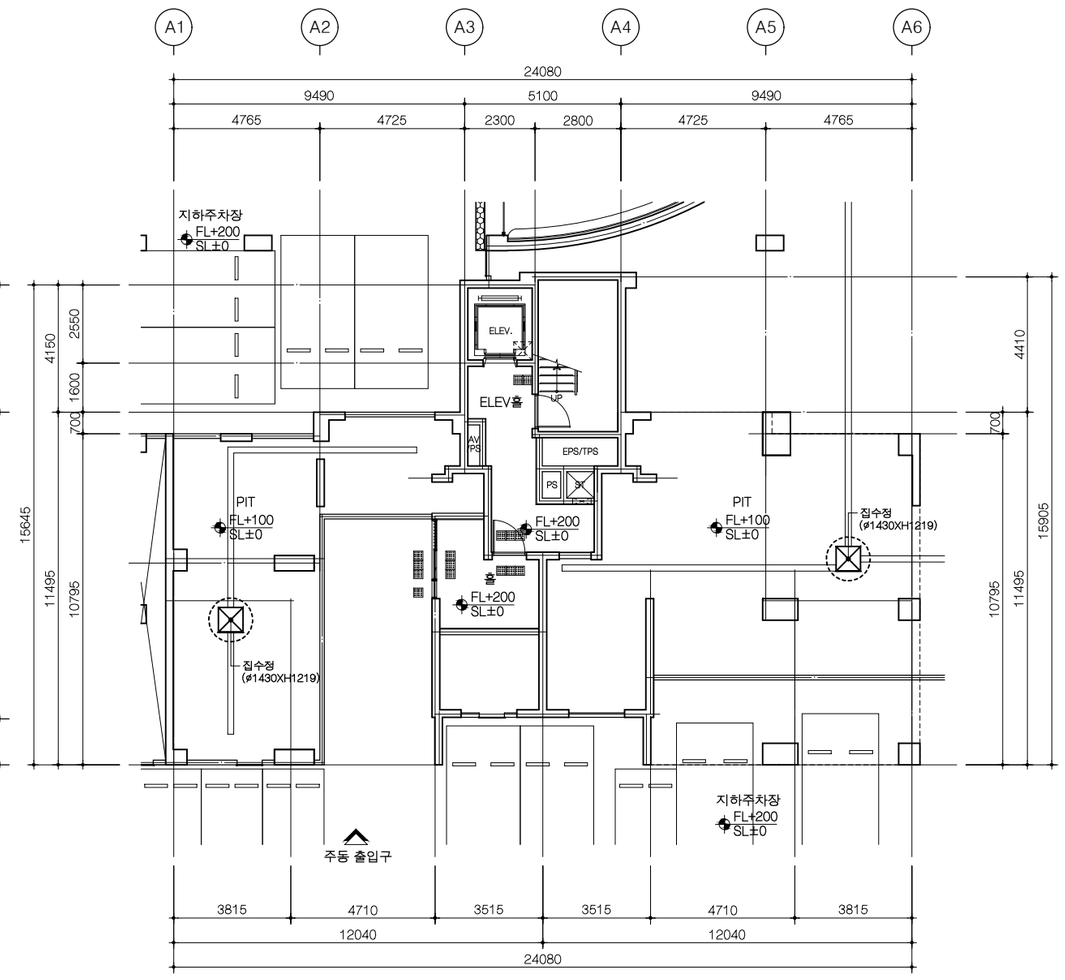

1 A 103동 지하3층 평면도

축척 = 1/100

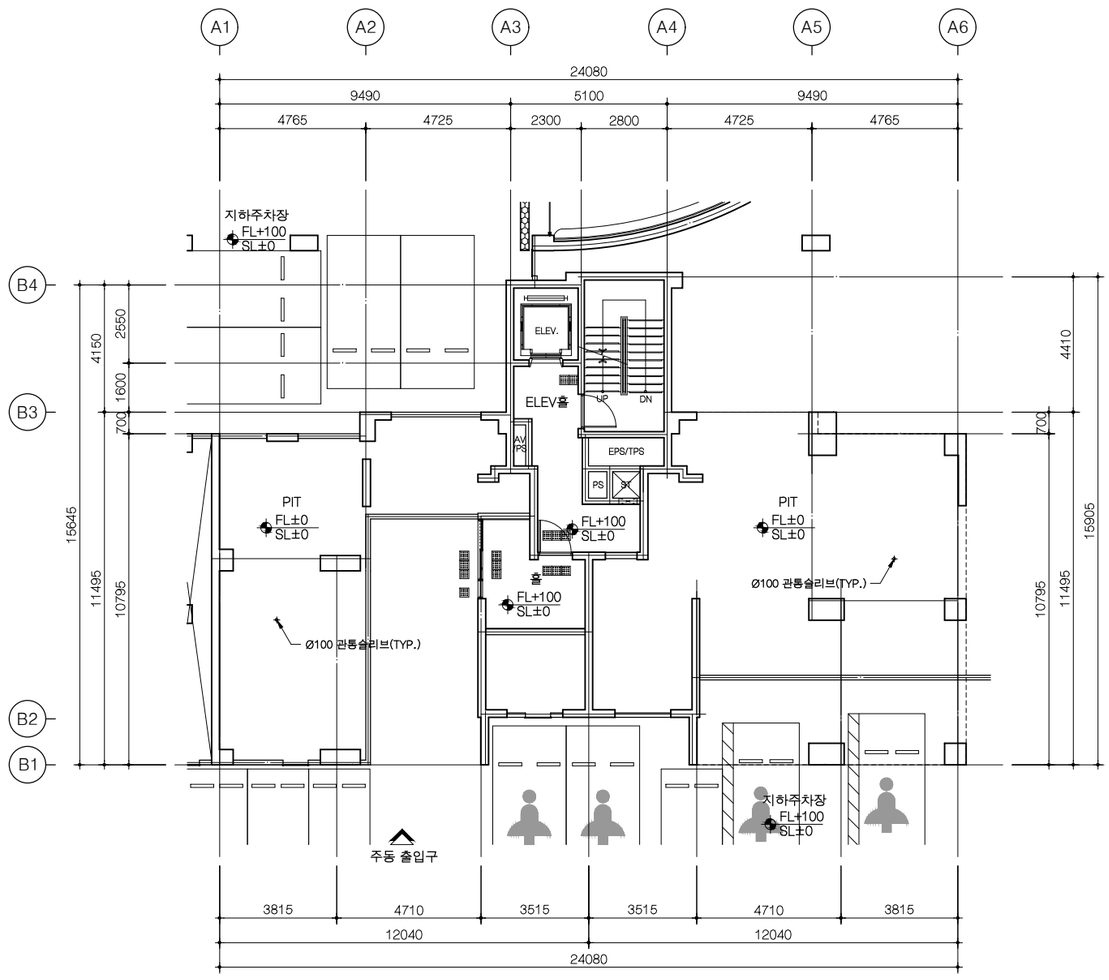

2 A 103동 지하2층 평면도

축척 = 1/100

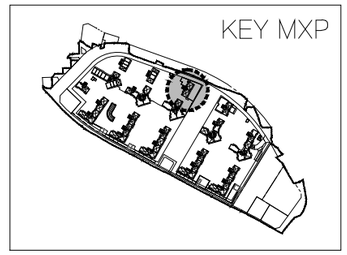

사업번호 PROJECT NO.

사업명 PROJECT TITLE

수색4재정비촉진구역
주택재개발 정비사업

KEY PLAN

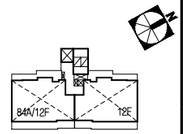

NOTE

1. 지하층 무근 콘크리트는 실시공시 THK80~120 범위로 변동이 있을수 있음.(SLOPE)
2. ELEV홀에 면한부위는 1.0B 조적쌓기임.
3. 지하주차장의 블록쌓기 기준은 높이가 3.6m이하인 경우 4인치 보강블록쌓기가 기준임 (단, 5.4m이하는 6인치쌓기, 5.4m초과는 8인치쌓기가 기준임)
4. ELEV.PIT 집수정은 (600X600X600)임.
5. 주차장 내의 창호는 주차장 창호도 참조.
6. 주차장 집수정 및 영구배수 집수정의 크기 및 위치는 지하주차장 평면도를 참조 할 것.
   ⊠: 주차장 집수정(ø1430XH1219)
   ⊠: 영구배수 집수정(ø1760XH1524)
   ⊗: 아파트 집수정(ø1430XH1219)

********** 지하3층 바닥LEVEL
B3SL±0 = B3FL±0 = EL+15.85
**** 지하2층 바닥LEVEL
B2SL±0 = B2FL±0 = EL+19.30

수정번호 REV. NO.	일 자 DATE	내 용 DESCRIPTION	승 인 CHKD
△			
△			
△			
△			

설계 DESIGNED BY

검토 CHECKED BY
최 진 규

심사 SUMMITED BY
정 호 혁

승인 APPROVED BY
이 승 준

일자 DATE
2019.08

도면명 DRAWING TITLE
103동
지하3층 및 지하2층 평면도

축 척 SCALE
A1: 1/100
A3: 1/200

도면번호 DRAWING NO.
A-321

일련번호 SHEET NO.

REV. NO.

HAUD
(주)하우드엔지니어링
종합건축사사무소
Architects, Planners & Engineers
TEL. 02 2140 4400, SEOUL, KOREA

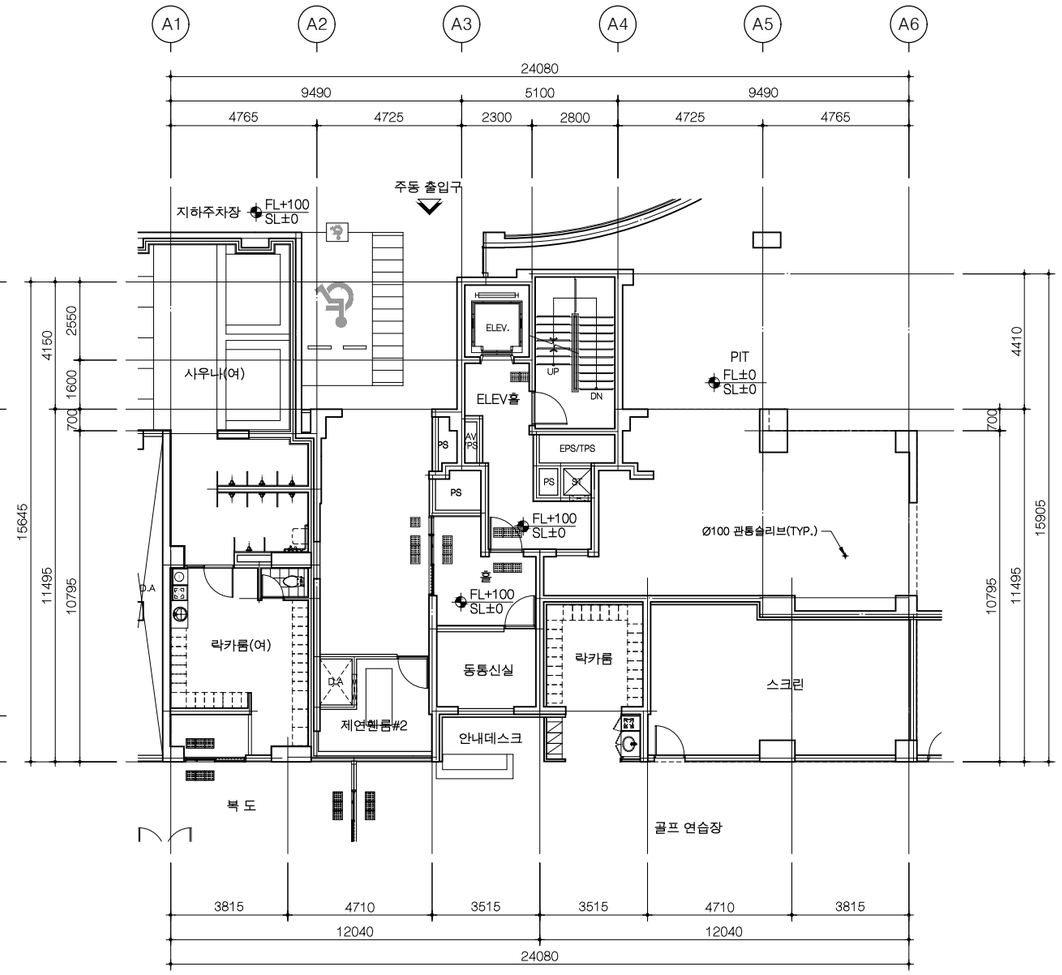

1 A 103동 지하1층 평면도

축척 = 1/100

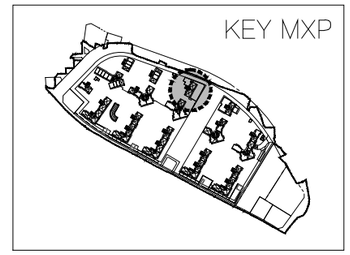

사업번호 PROJECT NO.

사업명 PROJECT TITLE

수색4재정비촉진구역
주택재개발 정비사업

KEY PLAN

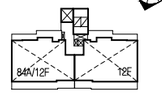

NOTE

1. 지하주차장의 ELEV홀에 면한부위는 1.0B 조적쌓기임.
2. 지하주차장의 블록쌓기 기준은 높이가 3.6m이하인 경우 4인치 보강블록쌓기가 기준임 (단, 5.4m이하는 6인치쌓기, 5.4m초과는 8인치쌓기가 기준임)
3. 주차장 내의 창호는 주차장 창호도 참조.

* 지하1층 바닥LEVEL
D1SL±0 = D1FL±0 = EL+23.00

수정번호 REV. NO.	일 자 DATE	내 용 DESCRIPTION	승 인 CHKD
△			
△			
△			
△			

설계 DESIGNED BY

검토 CHECKED BY
최 진 규

심사 SUMMITED BY
정 호 혁

승인 APPROVED BY
이 승 준

일자 DATE
2019.08

도면명 DRAWING TITLE
103동
지하1층 평면도

축 척 SCALE
A1: 1/100
A3: 1/200

도면번호 DRAWING NO.
A-322

일련번호 SHEET NO.

REV. NO.

HAUD
㈜하우드엔지니어링
종합건축사사무소
Architects, Planners & Engineers
TEL. 02 2140 4400, SEOUL, KOREA

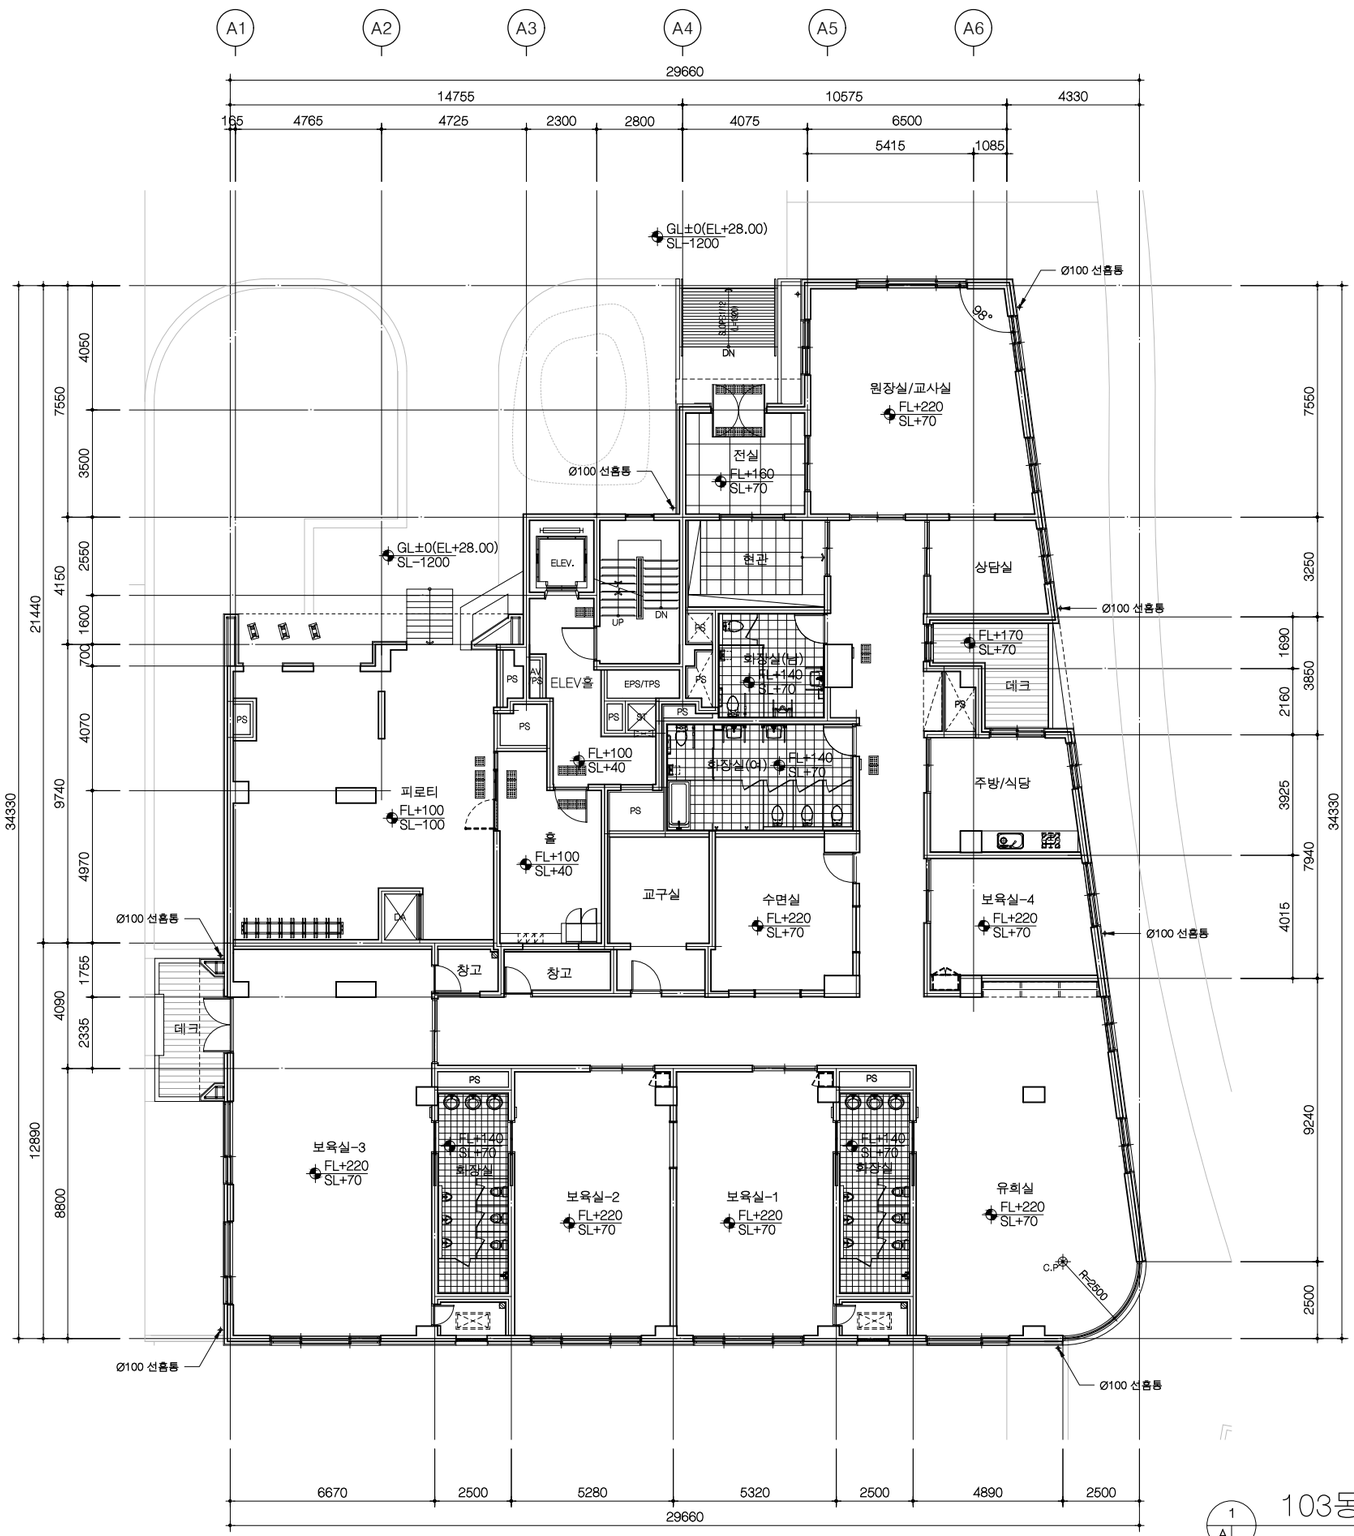

103동 1층 평면도

축척 = 1/100

KEY MXP

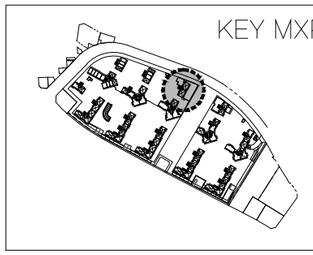

사업번호 PROJECT NO.

사업명 PROJECT TITLE

수색4재정비촉진구역
주택재개발 정비사업

KEY PLAN

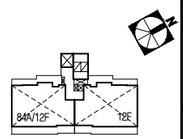

NOTE

1. 우편물 수취함 설치 위치는 변경될 수 있음

• 1층 바닥LEVEL
1SL±0 = 1FL±0 = GL±0 = EL+28.00

수정번호 REV. NO.	일 자 DATE	내 용 DESCRIPTION	승 인 CHKD
△			
△			
△			
△			

설계 DESIGNED BY

검토 CHECKED BY
최 진 규

심사 SUMMITED BY
정 호 혁

승인 APPROVED BY
이 승 준

일자 DATE
2019.08

도면명 DRAWING TITLE
103동
1층 평면도

축 척 SCALE
A1: 1/100
A3: 1/200

도면번호 DRAWING NO.
A-323

일련번호 SHEET NO.

△ REV. NO.

HAUD
㈜하우드엔지니어링
종합건축사사무소
Architects, Planners & Engineers
TEL. 02 2140 4466, SEOUL, KOREA

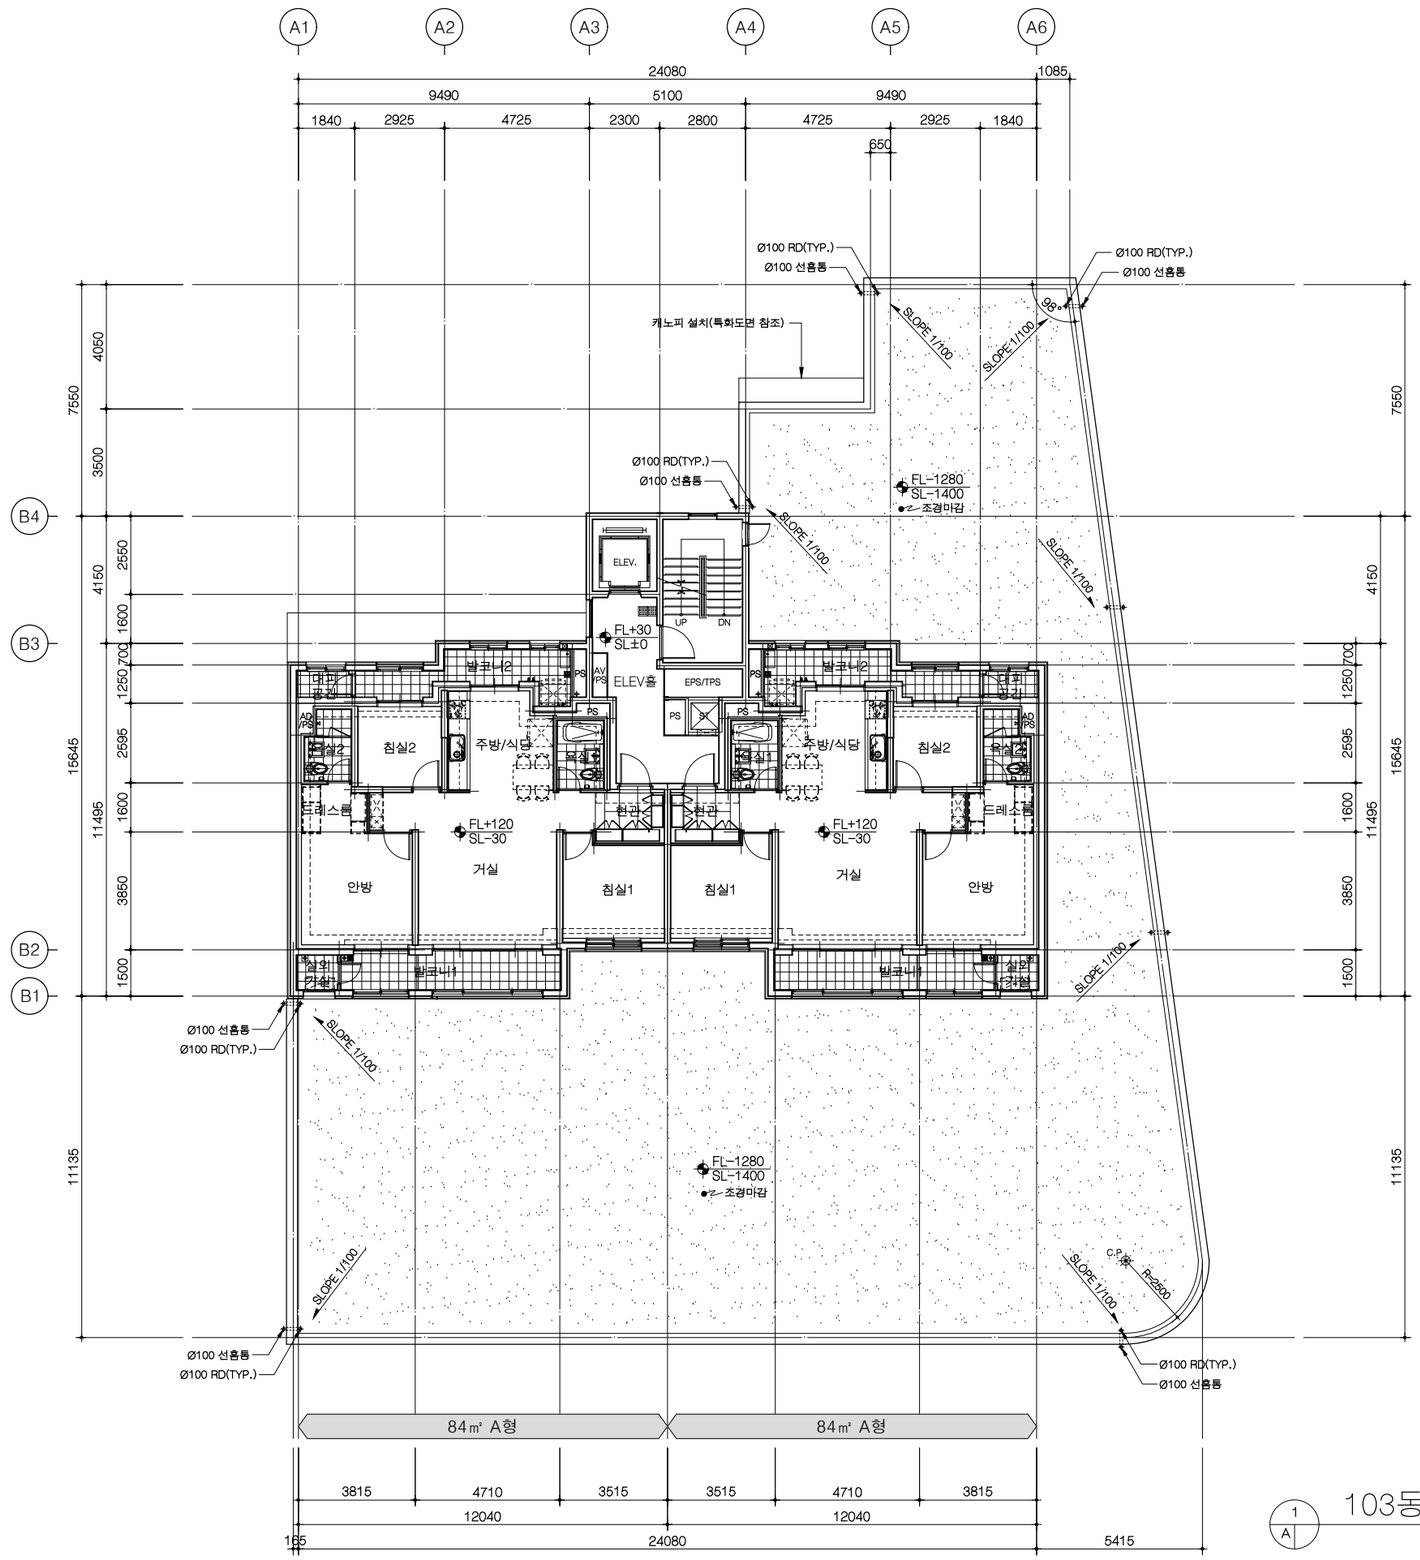

103동 2층 평면도

1/A

축척 = 1/100

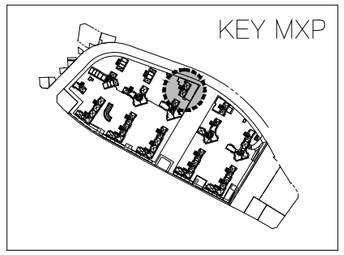

사업번호 PROJECT NO.

사업명 PROJECT TITLE

수색4재정비촉진구역
주택재개발 정비사업

KEY PLAN

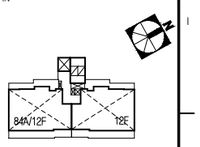

NOTE

1. 본 도면은 발코니 확장전를 기준으로 작성됨.
2. 지붕층 난간의 형태와 설치 위치는 안전성과 입면디자인을 고려하여 변경 가능함.
3. 지붕의 재료, 형태, 구조는 실시공 시 변경 될 수 있음.
4. 지붕 및 옥탑 구조물의 형태와 구조는 실시공 시 변경될 수 있음.
5. 옥상 출눈의 간격은 실시공 시 변경될 수 있음.
6. 옥상 출눈 틈에 실란트 시공되지 않음
7. 우편물 수취함 설치 위치는 변경될 수 있음

2층 바닥LEVEL
2SL±0 = 2FL±0 = EL+33.10

수정번호 REV. NO.	일 자 DATE	내 용 DESCRIPTION	승 인 CHKD
△			
△			
△			
△			

설계 DESIGNED BY

검토 CHECKED BY
최 진 규

심사 SUMMITED BY
정 호 혁

승인 APPROVED BY
이 승 준

일자 DATE
2019.08

도면명 DRAWING TITLE
103동
2층 평면도

축 척 SCALE
A1: 1/100
A3: 1/200

도면번호 DRAWING NO.
A-324

일련번호 SHEET NO.

REV. NO.

HAUD
㈜하우드엔지니어링
종합건축사사무소
Architects, Planners & Engineers
TEL. 02 2149 4400, SEOUL, KOREA

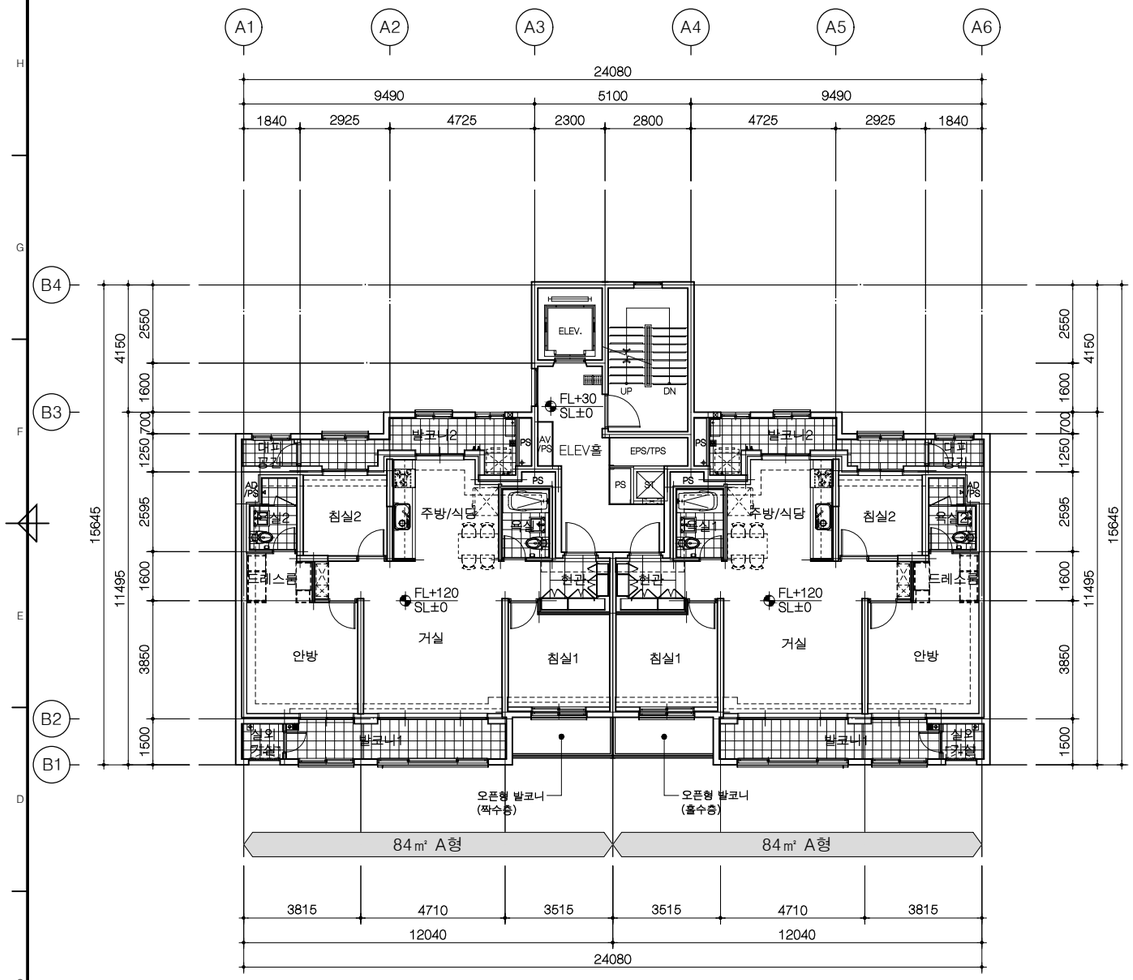

1 A 103동 3~12층 평면도

축척 = 1/100

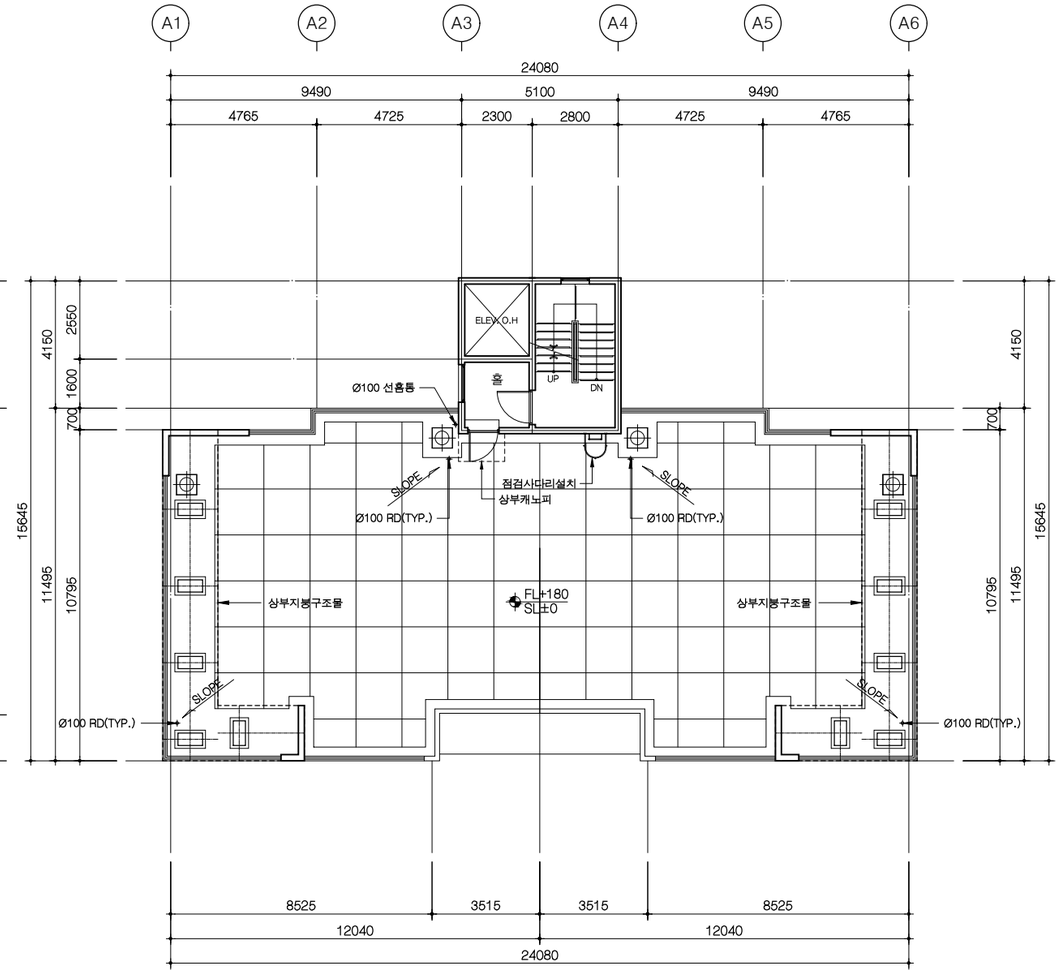

2 A 103동 지붕 평면도

축척 = 1/100

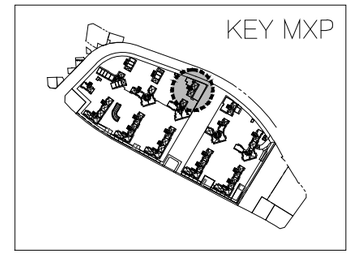

사업번호 PROJECT NO.

사업명 PROJECT TITLE

수색4재정비촉진구역
주택재개발 정비사업

KEY PLAN

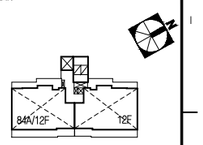

NOTE

1. 본 도면은 발코니 확장전를 기준으로 작성됨.
2. 지붕층 난간의 형태와 설치 위치는 안전성과 입면디자인을 고려하여 변경 가능함.
3. 지붕의 재료, 형태, 구조는 실시공 시 변경 될 수 있음.
4. 지붕 및 옥탑 구조물의 형태와 구조는 실시공 시 변경될 수 있음.
5. 옥상 출눈의 간격은 실시공 시 변경될 수 있음.
6. 옥상 출눈 틈에 실란트 시공되지 않음
7. 우편물 수취함 설치 위치는 변경될 수 있음

수정번호 REV. NO.	일 자 DATE	내 용 DESCRIPTION	승 인 CHKD
△			
△			
△			
△			

설계 DESIGNED BY

검토 CHECKED BY
최 진 규

심사 SUMMITED BY
정 호 혁

승인 APPROVED BY
이 승 준

일자 DATE
2019.08

도면명 DRAWING TITLE
103동
3~12층 및 지붕 평면도

축 척 SCALE
A1: 1/100
A3: 1/200

도면번호 DRAWING NO.
A-325

일련번호 SHEET NO.

△ REV. NO.

HAUD
(주)하우드엔지니어링
종합건축사사무소
Architects, Planners & Engineers
TEL. 82 2140 4400, SEOUL, KOREA

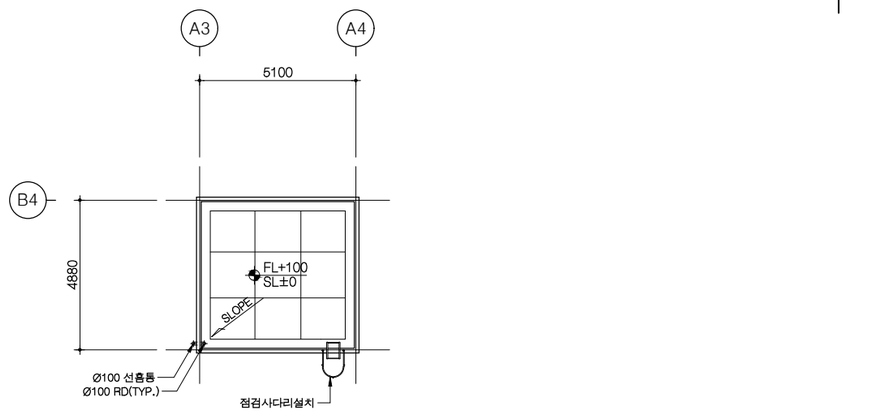

2 A 103동 옥탑지붕 평면도

축척 = 1/100

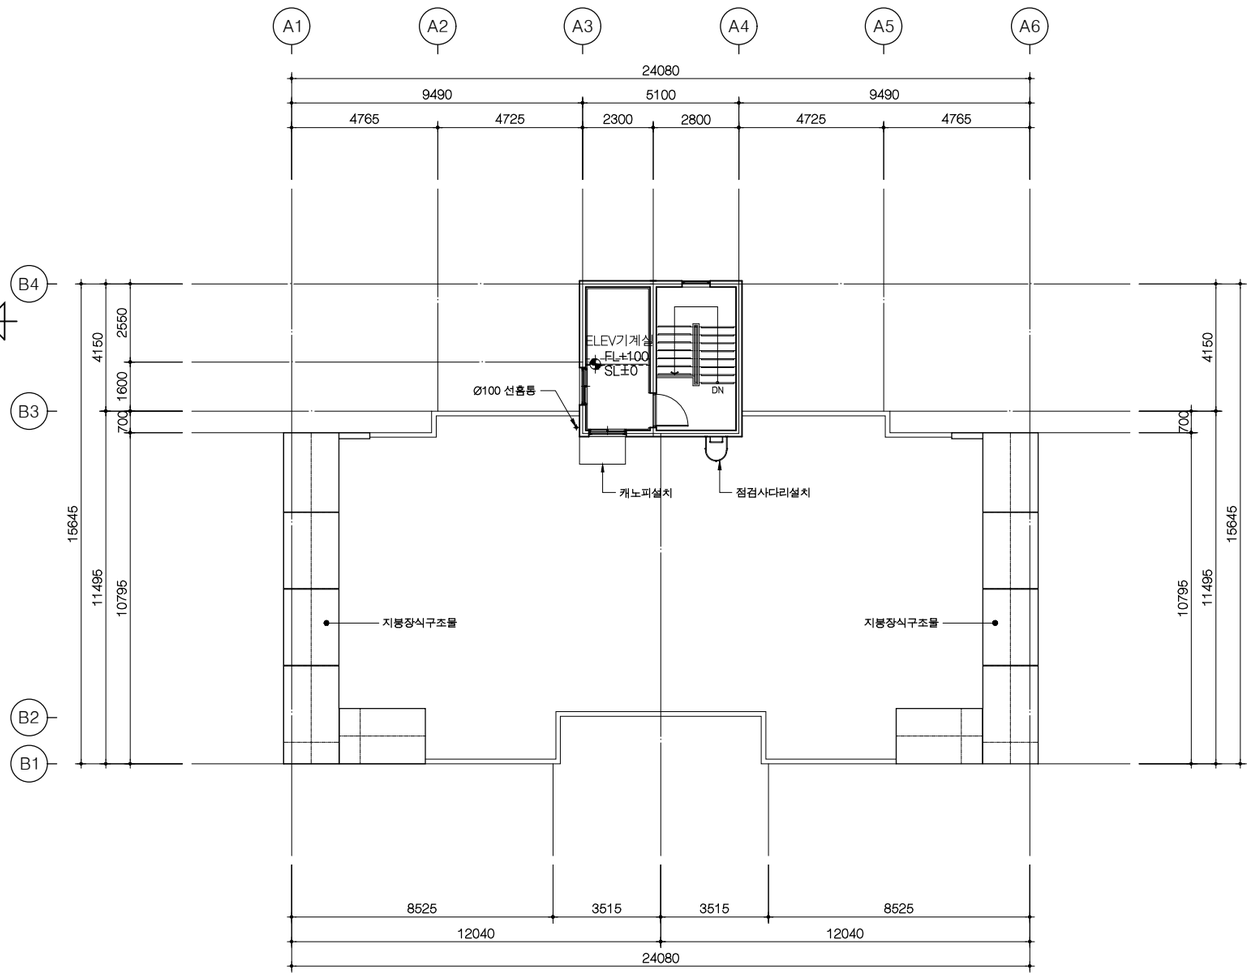

1 A 103동 옥탑층 평면도

축척 = 1/100

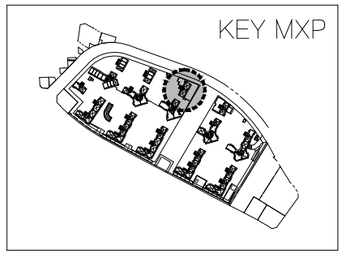

사업번호 PROJECT NO.

사업명 PROJECT TITLE

수색4재정비촉진구역
주택재개발 정비사업

KEY PLAN

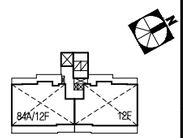

NOTE

1. 지붕바닥
   ① EXP. JOINT: 3000 X 3000
2. 본 평면도는 발코니확장전을 기준으로 작성됨
3. 재료마감은 실내,외 재료마감표 참조
4. 지붕 난간형태/설치위치는 안전성과 입면을 고려하여 실시공시 변경될 수 있음
5. 지붕재료 및 형태,구조는 실시공시 변경될수 있음
6. 지붕(옥탑지붕)의 배수드레인,청소용고리, 베기탑,점검사다리(점검구) 등의 설치위치/개소는 실시공시 변경될 수 있음
7. 옥상 상부구조물은 PC구조물 임.
8. 정화조 배기는 기계도서 참조

수정번호 REV. NO.	일 자 DATE	내 용 DESCRIPTION	승 인 CHKD
△			
△			
△			
△			

설계 DESIGNED BY

검토 CHECKED BY
최 진 규

심사 SUMMITED BY
정 호 혁

승인 APPROVED BY
이 승 준

일자 DATE
2019.08

도면명 DRAWING TITLE

103동
옥탑층 및 옥탑지붕 평면도

축 척 SCALE
A1: 1/100
A3: 1/200

도면번호 DRAWING NO.
A-326

일련번호 SHEET NO.

REV. NO.

HAUD
(주)하우드엔지니어링
종합건축사사무소
Architects, Planners & Engineers
TEL. 02 2140 4400, SEOUL, KOREA

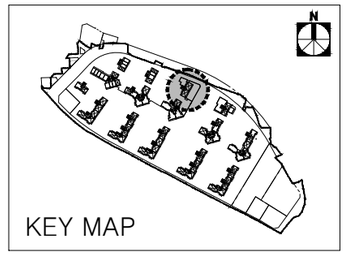

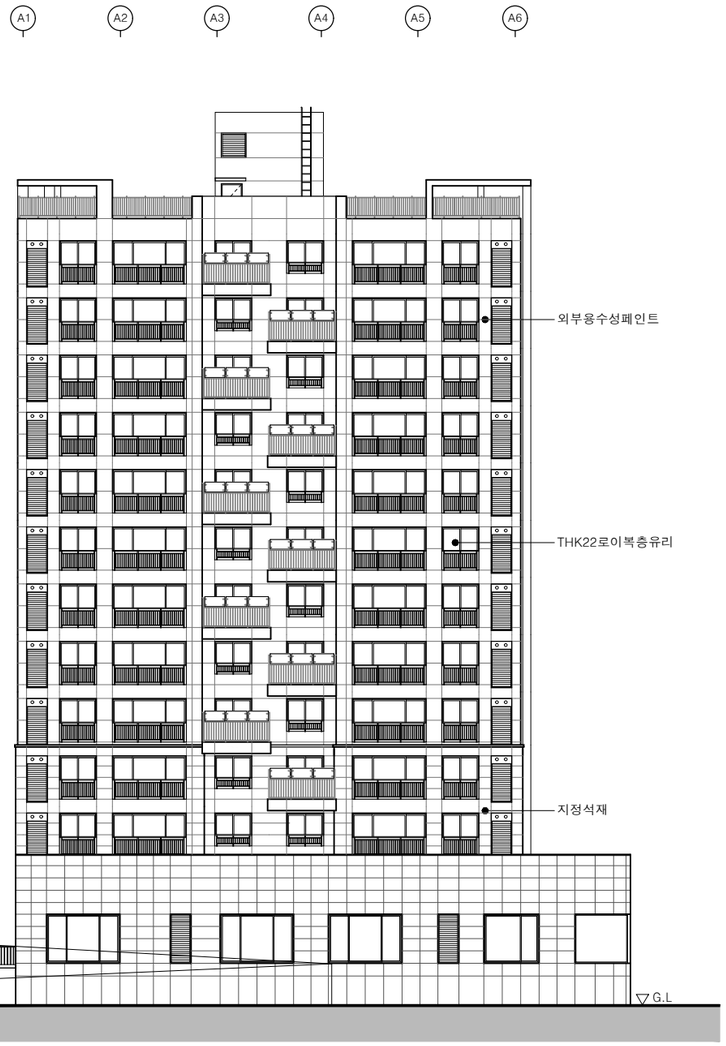

1 A 103동 정면도

축척 = 1/150

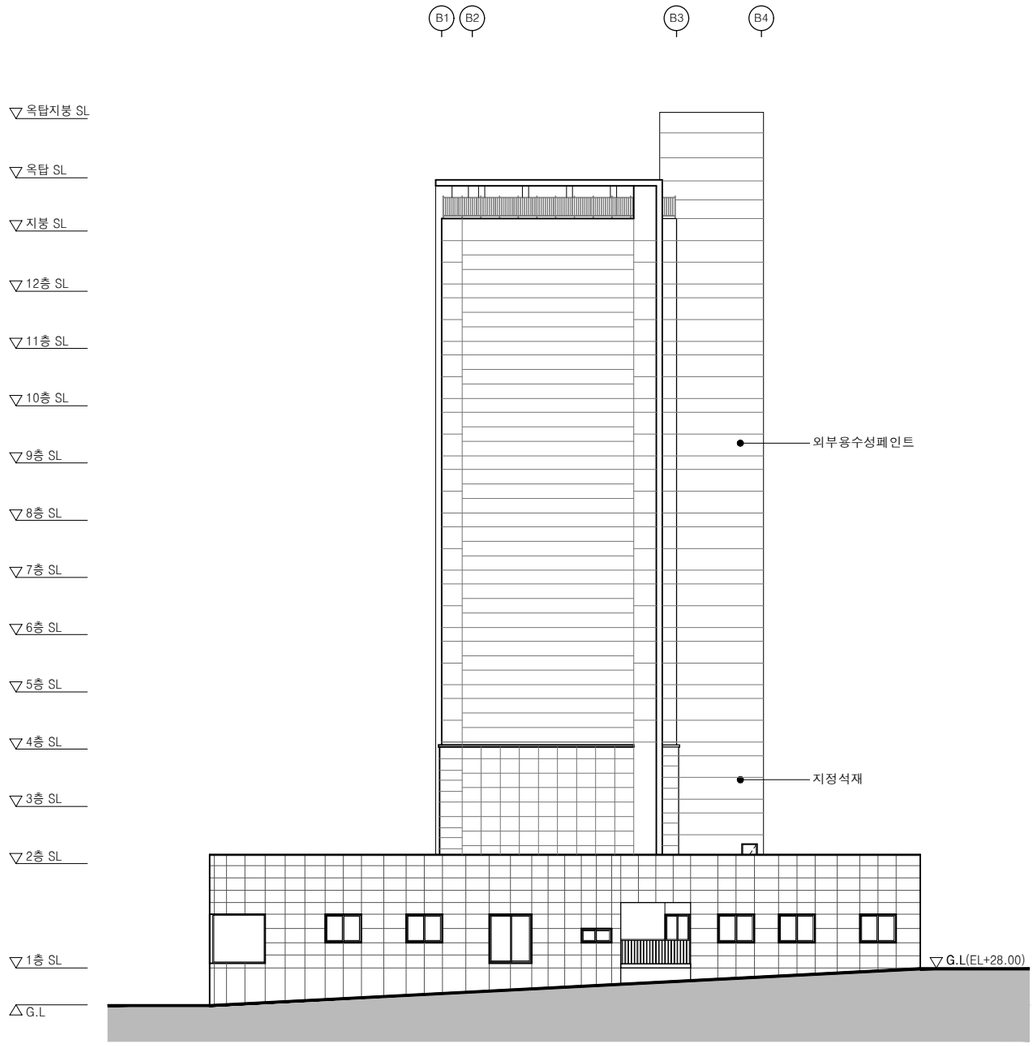

2 A 103동 우측면도

축척 = 1/150

사업번호 PROJECT NO.

사업명 PROJECT TITLE

수색4재정비촉진구역
주택재개발 정비사업

KEY PLAN

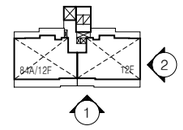

NOTE

1. 1층 바닥 LEVEL
   1SL±0 = 1FL±0 = GL±0 = EL+28.00
2. 지붕 난간의 형태 및 설치위치는 안전성과 입면디자인을 고려하여 변경가능함.
3. 지붕의 재료, 형태, 구조는 실시공시 변경될 수 있음.
4. 지붕 및 옥탑구조물의 형태와 구조는 실시공시 변경될 수 있음.
5. 외벽 및 측벽 문양은 실시공시 변경될 수 있음
6. 입면의 줄눈 및 마감선은 실시공시 변경될 수 있음.
7. 저층부 석재마감 및 입면 마감 색상, 재료에 대한 모든 기준은 특화도면을 우선 적용함.

수정번호 REV. NO.	일 자 DATE	내 용 DESCRIPTION	승 인 CHKD
△			
△			
△			
△			

설계 DESIGNED BY

검토 CHECKED BY
최 진 규

심사 SUMMITED BY
정 호 혁

승인 APPROVED BY
이 승 준

일자 DATE
2019.08

도면명 DRAWING TITLE
103동 정면도,우측면도

축 척 SCALE
A1: 1/150
A3: 1/300

도면번호 DRAWING NO.
A-327

일련번호 SHEET NO.

△ REV. NO.

HAUD
(주)하우드엔지니어링
종합건축사사무소
Architects, Planners & Engineers
TEL. 02 2149 4400, SEOUL, KOREA

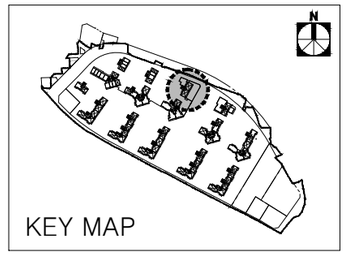

사업번호 PROJECT NO.

사업명 PROJECT TITLE

수색4재정비촉진구역
주택재개발 정비사업

KEY PLAN

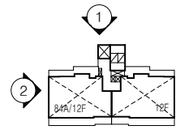

NOTE

1. 1층 바닥 LEVEL
   1SL±0 = 1FL±0 = GL±0 = EL+28.00
2. 지붕 난간의 형태 및 설치위치는 안전성과 입면디자인을 고려하여 변경가능함.
3. 지붕의 재료, 형태, 구조는 실시공시 변경될 수 있음.
4. 지붕 및 옥탑구조물의 형태와 구조는 실시공시 변경될 수 있음.
5. 외벽 및 측벽 문양은 실시공시 변경될 수 있음.
6. 입면의 줄눈 및 마감선은 실시공시 변경될 수 있음.
7. 저층부 석재마감 및 입면 마감 색상, 재료에 대한 모든 기준은 특화도면을 우선 적용함.

1 A 103동 배면도

축척 = 1/150

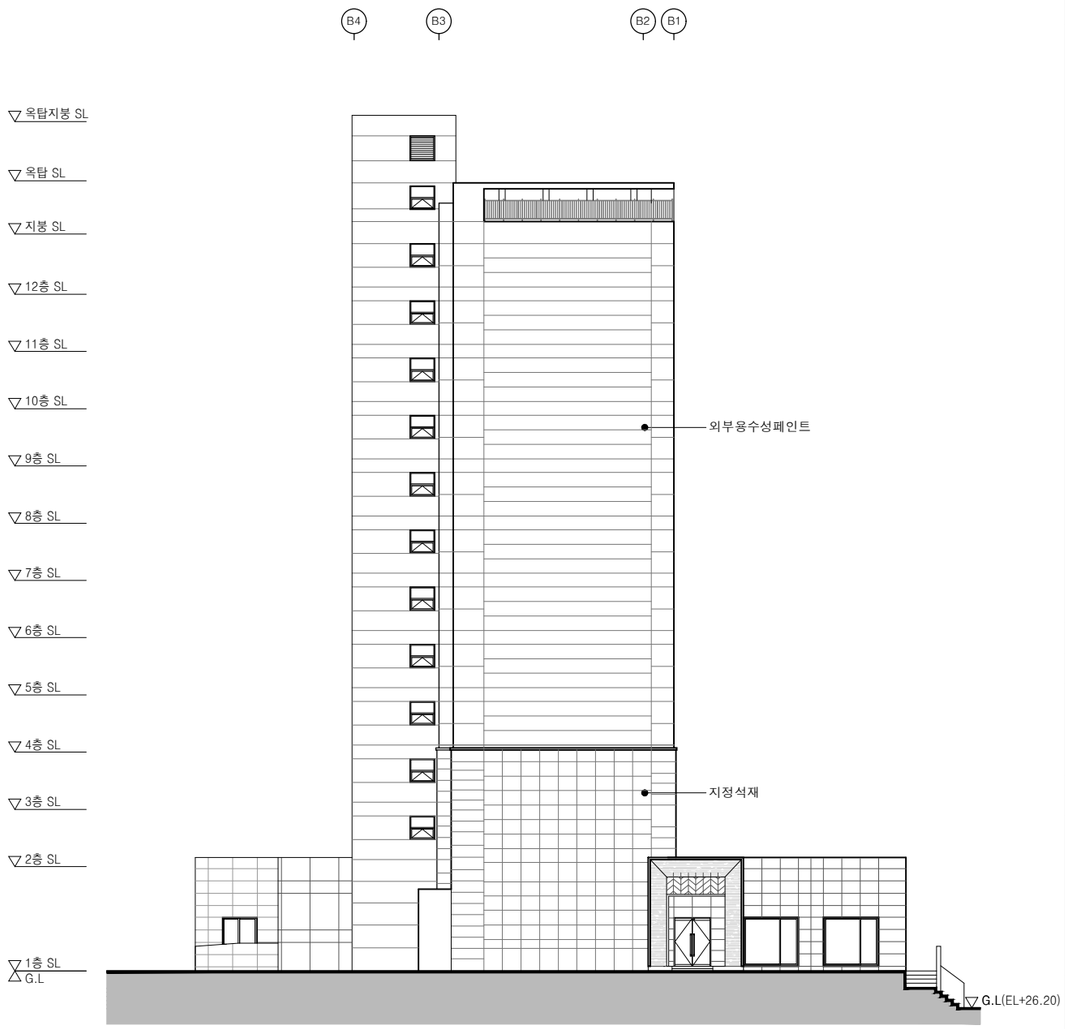

2 A 103동 좌측면도

축척 = 1/150

수정번호 REV. NO.	일 자 DATE	내 용 DESCRIPTION	승 인 CHKD
△			
△			
△			
△			

설계 DESIGNED BY

검토 CHECKED BY
최 진 규

심사 SUMMITED BY
정 호 혁

승인 APPROVED BY
이 승 준

일자 DATE
2019.08

도면명 DRAWING TITLE
103동 배면도,좌측면도

축 척 SCALE
A1: 1/150
A3: 1/300

도면번호 DRAWING NO.
A-328

일련번호 SHEET NO. | REV. NO. △

HAUD
(주)하우드엔지니어링
종합건축사사무소
Architects, Planners & Engineers
TEL. 02 2140 4400, SEOUL, KOREA

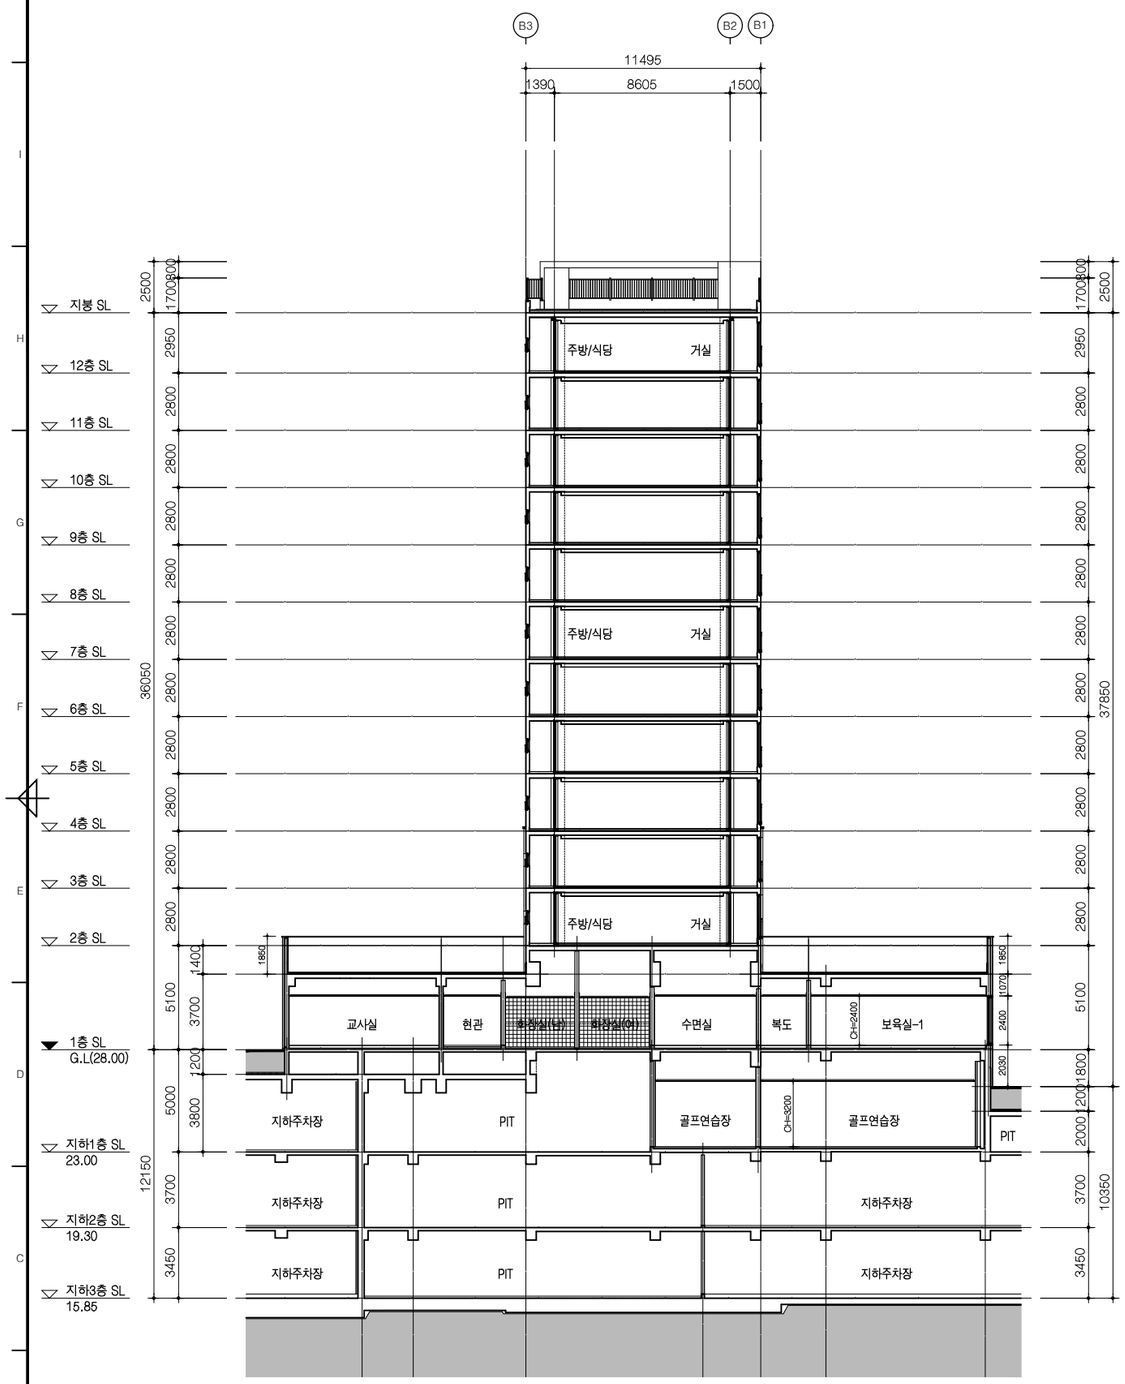

1 A 103동 종단면도

축척 = 1/150

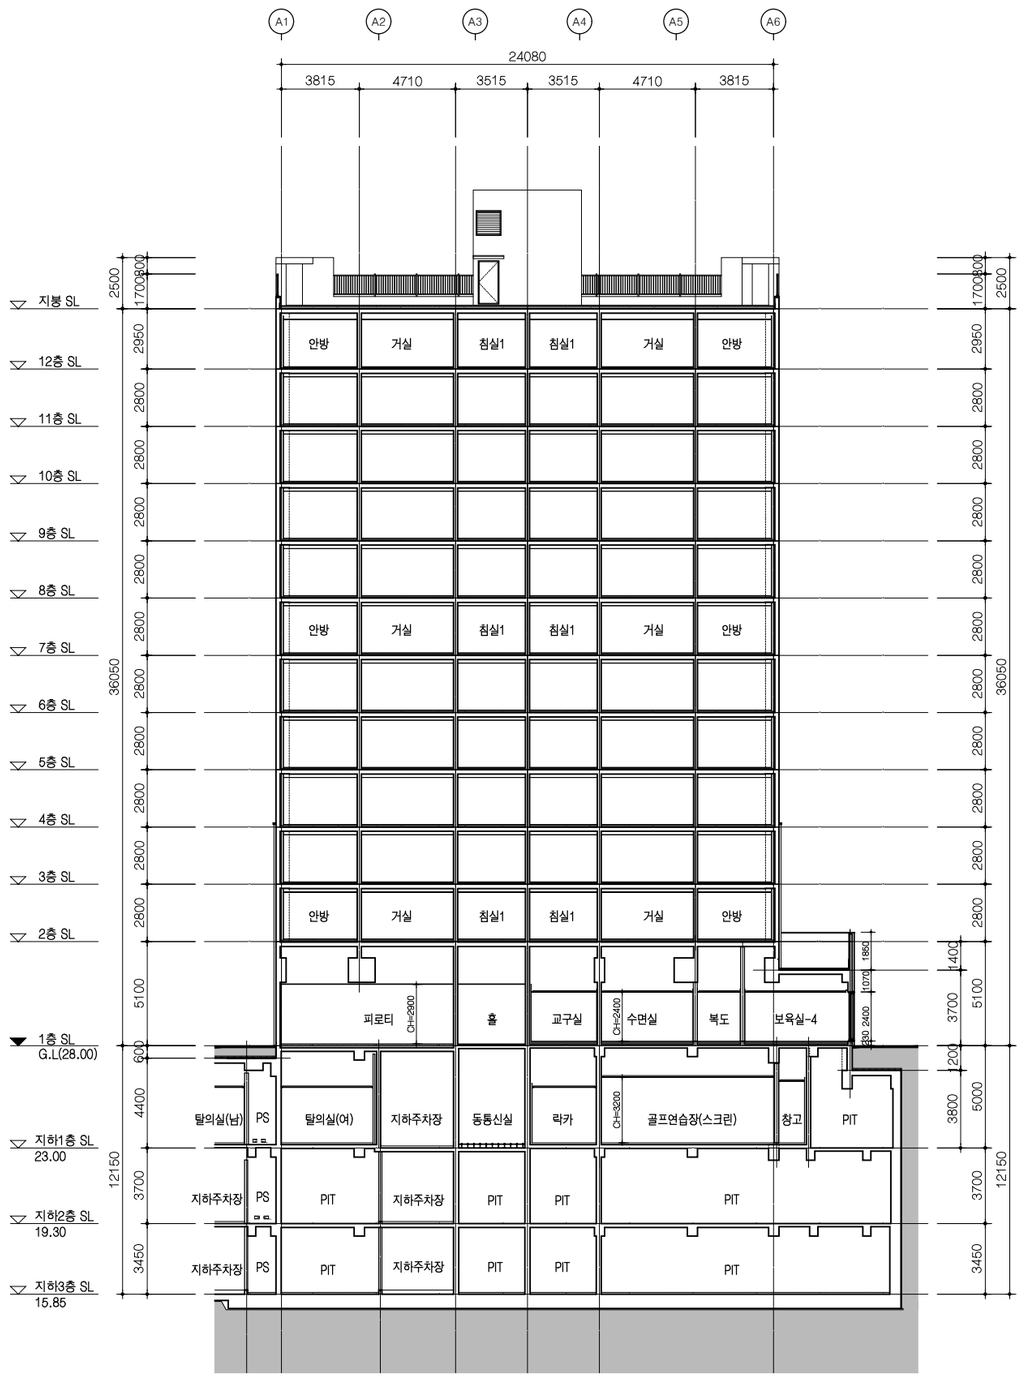

2 A 103동 횡단면도

축척 = 1/150

사업번호 PROJECT NO.

사업명 PROJECT TITLE

수색4재정비촉진구역
주택재개발 정비사업

KEY PLAN

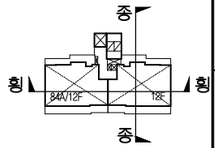

NOTE

REV. NO.	DATE	DESCRIPTION	CHKD
△			
△			
△			
△			

설계 DESIGNED BY

검토 CHECKED BY
최 진 규

심사 SUMMITED BY
정 호 혁

승인 APPROVED BY
이 승 준

일자 DATE
2019.08

도면명 DRAWING TITLE
103동 종,횡단면도

축 척 SCALE
A1: 1/150
A3: 1/300

도면번호 DRAWING NO.
A-329

일련번호 SHEET NO.

REV. NO. △

HAUD
(주)하우드엔지니어링
종합건축사사무소
Architects, Planners & Engineers
TEL. 02 2140 4400, SEOUL, KOREA

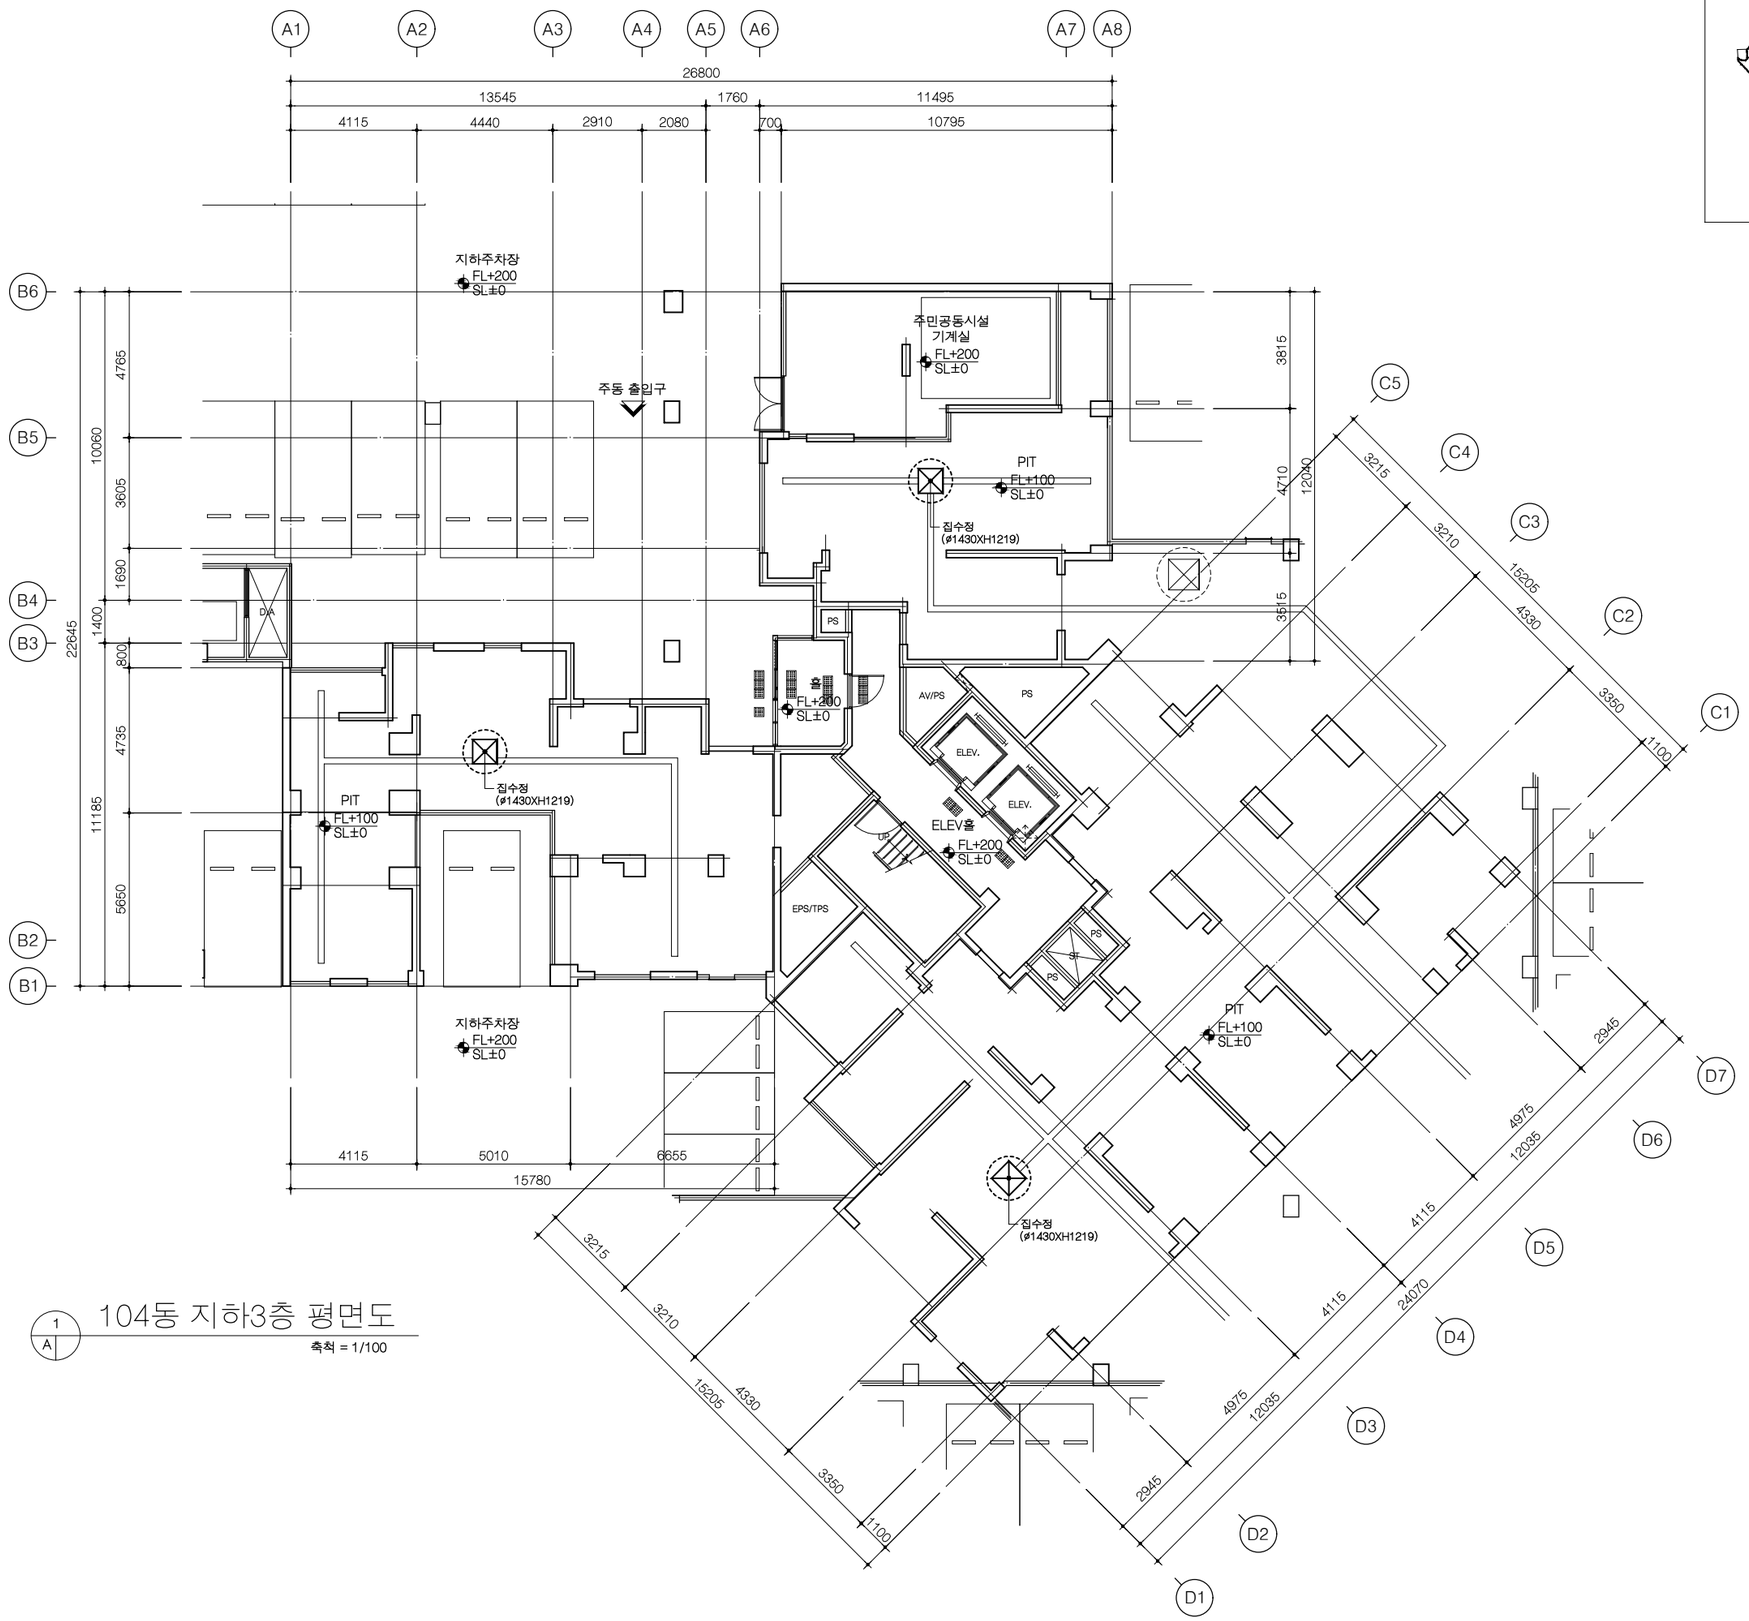

1 A 104동 지하3층 평면도

축척 = 1/100

KEY MXP

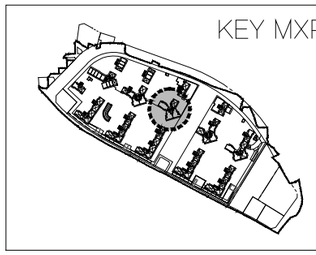

사업번호 PROJECT NO.

사업명 PROJECT TITLE

수색4재정비촉진구역
주택재개발 정비사업

KEY PLAN

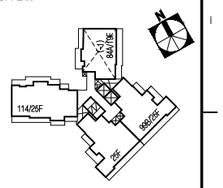

NOTE

1. 지하층 무근 콘크리트는 실시공시 THK80~120 범위로 변동이 있을수 있음.(SLOPE)
2. ELEV홀에 면한부위는 1.0B 조적쌓기임.
3. 지하주차장의 블록쌓기 기준은 높이가 3.6m이하인 경우 4인치 보강블록쌓기가 기준임 (단, 5.4m이하는 6인치쌓기, 5.4m초과는 8인치쌓기가 기준임)
4. ELEV.PIT 집수정은 (600X600X600)임.
5. 주차장 내의 창호는 주차장 창호도 참조.
6. 주차장 집수정 및 영구배수 집수정의 크기 및 위치는 지하주차장 평면도를 참조 할 것.
   ☒ : 주차장 집수정
   ☒ : 영구배수 집수정

********** 지하3층 바닥LEVEL
B3SL±0 = B3FL±0 = EL+15.85

수정번호 REV. NO.	일 자 DATE	내 용 DESCRIPTION	승 인 CHKD
△			
△			
△			
△			

설계 DESIGNED BY

검토 CHECKED BY
최 진 규

심사 SUMMITED BY
정 호 혁

승인 APPROVED BY
이 승 준

일자 DATE
2019.08

도면명 DRAWING TITLE
104동
지하3층 평면도

축 척 SCALE
A1: 1/100
A3: 1/200

도면번호 DRAWING NO.
A-331

일련번호 SHEET NO. △ REV. NO.

HAUD
㈜하우드엔지니어링
종합건축사사무소
Architects, Planners & Engineers
TEL. 82 2 143 4400, SEOUL, KOREA

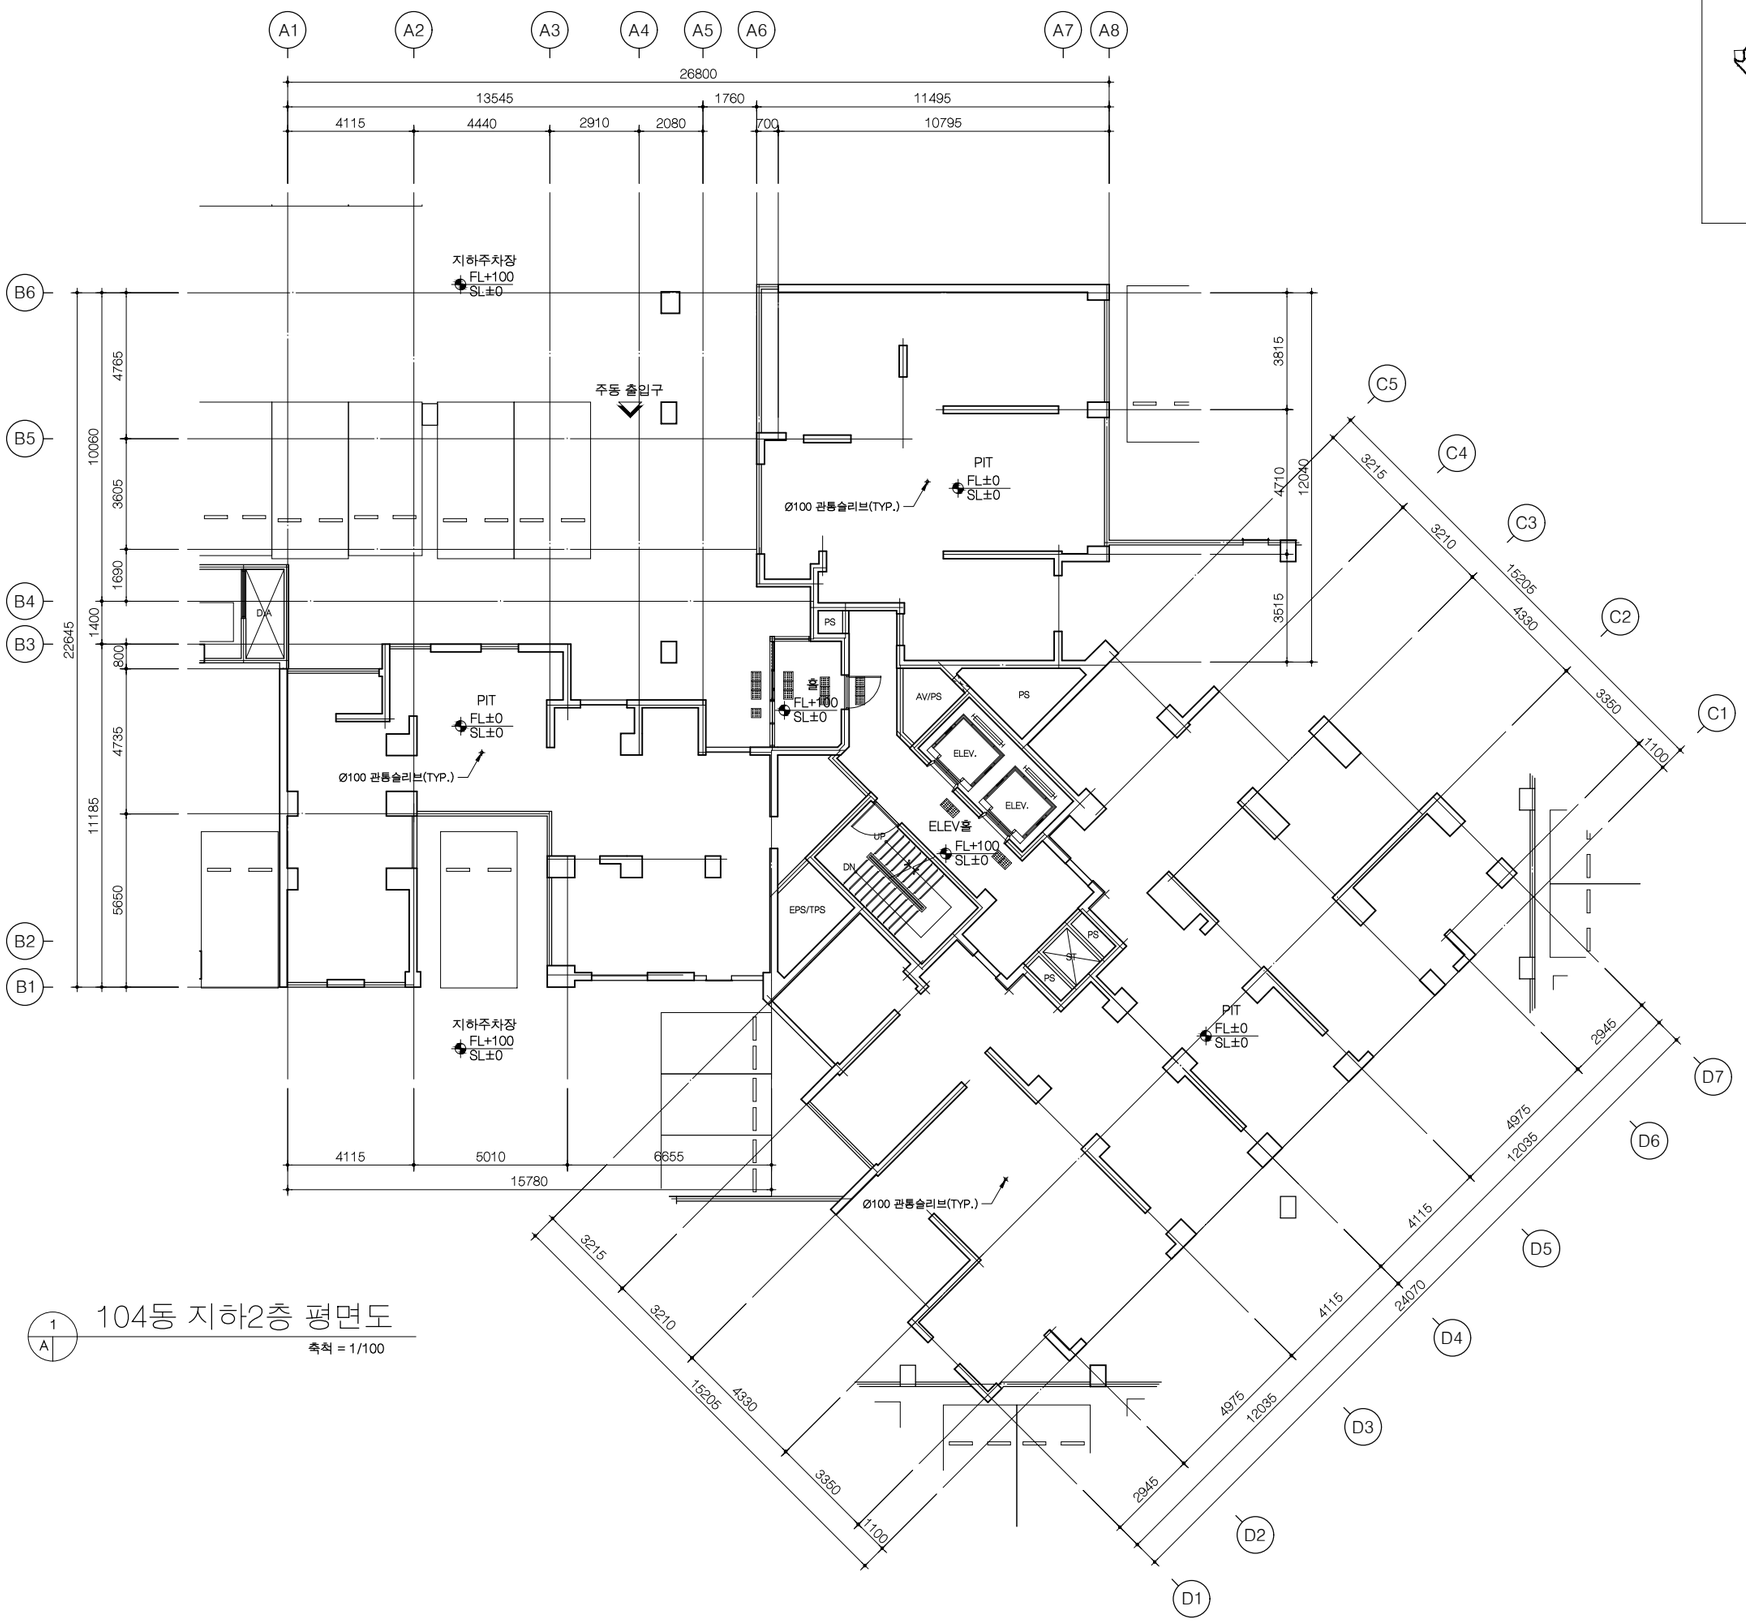

1 / A 104동 지하2층 평면도

축척 = 1/100

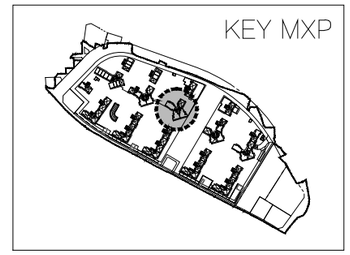

사업번호 PROJECT NO.

사업명 PROJECT TITLE

수색4재정비촉진구역
주택재개발 정비사업

KEY PLAN

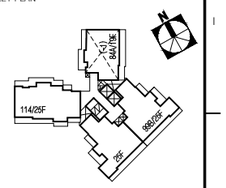

NOTE

1. 지하주차장의 ELEV홀에 면한부위는 1.0B 조적쌓기임.
2. 지하주차장의 블록쌓기 기준은 높이가 3.6m이하인 경우 4인치 보강블록쌓기가 기준임 (단, 5.4m이하는 6인치쌓기, 5.4m초과는 8인치쌓기가 기준임)
3. 주차장 내의 창호는 주차장 창호도 참조.

**** 지하2층 바닥LEVEL
D2SL±0 = D2FL±0 = EL+19.30

수정번호 REV. NO.	일 자 DATE	내 용 DESCRIPTION	승 인 CHKD
△			
△			
△			
△			

설계 DESIGNED BY

검토 CHECKED BY
최 진 규

심사 SUMMITED BY
정 호 혁

승인 APPROVED BY
이 승 준

일자 DATE
2019.08

도면명 DRAWING TITLE
104동
지하2층 평면도

축 척 SCALE
A1: 1/100
A3: 1/200

도면번호 DRAWING NO.
A-332

일련번호 SHEET NO.

△ REV. NO.

HAUD
㈜하우드엔지니어링
종합건축사사무소
Architects, Planners & Engineers
TEL. 02-2149-4400, SEOUL, KOREA

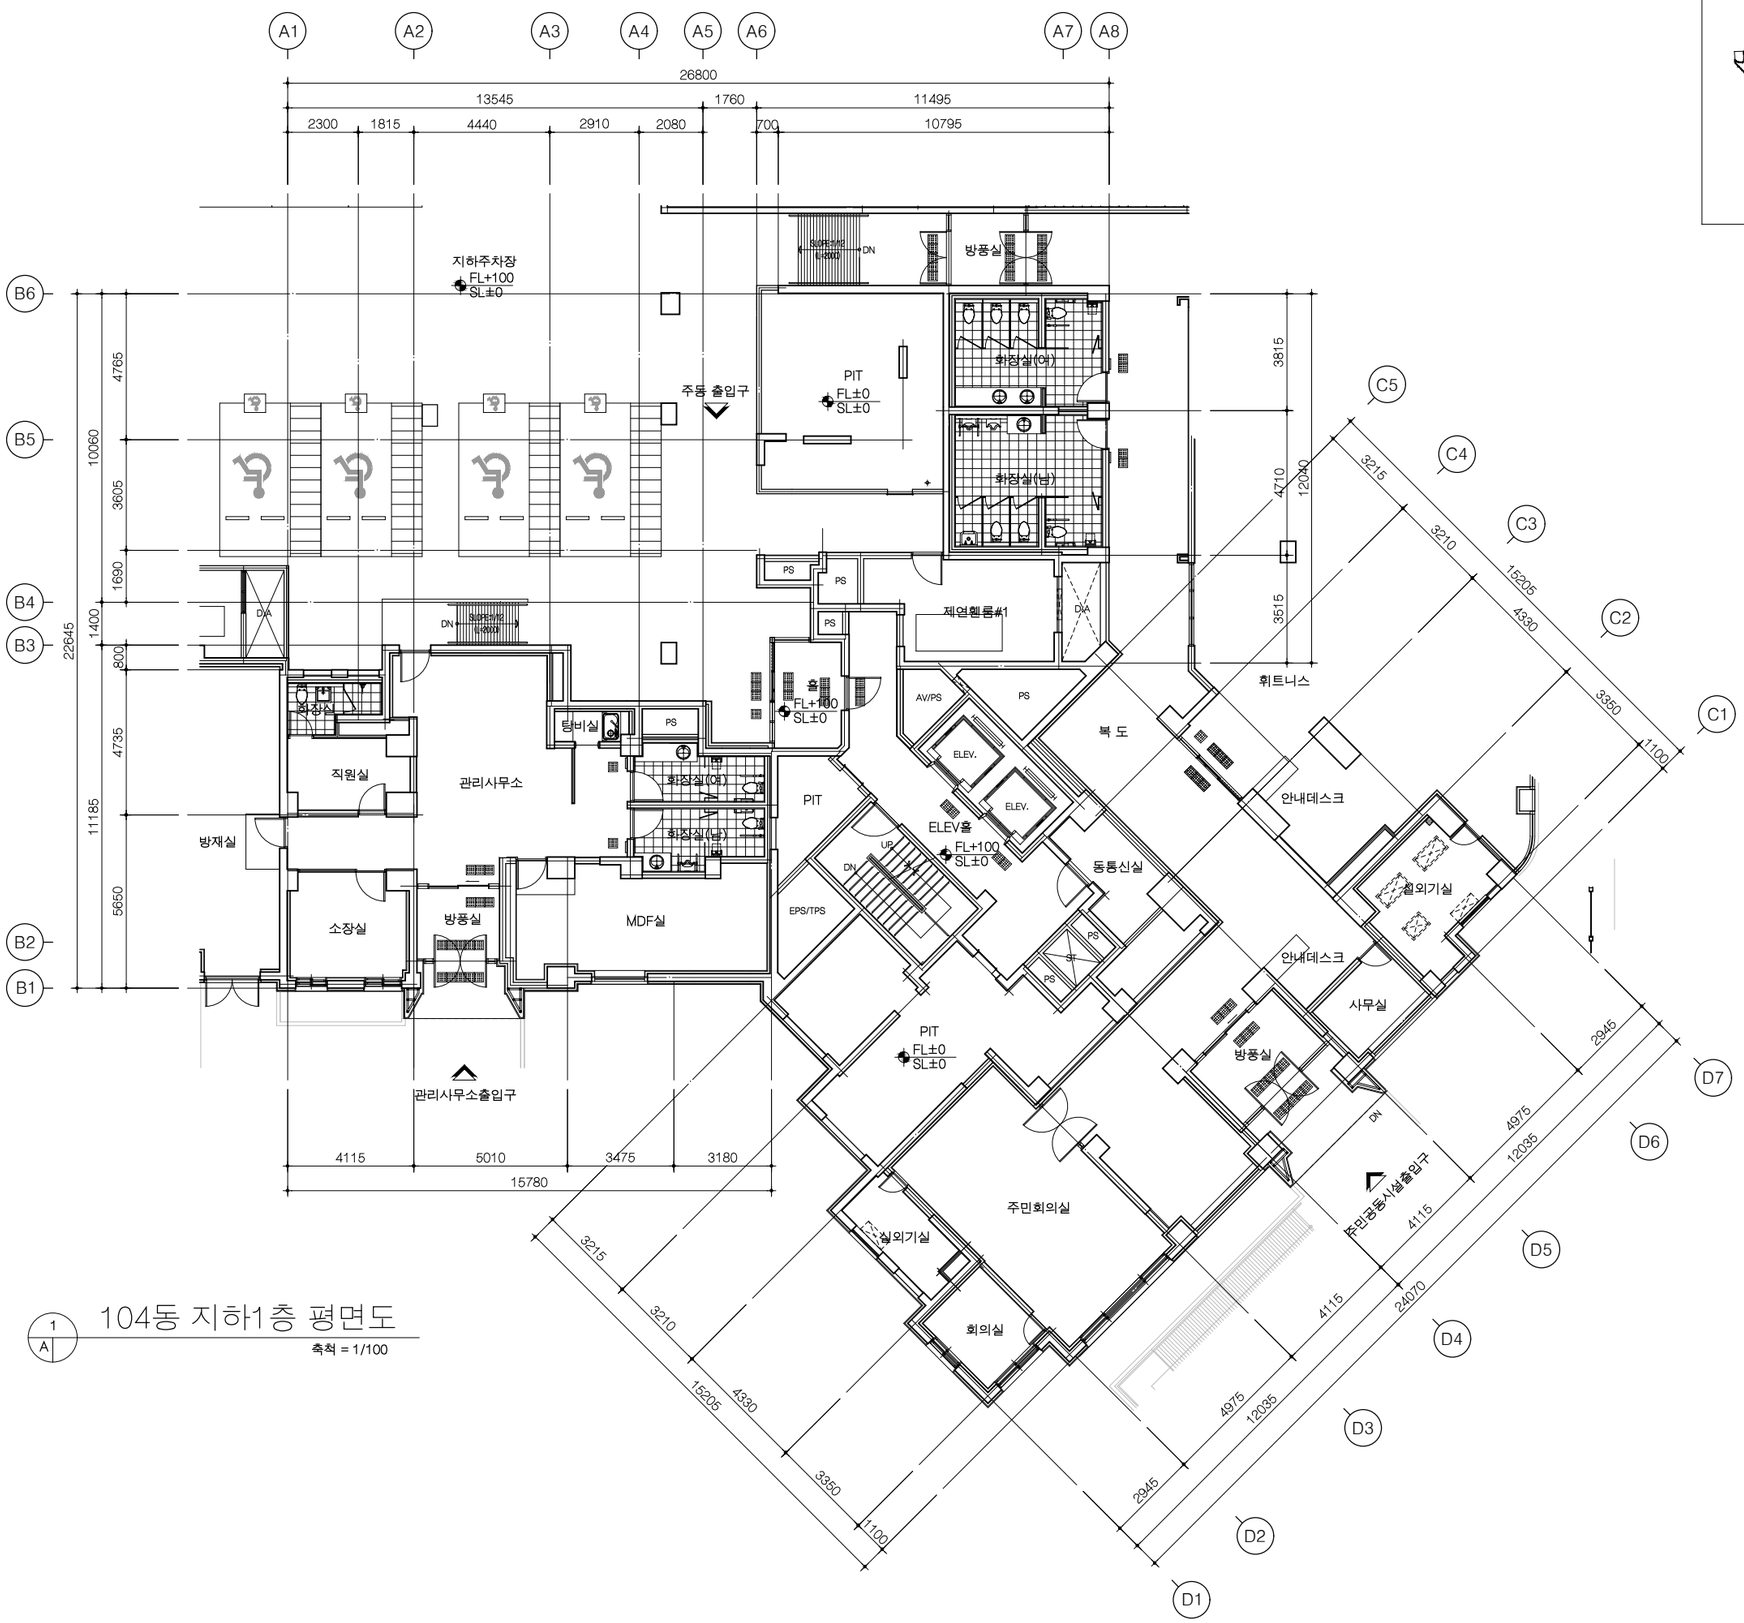

1 / A 104동 지하1층 평면도

축척 = 1/100

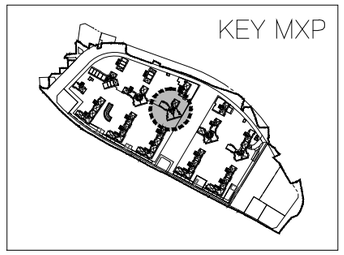

사업번호 PROJECT NO.

사업명 PROJECT TITLE

수색4재정비촉진구역
주택재개발 정비사업

KEY PLAN

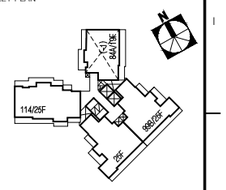

NOTE

1. 지하주차장의 ELEV홀에 면한부위는 1.0B 조적쌓기임.
2. 지하주차장의 블록쌓기 기준은 높이가 3.6m이하인 경우 4인치 보강블록쌓기가 기준임 (단, 5.4m이하는 6인치쌓기, 5.4m초과는 8인치쌓기가 기준임)
3. 주차장 내의 창호는 주차장 창호도 참조.

* 지하1층 바닥LEVEL
D1SL±0 = D1FL±0 = EL+23.00

수정번호 REV. NO.	일 자 DATE	내 용 DESCRIPTION	승 인 CHKD
△			
△			
△			
△			

설계 DESIGNED BY

검토 CHECKED BY
최 진 규

심사 SUMMITED BY
정 호 혁

승인 APPROVED BY
이 승 준

일자 DATE
2019.08

도면명 DRAWING TITLE
104동
지하1층 평면도

축 척 SCALE
A1: 1/100
A3: 1/200

도면번호 DRAWING NO.
A-333

일련번호 SHEET NO. △ REV. NO.

HAUD
(주)하우드엔지니어링
종합건축사사무소
Architects, Planners & Engineers
TEL. 82 2 140 4400, SEOUL, KOREA

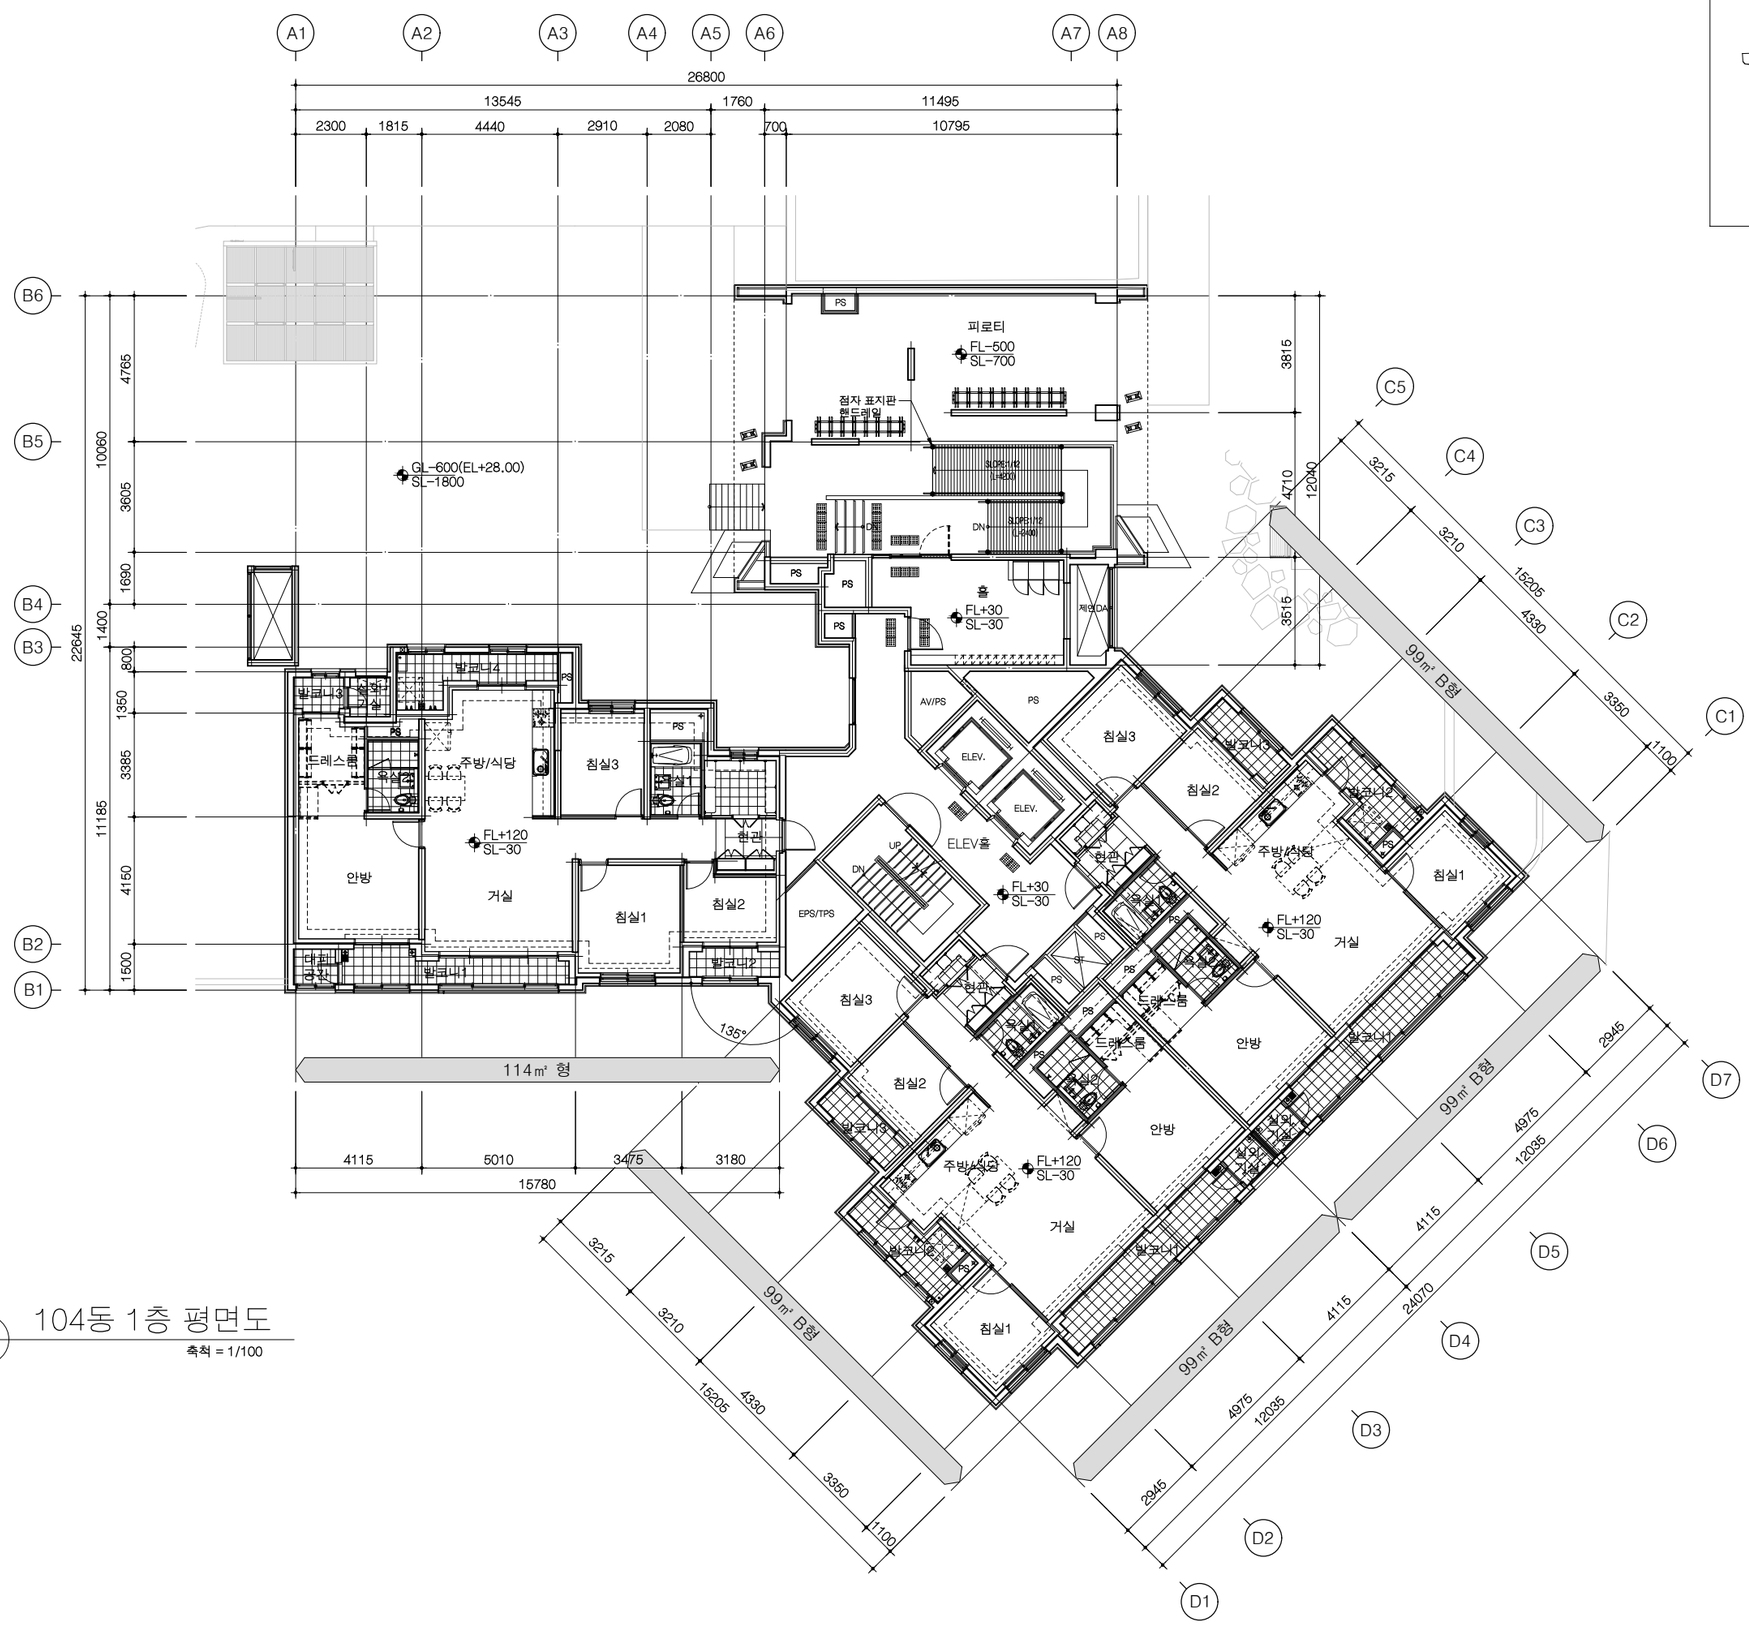

1 / A 104동 1층 평면도

축척 = 1/100

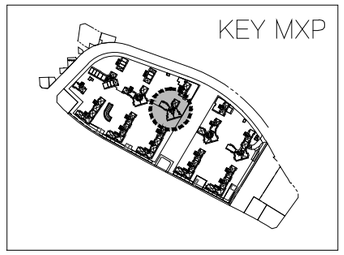

사업번호 PROJECT NO.

사업명 PROJECT TITLE

수색4재정비촉진구역
주택재개발 정비사업

KEY PLAN

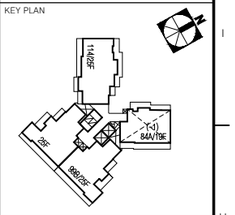

NOTE

1. 본 도면은 발코니 확장전를 기준으로 작성됨.
2. 지붕층 난간의 형태와 설치 위치는 안전성과 입면디자인을 고려하여 변경 가능함.
3. 지붕의 재료, 형태, 구조는 실시공 시 변경 될 수 있음.
4. 지붕 및 옥탑 구조물의 형태와 구조는 실시공 시 변경될 수 있음.
5. 옥상 출눈의 간격은 실시공 시 변경될 수 있음.
6. 옥상 출눈 틈에 실란트 시공되지 않음
7. 우편물 수취함 설치 위치는 변경될 수 있음

* 1층 바닥LEVEL
1SL±0 = 1FL±0 = GL±0 = EL+28.60
GL-600 = EL+28.00(토목도면 참조)

수정번호 REV. NO.	일 자 DATE	내 용 DESCRIPTION	승 인 CHKD
△			
△			
△			
△			

설계 DESIGNED BY

검토 CHECKED BY
최 진 규

심사 SUMMITED BY
정 호 혁

승인 APPROVED BY
이 승 준

일자 DATE
2019.08

도면명 DRAWING TITLE
104동
1층 평면도

축 척 SCALE
A1: 1/100
A3: 1/200

도면번호 DRAWING NO.
A-334

일련번호 SHEET NO. △ REV. NO.

HAUD
㈜하우드엔지니어링
종합건축사사무소
Architects, Planners & Engineers
TEL. 82 2149 4400, SEOUL, KOREA

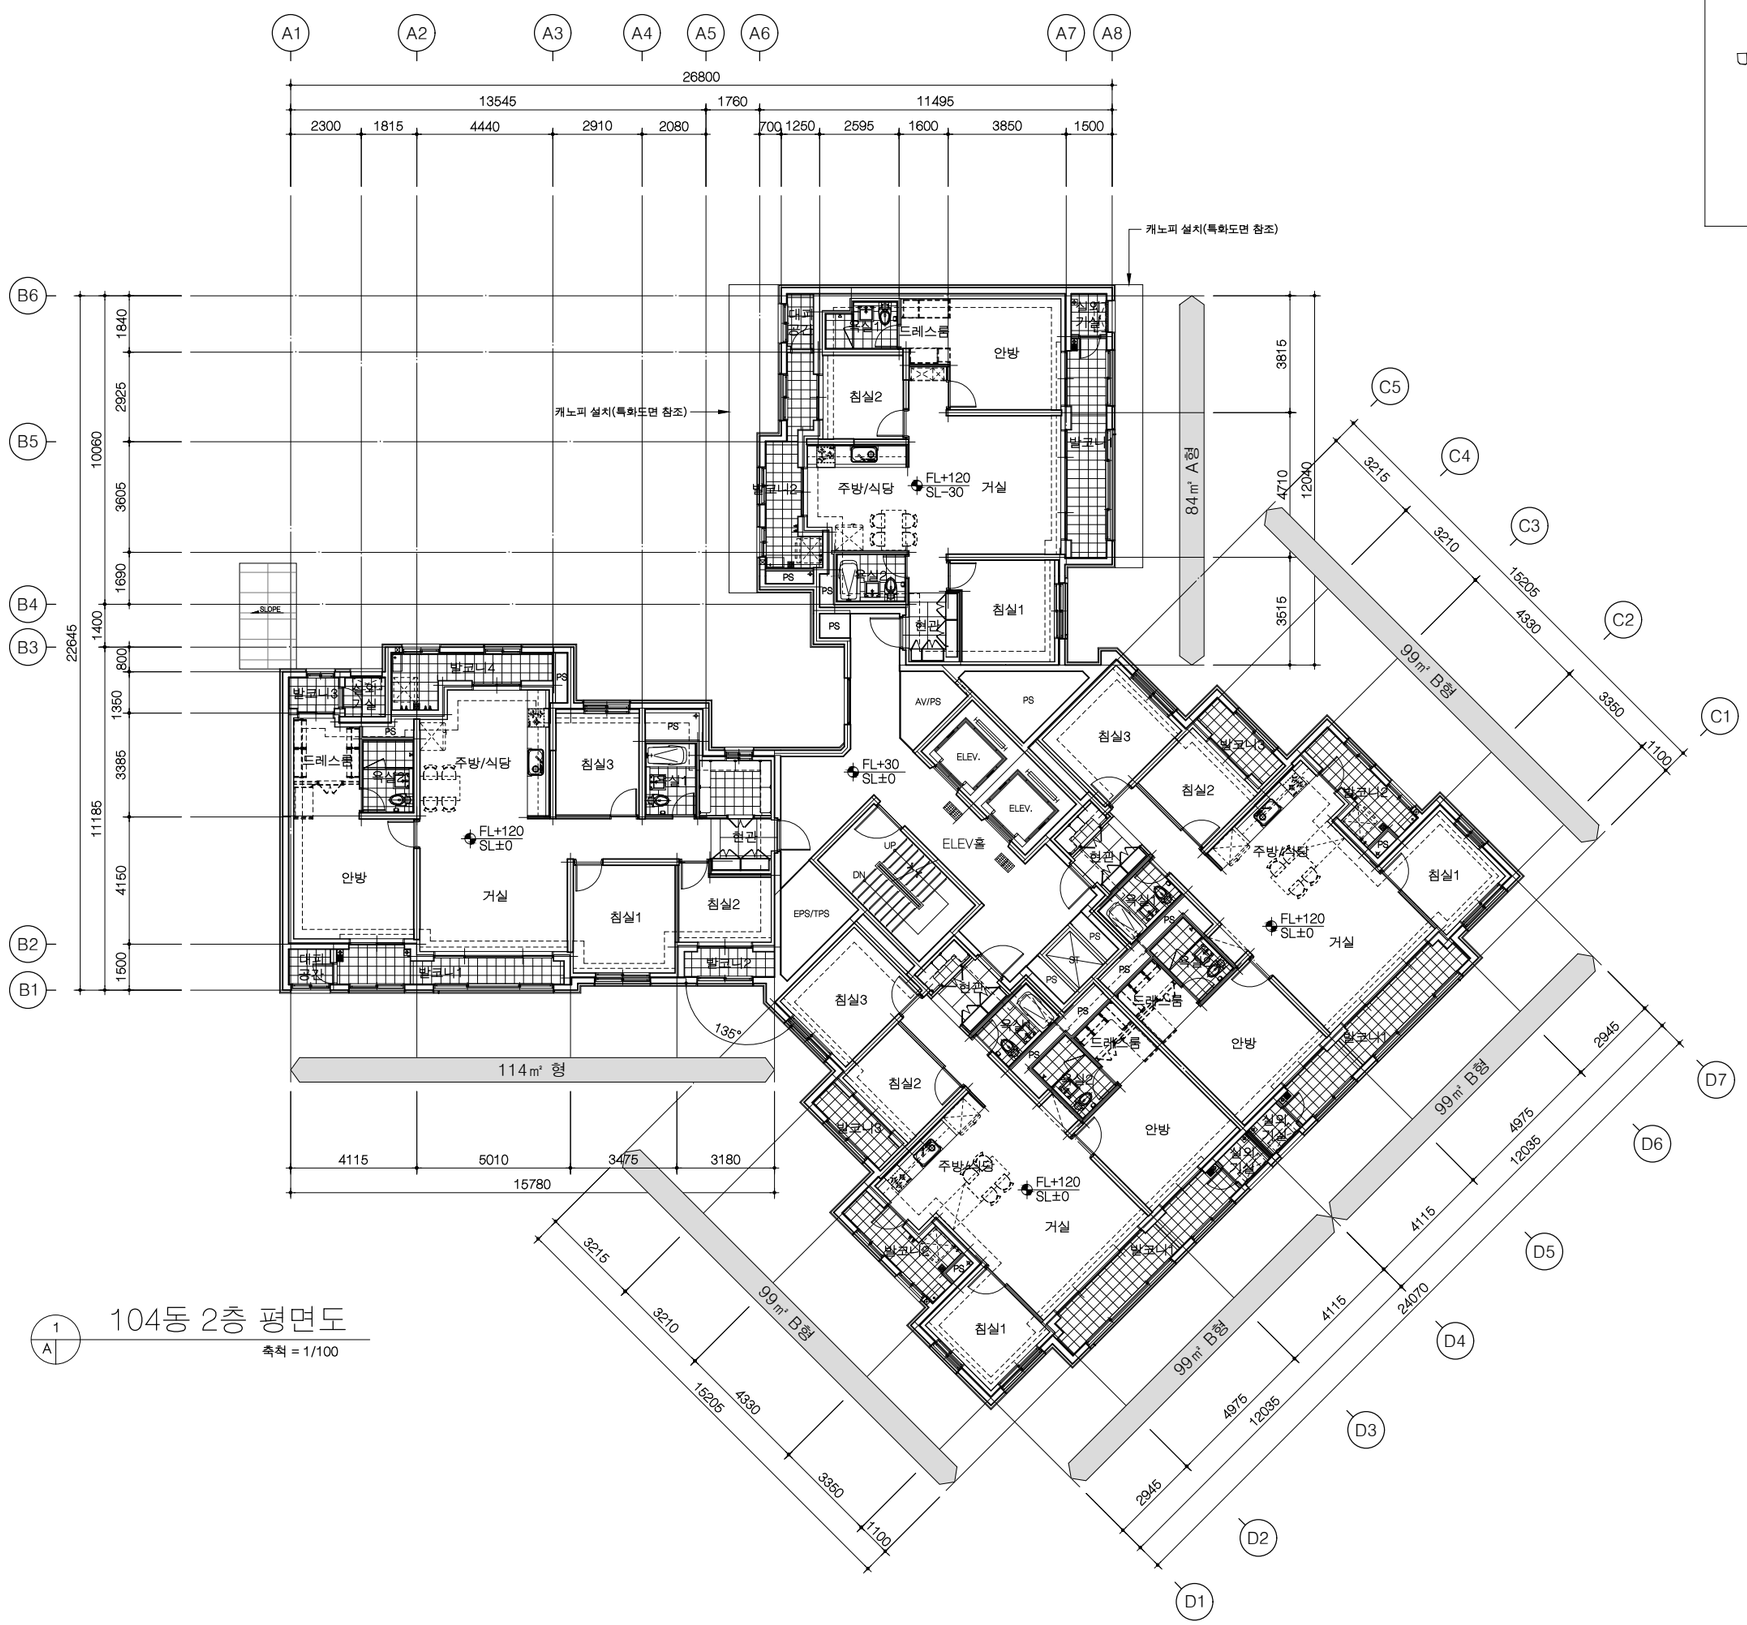

1 A 104동 2층 평면도

축척 = 1/100

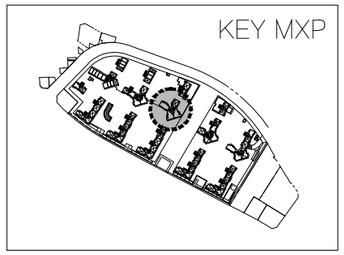

사업번호 PROJECT NO.

사업명 PROJECT TITLE

수색4재정비촉진구역
주택재개발 정비사업

KEY PLAN

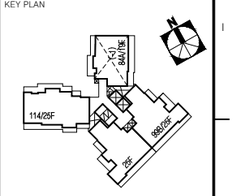

NOTE

1. 본 도면은 발코니 확장전를 기준으로 작성됨.
2. 지붕층 난간의 형태와 설치 위치는 안전성과 입면디자인을 고려하여 변경 가능함.
3. 지붕의 재료, 형태, 구조는 실시공 시 변경 될 수 있음.
4. 지붕 및 옥탑 구조물의 형태와 구조는 실시공 시 변경될 수 있음.
5. 옥상 출눈의 간격은 실시공 시 변경될 수 있음.
6. 옥상 출눈 틈에 실란트 시공되지 않음
7. 우편물 수취함 설치 위치는 변경될 수 있음
8. 오픈형 발코니 3층이상 ~ 20층이하 설치

2층 바닥LEVEL
2SL±0 = 2FL±0 = EL+31.80

수정번호 REV. NO.	일 자 DATE	내 용 DESCRIPTION	승 인 CHKD
△			
△			
△			
△			

설계 DESIGNED BY

검토 CHECKED BY
최 진 규

심사 SUMMITED BY
정 호 혁

승인 APPROVED BY
이 승 준

일자 DATE
2019.08

도면명 DRAWING TITLE
104동
2층 평면도

축 척 SCALE
A1: 1/100
A3: 1/200

도면번호 DRAWING NO.
A-335

일련번호 SHEET NO. △ REV. NO.

HAUD
㈜하우드엔지니어링
종합건축사사무소
Architects, Planners & Engineers
TEL. 82 2149 4400, SEOUL, KOREA

1 A 104동 3층~19층 평면도

축척 = 1/100

KEY MXP

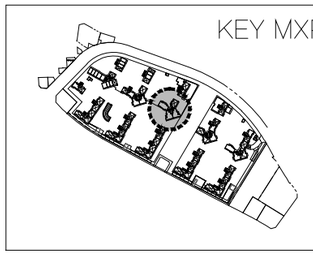

사업번호 PROJECT NO.

사업명 PROJECT TITLE

수색4재정비촉진구역
주택재개발 정비사업

KEY PLAN

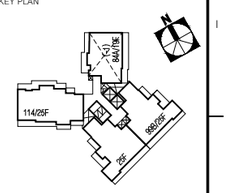

NOTE

1. 본 도면은 발코니 확장전를 기준으로 작성됨.
2. 지붕층 난간의 형태와 설치 위치는 안전성과 입면디자인을 고려하여 변경 가능함.
3. 지붕의 재료, 형태, 구조는 실시공 시 변경 될 수 있음.
4. 지붕 및 옥탑 구조물의 형태와 구조는 실시공 시 변경될 수 있음.
5. 옥상 출눈의 간격은 실시공 시 변경될 수 있음.
6. 옥상 출눈 틈에 실란트 시공되지 않음
7. 우편물 수취함 설치 위치는 변경될 수 있음
8. 오픈형 발코니 3층이상 ~ 20층이하 설치

수정번호 REV. NO.	일 자 DATE	내 용 DESCRIPTION	승 인 CHKD
△			
△			
△			
△			

설계 DESIGNED BY

검토 CHECKED BY
최 진 규

심사 SUMMITED BY
정 호 혁

승인 APPROVED BY
이 승 준

일자 DATE
2019.08

도면명 DRAWING TITLE
104동
3층~19층 평면도

축 척 SCALE
A1: 1/100
A3: 1/200

도면번호 DRAWING NO.
A-336

일련번호 SHEET NO.

△ REV. NO.

HAUD
(주)하우드엔지니어링
종합건축사사무소
Architects, Planners & Engineers
TEL. 02 2140 4400, SEOUL, KOREA

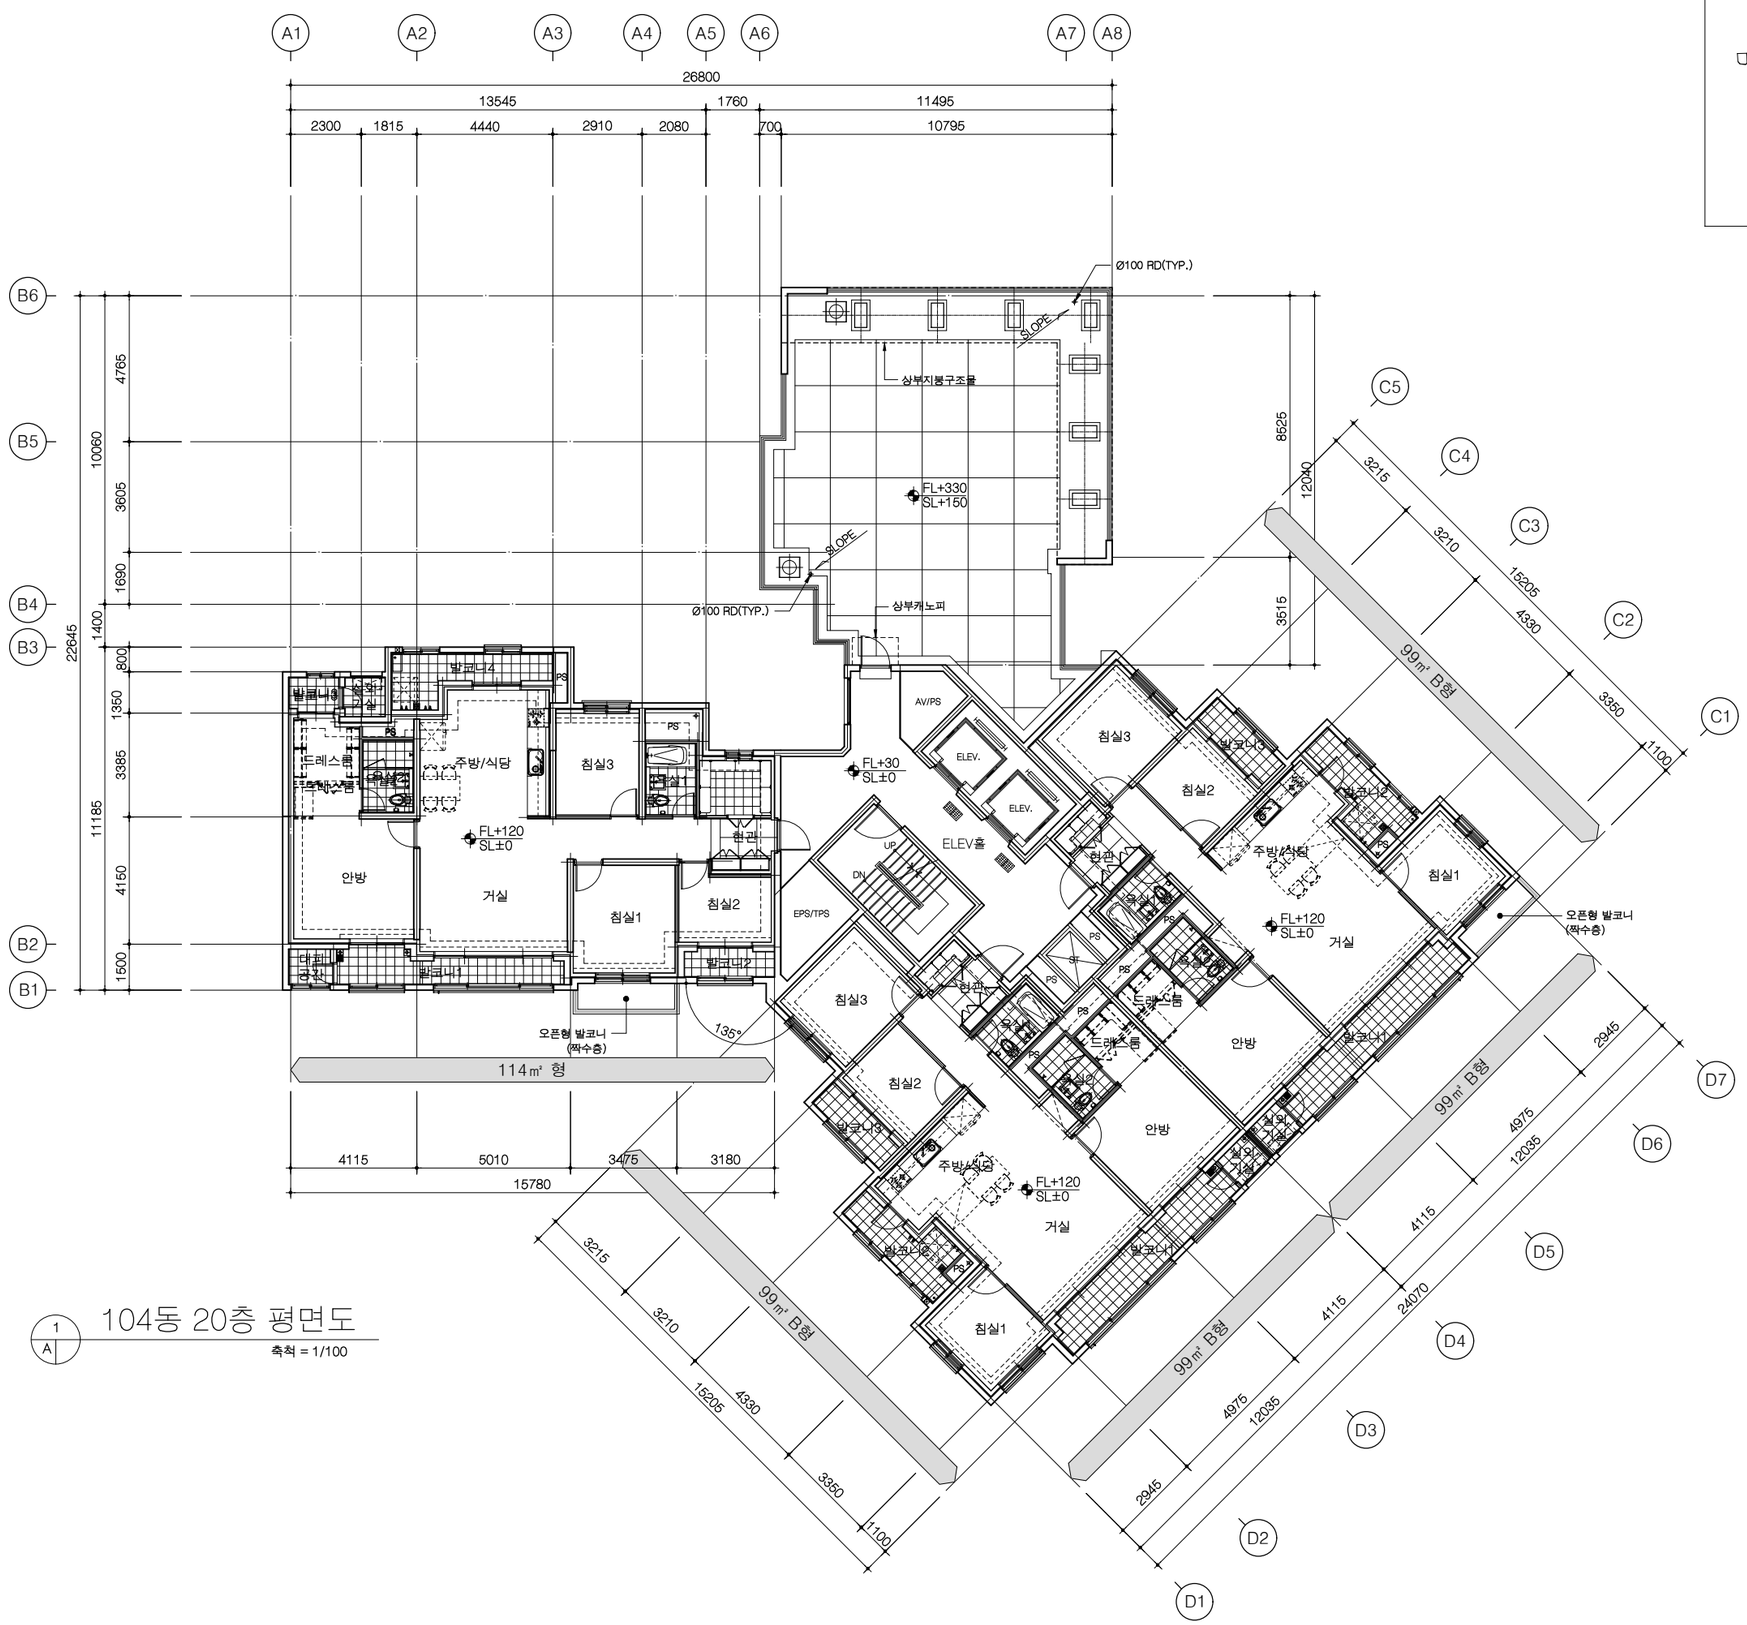

104동 20층 평면도

1 / A

축척 = 1/100

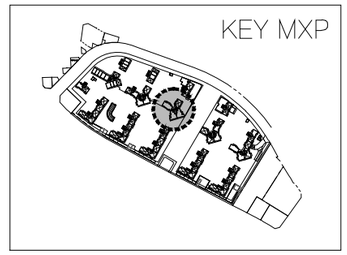

사업번호 PROJECT NO.

사업명 PROJECT TITLE

수색4재정비촉진구역
주택재개발 정비사업

KEY PLAN

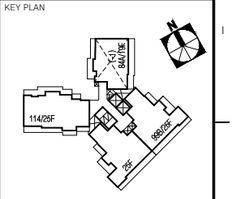

NOTE

1. 본 도면은 발코니 확장전를 기준으로 작성됨.
2. 지붕층 난간의 형태와 설치 위치는 안전성과 입면디자인을 고려하여 변경 가능함.
3. 지붕의 재료, 형태, 구조는 실시공 시 변경 될 수 있음.
4. 지붕 및 옥탑 구조물의 형태와 구조는 실시공 시 변경될 수 있음.
5. 옥상 출눈의 간격은 실시공 시 변경될 수 있음.
6. 옥상 출눈 틈에 실란트 시공되지 않음
7. 우편물 수취함 설치 위치는 변경될 수 있음
8. 오픈형 발코니 3층이상 ~ 20층이하 설치

수정번호 REV. NO.	일 자 DATE	내 용 DESCRIPTION	승 인 CHKD
△			
△			
△			
△			

설계 DESIGNED BY

검토 CHECKED BY
최 진 규

심사 SUMMITED BY
정 호 혁

승인 APPROVED BY
이 승 준

일자 DATE
2019.08

도면명 DRAWING TITLE
104동
20층 평면도

축 척 SCALE
A1: 1/100
A3: 1/200

도면번호 DRAWING NO.
A-337

일련번호 SHEET NO. △ REV. NO.

HAUD
㈜하우드엔지니어링
종합건축사사무소
Architects, Planners & Engineers
TEL. 82 2143 4400, SEOUL, KOREA

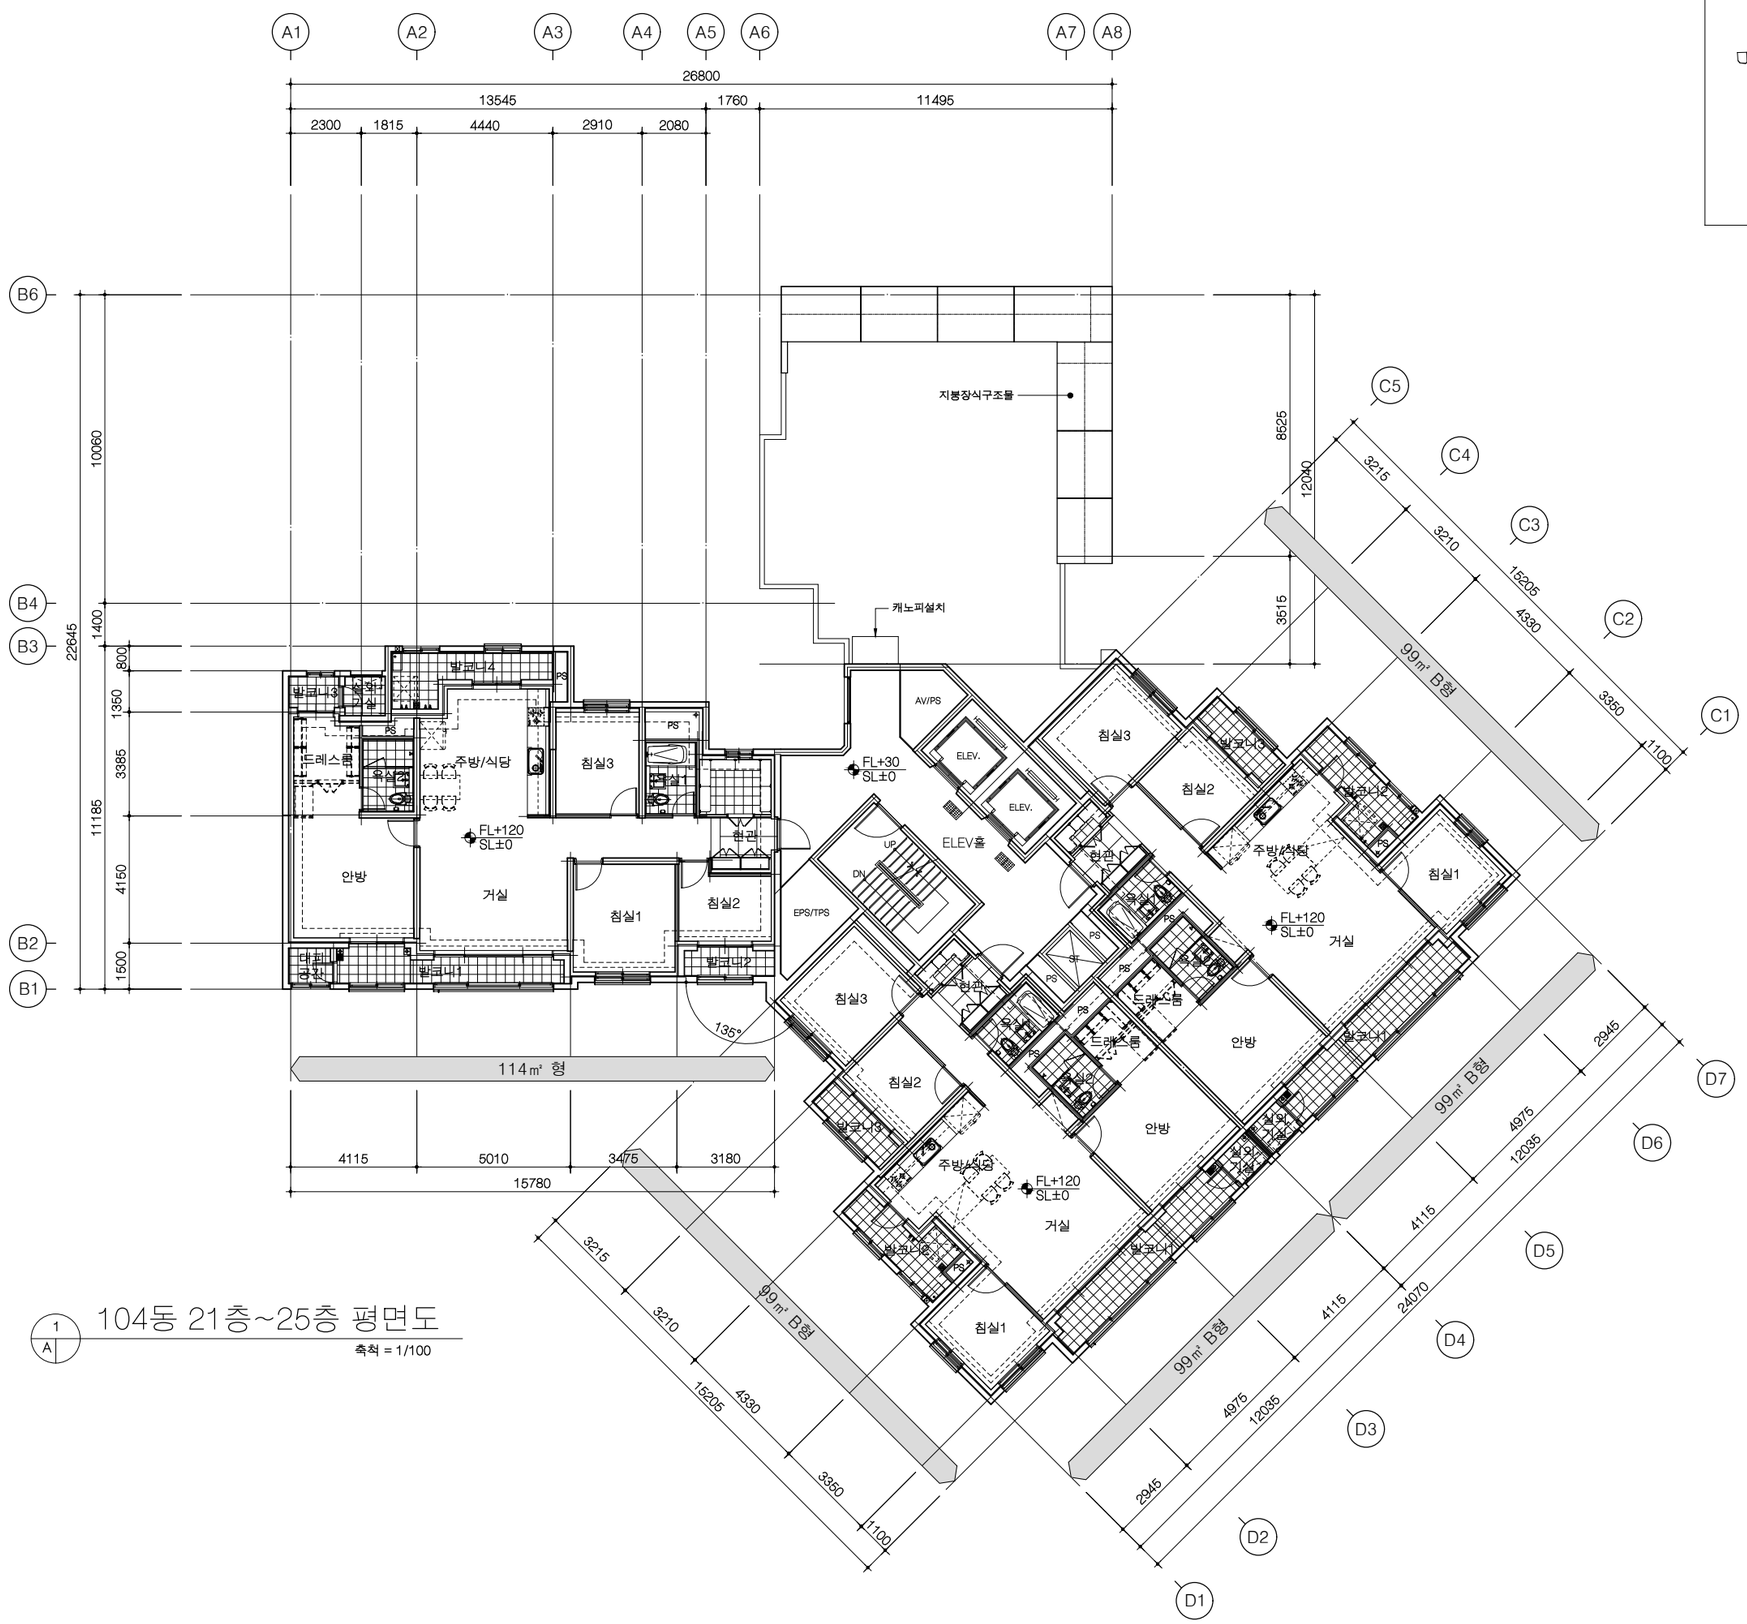

1 A 104동 21층~25층 평면도

축척 = 1/100

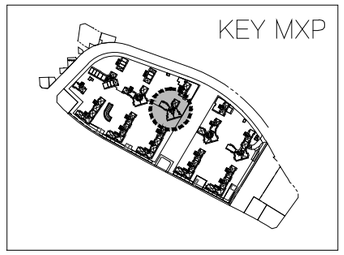

사업번호 PROJECT NO.

사업명 PROJECT TITLE

수색4재정비촉진구역
주택재개발 정비사업

KEY PLAN

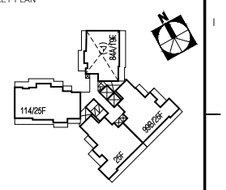

NOTE

1. 본 도면은 발코니 확장전를 기준으로 작성됨.
2. 지붕층 난간의 형태와 설치 위치는 안전성과 입면디자인을 고려하여 변경 가능함.
3. 지붕의 재료, 형태, 구조는 실시공 시 변경 될 수 있음.
4. 지붕 및 옥탑 구조물의 형태와 구조는 실시공 시 변경될 수 있음.
5. 옥상 출눈의 간격은 실시공 시 변경될 수 있음.
6. 옥상 출눈 틈에 실란트 시공되지 않음
7. 우편물 수취함 설치 위치는 변경될 수 있음
8. 오픈형 발코니 3층이상 ~ 20층이하 설치

수정번호 REV. NO.	일 자 DATE	내 용 DESCRIPTION	승 인 CHKD
△			
△			
△			
△			

설계 DESIGNED BY

검토 CHECKED BY
최 진 규

심사 SUMMITED BY
정 호 혁

승인 APPROVED BY
이 승 준

일자 DATE
2019.08

도면명 DRAWING TITLE
104동
21층~25층 평면도

축 척 SCALE
A1: 1/100
A3: 1/200

도면번호 DRAWING NO.
A-338

일련번호 SHEET NO. △ REV. NO.

HAUD
(주)하우드엔지니어링
종합건축사사무소
Architects, Planners & Engineers
TEL. 02 2140 4400, SEOUL, KOREA

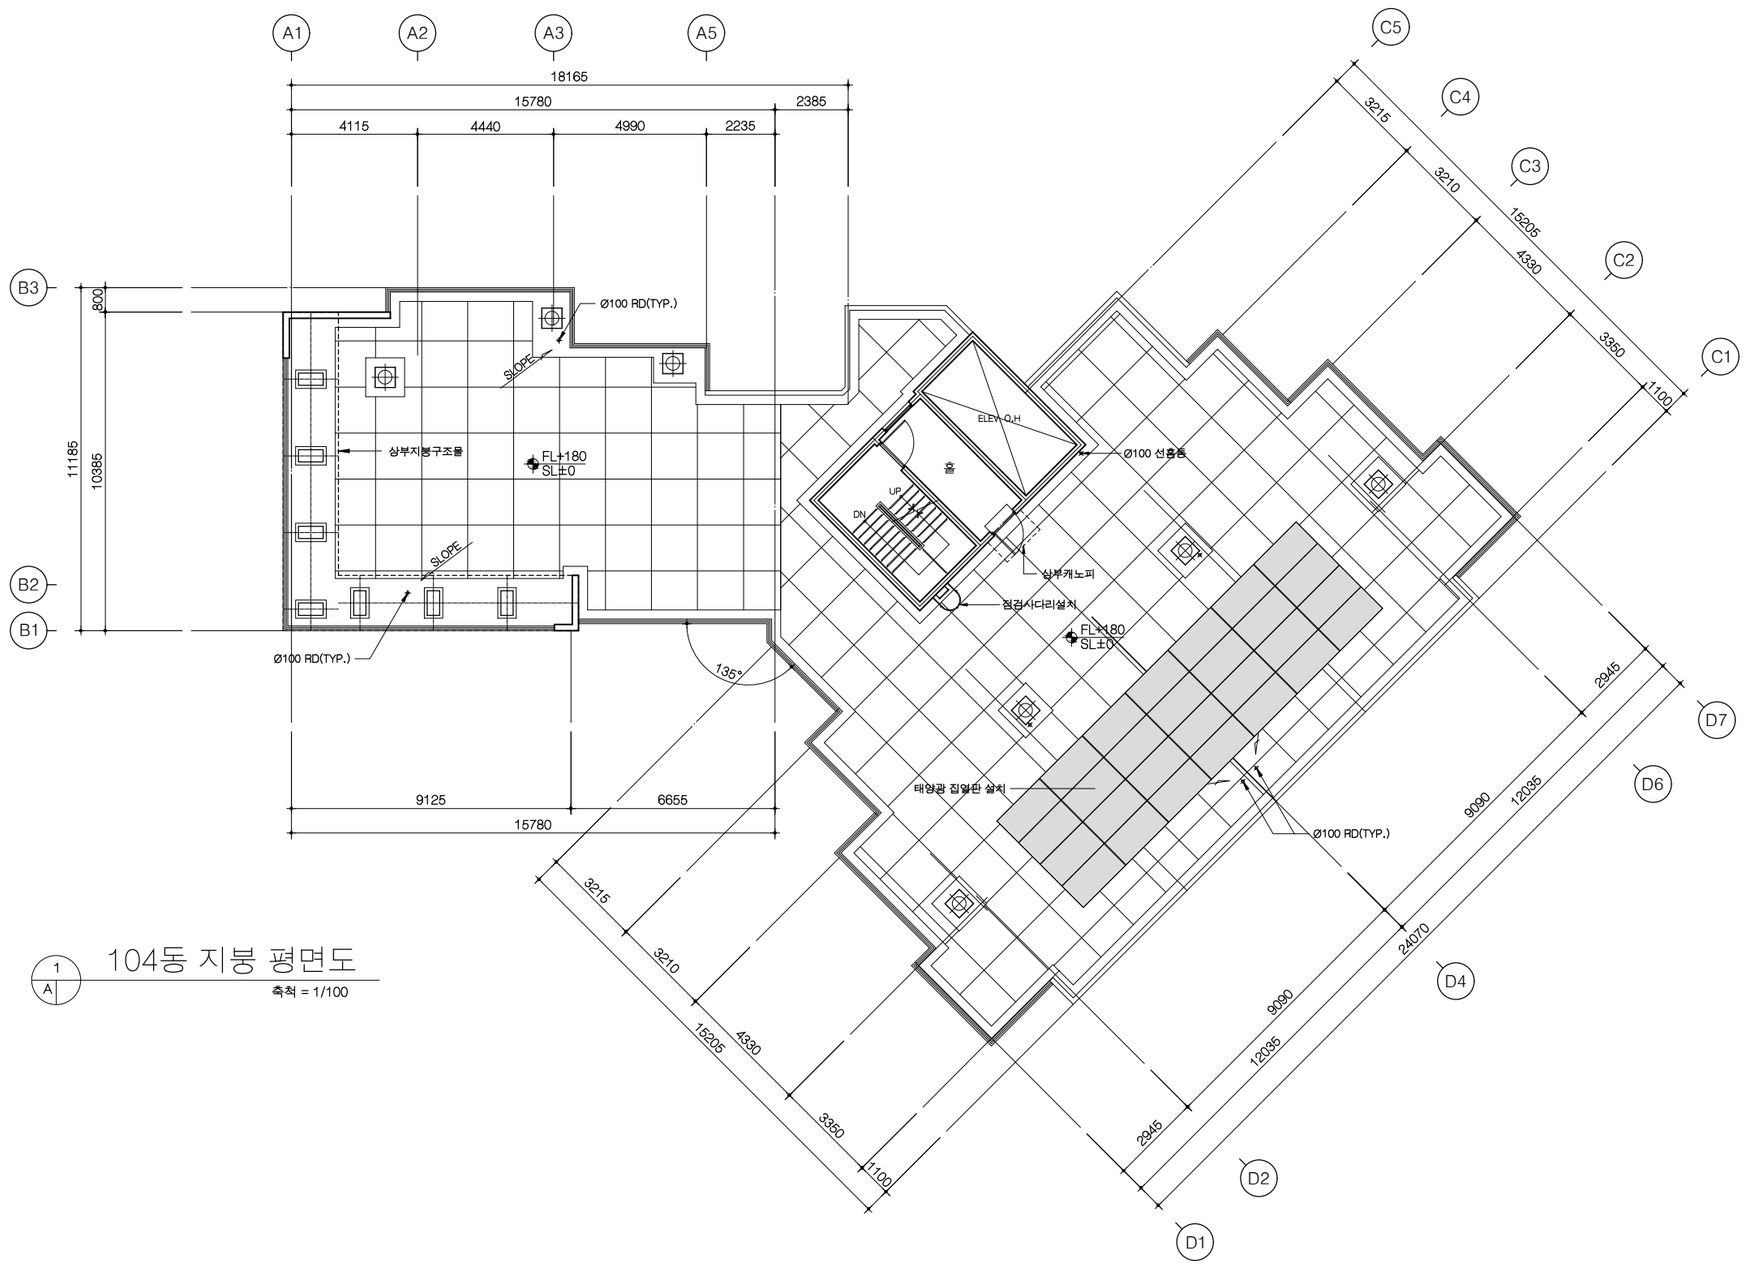

1 A 104동 지붕 평면도

축척 = 1/100

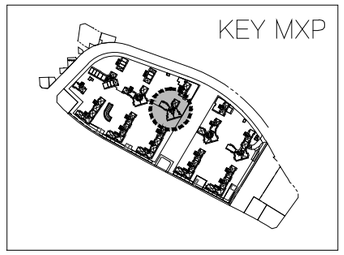

사업번호 PROJECT NO.

사업명 PROJECT TITLE

수색4재정비촉진구역
주택재개발 정비사업

KEY PLAN

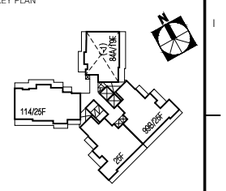

NOTE

1. 지붕바닥
   ① EXP. JOINT: 3000 X 3000
2. 본 평면도는 발코니확장전을 기준으로 작성됨
3. 재료마감은 실내,외 재료마감표 참조
4. 지붕 난간형태/설치위치는 안전성과 입면을 고려하여 실시공시 변경될 수 있음
5. 지붕재료 및 형태,구조는 실시공시 변경될수 있음
6. 지붕(옥탑지붕)의 배수드레인,환소용고리, 베기탑,점검사다리(점검구) 등의 설치위치/개소는 실시공시 변경될 수 있음
7. 옥상 상부구조물은 PC구조물 임.
8. 정화조 배기는 기계도서 참조

수정번호 REV. NO.	일 자 DATE	내 용 DESCRIPTION	승 인 CHKD
△			
△			
△			
△			

설계 DESIGNED BY

검토 CHECKED BY
최 진 규

심사 SUMMITED BY
정 호 혁

승인 APPROVED BY
이 승 준

일자 DATE
2019.08

도면명 DRAWING TITLE
104동
지붕 평면도

축 척 SCALE
A1: 1/100
A3: 1/200

도면번호 DRAWING NO.
A-339

일련번호 SHEET NO.

△ REV. NO.

HAUD
(주)하우드엔지니어링
종합건축사사무소
Architects, Planners & Engineers
TEL. 02 2140 4400, SEOUL, KOREA

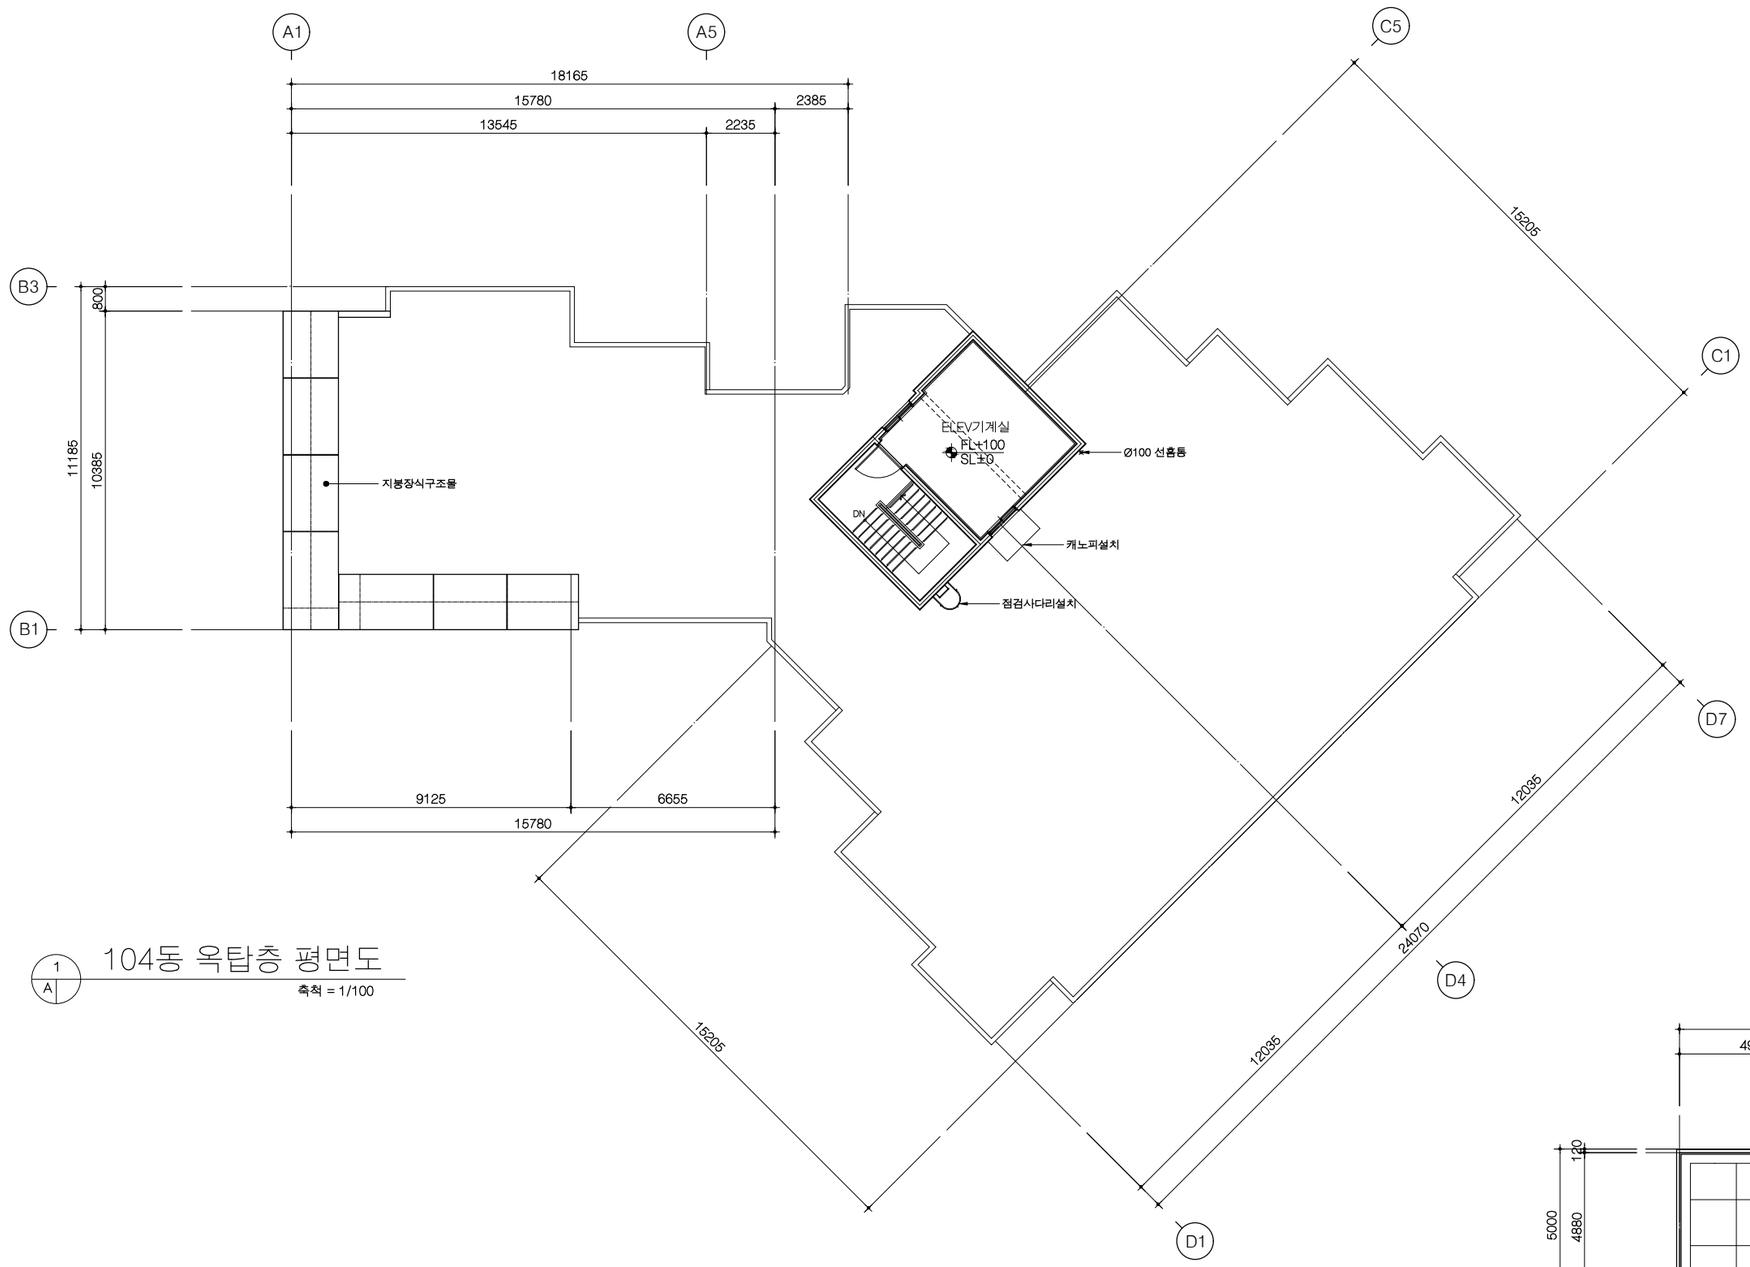

1 A 104동 옥탑층 평면도

축척 = 1/100

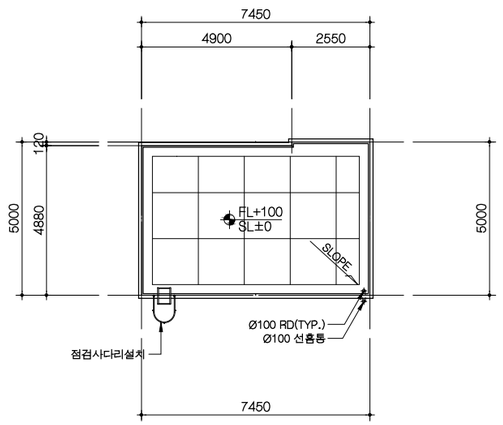

2 A 104동 옥탑지붕 평면도

축척 = 1/100

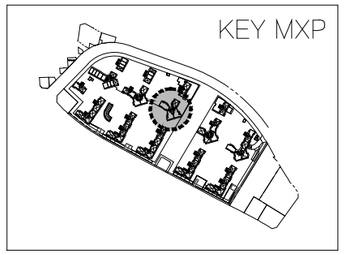

사업번호 PROJECT NO.

사업명 PROJECT TITLE

수색4재정비촉진구역
주택재개발 정비사업

KEY PLAN

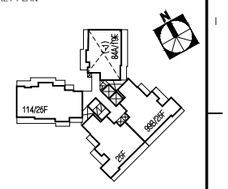

NOTE

1. 지붕바닥
   ① EXP. JOINT: 3000 X 3000
2. 본 평면도는 발코니확장전을 기준으로 작성됨
3. 재료마감은 실내,외 재료마감표 참조
4. 지붕 난간형태/설치위치는 안전성과 입면을 고려하여 실시공시 변경될 수 있음
5. 지붕재료 및 형태,구조는 실시공시 변경될수 있음
6. 지붕(옥탑지붕)의 배수드레인,청소용고리, 베기탑,점검사다리(점검구) 등의 설치위치/개소는 실시공시 변경될 수 있음
7. 옥상 상부구조물은 PC구조물 임.
8. 정화조 배기는 기계도서 참조

수정번호 REV. NO.	일 자 DATE	내 용 DESCRIPTION	승 인 CHKD
△			
△			
△			
△			

설계 DESIGNED BY

검토 CHECKED BY
최 진 규

심사 SUMMITED BY
정 호 혁

승인 APPROVED BY
이 승 준

일자 DATE
2019.08

도면명 DRAWING TITLE
104동
옥탑층 및 옥탑지붕 평면도

축 척 SCALE
A1: 1/100
A3: 1/200

도면번호 DRAWING NO.
A-340

일련번호 SHEET NO.

△ REV. NO.

HAUD
(주)하우드엔지니어링
종합건축사사무소
Architects, Planners & Engineers
TEL. 02 2140 4400, SEOUL, KOREA

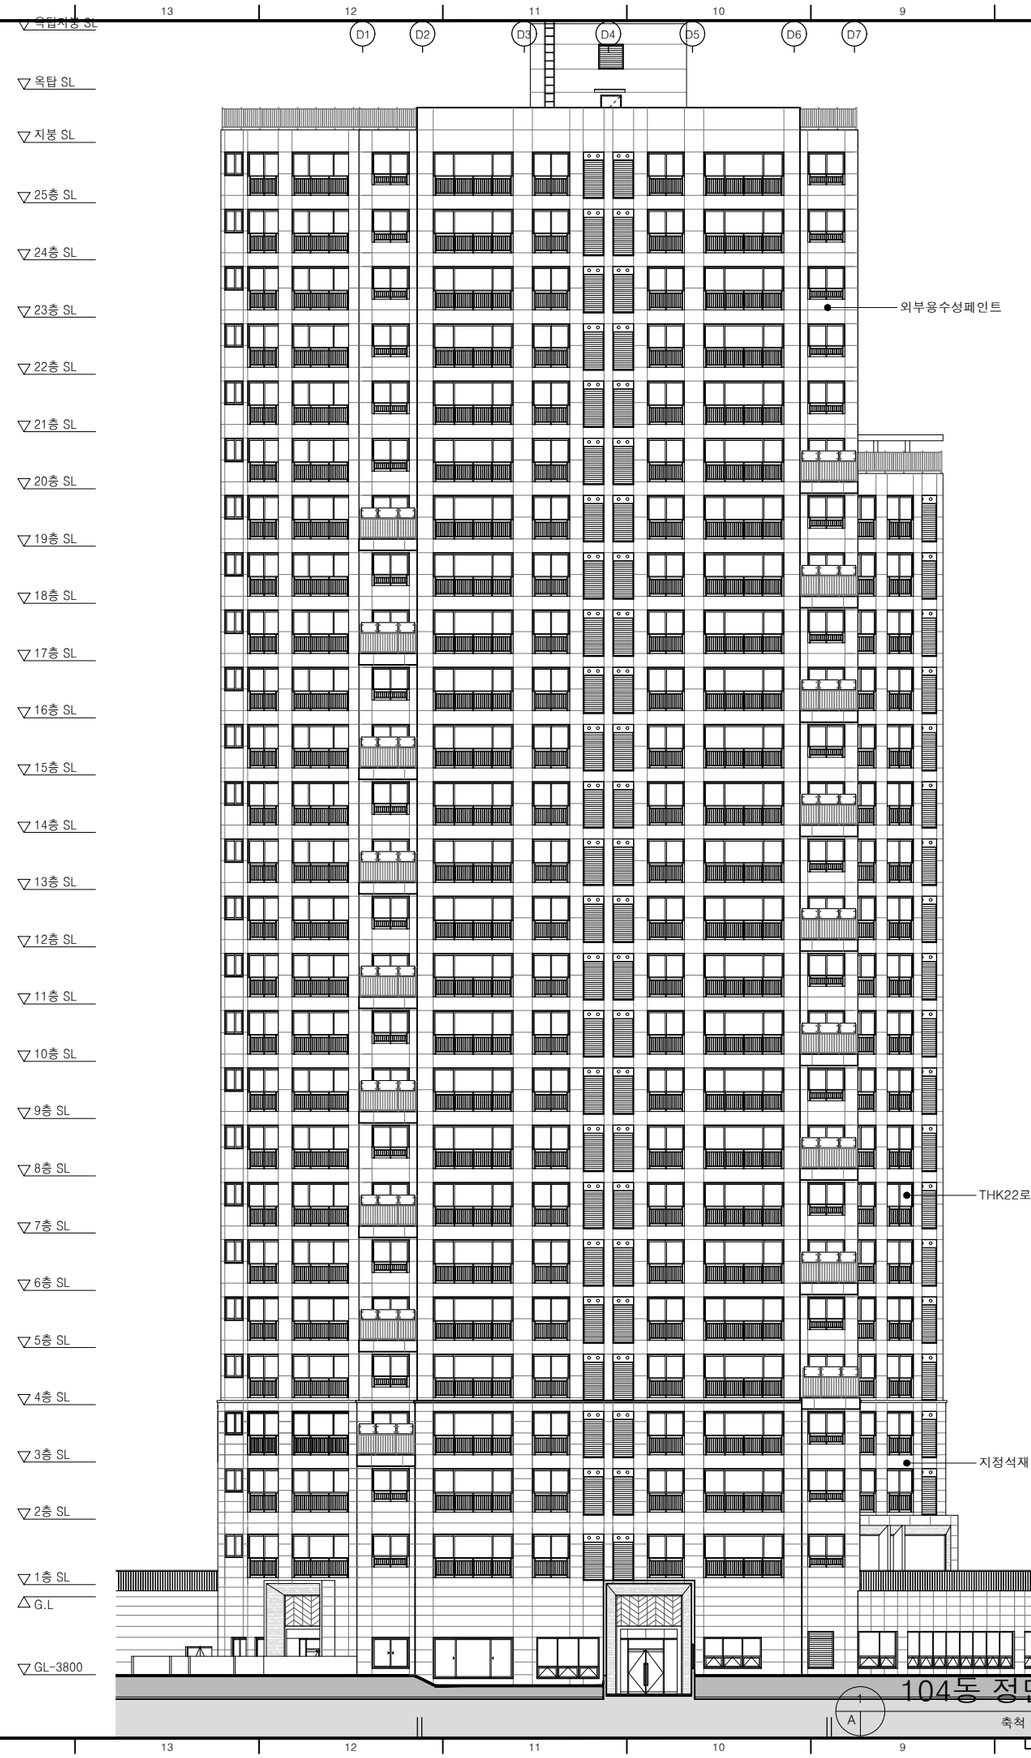

1 A 104동 정면도

축척 = 1/150

2 A 104동 우측면도

축척 = 1/150

사업번호 PROJECT NO.

사업명 PROJECT TITLE

수색4재정비촉진구역
주택재개발 정비사업

KEY PLAN

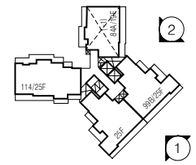

NOTE

1. 1층 바닥 LEVEL
   1SL±0 = 1FL±0 = GL±0 = EL+28.60
2. 지붕 난간의 형태 및 설치위치는 안전성과 입면디자인을 고려하여 변경가능함.
3. 지붕의 재료, 형태, 구조는 실시공시 변경될 수 있음.
4. 지붕 및 옥탑구조물의 형태와 구조는 실시공시 변경될 수 있음.
5. 외벽 및 측벽 문양은 실시공시 변경될 수 있음
6. 입면의 줄눈 및 마감선은 실시공시 변경될 수 있음.
7. 저층부 석재마감 및 입면 마감 색상, 재료에 대한 모든 기준은 특화도면을 우선 적용함.

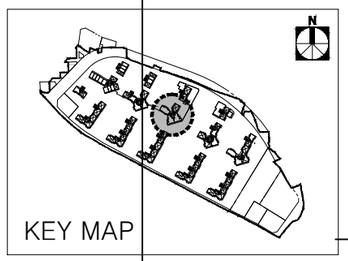

수정번호 REV. NO.	일 자 DATE	내 용 DESCRIPTION	승 인 CHKD
△			
△			
△			
△			

설계 DESIGNED BY

검토 CHECKED BY
최 진 규

심사 SUMMITED BY
정 호 혁

승인 APPROVED BY
이 승 준

일자 DATE
2019.08

도면명 DRAWING TITLE
104동 정면도,우측면도

축 척 SCALE
A1: 1/150
A3: 1/300

도면번호 DRAWING NO.
A-341

일련번호 SHEET NO. △ REV. NO.

HAUD
㈜하우드엔지니어링
종합건축사사무소
Architects, Planners & Engineers
TEL. 82 2 140 4400, SEOUL, KOREA

옥탑지붕 SL
옥탑 SL
지붕 SL
25층 SL
24층 SL
23층 SL
22층 SL
21층 SL
20층 SL
19층 SL
18층 SL
17층 SL
16층 SL
15층 SL
14층 SL
13층 SL
12층 SL
11층 SL
10층 SL
9층 SL
8층 SL
7층 SL
6층 SL
5층 SL
4층 SL
3층 SL
2층 SL
1층 SL
G.L
GL-3800

외부용수성페인트
지정석재

1 A 104동 배면도
축척 = 1/150

THK22로이복층유리
외부용수성페인트
지정석재

2 A 104동 좌측면도
축척 = 1/150

사업번호 PROJECT NO.

사업명 PROJECT TITLE

수색4재정비촉진구역
주택재개발 정비사업

KEY PLAN

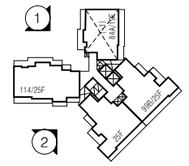

NOTE

1. 1층 바닥 LEVEL
   1SL±0 = 1FL±0 = GL±0 = EL+28.60
2. 지붕 난간의 형태 및 설치위치는 안전성과 입면디자인을 고려하여 변경가능함.
3. 지붕의 재료, 형태, 구조는 실시공시 변경될 수 있음.
4. 지붕 및 옥탑구조물의 형태와 구조는 실시공시 변경될 수 있음.
5. 외벽 및 측벽 문양은 실시공시 변경될 수 있음
6. 입면의 줄눈 및 마감선은 실시공시 변경될 수 있음.
7. 저층부 석재마감 및 입면 마감 색상, 재료에 대한 모든 기준은 특화도면을 우선 적용함.

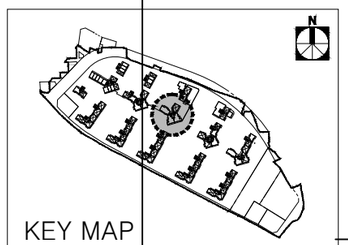

수정번호 REV. NO.	일 자 DATE	내 용 DESCRIPTION	승 인 CHKD
△			
△			
△			
△			

설계 DESIGNED BY

검토 CHECKED BY
최 진 규

심사 SUMMITED BY
정 호 혁

승인 APPROVED BY
이 승 준

일자 DATE
2019.08

도면명 DRAWING TITLE
104동 배면도,좌측면도

축 척 SCALE
A1: 1/150
A3: 1/300

도면번호 DRAWING NO.
A-342

일련번호 SHEET NO.

△ REV. NO.

HAUD
(주)하우드엔지니어링
종합건축사사무소
Architects, Planners & Engineers
TEL. 82 2 140 4400, SEOUL, KOREA

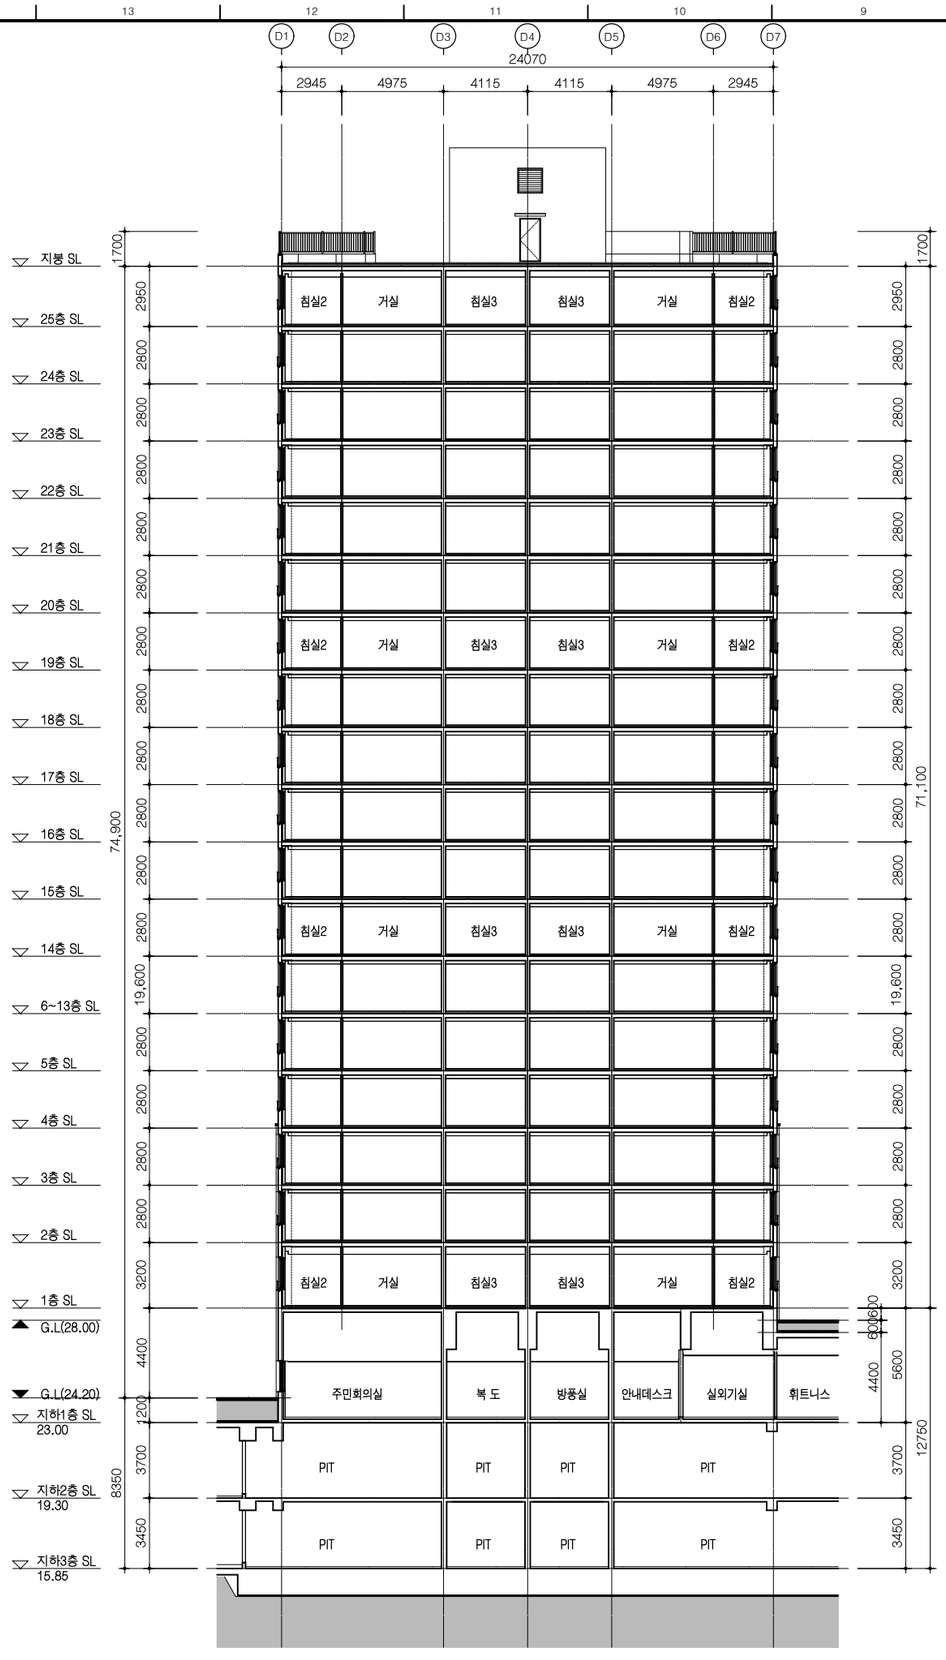

1 A 104동 종단면도

축척 = 1/150

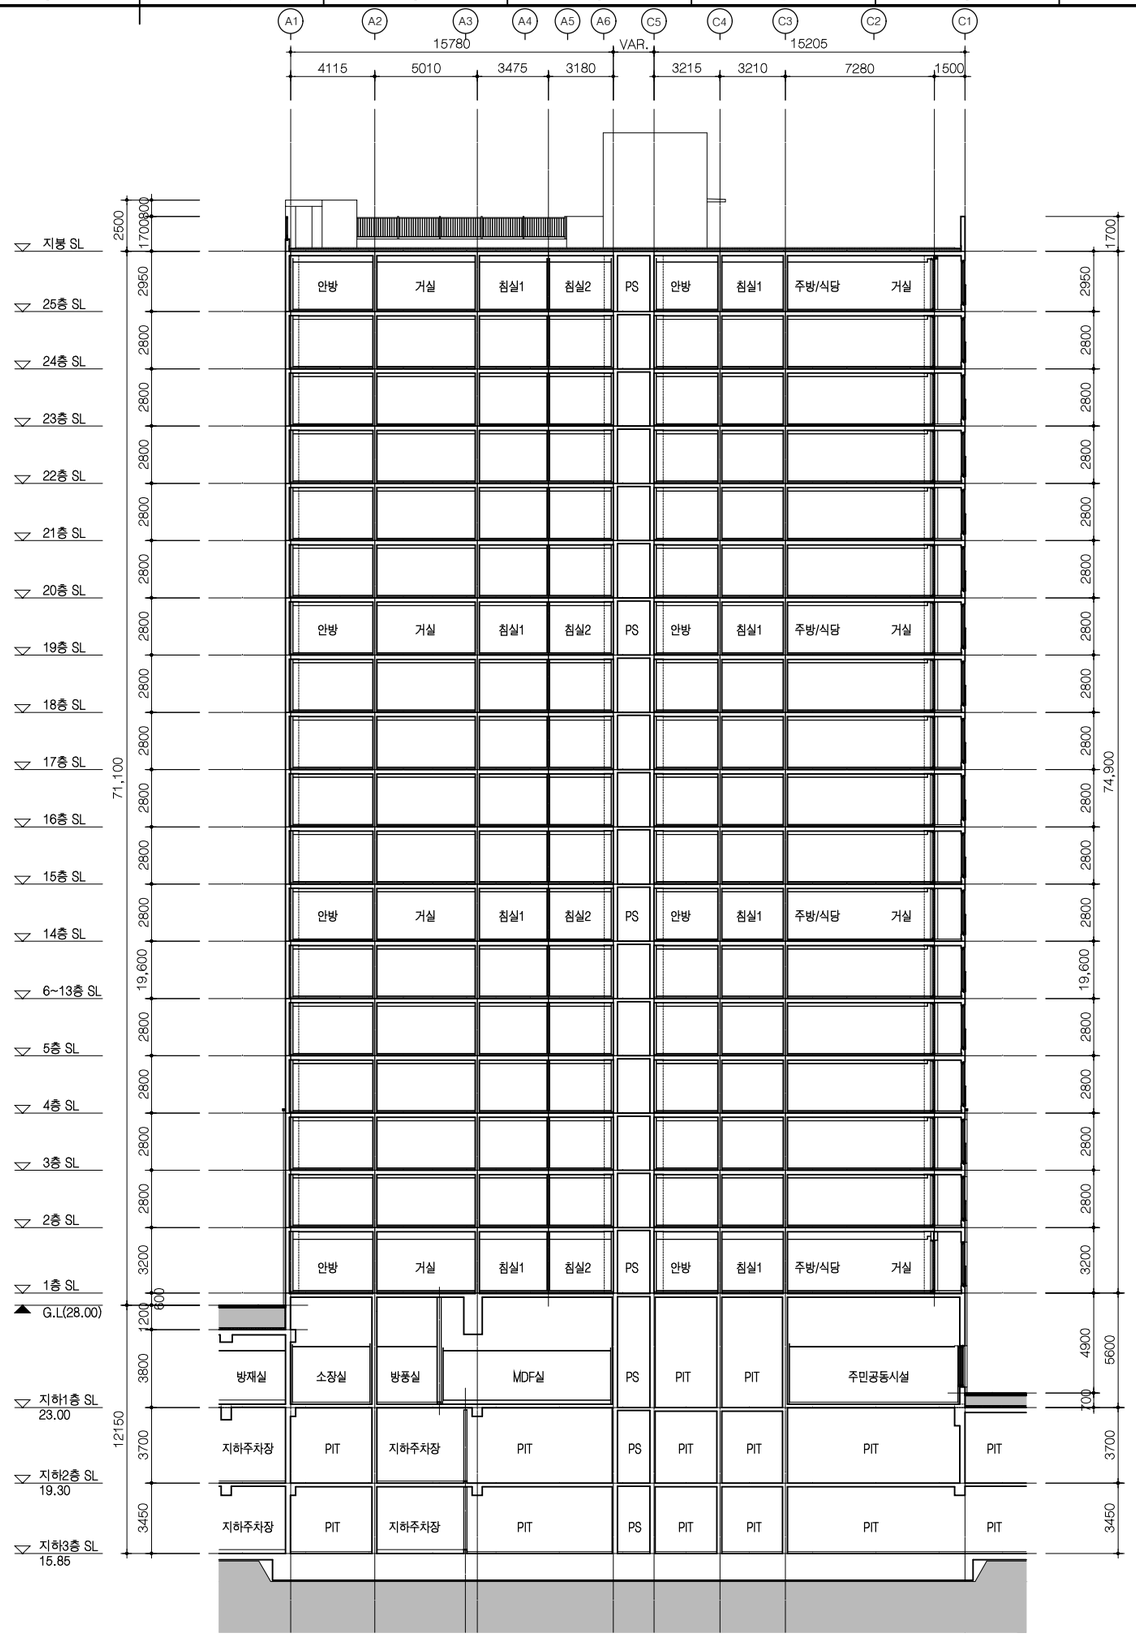

2 A 104동 횡단면도

축척 = 1/150

사업번호 PROJECT NO.

사업명 PROJECT TITLE

수색4재정비촉진구역
주택재개발 정비사업

KEY PLAN

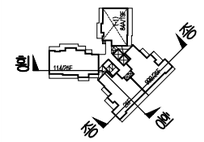

NOTE

수정번호 REV. NO.	일 자 DATE	내 용 DESCRIPTION	승 인 CHKD
△			
△			
△			
△			

설계 DESIGNED BY

검토 CHECKED BY
최 진 규

심사 SUMMITED BY
정 호 혁

승인 APPROVED BY
이 승 준

일자 DATE
2019.08

도면명 DRAWING TITLE
104동 종,횡단면도

축 척 SCALE
A1: 1/150
A3: 1/300

도면번호 DRAWING NO.
A-343

일련번호 SHEET NO.

REV. NO. △

HAUD
(주)하우드엔지니어링
종합건축사사무소
Architects, Planners & Engineers
TEL. 02 2140 4400, SEOUL, KOREA

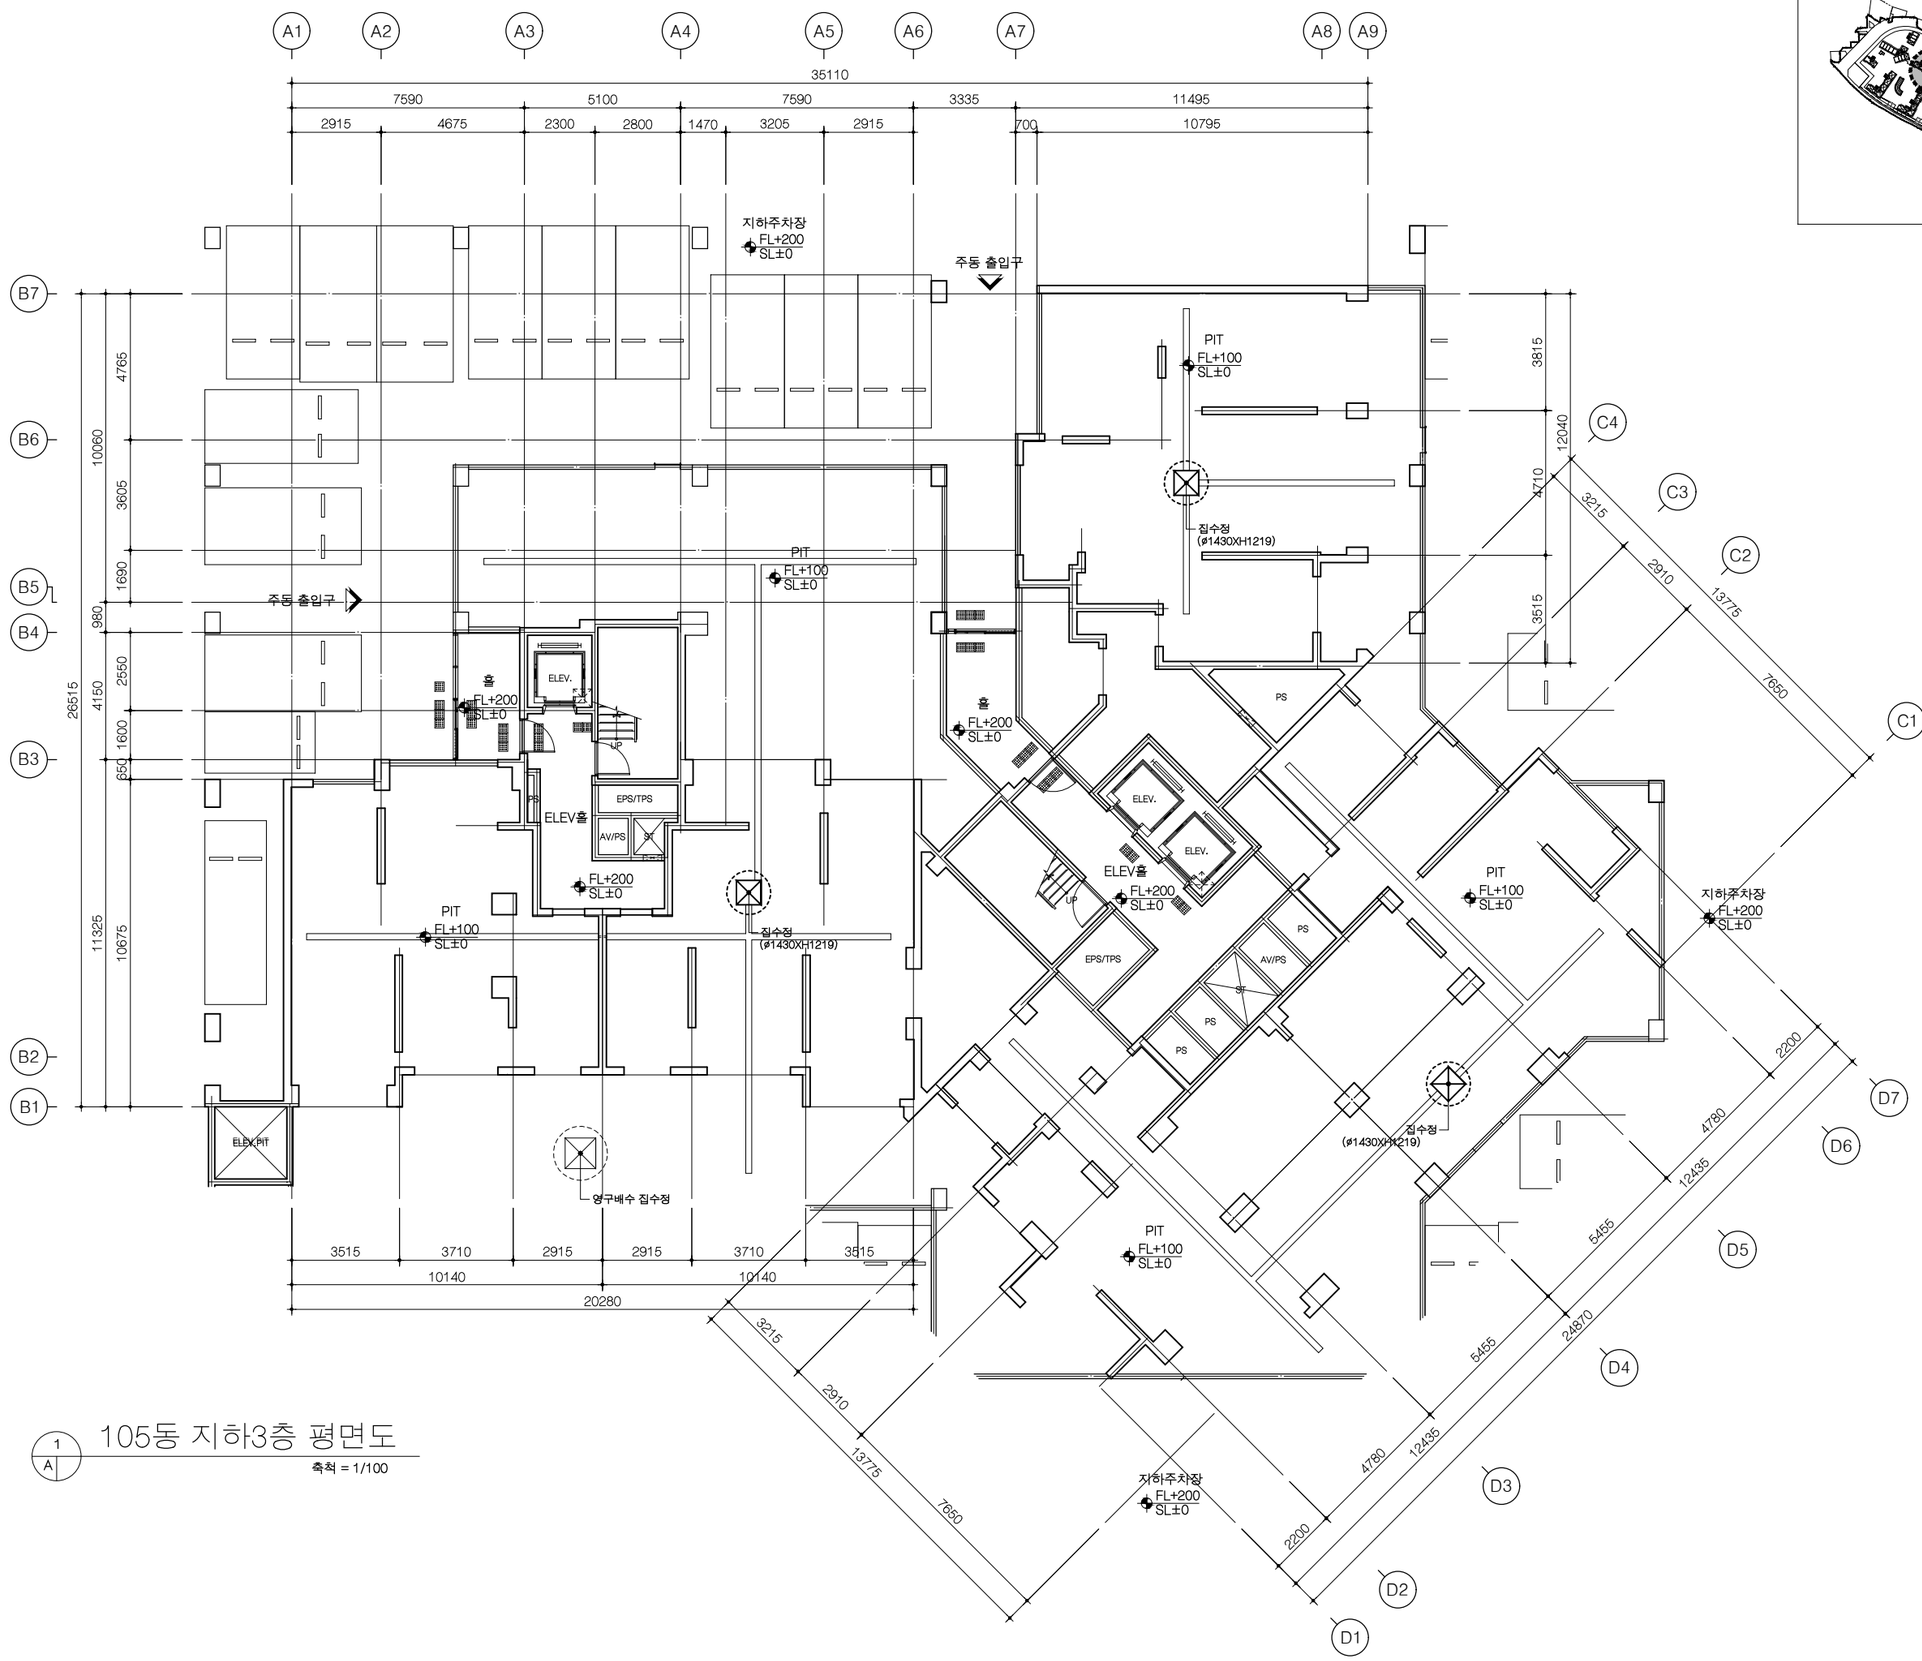

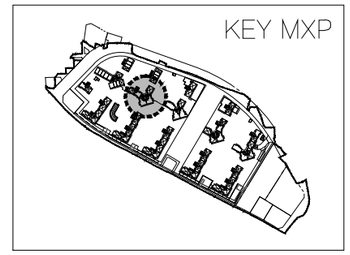

사업번호 PROJECT NO.

사업명 PROJECT TITLE

수색4재정비촉진구역
주택재개발 정비사업

KEY PLAN

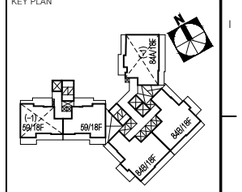

NOTE

1. 지하층 무근 콘크리트는 실시공시 THK80~120 범위로 변동이 있을수 있음.(SLOPE)
2. ELEV홀에 면한부위는 1.0B 조적쌓기임.
3. 지하주차장의 블록쌓기 기준은 높이가 3.6m이하인 경우 4인치 보강블록쌓기가 기준임 (단, 5.4m이하는 6인치쌓기, 5.4m초과는 8인치쌓기가 기준임)
4. ELEV.PIT 집수정은 (600X600X600)임.
5. 주차장 내의 창호는 주차장 창호도 참조.
6. 주차장 집수정 및 영구배수 집수정의 크기 및 위치는 지하주차장 평면도를 참조 할 것.
   ☒ : 주차장 집수정
   ☒ : 영구배수 집수정

********** 지하3층 바닥LEVEL
B3SL±0 = B3FL±0 = EL+15.85

수정번호 REV. NO.	일 자 DATE	내 용 DESCRIPTION	승 인 CHKD
△			
△			
△			
△			

설계 DESIGNED BY

검토 CHECKED BY
최 진 규

심사 SUMMITED BY
정 호 혁

승인 APPROVED BY
이 승 준

일자 DATE
2019.08

도면명 DRAWING TITLE
105동
지하3층 평면도

축 척 SCALE
A1: 1/100
A3: 1/200

도면번호 DRAWING NO.
A-351

일련번호 SHEET NO.

△ REV. NO.

HAUD
㈜하우드엔지니어링
종합건축사사무소
Architects, Planners & Engineers
TEL. 02 2140 4466, SEOUL, KOREA

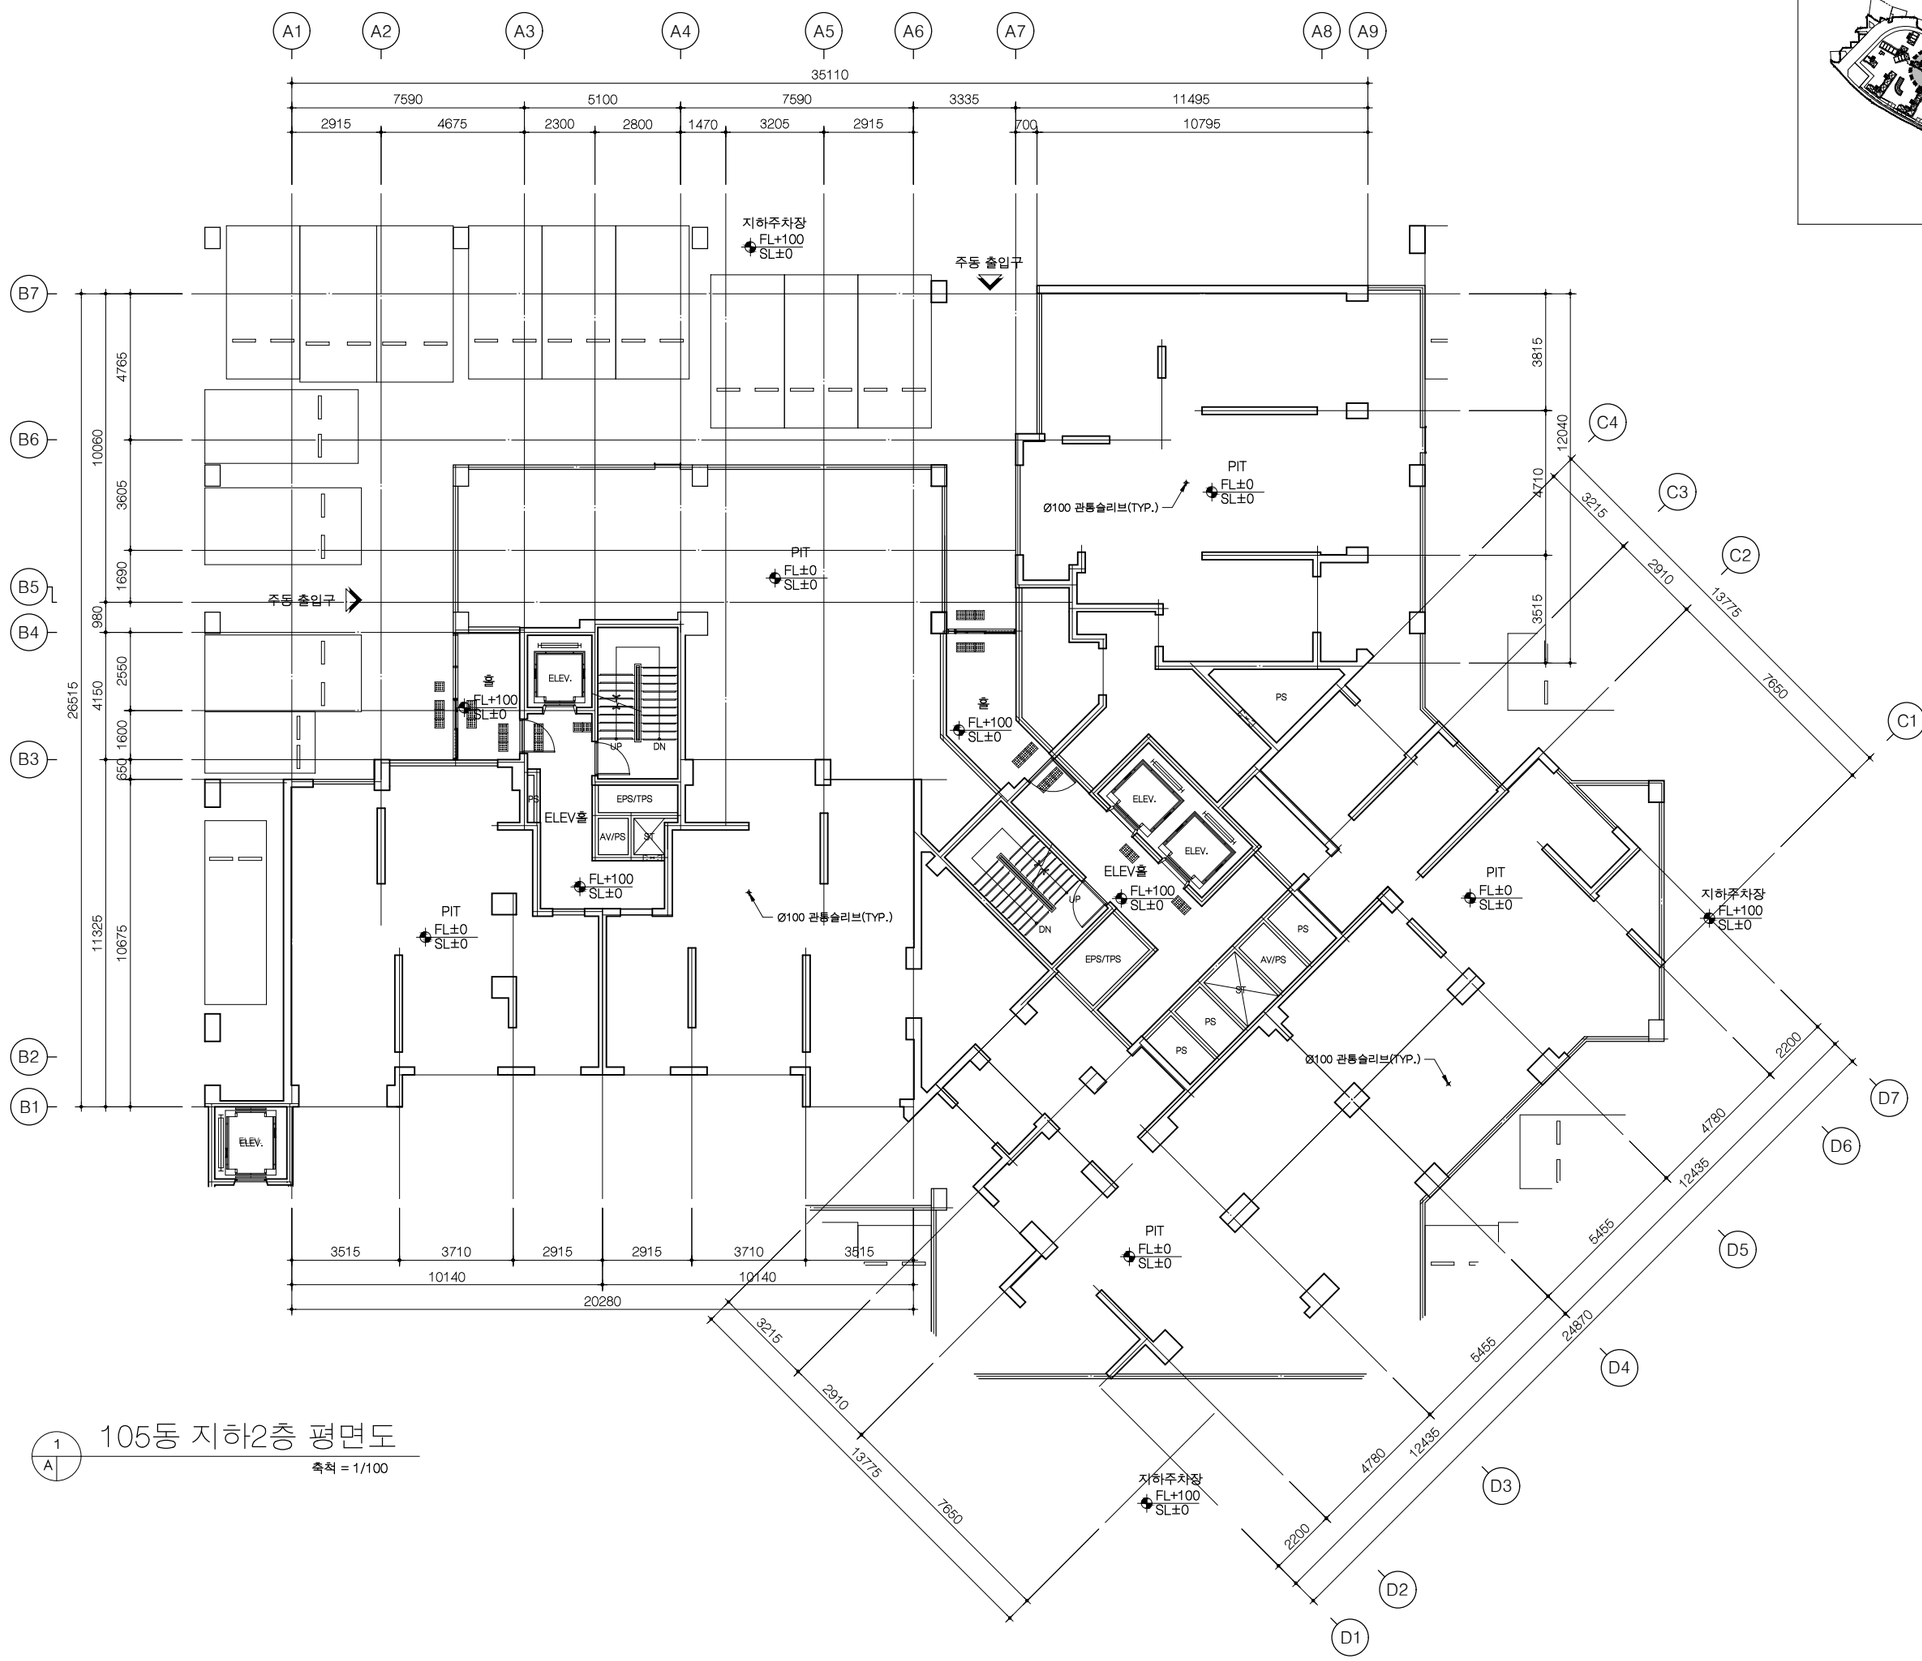

1 / A 105동 지하2층 평면도

축척 = 1/100

KEY MXP

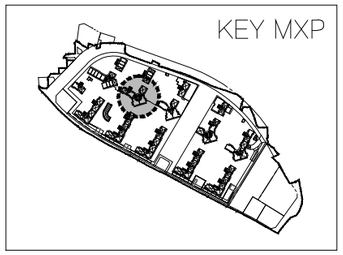

사업번호 PROJECT NO.

사업명 PROJECT TITLE

수색4재정비촉진구역
주택재개발 정비사업

KEY PLAN

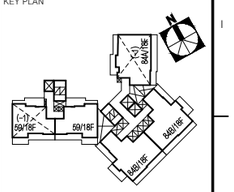

NOTE

1. 지하주차장의 ELEV홀에 면한부위는 1.0B 조적쌓기임.
2. 지하주차장의 블록쌓기 기준은 높이가 3.6m이하인 경우 4인치 보강블록쌓기가 기준임 (단, 5.4m이하는 6인치쌓기, 5.4m초과는 8인치쌓기가 기준임)
3. 주차장 내의 창호는 주차장 창호도 참조.

**** 지하2층 바닥LEVEL
D2SL±0 = D2FL±0 = EL+19.30

수정번호 REV. NO.	일 자 DATE	내 용 DESCRIPTION	승 인 CHKD
△			
△			
△			
△			

설계 DESIGNED BY

검토 CHECKED BY
최 진 규

심사 SUMMITED BY
정 호 혁

승인 APPROVED BY
이 승 준

일자 DATE
2019.08

도면명 DRAWING TITLE
105동
지하2층 평면도

축 척 SCALE
A1: 1/100
A3: 1/200

도면번호 DRAWING NO.
A-352

일련번호 SHEET NO.

△ REV. NO.

HAUD
㈜하우드엔지니어링
종합건축사사무소
Architects, Planners & Engineers
TEL. 02 2140 4466, SEOUL, KOREA

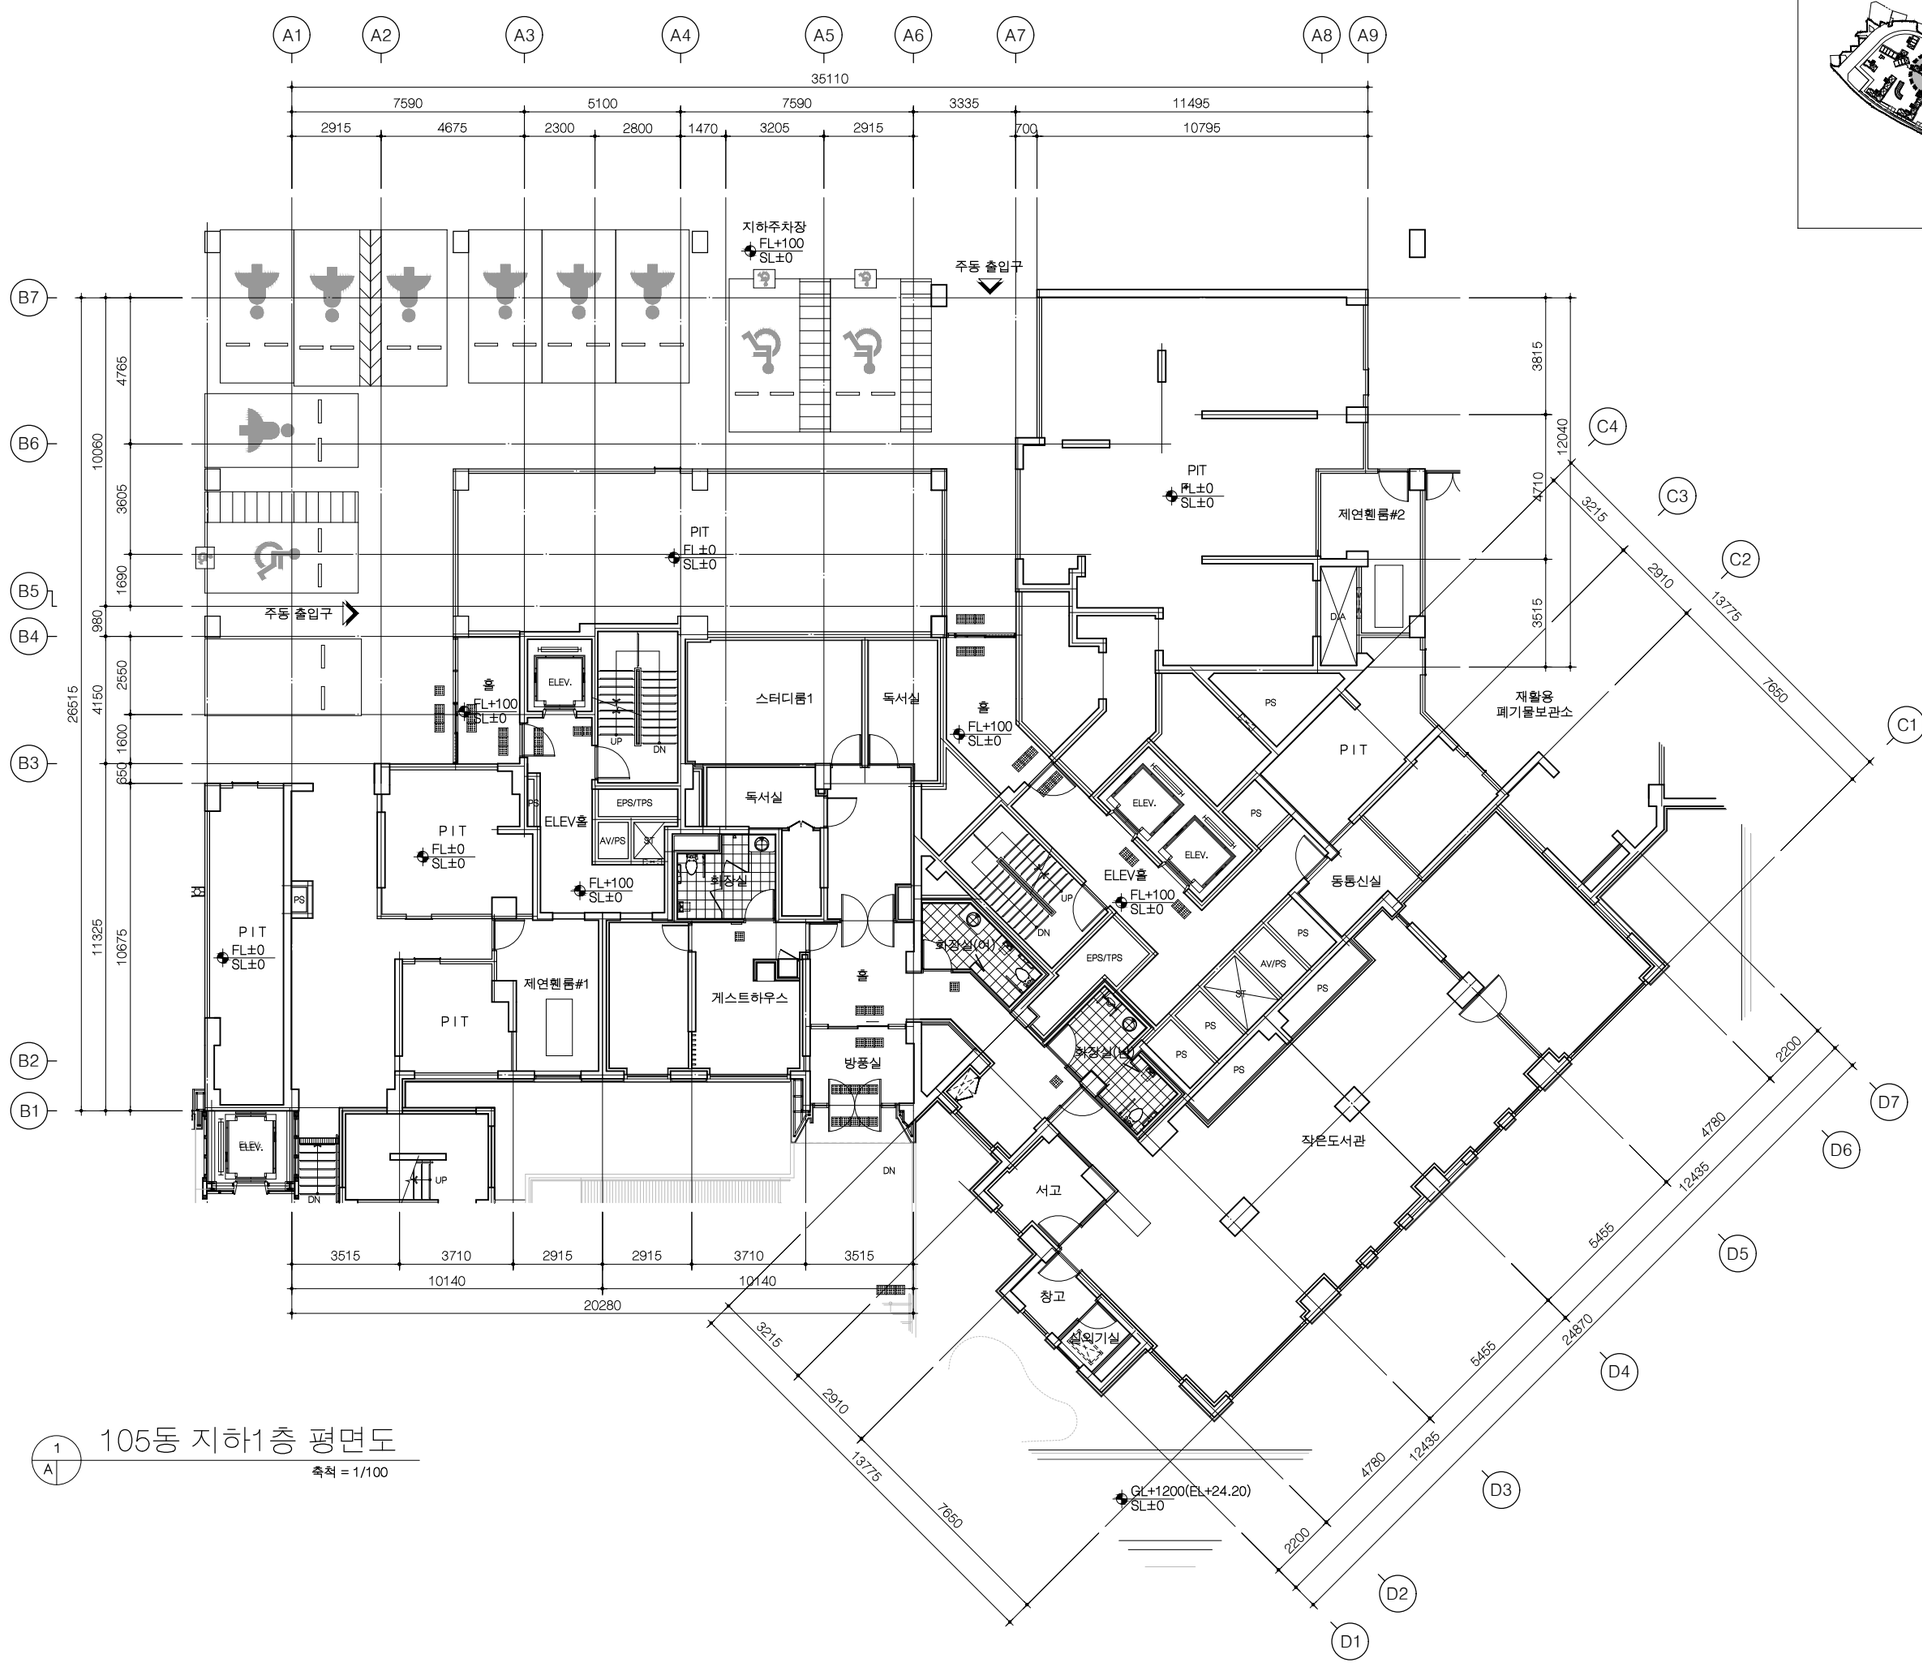

1 A 105동 지하1층 평면도

축척 = 1/100

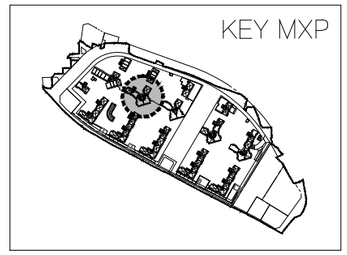

사업번호 PROJECT NO.

사업명 PROJECT TITLE

수색4재정비촉진구역
주택재개발 정비사업

KEY PLAN

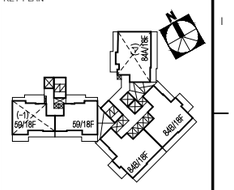

NOTE

1. 지하주차장의 ELEV홀에 면한부위는 1.0B 조적쌓기임.
2. 지하주차장의 블록쌓기 기준은 높이가 3.6m이하인 경우 4인치 보강블록쌓기가 기준임 (단, 5.4m이하는 6인치쌓기, 5.4m초과는 8인치쌓기가 기준임)
3. 주차장 내의 창호는 주차장 창호도 참조.

• 지하1층 바닥LEVEL
D1SL±0 = D1FL±0 = EL+23.00

수정번호 REV. NO.	일 자 DATE	내 용 DESCRIPTION	승 인 CHKD

설계 DESIGNED BY

검토 CHECKED BY
최 진 규

심사 SUMMITED BY
정 호 혁

승인 APPROVED BY
이 승 준

일자 DATE
2019.08

도면명 DRAWING TITLE
105동
지하1층 평면도

축 척 SCALE
A1: 1/100
A3: 1/200

도면번호 DRAWING NO.
A-353

일련번호 SHEET NO.

REV. NO.

HAUD
㈜하우드랜지니어링
종합건축사사무소
Architects, Planners & Engineers
TEL. 02 2140 4400, SEOUL, KOREA

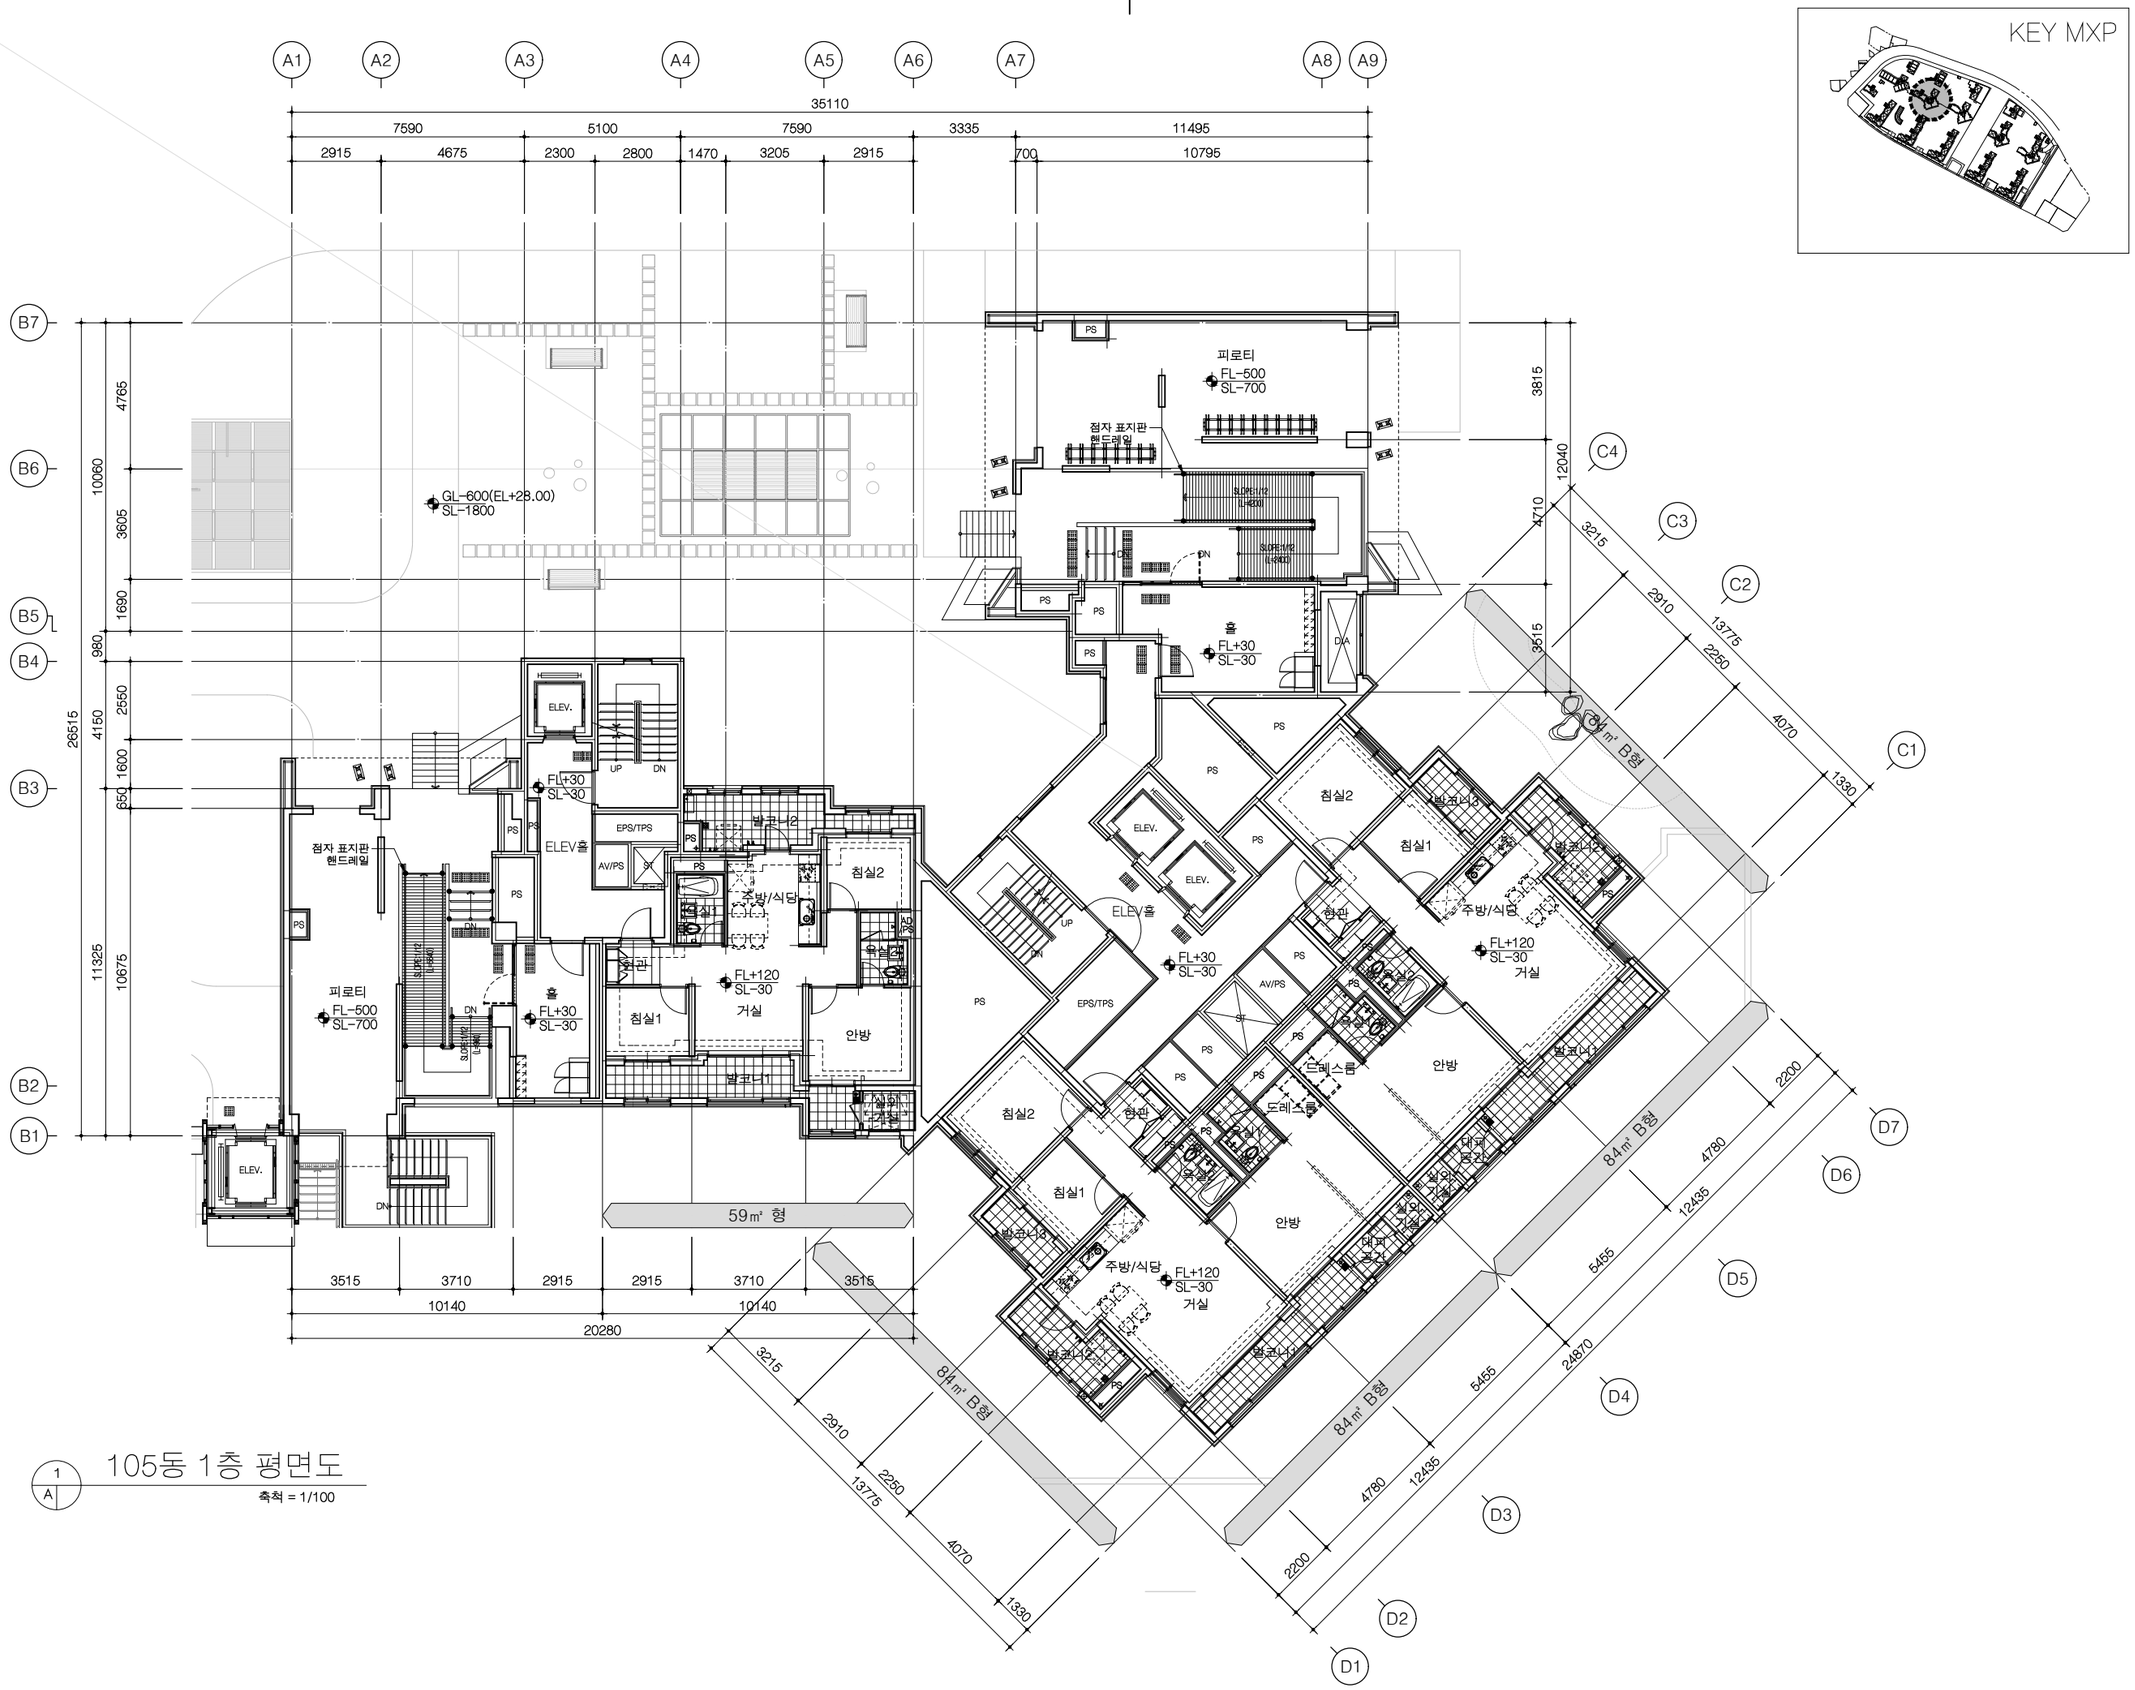

1 / A 105동 1층 평면도

축척 = 1/100

KEY MXP

사업번호 PROJECT NO.

사업명 PROJECT TITLE

수색4재정비촉진구역
주택재개발 정비사업

KEY PLAN

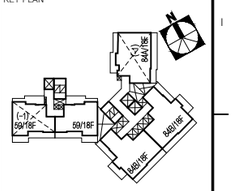

NOTE

1. 본 도면은 발코니 확장전를 기준으로 작성됨.
2. 지붕층 난간의 형태와 설치 위치는 안전성과 입면디자인을 고려하여 변경 가능함.
3. 지붕의 재료, 형태, 구조는 실시공 시 변경 될 수 있음.
4. 지붕 및 옥탑 구조물의 형태와 구조는 실시공 시 변경될 수 있음.
5. 옥상 출눈의 간격은 실시공 시 변경될 수 있음.
6. 옥상 출눈 틈에 실란트 시공되지 않음
7. 우편물 수취함 설치 위치는 변경될 수 있음

* 1층 바닥LEVEL
1SL±0 = 1FL±0 = GL±0 = EL+28.60
GL-600 = EL+28.00(토목도면 참조)

수정번호 REV. NO.	일 자 DATE	내 용 DESCRIPTION	승 인 CHKD
△			
△			
△			
△			

설계 DESIGNED BY

검토 CHECKED BY
최 진 규

심사 SUMMITED BY
정 호 혁

승인 APPROVED BY
이 승 준

일자 DATE
2019.08

도면명 DRAWING TITLE
105동
1층 평면도

축 척 SCALE
A1: 1/100
A3: 1/200

도면번호 DRAWING NO.
A-354

일련번호 SHEET NO.

REV. NO. △

HAUD
(주)하우드엔지니어링
종합건축사사무소
Architects, Planners & Engineers
TEL. 02 3143 4400, SEOUL, KOREA

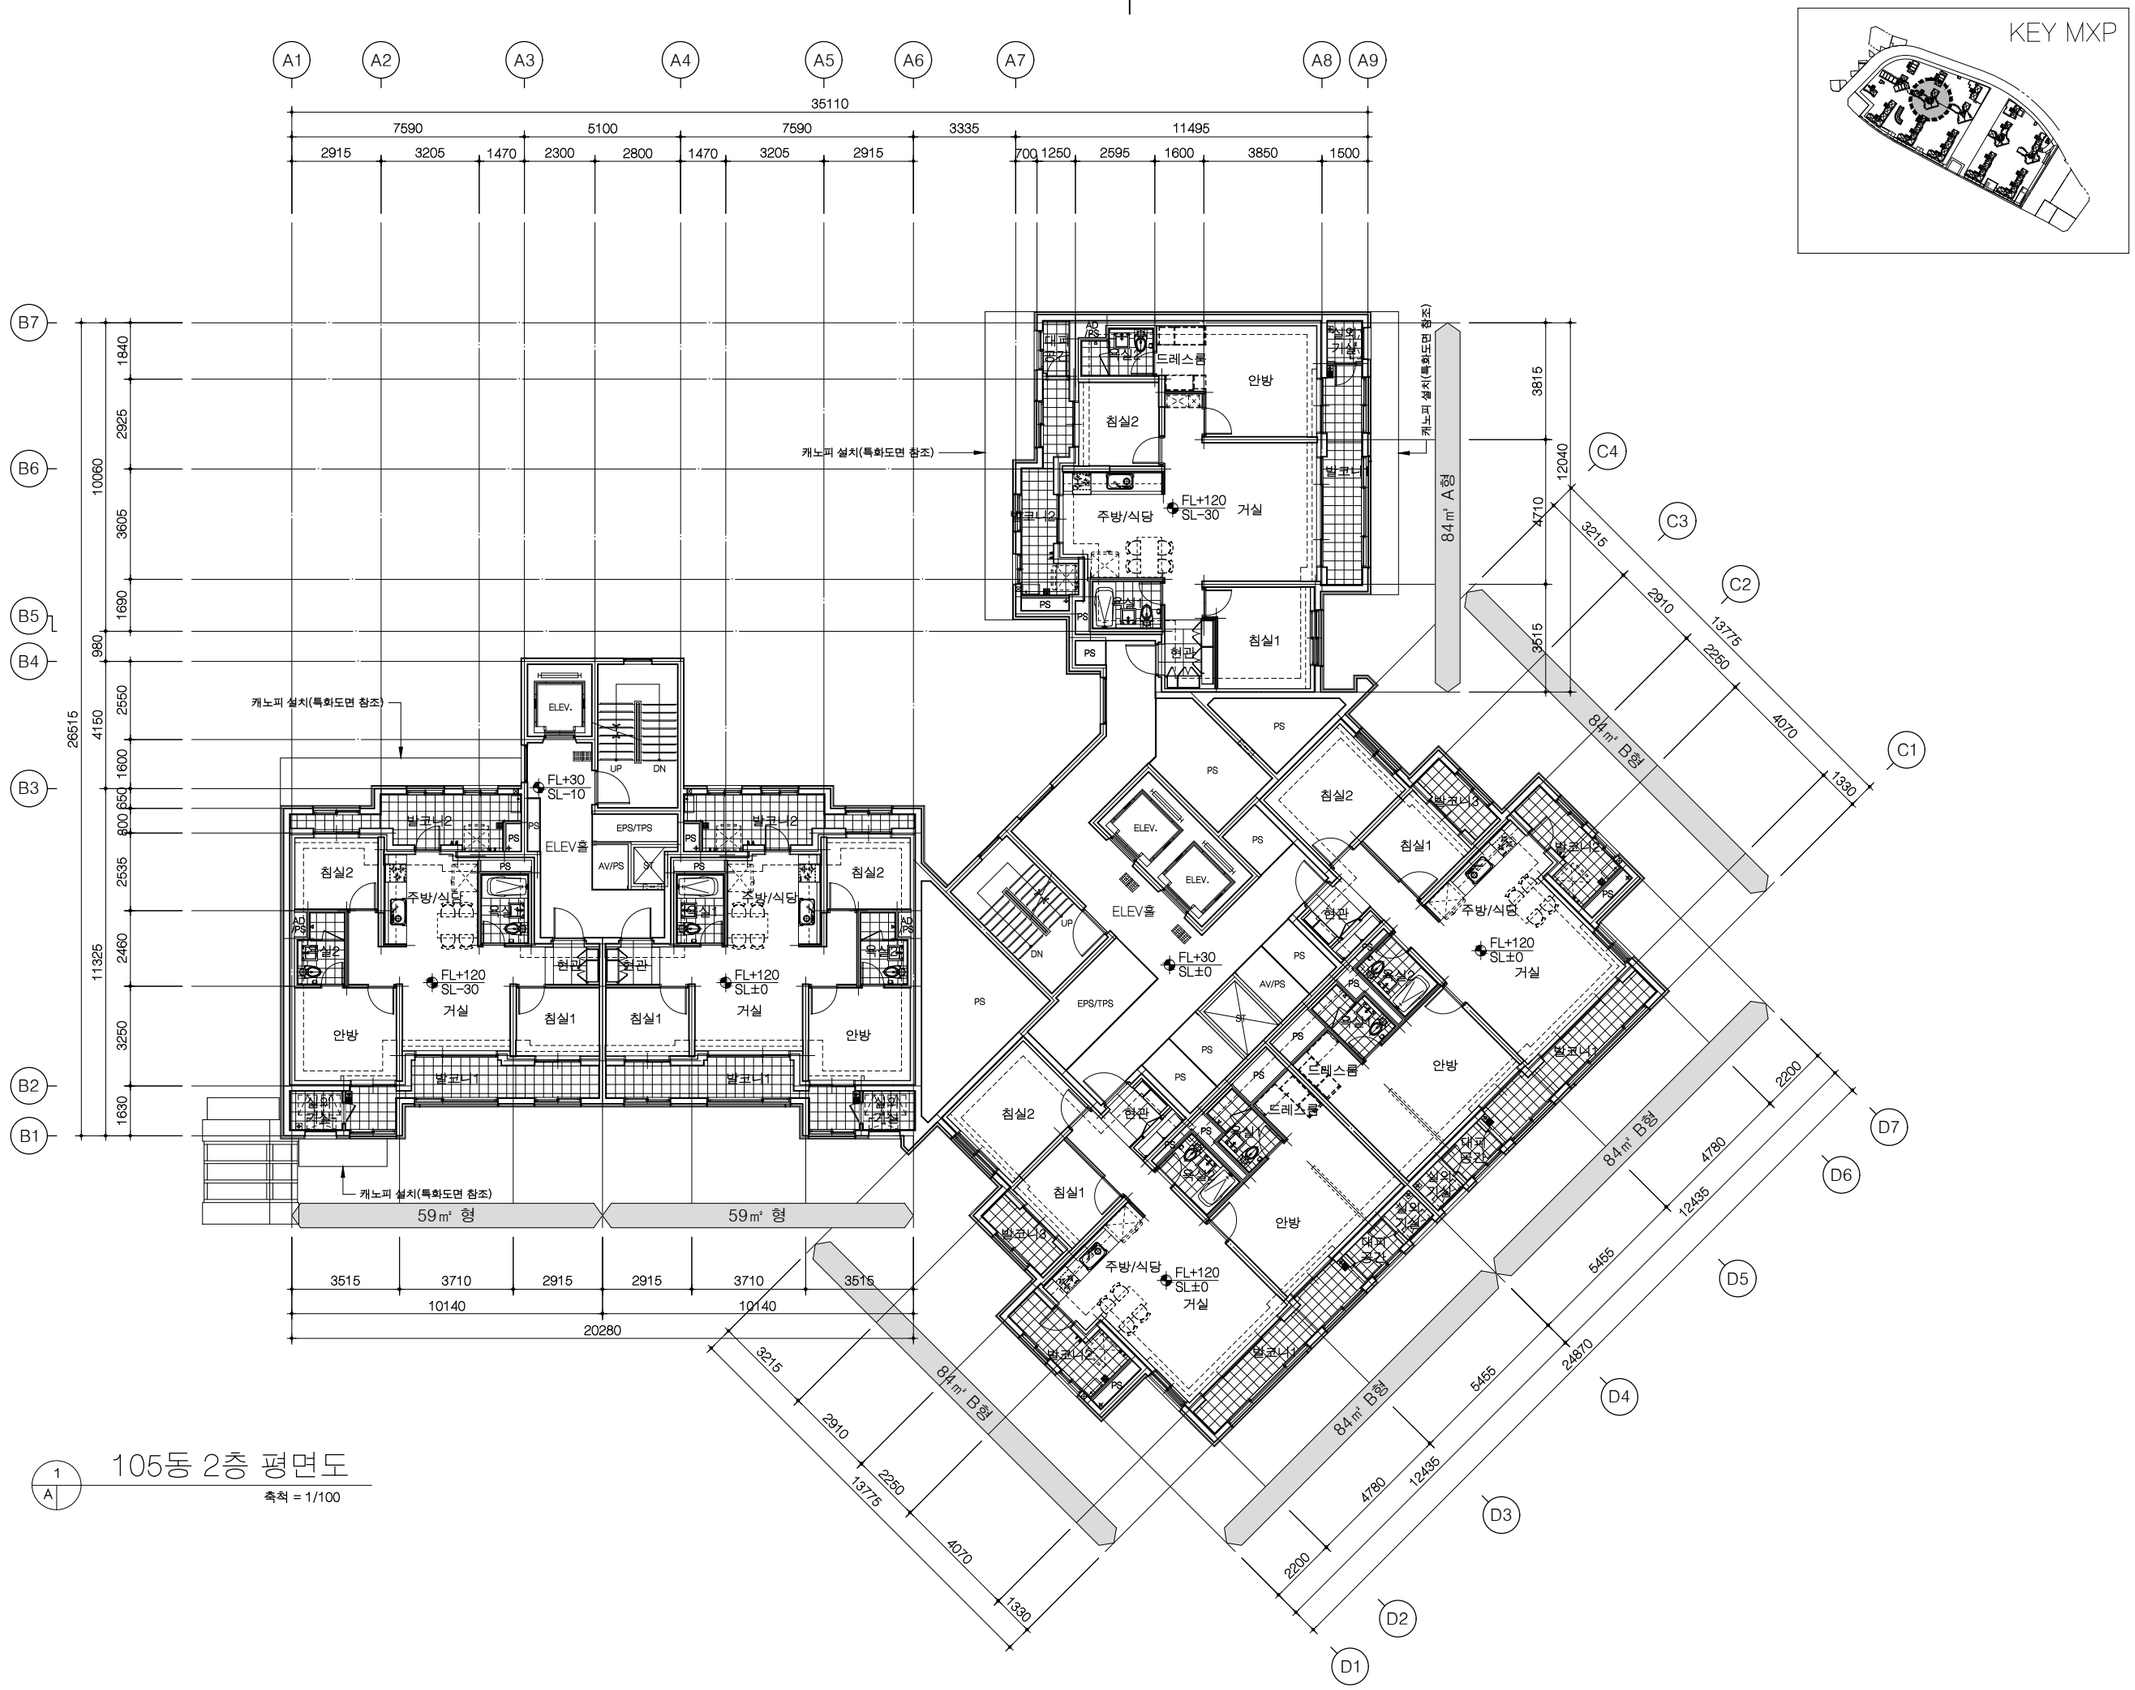

1 A 105동 2층 평면도

축척 = 1/100

사업번호 PROJECT NO.

사업명 PROJECT TITLE

수색4재정비촉진구역
주택재개발 정비사업

KEY PLAN

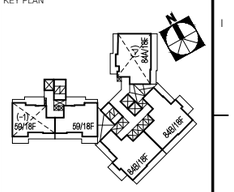

NOTE

1. 본 도면은 발코니 확장전를 기준으로 작성됨.
2. 지붕층 난간의 형태와 설치 위치는 안전성과 입면디자인을 고려하여 변경 가능함.
3. 지붕의 재료, 형태, 구조는 실시공 시 변경 될 수 있음.
4. 지붕 및 옥탑 구조물의 형태와 구조는 실시공 시 변경될 수 있음.
5. 옥상 출눈의 간격은 실시공 시 변경될 수 있음.
6. 옥상 출눈 틈에 실란트 시공되지 않음
7. 우편물 수취함 설치 위치는 변경될 수 있음
8. 오픈형 발코니 3층이상 ~ 20층이하 설치

2층 바닥LEVEL
2SL±0 = 2FL±0 = EL+31.80

수정번호 REV. NO.	일 자 DATE	내 용 DESCRIPTION	승 인 CHKD

설계 DESIGNED BY

검토 CHECKED BY
최 진 규

심사 SUMMITED BY
정 호 혁

승인 APPROVED BY
이 승 준

일자 DATE
2019.08

도면명 DRAWING TITLE
105동
2층 평면도

축 척 SCALE
A1: 1/100
A3: 1/200

도면번호 DRAWING NO.
A-355

일련번호 SHEET NO.

REV. NO.

HAUD
(주)하우드엔지니어링
종합건축사사무소
Architects, Planners & Engineers
TEL. 02 2149 4400, SEOUL, KOREA

1 A 105동 3층~18층 평면도

축척 = 1/100

KEY MXP

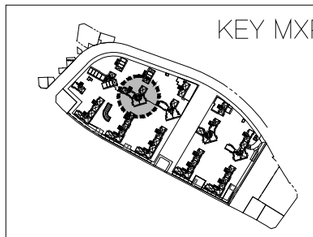

사업번호 PROJECT NO.

사업명 PROJECT TITLE

수색4재정비촉진구역
주택재개발 정비사업

KEY PLAN

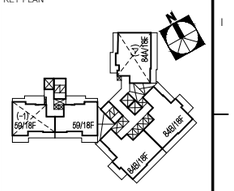

NOTE

1. 본 도면은 발코니 확장전를 기준으로 작성됨.
2. 지붕층 난간의 형태와 설치 위치는 안전성과 입면디자인을 고려하여 변경 가능함.
3. 지붕의 재료, 형태, 구조는 실시공 시 변경 될 수 있음.
4. 지붕 및 옥탑 구조물의 형태와 구조는 실시공 시 변경될 수 있음.
5. 옥상 출눈의 간격은 실시공 시 변경될 수 있음.
6. 옥상 출눈 틈에 실란트 시공되지 않음
7. 우편물 수취함 설치 위치는 변경될 수 있음
8. 오픈형 발코니 3층이상 ~ 20층이하 설치

수정번호 REV. NO.	일 자 DATE	내 용 DESCRIPTION	승 인 CHKD

설계 DESIGNED BY

검토 CHECKED BY
최 진 규

심사 SUMMITED BY
정 호 혁

승인 APPROVED BY
이 승 준

일자 DATE
2019.08

도면명 DRAWING TITLE
105동
3층~18층 평면도

축 척 SCALE
A1: 1/100
A3: 1/200

도면번호 DRAWING NO.
A-356

일련번호 SHEET NO.

REV. NO.

HAUD
(주)하우드엔지니어링
종합건축사사무소
Architects, Planners & Engineers
TEL. 02 2149 4400, SEOUL, KOREA

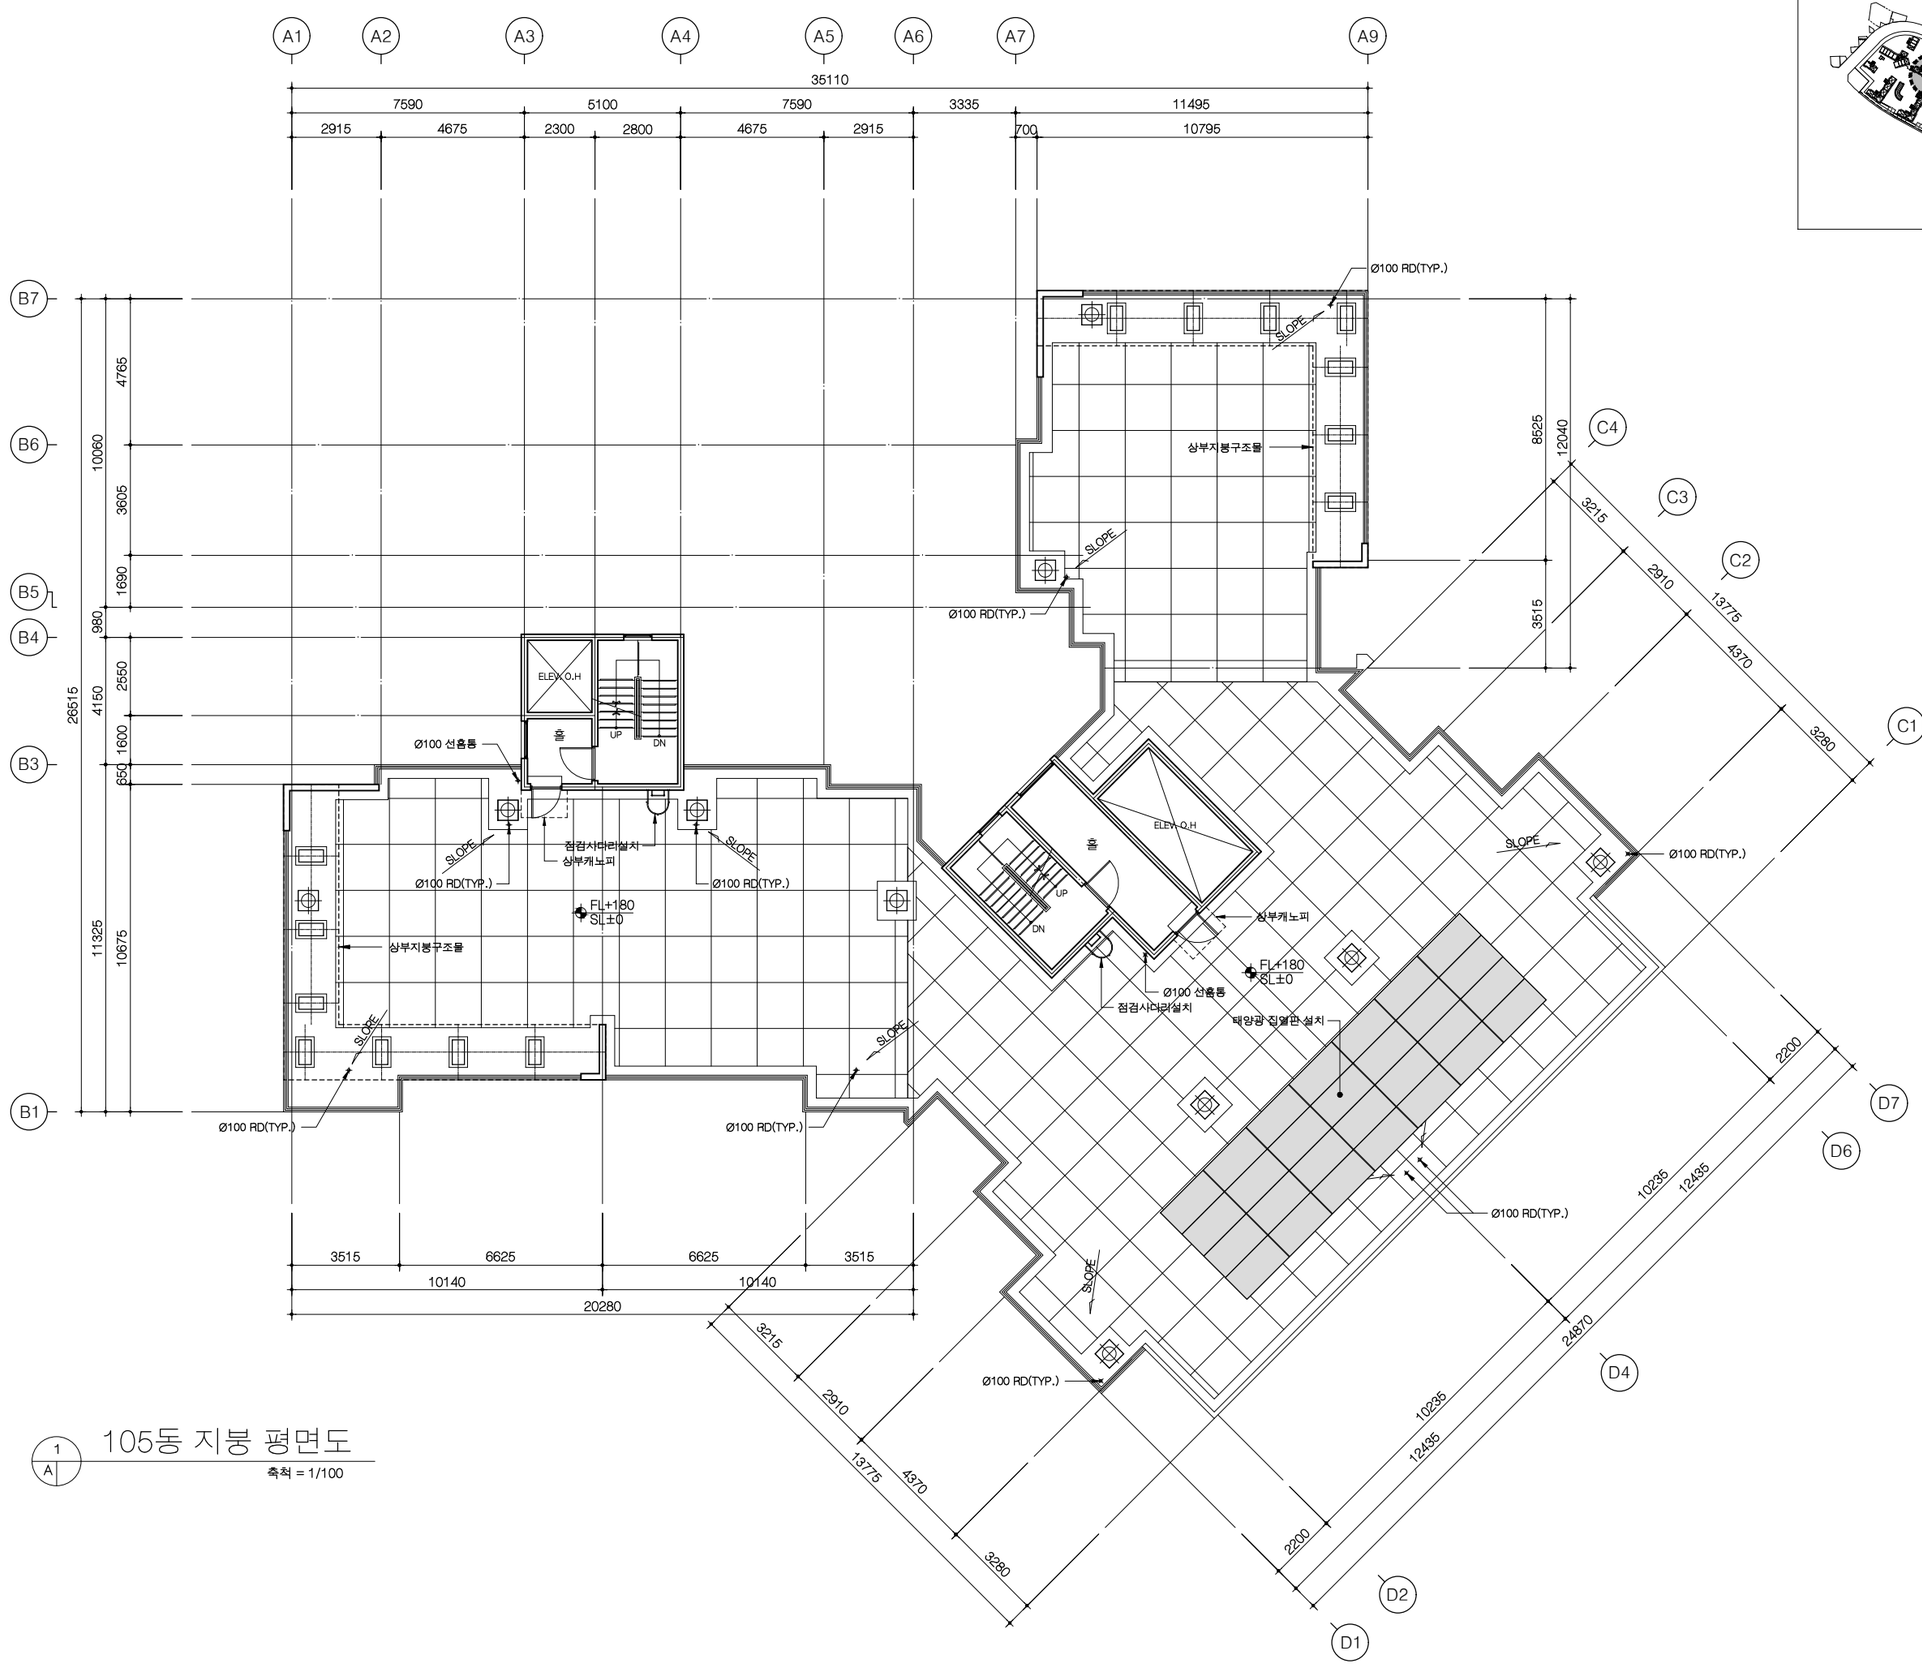

1 A 105동 지붕 평면도

축척 = 1/100

KEY MXP

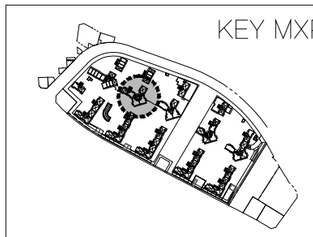

사업번호 PROJECT NO.

사업명 PROJECT TITLE

수색4재정비촉진구역
주택재개발 정비사업

KEY PLAN

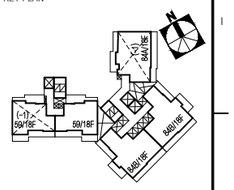

NOTE

1. 지붕바닥
   ① EXP. JOINT: 3000 X 3000
2. 본 평면도는 발코니확장전을 기준으로 작성됨
3. 재료마감은 실내,외 재료마감표 참조
4. 지붕 난간형태/설치위치는 안전성과 입면을 고려하여 실시공시 변경될 수 있음
5. 지붕재료 및 형태,구조는 실시공시 변경될수 있음
6. 지붕(옥탑지붕)의 배수드레인,환소용고리, 베기탑,점검사다리(점검구) 등의 설치위치/개소는 실시공시 변경될 수 있음
7. 옥상 상부구조물은 PC구조물 임.
8. 정화조 배기는 기계도서 참조

수정번호 REV. NO.	일 자 DATE	내 용 DESCRIPTION	승 인 CHKD

설계 DESIGNED BY

검토 CHECKED BY
최 진 규

심사 SUMMITED BY
정 호 혁

승인 APPROVED BY
이 승 준

일자 DATE
2019.08

도면명 DRAWING TITLE
105동
지붕 평면도

축 척 SCALE
A1: 1/100
A3: 1/200

도면번호 DRAWING NO.
A-357

일련번호 SHEET NO.

REV. NO.

HAUD
㈜하우드엔지니어링
종합건축사사무소
Architects, Planners & Engineers
TEL. 02 2140 4400, SEOUL, KOREA

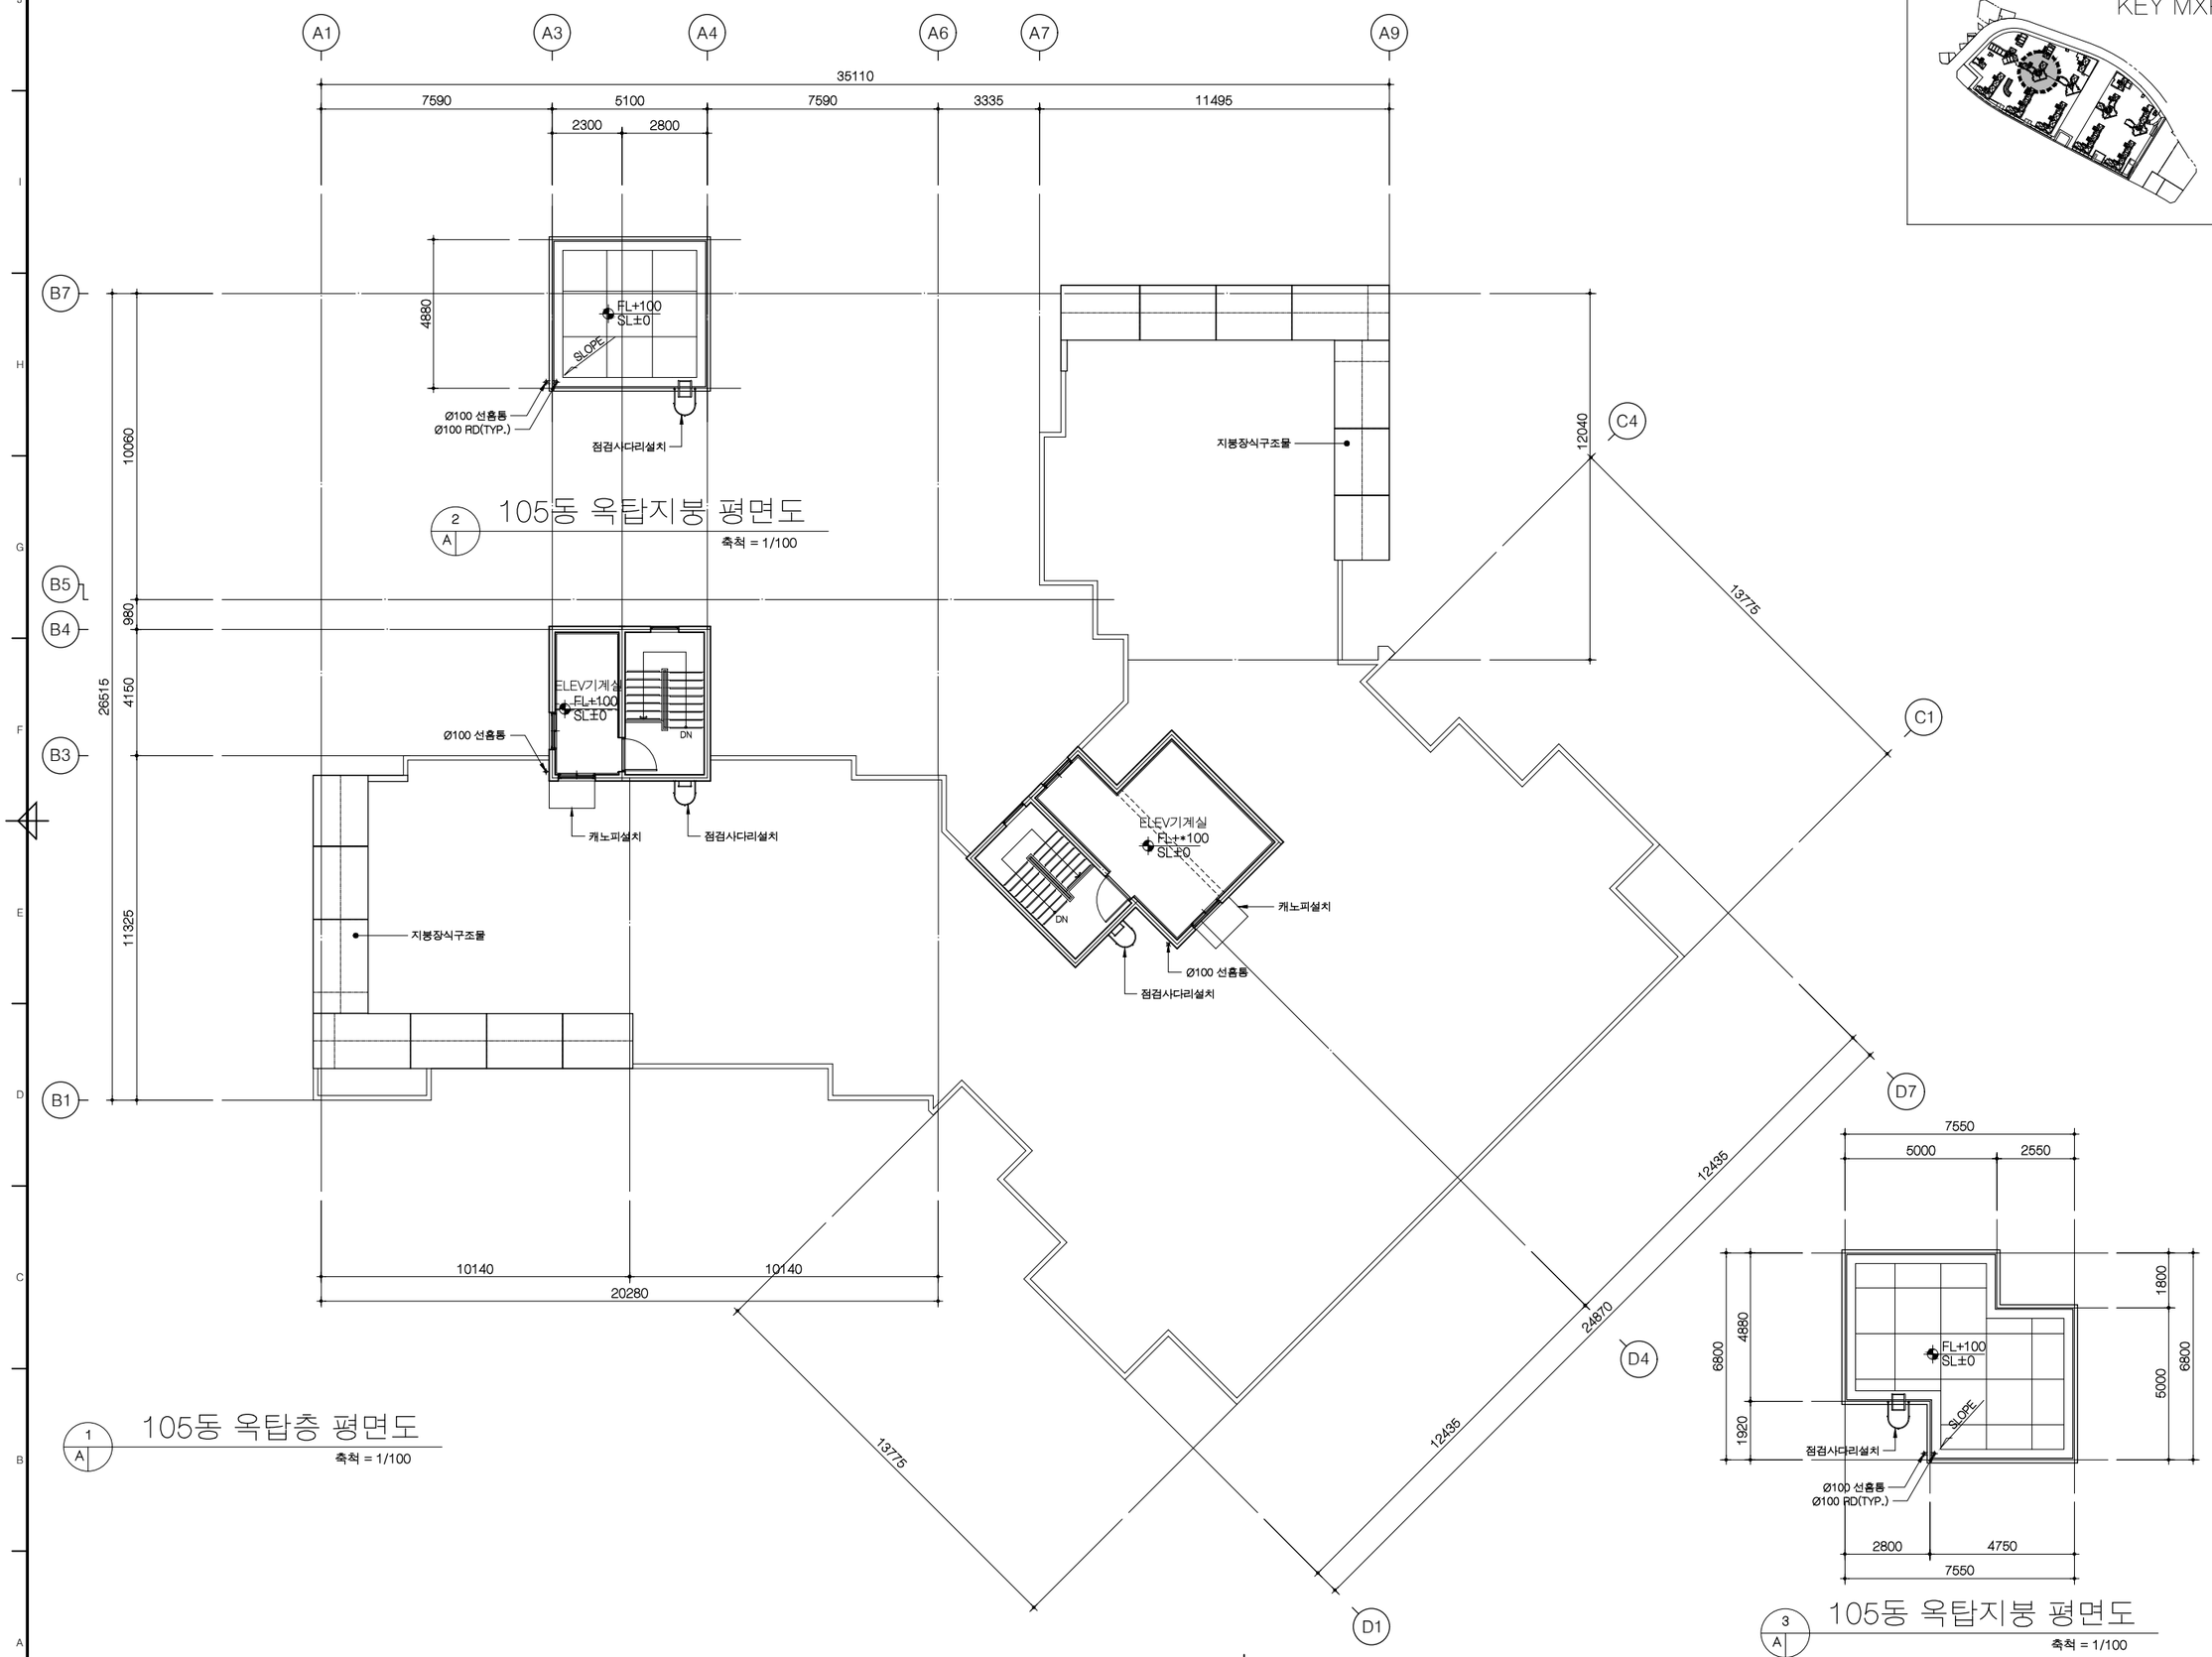

2 A 105동 옥탑지붕 평면도

축척 = 1/100

1 A 105동 옥탑층 평면도

축척 = 1/100

3 A 105동 옥탑지붕 평면도

축척 = 1/100

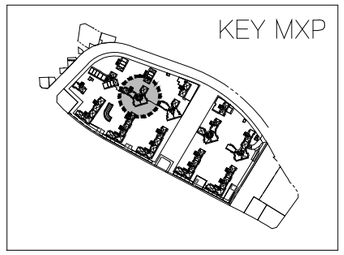

사업번호 PROJECT NO.

사업명 PROJECT TITLE

수색4재정비촉진구역
주택재개발 정비사업

KEY PLAN

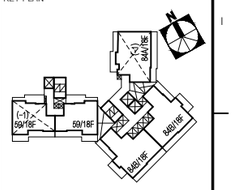

NOTE

1. 지붕바닥
   ① EXP. JOINT: 3000 X 3000
2. 본 평면도는 발코니확장전을 기준으로 작성됨
3. 재료마감은 실내,외 재료마감표 참조
4. 지붕 난간형태/설치위치는 안전성과 입면을 고려하여 실시공시 변경될 수 있음
5. 지붕재료 및 형태,구조는 실시공시 변경될수 있음
6. 지붕(옥탑지붕)의 배수드레인,환소용고리, 베기탑,점검사다리(점검구) 등의 설치위치/개소는 실시공시 변경될 수 있음
7. 옥상 상부구조물은 PC구조물 임.
8. 정화조 배기는 기계도서 참조

수정번호 REV. NO.	일 자 DATE	내 용 DESCRIPTION	승 인 CHKD
△			
△			
△			
△			

설계 DESIGNED BY

검토 CHECKED BY
최 진 규

심사 SUMMITED BY
정 호 혁

승인 APPROVED BY
이 승 준

일자 DATE
2019.08

도면명 DRAWING TITLE
105동
옥탑층 및 옥탑지붕 평면도

축 척 SCALE
A1: 1/100
A3: 1/200

도면번호 DRAWING NO.
A-358

일련번호 SHEET NO.

△ REV. NO.

HAUD
(주)하우드엔지니어링
종합건축사사무소
Architects, Planners & Engineers
TEL. 02 2143 4400, SEOUL, KOREA

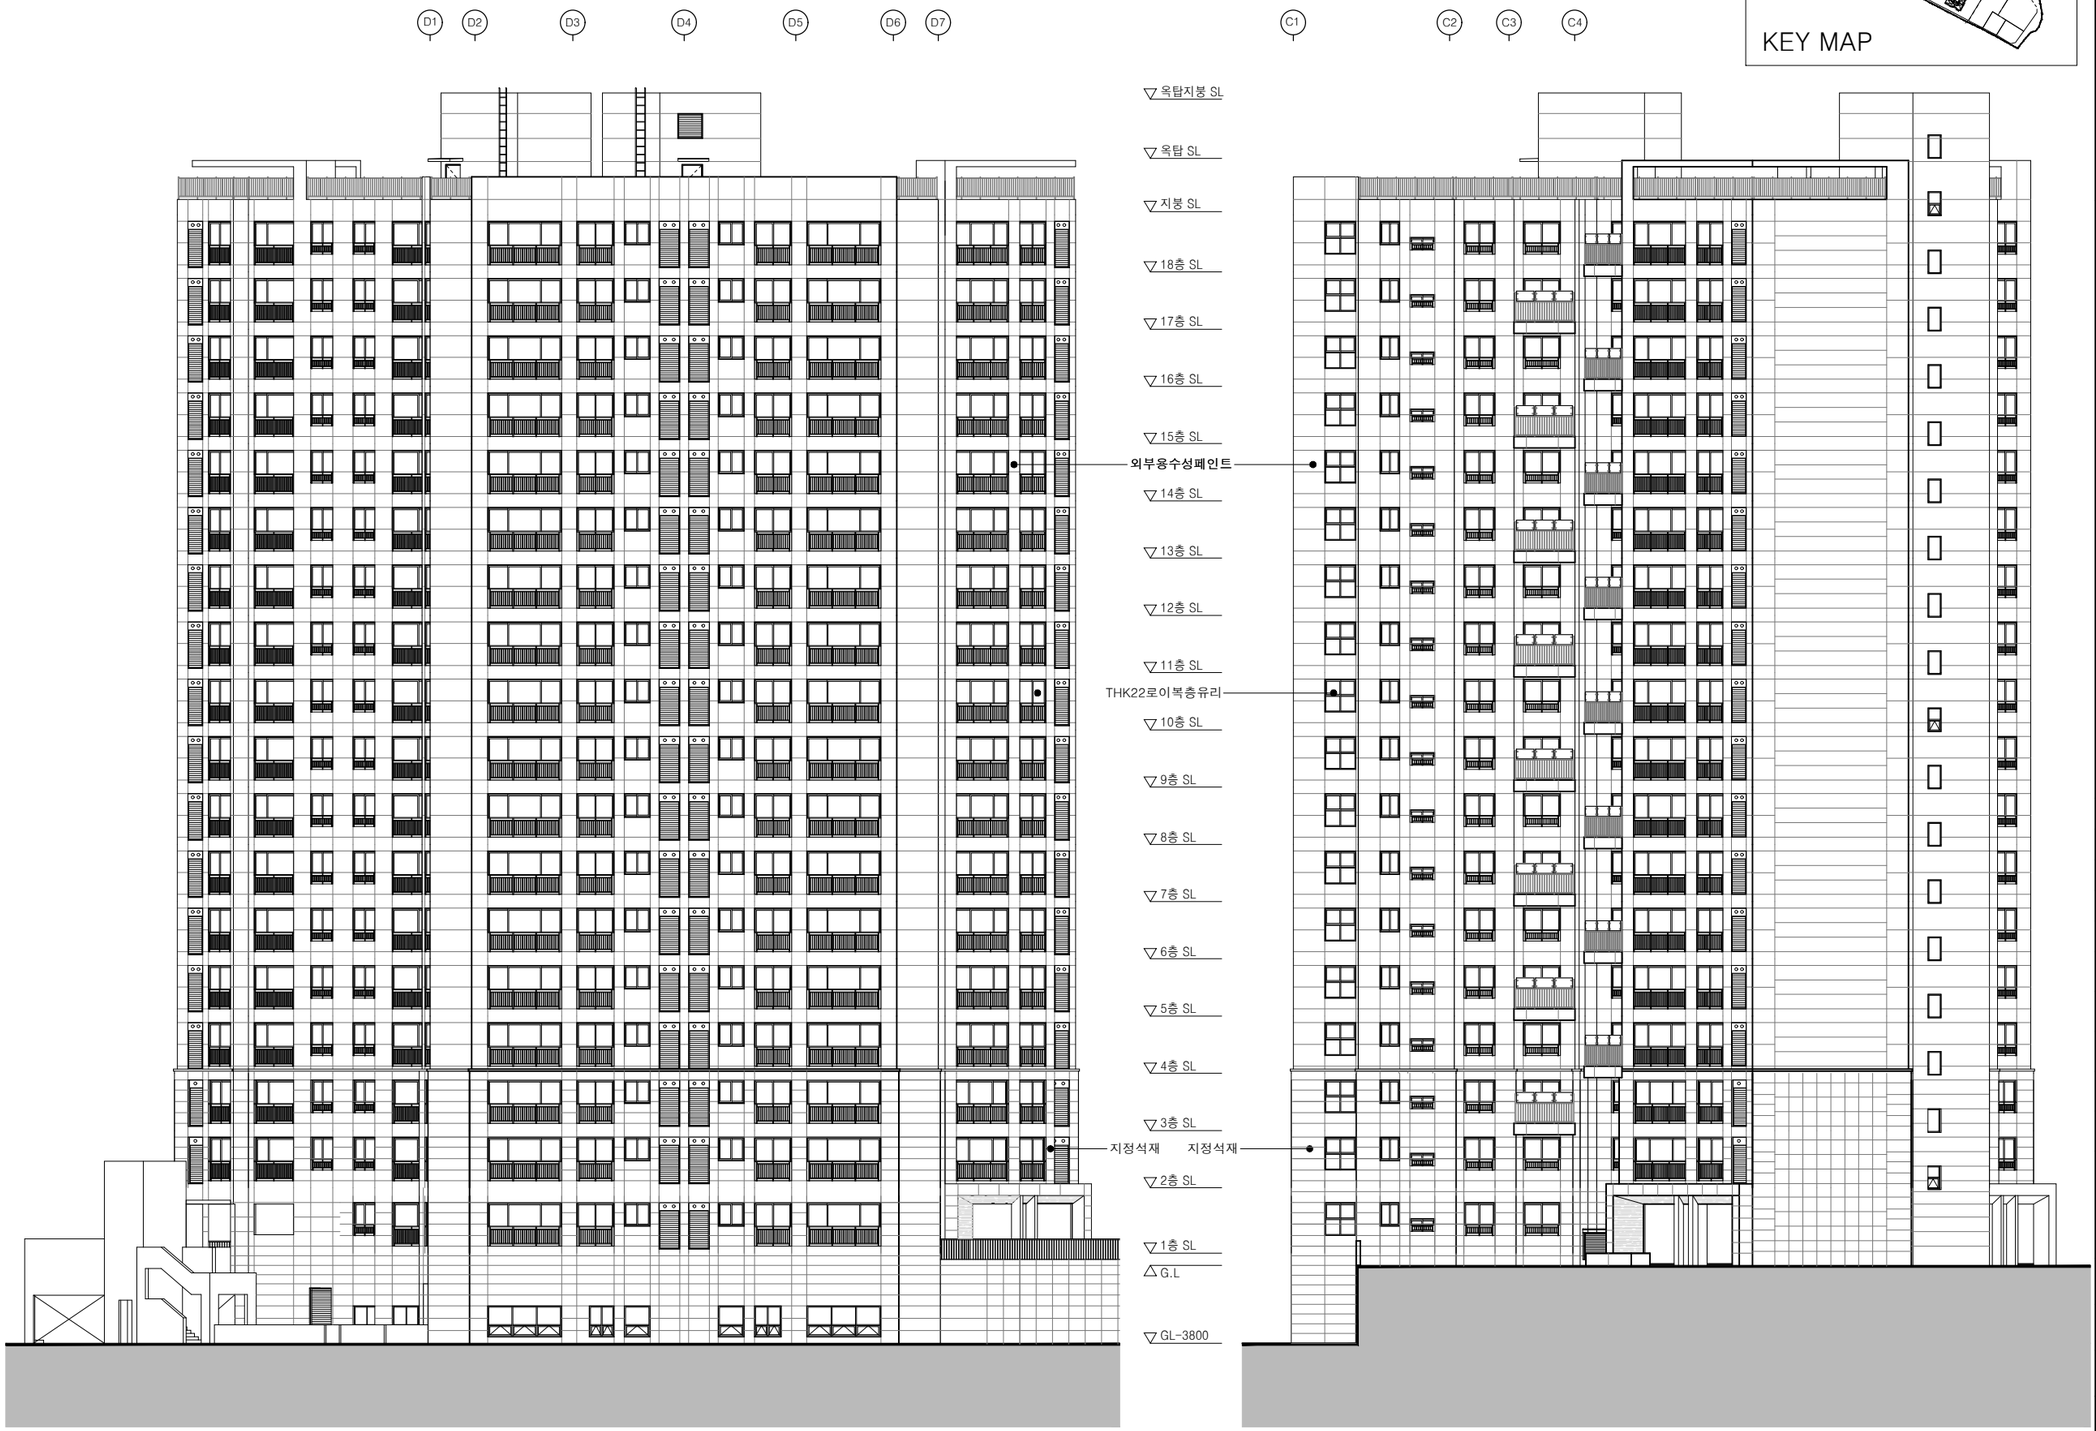

1 A 105동 정면도

축척 = 1/150

2 A 105동 우측면도

축척 = 1/150

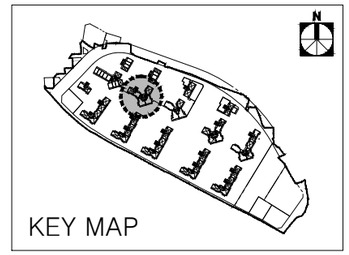

사업번호 PROJECT NO.

사업명 PROJECT TITLE

수색4재정비촉진구역
주택재개발 정비사업

KEY PLAN

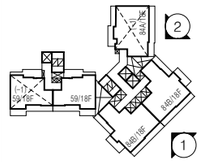
2
1
84/18F
59/18F
59/18F
59

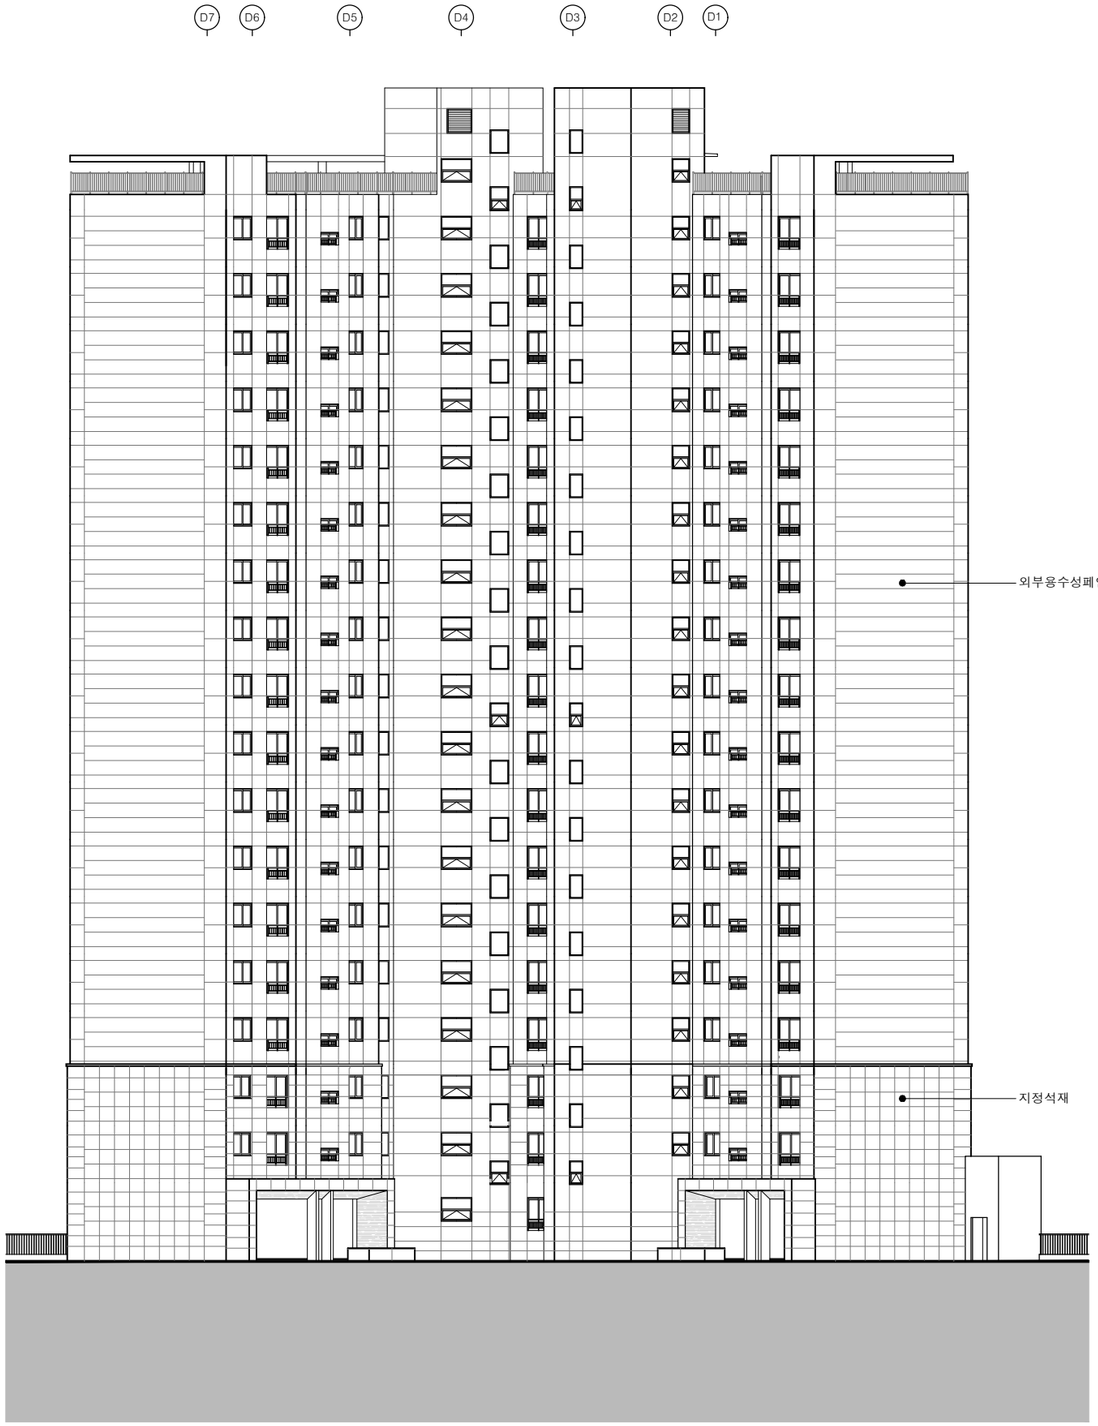

1 A 105동 배면도

축척 = 1/150

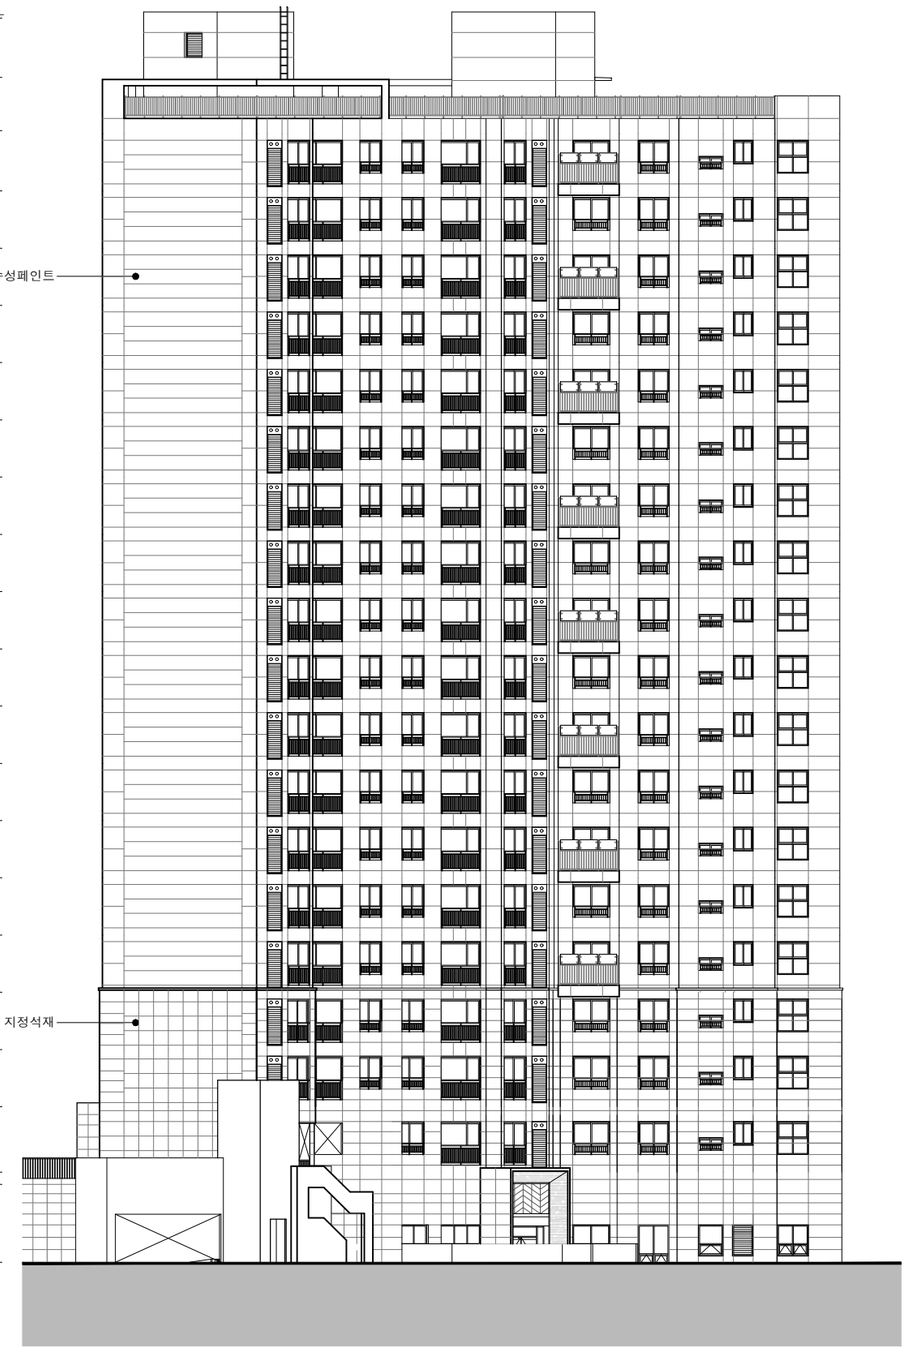

2 A 105동 좌측면도

축척 = 1/150

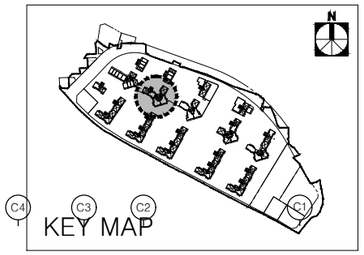

사업번호 PROJECT NO.

사업명 PROJECT TITLE

수색4재정비촉진구역
주택재개발 정비사업

KEY PLAN

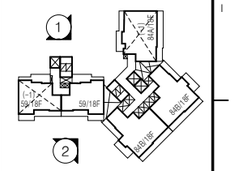

NOTE

1. 1층 바닥 LEVEL
   1SL±0 = 1FL±0 = GL±0 = EL+28.60
2. 지붕 난간의 형태 및 설치위치는 안전성과 입면디자인을 고려하여 변경가능함.
3. 지붕의 재료, 형태, 구조는 실시공시 변경될 수 있음.
4. 지붕 및 옥탑구조물의 형태와 구조는 실시공시 변경될 수 있음.
5. 외벽 및 측벽 문양은 실시공시 변경될 수 있음
6. 입면의 줄눈 및 마감선은 실시공시 변경될 수 있음.
7. 저층부 석재마감 및 입면 마감 색상, 재료에 대한 모든 기준은 특화도면을 우선 적용함.

수정번호 REV. NO.	일 자 DATE	내 용 DESCRIPTION	승 인 CHKD
△			
△			
△			
△			

설계 DESIGNED BY

검토 CHECKED BY
최 진 규

심사 SUMMITED BY
정 호 혁

승인 APPROVED BY
이 승 준

일자 DATE
2019.08

도면명 DRAWING TITLE
105동 배면도,좌측면도

축 척 SCALE
A1: 1/150
A3: 1/300

도면번호 DRAWING NO.
A-360

일련번호 SHEET NO. △ REV. NO.

HAUD
(주)하우드엔지니어링
종합건축사사무소
Architects, Planners & Engineers
TEL. 82 2140 4400, SEOUL, KOREA

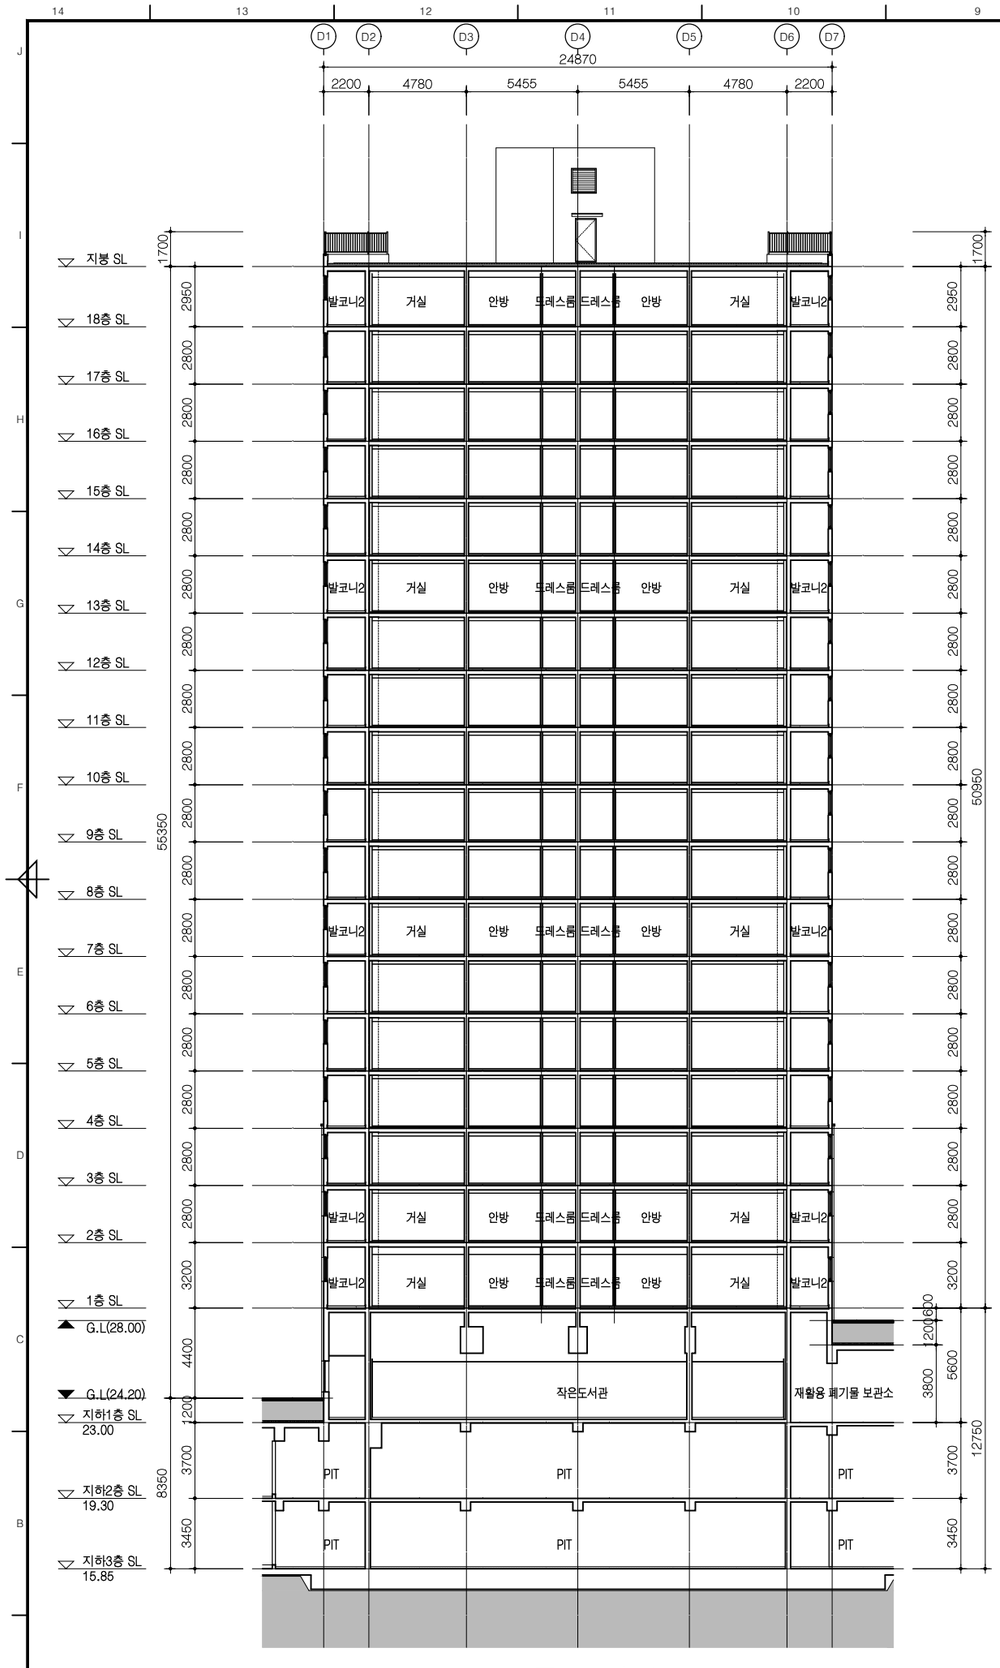

1 A 105동 종단면도

축척 = 1/150

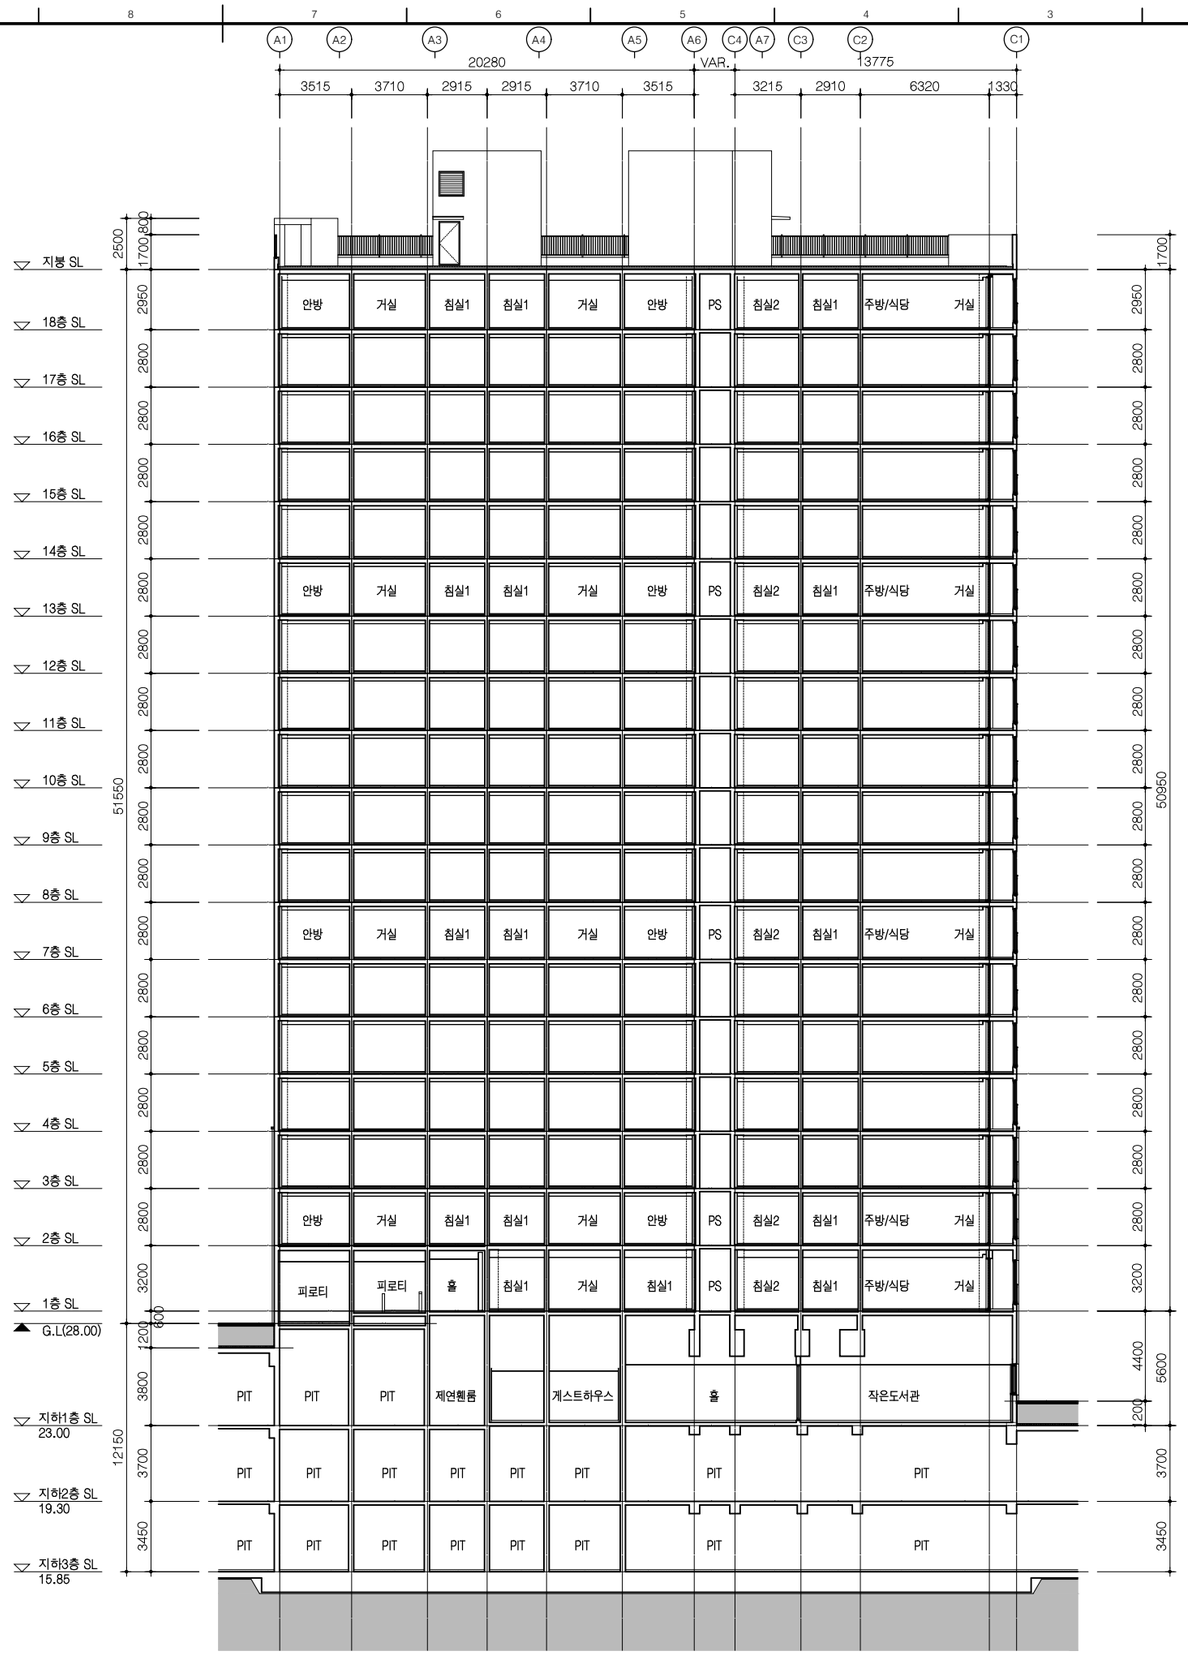

2 A 105동 횡단면도

축척 = 1/150

사업번호 PROJECT NO.

사업명 PROJECT TITLE

수색4재정비촉진구역
주택재개발 정비사업

KEY PLAN

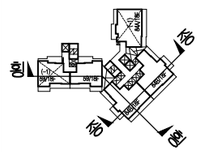

NOTE

수정번호 REV. NO.	일 자 DATE	내 용 DESCRIPTION	승 인 CHKD
1			
2			
3			
4			

설계 DESIGNED BY

검토 CHECKED BY
최 진 규

심사 SUMMITED BY
정 호 혁

승인 APPROVED BY
이 승 준

일자 DATE
2019.08

도면명 DRAWING TITLE
105동 종,횡단면도

축 척 SCALE
A1: 1/150
A3: 1/300

도면번호 DRAWING NO.
A-361

일련번호 SHEET NO.

REV. NO.

HAUD
(주)하우드엔지니어링
종합건축사사무소
Architects, Planners & Engineers
TEL. 02 2148 4400, SEOUL, KOREA

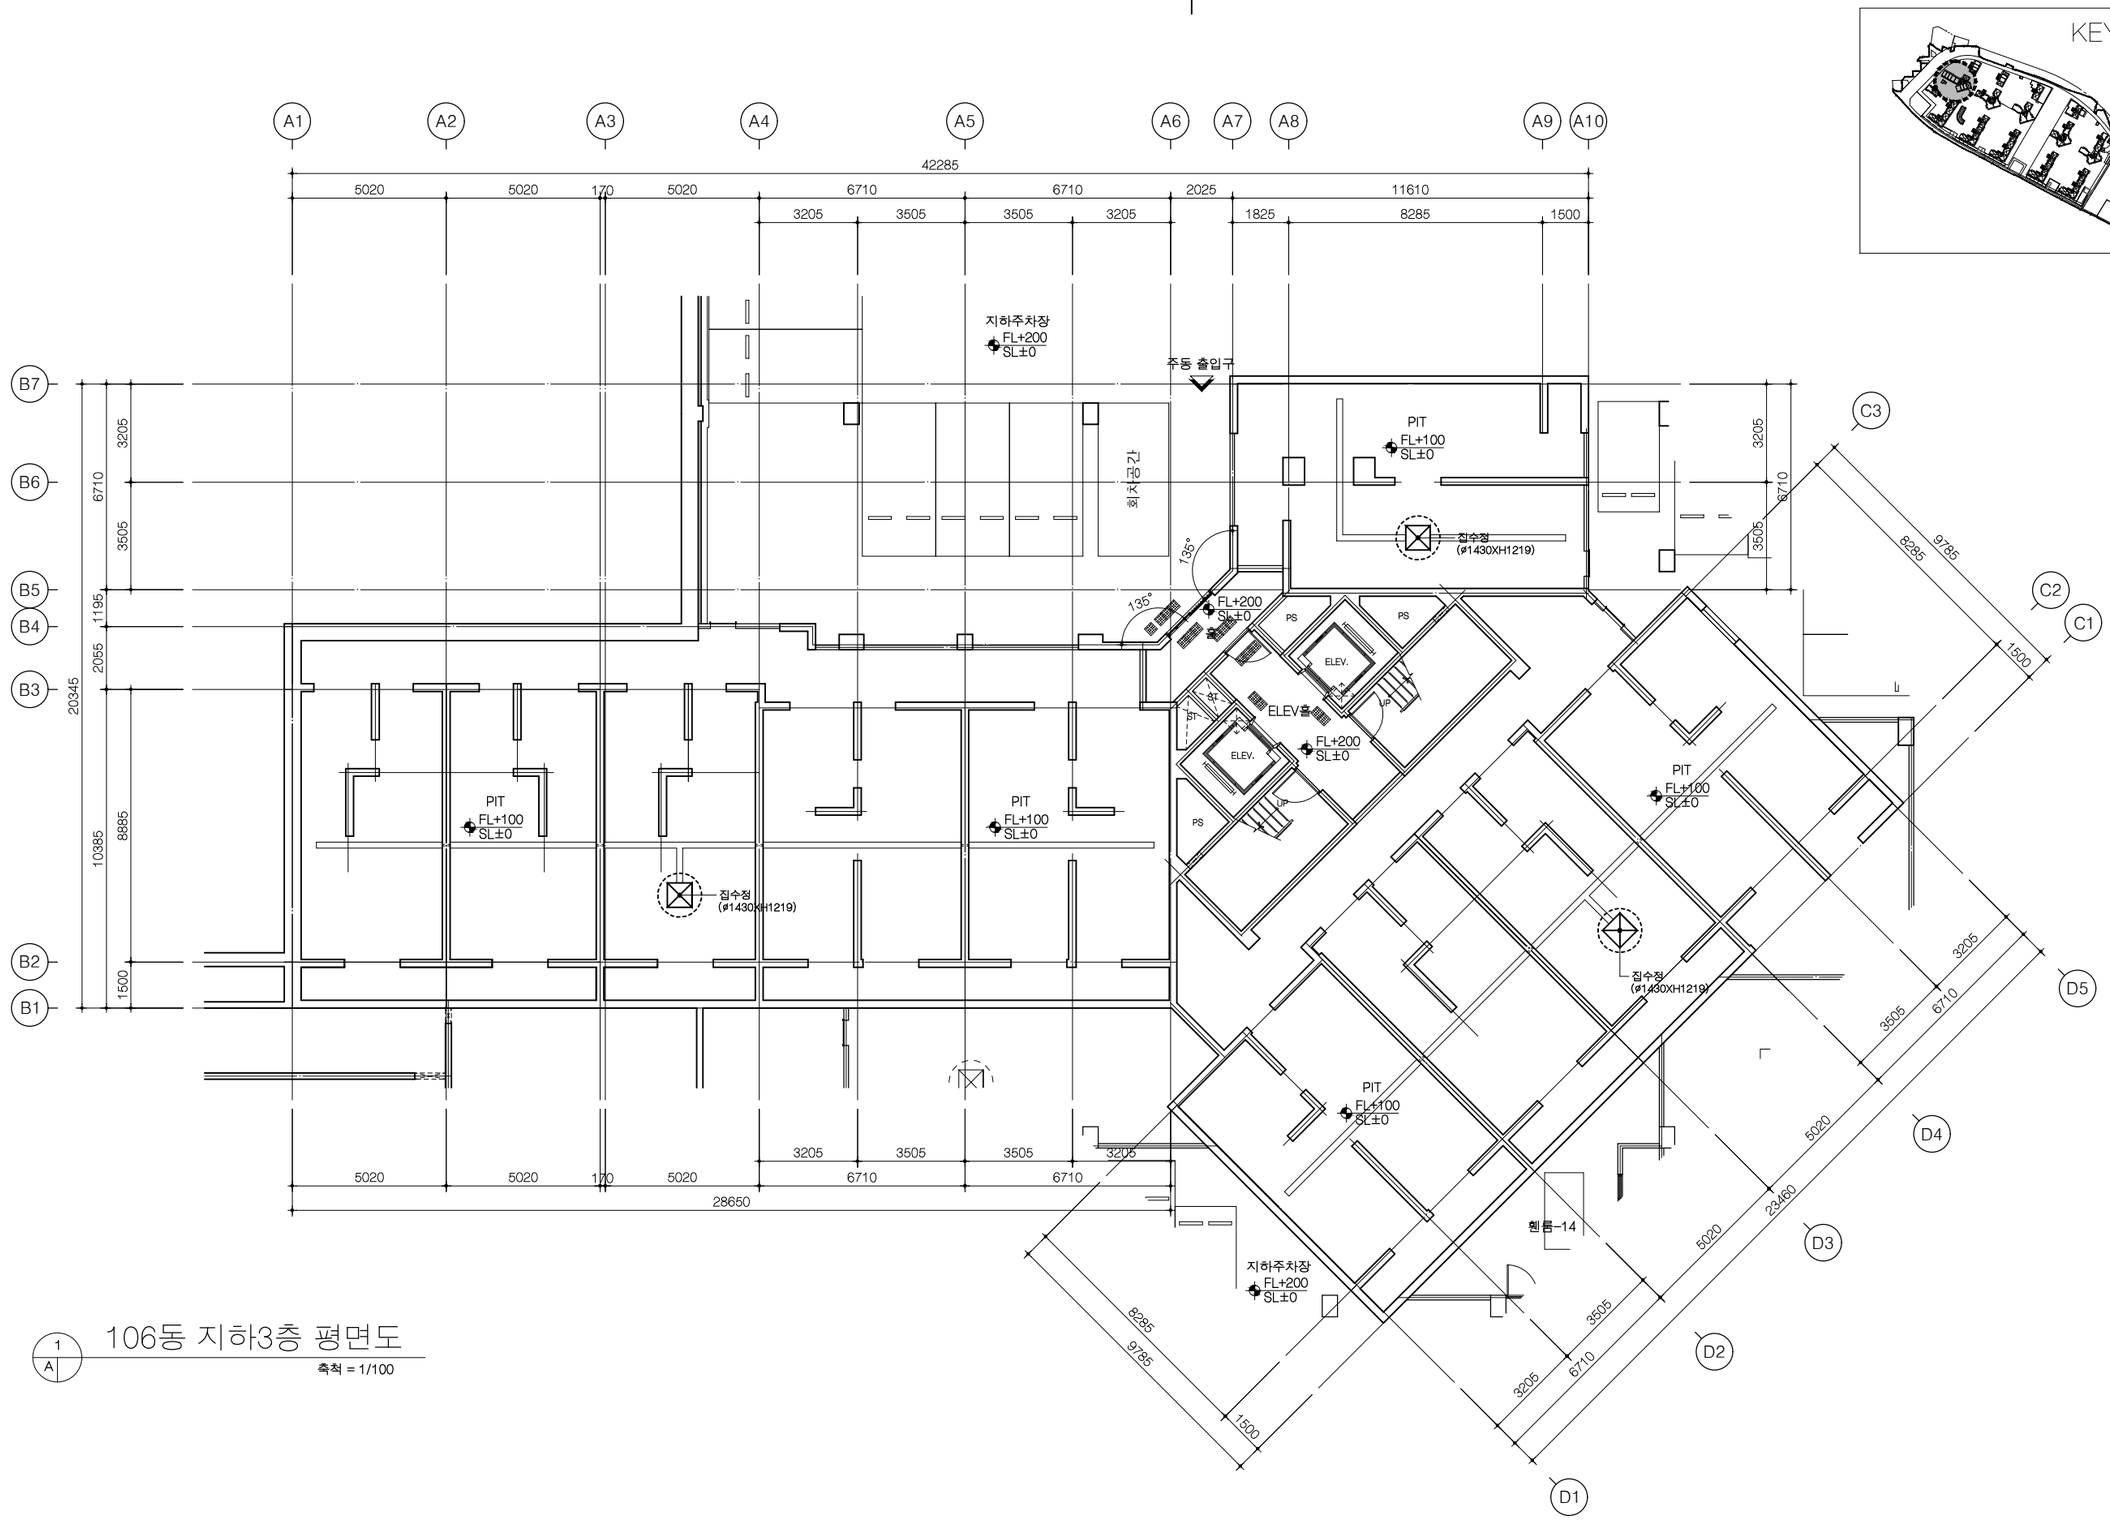

106동 지하3층 평면도

1
A

축척 = 1/100

KEY MXP

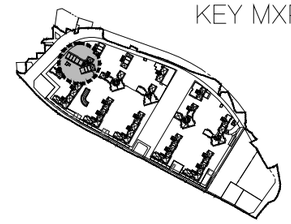

사업번호 PROJECT NO.

사업명 PROJECT TITLE

수색4재정비촉진구역
주택재개발 정비사업

KEY PLAN

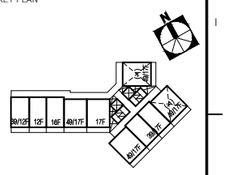

NOTE

1. 지하층 무근 콘크리트는 실시공시 THK80~120 범위로 변동이 있을수 있음.(SLOPE)
2. ELEV홀에 면한부위는 1.0B 조적쌓기임.
3. 지하주차장의 블록쌓기 기준은 높이가 3.6m이하인 경우 4인치 보강블록쌓기가 기준임 (단, 5.4m이하는 6인치쌓기, 5.4m초과는 8인치쌓기가 기준임)
4. ELEV.PIT 집수정은 (600X600X600)임.
5. 주차장 내의 창호는 주차장 창호도 참조.
6. 주차장 집수정 및 영구배수 집수정의 크기 및 위치는 지하주차장 평면도를 참조 할 것.
   ☒ : 주차장 집수정
   ☒ : 영구배수 집수정

********** 지하3층 바닥LEVEL
B3SL±0 = B3FL±0 = EL+15.85

수정번호 REV. NO.	일 자 DATE	내 용 DESCRIPTION	승 인 CHKD
△			
△			
△			
△			

설계 DESIGNED BY

검토 CHECKED BY
최 진 규

심사 SUMMITED BY
정 호 혁

승인 APPROVED BY
이 승 준

일자 DATE
2019.08

도면명 DRAWING TITLE
106동
지하3층 평면도

축 척 SCALE
A1: 1/100
A3: 1/200

도면번호 DRAWING NO.
A-371

일련번호 SHEET NO.

△ REV. NO.

HAUD
㈜하우드엔지니어링
종합건축사사무소
Architects, Planners & Engineers
TEL. 02-2149-4400, SEOUL, KOREA

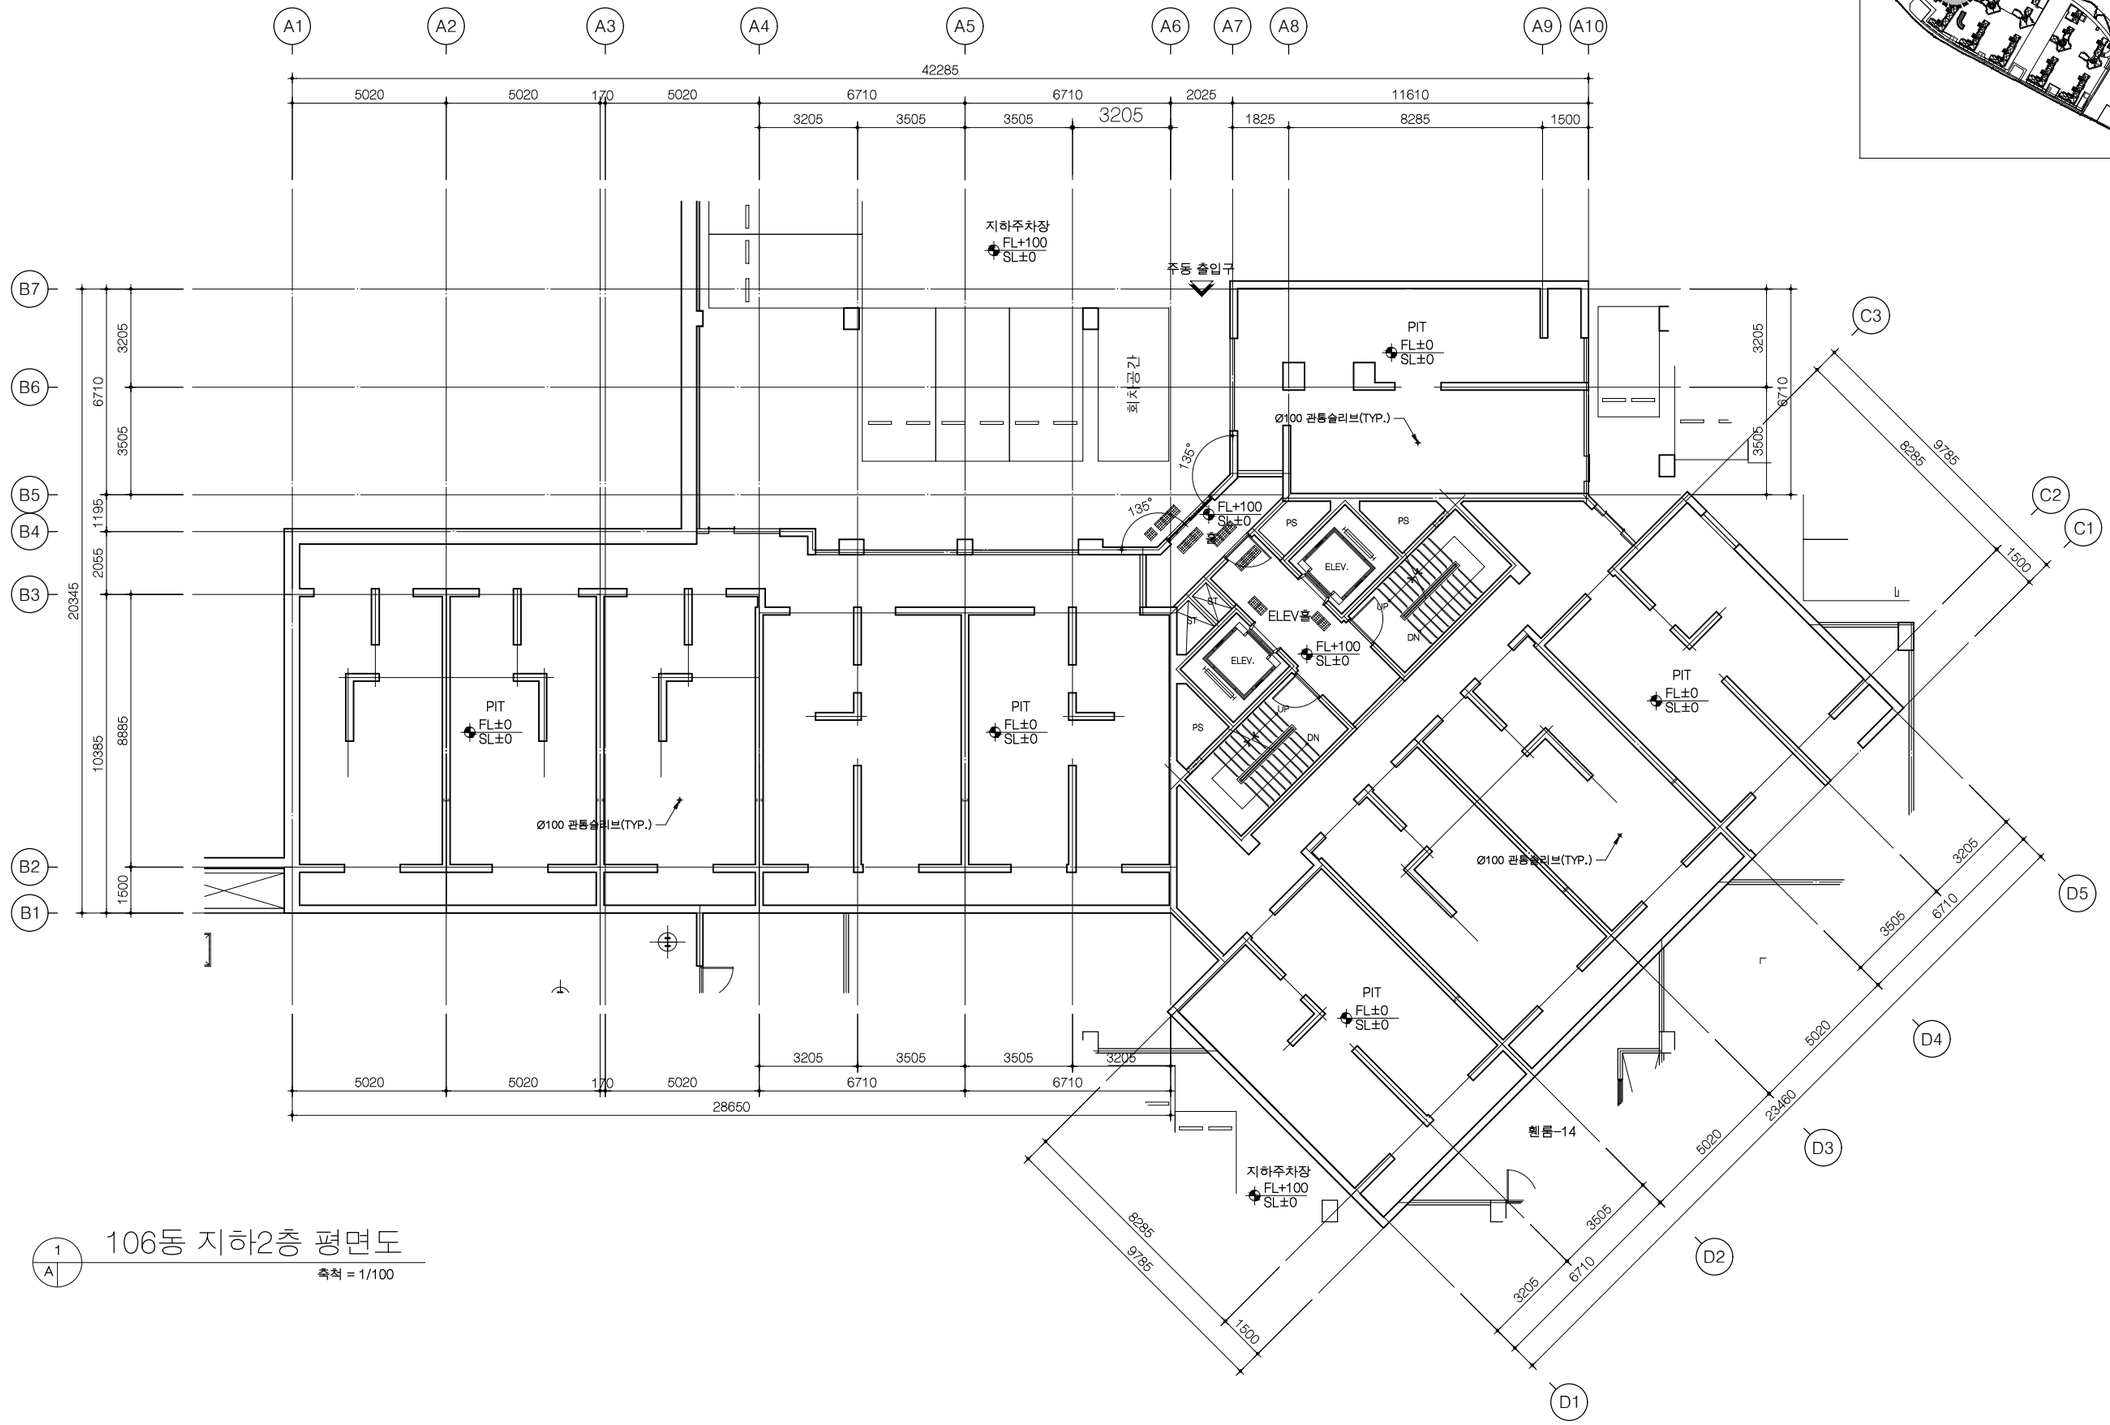

106동 지하2층 평면도

1 / A

축척 = 1/100

KEY MXP

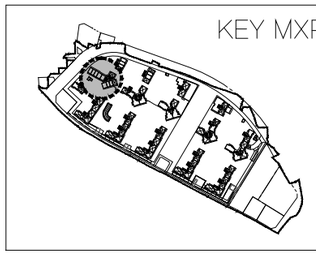

사업번호 PROJECT NO.

사업명 PROJECT TITLE

수색4재정비촉진구역
주택재개발 정비사업

KEY PLAN

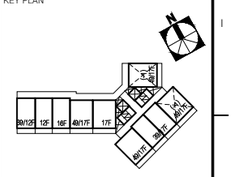

NOTE

1. 지하주차장의 ELEV홀에 면한부위는 1.0B 조적쌓기임.
2. 지하주차장의 블록쌓기 기준은 높이가 3.6m이하인 경우 4인치 보강블록쌓기가 기준임 (단, 5.4m이하는 6인치쌓기, 5.4m초과는 8인치쌓기가 기준임)
3. 주차장 내의 창호는 주차장 창호도 참조.

**** 지하2층 바닥LEVEL
D2SL±0 = D2FL±0 = EL+19.30

수정번호 REV. NO.	일 자 DATE	내 용 DESCRIPTION	승 인 CHKD
△			
△			
△			
△			

설계 DESIGNED BY

검토 CHECKED BY
최 진 규

심사 SUMMITED BY
정 호 혁

승인 APPROVED BY
이 승 준

일자 DATE
2019.08

도면명 DRAWING TITLE
106동
지하2층 평면도

축 척 SCALE
A1: 1/100
A3: 1/200

도면번호 DRAWING NO.
A-372

일련번호 SHEET NO. / REV. NO.

HAUD
㈜하우드엔지니어링
종합건축사사무소
Architects, Planners & Engineers
TEL. 02 2140 4400, SEOUL, KOREA

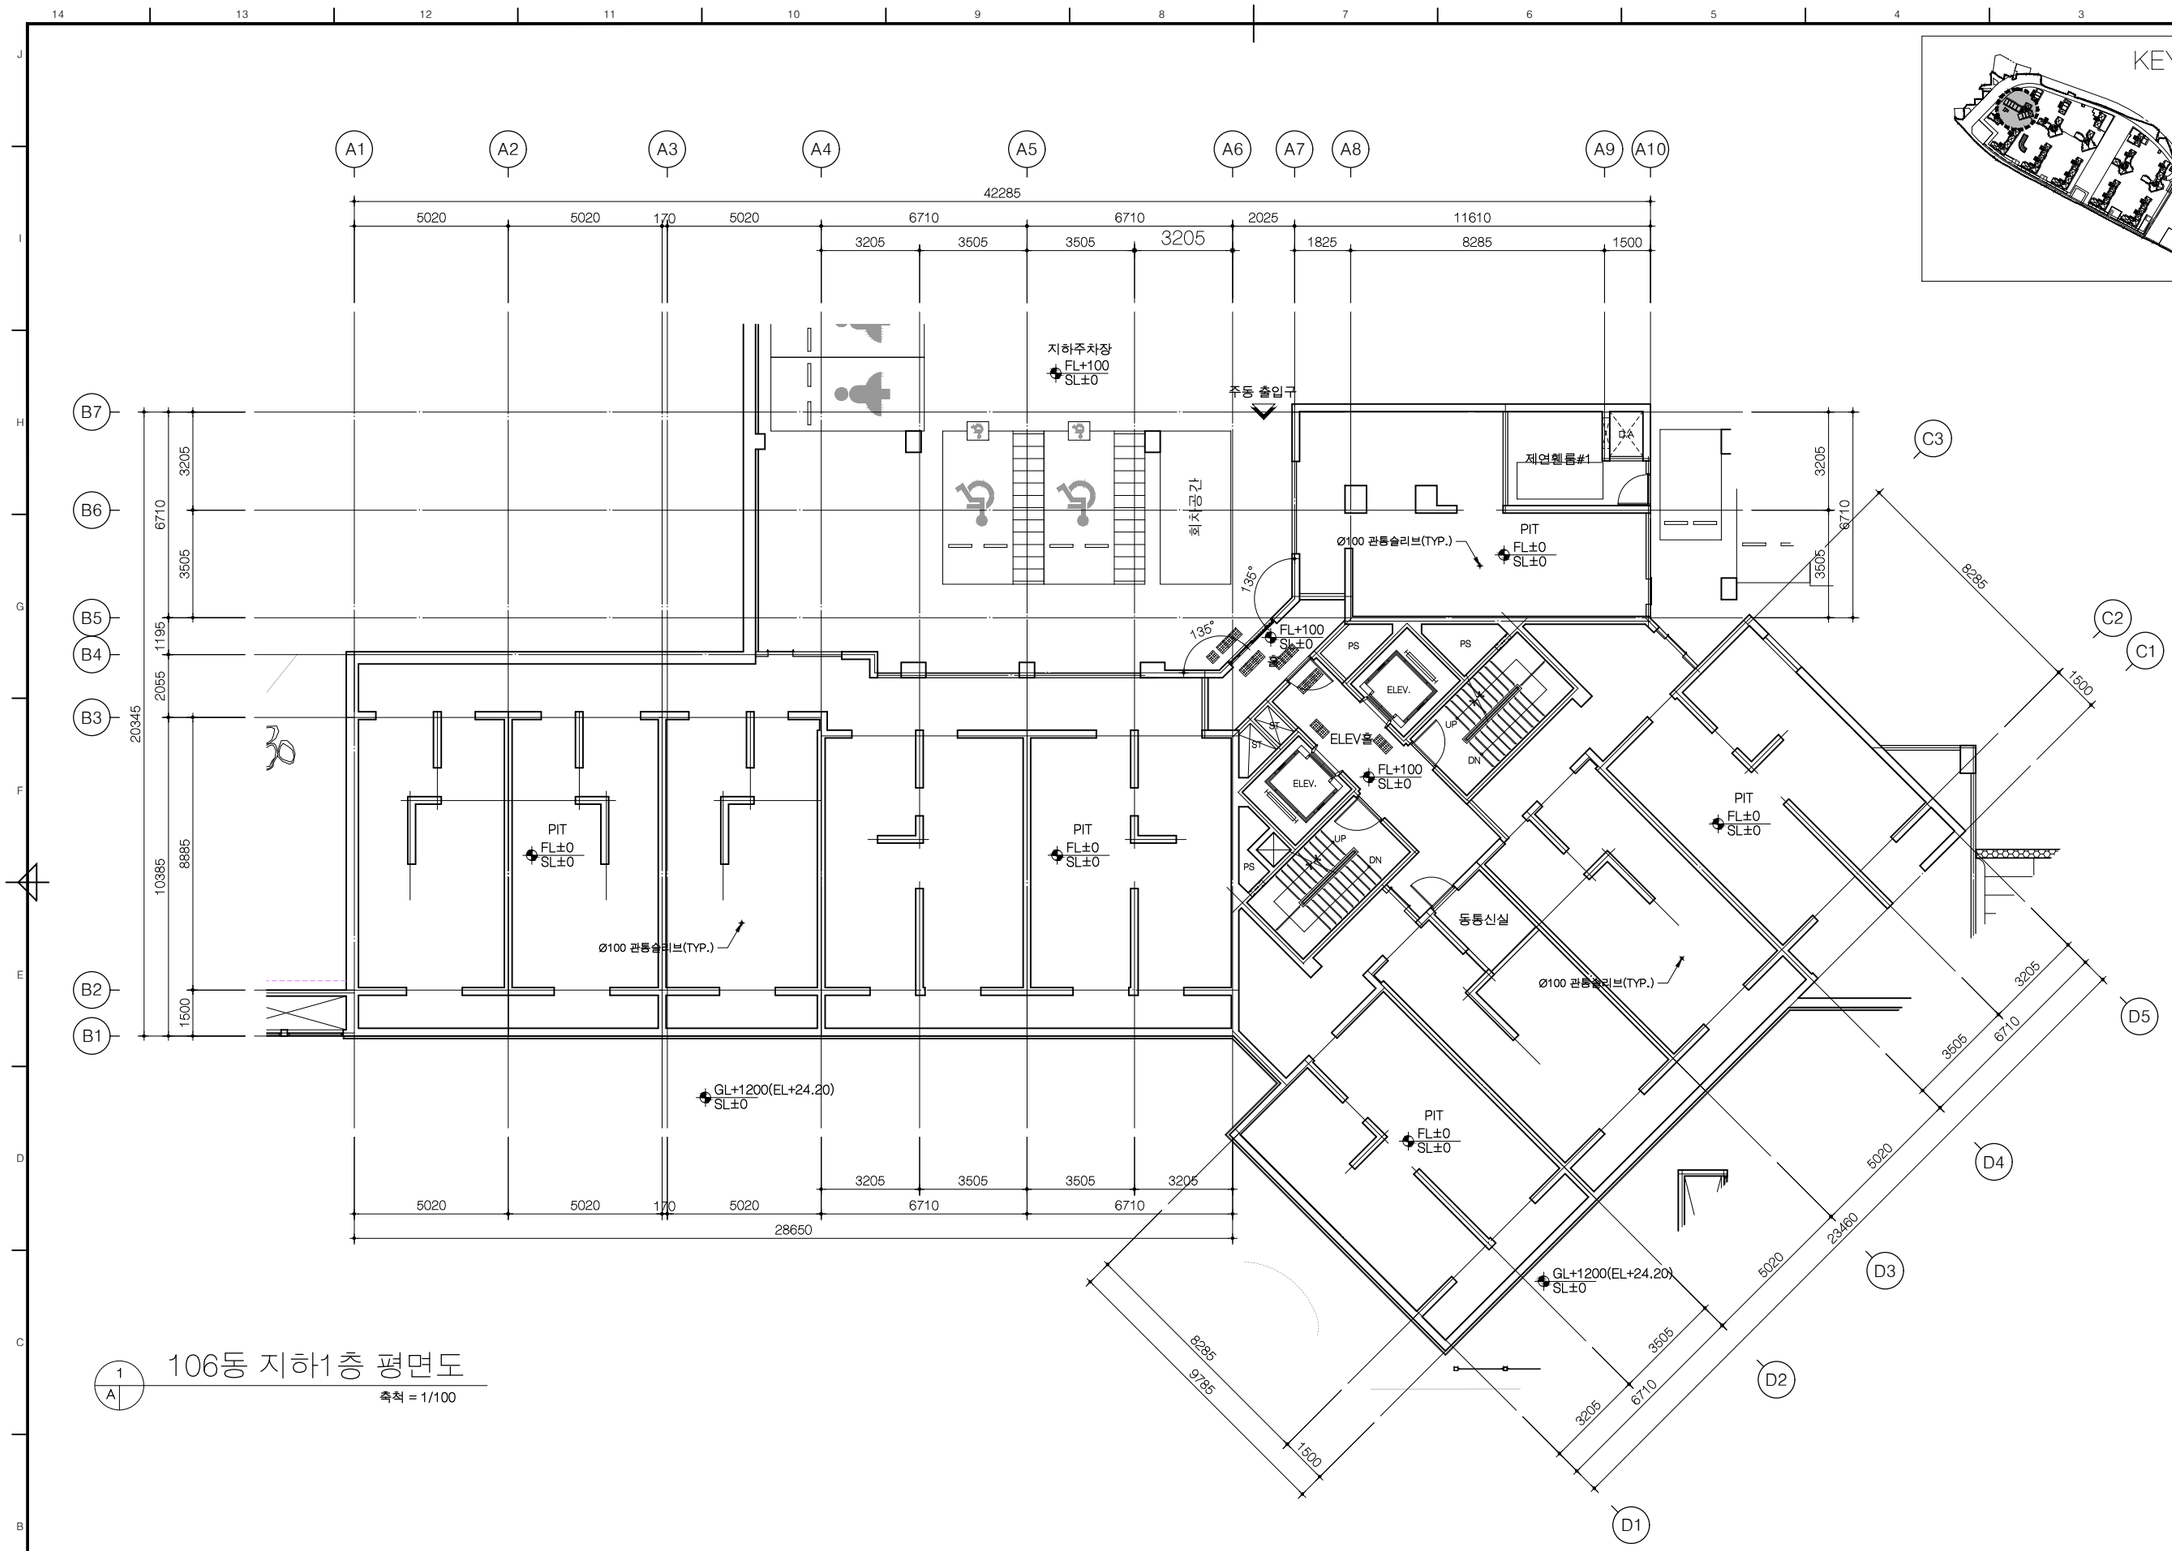

1 / A 106동 지하1층 평면도

축척 = 1/100

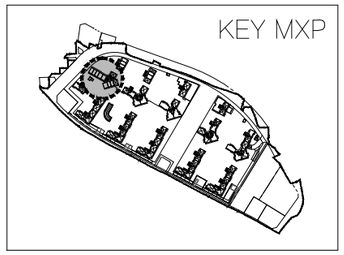

사업번호 PROJECT NO.

사업명 PROJECT TITLE

수색4재정비촉진구역
주택재개발 정비사업

KEY PLAN

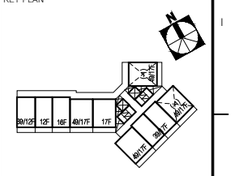

NOTE

1. 지하주차장의 ELEV홀에 면한부위는 1.0B 조적쌓기임.
2. 지하주차장의 블록쌓기 기준은 높이가 3.6m이하인 경우 4인치 보강블록쌓기가 기준임 (단, 5.4m이하는 6인치쌓기, 5.4m초과는 8인치쌓기가 기준임)
3. 주차장 내의 창호는 주차장 창호도 참조.

* 지하1층 바닥LEVEL
D1SL±0 = D1FL±0 = EL+23.00

수정번호 REV. NO.	일 자 DATE	내 용 DESCRIPTION	승 인 CHKD
△			
△			
△			
△			

설계 DESIGNED BY

검토 CHECKED BY
최 진 규

심사 SUMMITED BY
정 호 혁

승인 APPROVED BY
이 승 준

일자 DATE
2019.08

도면명 DRAWING TITLE
106동
지하1층 평면도

축 척 SCALE
A1: 1/100
A3: 1/200

도면번호 DRAWING NO.
A-373

일련번호 SHEET NO. △ REV. NO.

HAUD
(주)하우드엔지니어링
종합건축사사무소
Architects, Planners & Engineers
TEL. 02 2140 4400, SEOUL, KOREA

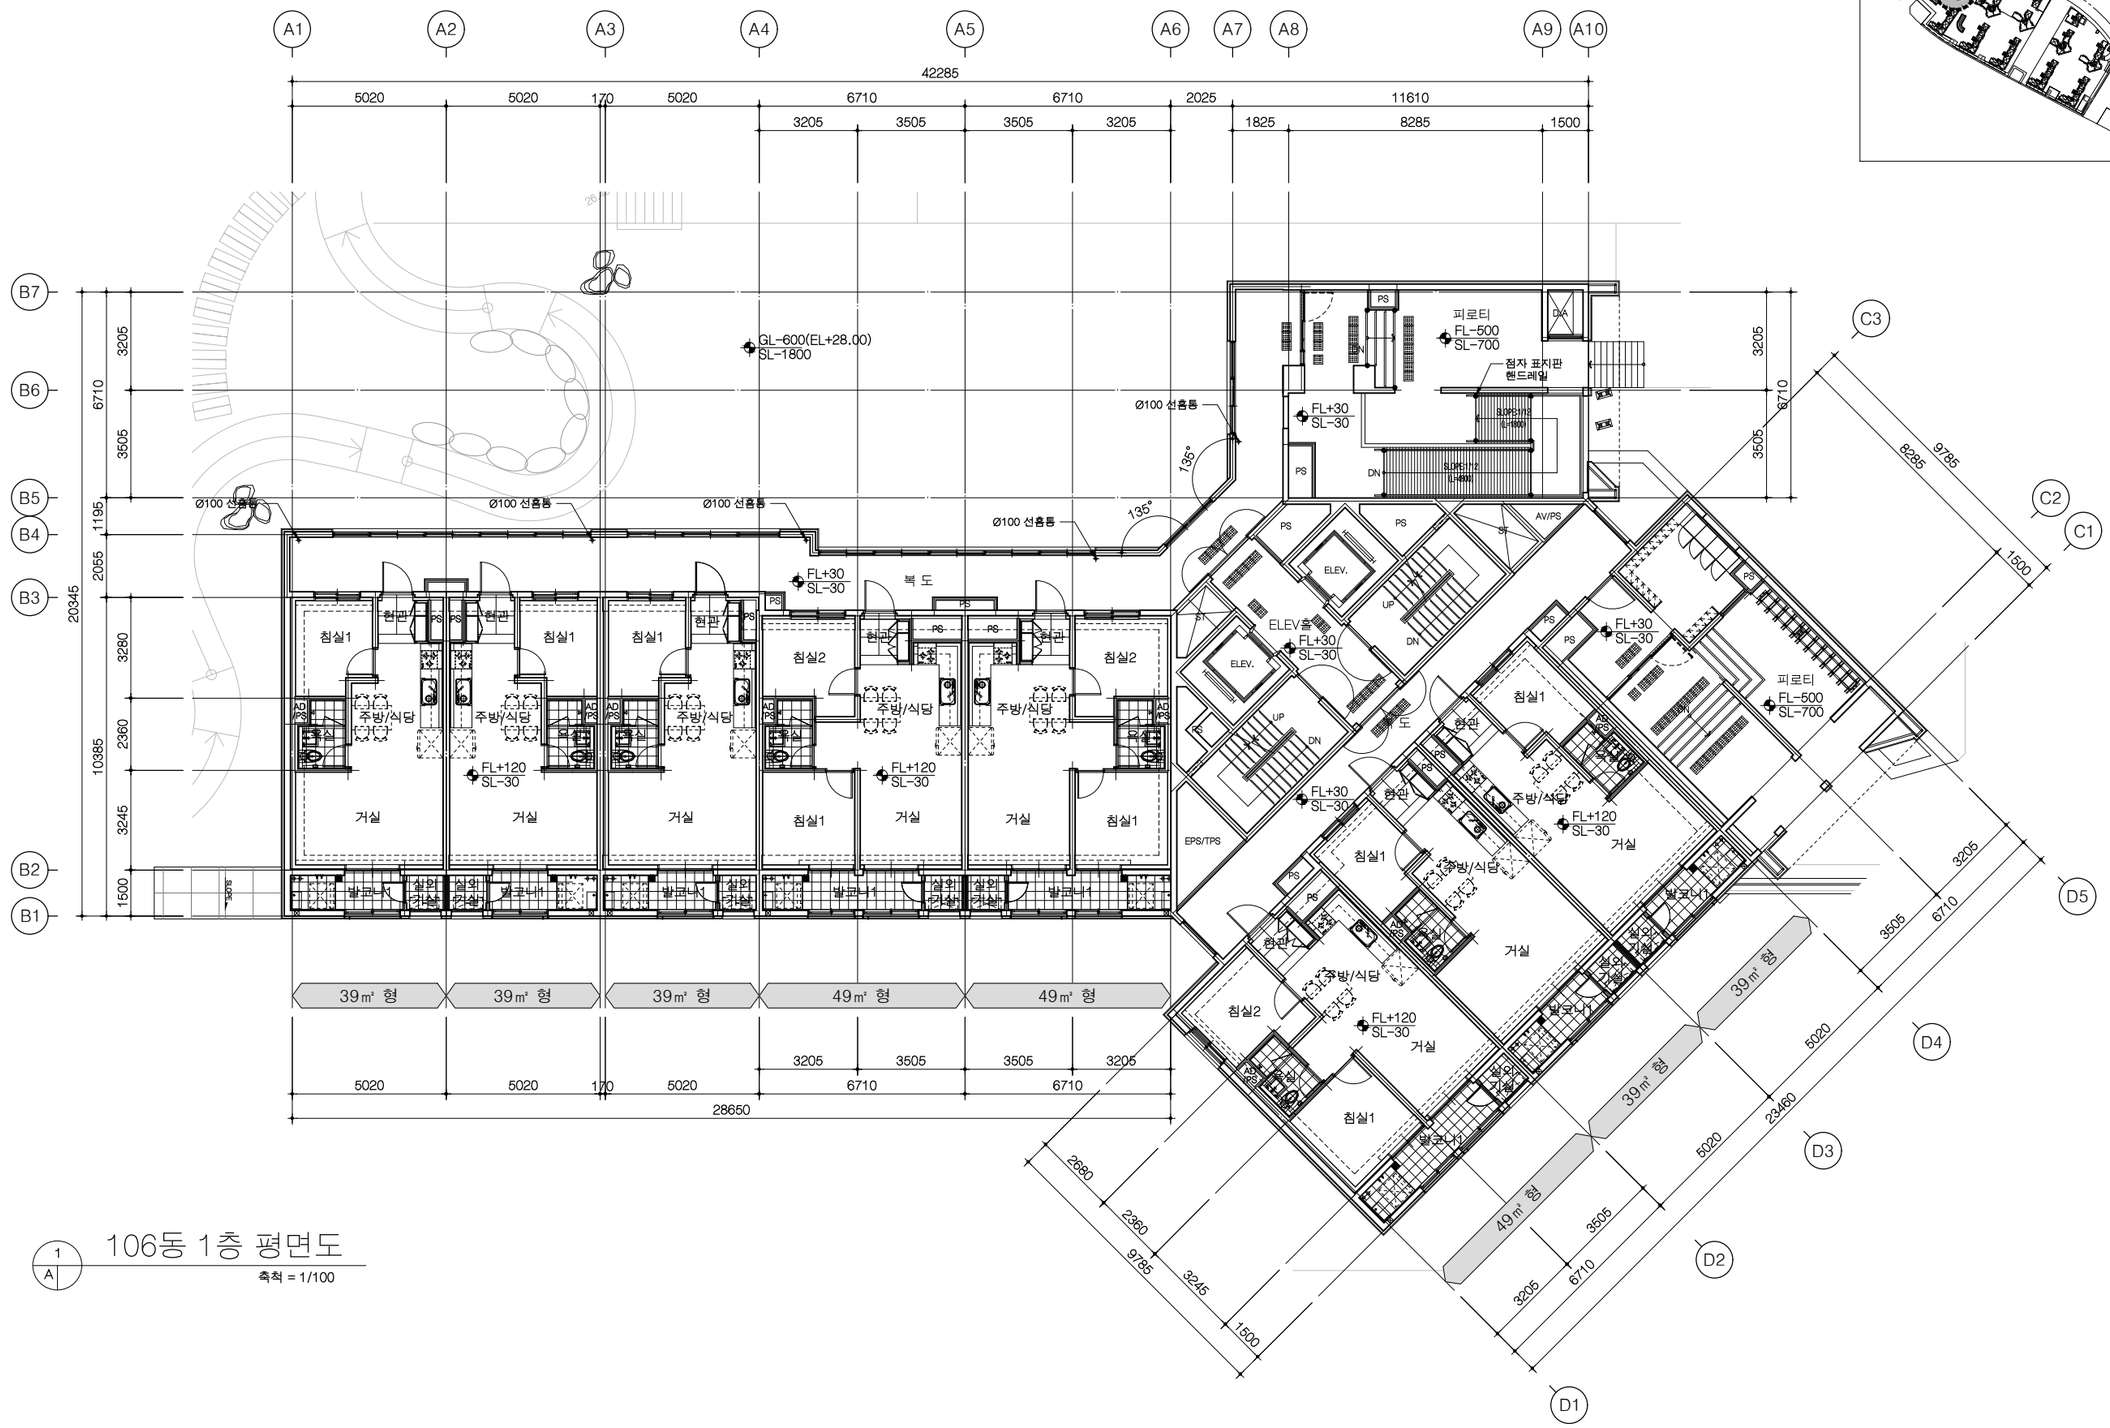

1 A 106동 1층 평면도

축척 = 1/100

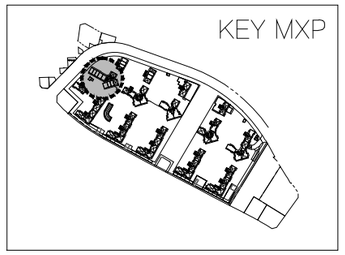

사업번호 PROJECT NO.

사업명 PROJECT TITLE

수색4재정비촉진구역
주택재개발 정비사업

KEY PLAN

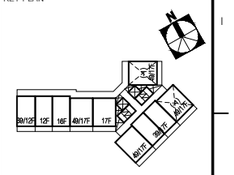

NOTE

1. 본 도면은 발코니 확장전를 기준으로 작성됨.
2. 지붕층 난간의 형태와 설치 위치는 안전성과 입면디자인을 고려하여 변경 가능함.
3. 지붕의 재료, 형태, 구조는 실시공 시 변경 될 수 있음.
4. 지붕 및 옥탑 구조물의 형태와 구조는 실시공 시 변경될 수 있음.
5. 옥상 출눈의 간격은 실시공 시 변경될 수 있음.
6. 옥상 출눈 틈에 실란트 시공되지 않음
7. 우편물 수취함 설치 위치는 변경될 수 있음

* 1층 바닥LEVEL
1SL±0 = 1FL±0 = GL±0 = EL+28.60
GL-600 = EL+28.00(토목도면 참조)

수정번호 REV. NO.	일 자 DATE	내 용 DESCRIPTION	승 인 CHKD
△			
△			
△			
△			

설계 DESIGNED BY

검토 CHECKED BY
최 진 규

심사 SUMMITED BY
정 호 혁

승인 APPROVED BY
이 승 준

일자 DATE
2019.08

도면명 DRAWING TITLE
106동
1층 평면도

축 척 SCALE
A1: 1/100
A3: 1/200

도면번호 DRAWING NO.
A-374

일련번호 SHEET NO. △ REV. NO.

HAUD
㈜하우드엔지니어링
종합건축사사무소
Architects, Planners & Engineers
TEL. 02 2143 4400, SEOUL, KOREA

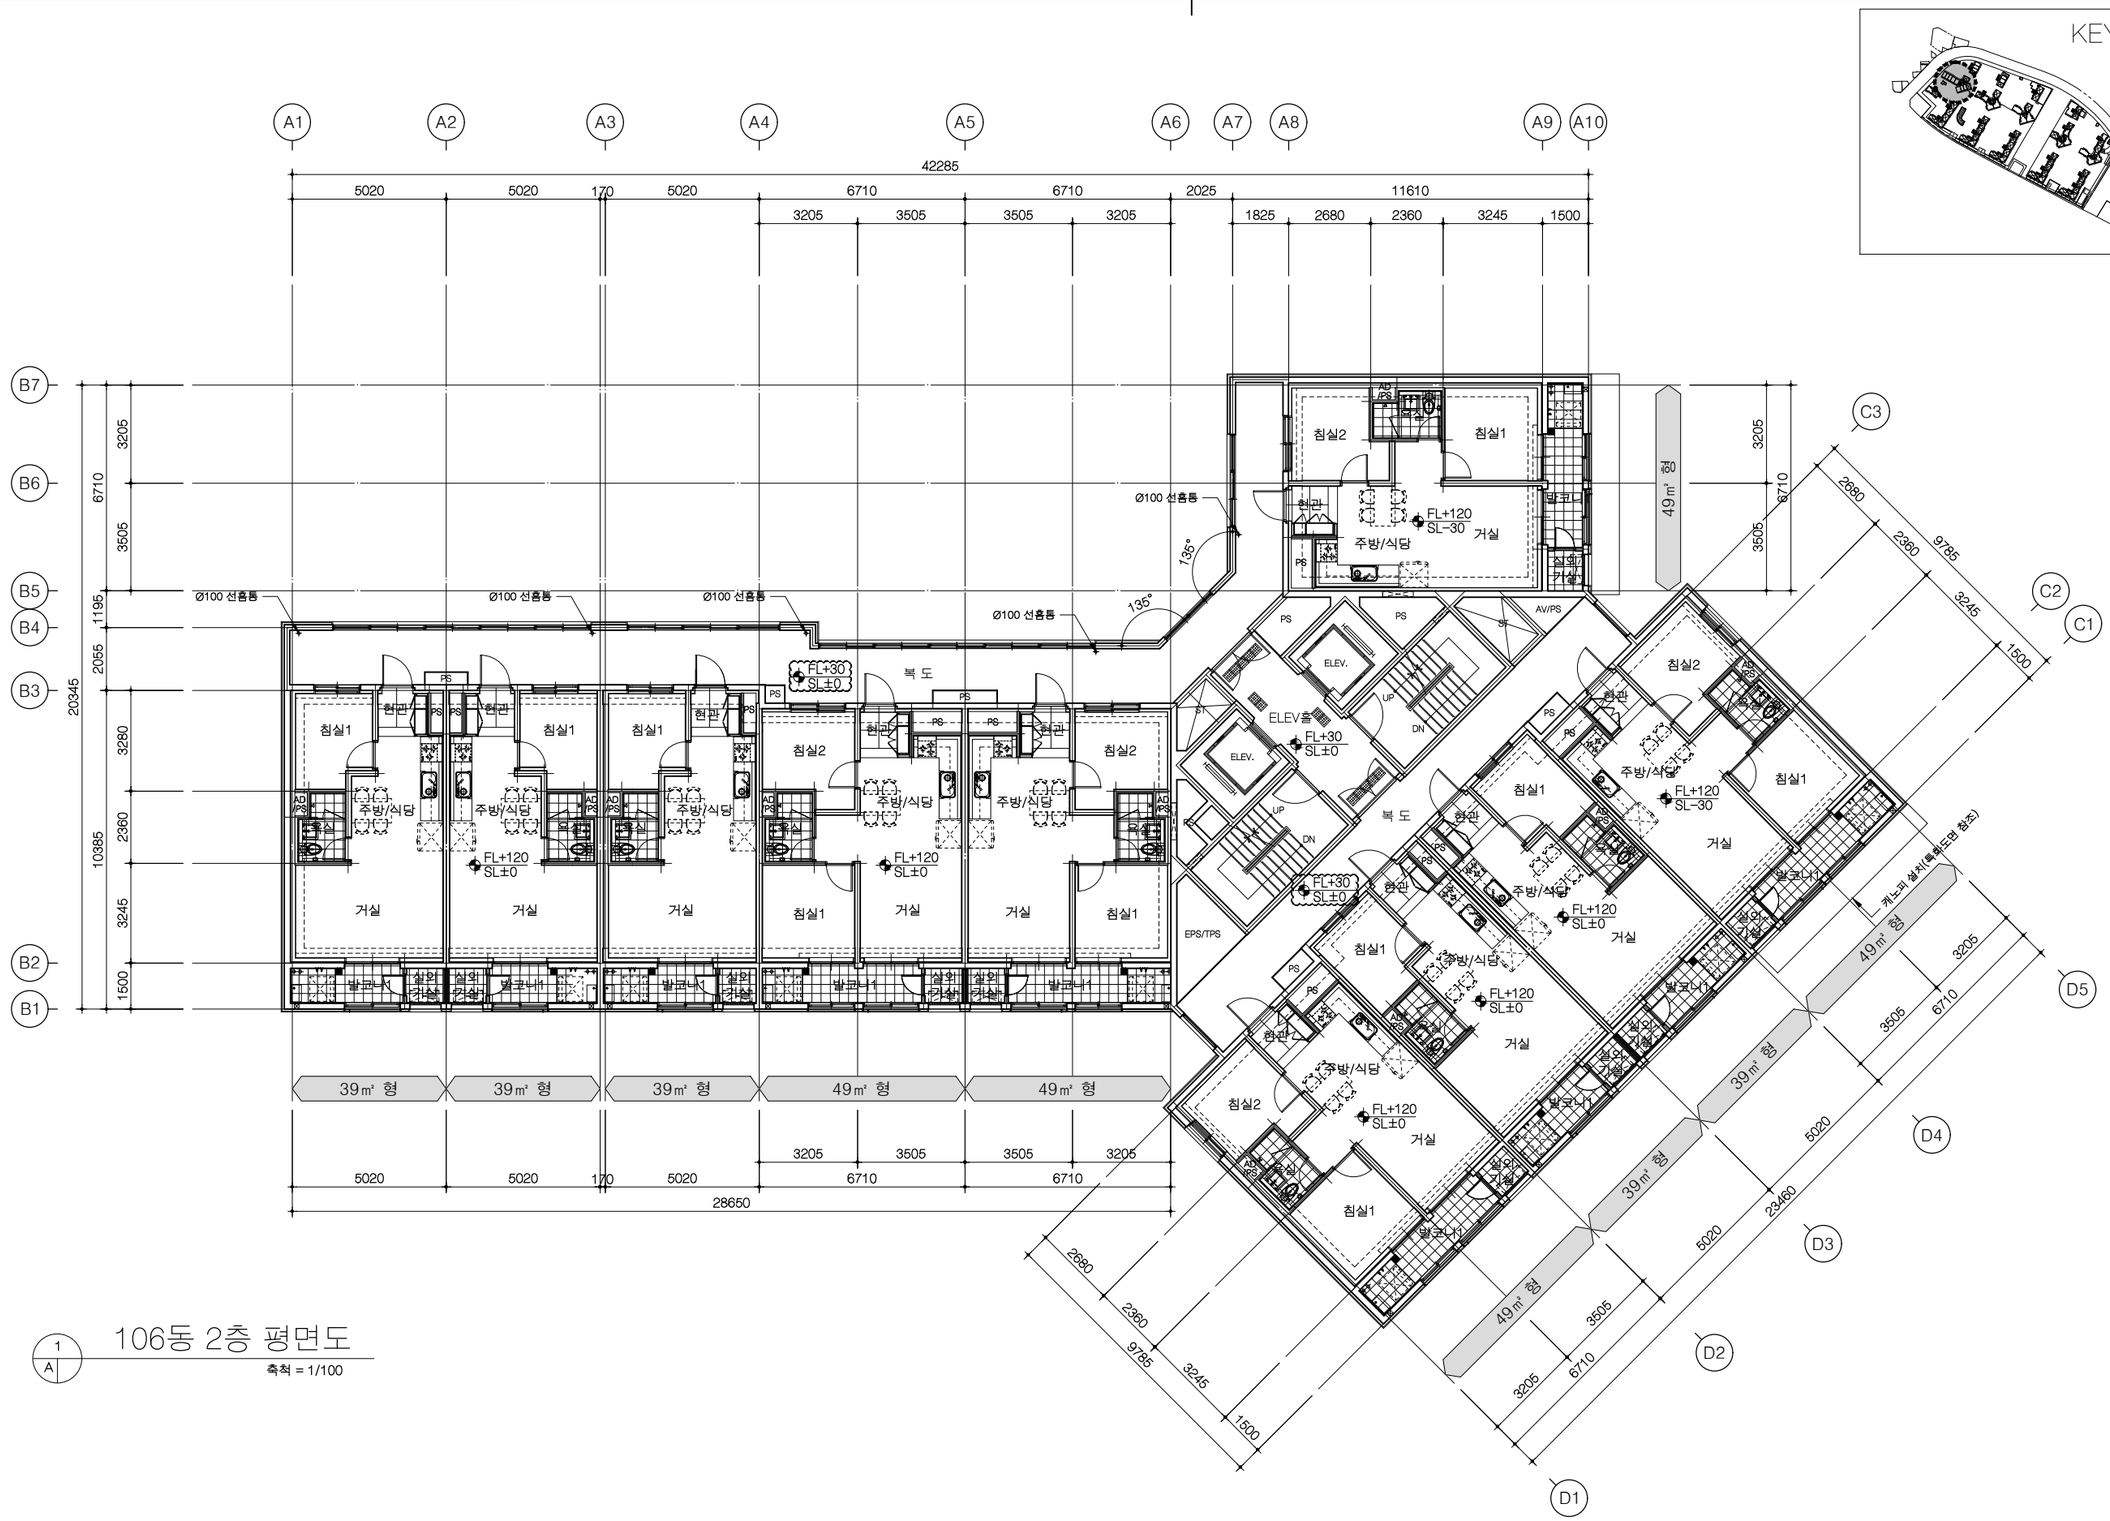

1 A 106동 2층 평면도

축척 = 1/100

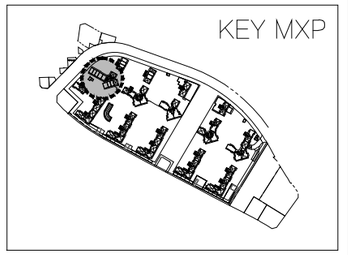

사업번호 PROJECT NO.

사업명 PROJECT TITLE

수색4재정비촉진구역
주택재개발 정비사업

KEY PLAN

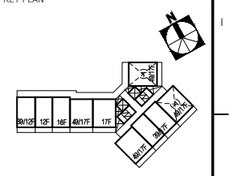

NOTE

1. 본 도면은 발코니 확장전를 기준으로 작성됨.
2. 지붕층 난간의 형태와 설치 위치는 안전성과 입면디자인을 고려하여 변경 가능함.
3. 지붕의 재료, 형태, 구조는 실시공 시 변경 될 수 있음.
4. 지붕 및 옥탑 구조물의 형태와 구조는 실시공 시 변경될 수 있음.
5. 옥상 출눈의 간격은 실시공 시 변경될 수 있음.
6. 옥상 출눈 틈에 실란트 시공되지 않음
7. 우편물 수취함 설치 위치는 변경될 수 있음

2층 바닥LEVEL
2SL±0 = 2FL±0 = EL+31.80

수정번호 REV. NO.	일 자 DATE	내 용 DESCRIPTION	승 인 CHKD
△			
△			
△			
△			

설계 DESIGNED BY

검토 CHECKED BY
최 진 규

심사 SUMMITED BY
정 호 혁

승인 APPROVED BY
이 승 준

일자 DATE
2019.08

도면명 DRAWING TITLE
106동
2층 평면도

축 척 SCALE
A1: 1/100
A3: 1/200

도면번호 DRAWING NO.
A-375

일련번호 SHEET NO. △ REV. NO.

HAUD
(주)하우드엔지니어링
종합건축사사무소
Architects, Planners & Engineers
TEL. 02 2143 4400, SEOUL, KOREA

106동 3층~12층 평면도

1 / A

축척 = 1/100

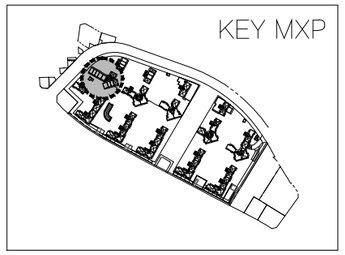

사업번호 PROJECT NO.

사업명 PROJECT TITLE

수색4재정비촉진구역
주택재개발 정비사업

KEY PLAN

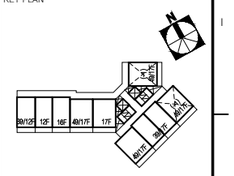

NOTE

1. 본 도면은 발코니 확장전를 기준으로 작성됨.
2. 지붕층 난간의 형태와 설치 위치는 안전성과 입면디자인을 고려하여 변경 가능함.
3. 지붕의 재료, 형태, 구조는 실시공 시 변경 될 수 있음.
4. 지붕 및 옥탑 구조물의 형태와 구조는 실시공 시 변경될 수 있음.
5. 옥상 출눈의 간격은 실시공 시 변경될 수 있음.
6. 옥상 출눈 틈에 실란트 시공되지 않음
7. 우편물 수취함 설치 위치는 변경될 수 있음

수정번호 REV. NO.	일 자 DATE	내 용 DESCRIPTION	승 인 CHKD
△			
△			
△			
△			

설계 DESIGNED BY

검토 CHECKED BY
최 진 규

심사 SUMMITED BY
정 호 혁

승인 APPROVED BY
이 승 준

일자 DATE
2019.08

도면명 DRAWING TITLE
106동
3층~12층 평면도

축 척 SCALE
A1: 1/100
A3: 1/200

도면번호 DRAWING NO.
A-376

일련번호 SHEET NO. / REV. NO. △

HAUD
(주)하우드캔지니어링
종합건축사사무소
Architects, Planners & Engineers
TEL. 02 2143 4400, SEOUL, KOREA

1 A 106동 13층 평면도

축척 = 1/100

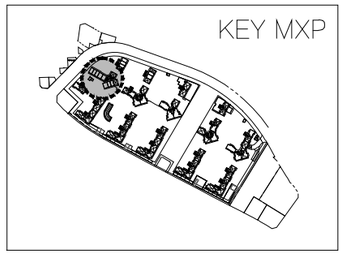

사업번호 PROJECT NO.

사업명 PROJECT TITLE

수색4재정비촉진구역
주택재개발 정비사업

KEY PLAN

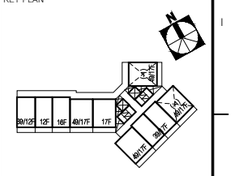

NOTE

1. 본 도면은 발코니 확장전를 기준으로 작성됨.
2. 지붕층 난간의 형태와 설치 위치는 안전성과 입면디자인을 고려하여 변경 가능함.
3. 지붕의 재료, 형태, 구조는 실시공 시 변경 될 수 있음.
4. 지붕 및 옥탑 구조물의 형태와 구조는 실시공 시 변경될 수 있음.
5. 옥상 출눈의 간격은 실시공 시 변경될 수 있음.
6. 옥상 출눈 틈에 실란트 시공되지 않음
7. 우편물 수취함 설치 위치는 변경될 수 있음

수정번호 REV. NO.	일 자 DATE	내 용 DESCRIPTION	승 인 CHKD
△			
△			
△			
△			

설계 DESIGNED BY

검토 CHECKED BY
최 진 규

심사 SUMMITED BY
정 호 혁

승인 APPROVED BY
이 승 준

일자 DATE
2019.08

도면명 DRAWING TITLE
106동
13층 평면도

축 척 SCALE
A1: 1/100
A3: 1/200

도면번호 DRAWING NO.
A-377

일련번호 SHEET NO. △ REV. NO.

HAUD
(주)하우드엔지니어링
종합건축사사무소
Architects, Planners & Engineers
TEL. 02 2143 4400, SEOUL, KOREA

1 A 106동 14층~16층 평면도

축척 = 1/100

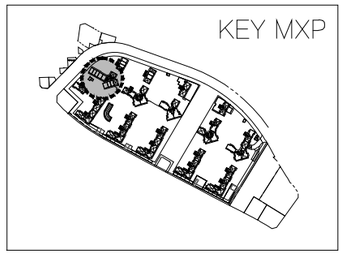

사업번호 PROJECT NO.

사업명 PROJECT TITLE

수색4재정비촉진구역
주택재개발 정비사업

KEY PLAN

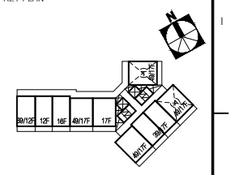

NOTE

1. 본 도면은 발코니 확장전를 기준으로 작성됨.
2. 지붕층 난간의 형태와 설치 위치는 안전성과 입면디자인을 고려하여 변경 가능함.
3. 지붕의 재료, 형태, 구조는 실시공 시 변경 될 수 있음.
4. 지붕 및 옥탑 구조물의 형태와 구조는 실시공 시 변경될 수 있음.
5. 옥상 출눈의 간격은 실시공 시 변경될 수 있음.
6. 옥상 출눈 틈에 실란트 시공되지 않음
7. 우편물 수취함 설치 위치는 변경될 수 있음

수정번호 REV. NO.	일 자 DATE	내 용 DESCRIPTION	승 인 CHKD
△			
△			
△			
△			

설계 DESIGNED BY

검토 CHECKED BY
최 진 규

심사 SUMMITED BY
정 호 혁

승인 APPROVED BY
이 승 준

일자 DATE
2019.08

도면명 DRAWING TITLE
106동
14층~16층 평면도

축 척 SCALE
A1: 1/100
A3: 1/200

도면번호 DRAWING NO.
A-378

일련번호 SHEET NO. △ REV. NO.

HAUD
(주)하우드엔지니어링
종합건축사사무소
Architects, Planners & Engineers
TEL. 02 2143 4400, SEOUL, KOREA

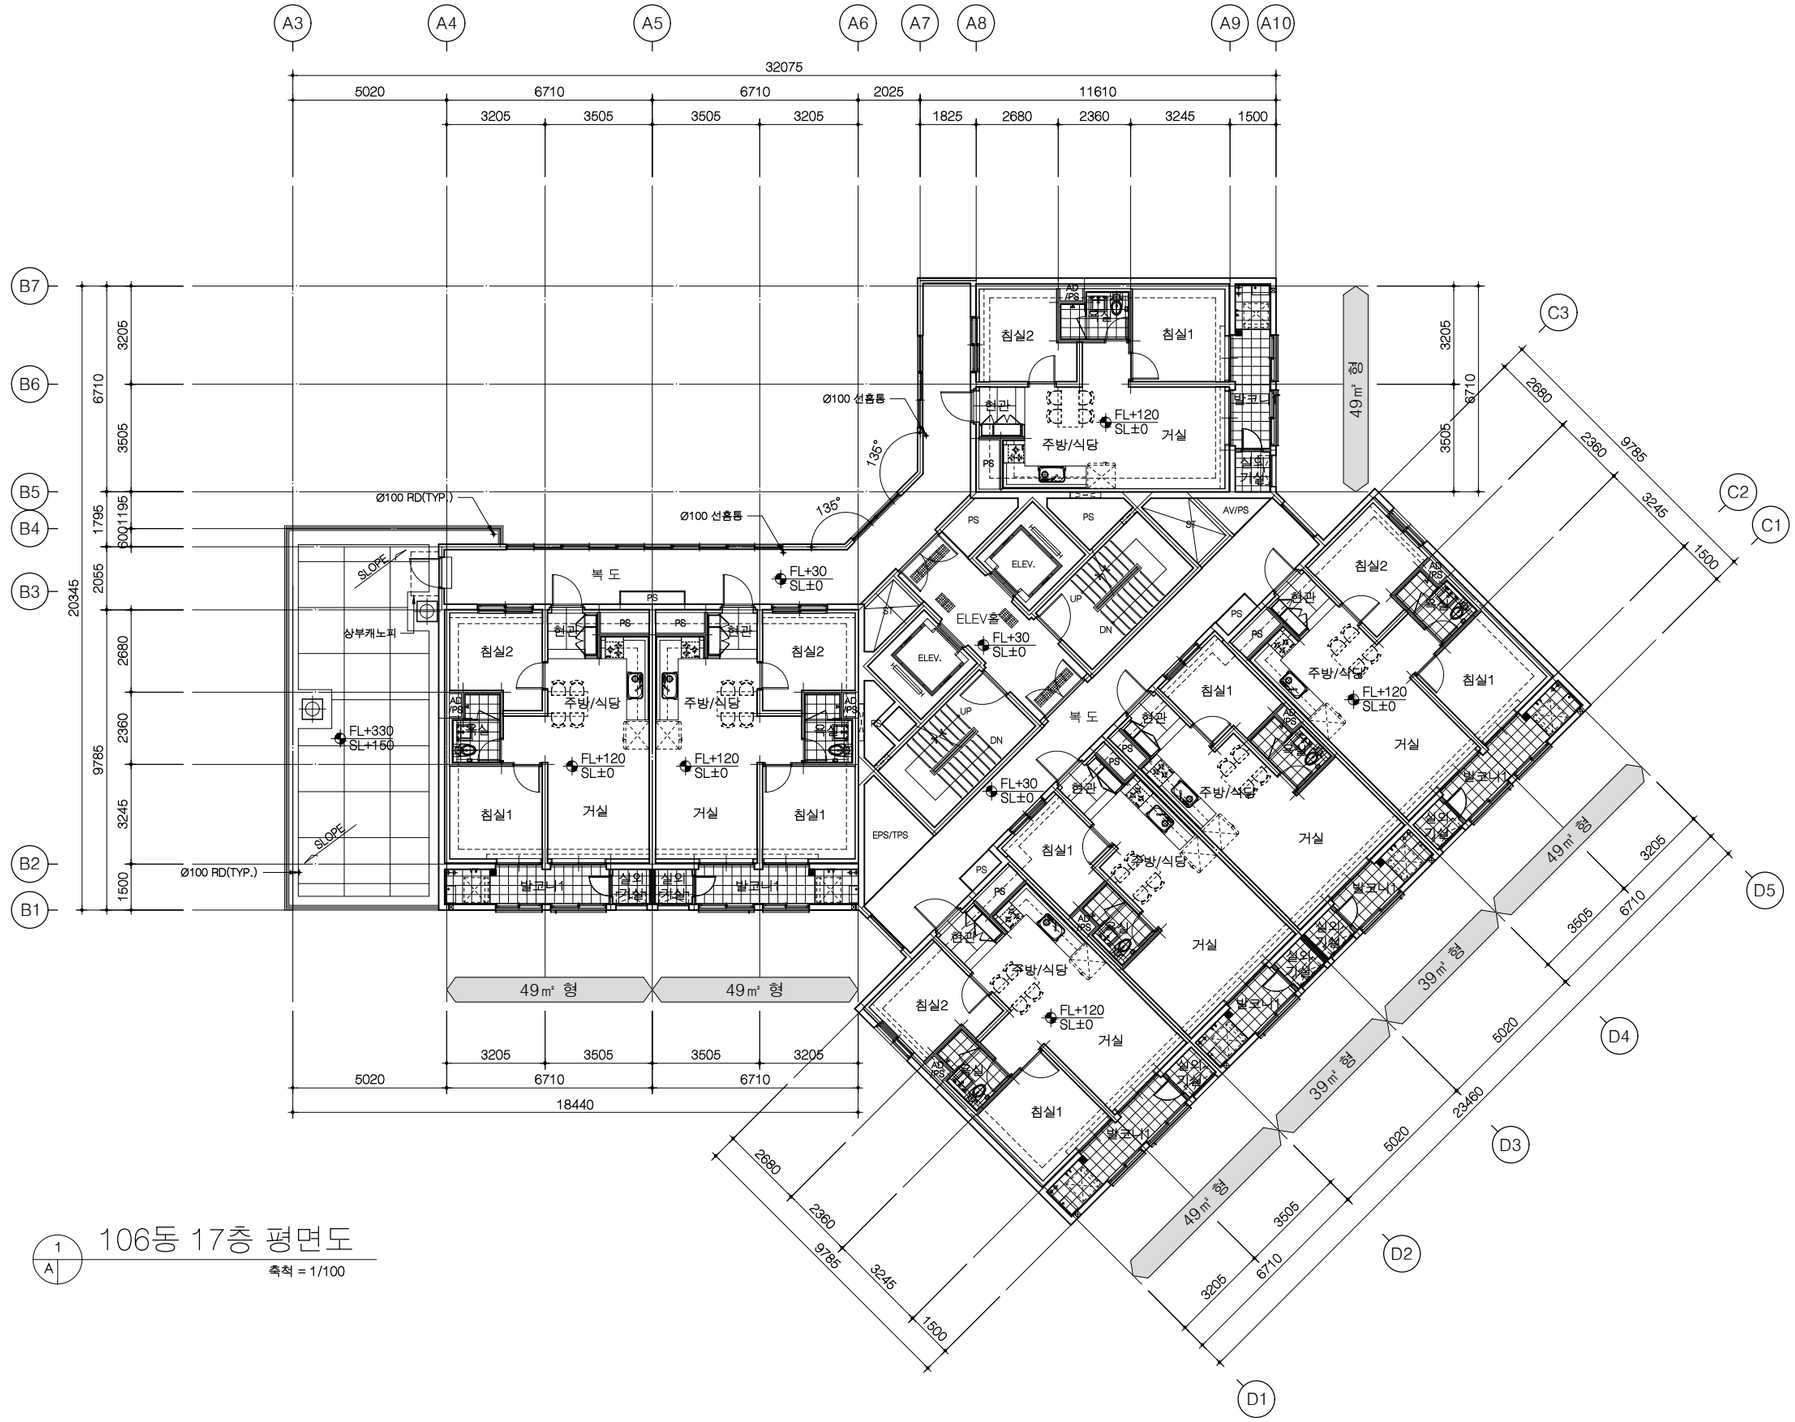

1 A 106동 17층 평면도

축척 = 1/100

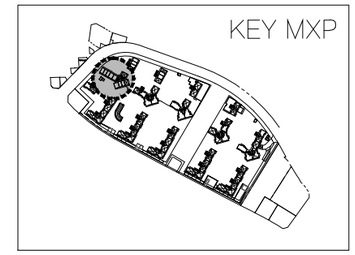

사업번호 PROJECT NO.

사업명 PROJECT TITLE

수색4재정비촉진구역
주택재개발 정비사업

KEY PLAN

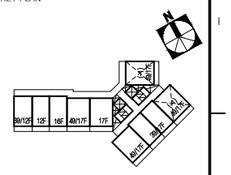

NOTE

1. 본 도면은 발코니 확장전를 기준으로 작성됨.
2. 지붕층 난간의 형태와 설치 위치는 안전성과 입면디자인을 고려하여 변경 가능함.
3. 지붕의 재료, 형태, 구조는 실시공 시 변경 될 수 있음.
4. 지붕 및 옥탑 구조물의 형태와 구조는 실시공 시 변경될 수 있음.
5. 옥상 출눈의 간격은 실시공 시 변경될 수 있음.
6. 옥상 출눈 틈에 실란트 시공되지 않음
7. 우편물 수취함 설치 위치는 변경될 수 있음

수정번호 REV. NO.	일 자 DATE	내 용 DESCRIPTION	승 인 CHKD
△			
△			
△			
△			

설계 DESIGNED BY

검토 CHECKED BY
최 진 규

심사 SUMMITED BY
정 호 혁

승인 APPROVED BY
이 승 준

일자 DATE
2019.08

도면명 DRAWING TITLE
106동
17층 평면도

축 척 SCALE
A1: 1/100
A3: 1/200

도면번호 DRAWING NO.
A-379

일련번호 SHEET NO. △ REV. NO.

HAUD
(주)하우드엔지니어링
종합건축사사무소
Architects, Planners & Engineers
TEL. 02 2143 4400, SEOUL, KOREA

1 A 106동 지붕 평면도

축척 = 1/100

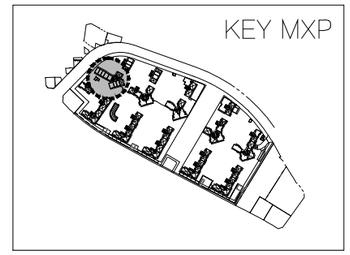

사업번호 PROJECT NO.

사업명 PROJECT TITLE

수색4재정비촉진구역
주택재개발 정비사업

KEY PLAN

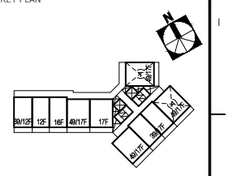

NOTE

1. 지붕바닥
   ① EXP. JOINT: 3000 X 3000
2. 본 평면도는 발코니확장전을 기준으로 작성됨
3. 재료마감은 실내,외 재료마감표 참조
4. 지붕 난간형태/설치위치는 안전성과 입면을 고려하여 실시공시 변경될 수 있음
5. 지붕재료 및 형태,구조는 실시공시 변경될수 있음
6. 지붕(옥탑지붕)의 배수드레인,청소용고리, 베기탑,점검사다리(점검구) 등의 설치위치/개소는 실시공시 변경될 수 있음
7. 옥상 상부구조물은 PC구조물 임.
8. 정화조 배기는 기계도서 참조

수정번호 REV. NO.	일 자 DATE	내 용 DESCRIPTION	승 인 CHKD
△			
△			
△			
△			

설계 DESIGNED BY

검토 CHECKED BY
최 진 규

심사 SUMMITED BY
정 호 혁

승인 APPROVED BY
이 승 준

일자 DATE
2019.08

도면명 DRAWING TITLE
106동
지붕 평면도

축 척 SCALE
A1: 1/100
A3: 1/200

도면번호 DRAWING NO.
A-380

일련번호 SHEET NO.

△ REV. NO.

HAUD
㈜하우드엔지니어링
종합건축사사무소
Architects, Planners & Engineers
TEL. 02 2140 4400, SEOUL, KOREA

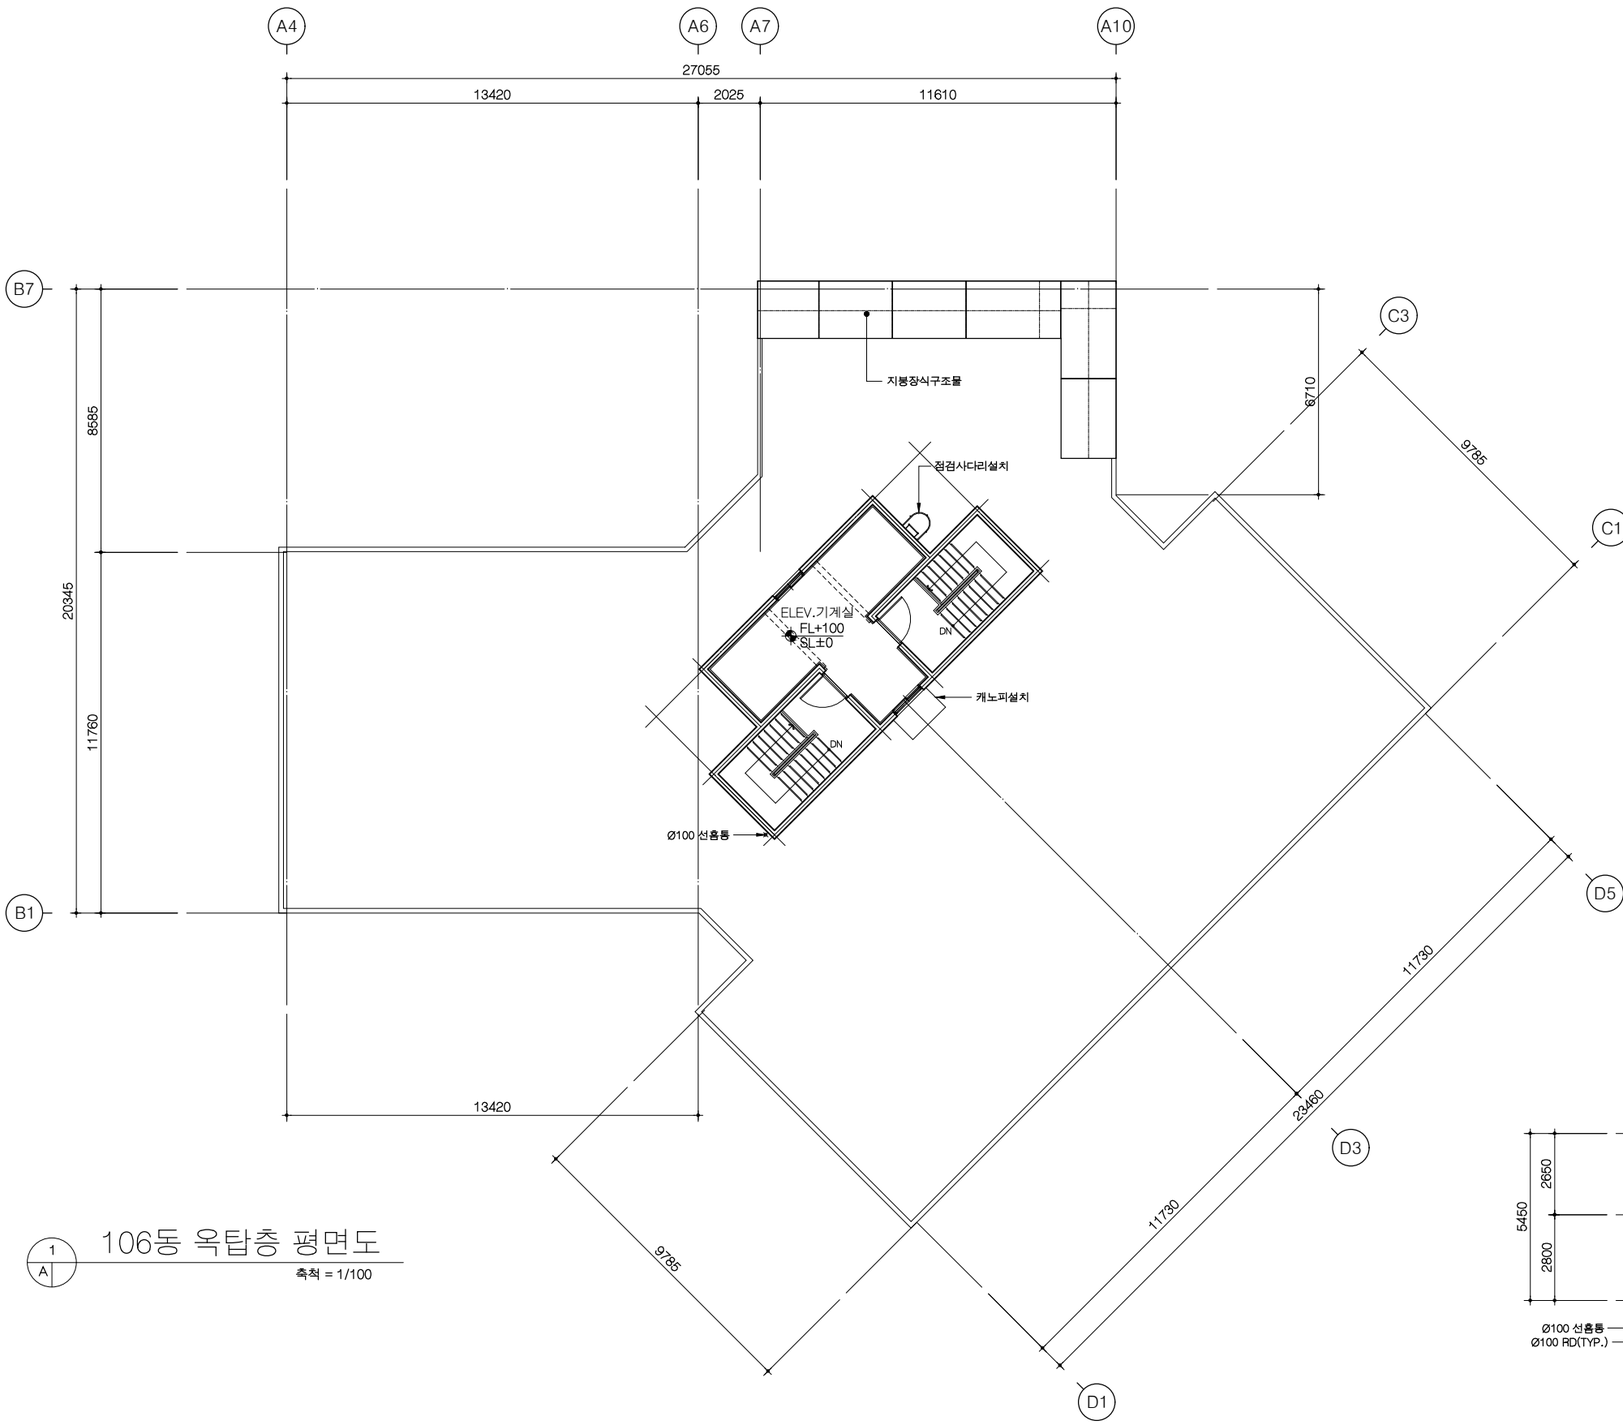

1 A 106동 옥탑층 평면도

축척 = 1/100

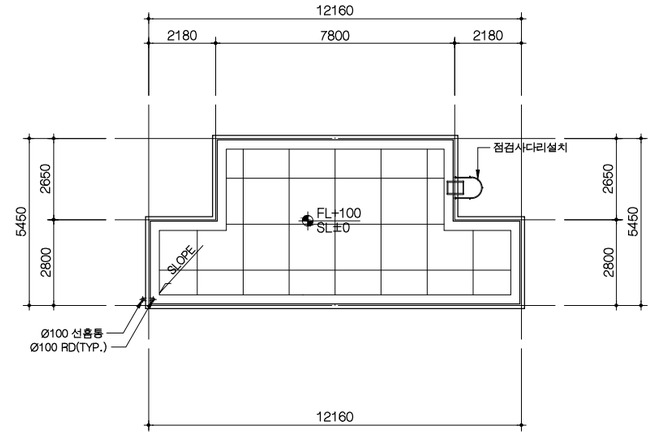

2 A 106동 옥탑지붕 평면도

축척 = 1/100

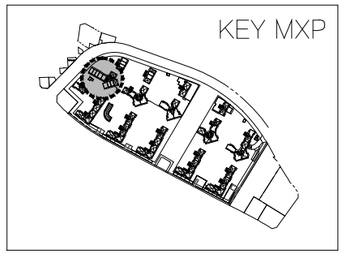

사업번호 PROJECT NO.

사업명 PROJECT TITLE

수색4재정비촉진구역
주택재개발 정비사업

KEY PLAN

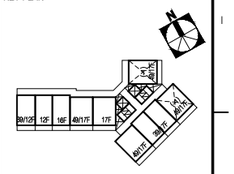

NOTE

1. 지붕바닥
   ① EXP. JOINT: 3000 X 3000
2. 본 평면도는 발코니확장전을 기준으로 작성됨
3. 재료마감은 실내,외 재료마감표 참조
4. 지붕 난간형태/설치위치는 안전성과 입면을 고려하여 실시공시 변경될 수 있음
5. 지붕재료 및 형태,구조는 실시공시 변경될수 있음
6. 지붕(옥탑지붕)의 배수드레인,환소음고리, 베기탑,점검사다리(점검구) 등의 설치위치/개소는 실시공시 변경될 수 있음
7. 옥상 상부구조물은 PC구조물 임.
8. 정화조 배기는 기계도서 참조

수정번호 REV. NO.	일 자 DATE	내 용 DESCRIPTION	승 인 CHKD

설계 DESIGNED BY

검토 CHECKED BY
최 진 규

심사 SUMMITED BY
정 호 혁

승인 APPROVED BY
이 승 준

일자 DATE
2019.08

도면명 DRAWING TITLE
106동
옥탑층 및 옥탑지붕 평면도

축 척 SCALE
A1: 1/100
A3: 1/200

도면번호 DRAWING NO.
A-381

일련번호 SHEET NO.

REV. NO.

HAUD
(주)하우드엔지니어링
종합건축사사무소
Architects, Planners & Engineers
TEL. 02 2140 4400, SEOUL, KOREA

1 A 106동 정면도

축척 = 1/150

2 A 106동 우측면도

축척 = 1/150

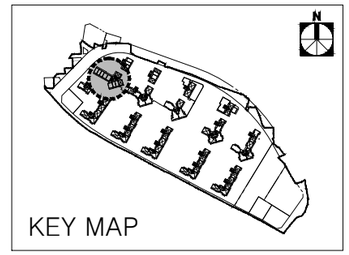

사업번호 PROJECT NO.

사업명 PROJECT TITLE

수색4재정비촉진구역
주택재개발 정비사업

KEY PLAN

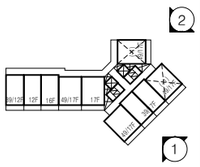

NOTE

1. 1층 바닥 LEVEL
   1SL±0 = 1FL±0 = GL±0 = EL+28.60
2. 지붕 난간의 형태 및 설치위치는 안전성과 입면디자인을 고려하여 변경가능함.
3. 지붕의 재료, 형태, 구조는 실시공시 변경될 수 있음.
4. 지붕 및 옥탑구조물의 형태와 구조는 실시공시 변경될 수 있음.
5. 외벽 및 측벽 문양은 실시공시 변경될 수 있음
6. 입면의 줄눈 및 마감선은 실시공시 변경될 수 있음.
7. 저층부 석재마감 및 입면 마감 색상, 재료에 대한 모든 기준은 특화도면을 우선 적용함.

수정번호 REV. NO.	일 자 DATE	내 용 DESCRIPTION	승 인 CHKD
△			
△			
△			
△			

설계 DESIGNED BY

검토 CHECKED BY
최 진 규

심사 SUMMITED BY
정 호 혁

승인 APPROVED BY
이 승 준

일자 DATE
2019.08

도면명 DRAWING TITLE
106동 정면도,우측면도

축 척 SCALE
A1: 1/150
A3: 1/300

도면번호 DRAWING NO.
A-382

일련번호 SHEET NO.

△ REV. NO.

HAUD
(주)하우드엔지니어링
종합건축사사무소
Architects, Planners & Engineers
TEL. 82 2140 4400, SEOUL, KOREA

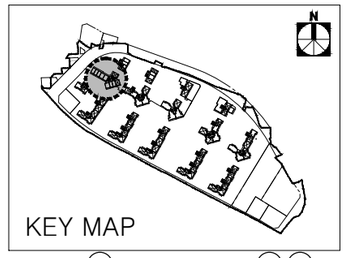

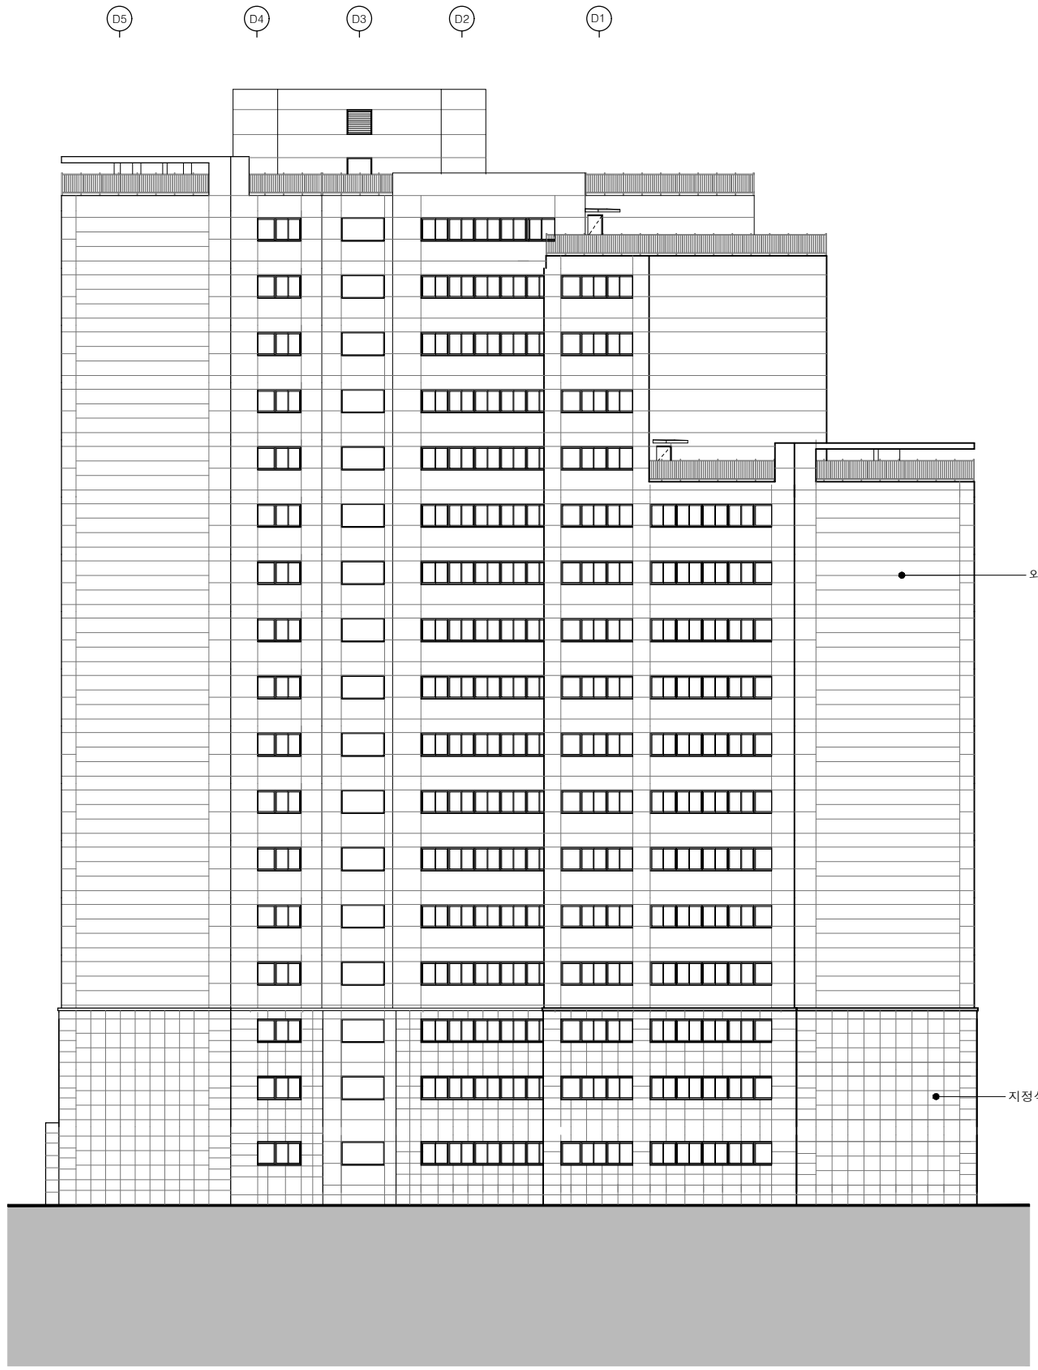

1 A 106동 배면도

축척 = 1/150

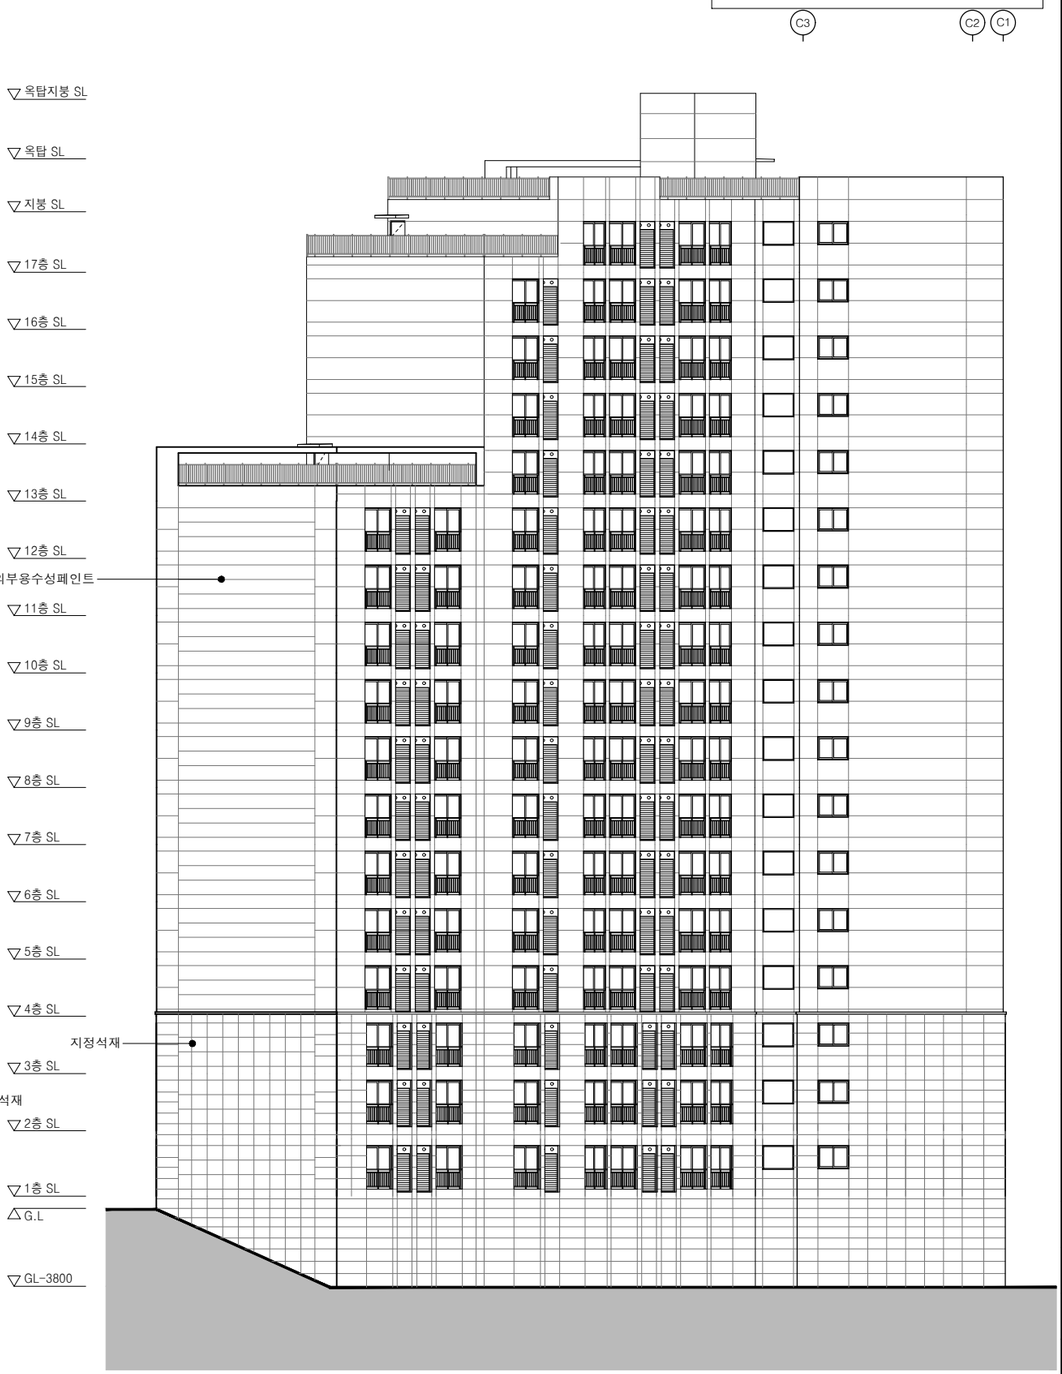

2 A 106동 좌측면도

축척 = 1/150

사업번호 PROJECT NO.

사업명 PROJECT TITLE

수색4재정비촉진구역
주택재개발 정비사업

KEY PLAN

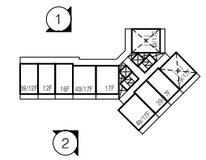

NOTE

1. 1층 바닥 LEVEL
   1SL±0 = 1FL±0 = GL±0 = EL+28.60
2. 지붕 난간의 형태 및 설치위치는 안전성과 입면디자인을 고려하여 변경가능함.
3. 지붕의 재료, 형태, 구조는 실시공시 변경될 수 있음.
4. 지붕 및 옥탑구조물의 형태와 구조는 실시공시 변경될 수 있음.
5. 외벽 및 측벽 문양은 실시공시 변경될 수 있음
6. 입면의 줄눈 및 마감선은 실시공시 변경될 수 있음.
7. 저층부 석재마감 및 입면 마감 색상, 재료에 대한 모든 기준은 특화도면을 우선 적용함.

수정번호 REV. NO.	일 자 DATE	내 용 DESCRIPTION	승 인 CHKD
△			
△			
△			
△			

설계 DESIGNED BY

검토 CHECKED BY
최 진 규

심사 SUMMITED BY
정 호 혁

승인 APPROVED BY
이 승 준

일자 DATE
2019.08

도면명 DRAWING TITLE
106동 배면도,좌측면도

축 척 SCALE
A1: 1/150
A3: 1/300

도면번호 DRAWING NO.
A-383

일련번호 SHEET NO.

△ REV. NO.

HAUD
(주)하우드엔지니어링
종합건축사사무소
Architects, Planners & Engineers
TEL. 82 2140 4400, SEOUL, KOREA

1 A 106동 종단면도

축척 = 1/150

2 A 106동 횡단면도

축척 = 1/150

사업번호 PROJECT NO.

사업명 PROJECT TITLE

수색4재정비촉진구역
주택재개발 정비사업

KEY PLAN

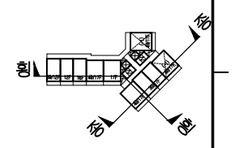

NOTE

수정번호 REV. NO.	일 자 DATE	내 용 DESCRIPTION	승 인 CHKD
1			
2			
3			
4			

설계 DESIGNED BY

검토 CHECKED BY 최 진 규

심사 SUMMITED BY 정 호 혁

승인 APPROVED BY 이 승 준

일자 DATE 2019.08

도면명 DRAWING TITLE

106동 종,횡단면도

축 척 SCALE
A1: 1/150
A3: 1/300

도면번호 DRAWING NO. A-384

일련번호 SHEET NO. REV. NO.

HAUD
(주)하우드엔지니어링
종합건축사사무소
Architects, Planners & Engineers
TEL. 82 2 1 4G 4408, SEOUL, KOREA

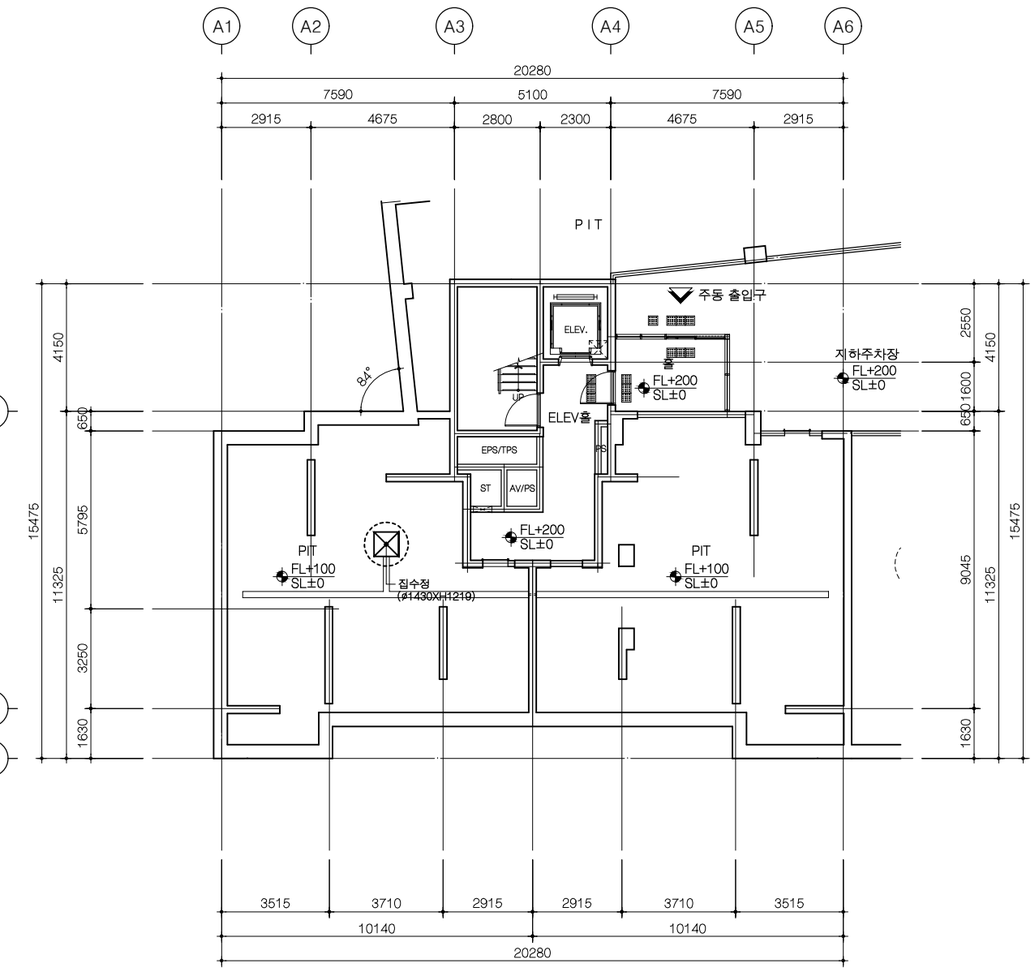

1 A 107동 지하3층 평면도

축척 = 1/100

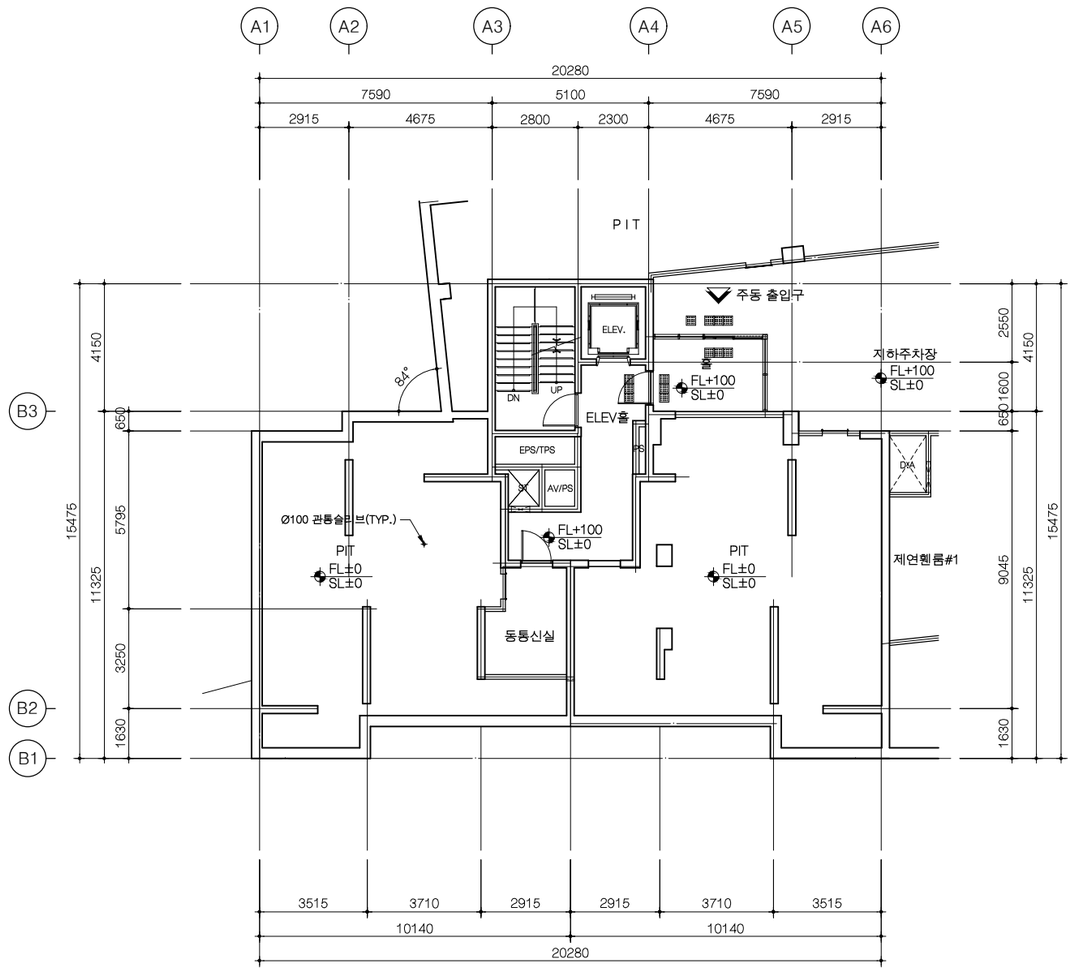

2 A 107동 지하2층 평면도

축척 = 1/100

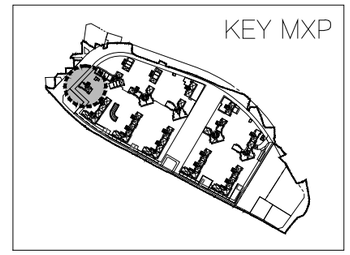

사업번호 PROJECT NO.

사업명 PROJECT TITLE

수색4재정비촉진구역
주택재개발 정비사업

KEY PLAN

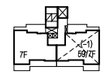

NOTE

1. 지하층 무근 콘크리트는 실시공시 THK80~120 범위로 변동이 있을수 있음.(SLOPE)
2. ELEV홀에 면한부위는 1.0B 조적쌓기임.
3. 지하주차장의 블록쌓기 기준은 높이가 3.6m이하인 경우 4인치 보강블록쌓기가 기준임 (단, 5.4m이하는 6인치쌓기, 5.4m초과는 8인치쌓기가 기준임)
4. ELEV.PIT 집수정은 (600X600X600)임.
5. 주차장 내의 창호는 주차장 창호도 참조.
6. 주차장 집수정 및 영구배수 집수정의 크기 및 위치는 지하주차장 평면도를 참조 할 것.
   ⊠: 주차장 집수정(ø1430XH1219)
   ⊠: 영구배수 집수정(ø1760XH1524)
   ⊠: 아파트 집수정(ø1430XH1219)

********** 지하3층 바닥LEVEL
B3SL±0 = B3FL±0 = EL+15.85
**** 지하2층 바닥LEVEL
B2SL±0 = B2FL±0 = EL+19.30

수정번호 REV. NO.	일 자 DATE	내 용 DESCRIPTION	승 인 CHKD
△			
△			
△			
△			

설계 DESIGNED BY

검토 CHECKED BY
최 진 규

심사 SUMMITED BY
정 호 혁

승인 APPROVED BY
이 승 준

일자 DATE
2019.08

도면명 DRAWING TITLE
107동
지하3층 및 지하2층 평면도

축 척 SCALE
A1: 1/100
A3: 1/200

도면번호 DRAWING NO.
A-391

얼럿번호 SHEET NO.

△ REV. NO.

HAUD
㈜하우드엔지니어링
종합건축사사무소
Architects, Planners & Engineers
TEL. 02 2140 4400, SEOUL, KOREA

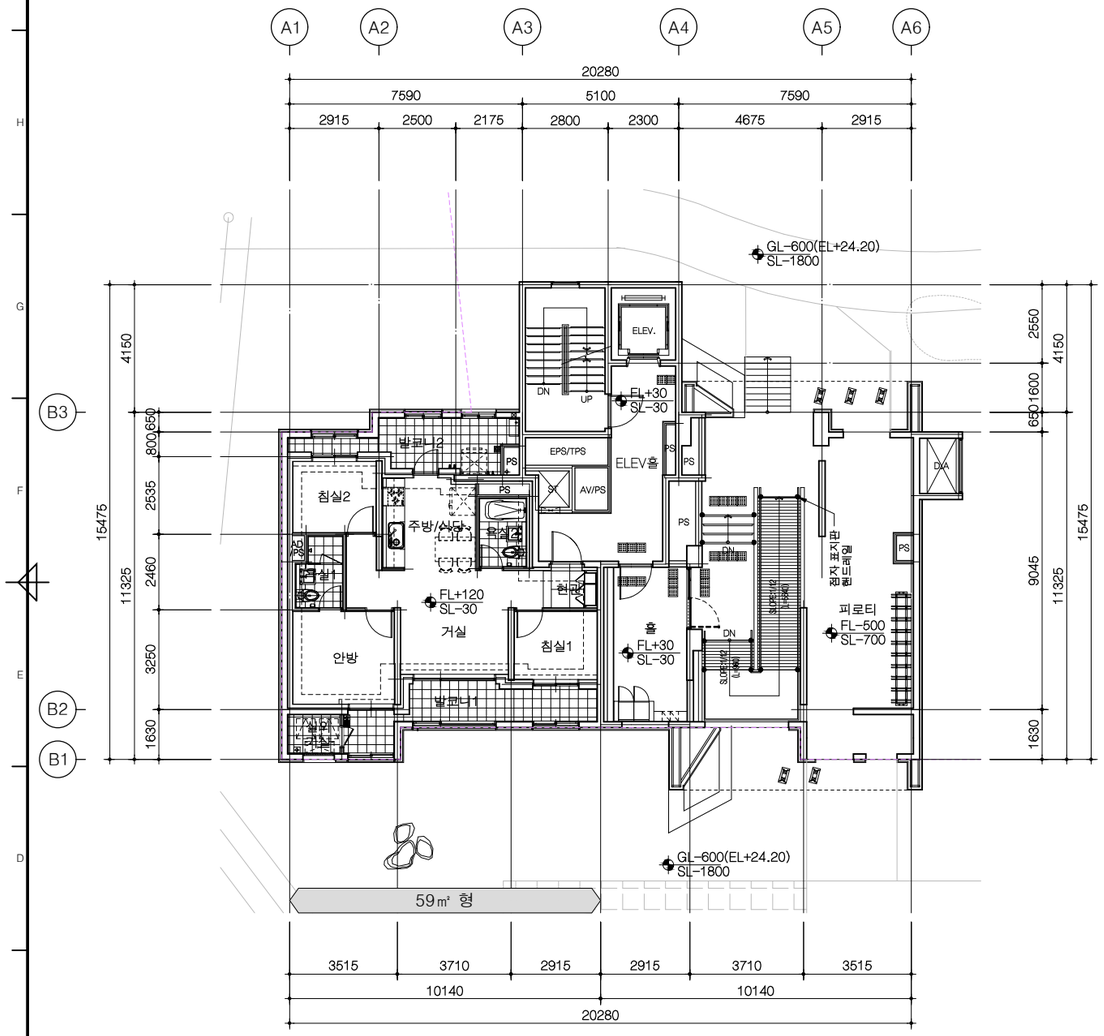

1 A 107동 1층 평면도

축척 = 1/100

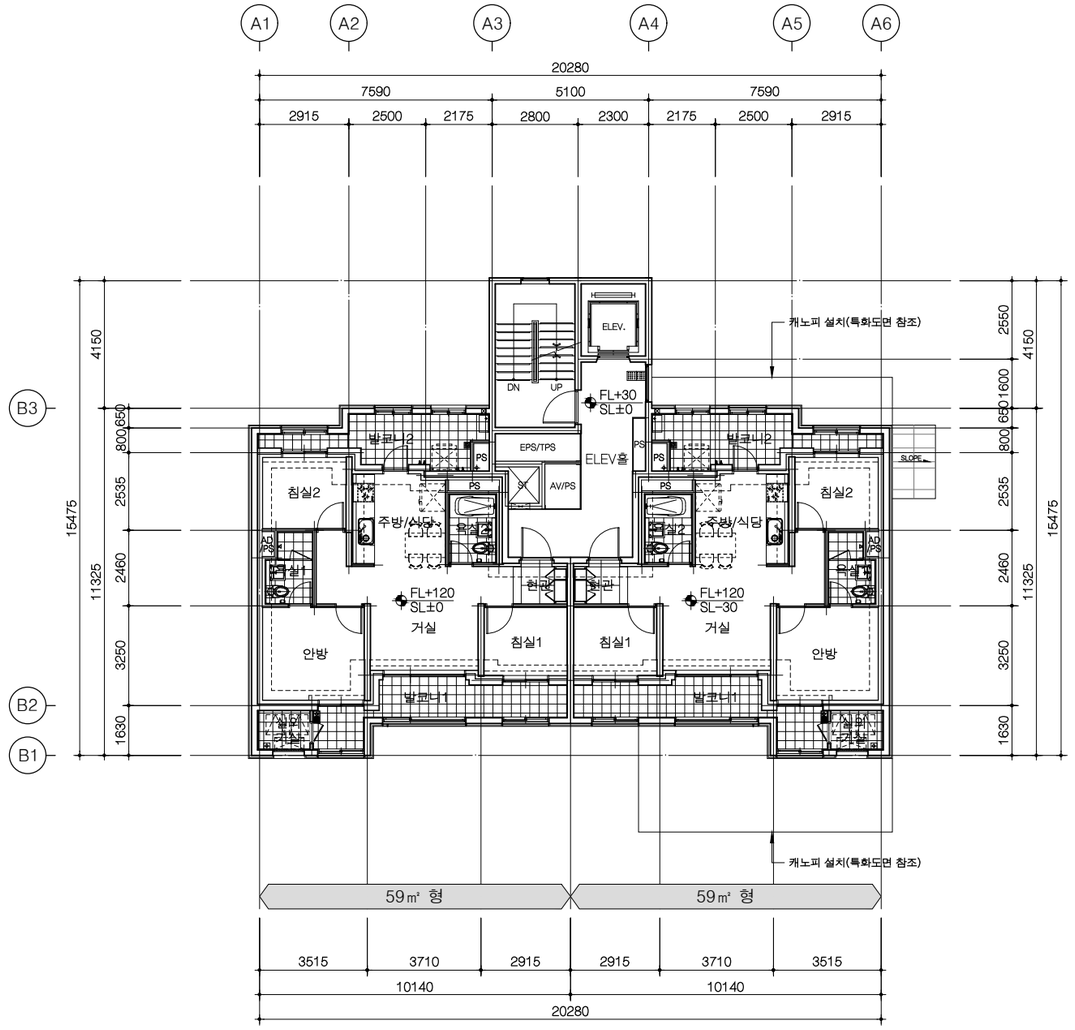

2 A 107동 2층 평면도

축척 = 1/100

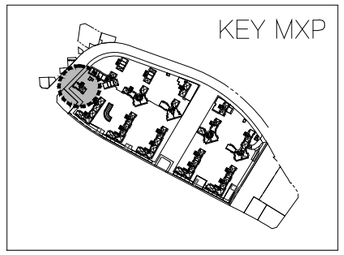

사업번호 PROJECT NO.

사업명 PROJECT TITLE

수색4재정비촉진구역
주택재개발 정비사업

KEY PLAN

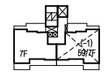

NOTE

1. 본 도면은 발코니 확장전를 기준으로 작성됨.
2. 지붕층 난간의 형태와 설치 위치는 안전성과 입면디자인을 고려하여 변경 가능함.
3. 지붕의 재료, 형태, 구조는 실시공 시 변경 될 수 있음.
4. 지붕 및 옥탑 구조물의 형태와 구조는 실시공 시 변경될 수 있음.
5. 옥상 출눈의 간격은 실시공 시 변경될 수 있음.
6. 옥상 출눈 틈에 실란트 시공되지 않음
7. 우편물 수취함 설치 위치는 변경될 수 있음

* 1층 바닥LEVEL
  1SL±0 = 1FL±0 = GL±0 = EL+24.80
  GL-600 = EL+24.20(토목도면 참조)
* 2층 바닥LEVEL
  2SL±0 = 2FL±0 = EL+28.00

수정번호 REV. NO.	일 자 DATE	내 용 DESCRIPTION	승 인 CHKD
1			
2			
3			
4			

설계 DESIGNED BY

검토 CHECKED BY
최 진 규

심사 SUMMITED BY
정 호 혁

승인 APPROVED BY
이 승 준

일자 DATE
2019.08

도면명 DRAWING TITLE
107동
1층 및 2층 평면도

축 척 SCALE
A1: 1/100
A3: 1/200

도면번호 DRAWING NO.
A-392

일련번호 SHEET NO.

REV. NO.

HAUD
㈜하우드엔지니어링
종합건축사사무소
Architects, Planners & Engineers
TEL. 02 2149 4400, SEOUL, KOREA

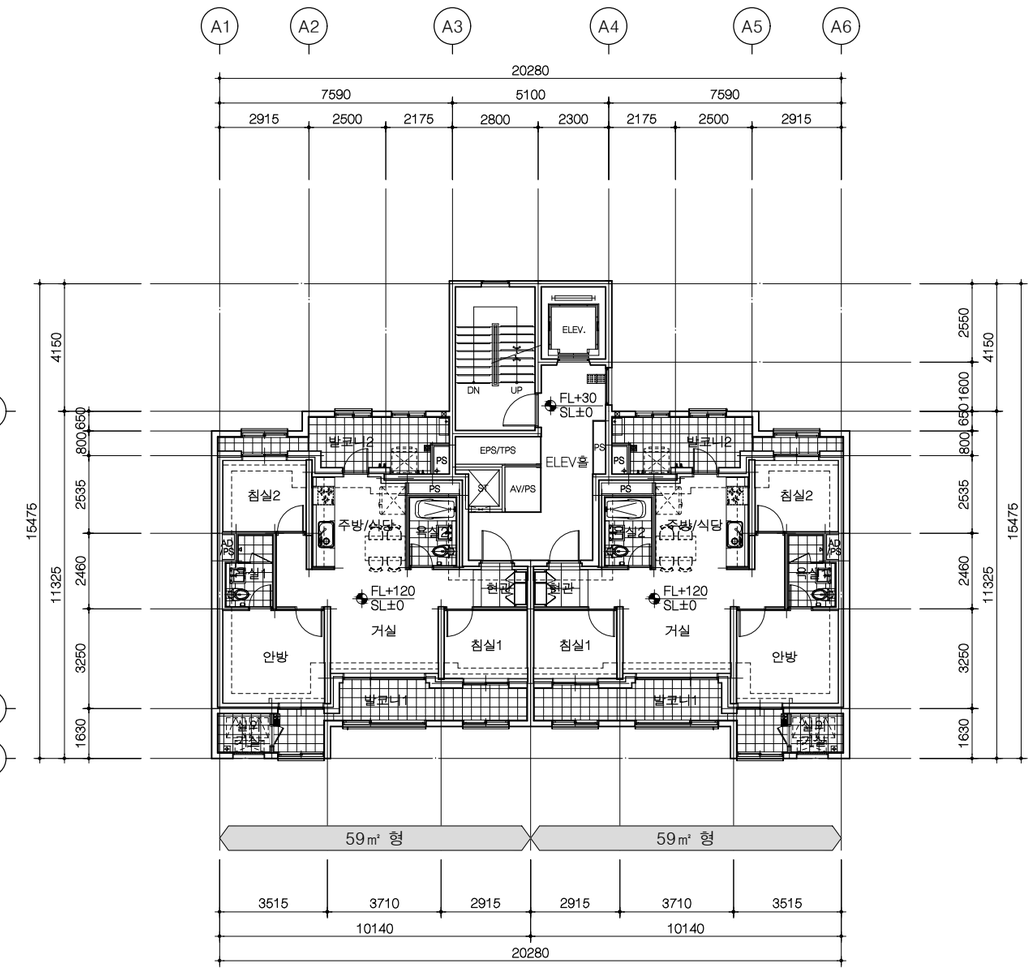

1 A 107동 3~7층 평면도

축척 = 1/100

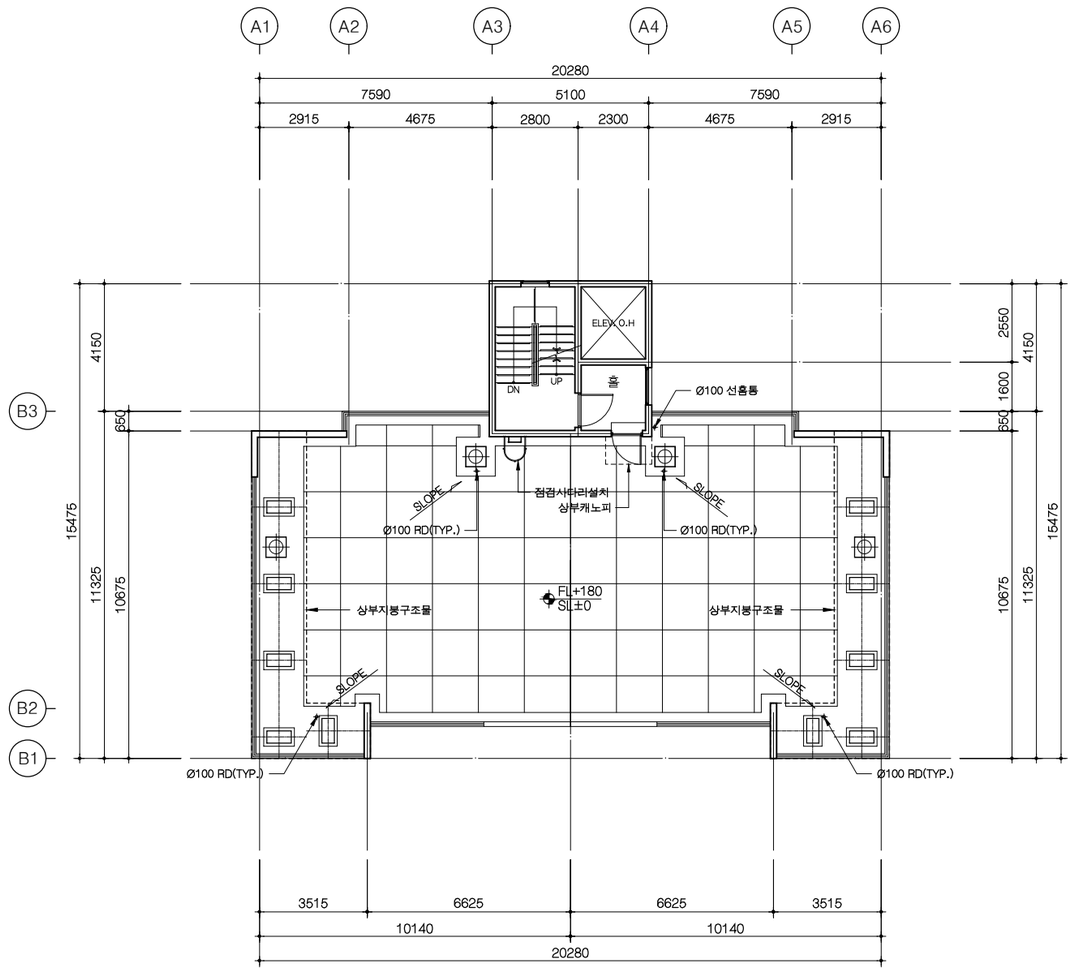

2 A 107동 지붕 평면도

축척 = 1/100

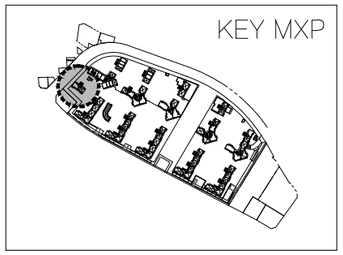

사업번호 PROJECT NO.

사업명 PROJECT TITLE

수색4재정비촉진구역
주택재개발 정비사업

KEY PLAN

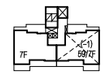

NOTE

1. 본 도면은 발코니 확장전를 기준으로 작성됨.
2. 지붕층 난간의 형태와 설치 위치는 안전성과 입면디자인을 고려하여 변경 가능함.
3. 지붕의 재료, 형태, 구조는 실시공 시 변경 될 수 있음.
4. 지붕 및 옥탑 구조물의 형태와 구조는 실시공 시 변경될 수 있음.
5. 옥상 출눈의 간격은 실시공 시 변경될 수 있음.
6. 옥상 출눈 틈에 실란트 시공되지 않음
7. 우편물 수취함 설치 위치는 변경될 수 있음

수정번호 REV. NO.	일 자 DATE	내 용 DESCRIPTION	승 인 CHKD
△			
△			
△			
△			

설계 DESIGNED BY

검토 CHECKED BY
최 진 규

심사 SUMMITED BY
정 호 혁

승인 APPROVED BY
이 승 준

일자 DATE
2019.08

도면명 DRAWING TITLE
107동
3~7층 및 지붕 평면도

축척 SCALE
A1: 1/100
A3: 1/200

도면번호 DRAWING NO.
A-393

일련번호 SHEET NO.

△ REV. NO.

HAUD
(주)하우드엔지니어링
종합건축사사무소
Architects, Planners & Engineers
TEL. 02 2140 4400, SEOUL, KOREA

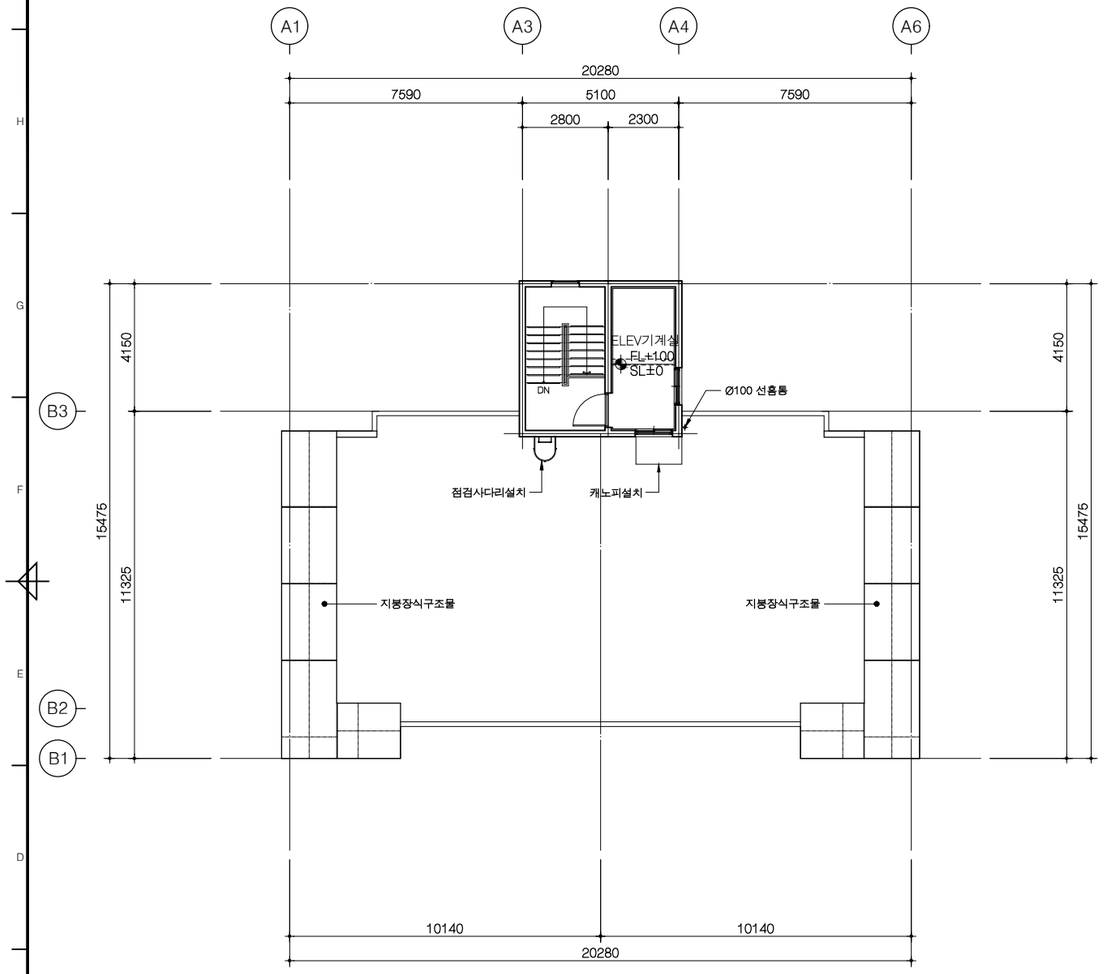

1 A 107동 옥탑층 평면도

축척 = 1/100

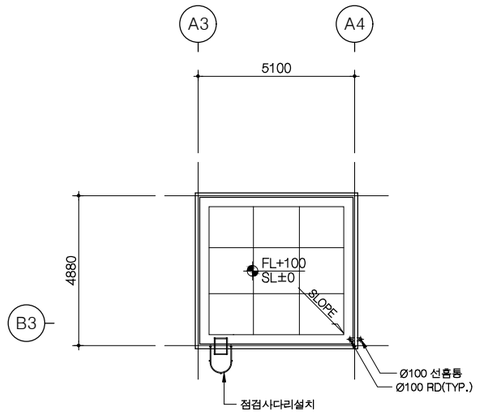

2 A 107동 옥탑지붕 평면도

축척 = 1/100

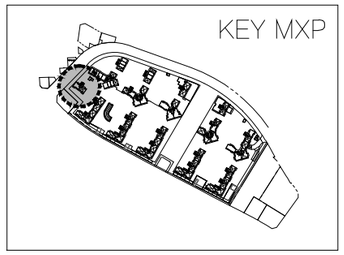

사업번호 PROJECT NO.

사업명 PROJECT TITLE

수색4재정비촉진구역
주택재개발 정비사업

KEY PLAN

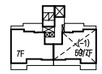

NOTE

1. 지붕바닥
   ① EXP. JOINT: 3000 X 3000
2. 본 평면도는 발코니확장전을 기준으로 작성됨
3. 재료마감은 실내,외 재료마감표 참조
4. 지붕 난간형태/설치위치는 안전성과 입면을 고려하여 실시공시 변경될 수 있음
5. 지붕재료 및 형태,구조는 실시공시 변경될수 있음
6. 지붕(옥탑지붕)의 배수드레인,청소용고리, 베기탑,점검사다리(점검구) 등의 설치위치/개소는 실시공시 변경될 수 있음
7. 옥상 상부구조물은 PC구조물 임.
8. 정화조 배기는 기계도서 참조

수정번호 REV. NO.	일 자 DATE	내 용 DESCRIPTION	승 인 CHKD
△			
△			
△			
△			

설계 DESIGNED BY

검토 CHECKED BY
최 진 규

심사 SUMMITED BY
정 호 혁

승인 APPROVED BY
이 승 준

일자 DATE
2019.08

도면명 DRAWING TITLE
107동
옥탑층 및 옥탑지붕 평면도

축 척 SCALE
A1: 1/100
A3: 1/200

도면번호 DRAWING NO.
A-394

일련번호 SHEET NO.

△ REV. NO.

HAUD
㈜하우드엔지니어링
종합건축사사무소
Architects, Planners & Engineers
TEL. 02 2140 4400, SEOUL, KOREA

1 A 107동 정면도

축척 = 1/150

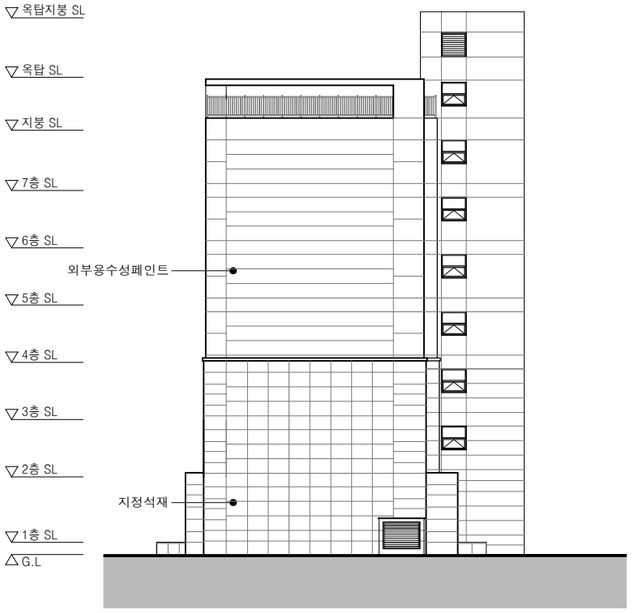

2 A 107동 우측면도

축척 = 1/150

3 A 107동 배면도

축척 = 1/150

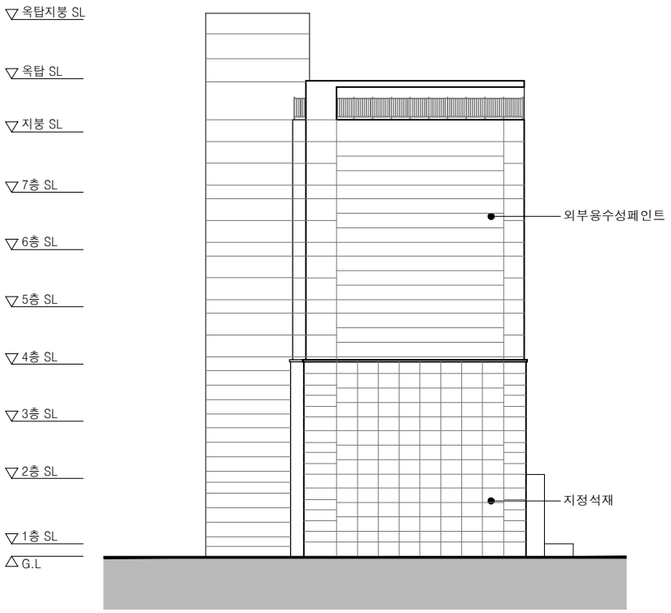

4 A 107동 좌측면도

축척 = 1/150

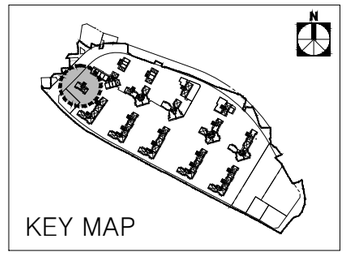

사업번호 PROJECT NO.

사업명 PROJECT TITLE

수색4재정비촉진구역
주택재개발 정비사업

KEY PLAN

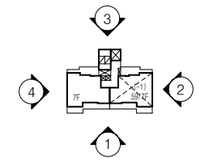

NOTE

1. 1층 바닥 LEVEL
   1SL±0 = 1FL±0 = GL±0 = EL+24.80
2. 지붕 난간의 형태 및 설치위치는 안전성과 입면디자인을 고려하여 변경가능함.
3. 지붕의 재료, 형태, 구조는 실시공시 변경될 수 있음.
4. 지붕 및 옥탑구조물의 형태와 구조는 실시공시 변경될 수 있음.
5. 외벽 및 측벽 문양은 실시공시 변경될 수 있음
6. 입면의 줄눈 및 마감선은 실시공시 변경될 수 있음.
7. 저층부 석재마감 및 입면 마감 색상, 재료에 대한 모든 기준은 특화도면을 우선 적용함.

수정번호 REV. NO.	일 자 DATE	내 용 DESCRIPTION	승 인 CHKD
△			
△			
△			
△			

설계 DESIGNED BY

검토 CHECKED BY
최 진 규

심사 SUMMITED BY
정 호 혁

승인 APPROVED BY
이 승 준

일자 DATE
2019.08

도면명 DRAWING TITLE

107동 정면도,우측면도
배면도,좌측면도

축 척 SCALE
A1: 1/150
A3: 1/300

도면번호 DRAWING NO.
A-395

일련번호 SHEET NO.

△ REV. NO.

HAUD
㈜하우드엔지니어링
종합건축사사무소
Architects, Planners & Engineers
TEL. 02 2143 4400, SEOUL, KOREA

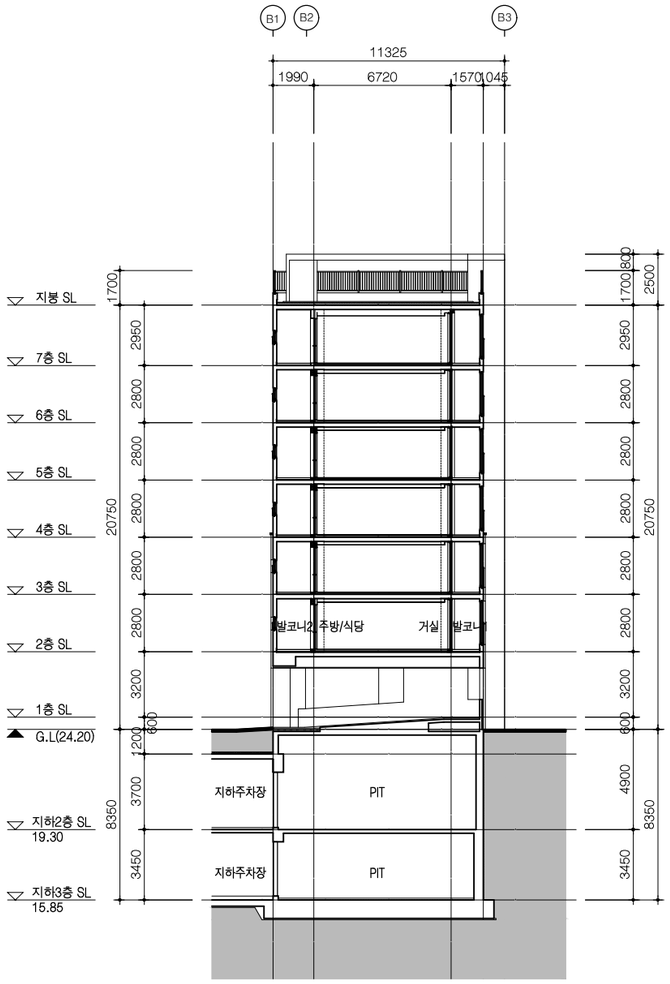

1 A 107동 종단면도

축척 = 1/150

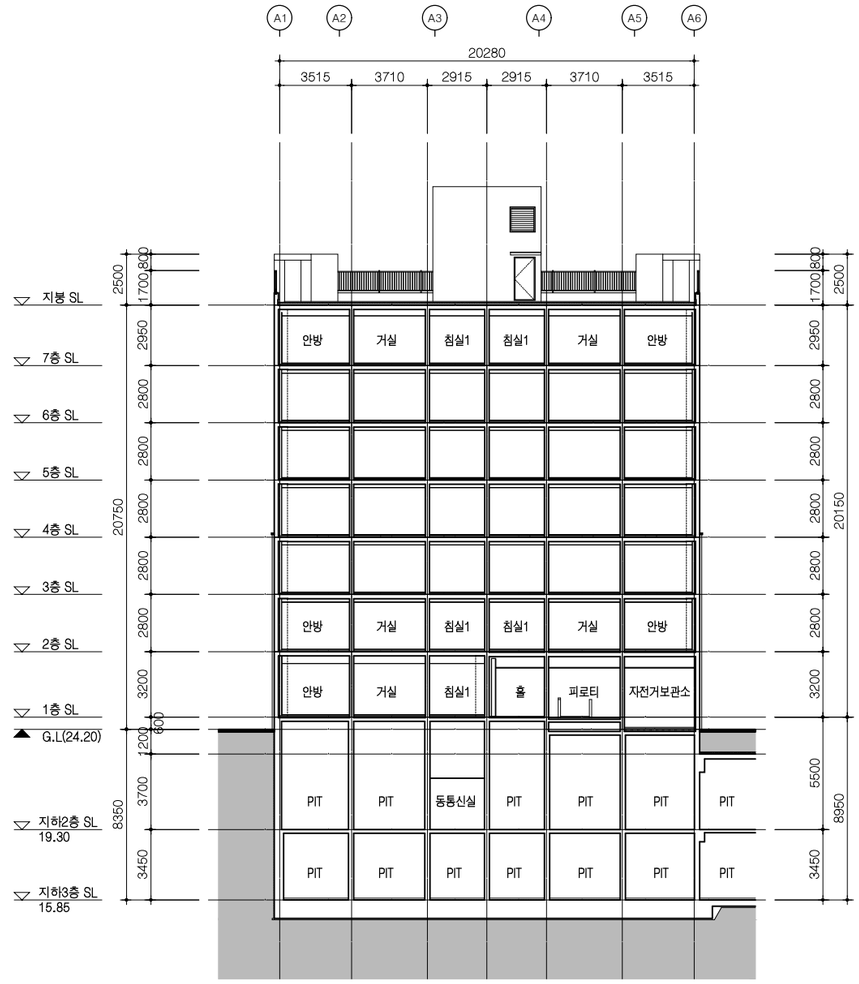

2 A 107동 횡단면도

축척 = 1/150

사업번호 PROJECT NO.

사업명 PROJECT TITLE

수색4재정비촉진구역
주택재개발 정비사업

KEY PLAN

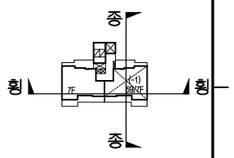

NOTE

수정번호 REV. NO.	일 자 DATE	내 용 DESCRIPTION	승 인 CHKD
△			
△			
△			
△			

설계 DESIGNED BY

검토 CHECKED BY
최 진 규

심사 SUMMITED BY
정 호 혁

승인 APPROVED BY
이 승 준

일자 DATE
2019.08

도면명 DRAWING TITLE
107동 종,횡단면도

축 척 SCALE
A1: 1/150
A3: 1/300

도면번호 DRAWING NO.
A-396

일련번호 SHEET NO.

REV. NO. △

HAUD
㈜하우드엔지니어링
종합건축사사무소
Architects, Planners & Engineers
TEL. 02 2149 4400, SEOUL, KOREA

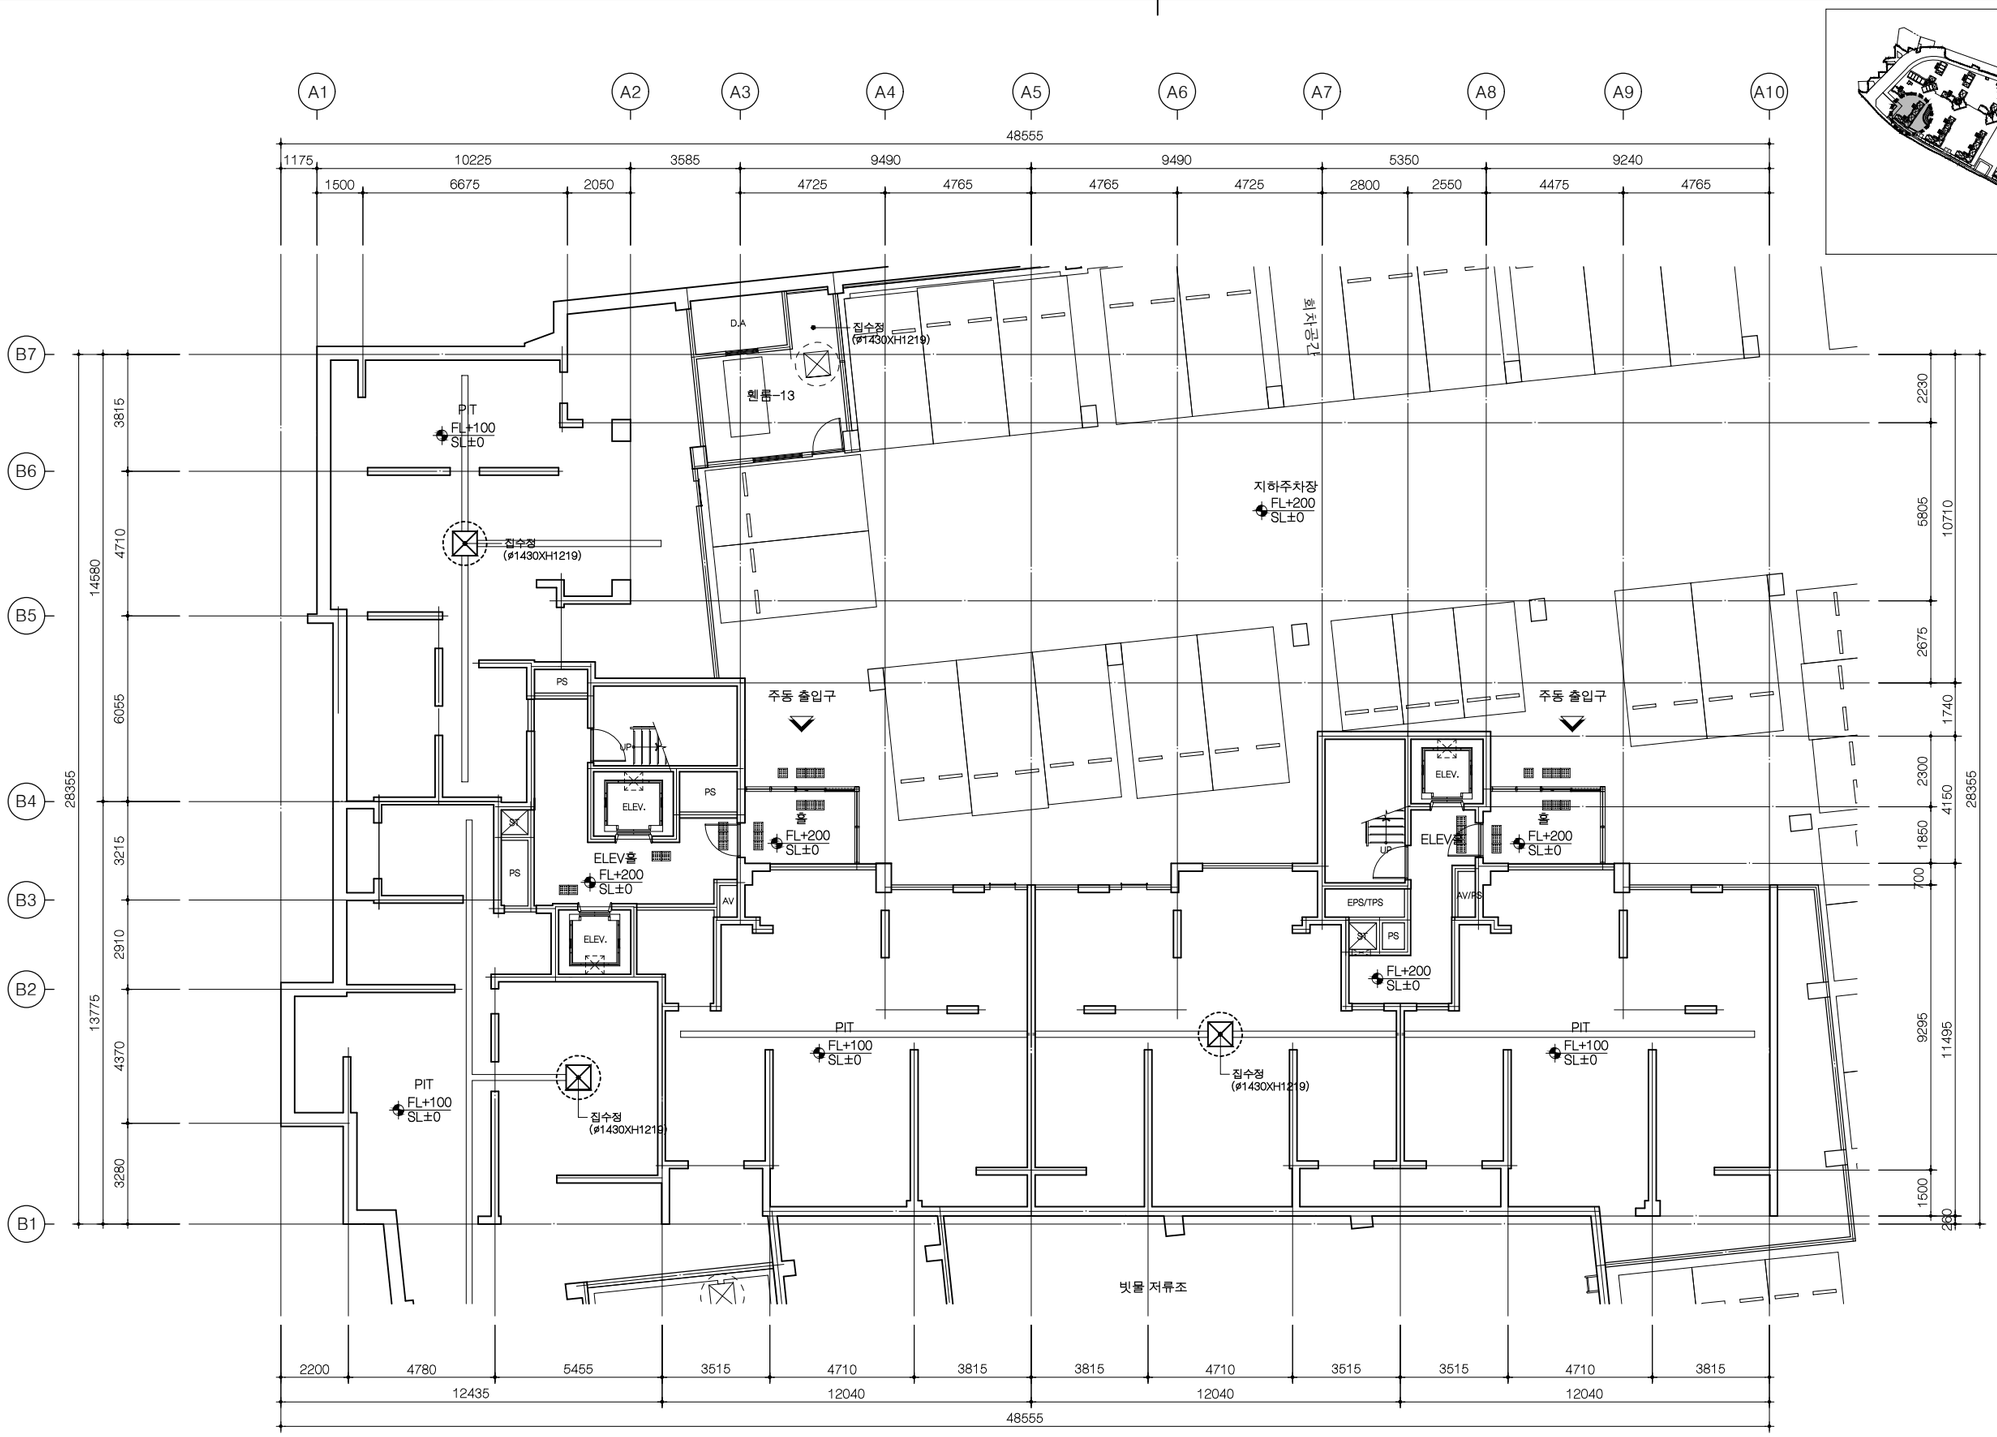

1 A 108동 지하3층 평면도

축척 = 1/100

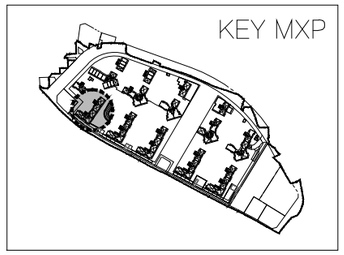

사업번호 PROJECT NO.

사업명 PROJECT TITLE

수색4재정비촉진구역
주택재개발 정비사업

KEY PLAN

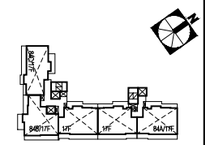

NOTE

1. 지하층 무근 콘크리트는 실시공시 THK80~120 범위로 변동이 있을수 있음.(SLOPE)
2. ELEV홀에 면한부위는 1.0B 조적쌓기임.
3. 지하주차장의 블록쌓기 기준은 높이가 3.6m이하인 경우 4인치 보강블록쌓기가 기준임 (단, 5.4m이하는 6인치쌓기, 5.4m초과는 8인치쌓기가 기준임)
4. ELEV.PIT 집수정은 (600X600X600)임.
5. 주차장 내의 창호는 주차장 창호도 참조.
6. 주차장 집수정 및 영구배수 집수정의 크기 및 위치는 지하주차장 평면도를 참조 할 것.
   ⊠: 주차장 집수정
   ⊠: 영구배수 집수정

********** 지하3층 바닥LEVEL
B3SL±0 = B3FL±0 = EL+15.85

수정번호 REV. NO.	일 자 DATE	내 용 DESCRIPTION	승 인 CHKD
△			
△			
△			
△			

설계 DESIGNED BY

검토 CHECKED BY
최 진 규

심사 SUMMITED BY
정 호 혁

승인 APPROVED BY
이 승 준

일자 DATE
2019.08

도면명 DRAWING TITLE
108동
지하3층 평면도

축 척 SCALE
A1: 1/100
A3: 1/200

도면번호 DRAWING NO.
A-401

일련번호 SHEET NO. △ REV. NO.

HAUD
㈜하우드엔지니어링 종합건축사사무소
Architects, Planners & Engineers
TEL. 82 2149 4400, SEOUL, KOREA

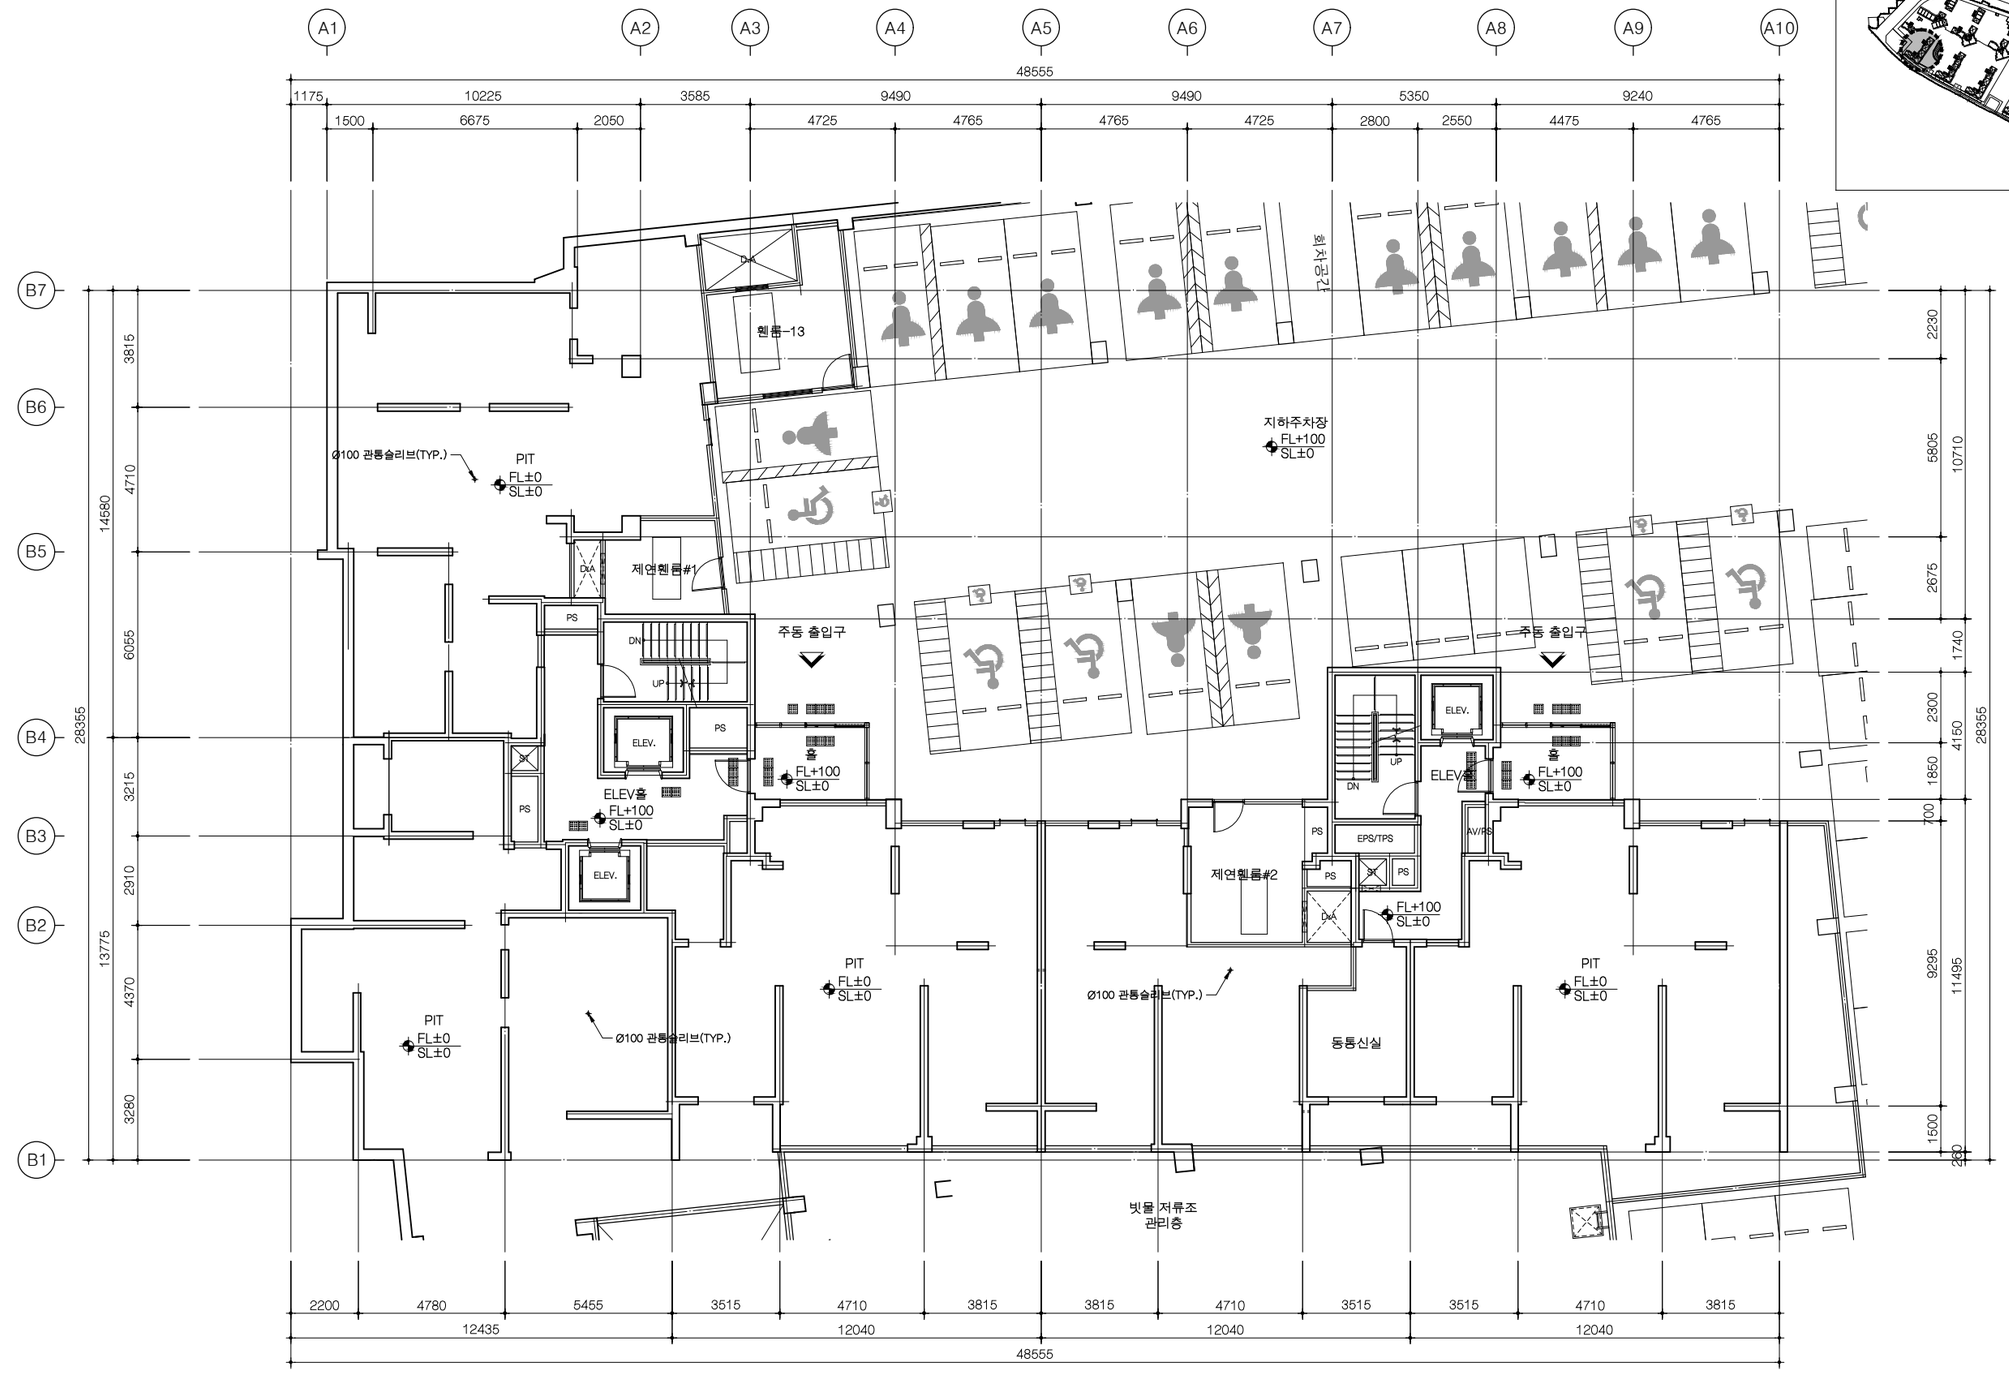

1 A 108동 지하2층 평면도

축척 = 1/100

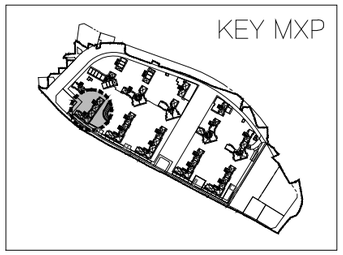

사업번호 PROJECT NO.

사업명 PROJECT TITLE

수색4재정비촉진구역
주택재개발 정비사업

KEY PLAN

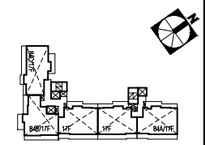

NOTE

1. 지하주차장의 ELEV홀에 면한부위는 1.0B 조적쌓기임.
2. 지하주차장의 블록쌓기 기준은 높이가 3.6m이하인 경우 4인치 보강블록쌓기가 기준임 (단, 5.4m이하는 6인치쌓기, 5.4m초과는 8인치쌓기가 기준임)
3. 주차장 내의 창호는 주차장 창호도 참조.

**** 지하2층 바닥LEVEL
D2SL±0 = D2FL±0 = EL+19.30

수정번호 REV. NO.	일 자 DATE	내 용 DESCRIPTION	승 인 CHKD
△			
△			
△			
△			

설계 DESIGNED BY

검토 CHECKED BY
최 진 규

심사 SUMMITED BY
정 호 혁

승인 APPROVED BY
이 승 준

일자 DATE
2019.08

도면명 DRAWING TITLE
108동
지하2층 평면도

축 척 SCALE
A1: 1/100
A3: 1/200

도면번호 DRAWING NO.
A-402

일련번호 SHEET NO. △ REV. NO.

HAUD
㈜하우드엔지니어링
종합건축사사무소
Architects, Planners & Engineers
TEL. 82 2 149 4400, SEOUL, KOREA

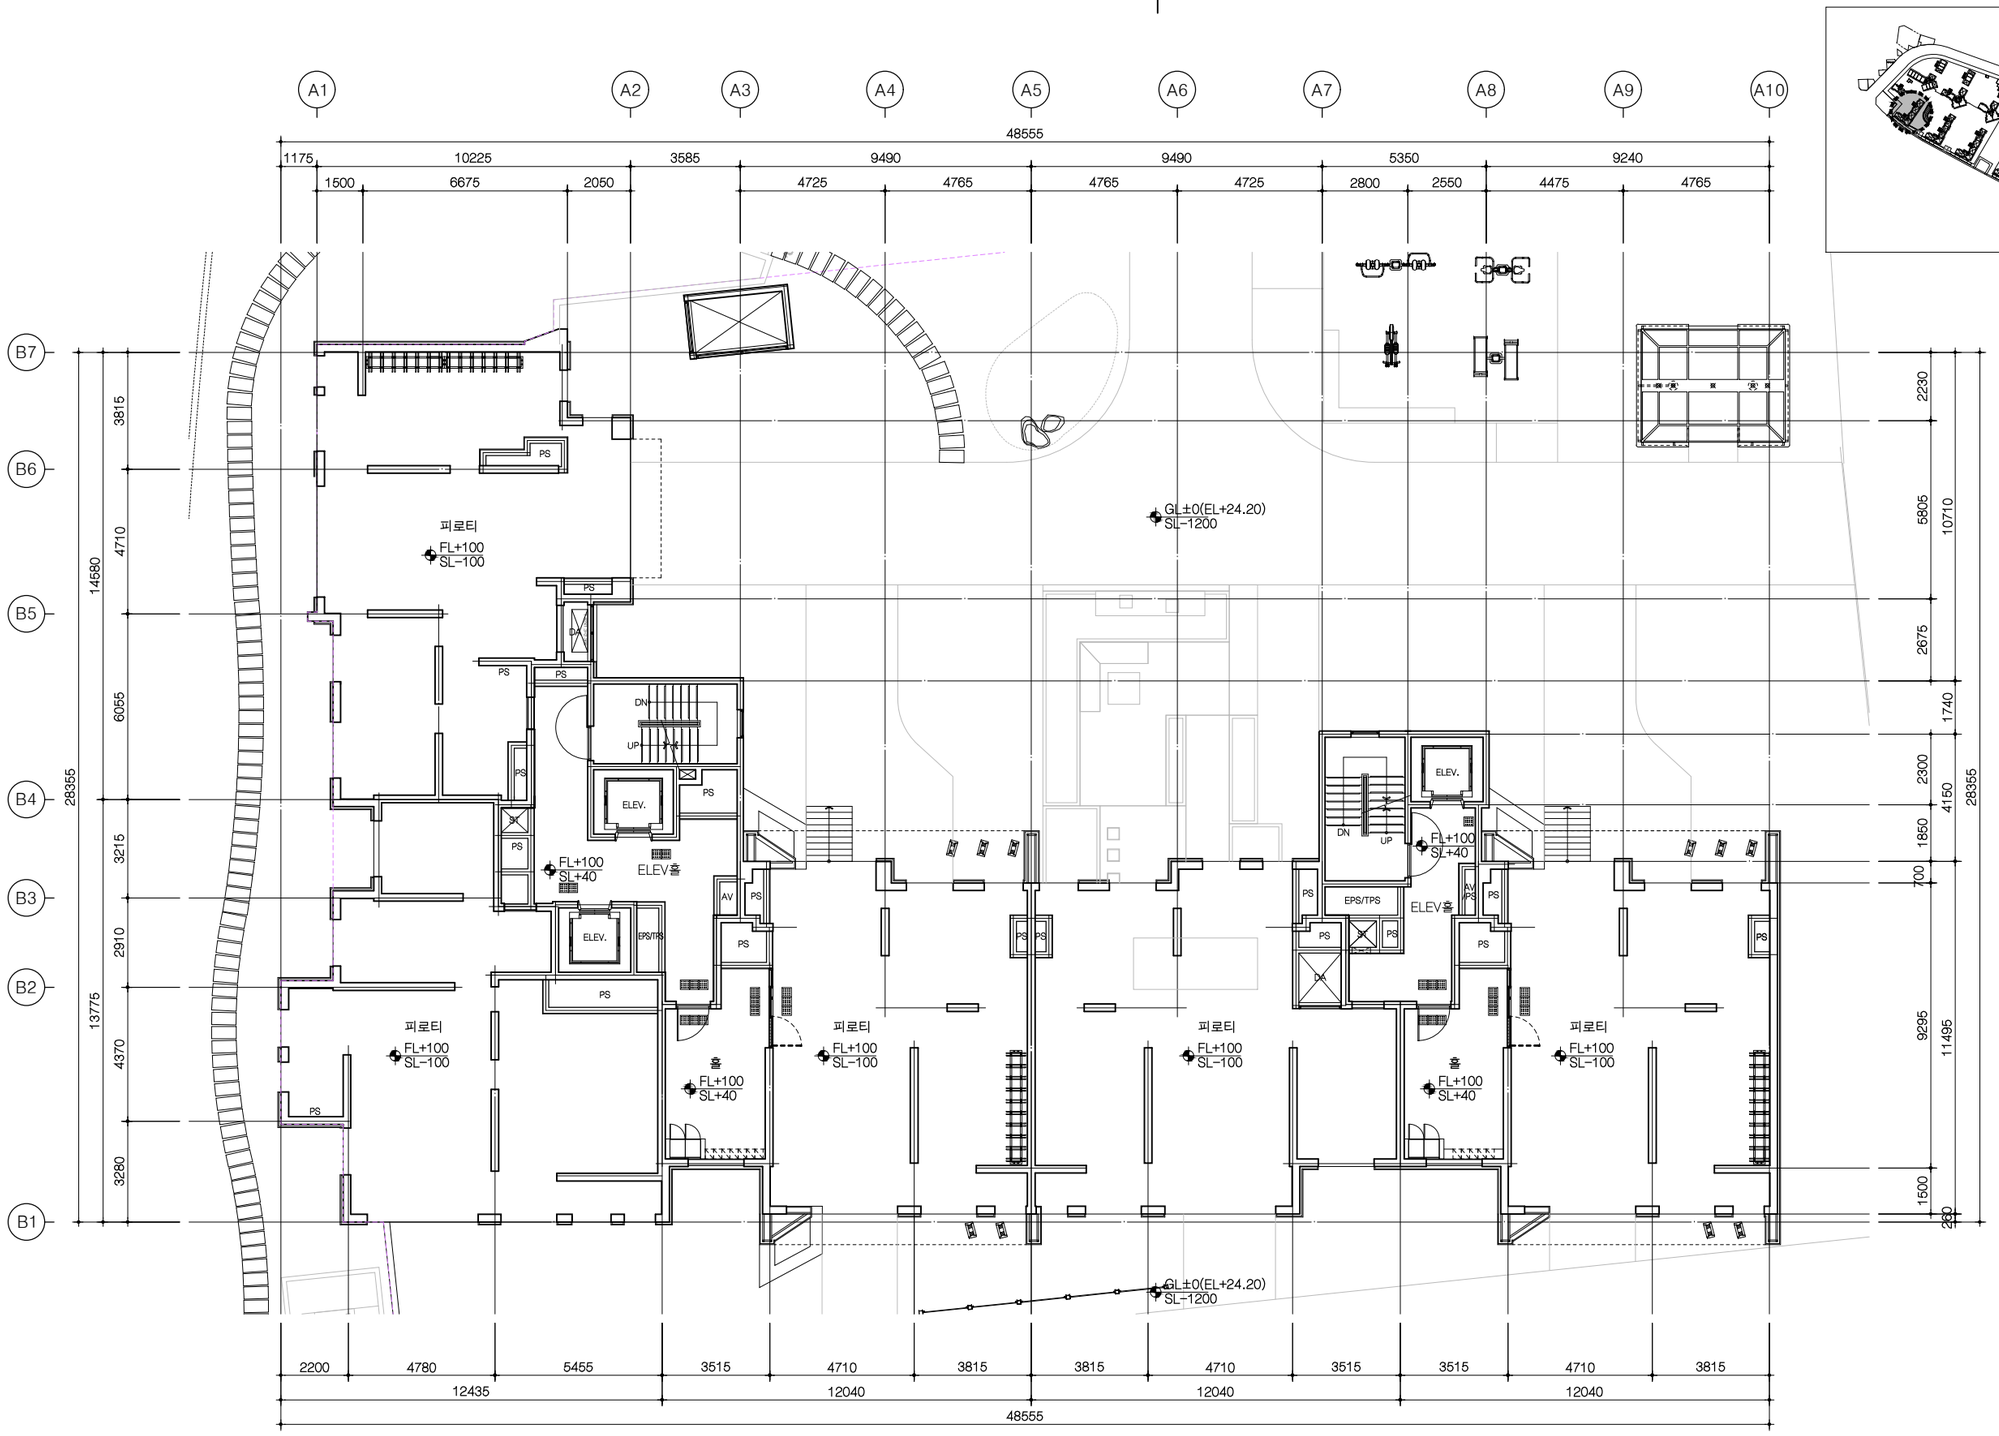

1 A 108동 1층 평면도

축척 = 1/100

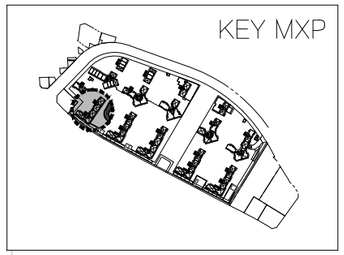

사업번호 PROJECT NO.

사업명 PROJECT TITLE

수색4재정비촉진구역
주택재개발 정비사업

KEY PLAN

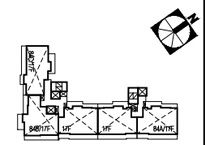

NOTE

1. 우려물 수취함 설치 위치는 변경될 수 있음

• 1층 바닥LEVEL
1SL±0 = 1FL±0 = GL±0 = EL+24.20

수정번호 REV. NO.	일 자 DATE	내 용 DESCRIPTION	승 인 CHKD
△			
△			
△			
△			

설계 DESIGNED BY

검토 CHECKED BY
최 진 규

심사 SUMMITED BY
정 호 혁

승인 APPROVED BY
이 승 준

일자 DATE
2019.08

도면명 DRAWING TITLE

108동
1층 평면도

축 척 SCALE
A1: 1/100
A3: 1/200

도면번호 DRAWING NO.
A-403

일련번호 SHEET NO.

△ REV. NO.

HAUD
(주)하우드엔지니어링
종합건축사사무소
Architects, Planners & Engineers
TEL. 02 2143 4400, SEOUL, KOREA

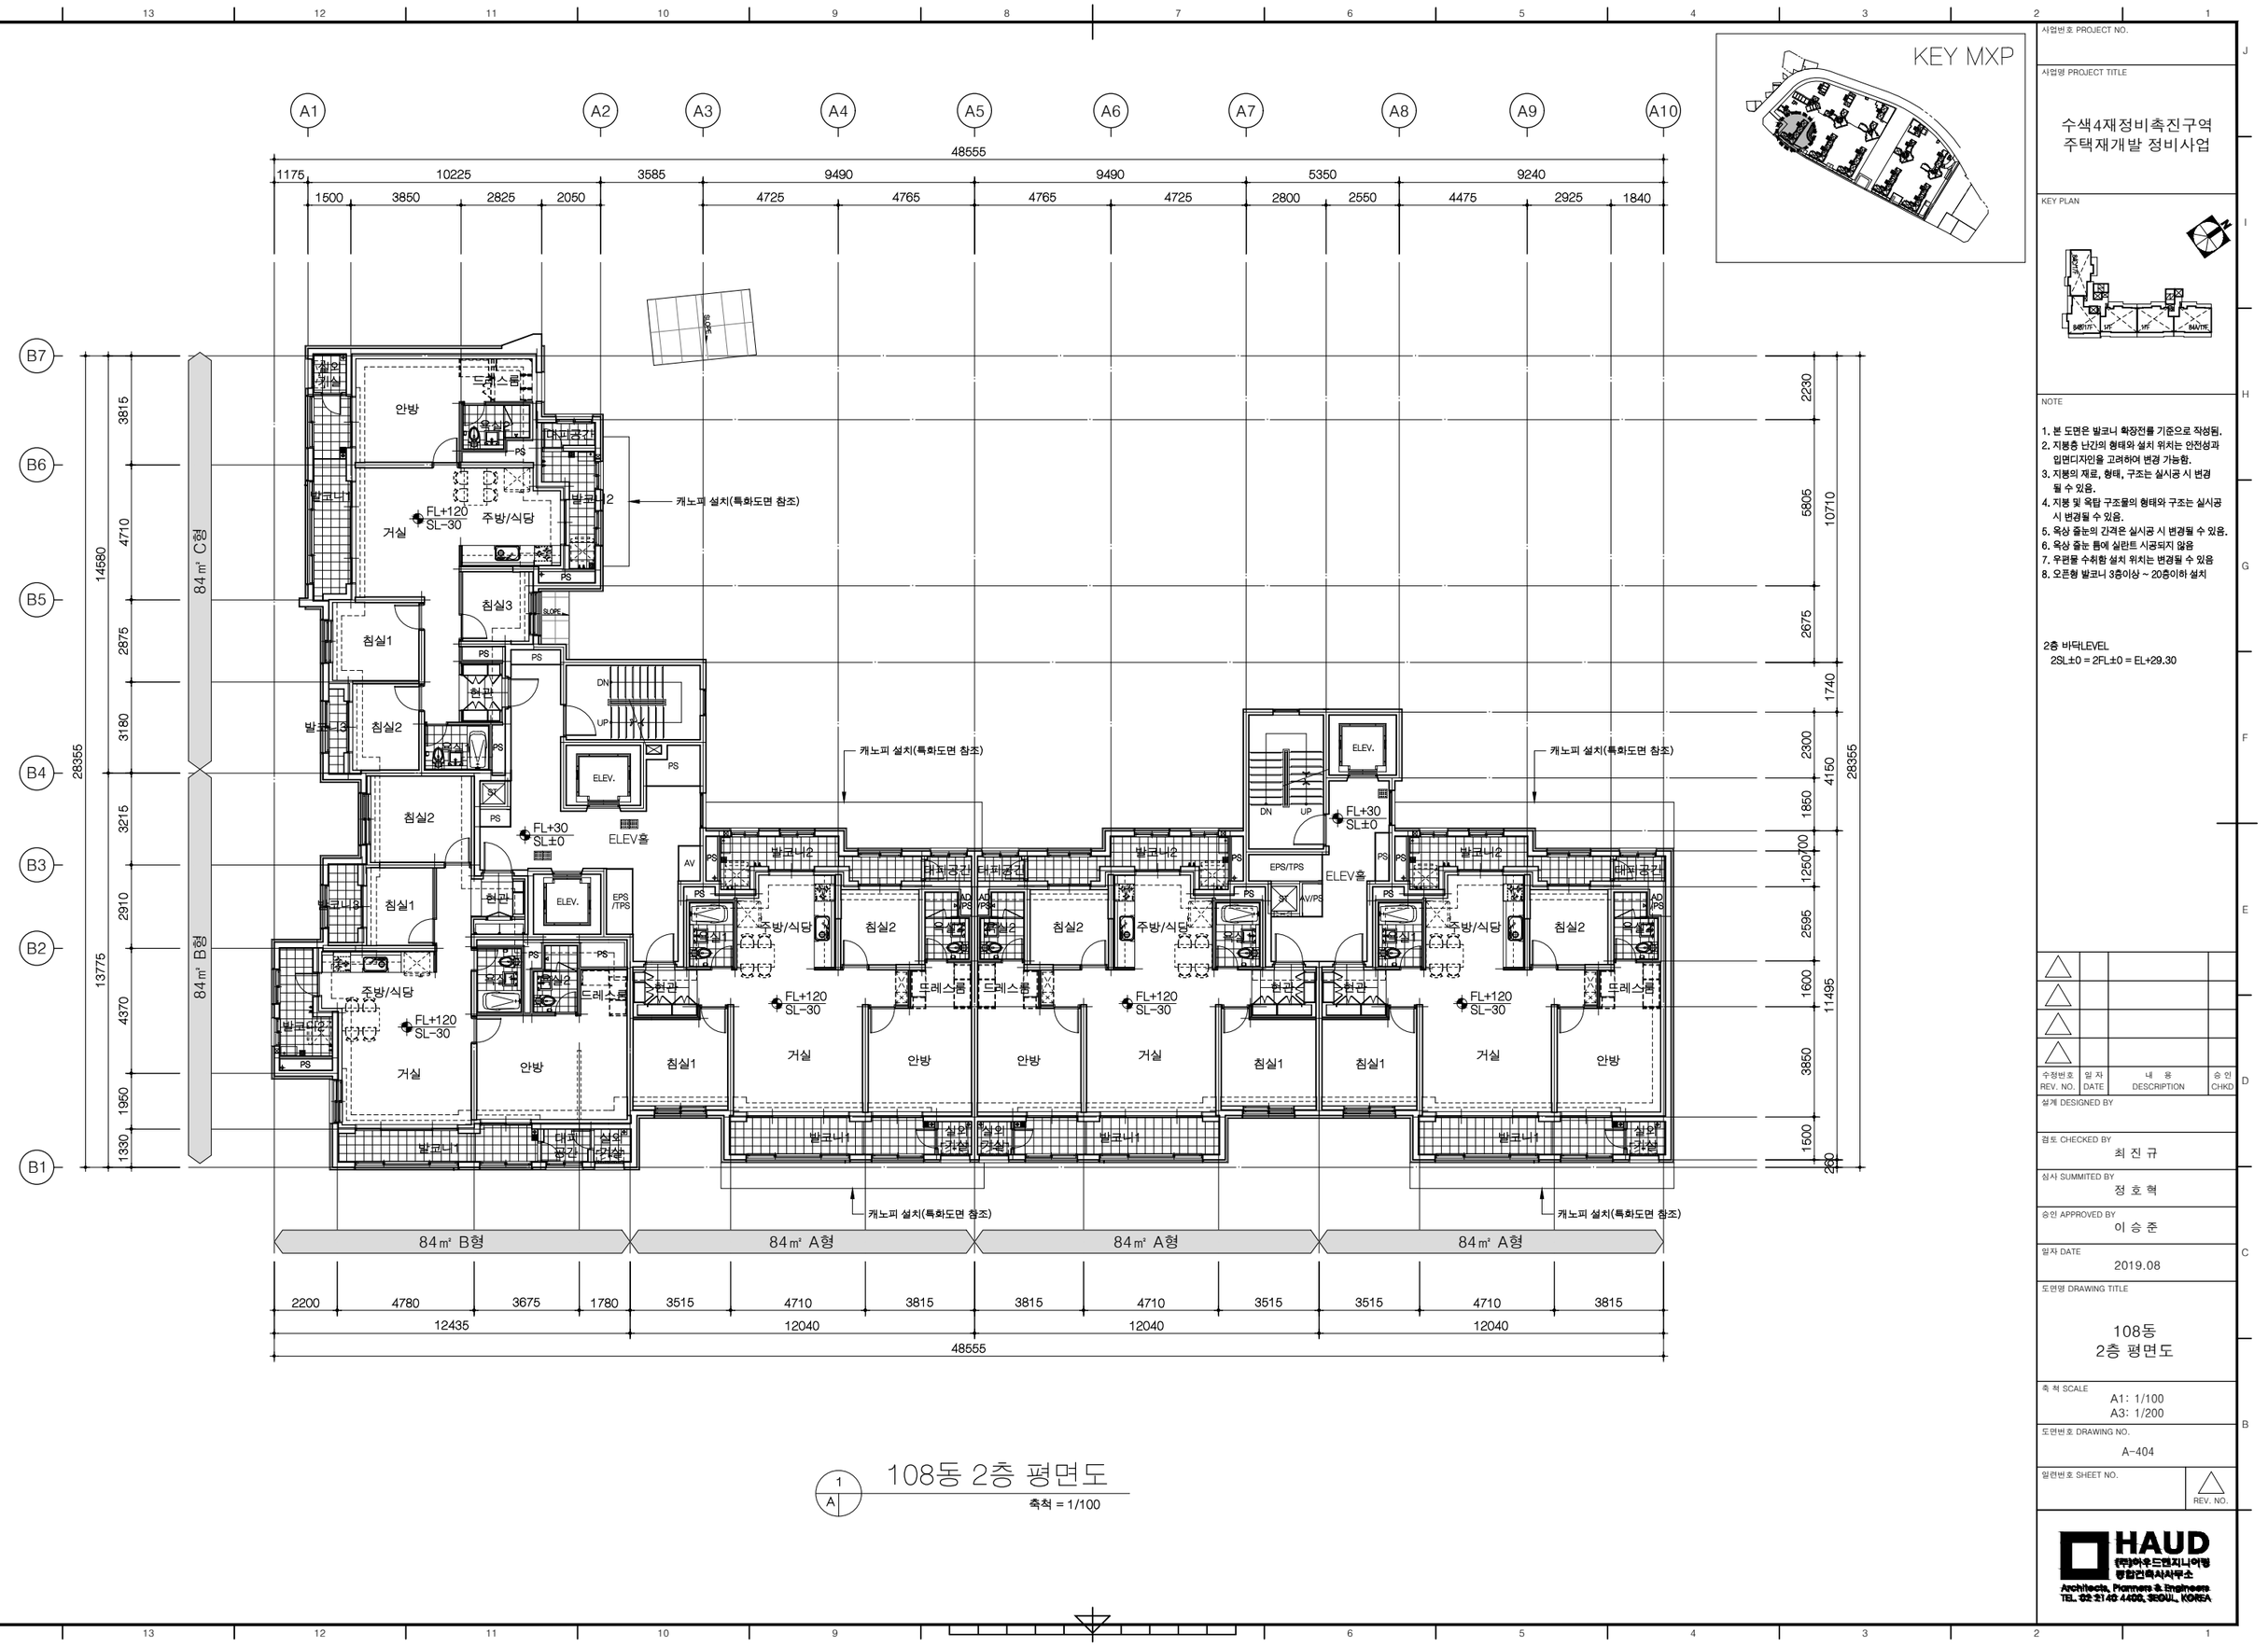

1 A 108동 2층 평면도

축척 = 1/100

사업번호 PROJECT NO.

사업명 PROJECT TITLE

수색4재정비촉진구역
주택재개발 정비사업

KEY PLAN

NOTE

1. 본 도면은 발코니 확장전를 기준으로 작성됨.
2. 지붕층 난간의 형태와 설치 위치는 안전성과 입면디자인을 고려하여 변경 가능함.
3. 지붕의 재료, 형태, 구조는 실시공 시 변경 될 수 있음.
4. 지붕 및 옥탑 구조물의 형태와 구조는 실시공 시 변경될 수 있음.
5. 옥상 출눈의 간격은 실시공 시 변경될 수 있음.
6. 옥상 출눈 틈에 실란트 시공되지 않음
7. 우편물 수취함 설치 위치는 변경될 수 있음
8. 오픈형 발코니 3층이상 ~ 20층이하 설치

2층 바닥LEVEL
2SL±0 = 2FL±0 = EL+29.30

수정번호 REV. NO.	일 자 DATE	내 용 DESCRIPTION	승 인 CHKD
△			
△			
△			
△			

설계 DESIGNED BY

검토 CHECKED BY
최 진 규

심사 SUMMITED BY
정 호 혁

승인 APPROVED BY
이 승 준

일자 DATE
2019.08

도면명 DRAWING TITLE

108동
2층 평면도

축 척 SCALE
A1: 1/100
A3: 1/200

도면번호 DRAWING NO.
A-404

일련번호 SHEET NO.

△ REV. NO.

HAUD
㈜하우드엔지니어링
종합건축사사무소
Architects, Planners & Engineers
TEL. 02 2140 4400, SEOUL, KOREA

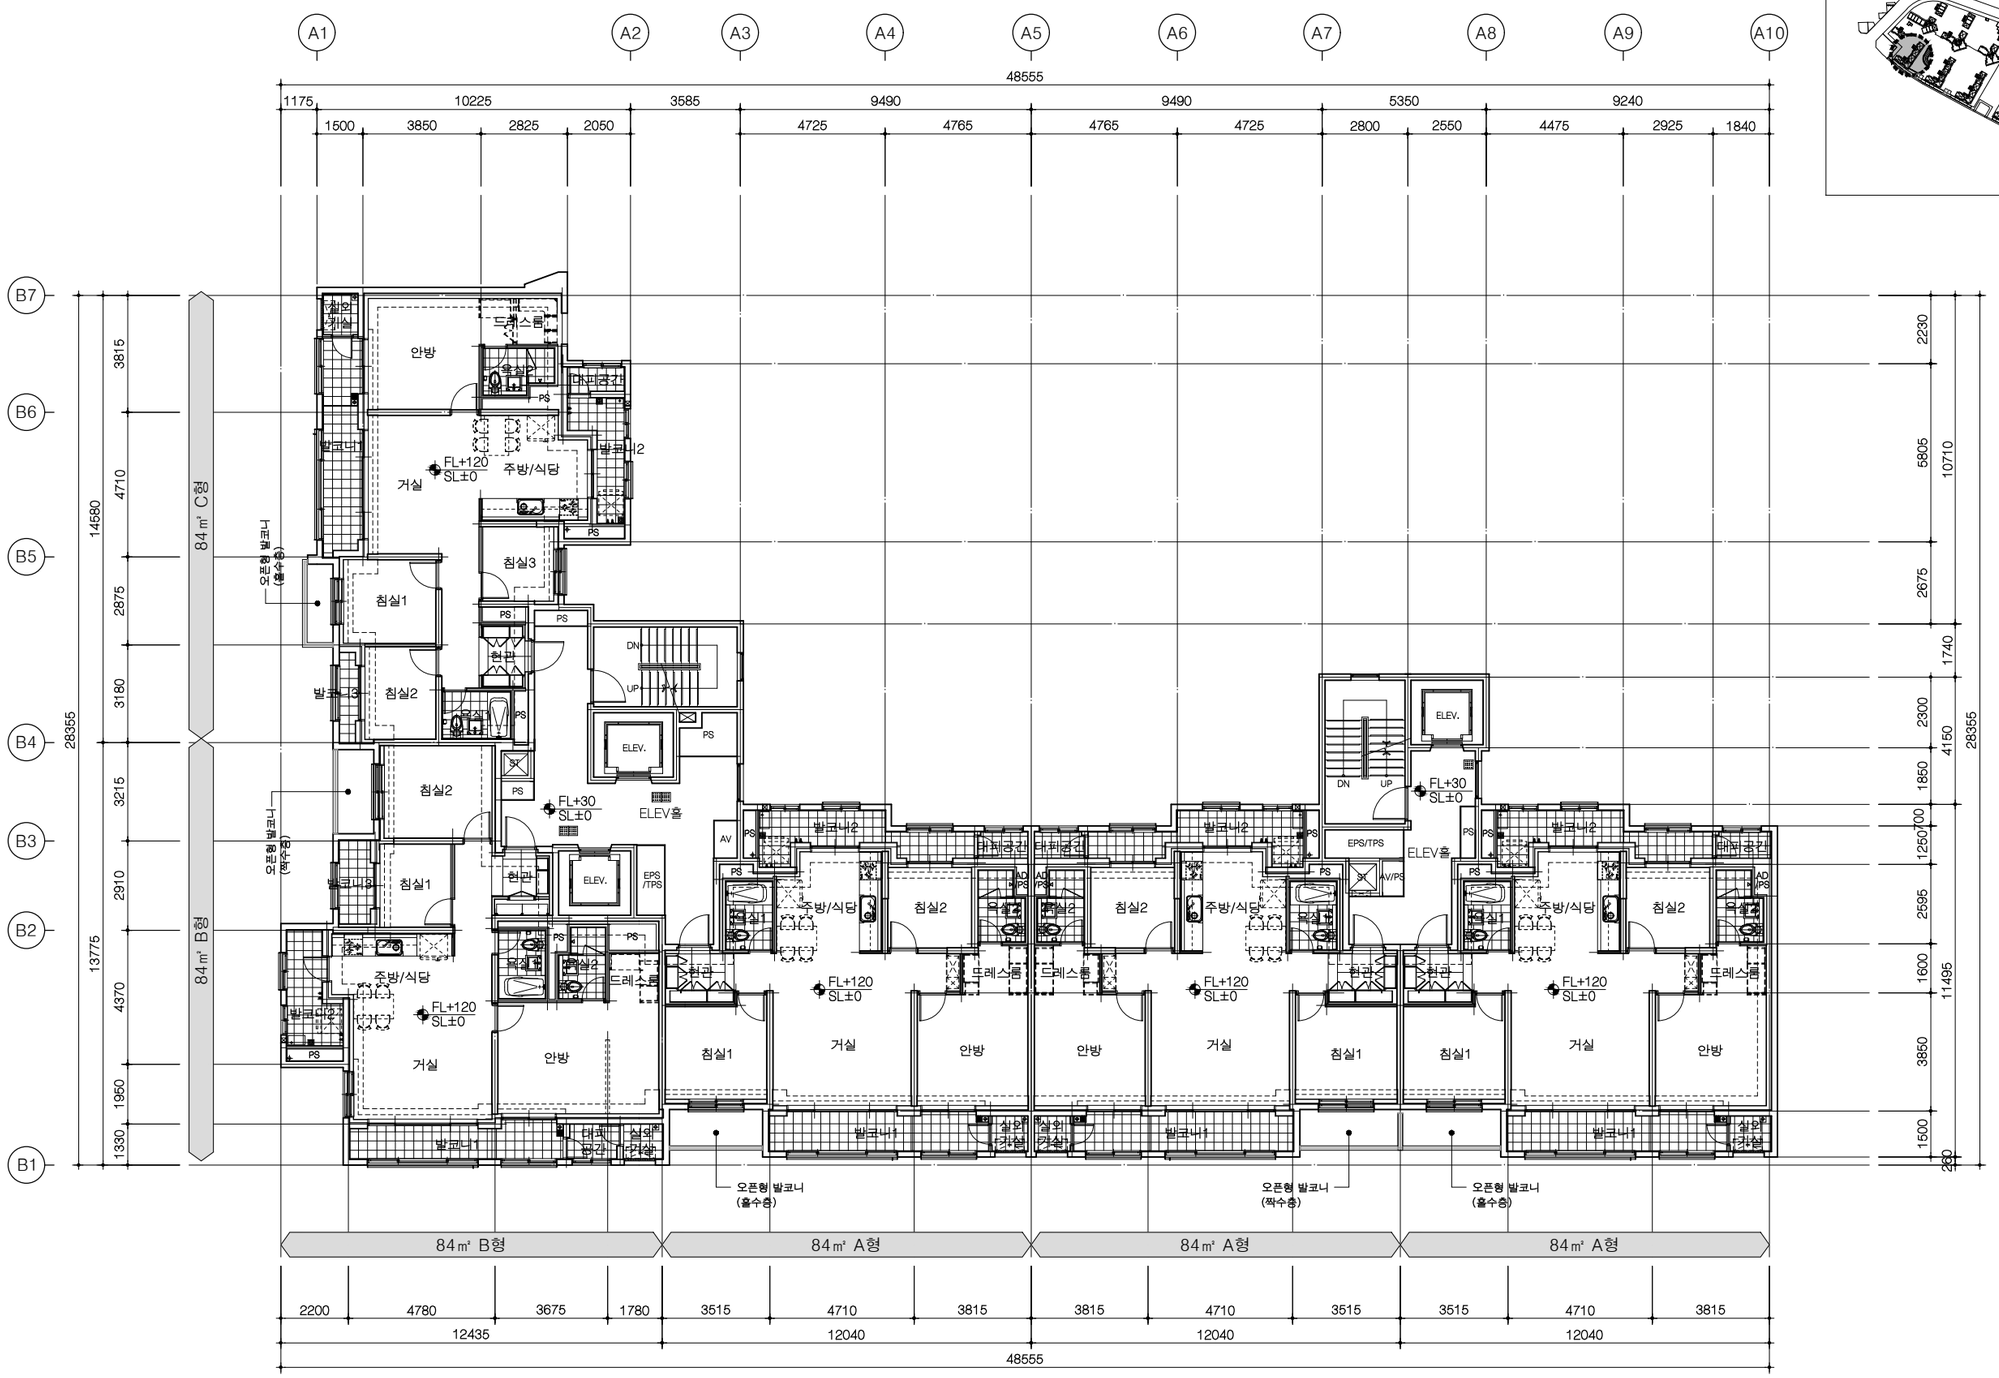

1 A 108동 3~17층 평면도

축척 = 1/100

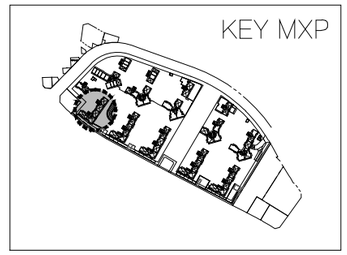

사업번호 PROJECT NO.

사업명 PROJECT TITLE

수색4재정비촉진구역
주택재개발 정비사업

KEY PLAN

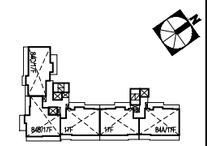

NOTE

1. 본 도면은 발코니 확장전를 기준으로 작성됨.
2. 지붕층 난간의 형태와 설치 위치는 안전성과 입면디자인을 고려하여 변경 가능함.
3. 지붕의 재료, 형태, 구조는 실시공 시 변경 될 수 있음.
4. 지붕 및 옥탑 구조물의 형태와 구조는 실시공 시 변경될 수 있음.
5. 옥상 출눈의 간격은 실시공 시 변경될 수 있음.
6. 옥상 출눈 틈에 실란트 시공되지 않음
7. 우편물 수취함 설치 위치는 변경될 수 있음
8. 오픈형 발코니 3층이상 ~ 20층이하 설치

수정번호 REV. NO.	일 자 DATE	내 용 DESCRIPTION	승 인 CHKD
△			
△			
△			
△			

설계 DESIGNED BY

검토 CHECKED BY
최 진 규

심사 SUMMITED BY
정 호 혁

승인 APPROVED BY
이 승 준

일자 DATE
2019.08

도면명 DRAWING TITLE
108동
3층~17층 평면도

축 척 SCALE
A1: 1/100
A3: 1/200

도면번호 DRAWING NO.
A-405

일련번호 SHEET NO.

△ REV. NO.

HAUD
㈜하우드엔지니어링
종합건축사사무소
Architects, Planners & Engineers
TEL. 02 2140 4400, SEOUL, KOREA

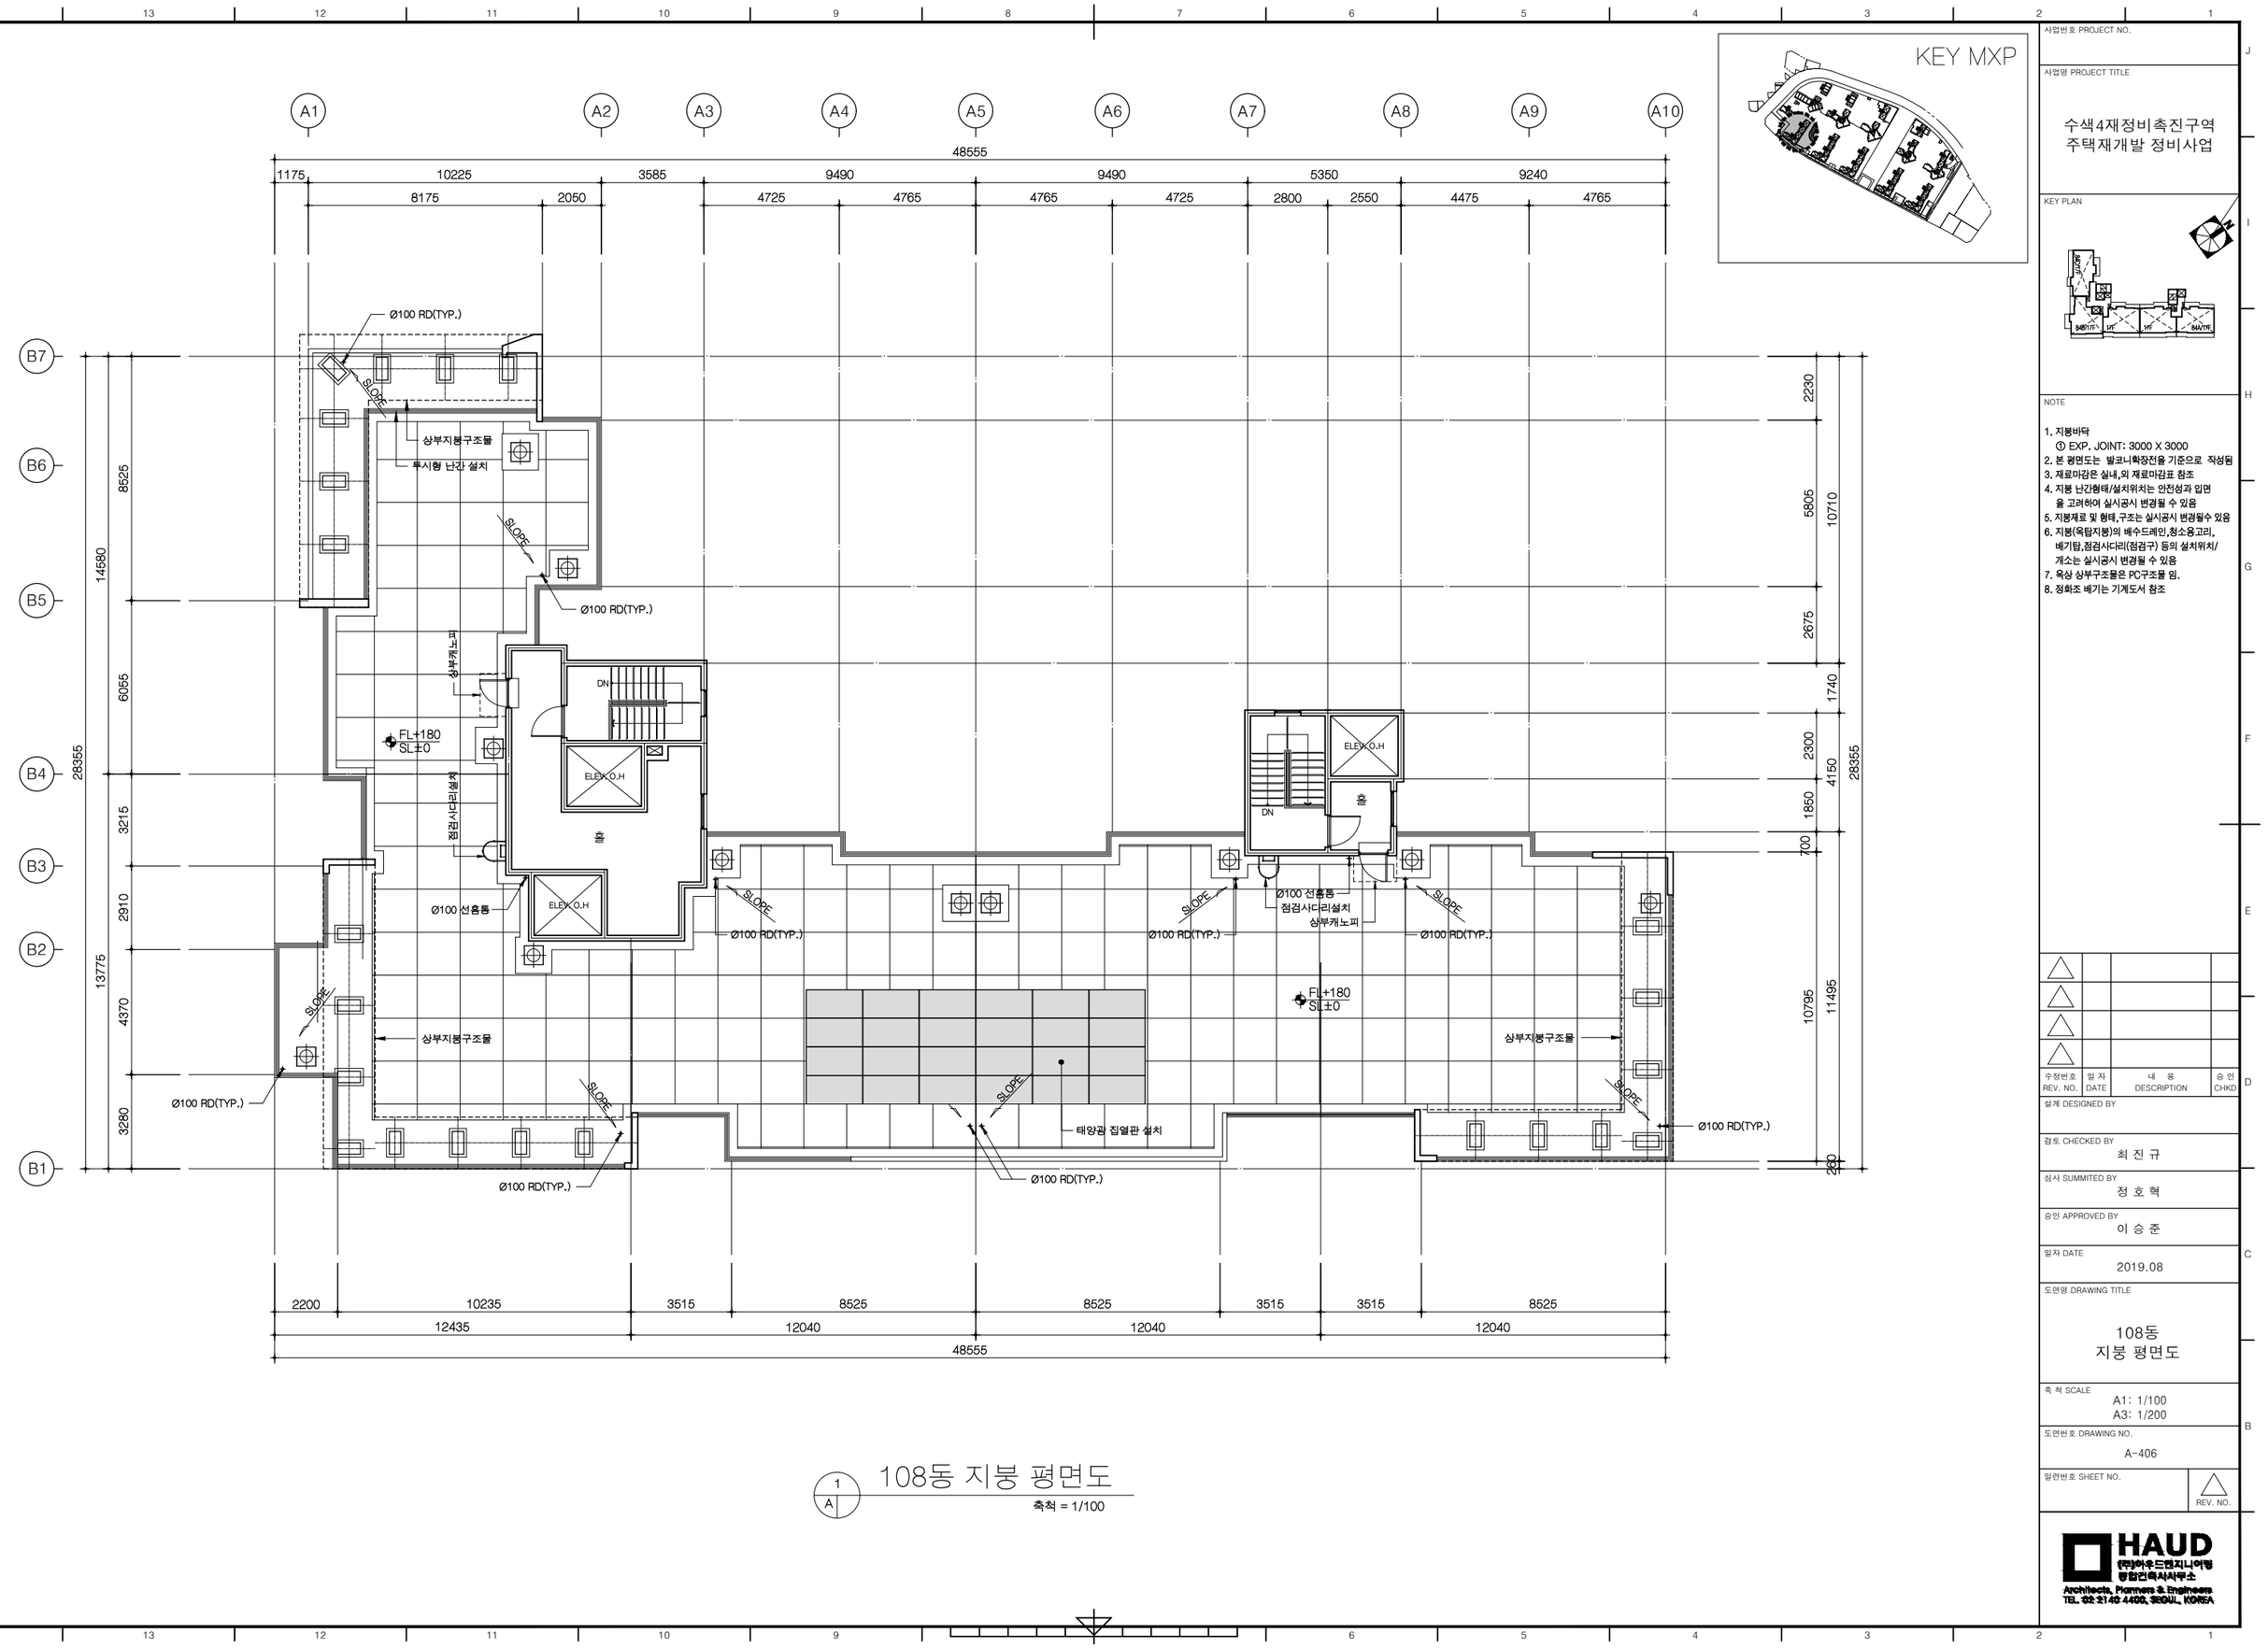

1 A 108동 지붕 평면도

축척 = 1/100

KEY MXP

사업번호 PROJECT NO.

사업명 PROJECT TITLE

수색4재정비촉진구역
주택재개발 정비사업

KEY PLAN

NOTE

1. 지붕바닥
   ① EXP. JOINT: 3000 X 3000
2. 본 평면도는 발코니확장전을 기준으로 작성됨
3. 재료마감은 실내,외 재료마감표 참조
4. 지붕 난간형태/설치위치는 안전성과 입면을 고려하여 실시공시 변경될 수 있음
5. 지붕재료 및 형태,구조는 실시공시 변경될수 있음
6. 지붕(옥탑지붕)의 배수드레인,환소음고리, 베기탑,점검사다리(점검구) 등의 설치위치/개소는 실시공시 변경될 수 있음
7. 옥상 상부구조물은 PC구조물 임.
8. 정화조 배기는 기계도서 참조

수정번호 REV. NO.	일 자 DATE	내 용 DESCRIPTION	승 인 CHKD
△			
△			
△			
△			

설계 DESIGNED BY

검토 CHECKED BY
최 진 규

심사 SUMMITED BY
정 호 혁

승인 APPROVED BY
이 승 준

일자 DATE
2019.08

도면명 DRAWING TITLE
108동
지붕 평면도

축 척 SCALE
A1: 1/100
A3: 1/200

도면번호 DRAWING NO.
A-406

일련번호 SHEET NO.

△ REV. NO.

HAUD
㈜하우드엔지니어링
종합건축사사무소
Architects, Planners & Engineers
TEL. 02-2149-4400, SEOUL, KOREA

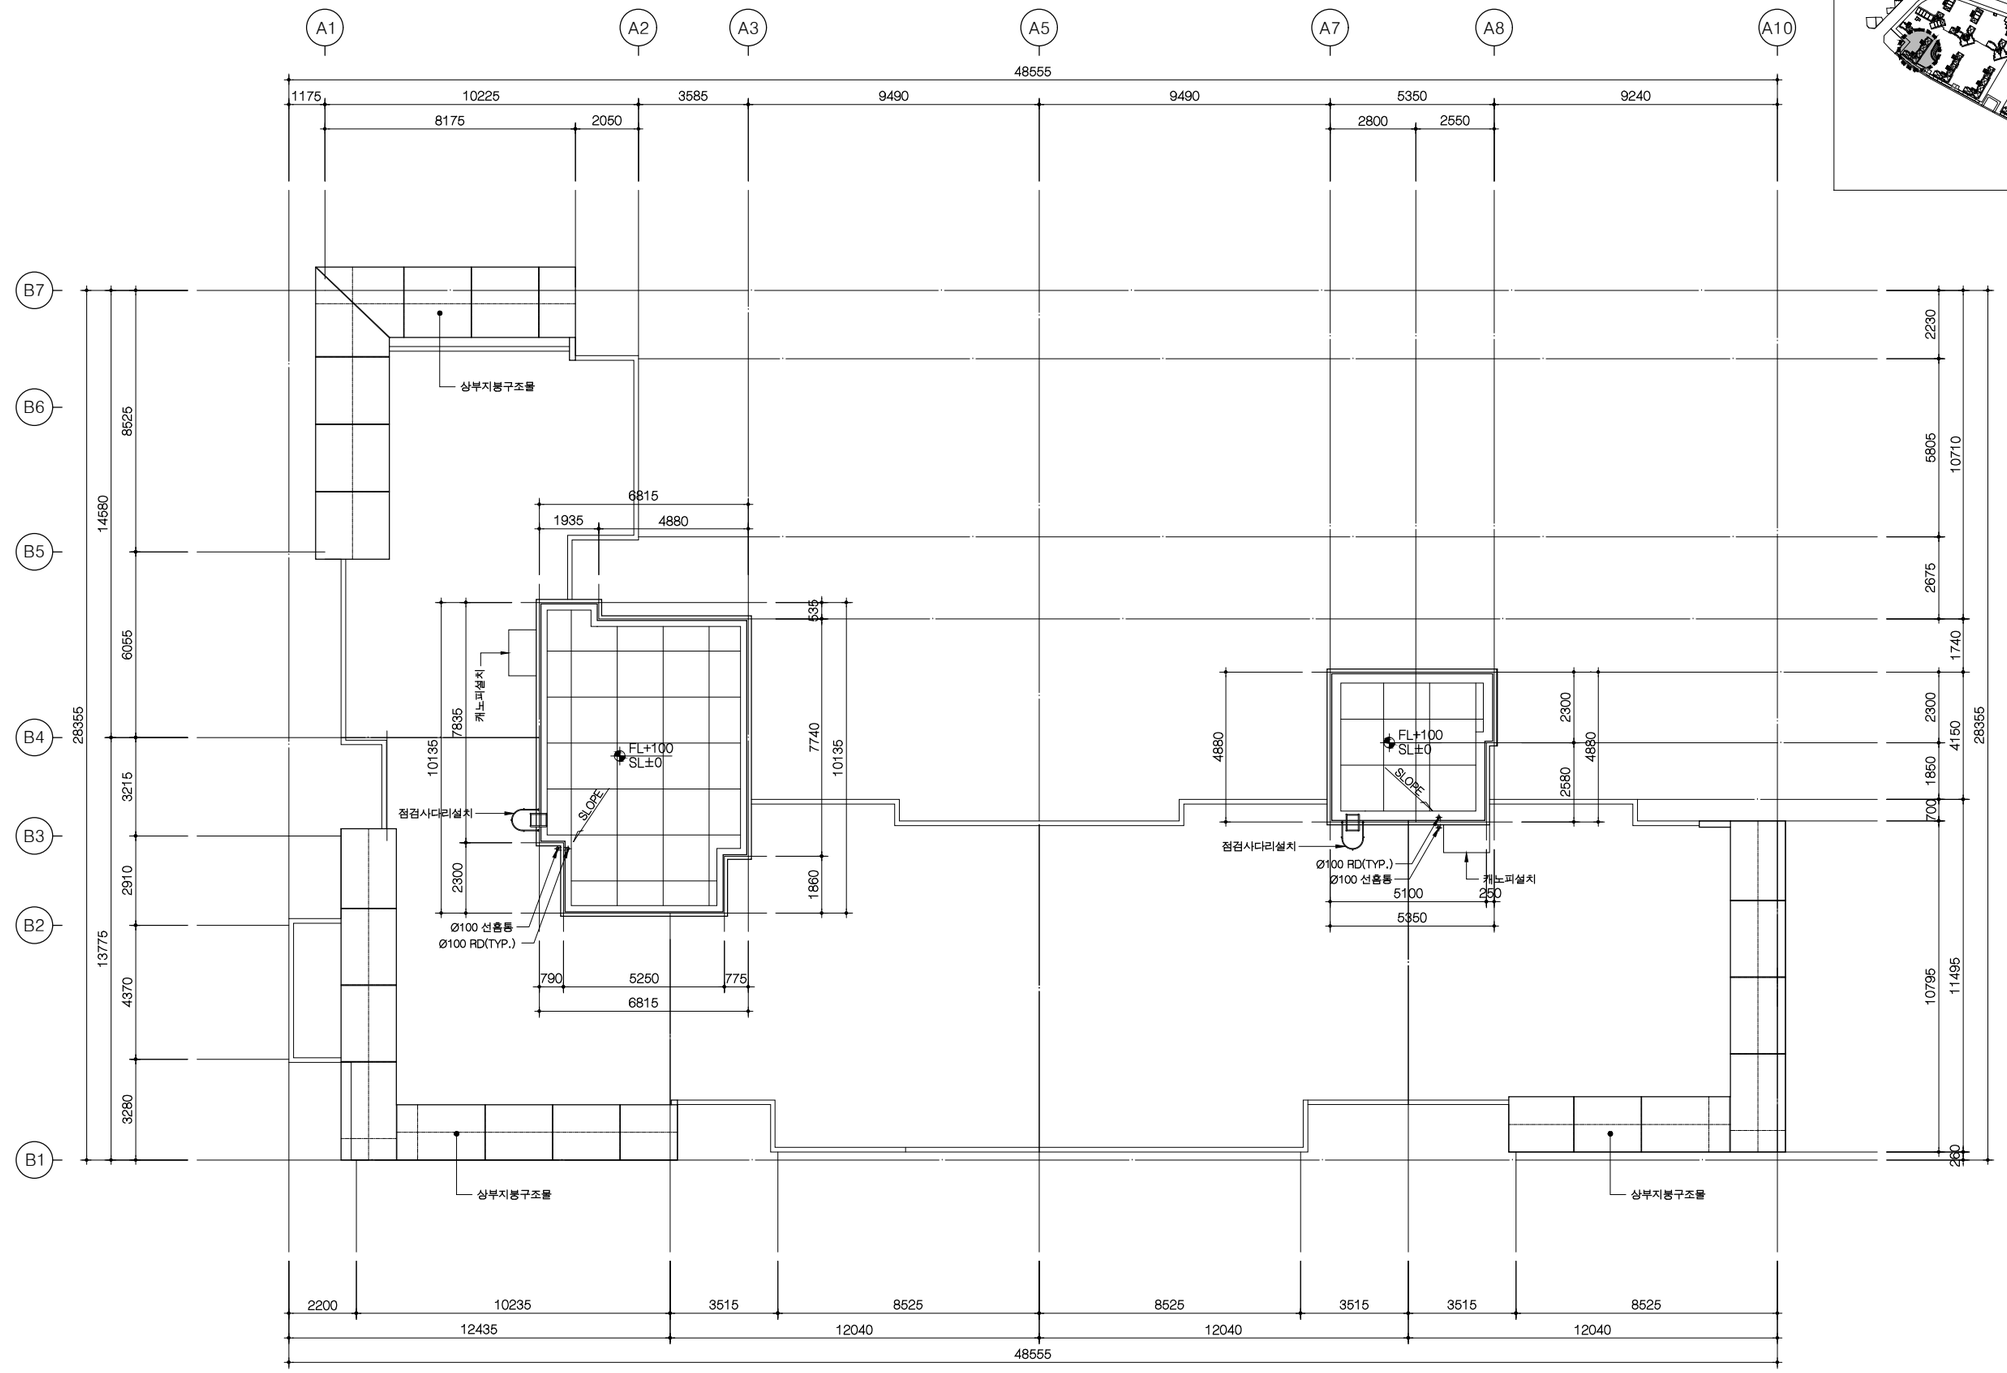

1 A 108동 옥탑지붕 평면도

축척 = 1/100

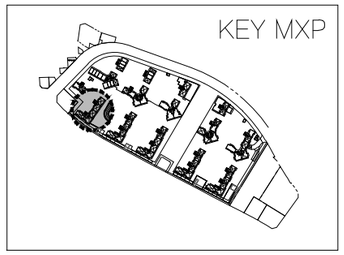

사업번호 PROJECT NO.

사업명 PROJECT TITLE

수색4재정비촉진구역
주택재개발 정비사업

KEY PLAN

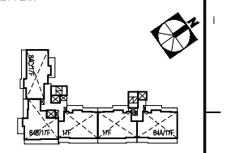

NOTE

1. 지붕바닥
   ① EXP. JOINT: 3000 X 3000
2. 본 평면도는 발코니확장전을 기준으로 작성됨
3. 재료마감은 실내,외 재료마감표 참조
4. 지붕 난간형태/설치위치는 안전성과 입면을 고려하여 실시공시 변경될 수 있음
5. 지붕재료 및 형태,구조는 실시공시 변경될수 있음
6. 지붕(옥탑지붕)의 배수드레인,창소용고리, 베기탑,점검사다리(점검구) 등의 설치위치/개소는 실시공시 변경될 수 있음
7. 옥상 상부구조물은 PC구조물 임.
8. 정화조 배기는 기계도서 참조

수정번호 REV. NO.	일 자 DATE	내 용 DESCRIPTION	승 인 CHKD
△			
△			
△			
△			

설계 DESIGNED BY

검토 CHECKED BY
최 진 규

심사 SUMMITED BY
정 호 혁

승인 APPROVED BY
이 승 준

일자 DATE
2019.08

도면명 DRAWING TITLE
108동
옥탑지붕 평면도

축 척 SCALE
A1: 1/100
A3: 1/200

도면번호 DRAWING NO.
A-407

일련번호 SHEET NO.

△ REV. NO.

HAUD
㈜하우드건축디자이너링
종합건축사사무소
Architects, Planners & Engineers
TEL. 02 2149 4400, SEOUL, KOREA

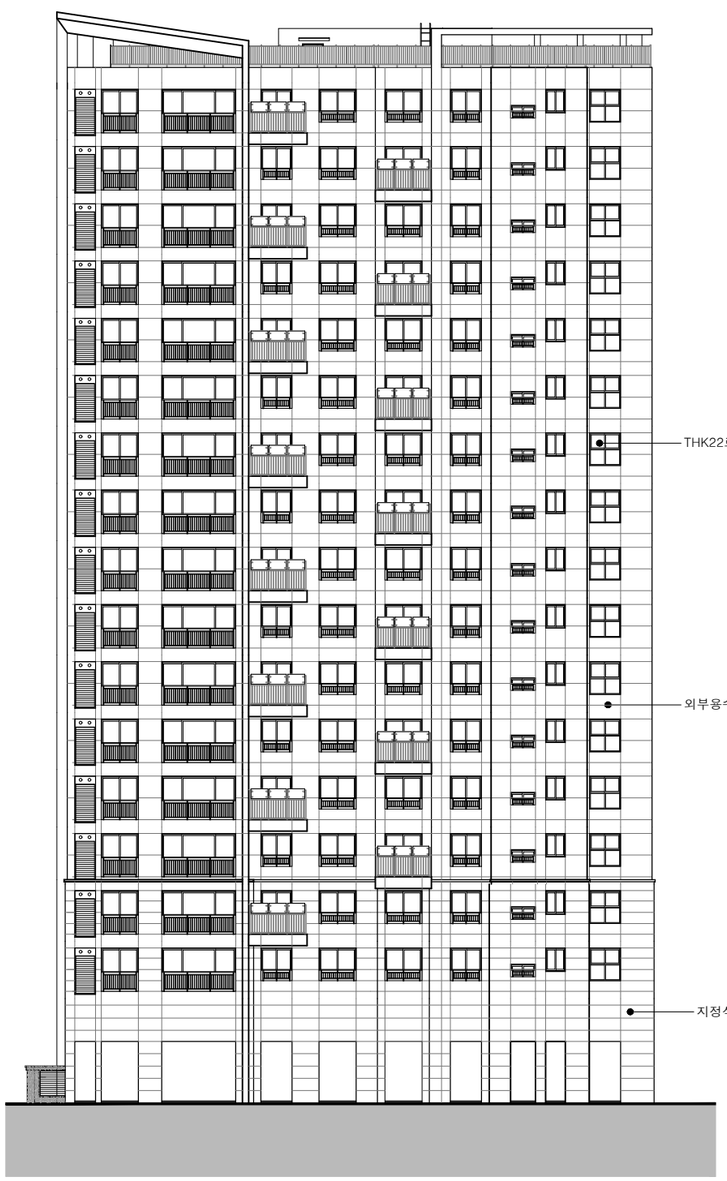

1 A 108동 정면도

축척 = 1/150

2 A 108동 우측면도

축척 = 1/150

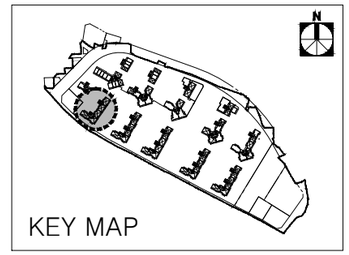

사업번호 PROJECT NO.

사업명 PROJECT TITLE

수색4재정비촉진구역
주택재개발 정비사업

KEY PLAN

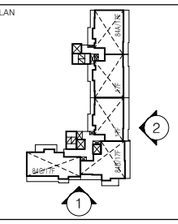

NOTE

1. 1층 바닥 LEVEL
   1SL±0 = 1FL±0 = GL±0 = EL+24.20
2. 지붕 난간의 형태 및 설치위치는 안전성과 입면디자인을 고려하여 변경가능함.
3. 지붕의 재료, 형태, 구조는 실시공시 변경될 수 있음.
4. 지붕 및 옥탑구조물의 형태와 구조는 실시공시 변경될 수 있음.
5. 외벽 및 측벽 문양은 실시공시 변경될 수 있음
6. 입면의 줄눈 및 마감선은 실시공시 변경될 수 있음.
7. 저층부 석재마감 및 입면 마감 색상, 재료에 대한 모든 기준은 특화도면을 우선 적용함.

수정번호 REV. NO.	일 자 DATE	내 용 DESCRIPTION	승 인 CHKD
△			
△			
△			
△			

설계 DESIGNED BY

검토 CHECKED BY
최 진 규

심사 SUMMITED BY
정 호 혁

승인 APPROVED BY
이 승 준

일자 DATE
2019.08

도면명 DRAWING TITLE
108동 정면도,우측면도

축 척 SCALE
A1: 1/150
A3: 1/300

도면번호 DRAWING NO.
A-408

일련번호 SHEET NO. △ REV. NO.

HAUD
(주)하우드엔지니어링
종합건축사사무소
Architects, Planners & Engineers
TEL. 82 2140 4400, SEOUL, KOREA

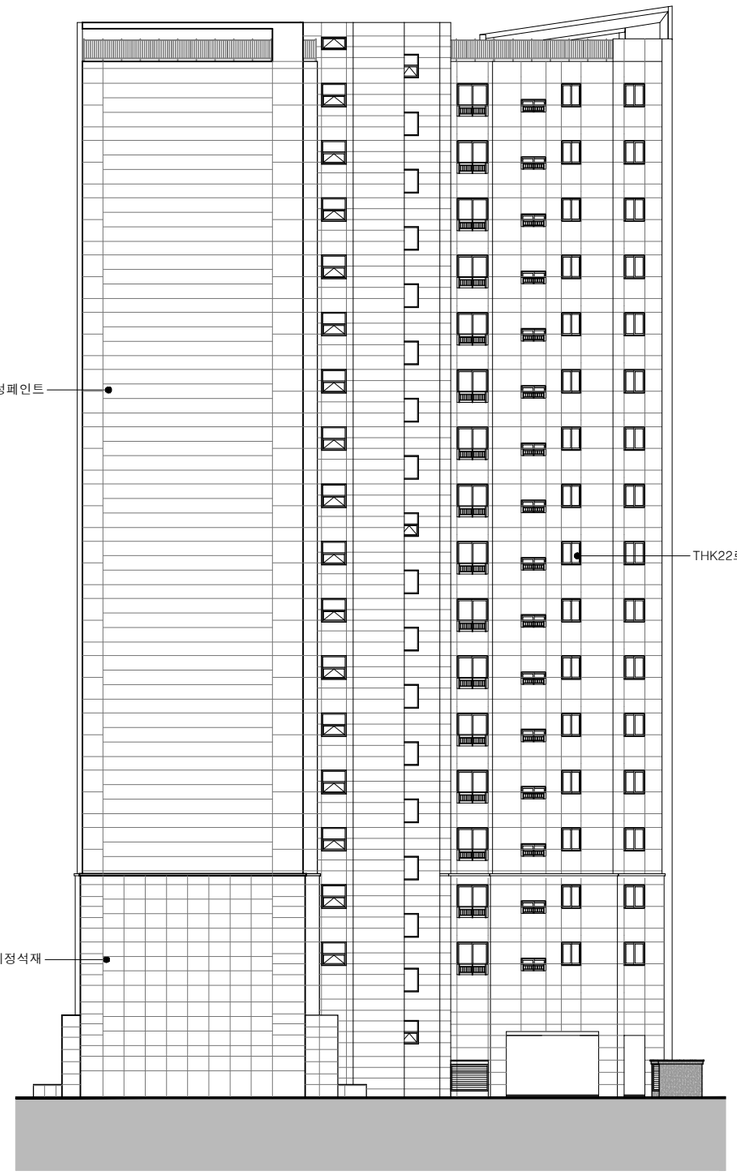

1 A 108동 배면도

축척 = 1/150

2 A 108동 좌측면도

축척 = 1/150

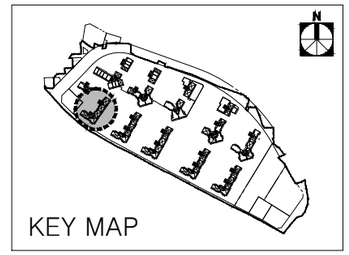

사업번호 PROJECT NO.

사업명 PROJECT TITLE

수색4재정비촉진구역
주택재개발 정비사업

KEY PLAN

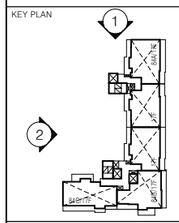

NOTE

1. 1층 바닥 LEVEL
   1SL±0 = 1FL±0 = GL±0 = EL+24.20
2. 지붕 난간의 형태 및 설치위치는 안전성과 입면디자인을 고려하여 변경가능함.
3. 지붕의 재료, 형태, 구조는 실시공시 변경될 수 있음.
4. 지붕 및 옥탑구조물의 형태와 구조는 실시공시 변경될 수 있음.
5. 외벽 및 측벽 문양은 실시공시 변경될 수 있음
6. 입면의 줄눈 및 마감선은 실시공시 변경될 수 있음.
7. 저층부 석재마감 및 입면 마감 색상, 재료에 대한 모든 기준은 특화도면을 우선 적용함.

수정번호 REV. NO.	일 자 DATE	내 용 DESCRIPTION	승 인 CHKD
△			
△			
△			
△			

설계 DESIGNED BY

검토 CHECKED BY
최 진 규

심사 SUMMITED BY
정 호 혁

승인 APPROVED BY
이 승 준

일자 DATE
2019.08

도면명 DRAWING TITLE
108동 배면도,좌측면도

축 척 SCALE
A1: 1/150
A3: 1/300

도면번호 DRAWING NO.
A-409

일련번호 SHEET NO.

△ REV. NO.

HAUD
㈜하우드건지니어링
종합건축사사무소
Architects, Planners & Engineers
TEL. 82-2-149 4400, SEOUL, KOREA

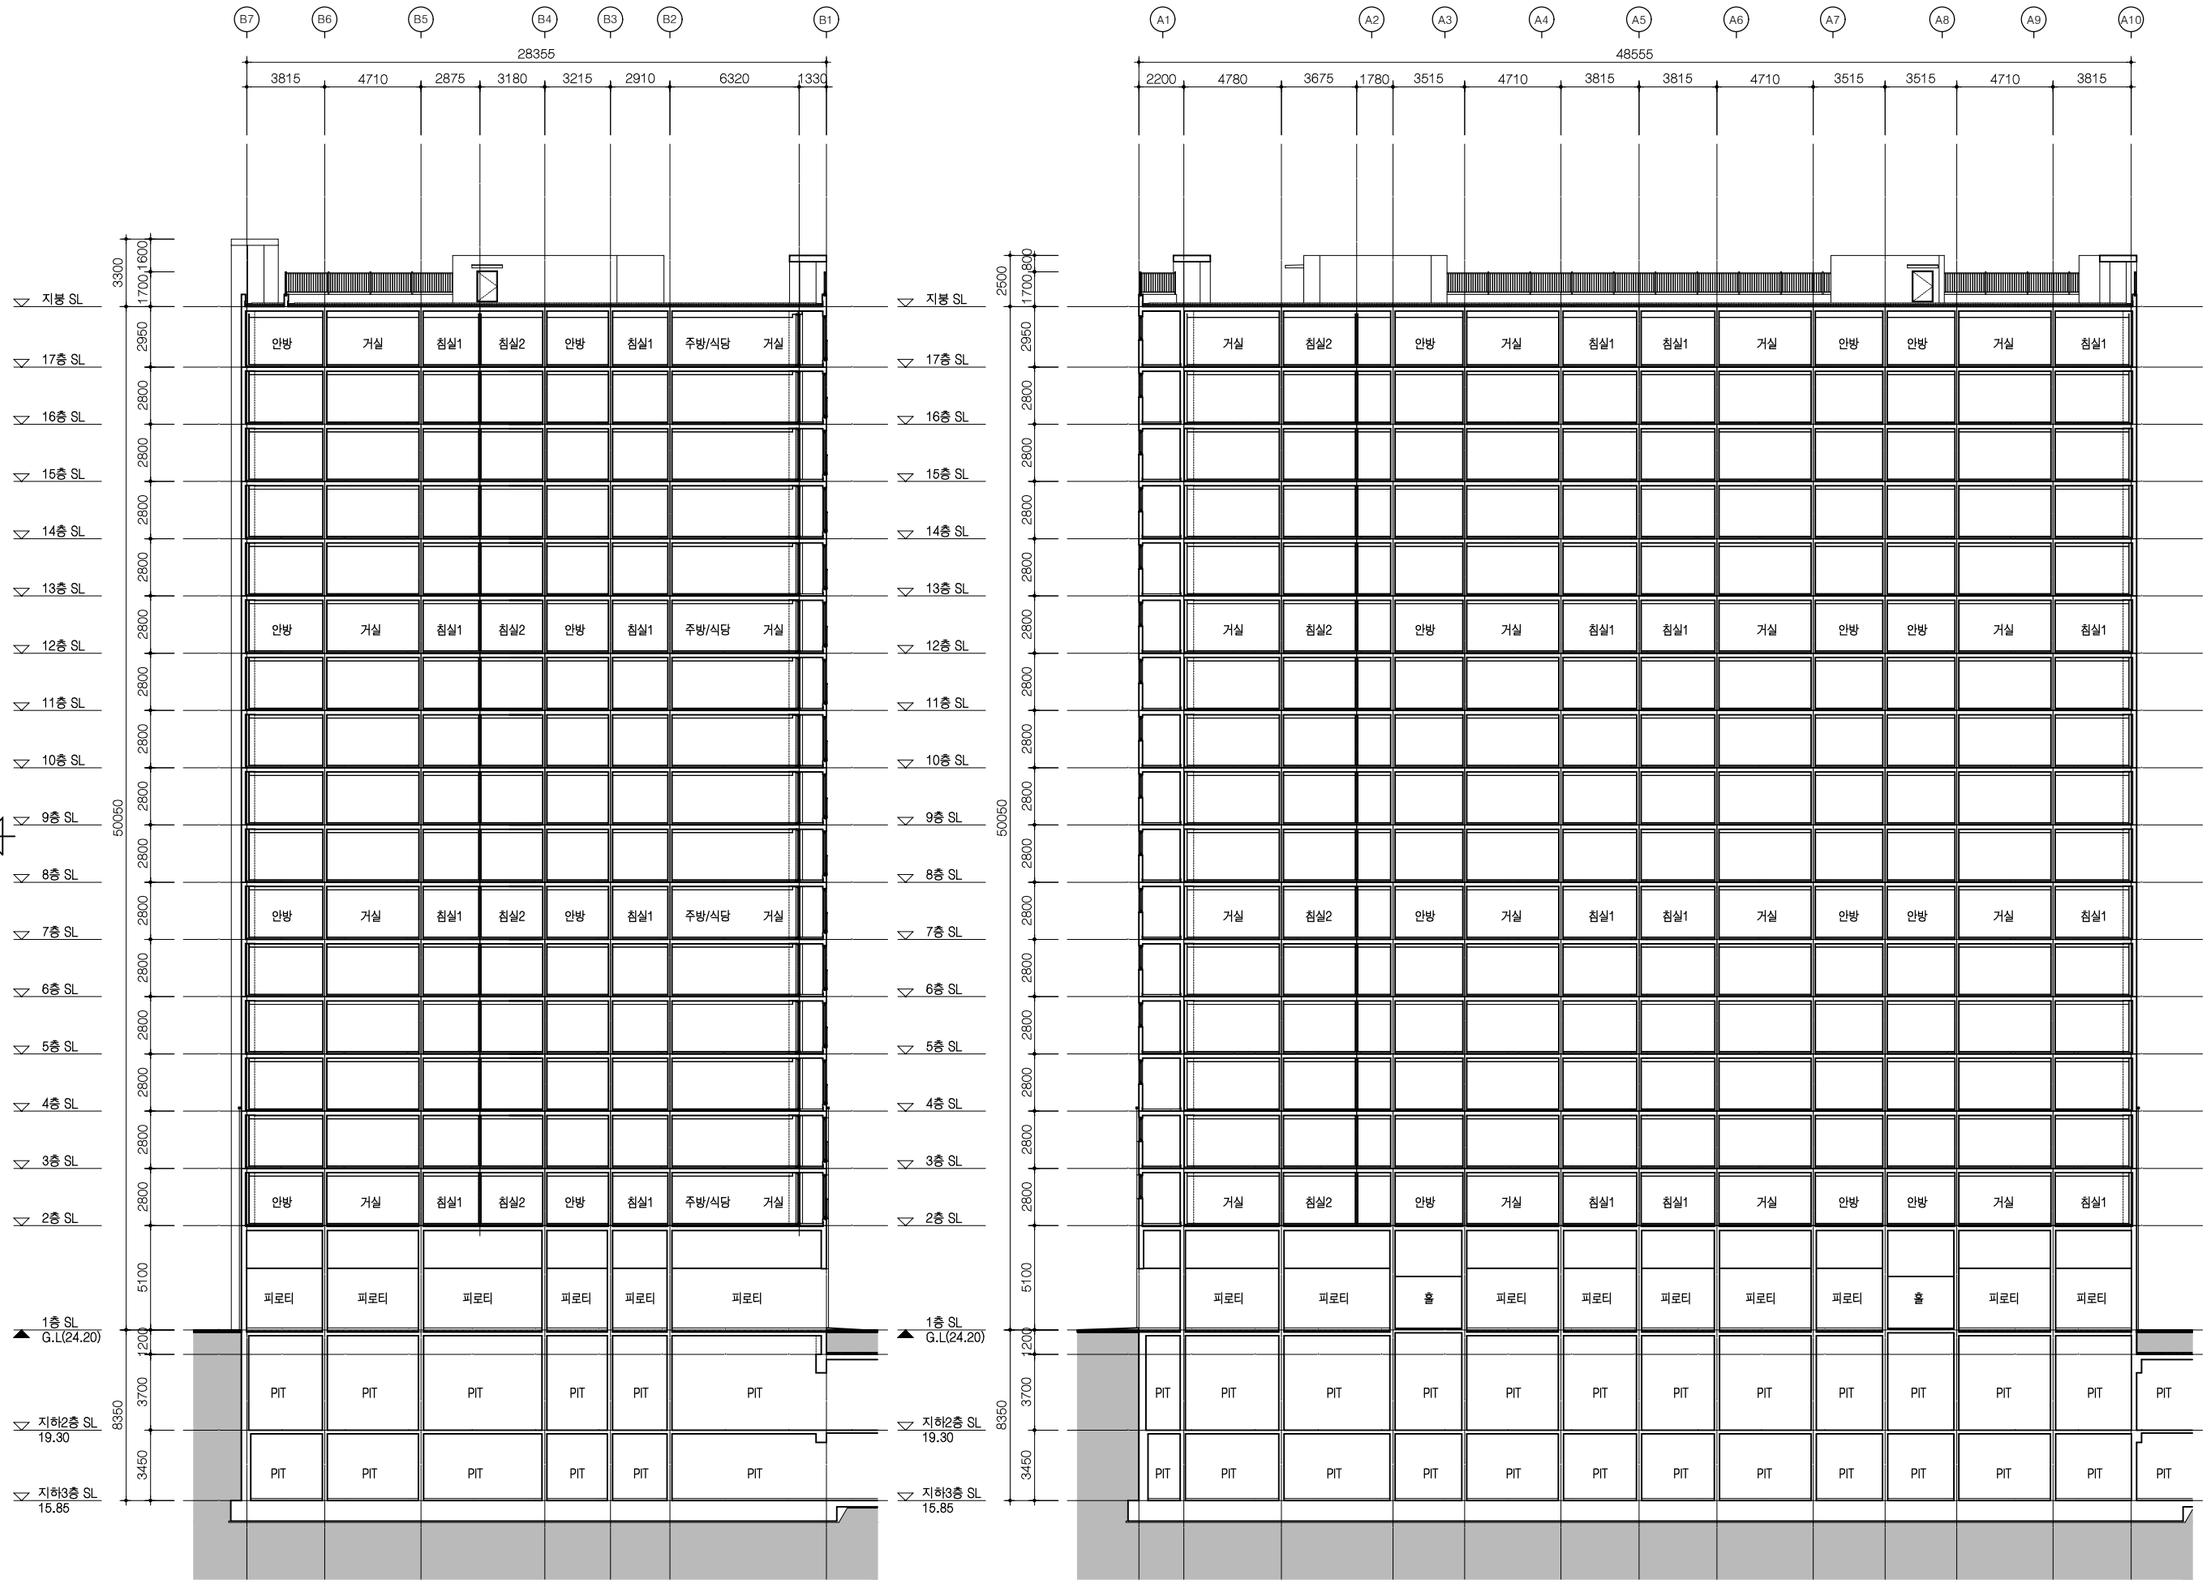
B7 B6 B5 B4 B3 B2 B1
28355
3815 4710 2875 3180 3215 2910 6320 1330
3300 1700 1600
지붕 SL
17층 SL
16층 SL
15층 SL
14층 SL
13층 SL
12층 SL
11층 SL
10층 SL
9층 SL
8층 SL
7층 SL
6층 SL
5층 SL
4층 SL
3층 SL
2층 SL
1층 SL
G.L(24.20)
지하2층 SL
19.30
지하3층 SL
15.85
2950 2800 2800 2800

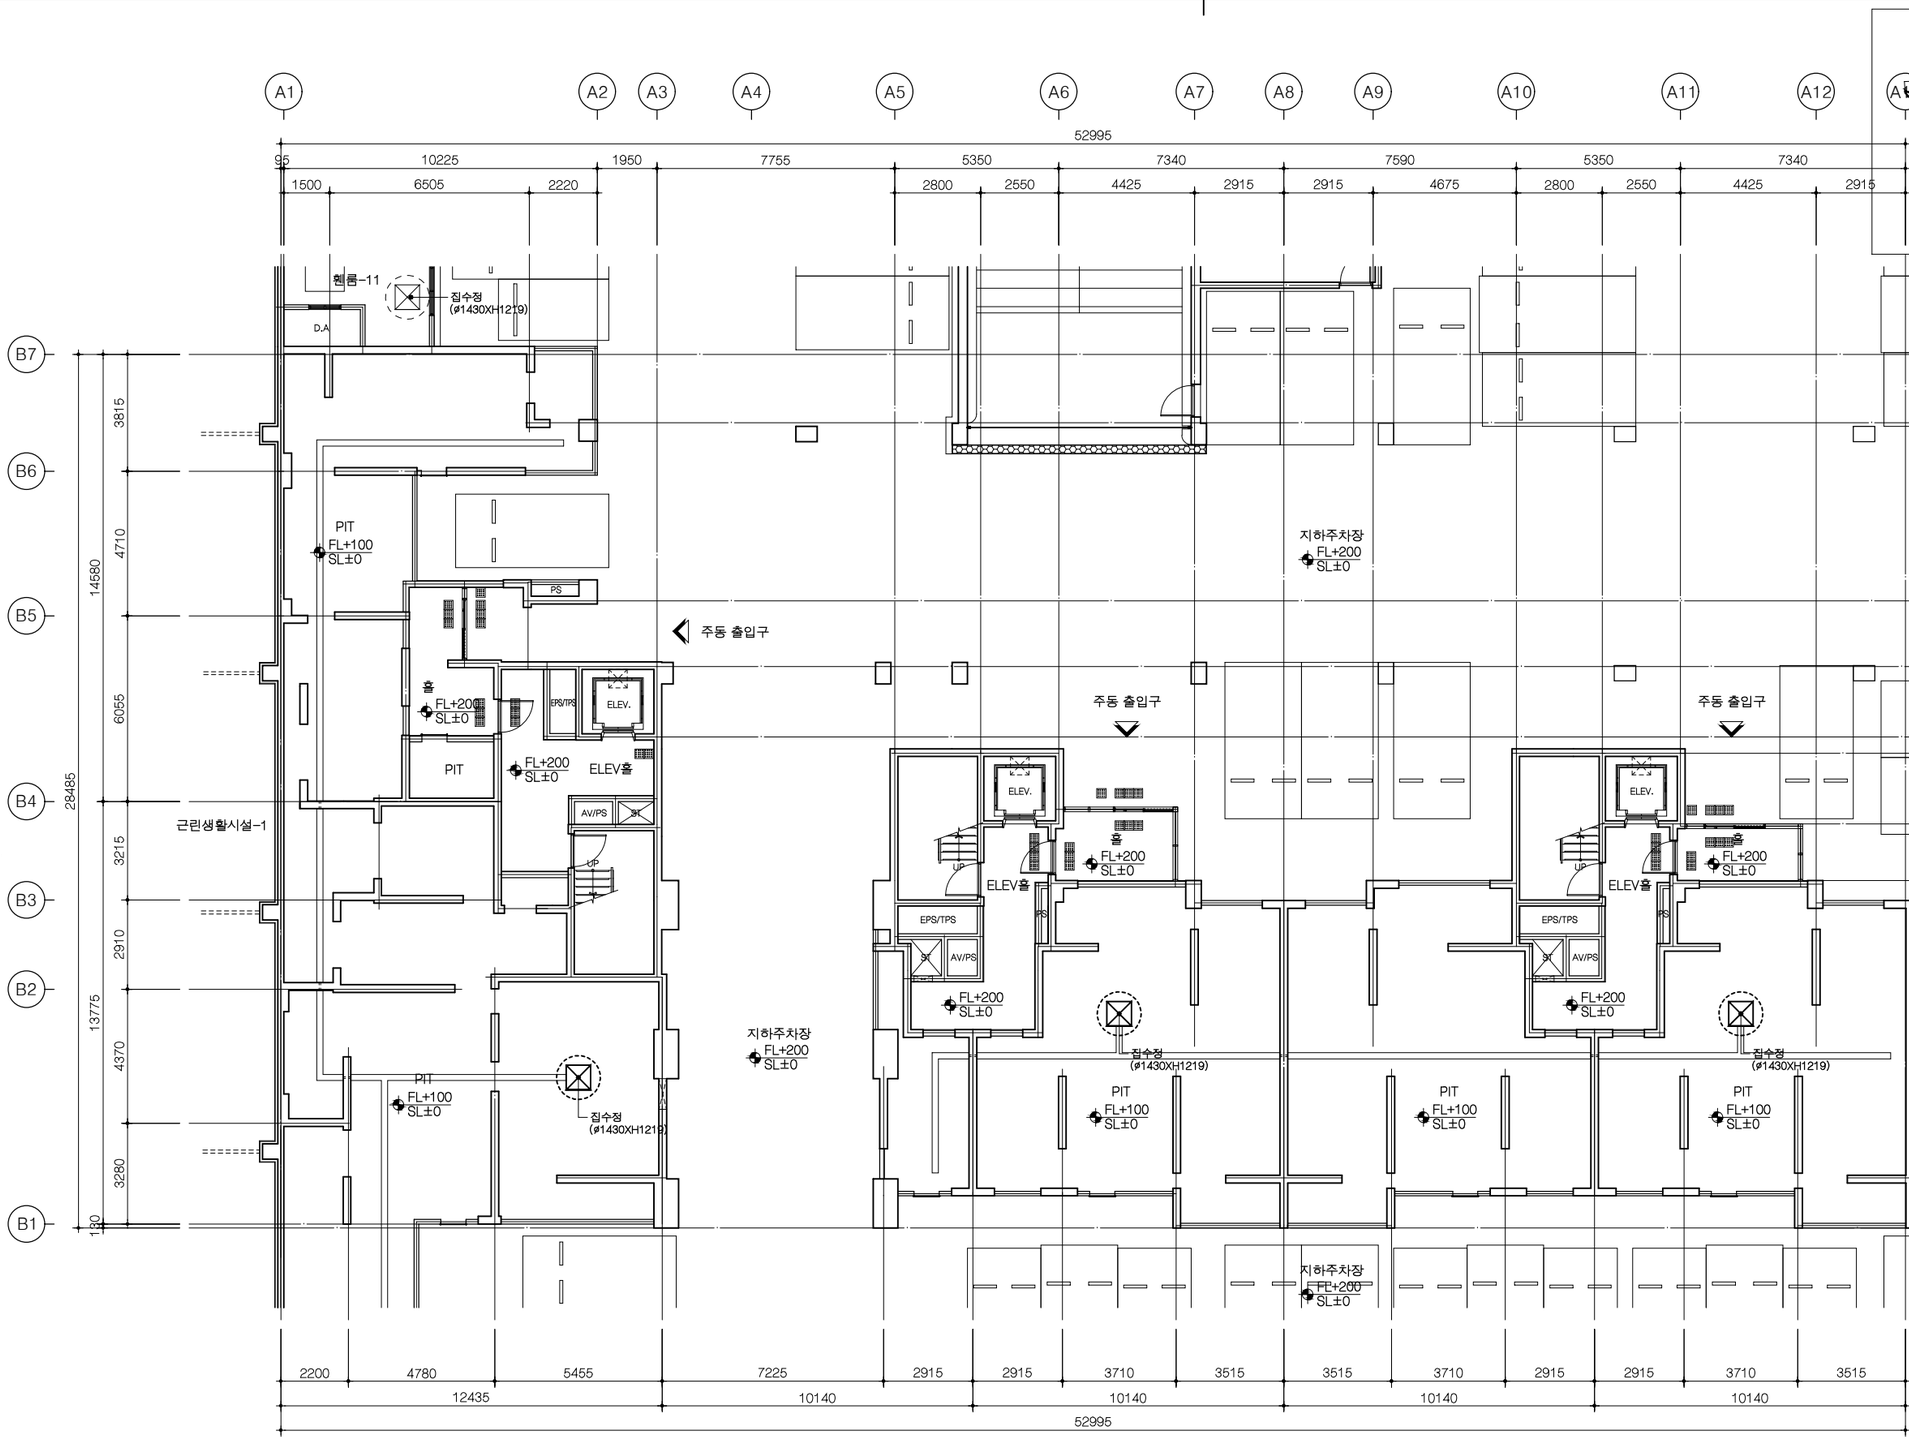

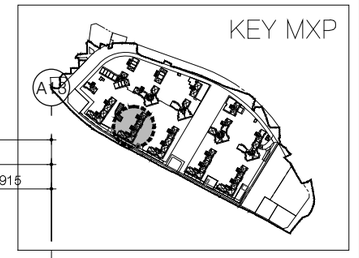

1 A 109동 지하3층 평면도

축척 = 1/100

사업번호 PROJECT NO.

사업명 PROJECT TITLE

수색4재정비촉진구역
주택재개발 정비사업

KEY PLAN

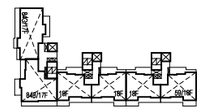

NOTE

1. 지하층 무근 콘크리트는 실시공시 THK80~120 범위로 변동이 있을수 있음.(SLOPE)
2. ELEV홀에 면한부위는 1.0B 조적쌓기임.
3. 지하주차장의 블록쌓기 기준은 높이가 3.6m이하인 경우 4인치 보강블록쌓기가 기준임 (단, 5.4m이하는 6인치쌓기, 5.4m초과는 8인치쌓기가 기준임)
4. ELEV.PIT 집수정은 (600X600X600)임.
5. 주차장 내의 창호는 주차장 창호도 참조.
6. 주차장 집수정 및 영구배수 집수정의 크기 및 위치는 지하주차장 평면도를 참조 할 것.
   ☒ : 주차장 집수정
   ☒ : 영구배수 집수정

********** 지하3층 바닥LEVEL
B3SL±0 = B3FL±0 = EL+15.85

수정번호 REV. NO.	일 자 DATE	내 용 DESCRIPTION	승 인 CHKD
△			
△			
△			
△			

설계 DESIGNED BY

검토 CHECKED BY
최 진 규

심사 SUMMITED BY
정 호 혁

승인 APPROVED BY
이 승 준

일자 DATE
2019.08

도면명 DRAWING TITLE
109동
지하3층 평면도

축 척 SCALE
A1: 1/100
A3: 1/200

도면번호 DRAWING NO.
A-411

일련번호 SHEET NO. △ REV. NO.

HAUD
(주)하우드엔지니어링
종합건축사사무소
Architects, Planners & Engineers
TEL. 02 2140 4400, SEOUL, KOREA

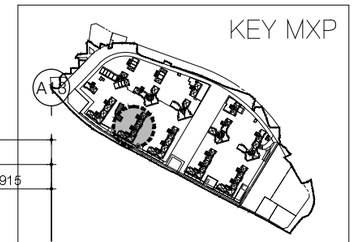

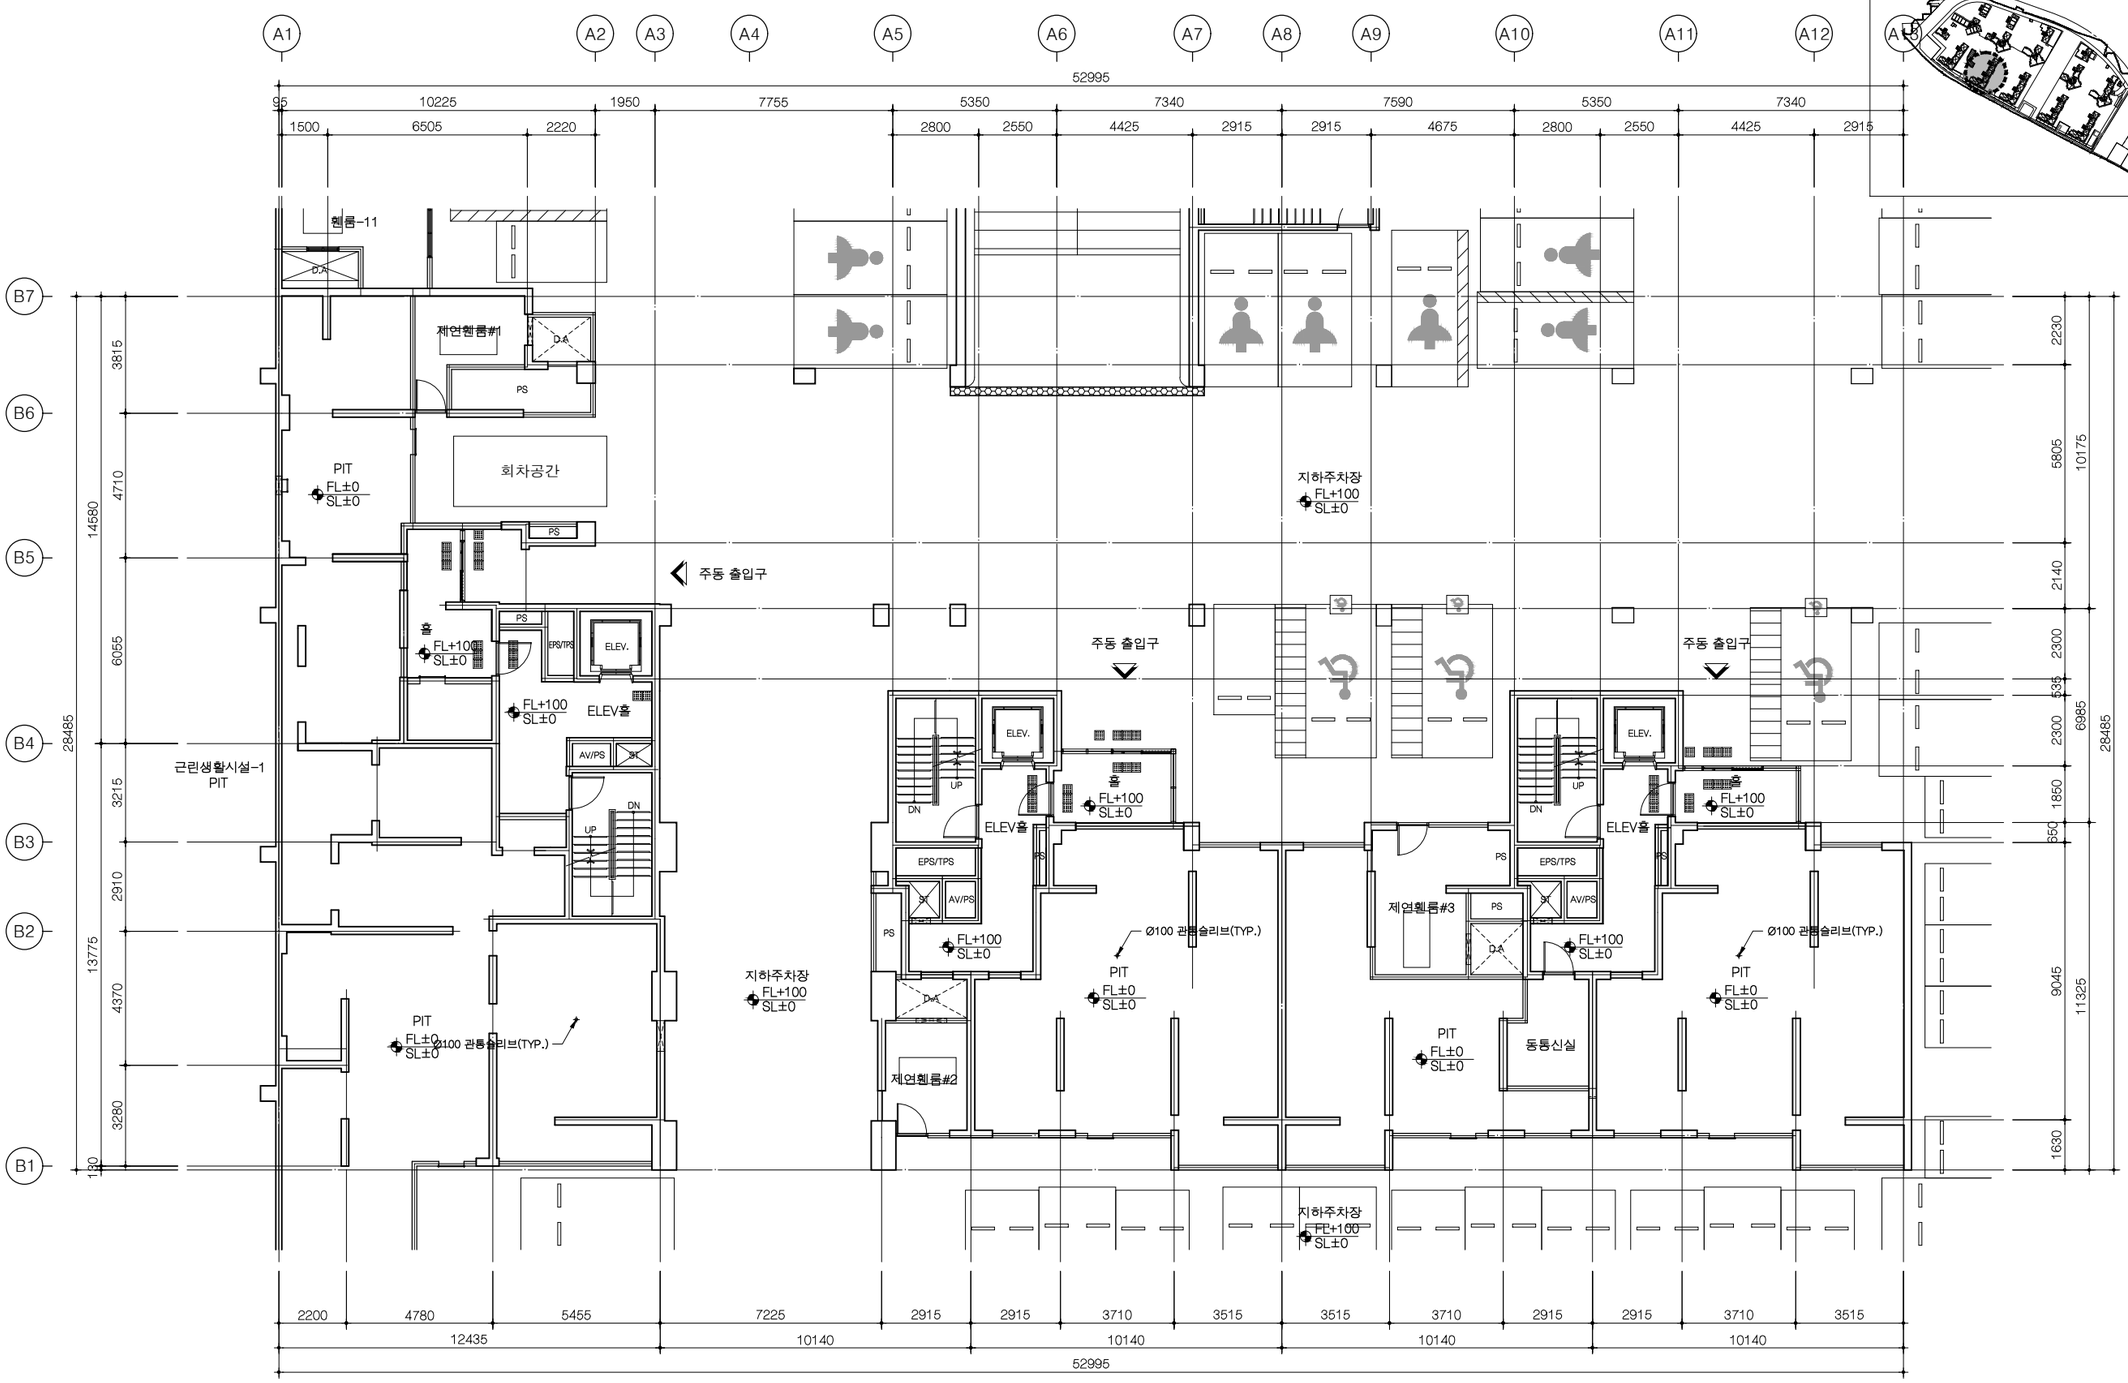

1 A 109동 지하2층 평면도

축척 = 1/100

사업번호 PROJECT NO.

사업명 PROJECT TITLE

수색4재정비촉진구역
주택재개발 정비사업

KEY PLAN

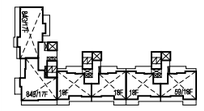

NOTE

1. 지하주차장의 ELEV홀에 면한부위는 1.0B 조적쌓기임.
2. 지하주차장의 블록쌓기 기준은 높이가 3.6m이하인 경우 4인치 보강블록쌓기가 기준임 (단, 5.4m이하는 6인치쌓기, 5.4m초과는 8인치쌓기가 기준임)
3. 주차장 내의 창호는 주차장 창호도 참조.

**** 지하2층 바닥LEVEL
D2SL±0 = D2FL±0 = EL+19.30

수정번호 REV. NO.	일 자 DATE	내 용 DESCRIPTION	승 인 CHKD

설계 DESIGNED BY

검토 CHECKED BY
최 진 규

심사 SUMMITED BY
정 호 혁

승인 APPROVED BY
이 승 준

일자 DATE
2019.08

도면명 DRAWING TITLE
109동
지하2층 평면도

축 척 SCALE
A1: 1/100
A3: 1/200

도면번호 DRAWING NO.
A-412

일련번호 SHEET NO.

REV. NO.

HAUD
(주)하우드엔지니어링
종합건축사사무소
Architects, Planners & Engineers
TEL. 02 2140 4400, SEOUL, KOREA

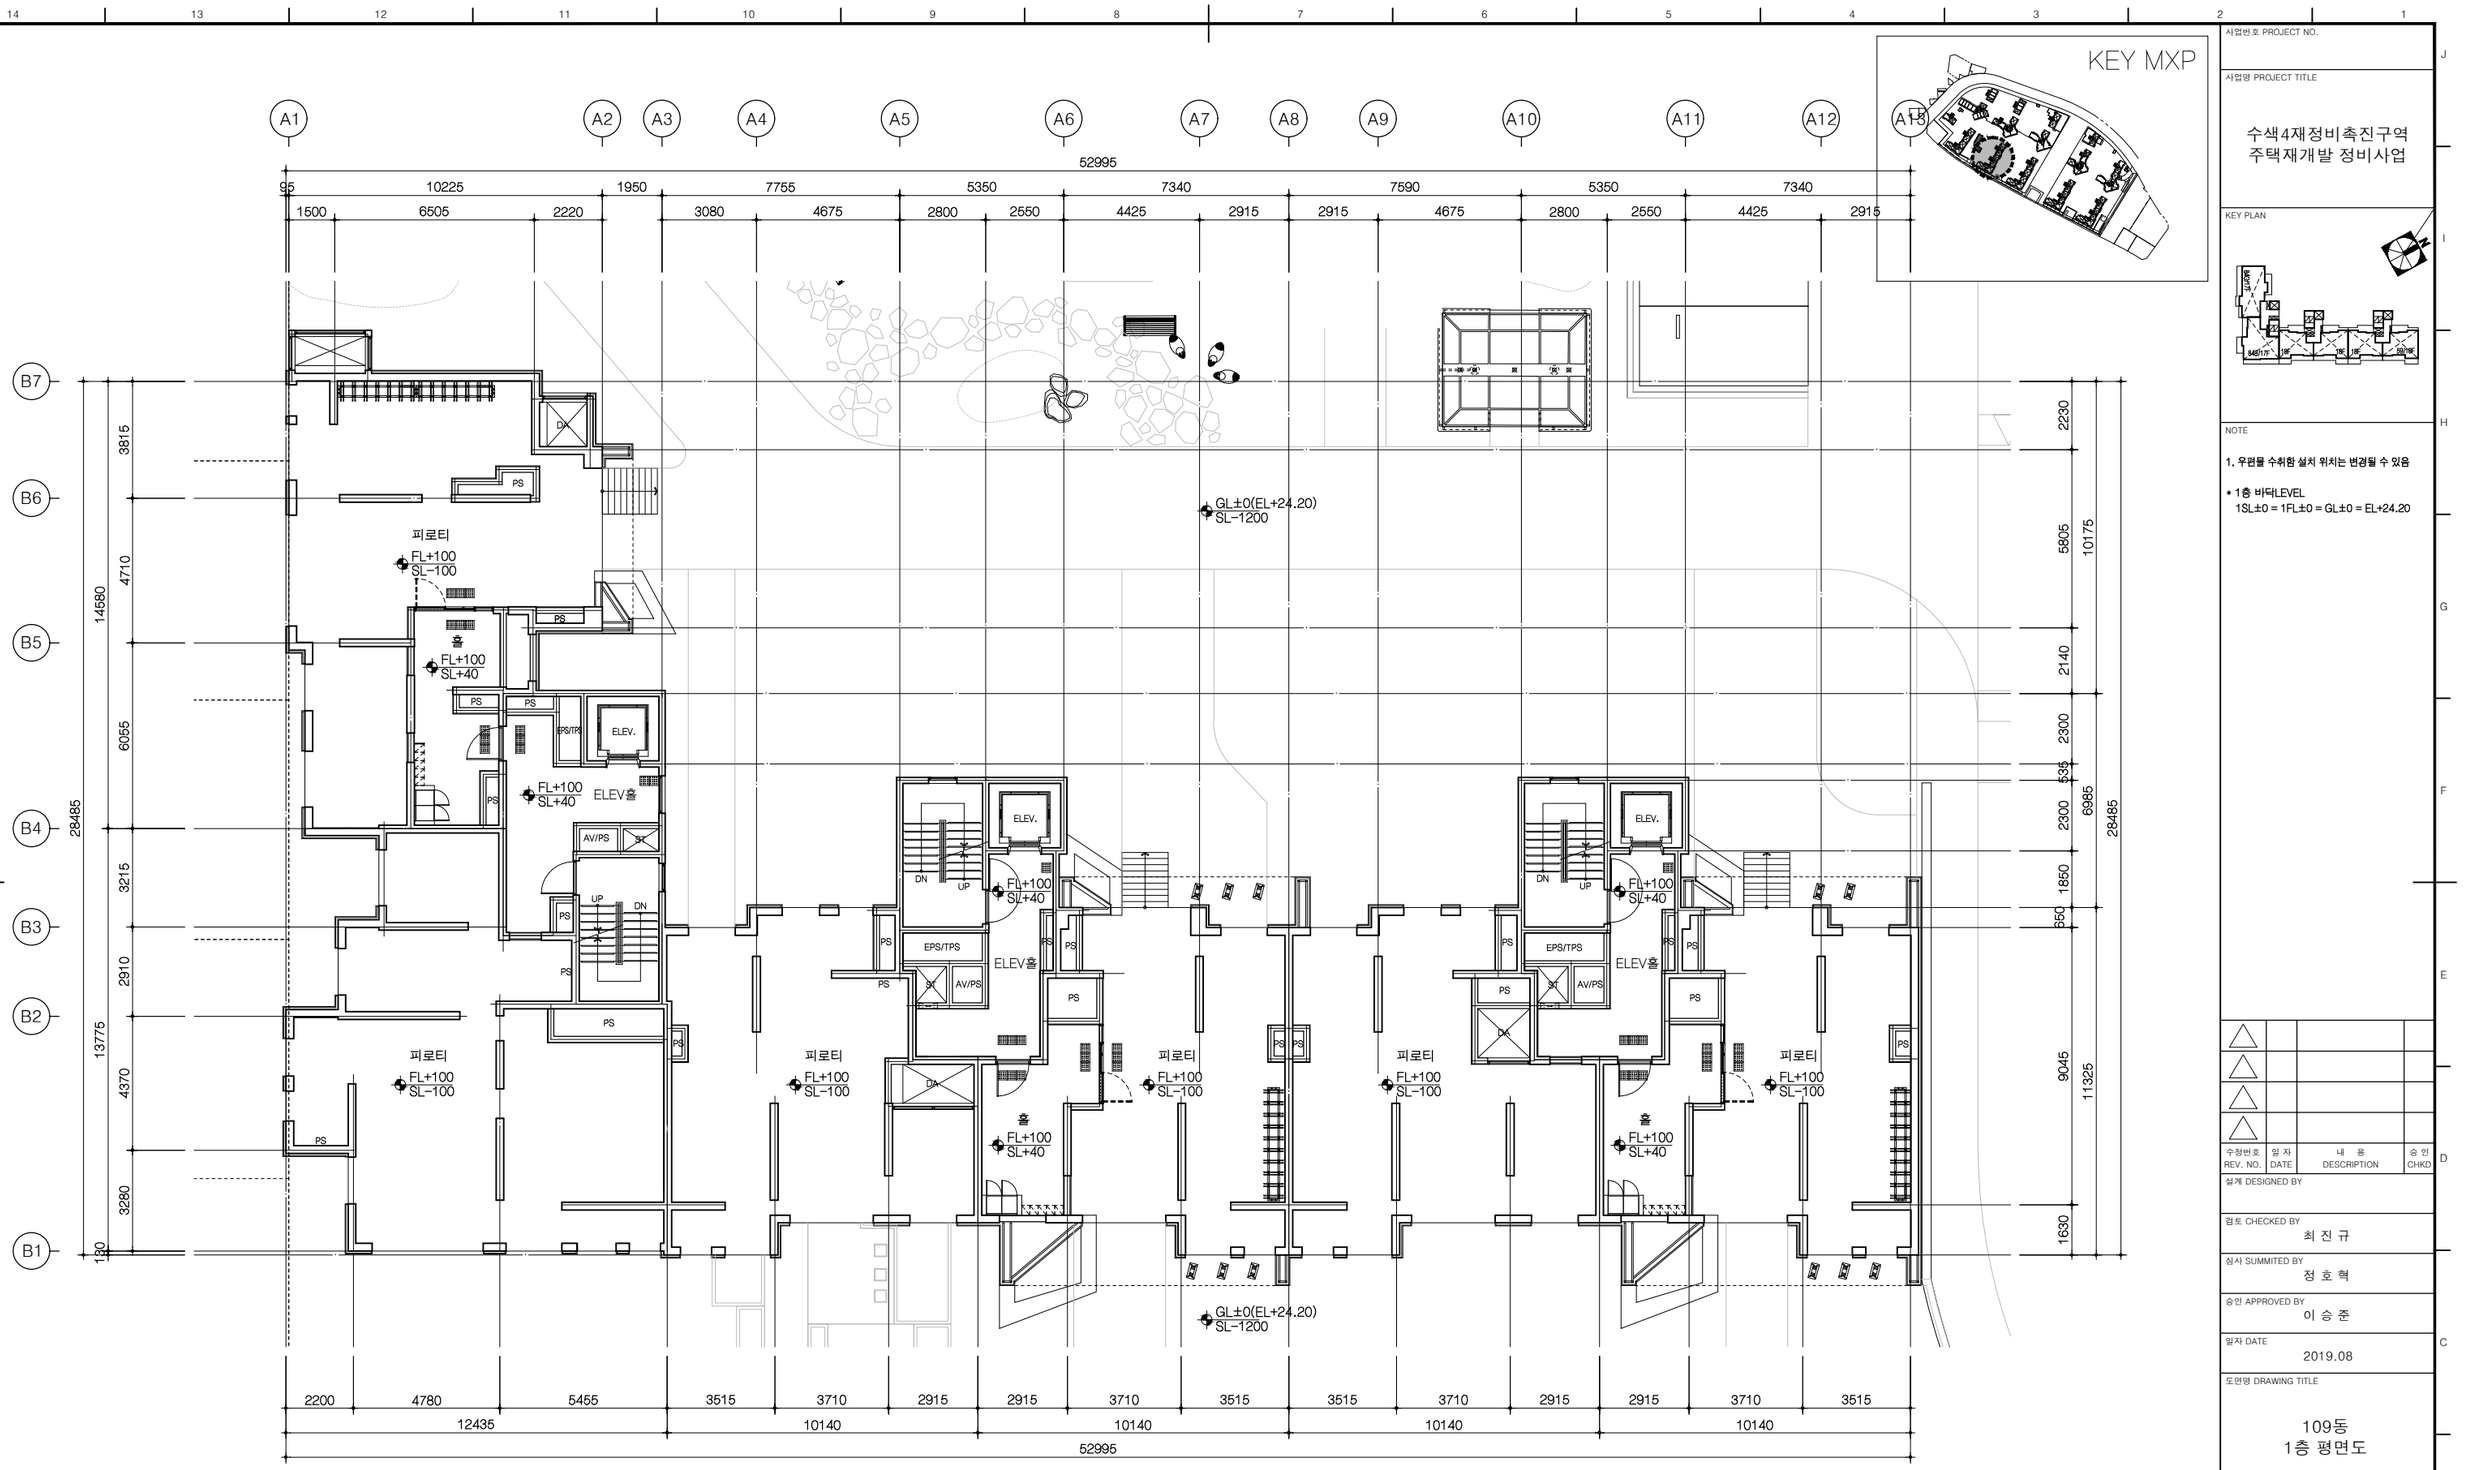

KEY MXP

1 A 109동 1층 평면도

축척 = 1/100

사업번호 PROJECT NO.

사업명 PROJECT TITLE

수색4재정비촉진구역
주택재개발 정비사업

KEY PLAN

NOTE

1. 우려물 수취함 설치 위치는 변경될 수 있음

• 1층 바닥LEVEL
1SL±0 = 1FL±0 = GL±0 = EL+24.20

수정번호 REV. NO.	일 자 DATE	내 용 DESCRIPTION	승 인 CHKD
△			
△			
△			
△			

설계 DESIGNED BY

검토 CHECKED BY
최 진 규

심사 SUMMITED BY
정 호 혁

승인 APPROVED BY
이 승 준

일자 DATE
2019.08

도면명 DRAWING TITLE
109동
1층 평면도

축 척 SCALE
A1: 1/100
A3: 1/200

도면번호 DRAWING NO.
A-413

일련번호 SHEET NO. △ REV. NO.

HAUD
(주)하우드엔지니어링
종합건축사사무소
Architects, Planners & Engineers
TEL. 02 2140 4400, SEOUL, KOREA

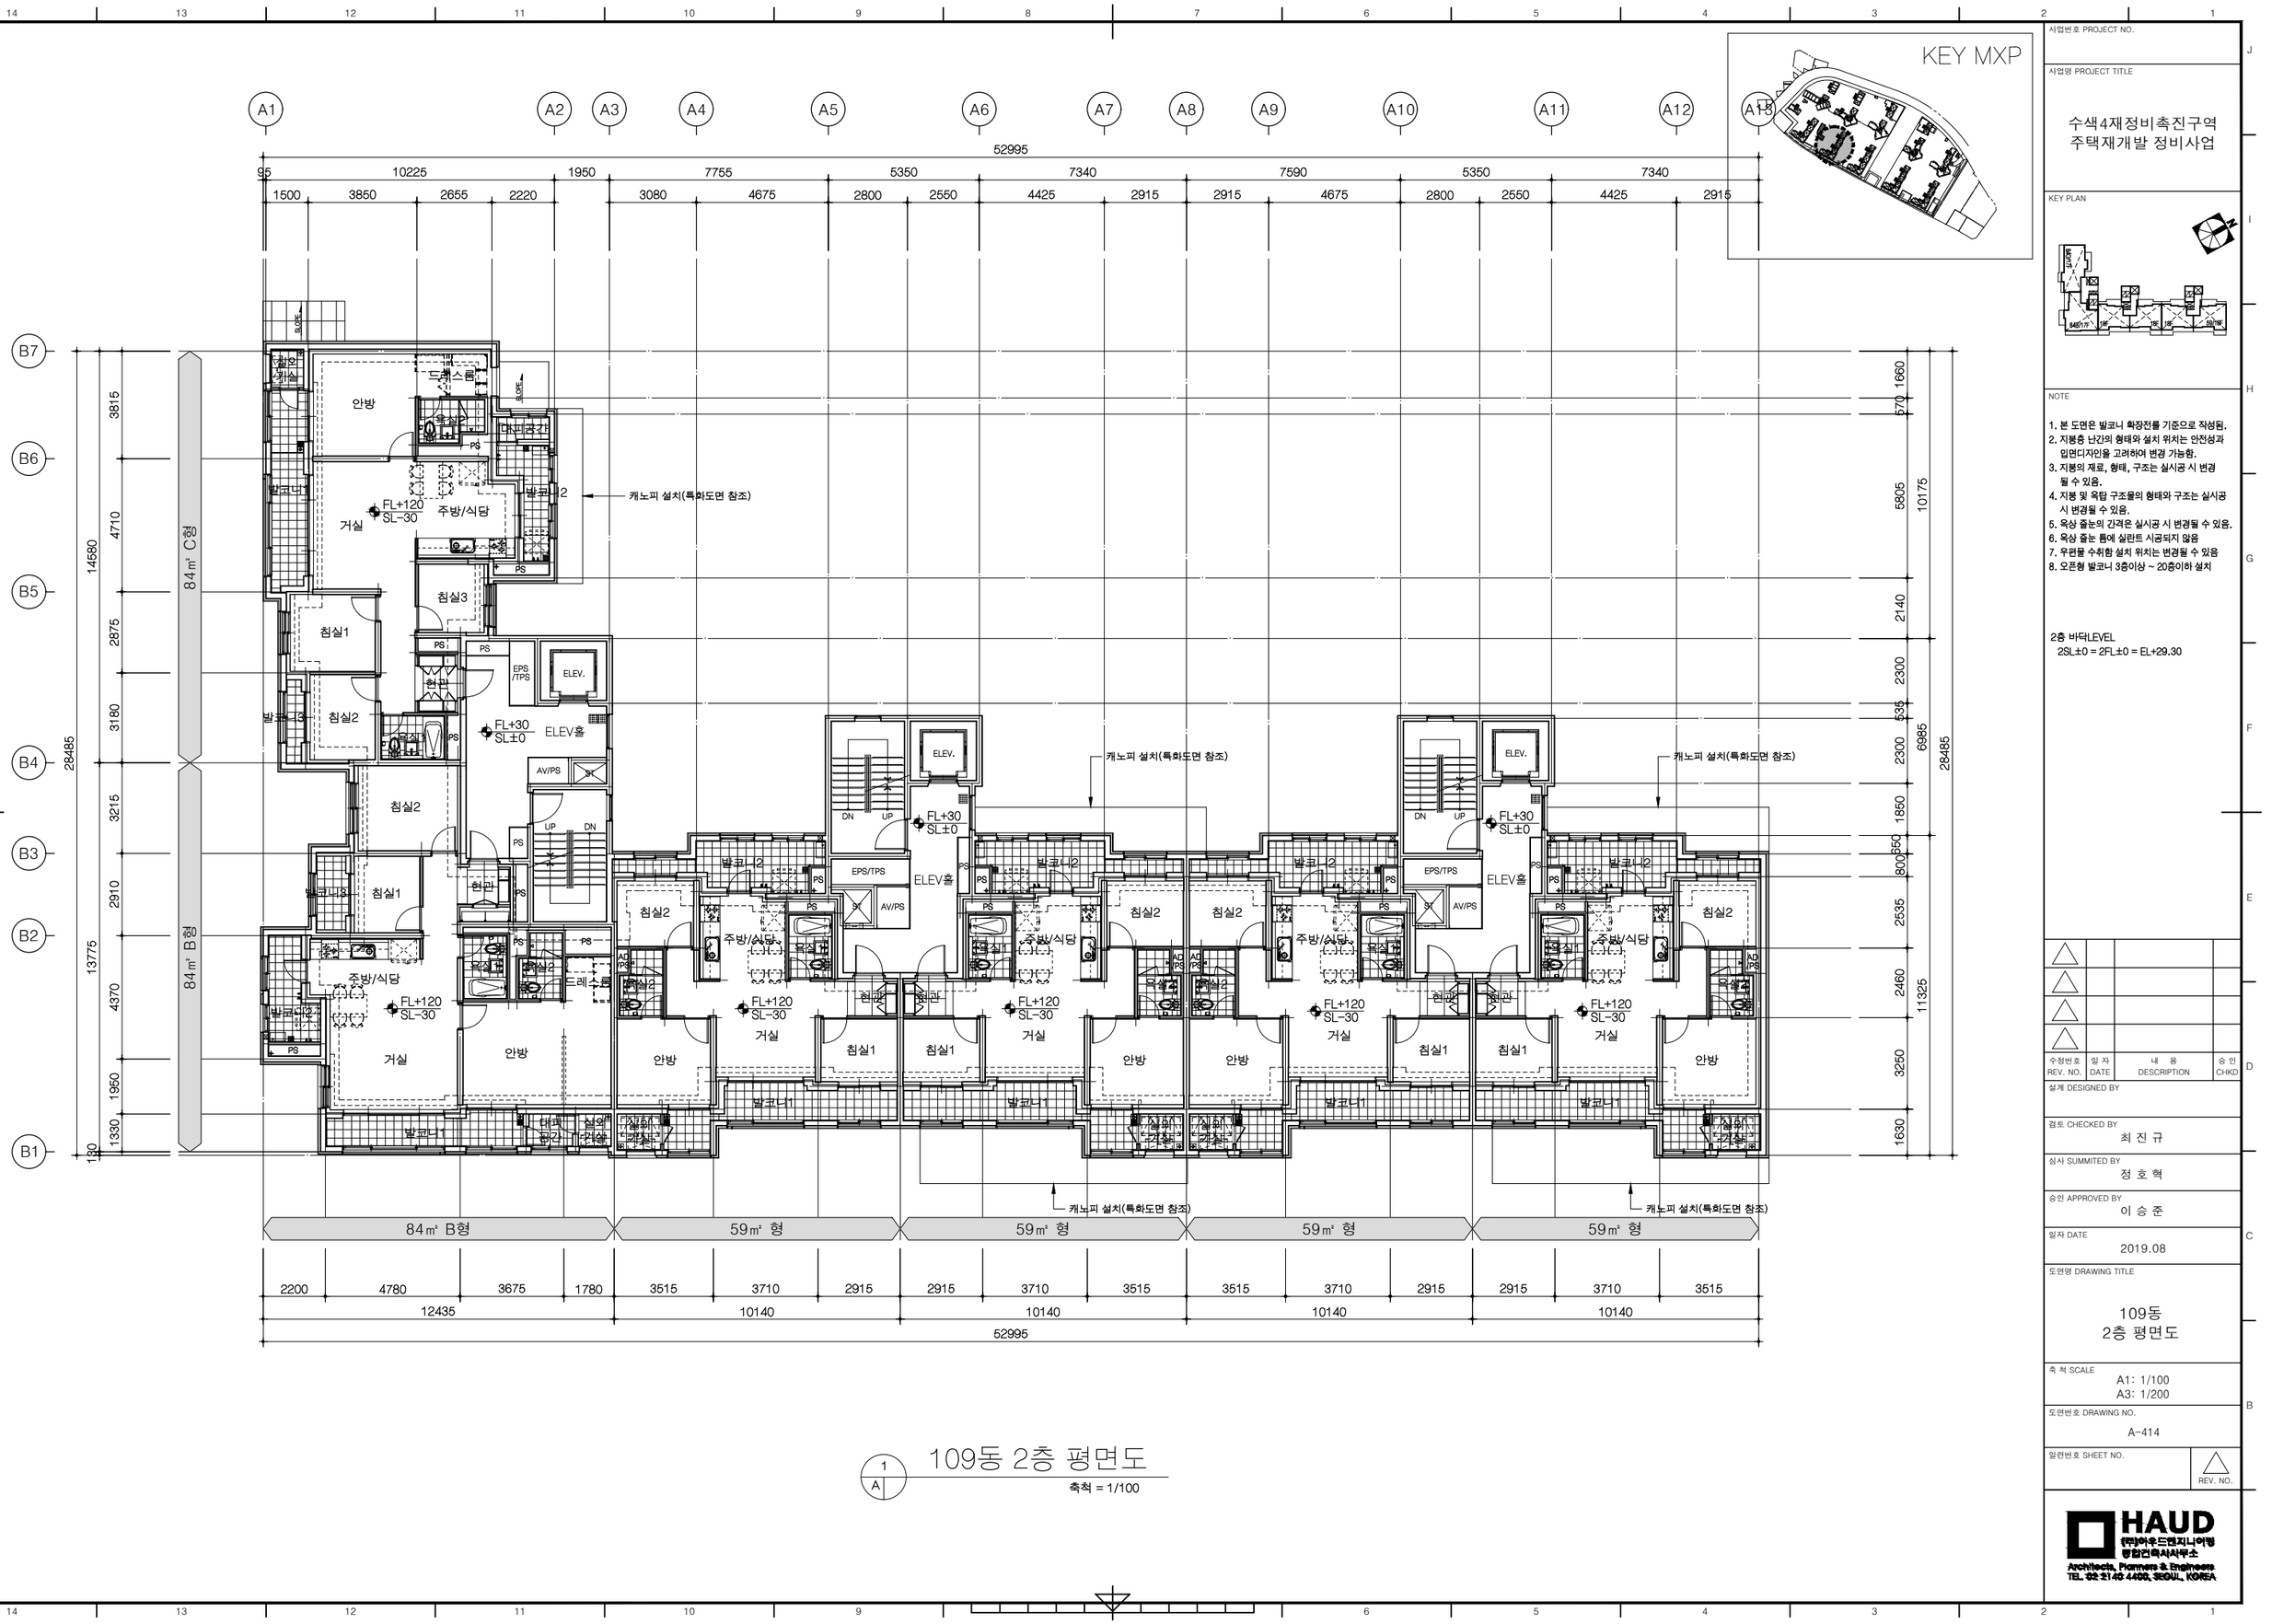

1 A 109동 2층 평면도

축척 = 1/100

KEY MXP

사업번호 PROJECT NO.

사업명 PROJECT TITLE

수색4재정비촉진구역
주택재개발 정비사업

KEY PLAN

NOTE

1. 본 도면은 발코니 확장전를 기준으로 작성됨.
2. 지붕층 난간의 형태와 설치 위치는 안전성과 입면디자인을 고려하여 변경 가능함.
3. 지붕의 재료, 형태, 구조는 실시공 시 변경 될 수 있음.
4. 지붕 및 옥탑 구조물의 형태와 구조는 실시공 시 변경될 수 있음.
5. 옥상 출눈의 간격은 실시공 시 변경될 수 있음.
6. 옥상 출눈 틈에 실란트 시공되지 않음
7. 우편물 수취함 설치 위치는 변경될 수 있음
8. 오픈형 발코니 3층이상 ~ 20층이하 설치

2층 바닥LEVEL
2SL±0 = 2FL±0 = EL+29.30

수정번호 REV. NO.	일 자 DATE	내 용 DESCRIPTION	승 인 CHKD
△			
△			
△			
△			

설계 DESIGNED BY

검토 CHECKED BY
최 진 규

심사 SUMMITED BY
정 호 혁

승인 APPROVED BY
이 승 준

일자 DATE
2019.08

도면명 DRAWING TITLE
109동
2층 평면도

축 척 SCALE
A1: 1/100
A3: 1/200

도면번호 DRAWING NO.
A-414

일련번호 SHEET NO. △ REV. NO.

HAUD
(주)하우드엔지니어링
종합건축사사무소
Architects, Planners & Engineers
TEL. 02 2140 4400, SEOUL, KOREA

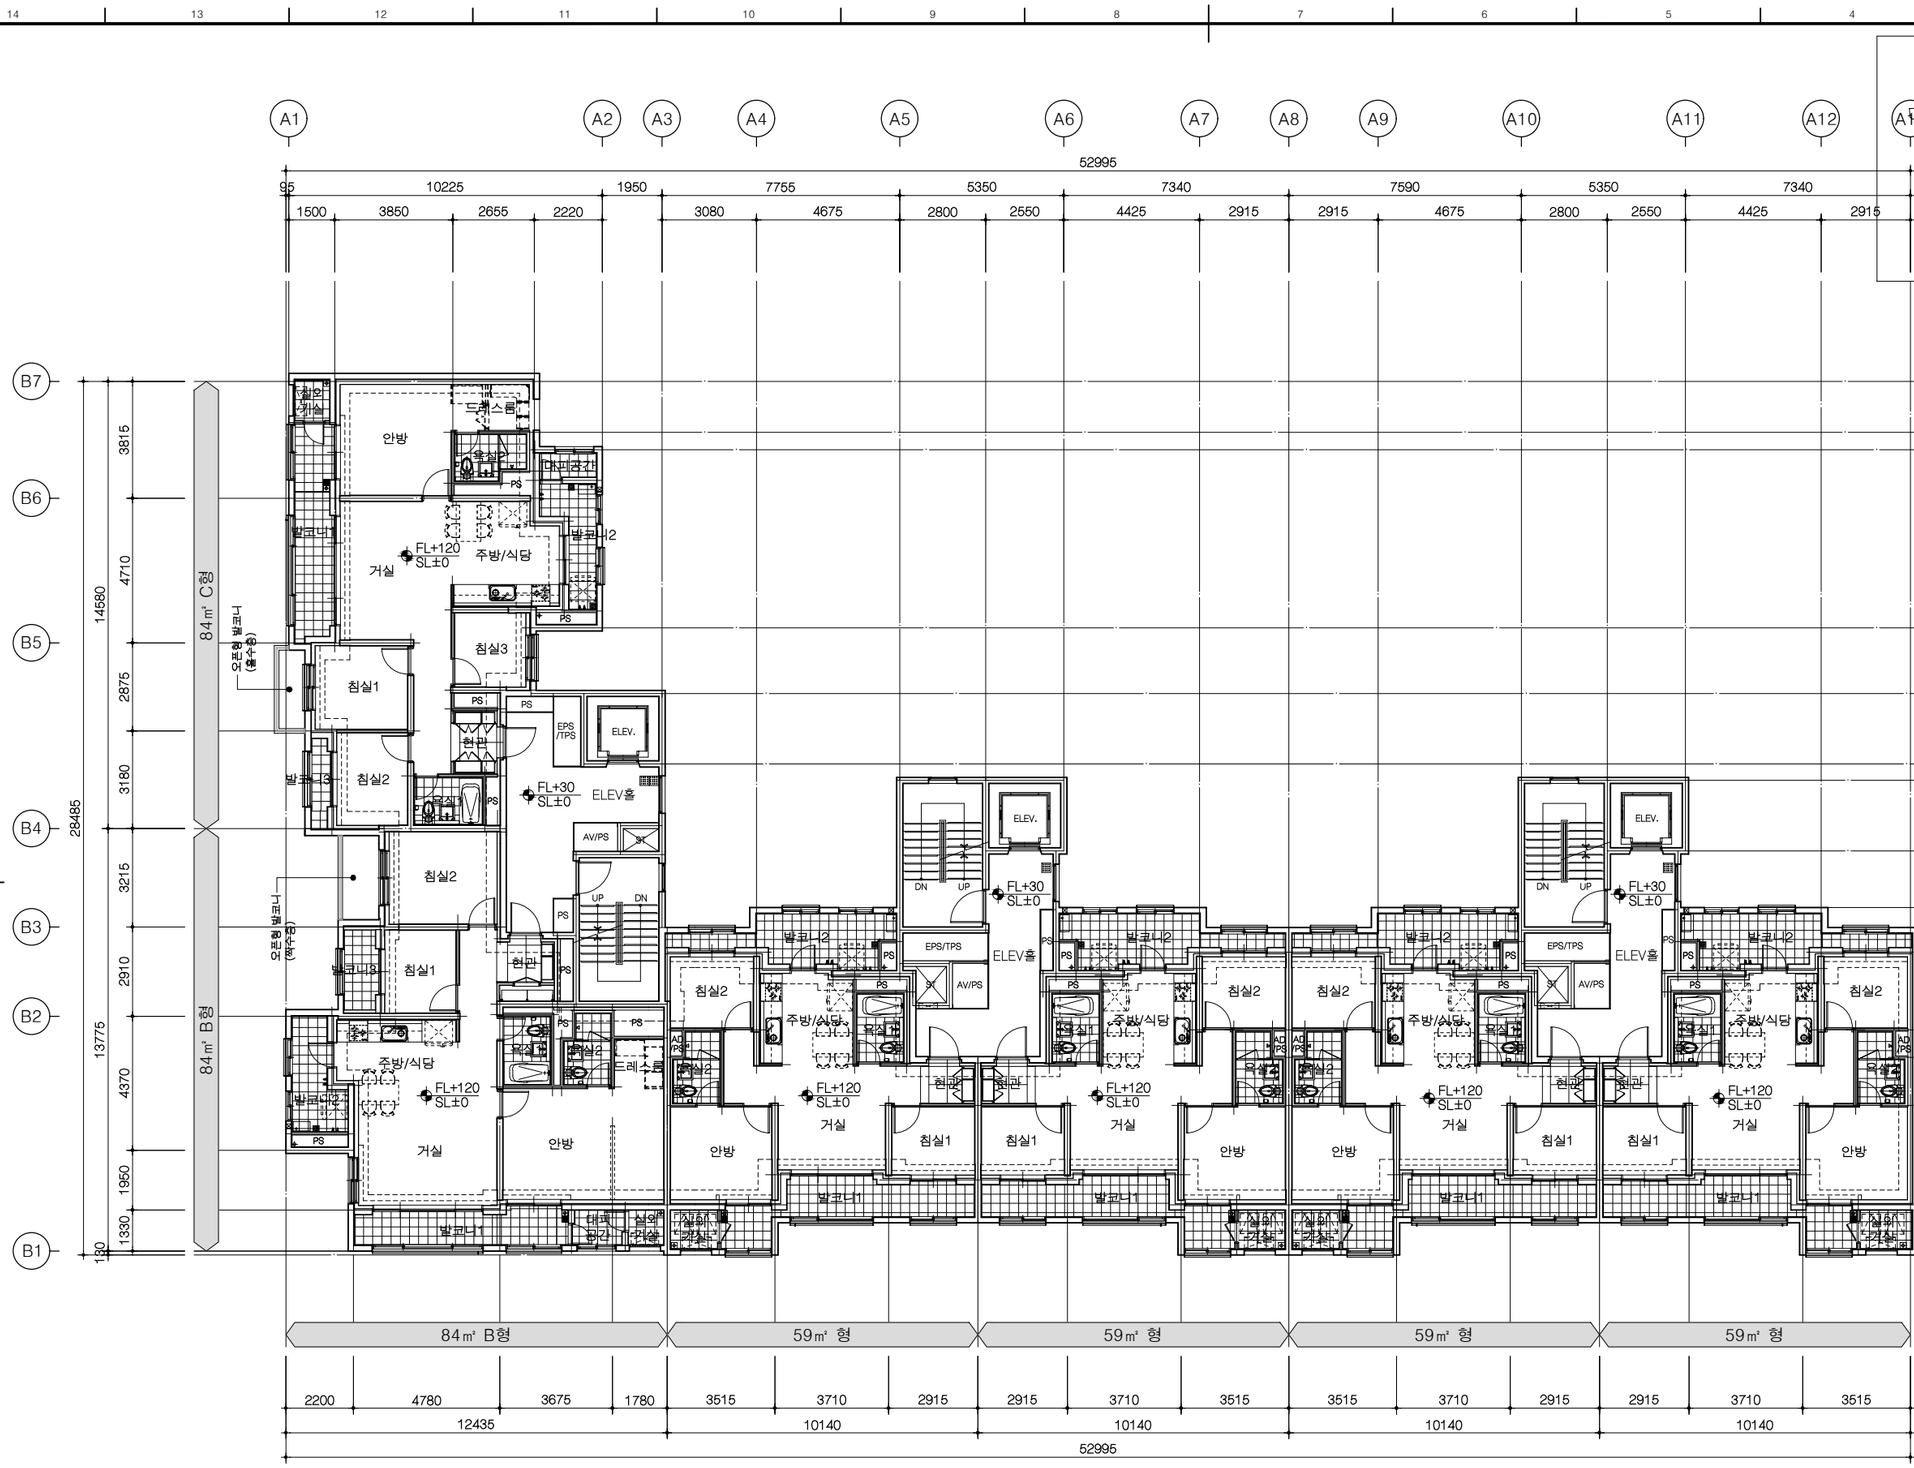

1 A 109동 3~17층 평면도

축척 = 1/100

KEY MXP

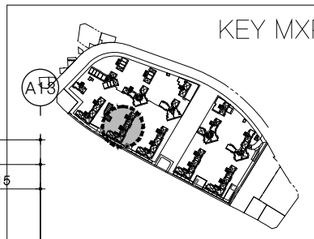

사업번호 PROJECT NO.

사업명 PROJECT TITLE

수색4재정비촉진구역
주택재개발 정비사업

KEY PLAN

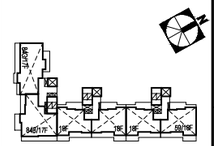

NOTE

1. 본 도면은 발코니 확장전를 기준으로 작성됨.
2. 지붕층 난간의 형태와 설치 위치는 안전성과 입면디자인을 고려하여 변경 가능함.
3. 지붕의 재료, 형태, 구조는 실시공 시 변경 될 수 있음.
4. 지붕 및 옥탑 구조물의 형태와 구조는 실시공 시 변경될 수 있음.
5. 옥상 출눈의 간격은 실시공 시 변경될 수 있음.
6. 옥상 출눈 틈에 실란트 시공되지 않음
7. 우편물 수취함 설치 위치는 변경될 수 있음
8. 오픈형 발코니 3층이상 ~ 20층이하 설치

수정번호 REV. NO.	일 자 DATE	내 용 DESCRIPTION	승 인 CHKD

설계 DESIGNED BY

검토 CHECKED BY
최 진 규

심사 SUMMITED BY
정 호 혁

승인 APPROVED BY
이 승 준

일자 DATE
2019.08

도면명 DRAWING TITLE
109동
3층~17층 평면도

축 척 SCALE
A1: 1/100
A3: 1/200

도면번호 DRAWING NO.
A-415

일련번호 SHEET NO.

REV. NO.

HAUD
(주)하우드엔지니어링
종합건축사사무소
Architects, Planners & Engineers
TEL. 02 2140 4400, SEOUL, KOREA

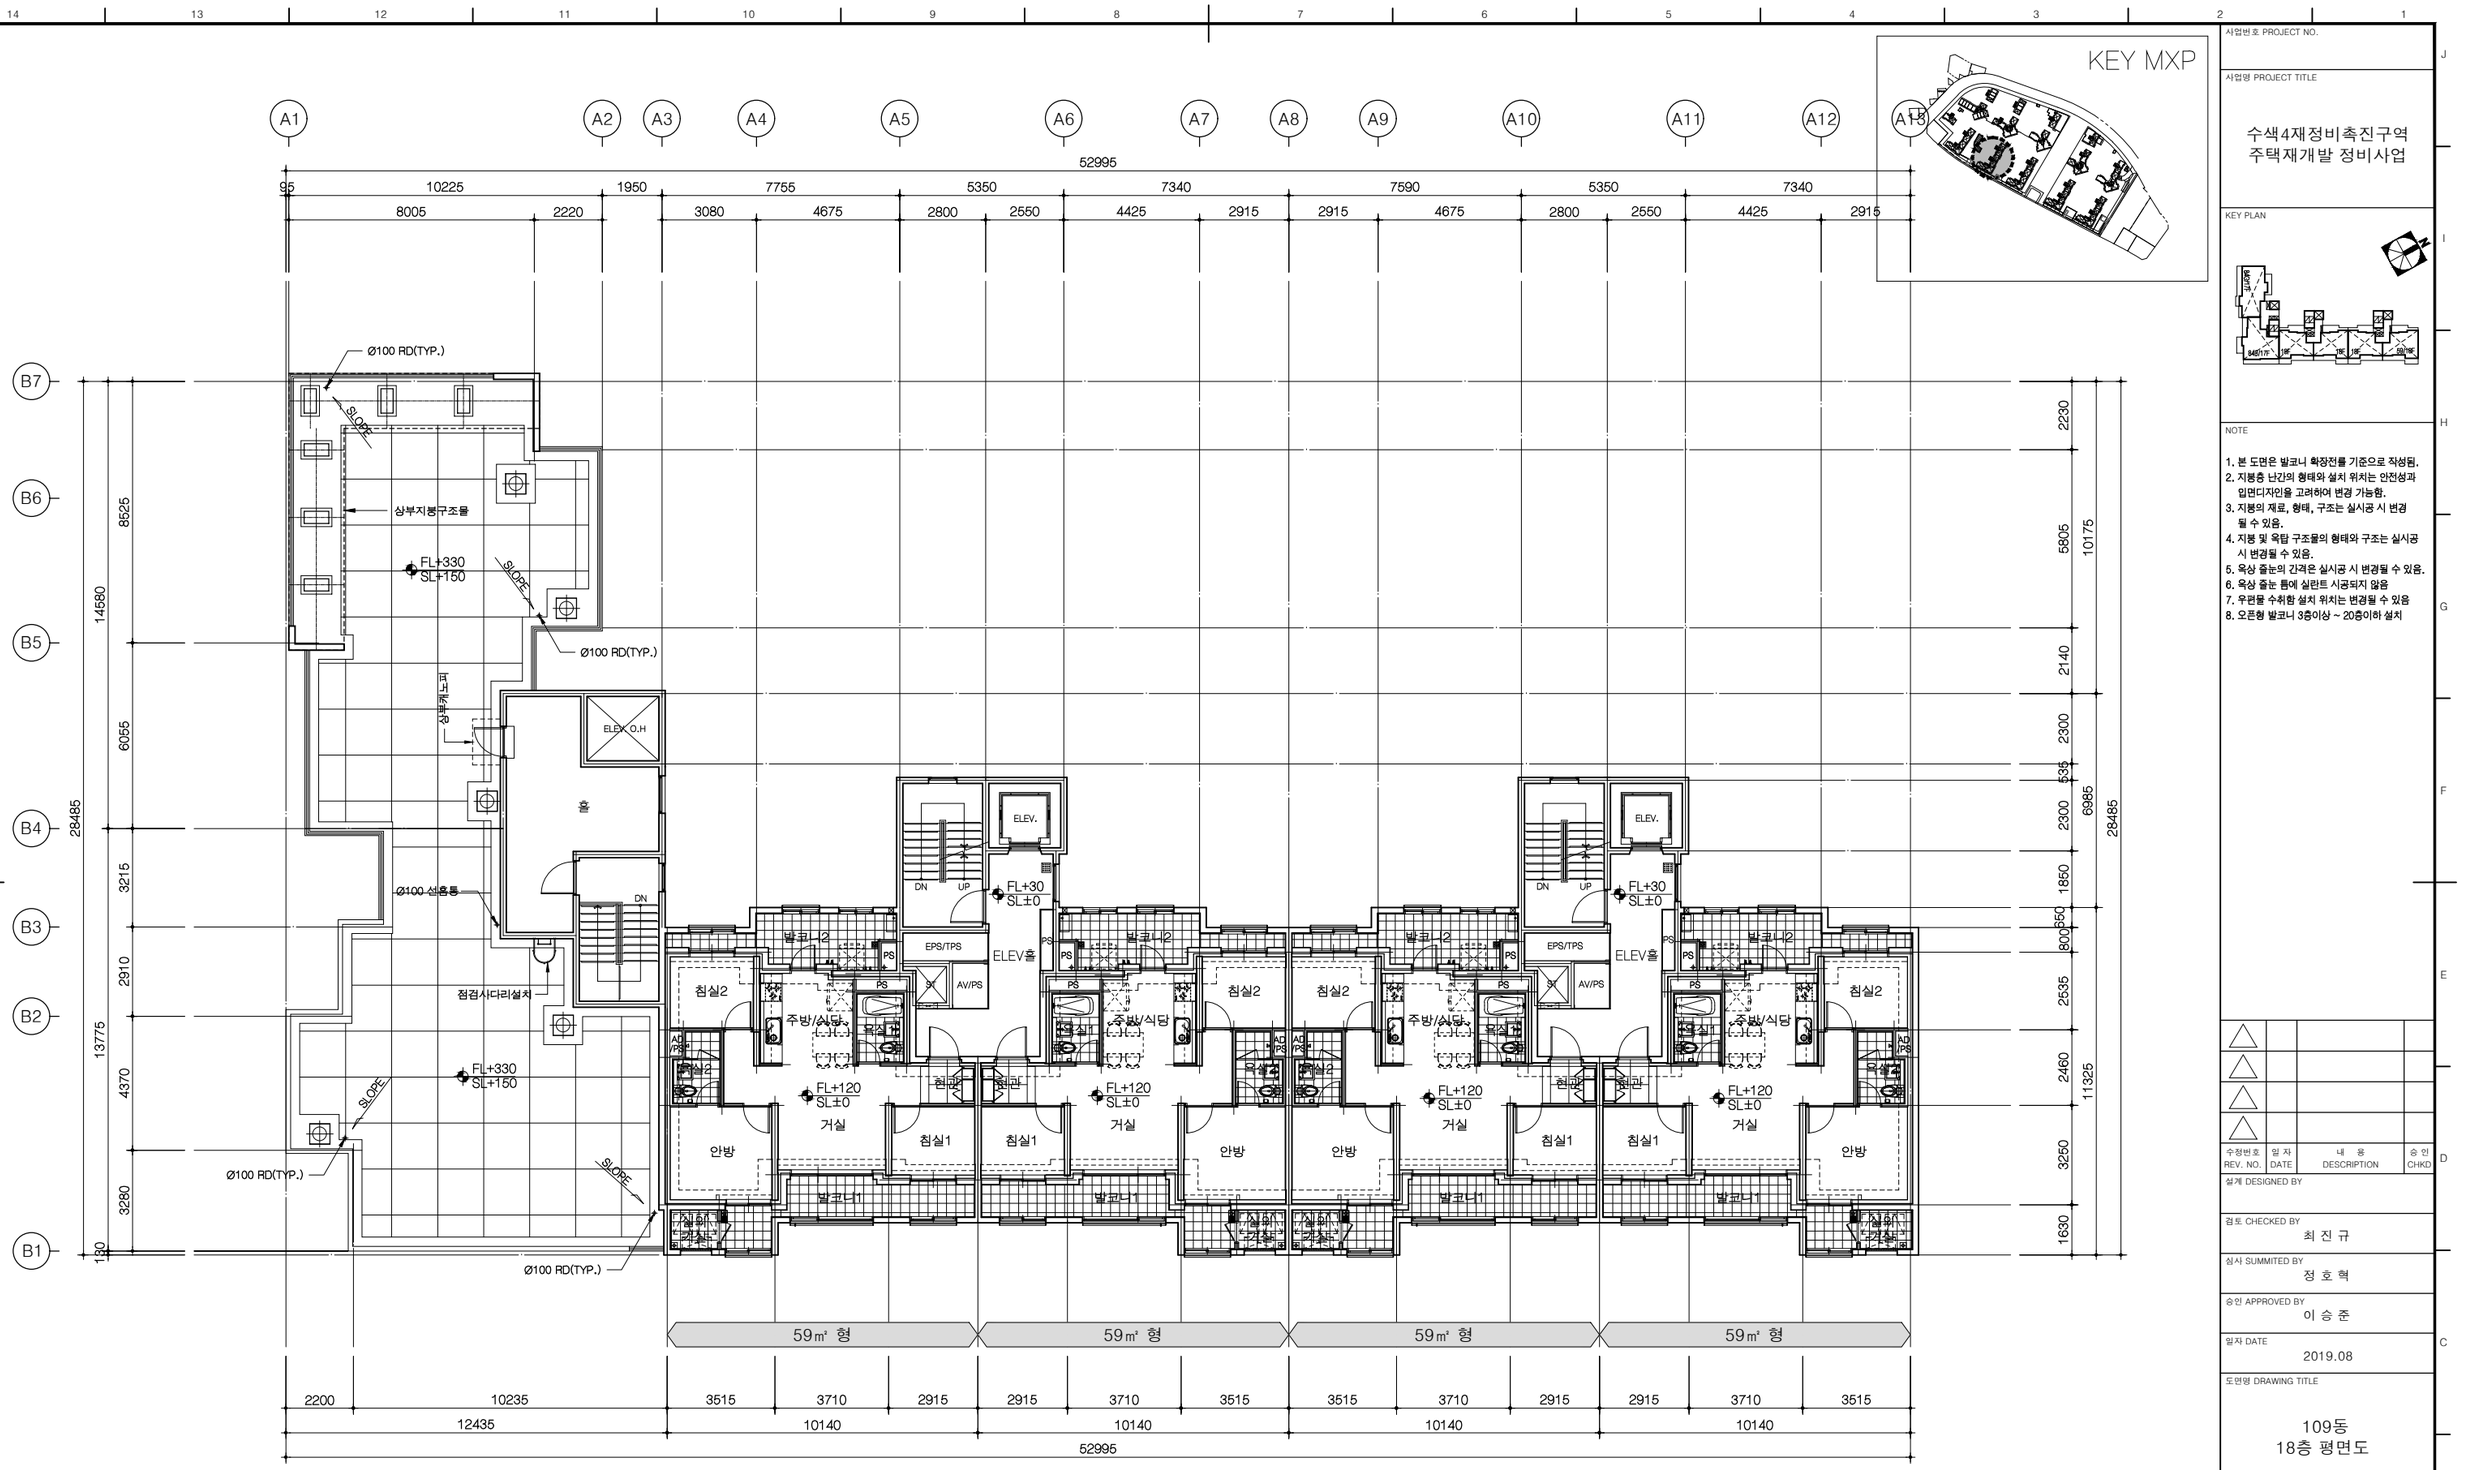

1 A 109동 18층 평면도

축척 = 1/100

사업번호 PROJECT NO.

사업명 PROJECT TITLE

수색4재정비촉진구역
주택재개발 정비사업

KEY PLAN

NOTE

1. 본 도면은 발코니 확장전를 기준으로 작성됨.
2. 지붕층 난간의 형태와 설치 위치는 안전성과 입면디자인을 고려하여 변경 가능함.
3. 지붕의 재료, 형태, 구조는 실시공 시 변경 될 수 있음.
4. 지붕 및 옥탑 구조물의 형태와 구조는 실시공 시 변경될 수 있음.
5. 옥상 출눈의 간격은 실시공 시 변경될 수 있음.
6. 옥상 출눈 틈에 실란트 시공되지 않음
7. 우편물 수취함 설치 위치는 변경될 수 있음
8. 오픈형 발코니 3층이상 ~ 20층이하 설치

수정번호 REV. NO.	일 자 DATE	내 용 DESCRIPTION	승 인 CHKD
△			
△			
△			
△			

설계 DESIGNED BY

검토 CHECKED BY
최 진 규

심사 SUMMITED BY
정 호 혁

승인 APPROVED BY
이 승 준

일자 DATE
2019.08

도면명 DRAWING TITLE
109동
18층 평면도

축 척 SCALE
A1: 1/100
A3: 1/200

도면번호 DRAWING NO.
A-416

일련번호 SHEET NO. △ REV. NO.

HAUD
㈜하우드엔지니어링
종합건축사사무소
Architects, Planners & Engineers
TEL. 02 2140 4400, SEOUL, KOREA

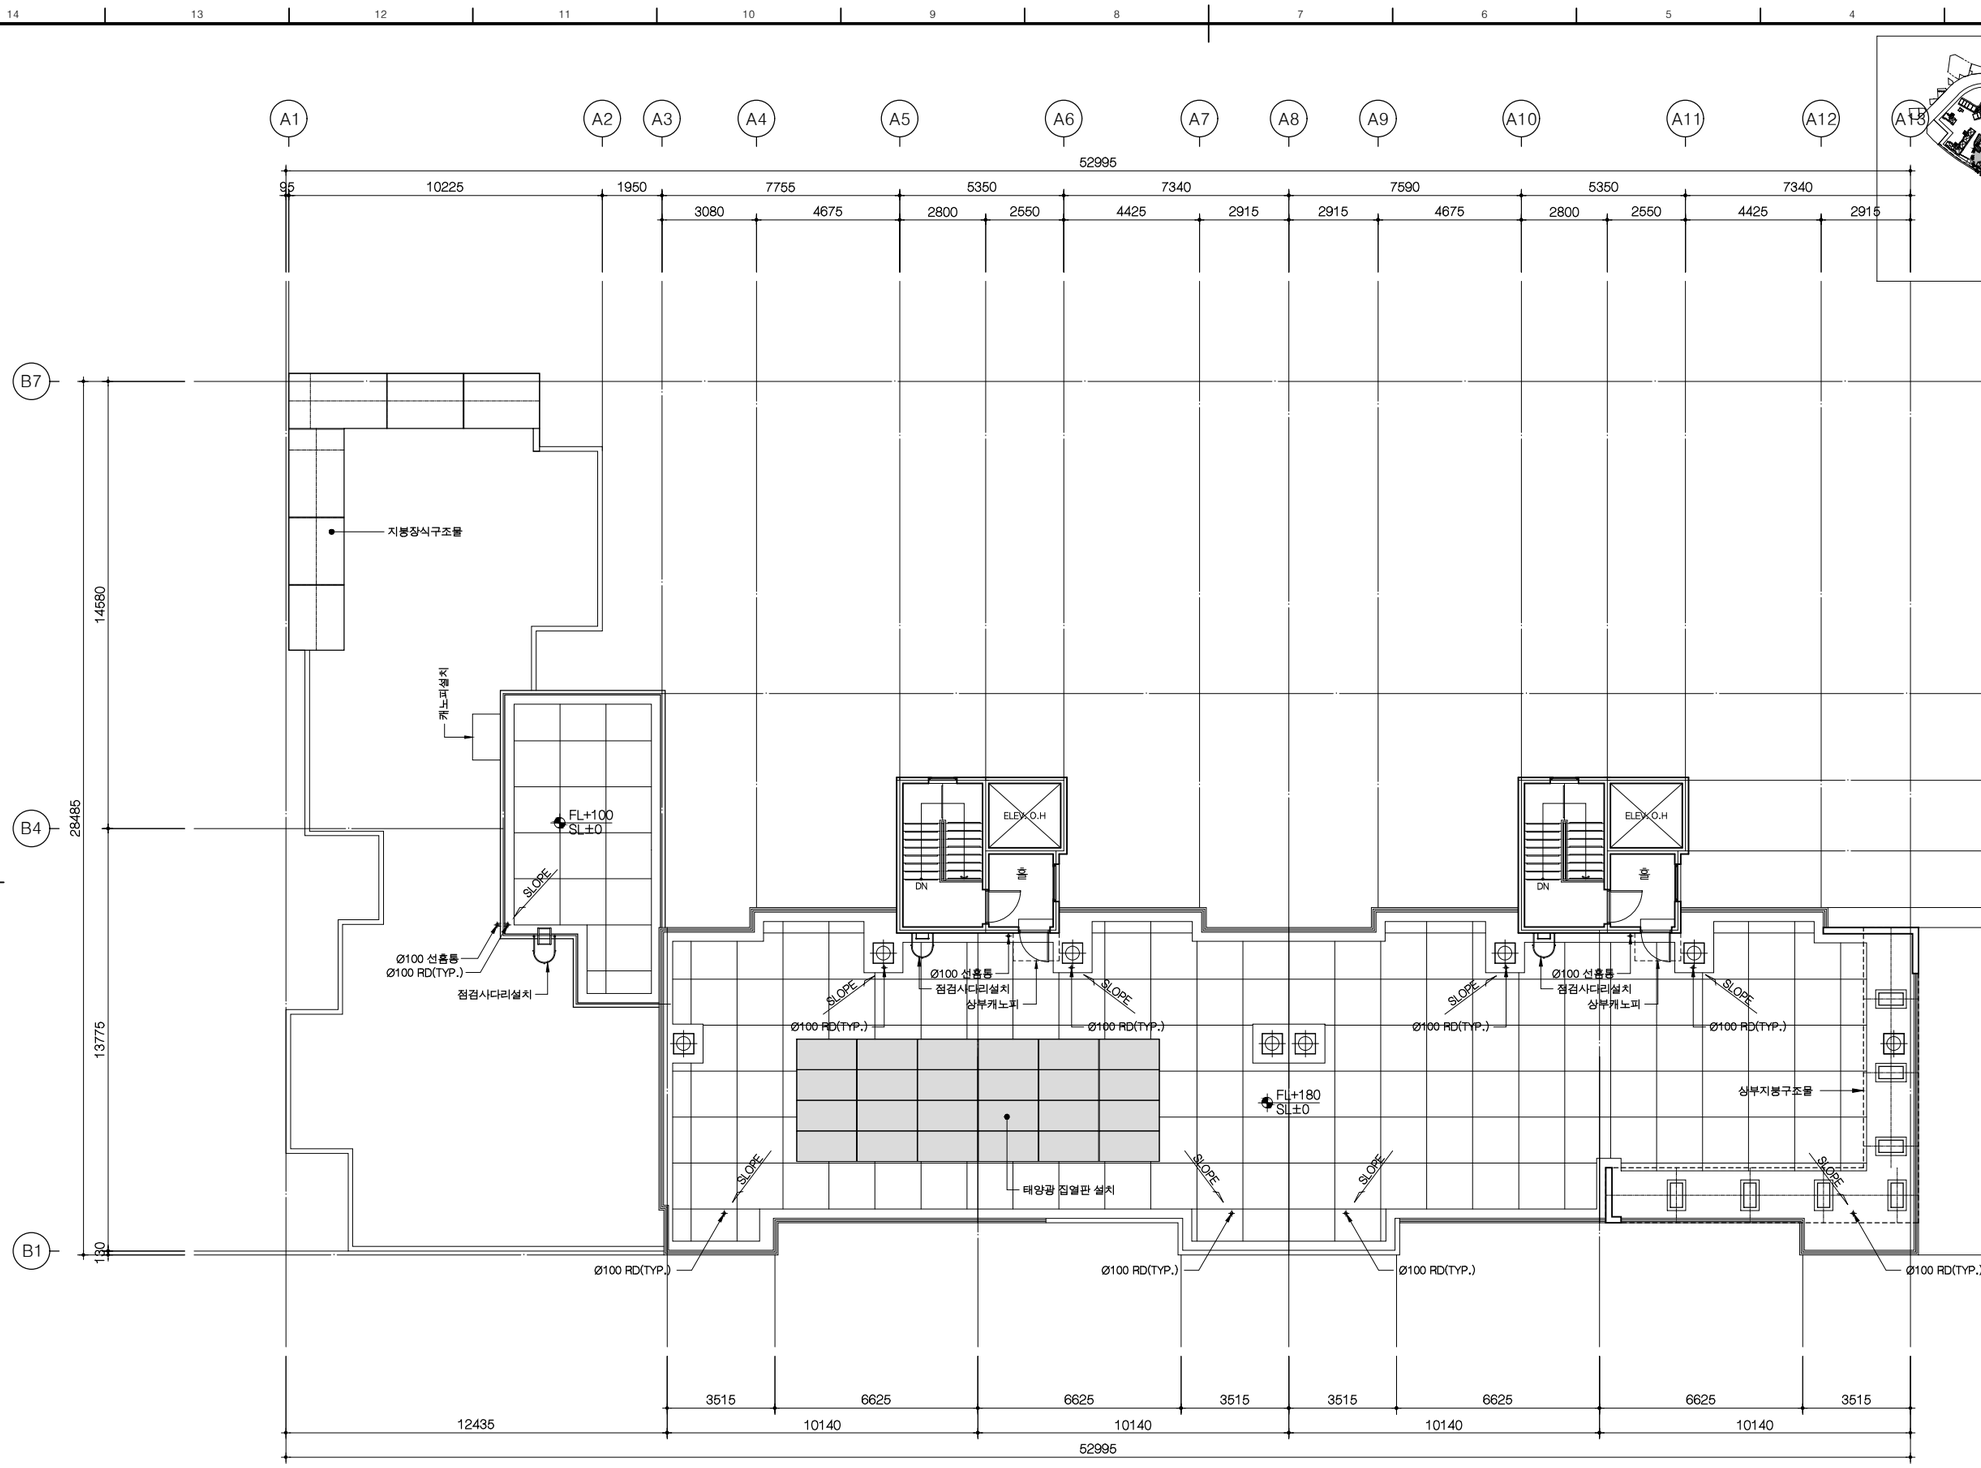

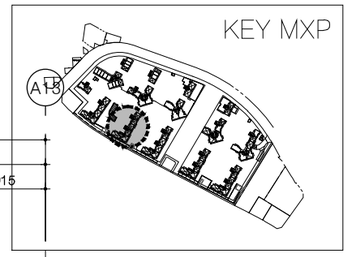

1
A

109동 지붕 평면도

축척 = 1/100

사업번호 PROJECT NO.

사업명 PROJECT TITLE

수색4재정비촉진구역
주택재개발 정비사업

KEY PLAN

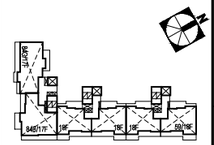

NOTE

1. 지붕바닥
   ① EXP. JOINT: 3000 X 3000
2. 본 평면도는 발코니확장전을 기준으로 작성됨
3. 재료마감은 실내,외 재료마감표 참조
4. 지붕 난간형태/설치위치는 안전성과 입면을 고려하여 실시공시 변경될 수 있음
5. 지붕재료 및 형태,구조는 실시공시 변경될수 있음
6. 지붕(옥탑지붕)의 배수드레인,청소용고리, 베기탑,점검사다리(점검구) 등의 설치위치/개소는 실시공시 변경될 수 있음
7. 옥상 상부구조물은 PC구조물 임.
8. 정화조 배기는 기계도서 참조

수정번호 REV. NO.	일 자 DATE	내 용 DESCRIPTION	승 인 CHKD
△			
△			
△			
△			

설계 DESIGNED BY

검토 CHECKED BY
최 진 규

심사 SUMMITED BY
정 호 혁

승인 APPROVED BY
이 승 준

일자 DATE
2019.08

도면명 DRAWING TITLE
109동
지붕 평면도

축 척 SCALE
A1: 1/100
A3: 1/200

도면번호 DRAWING NO.
A-417

일련번호 SHEET NO.

△ REV. NO.

HAUD
㈜하우드엔지니어링
종합건축사사무소
Architects, Planners & Engineers
TEL. 02 2140 4400, SEOUL, KOREA

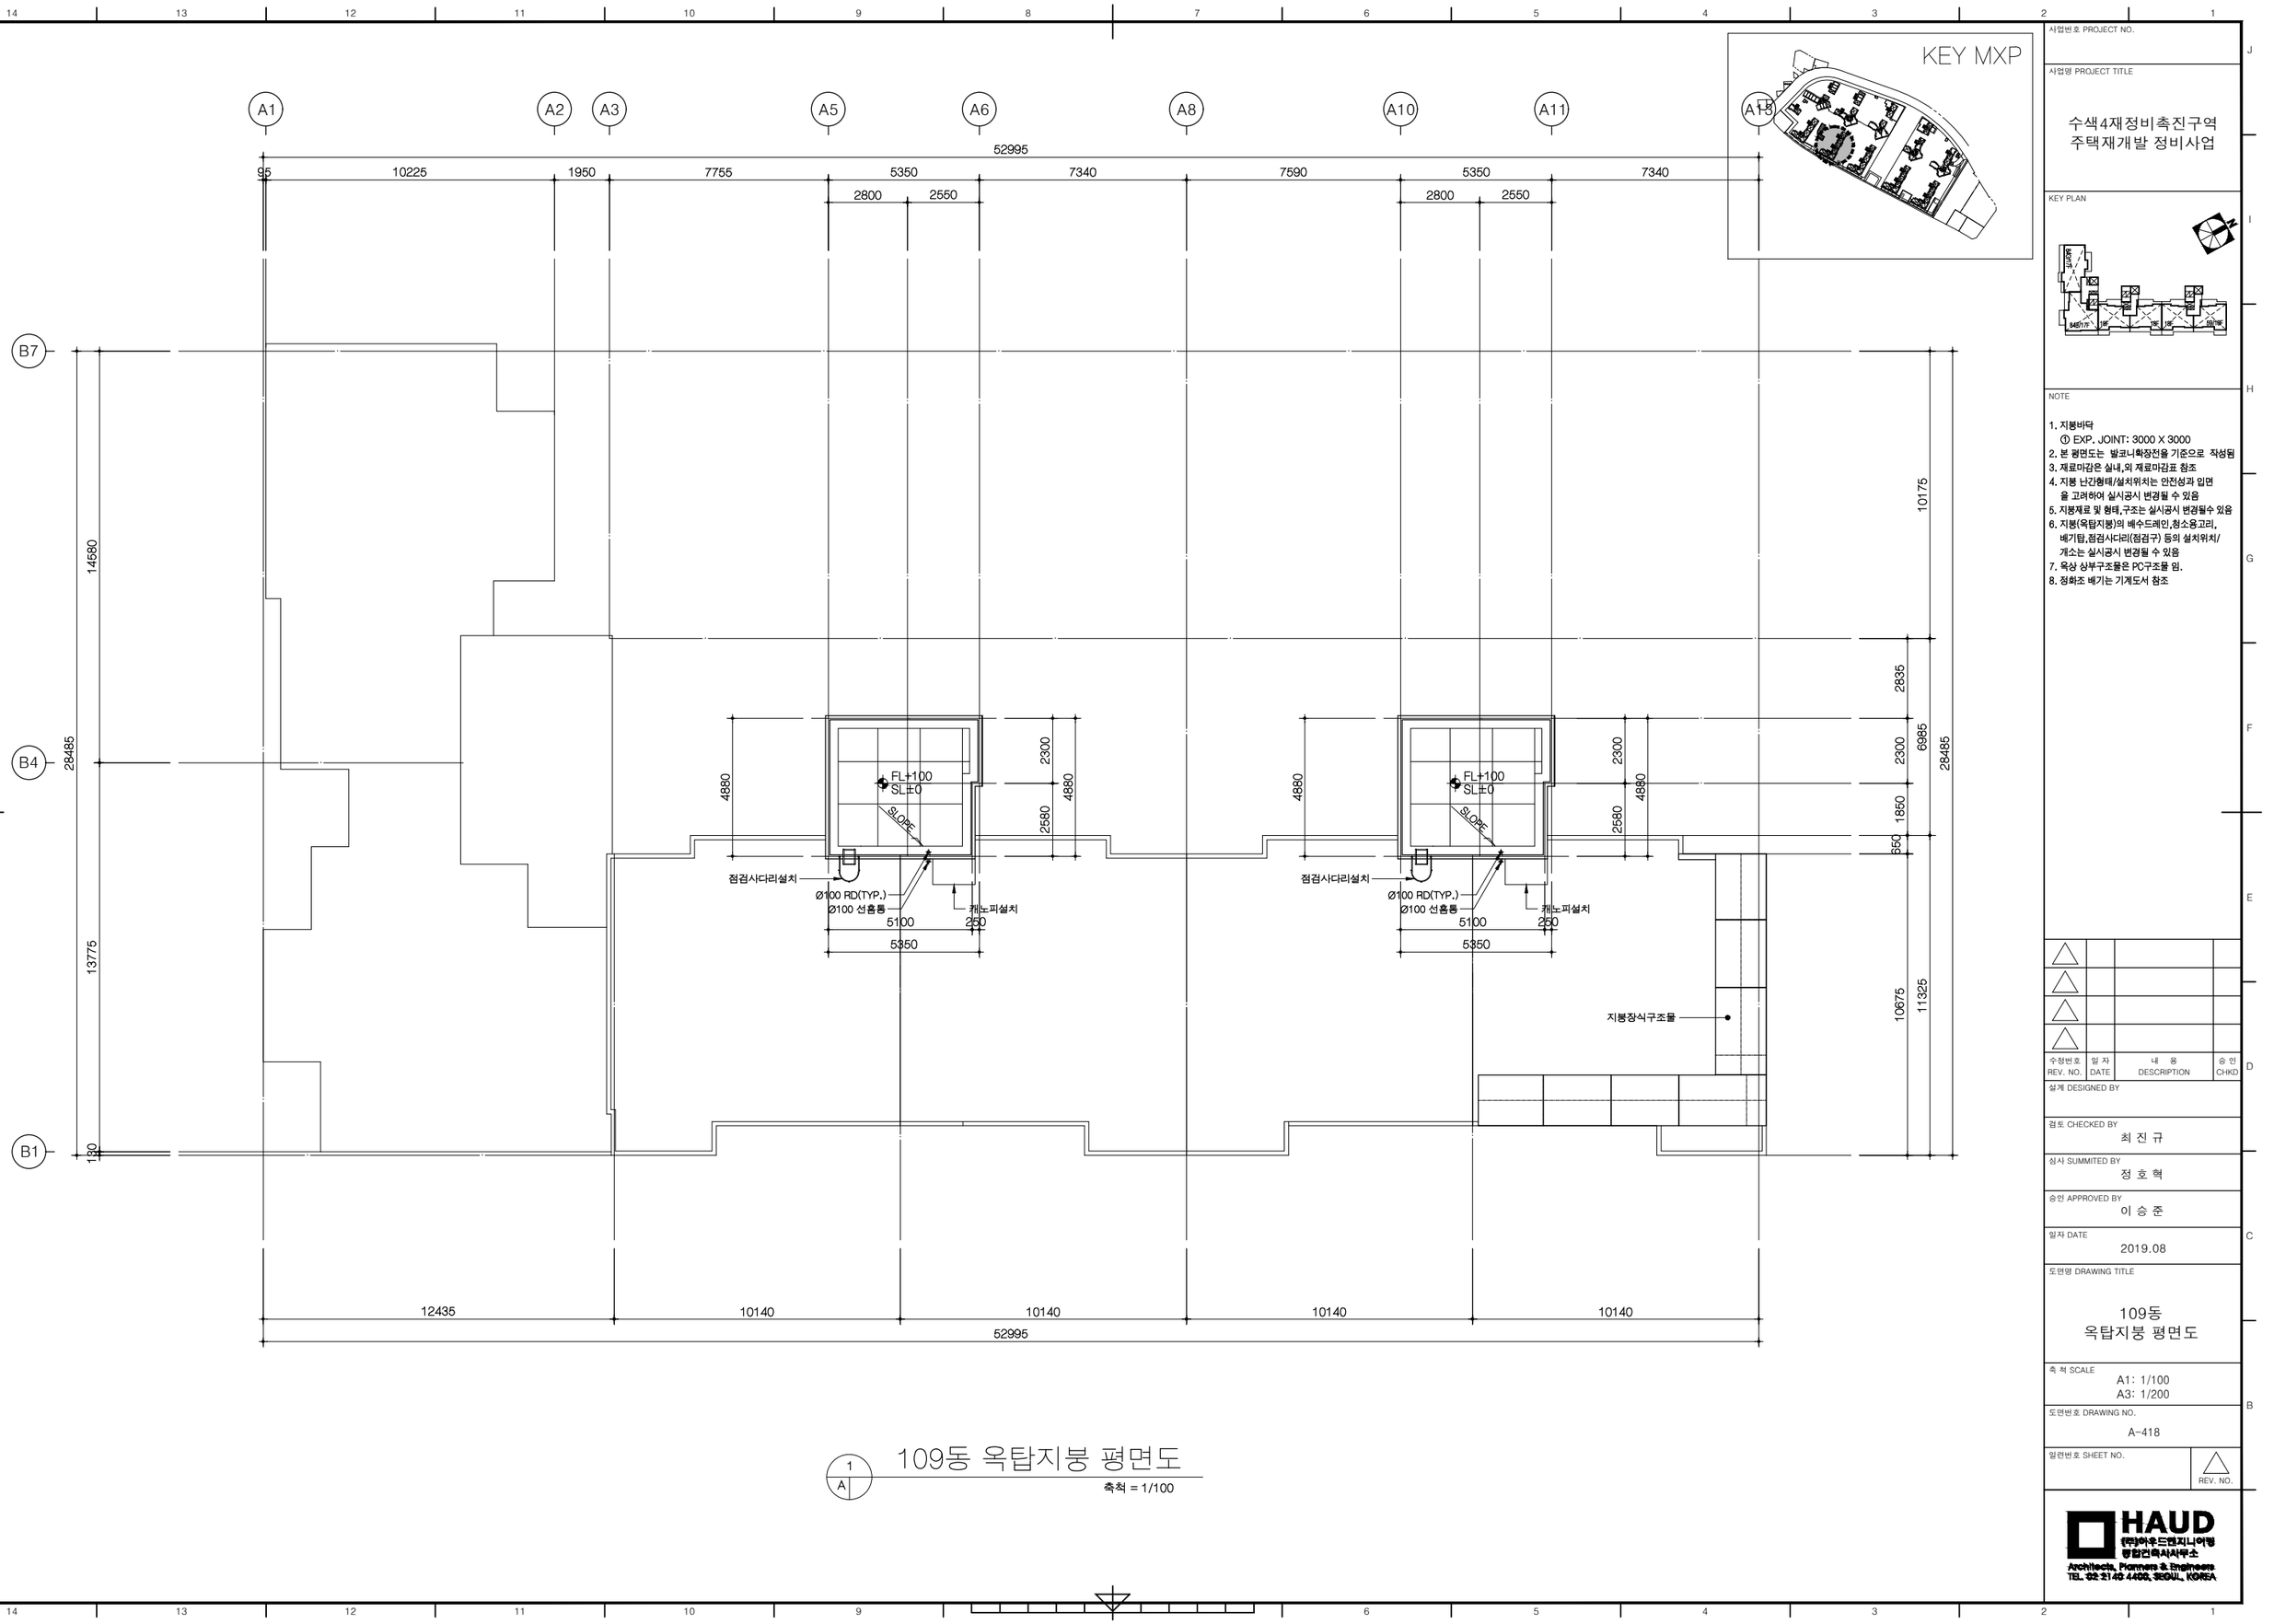

KEY MXP

1
A

109동 옥탑지붕 평면도

축척 = 1/100

사업번호 PROJECT NO.

사업명 PROJECT TITLE

수색4재정비촉진구역
주택재개발 정비사업

KEY PLAN

NOTE

1. 지붕바닥
   ① EXP. JOINT: 3000 X 3000
2. 본 평면도는 발코니확장전을 기준으로 작성됨
3. 재료마감은 실내,외 재료마감표 참조
4. 지붕 난간형태/설치위치는 안전성과 입면을 고려하여 실시공시 변경될 수 있음
5. 지붕재료 및 형태,구조는 실시공시 변경될수 있음
6. 지붕(옥탑지붕)의 배수드레인,청소용고리, 베기탑,점검사다리(점검구) 등의 설치위치/개소는 실시공시 변경될 수 있음
7. 옥상 상부구조물은 PC구조물 임.
8. 정화조 배기는 기계도서 참조

수정번호 REV. NO.	일 자 DATE	내 용 DESCRIPTION	승 인 CHKD

설계 DESIGNED BY

검토 CHECKED BY
최 진 규

심사 SUMMITED BY
정 호 혁

승인 APPROVED BY
이 승 준

일자 DATE
2019.08

도면명 DRAWING TITLE
109동
옥탑지붕 평면도

축 척 SCALE
A1: 1/100
A3: 1/200

도면번호 DRAWING NO.
A-418

얼럿번호 SHEET NO.

REV. NO.

HAUD
(주)하우드엔지니어링
종합건축사사무소
Architects, Planners & Engineers
TEL. 02 2140 4400, SEOUL, KOREA

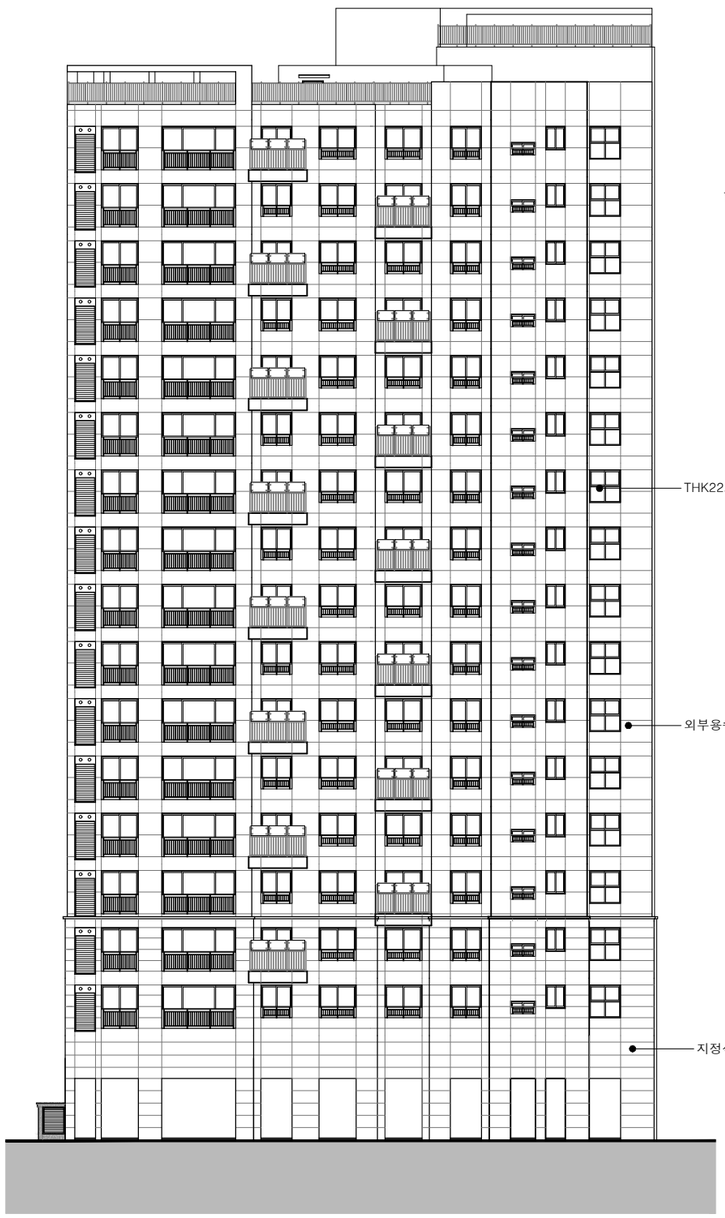

1 A 109동 정면도

축척 = 1/150

2 A 109동 우측면도

축척 = 1/150

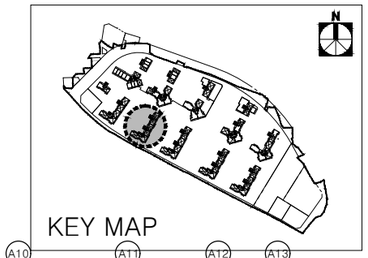

사업번호 PROJECT NO.

사업명 PROJECT TITLE

수색4재정비촉진구역
주택재개발 정비사업

KEY PLAN

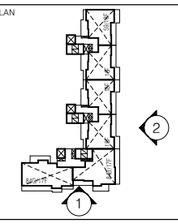

NOTE

1. 1층 바닥 LEVEL
   1SL±0 = 1FL±0 = GL±0 = EL+24.20
2. 지붕 난간의 형태 및 설치위치는 안전성과 입면디자인을 고려하여 변경가능함.
3. 지붕의 재료, 형태, 구조는 실시공시 변경될 수 있음.
4. 지붕 및 옥탑구조물의 형태와 구조는 실시공시 변경될 수 있음.
5. 외벽 및 측벽 문양은 실시공시 변경될 수 있음
6. 입면의 줄눈 및 마감선은 실시공시 변경될 수 있음.
7. 저층부 석재마감 및 입면 마감 색상, 재료에 대한 모든 기준은 특화도면을 우선 적용함.

수정번호 REV. NO.	일 자 DATE	내 용 DESCRIPTION	승 인 CHKD
△			
△			
△			
△			

설계 DESIGNED BY

검토 CHECKED BY
최 진 규

심사 SUMMITED BY
정 호 혁

승인 APPROVED BY
이 승 준

일자 DATE
2019.08

도면명 DRAWING TITLE
109동 정면도,우측면도

축 척 SCALE
A1: 1/150
A3: 1/300

도면번호 DRAWING NO.
A-419

일련번호 SHEET NO.

△ REV. NO.

HAUD
㈜하우드엔지니어링
종합건축사사무소
Architects, Planners & Engineers
TEL. 02 2140 4400, SEOUL, KOREA

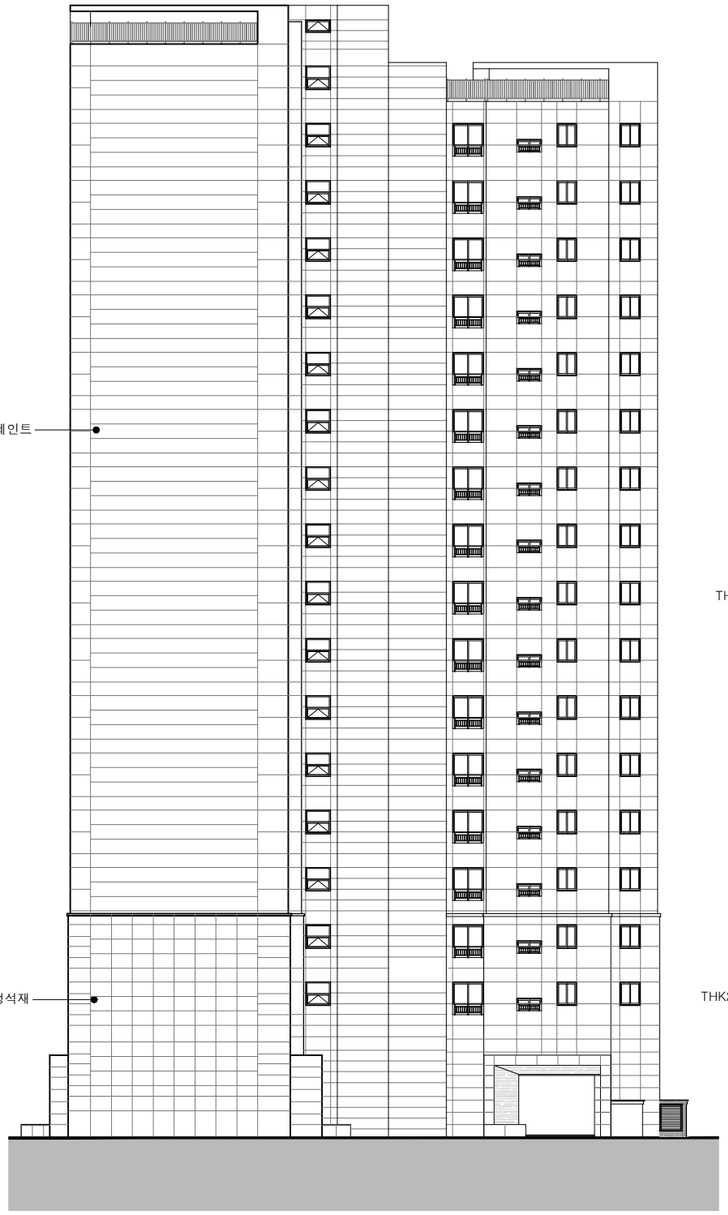

1 A 109동 배면도

축척 = 1/150

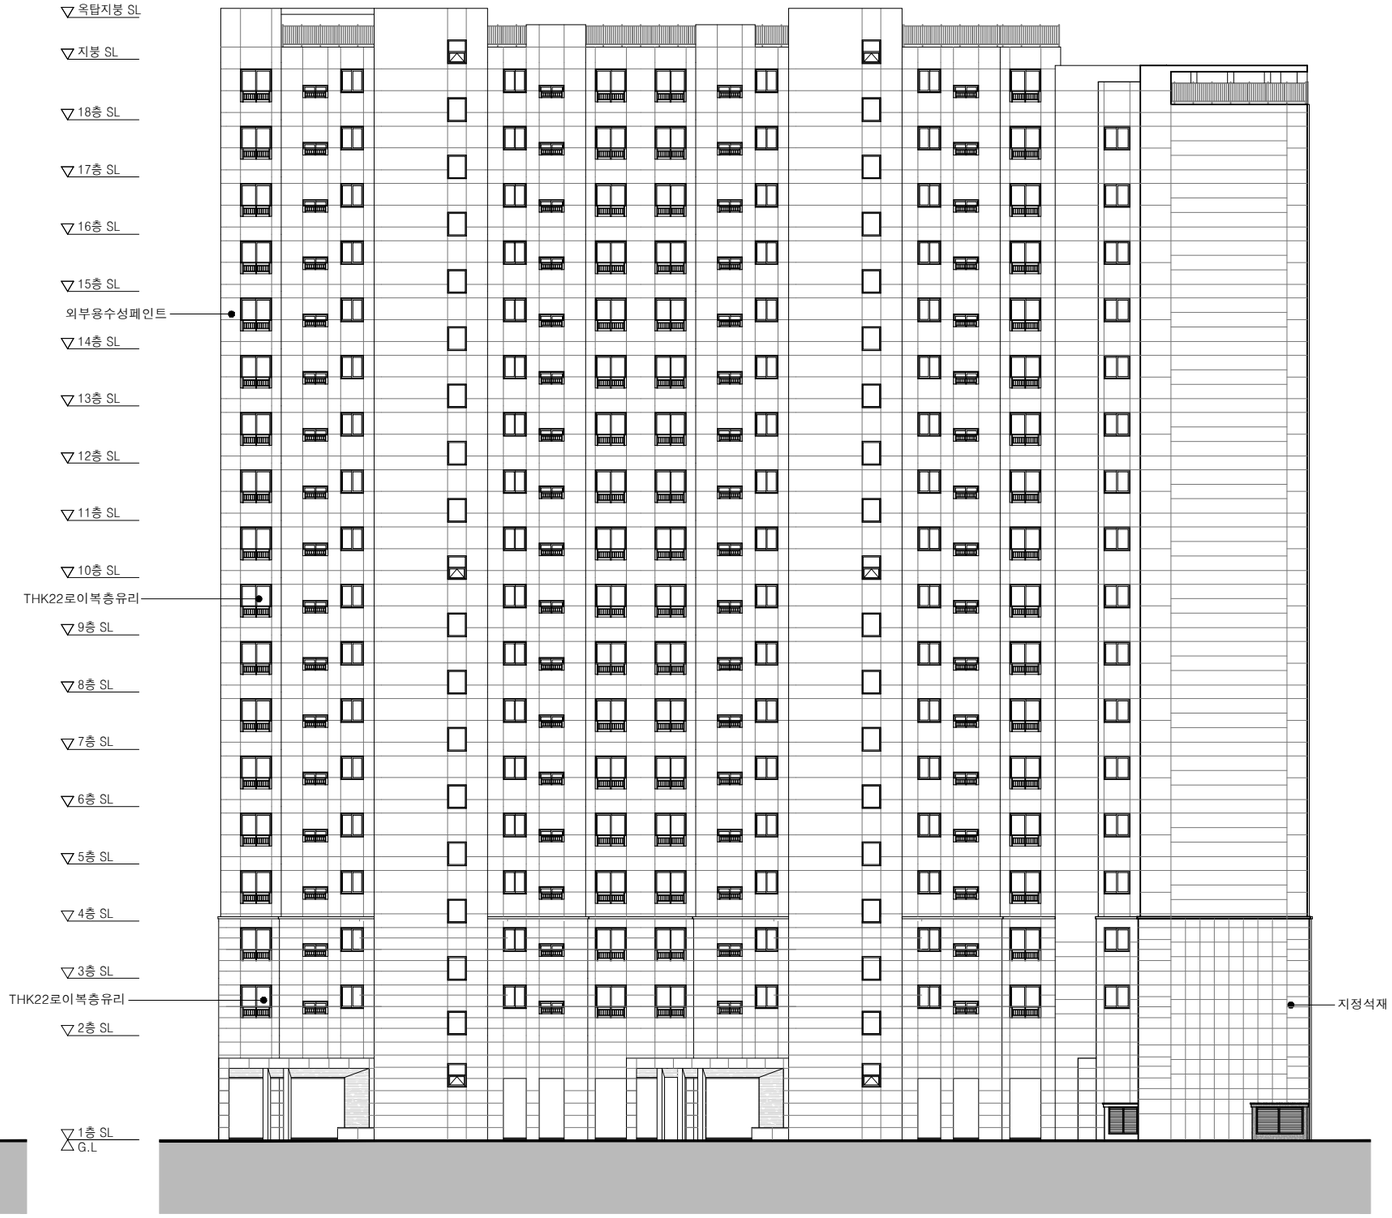

2 A 109동 좌측면도

축척 = 1/150

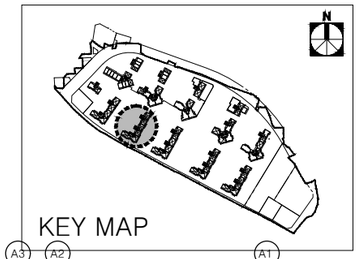

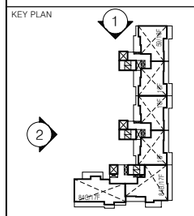

NOTE

1. 1층 바닥 LEVEL
   1SL±0 = 1FL±0 = GL±0 = EL+24.20
2. 지붕 난간의 형태 및 설치위치는 안전성과 입면디자인을 고려하여 변경가능함.
3. 지붕의 재료, 형태, 구조는 실시공시 변경될 수 있음.
4. 지붕 및 옥탑구조물의 형태와 구조는 실시공시 변경될 수 있음.
5. 외벽 및 측벽 문양은 실시공시 변경될 수 있음
6. 입면의 줄눈 및 마감선은 실시공시 변경될 수 있음.
7. 저층부 석재마감 및 입면 마감 색상, 재료에 대한 모든 기준은 특화도면을 우선 적용함.

수정번호 REV. NO.	일 자 DATE	내 용 DESCRIPTION	승 인 CHKD
△			
△			
△			
△			

사업번호 PROJECT NO.

사업명 PROJECT TITLE

수색4재정비촉진구역
주택재개발 정비사업

설계 DESIGNED BY

검토 CHECKED BY
최 진 규

심사 SUMMITED BY
정 호 혁

승인 APPROVED BY
이 승 준

일자 DATE
2019.08

도면명 DRAWING TITLE
109동 배면도,좌측면도

축 척 SCALE
A1: 1/150
A3: 1/300

도면번호 DRAWING NO.
A-420

일련번호 SHEET NO. △ REV. NO.

HAUD
㈜하우드건지니어링
종합건축사사무소
Architects, Planners & Engineers
TEL. 02-2149 4400, SEOUL, KOREA

109동 종단면도

1 / A

축척 = 1/150

109동 횡단면도

2 / A

축척 = 1/150

사업번호 PROJECT NO.

사업명 PROJECT TITLE

수색4재정비촉진구역
주택재개발 정비사업

KEY PLAN

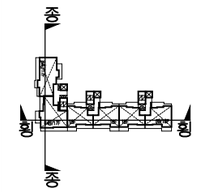

NOTE

수정번호 REV. NO.	일 자 DATE	내 용 DESCRIPTION	승 인 CHKD

설계 DESIGNED BY

검토 CHECKED BY
최 진 규

심사 SUMMITED BY
정 호 혁

승인 APPROVED BY
이 승 준

일자 DATE
2019.08

도면명 DRAWING TITLE
109동 종,횡단면도

축 척 SCALE
A1: 1/150
A3: 1/300

도면번호 DRAWING NO.
A-421

일련번호 SHEET NO.

REV. NO.

HAUD
(주)하우드엔지니어링
종합건축사사무소
Architects, Planners & Engineers
TEL. 02 2140 4400, SEOUL, KOREA

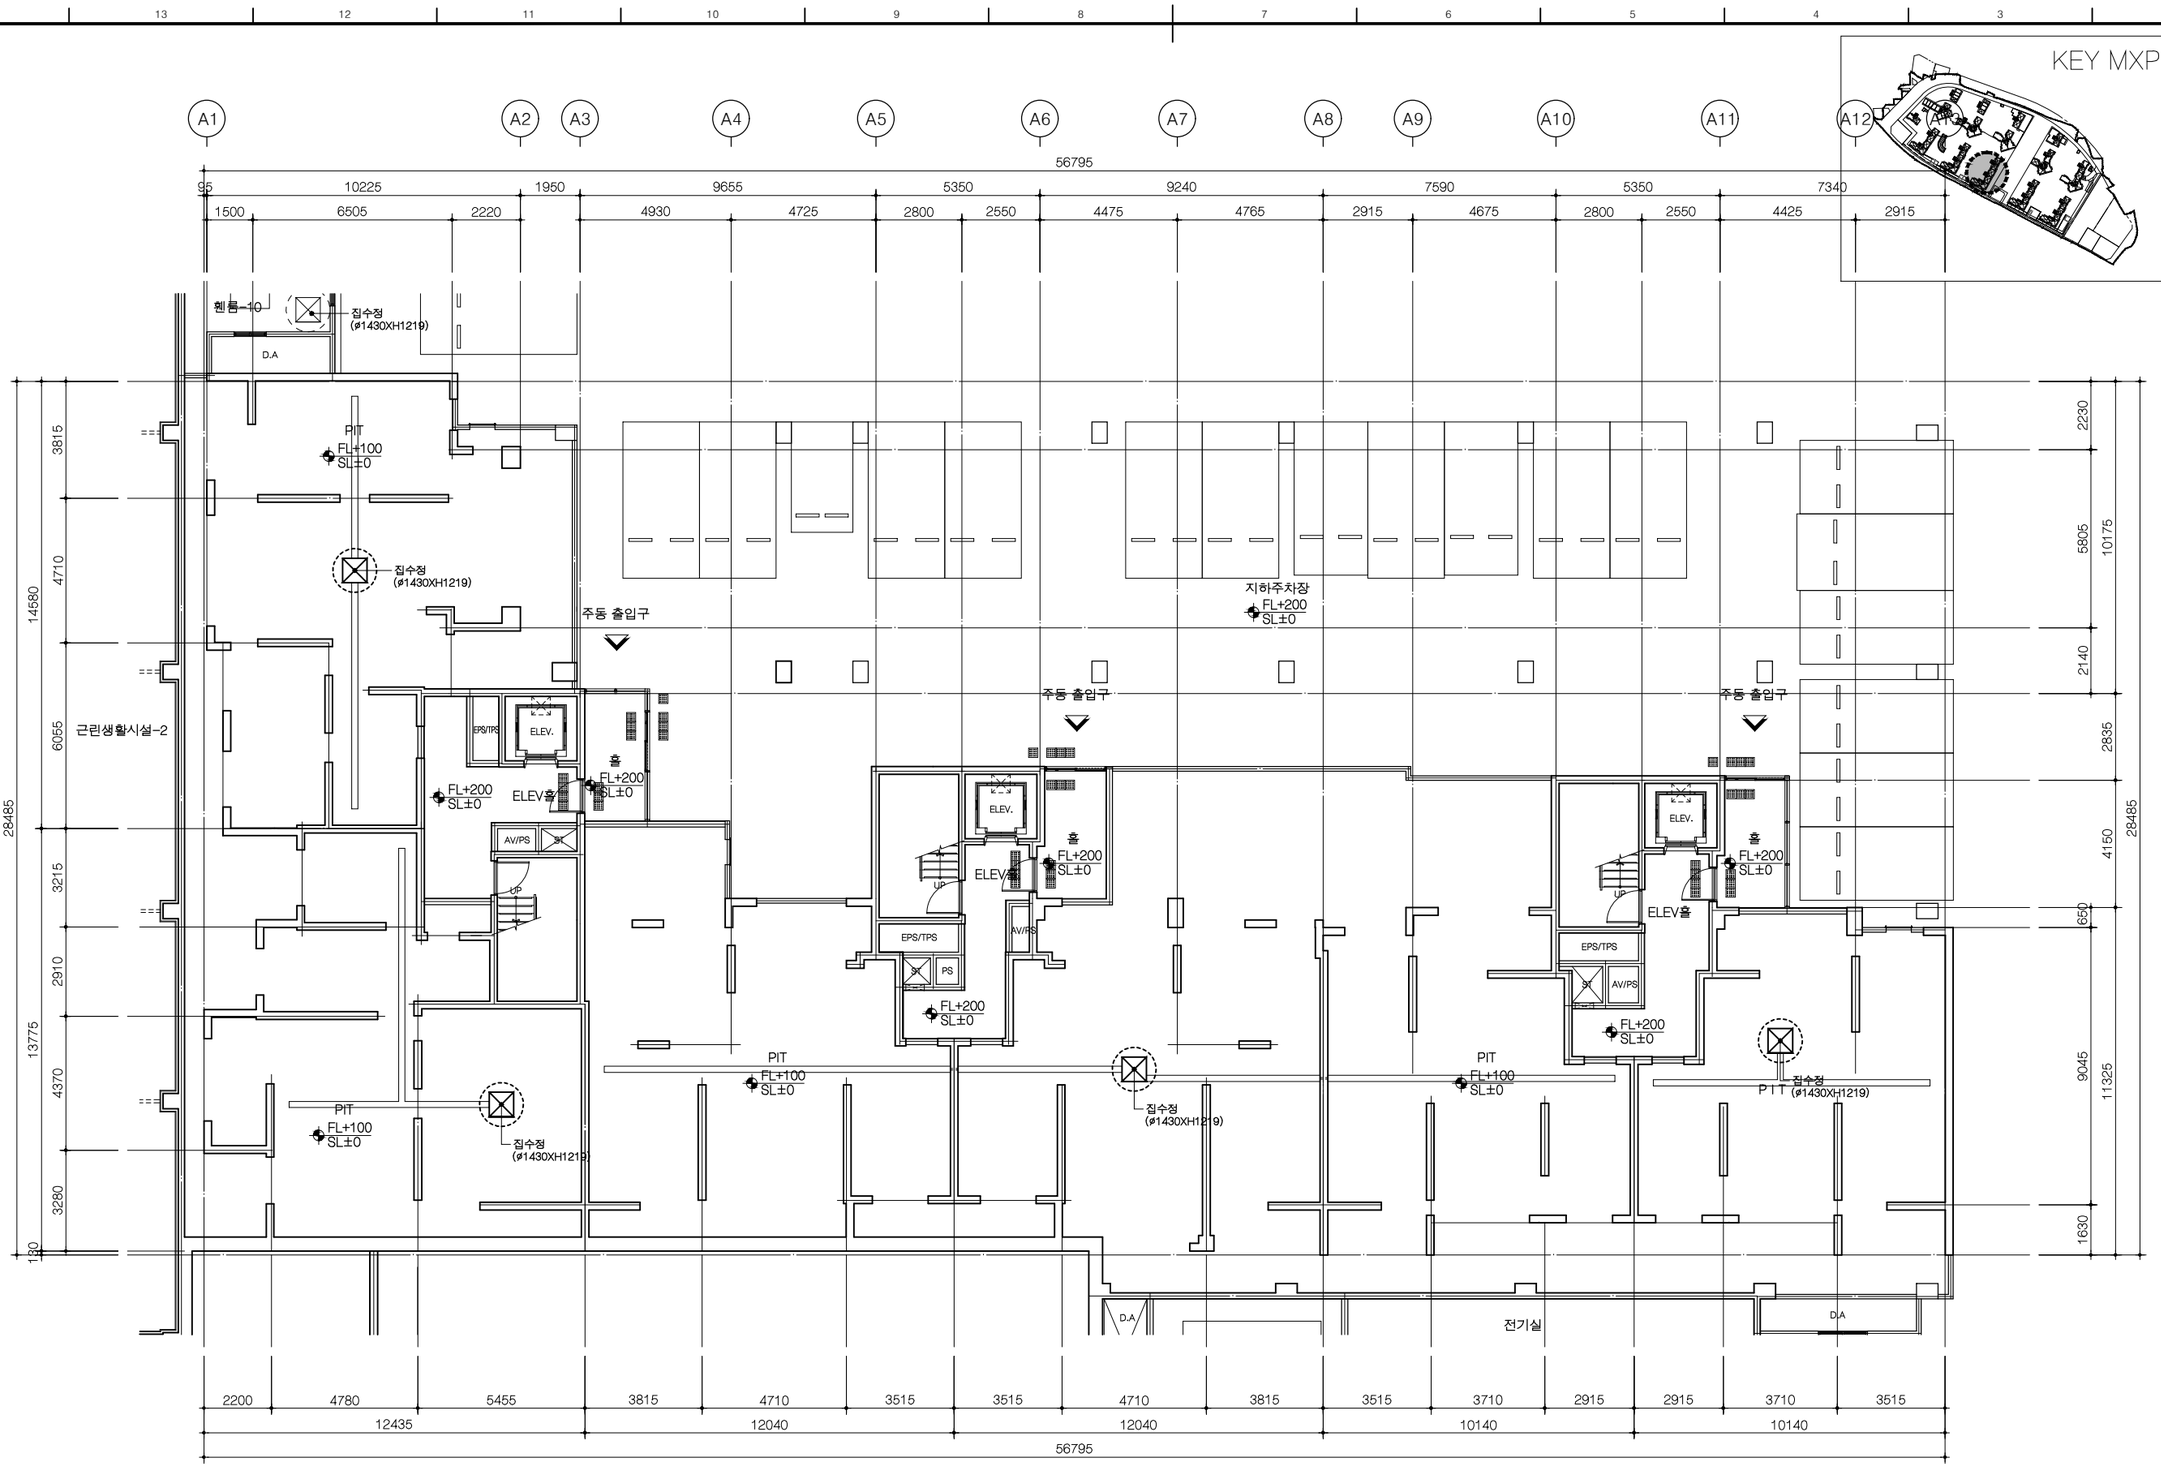

KEY MXP

1
A

110동 지하3층 평면도

축척 = 1/100

사업번호 PROJECT NO.

사업명 PROJECT TITLE

수색4재정비촉진구역
주택재개발 정비사업

KEY PLAN

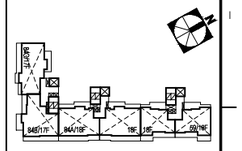

NOTE

1. 지하층 무근 콘크리트는 실시공시 THK80~120 범위로 변동이 있을수 있음.(SLOPE)
2. ELEV홀에 면한부위는 1.0B 조적쌓기임.
3. 지하주차장의 블록쌓기 기준은 높이가 3.6m이하인 경우 4인치 보강블록쌓기가 기준임 (단, 5.4m이하는 6인치쌓기, 5.4m초과는 8인치쌓기가 기준임)
4. ELEV.PIT 집수정은 (600X600X600)임.
5. 주차장 내의 창호는 주차장 창호도 참조.
6. 주차장 집수정 및 영구배수 집수정의 크기 및 위치는 지하주차장 평면도를 참조 할 것.
   ☒ : 주차장 집수정
   ☒ : 영구배수 집수정

********** 지하3층 바닥LEVEL
B3SL±0 = B3FL±0 = EL+15.85

수정번호 REV. NO.	일 자 DATE	내 용 DESCRIPTION	승 인 CHKD
△			
△			
△			
△			

설계 DESIGNED BY

검토 CHECKED BY
최 진 규

심사 SUMMITED BY
정 호 혁

승인 APPROVED BY
이 승 준

일자 DATE
2019.08

도면명 DRAWING TITLE
110동
지하3층 평면도

축 척 SCALE
A1: 1/100
A3: 1/200

도면번호 DRAWING NO.
A-431

일련번호 SHEET NO. △ REV. NO.

HAUD
(주)하우드엔지니어링
종합건축사사무소
Architects, Planners & Engineers
TEL. 82 2 140 4400, SEOUL, KOREA

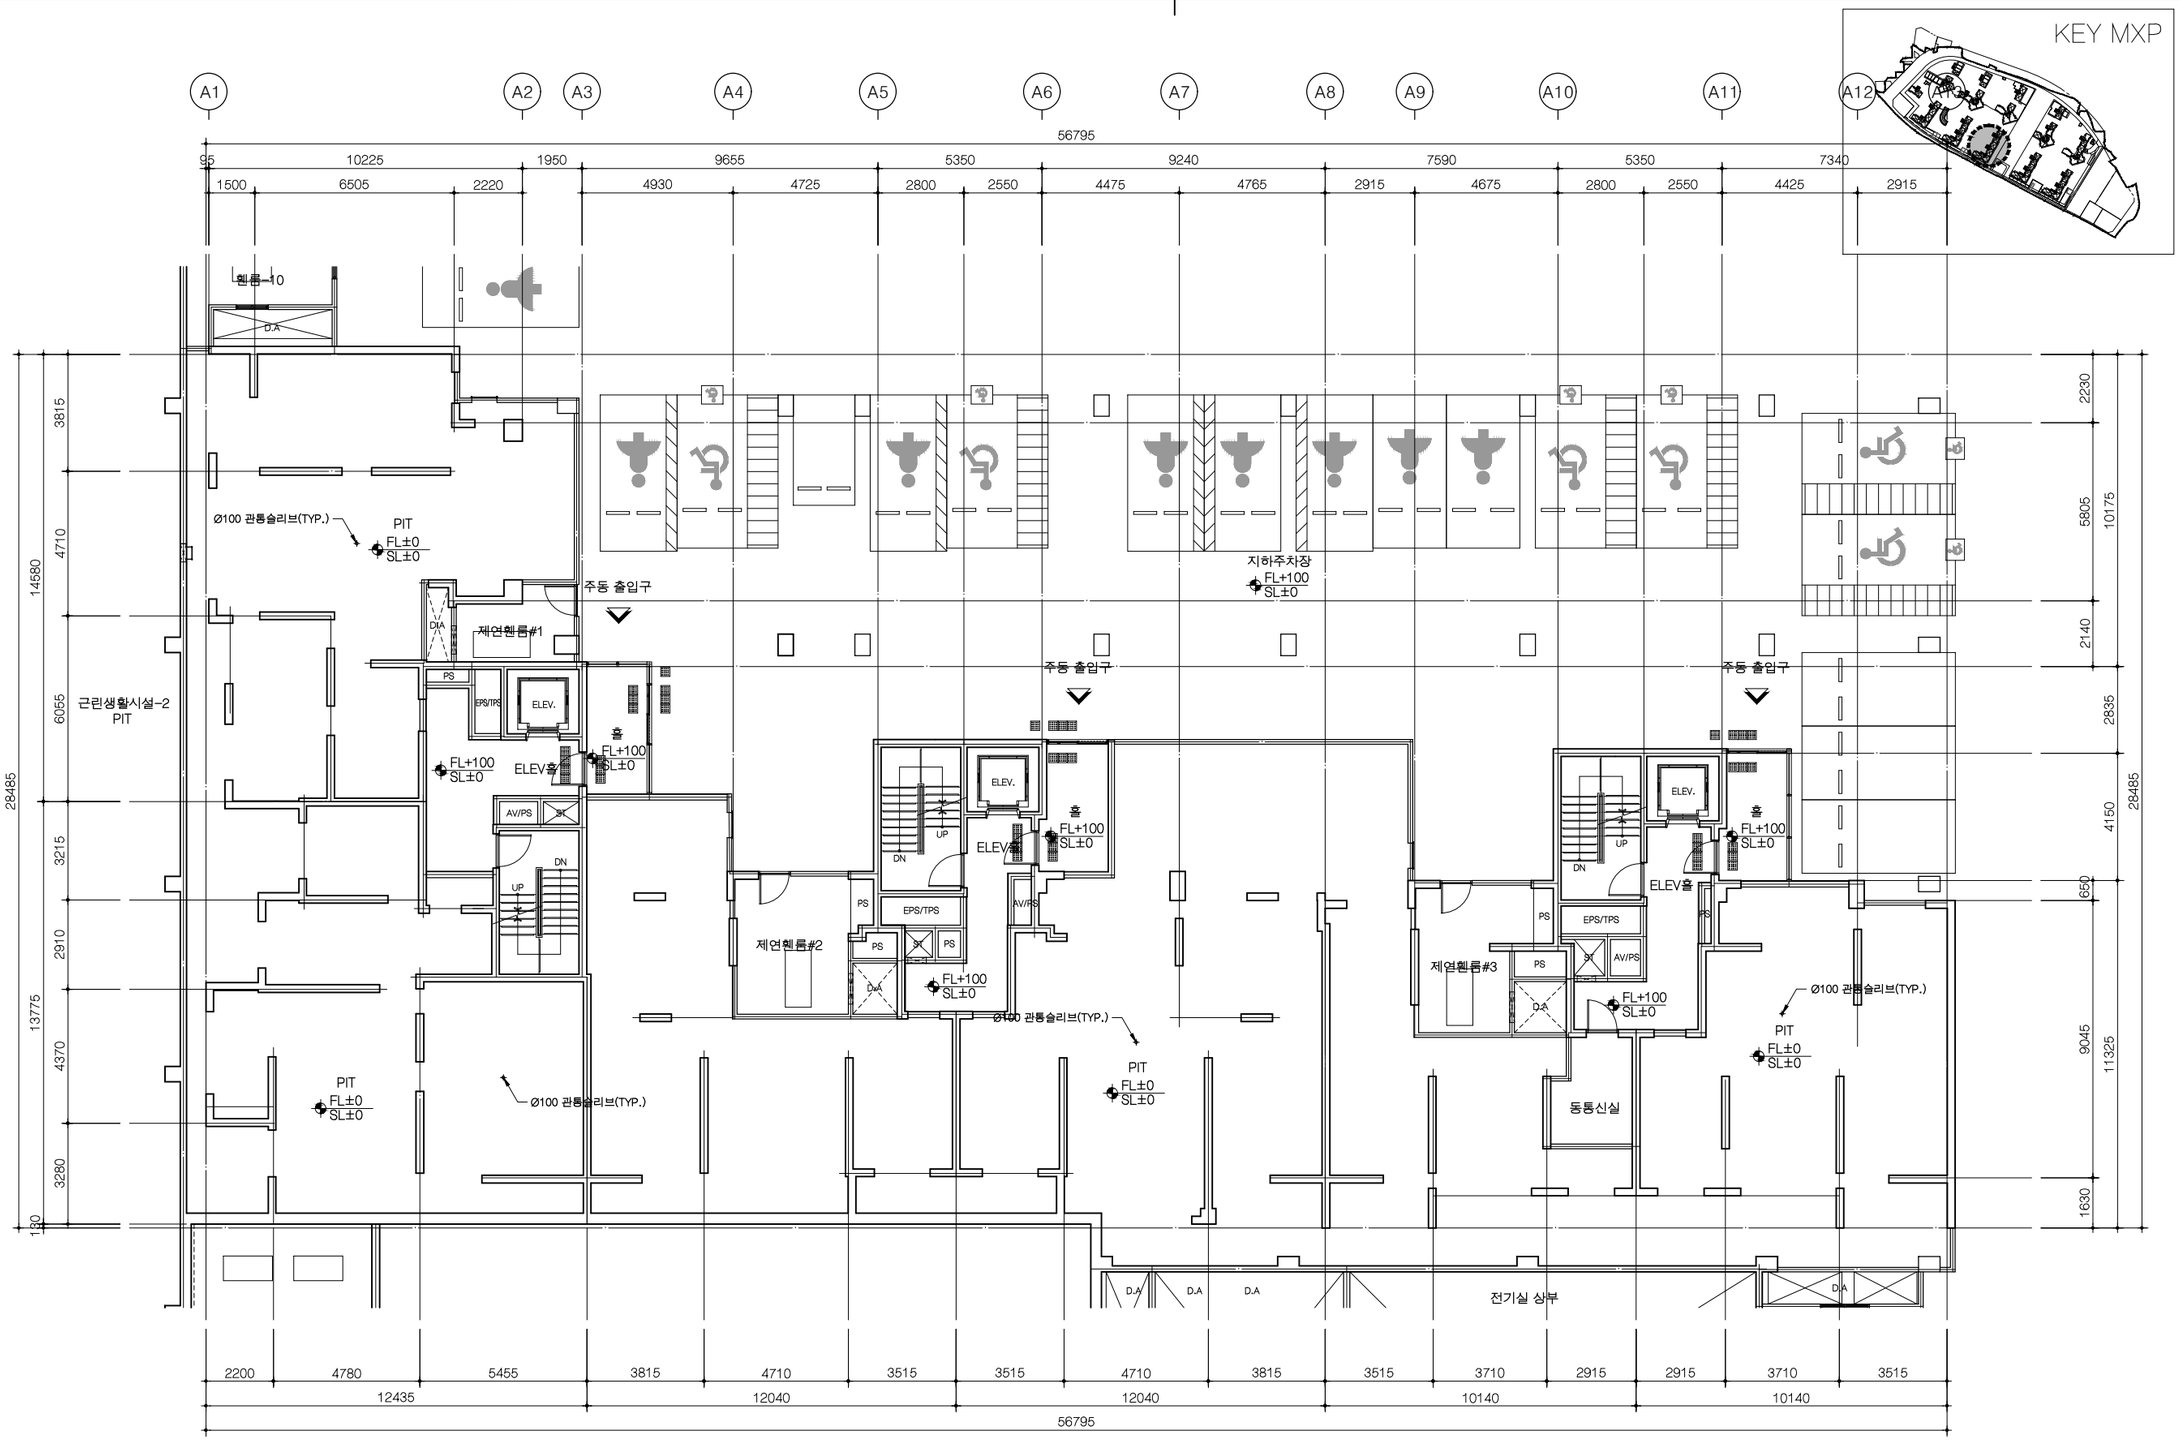

1 A 110동 지하2층 평면도

축척 = 1/100

KEY MXP

사업번호 PROJECT NO.

사업명 PROJECT TITLE

수색4재정비촉진구역
주택재개발 정비사업

KEY PLAN

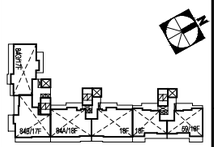

NOTE

1. 지하주차장의 ELEV홀에 면한부위는 1.0B 조적쌓기임.
2. 지하주차장의 블록쌓기 기준은 높이가 3.6m이하인 경우 4인치 보강블록쌓기가 기준임 (단, 5.4m이하는 6인치쌓기, 5.4m초과는 8인치쌓기가 기준임)
3. 주차장 내의 창호는 주차장 창호도 참조.

**** 지하2층 바닥LEVEL
D2SL±0 = D2FL±0 = EL+19.30

수정번호 REV. NO.	일 자 DATE	내 용 DESCRIPTION	승 인 CHKD
△			
△			
△			
△			

설계 DESIGNED BY

검토 CHECKED BY
최 진 규

심사 SUMMITED BY
정 호 혁

승인 APPROVED BY
이 승 준

일자 DATE
2019.08

도면명 DRAWING TITLE
110동
지하2층 평면도

축 척 SCALE
A1: 1/100
A3: 1/200

도면번호 DRAWING NO.
A-432

일련번호 SHEET NO. △ REV. NO.

HAUD
㈜하우드엔지니어링
종합건축사사무소
Architects, Planners & Engineers
TEL. 82 2 749 4400, SEOUL, KOREA

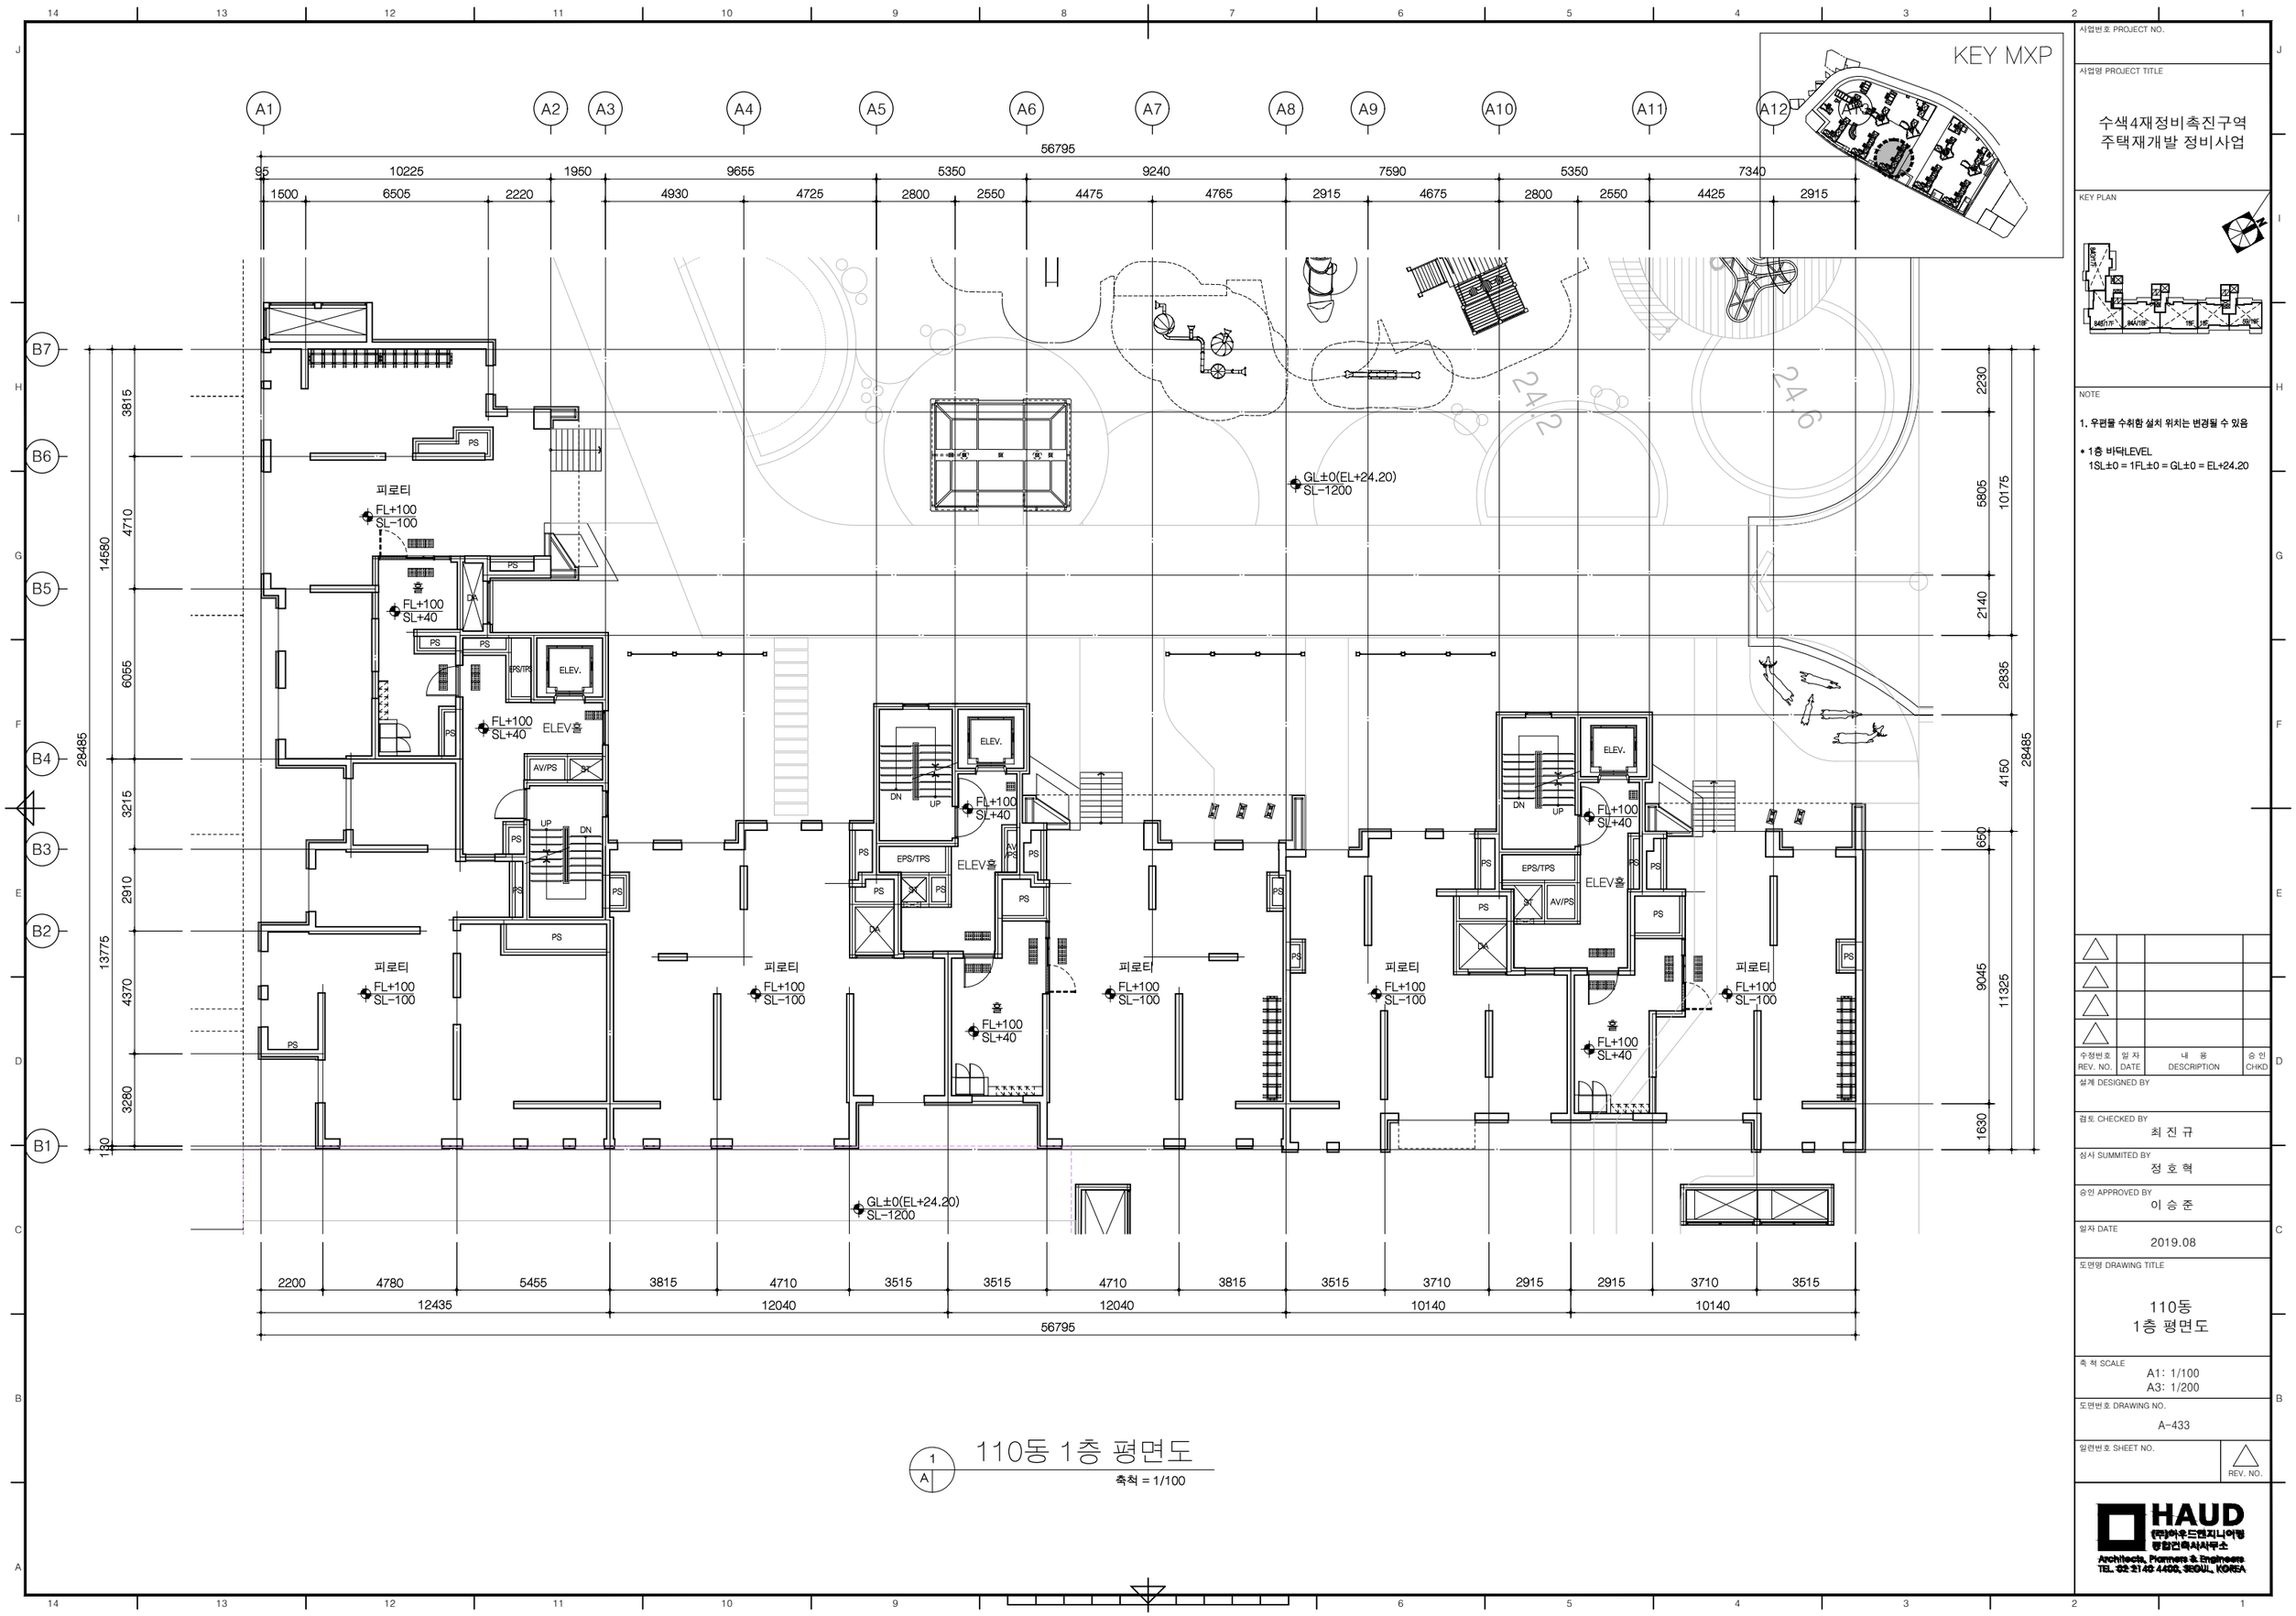

1 A 110동 1층 평면도

축척 = 1/100

사업번호 PROJECT NO.

사업명 PROJECT TITLE

수색4재정비촉진구역
주택재개발 정비사업

KEY PLAN

NOTE

1. 우려물 수취함 설치 위치는 변경될 수 있음

• 1층 바닥LEVEL
1SL±0 = 1FL±0 = GL±0 = EL+24.20

수정번호 REV. NO.	일 자 DATE	내 용 DESCRIPTION	승 인 CHKD

설계 DESIGNED BY

검토 CHECKED BY
최 진 규

심사 SUMMITED BY
정 호 혁

승인 APPROVED BY
이 승 준

일자 DATE
2019.08

도면명 DRAWING TITLE
110동
1층 평면도

축 척 SCALE
A1: 1/100
A3: 1/200

도면번호 DRAWING NO.
A-433

일련번호 SHEET NO.

REV. NO.

HAUD
㈜하우드엔지니어링
종합건축사사무소
Architects, Planners & Engineers
TEL. 02 2140 4400, SEOUL, KOREA

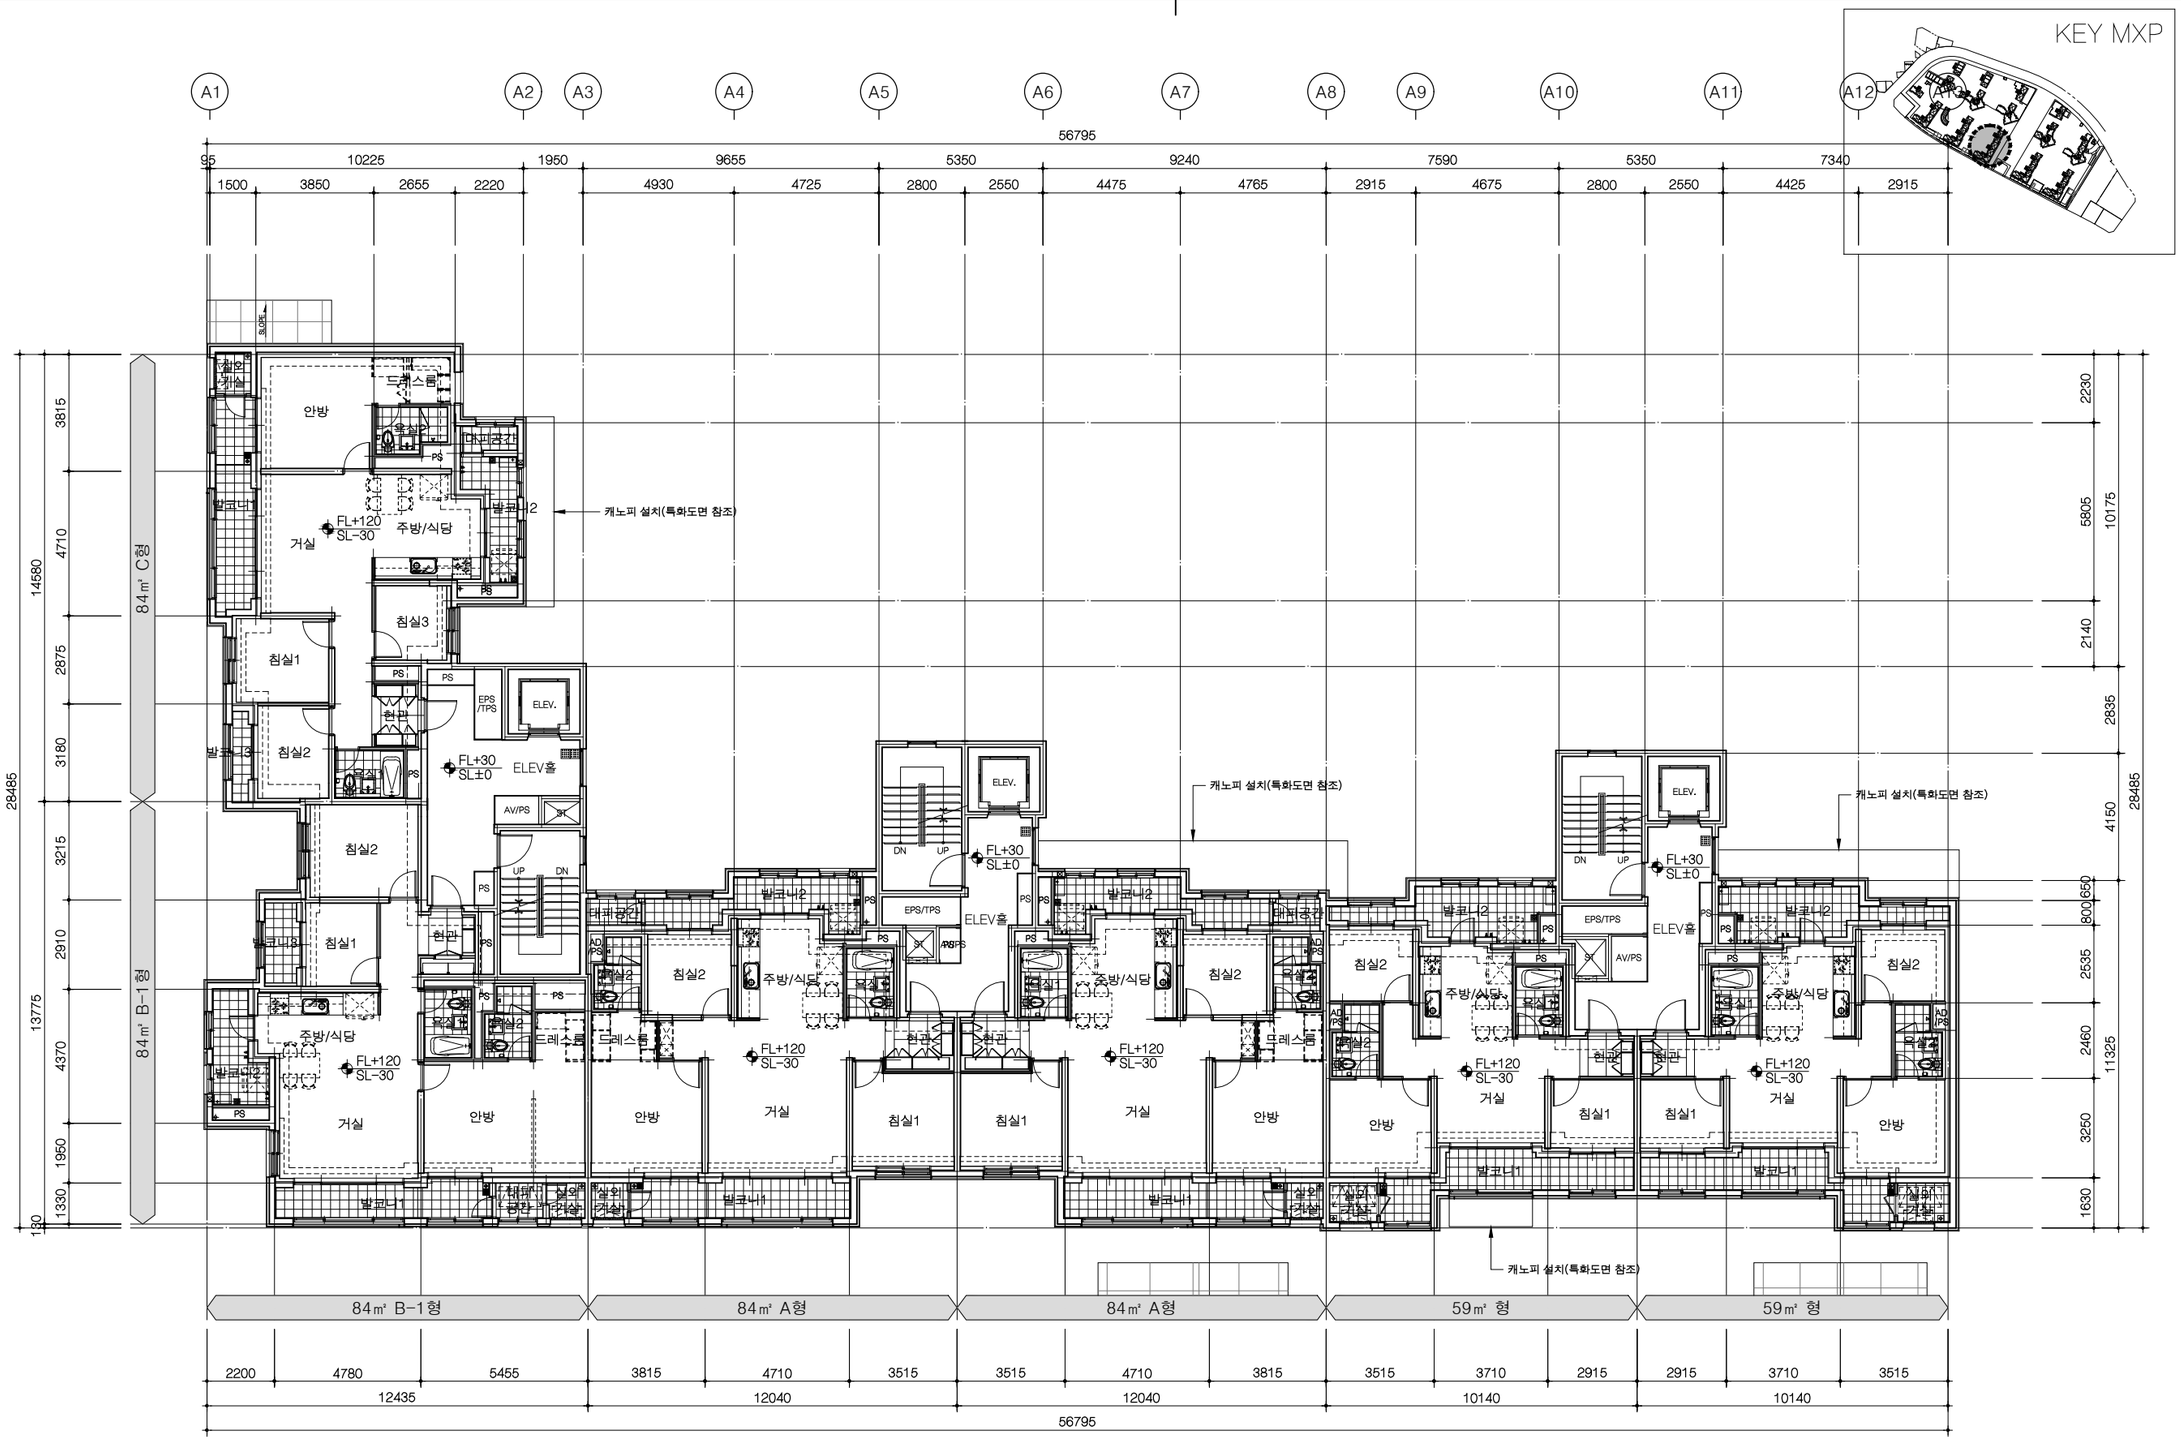

1 A 110동 2층 평면도

축척 = 1/100

KEY MXP

사업번호 PROJECT NO.

사업명 PROJECT TITLE

수색4재정비촉진구역
주택재개발 정비사업

KEY PLAN

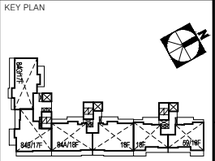

NOTE

1. 본 도면은 발코니 확장전를 기준으로 작성됨.
2. 지붕층 난간의 형태와 설치 위치는 안전성과 입면디자인을 고려하여 변경 가능함.
3. 지붕의 재료, 형태, 구조는 실시공 시 변경 될 수 있음.
4. 지붕 및 옥탑 구조물의 형태와 구조는 실시공 시 변경될 수 있음.
5. 옥상 출눈의 간격은 실시공 시 변경될 수 있음.
6. 옥상 출눈 틈에 실란트 시공되지 않음
7. 우편물 수취함 설치 위치는 변경될 수 있음
8. 오픈형 발코니 3층이상 ~ 20층이하 설치

2층 바닥LEVEL
2SL±0 = 2FL±0 = EL+29.30

수정번호 REV. NO.	일 자 DATE	내 용 DESCRIPTION	승 인 CHKD
△			
△			
△			
△			

설계 DESIGNED BY

검토 CHECKED BY
최 진 규

심사 SUMMITED BY
정 호 혁

승인 APPROVED BY
이 승 준

일자 DATE
2019.08

도면명 DRAWING TITLE
110동
2층 평면도

축 척 SCALE
A1: 1/100
A3: 1/200

도면번호 DRAWING NO.
A-434

일련번호 SHEET NO. △ REV. NO.

HAUD
㈜하우드엔지니어링
종합건축사사무소
Architects, Planners & Engineers
TEL. 02 2140 4400, SEOUL, KOREA

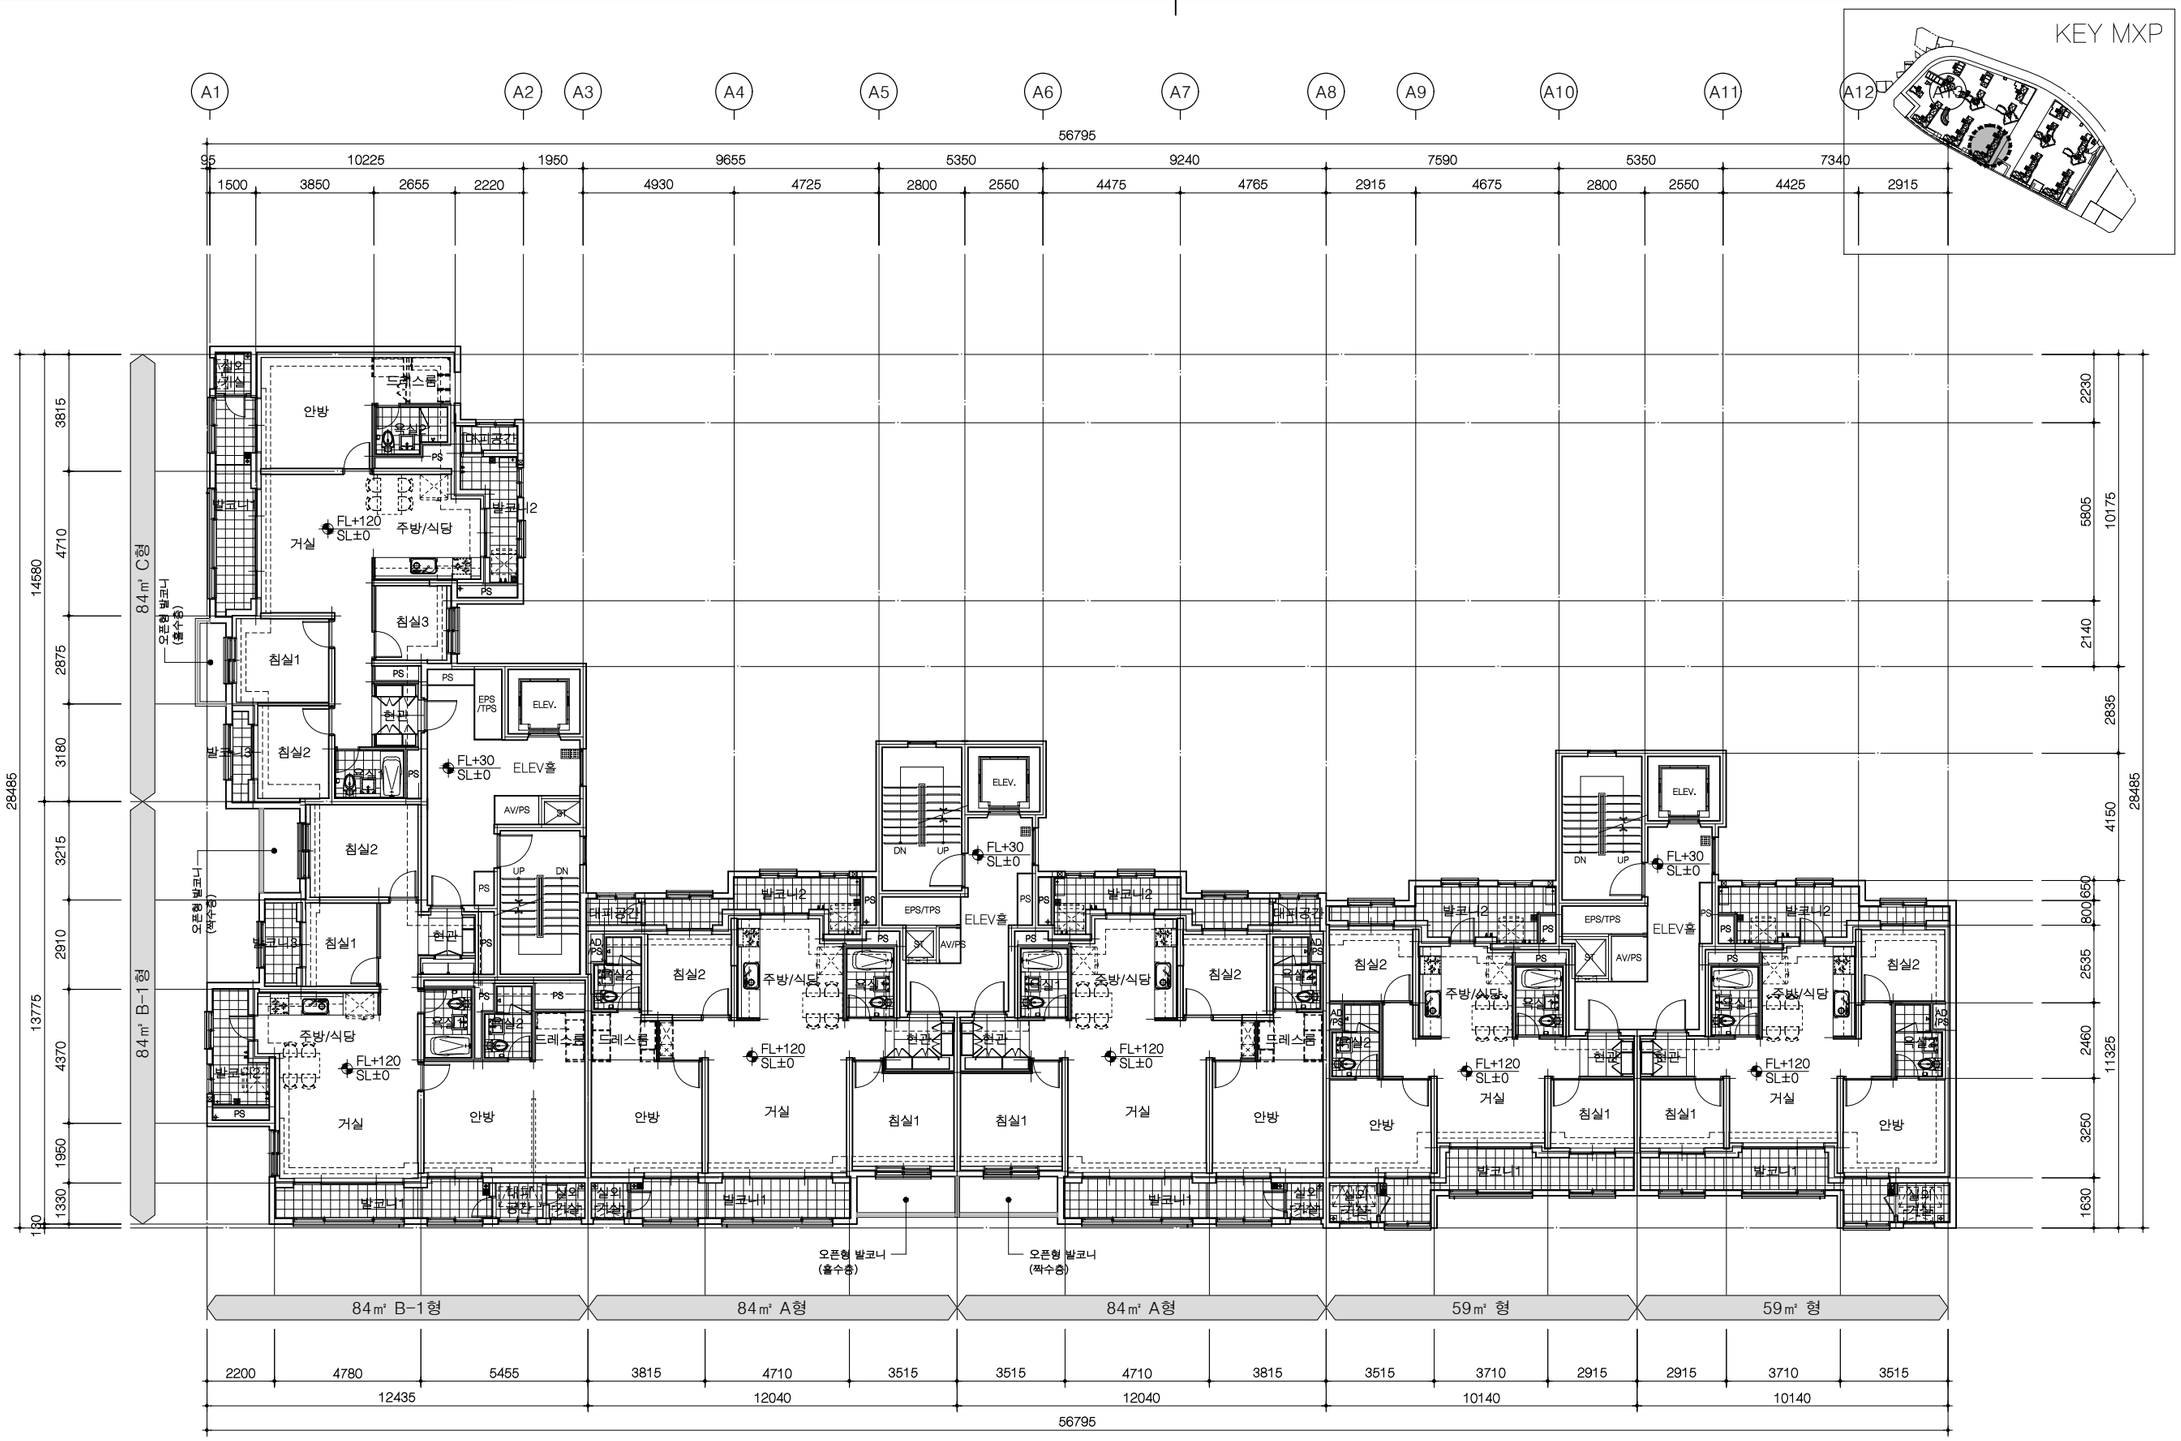

KEY MXP

110동 3~17층 평면도

축척 = 1/100

사업번호 PROJECT NO.

사업명 PROJECT TITLE

수색4재정비촉진구역
주택재개발 정비사업

KEY PLAN

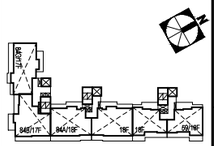

NOTE

1. 본 도면은 발코니 확장전를 기준으로 작성됨.
2. 지붕층 난간의 형태와 설치 위치는 안전성과 입면디자인을 고려하여 변경 가능함.
3. 지붕의 재료, 형태, 구조는 실시공 시 변경 될 수 있음.
4. 지붕 및 옥탑 구조물의 형태와 구조는 실시공 시 변경될 수 있음.
5. 옥상 출눈의 간격은 실시공 시 변경될 수 있음.
6. 옥상 출눈 틈에 실란트 시공되지 않음
7. 우편물 수취함 설치 위치는 변경될 수 있음
8. 오픈형 발코니 3층이상 ~ 20층이하 설치

수정번호 REV. NO.	일 자 DATE	내 용 DESCRIPTION	승 인 CHKD
△			
△			
△			
△			

설계 DESIGNED BY

검토 CHECKED BY
최 진 규

심사 SUMMITED BY
정 호 혁

승인 APPROVED BY
이 승 준

일자 DATE
2019.08

도면명 DRAWING TITLE
110동
3~17층 평면도

축 척 SCALE
A1: 1/100
A3: 1/200

도면번호 DRAWING NO.
A-435

일련번호 SHEET NO. △ REV. NO.

HAUD
(주)하우드엔지니어링
종합건축사사무소
Architects, Planners & Engineers
TEL. 02 2140 4400, SEOUL, KOREA

110동 18층 평면도

1 / A

축척 = 1/100

사업번호 PROJECT NO.

사업명 PROJECT TITLE

수색4재정비촉진구역
주택재개발 정비사업

KEY PLAN

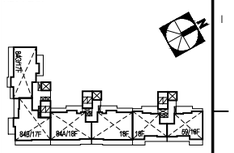

NOTE

1. 본 도면은 발코니 확장전를 기준으로 작성됨.
2. 지붕층 난간의 형태와 설치 위치는 안전성과 입면디자인을 고려하여 변경 가능함.
3. 지붕의 재료, 형태, 구조는 실시공 시 변경 될 수 있음.
4. 지붕 및 옥탑 구조물의 형태와 구조는 실시공 시 변경될 수 있음.
5. 옥상 출눈의 간격은 실시공 시 변경될 수 있음.
6. 옥상 출눈 틈에 실란트 시공되지 않음
7. 우편물 수취함 설치 위치는 변경될 수 있음
8. 오픈형 발코니 3층이상 ~ 20층이하 설치

수정번호 REV. NO.	일 자 DATE	내 용 DESCRIPTION	승 인 CHKD
△			
△			
△			
△			

설계 DESIGNED BY

검토 CHECKED BY
최 진 규

심사 SUMMITED BY
정 호 혁

승인 APPROVED BY
이 승 준

일자 DATE
2019.08

도면명 DRAWING TITLE
110동
18층 평면도

축 척 SCALE
A1: 1/100
A3: 1/200

도면번호 DRAWING NO.
A-436

일련번호 SHEET NO. △ REV. NO.

HAUD
㈜하우드엔지니어링
종합건축사사무소
Architects, Planners & Engineers
TEL. 02 2140 4400, SEOUL, KOREA

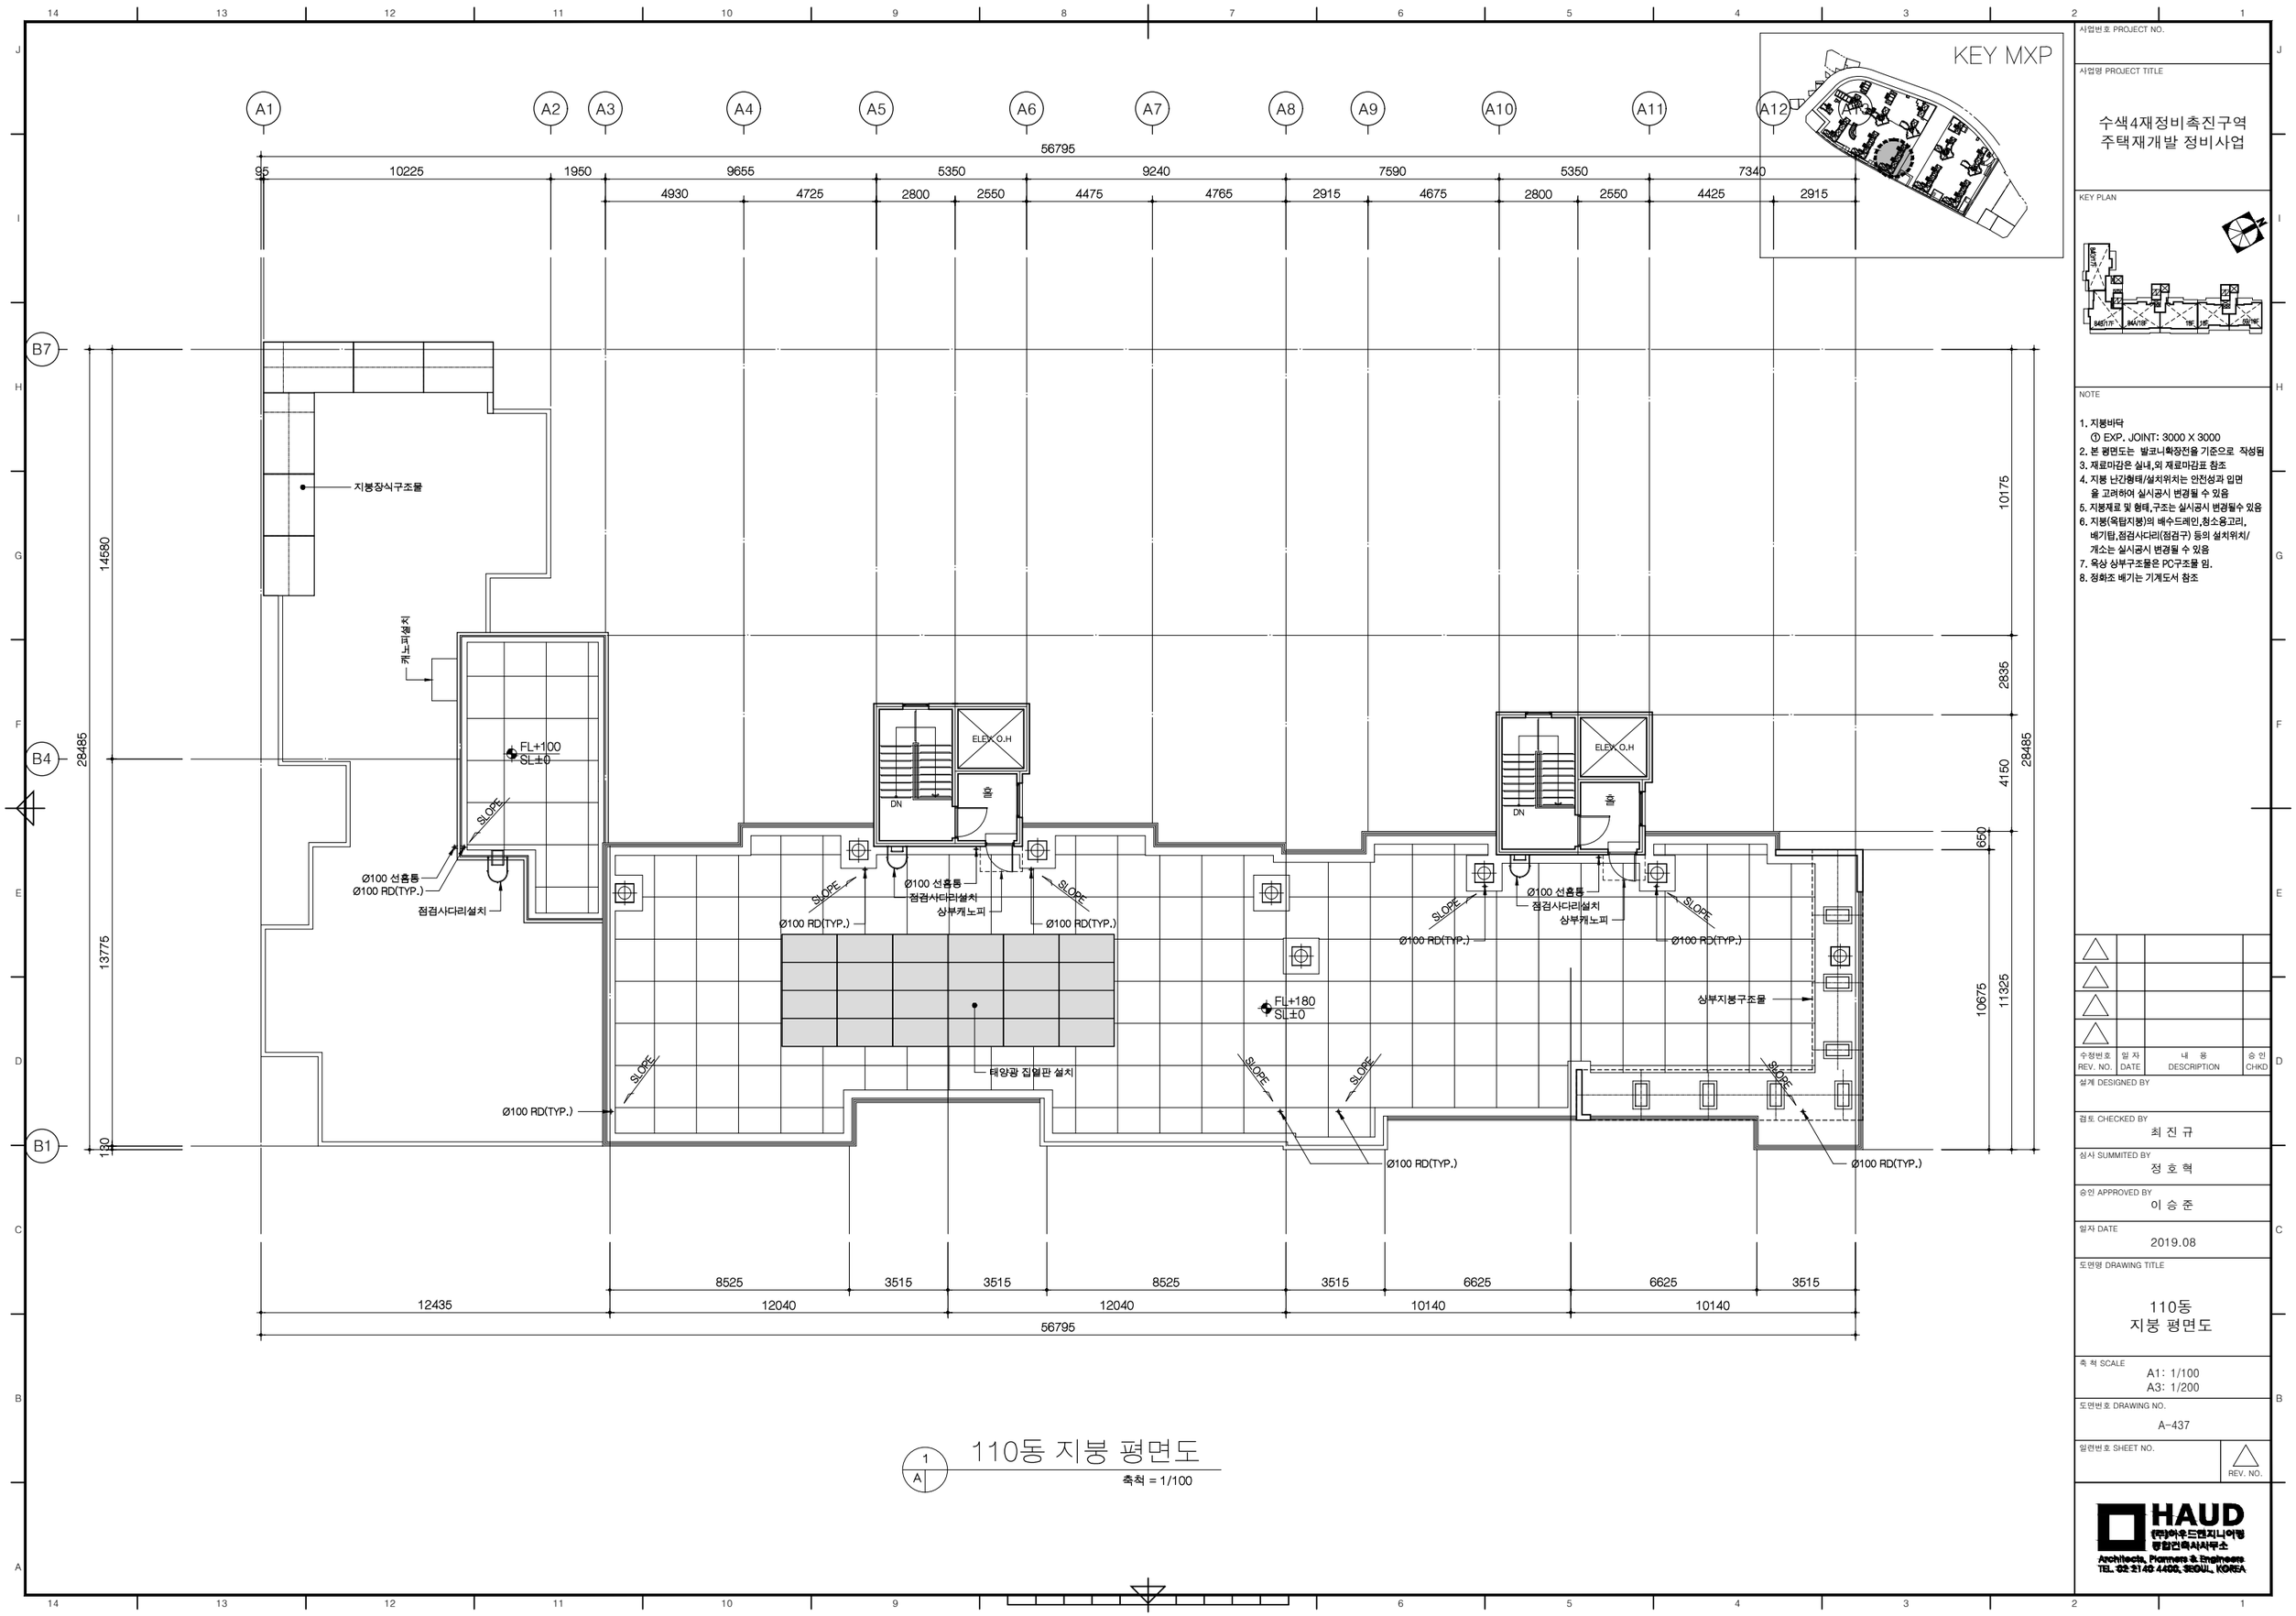

KEY MXP

1 A 110동 지붕 평면도

축척 = 1/100

사업번호 PROJECT NO.

사업명 PROJECT TITLE

수색4재정비촉진구역
주택재개발 정비사업

KEY PLAN

NOTE

1. 지붕바닥
   ① EXP. JOINT: 3000 X 3000
2. 본 평면도는 발코니확장전을 기준으로 작성됨
3. 재료마감은 실내,외 재료마감표 참조
4. 지붕 난간형태/설치위치는 안전성과 입면을 고려하여 실시공시 변경될 수 있음
5. 지붕재료 및 형태,구조는 실시공시 변경될수 있음
6. 지붕(옥탑지붕)의 배수드레인,청소용고리, 베기탑,점검사다리(점검구) 등의 설치위치/개소는 실시공시 변경될 수 있음
7. 옥상 상부구조물은 PC구조물 임.
8. 정화조 배기는 기계도서 참조

수정번호 REV. NO.	일 자 DATE	내 용 DESCRIPTION	승 인 CHKD
△			
△			
△			
△			

설계 DESIGNED BY

검토 CHECKED BY
최 진 규

심사 SUMMITED BY
정 호 혁

승인 APPROVED BY
이 승 준

일자 DATE
2019.08

도면명 DRAWING TITLE

110동
지붕 평면도

축 척 SCALE
A1: 1/100
A3: 1/200

도면번호 DRAWING NO.
A-437

일련번호 SHEET NO. △ REV. NO.

HAUD
㈜하우드엔지니어링
종합건축사사무소
Architects, Planners & Engineers
TEL. 02 2143 4400, SEOUL, KOREA

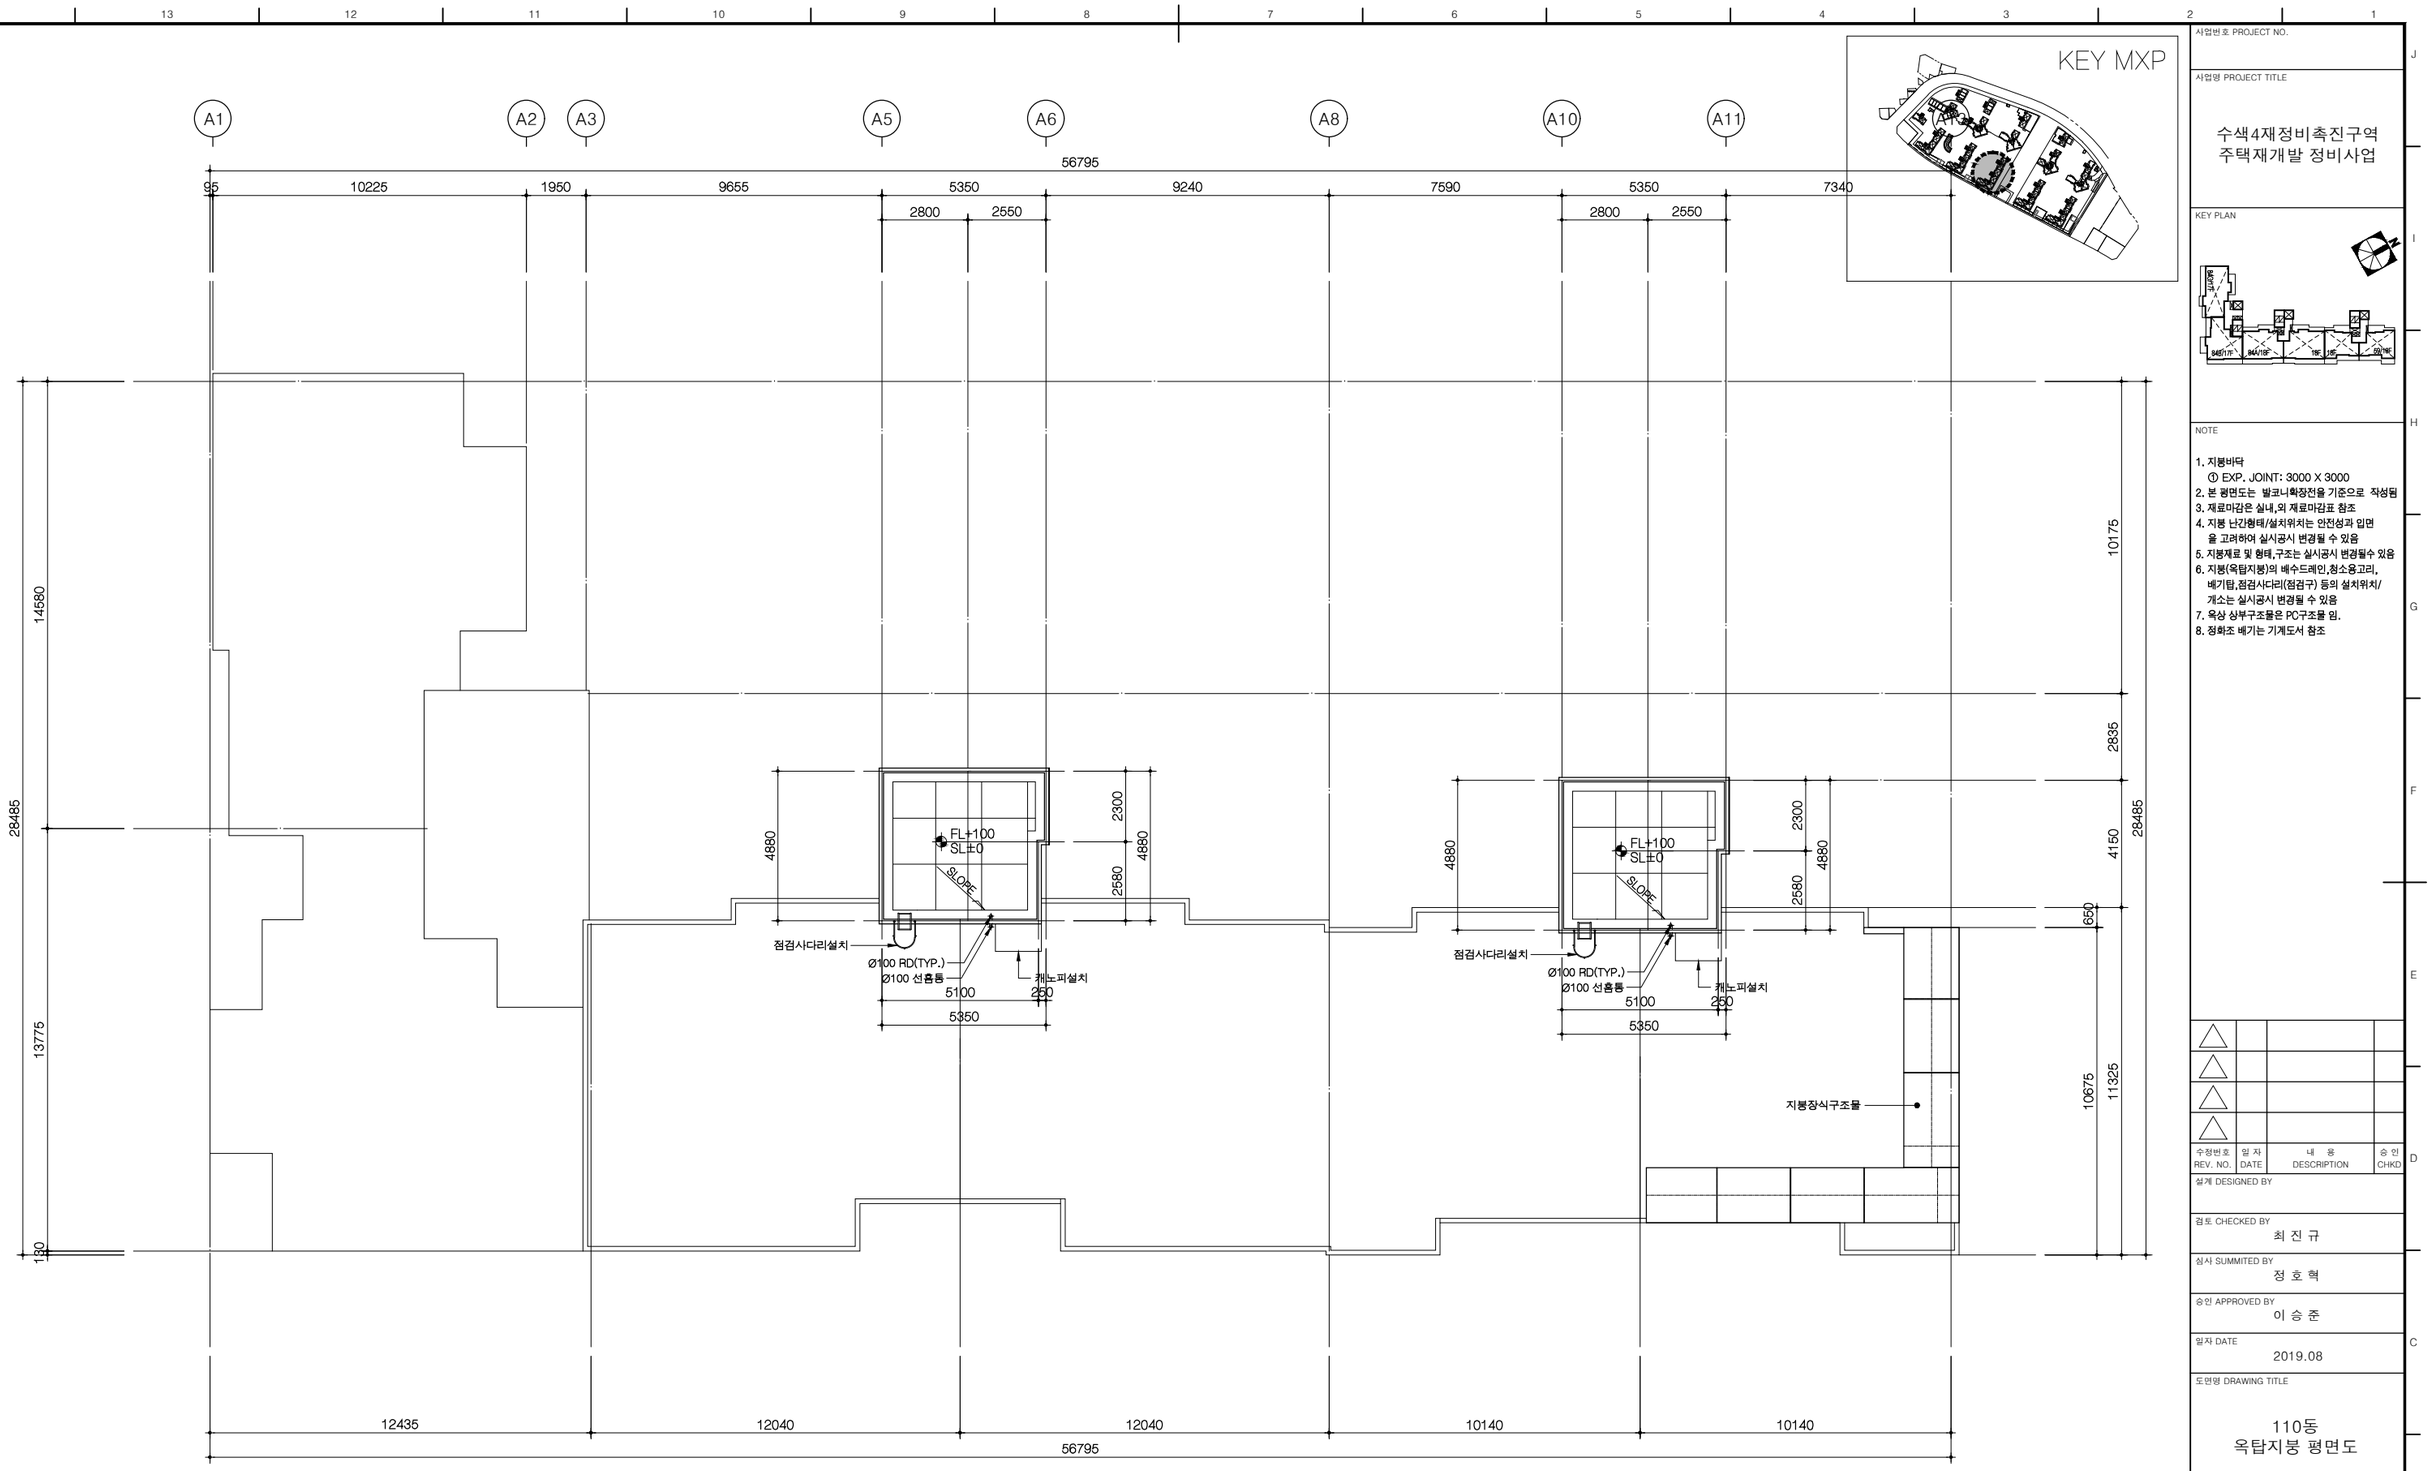

KEY MXP

1 A 110동 옥탑지붕 평면도

축척 = 1/100

사업번호 PROJECT NO.

사업명 PROJECT TITLE

수색4재정비촉진구역
주택재개발 정비사업

KEY PLAN

NOTE

1. 지붕바닥
   ① EXP. JOINT: 3000 X 3000
2. 본 평면도는 발코니확장전을 기준으로 작성됨
3. 재료마감은 실내,외 재료마감표 참조
4. 지붕 난간형태/설치위치는 안전성과 입면을 고려하여 실시공시 변경될 수 있음
5. 지붕재료 및 형태,구조는 실시공시 변경될수 있음
6. 지붕(옥탑지붕)의 배수드레인,창소용고리, 베기탑,점검사다리(점검구) 등의 설치위치/개소는 실시공시 변경될 수 있음
7. 옥상 상부구조물은 PC구조물 임.
8. 정화조 배기는 기계도서 참조

수정번호 REV. NO.	일 자 DATE	내 용 DESCRIPTION	승 인 CHKD
△			
△			
△			
△			

설계 DESIGNED BY

검토 CHECKED BY
최 진 규

심사 SUMMITED BY
정 호 혁

승인 APPROVED BY
이 승 준

일자 DATE
2019.08

도면명 DRAWING TITLE
110동
옥탑지붕 평면도

축 척 SCALE
A1: 1/100
A3: 1/200

도면번호 DRAWING NO.
A-438

일련번호 SHEET NO.

△ REV. NO.

HAUD
(주)하우드엔지니어링
종합건축사사무소
Architects, Planners & Engineers
TEL. 82 2 1 4G 4408, SEOUL, KOREA

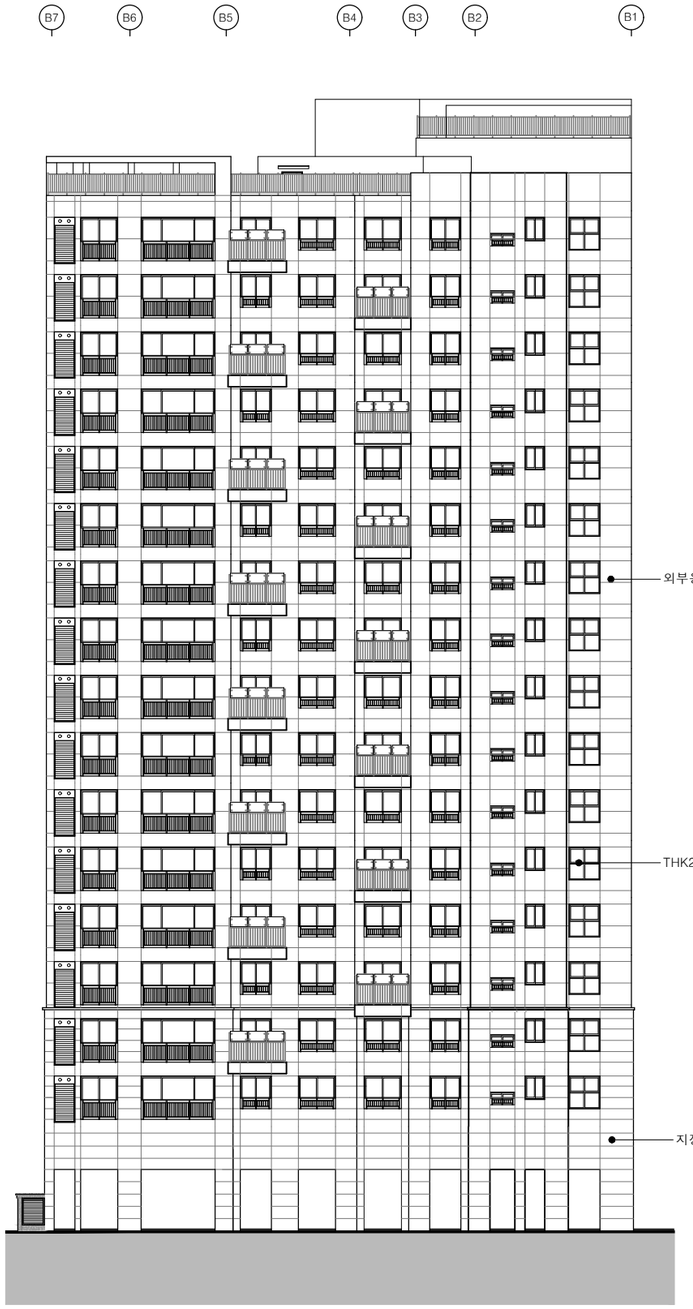

1 A 110동 정면도

축척 = 1/150

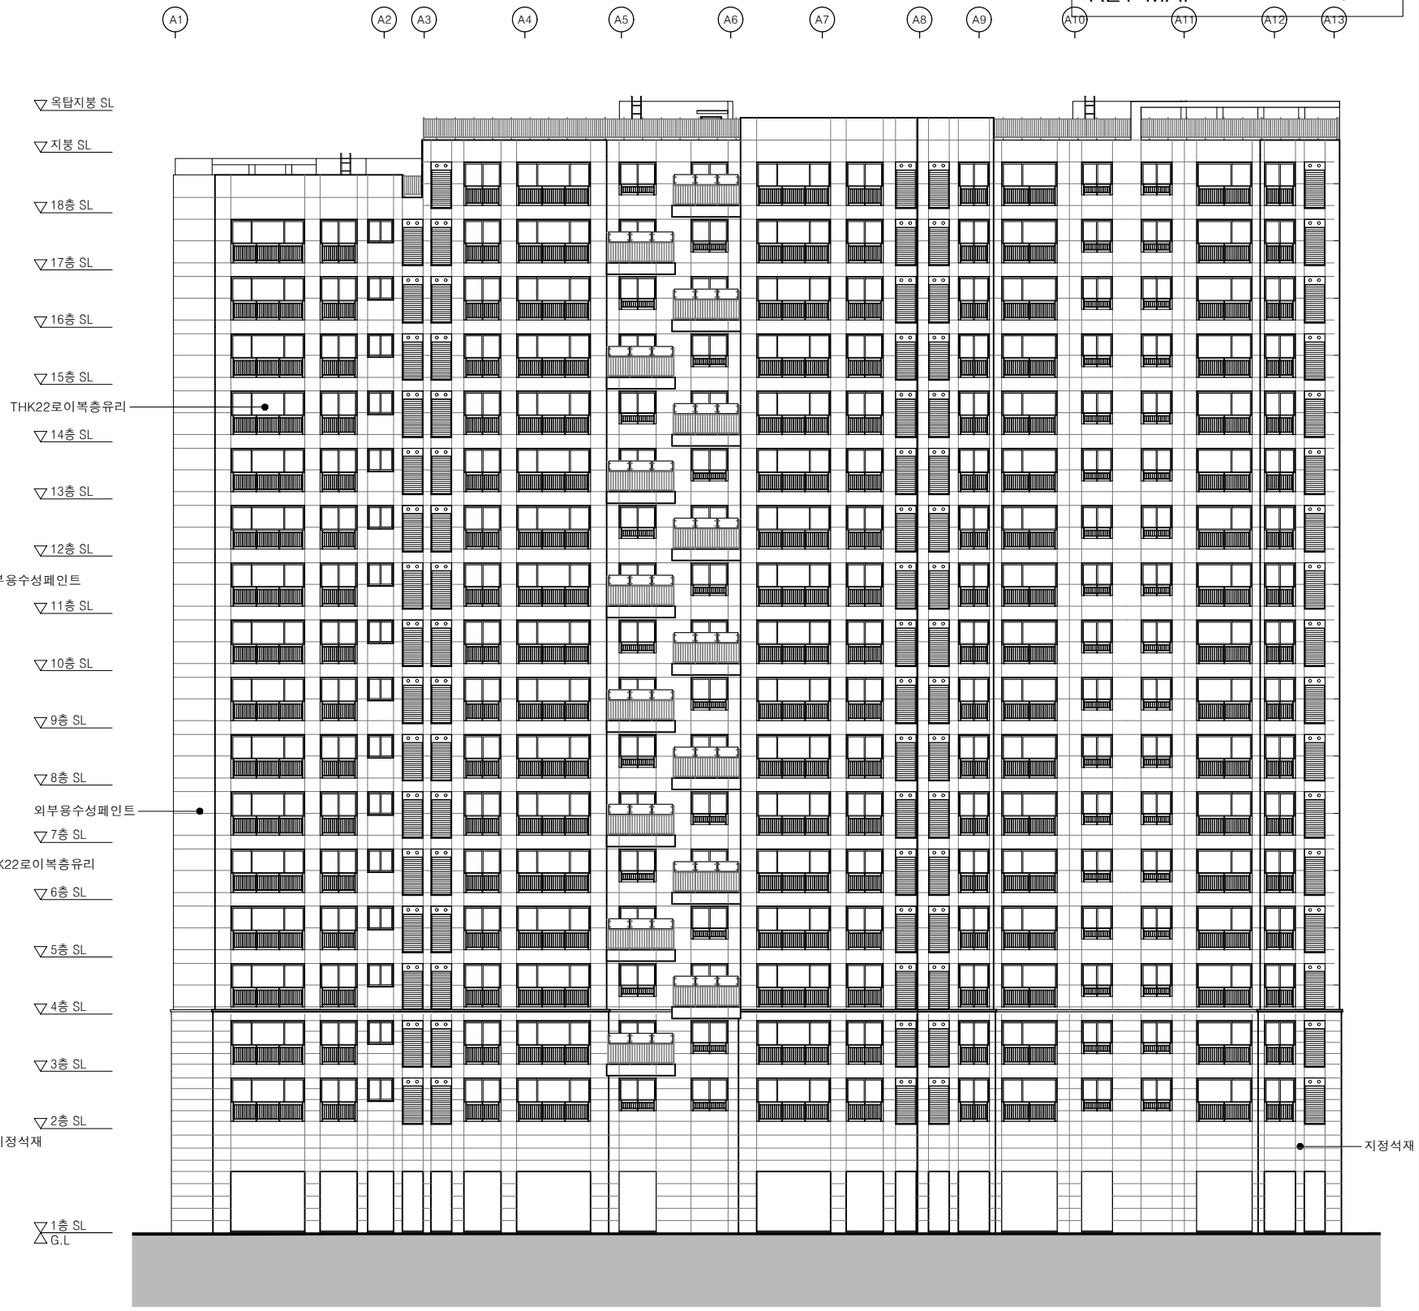

2 A 110동 우측면도

축척 = 1/150

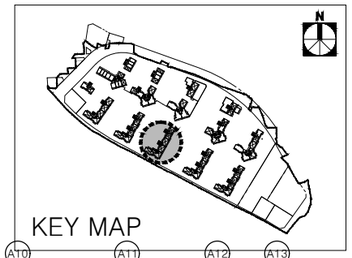

사업번호 PROJECT NO.

사업명 PROJECT TITLE

수색4재정비촉진구역
주택재개발 정비사업

KEY PLAN

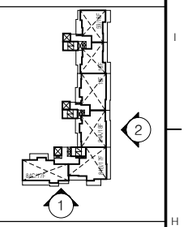

NOTE

1. 1층 바닥 LEVEL
   1SL±0 = 1FL±0 = GL±0 = EL+24.20
2. 지붕 난간의 형태 및 설치위치는 안전성과 입면디자인을 고려하여 변경가능함.
3. 지붕의 재료, 형태, 구조는 실시공시 변경될 수 있음.
4. 지붕 및 옥탑구조물의 형태와 구조는 실시공시 변경될 수 있음.
5. 외벽 및 측벽 문양은 실시공시 변경될 수 있음
6. 입면의 줄눈 및 마감선은 실시공시 변경될 수 있음.
7. 저층부 석재마감 및 입면 마감 색상, 재료에 대한 모든 기준은 특화도면을 우선 적용함.

수정번호 REV. NO.	일 자 DATE	내 용 DESCRIPTION	승 인 CHKD
△			
△			
△			
△			

설계 DESIGNED BY

검토 CHECKED BY
최 진 규

심사 SUMMITED BY
정 호 혁

승인 APPROVED BY
이 승 준

일자 DATE
2019.08

도면명 DRAWING TITLE
110동 정면도,우측면도

축 척 SCALE
A1: 1/150
A3: 1/300

도면번호 DRAWING NO.
A-439

일련번호 SHEET NO. △ REV. NO.

HAUD
㈜하우드엔지니어링
종합건축사사무소
Architects, Planners & Engineers
TEL. 02 2140 4400, SEOUL, KOREA

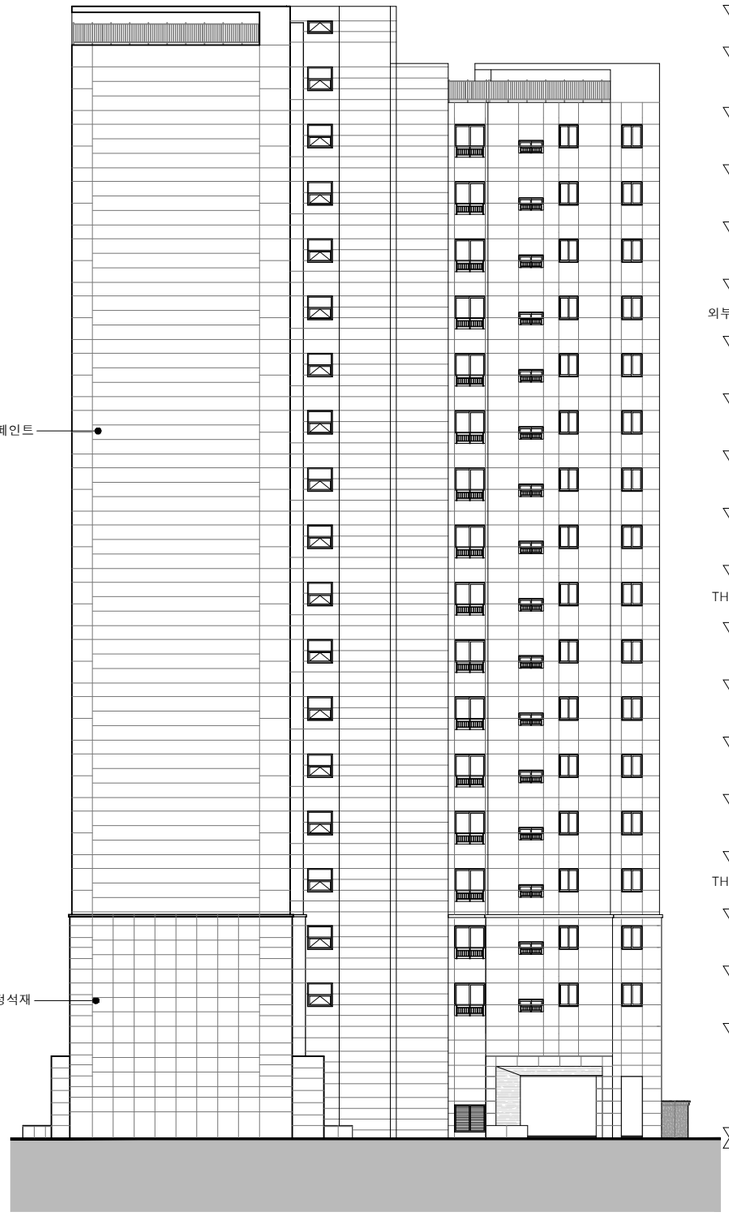

1 A 110동 배면도

축척 = 1/150

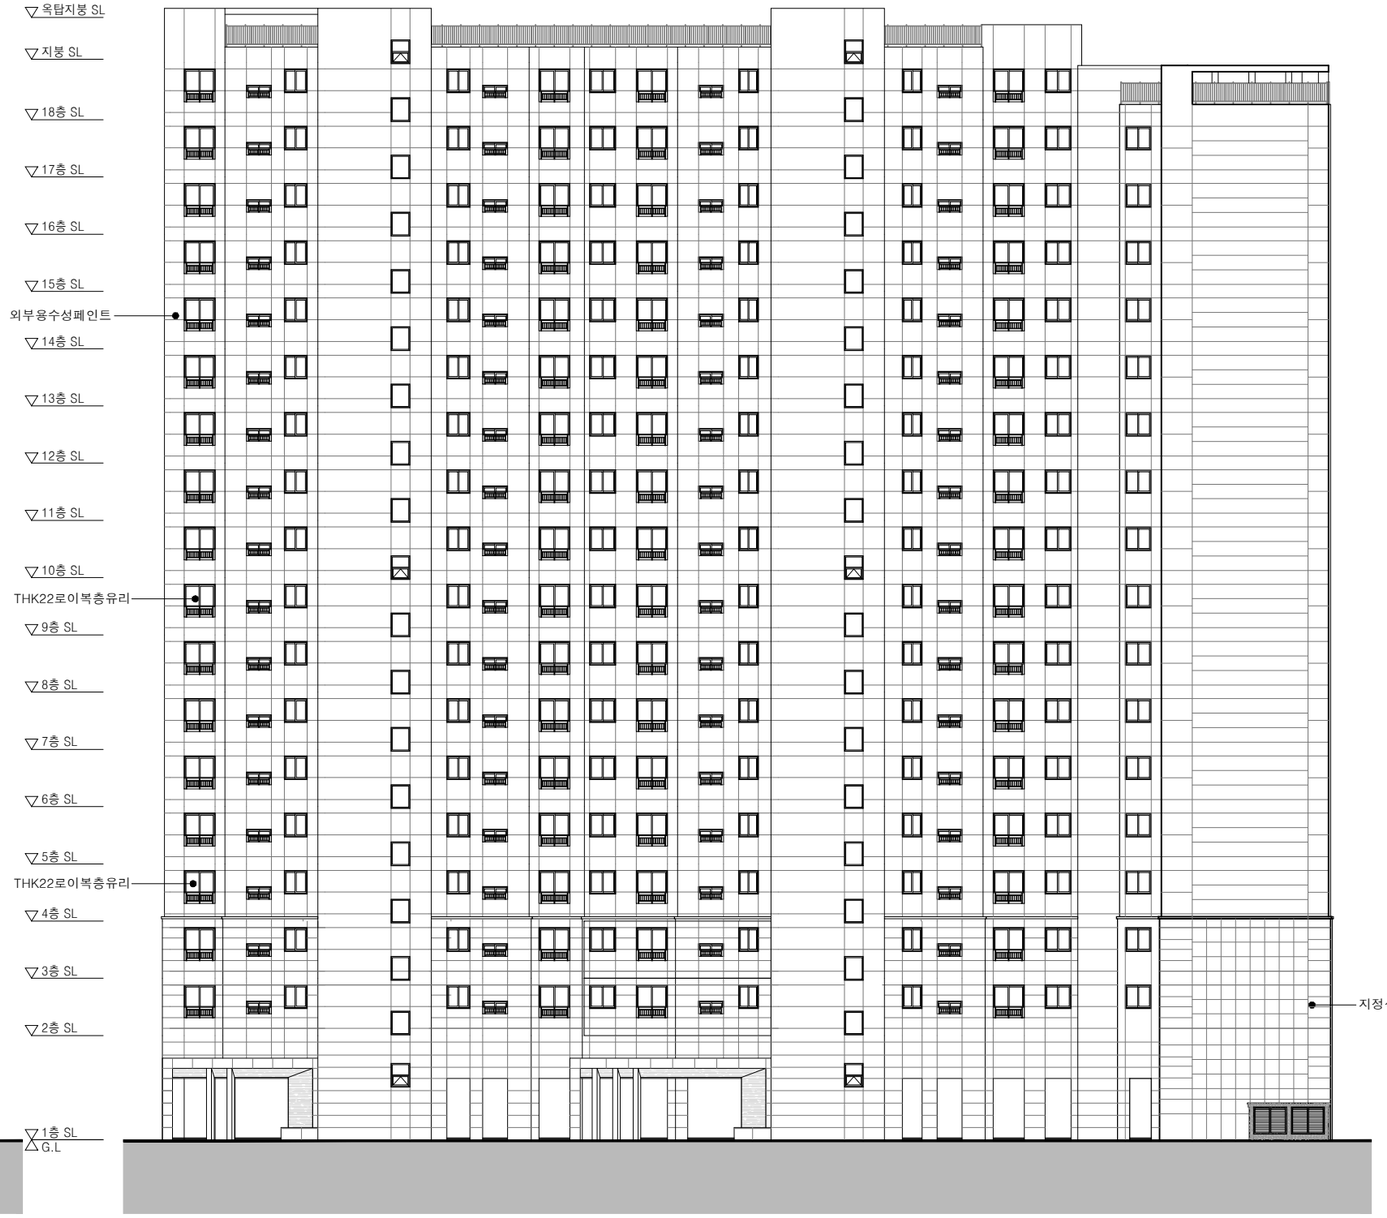

2 A 110동 좌측면도

축척 = 1/150

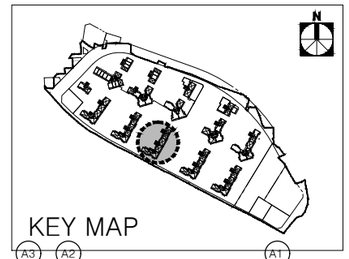

사업번호 PROJECT NO.

사업명 PROJECT TITLE

수색4재정비촉진구역
주택재개발 정비사업

KEY PLAN

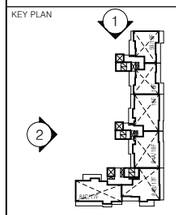

NOTE

1. 1층 바닥 LEVEL
   1SL±0 = 1FL±0 = GL±0 = EL+24.20
2. 지붕 난간의 형태 및 설치위치는 안전성과 입면디자인을 고려하여 변경가능함.
3. 지붕의 재료, 형태, 구조는 실시공시 변경될 수 있음.
4. 지붕 및 옥탑구조물의 형태와 구조는 실시공시 변경될 수 있음.
5. 외벽 및 측벽 문양은 실시공시 변경될 수 있음
6. 입면의 줄눈 및 마감선은 실시공시 변경될 수 있음.
7. 저층부 석재마감 및 입면 마감 색상, 재료에 대한 모든 기준은 특화도면을 우선 적용함.

수정번호 REV. NO.	일 자 DATE	내 용 DESCRIPTION	승 인 CHKD
△			
△			
△			
△			

설계 DESIGNED BY

검토 CHECKED BY
최 진 규

심사 SUMMITED BY
정 호 혁

승인 APPROVED BY
이 승 준

일자 DATE
2019.08

도면명 DRAWING TITLE

110동 배면도,좌측면도

축 척 SCALE
A1: 1/150
A3: 1/300

도면번호 DRAWING NO.
A-440

일련번호 SHEET NO.

△ REV. NO.

HAUD
㈜하우드엔지니어링
종합건축사사무소
Architects, Planners & Engineers
TEL. 02 2140 4400, SEOUL, KOREA

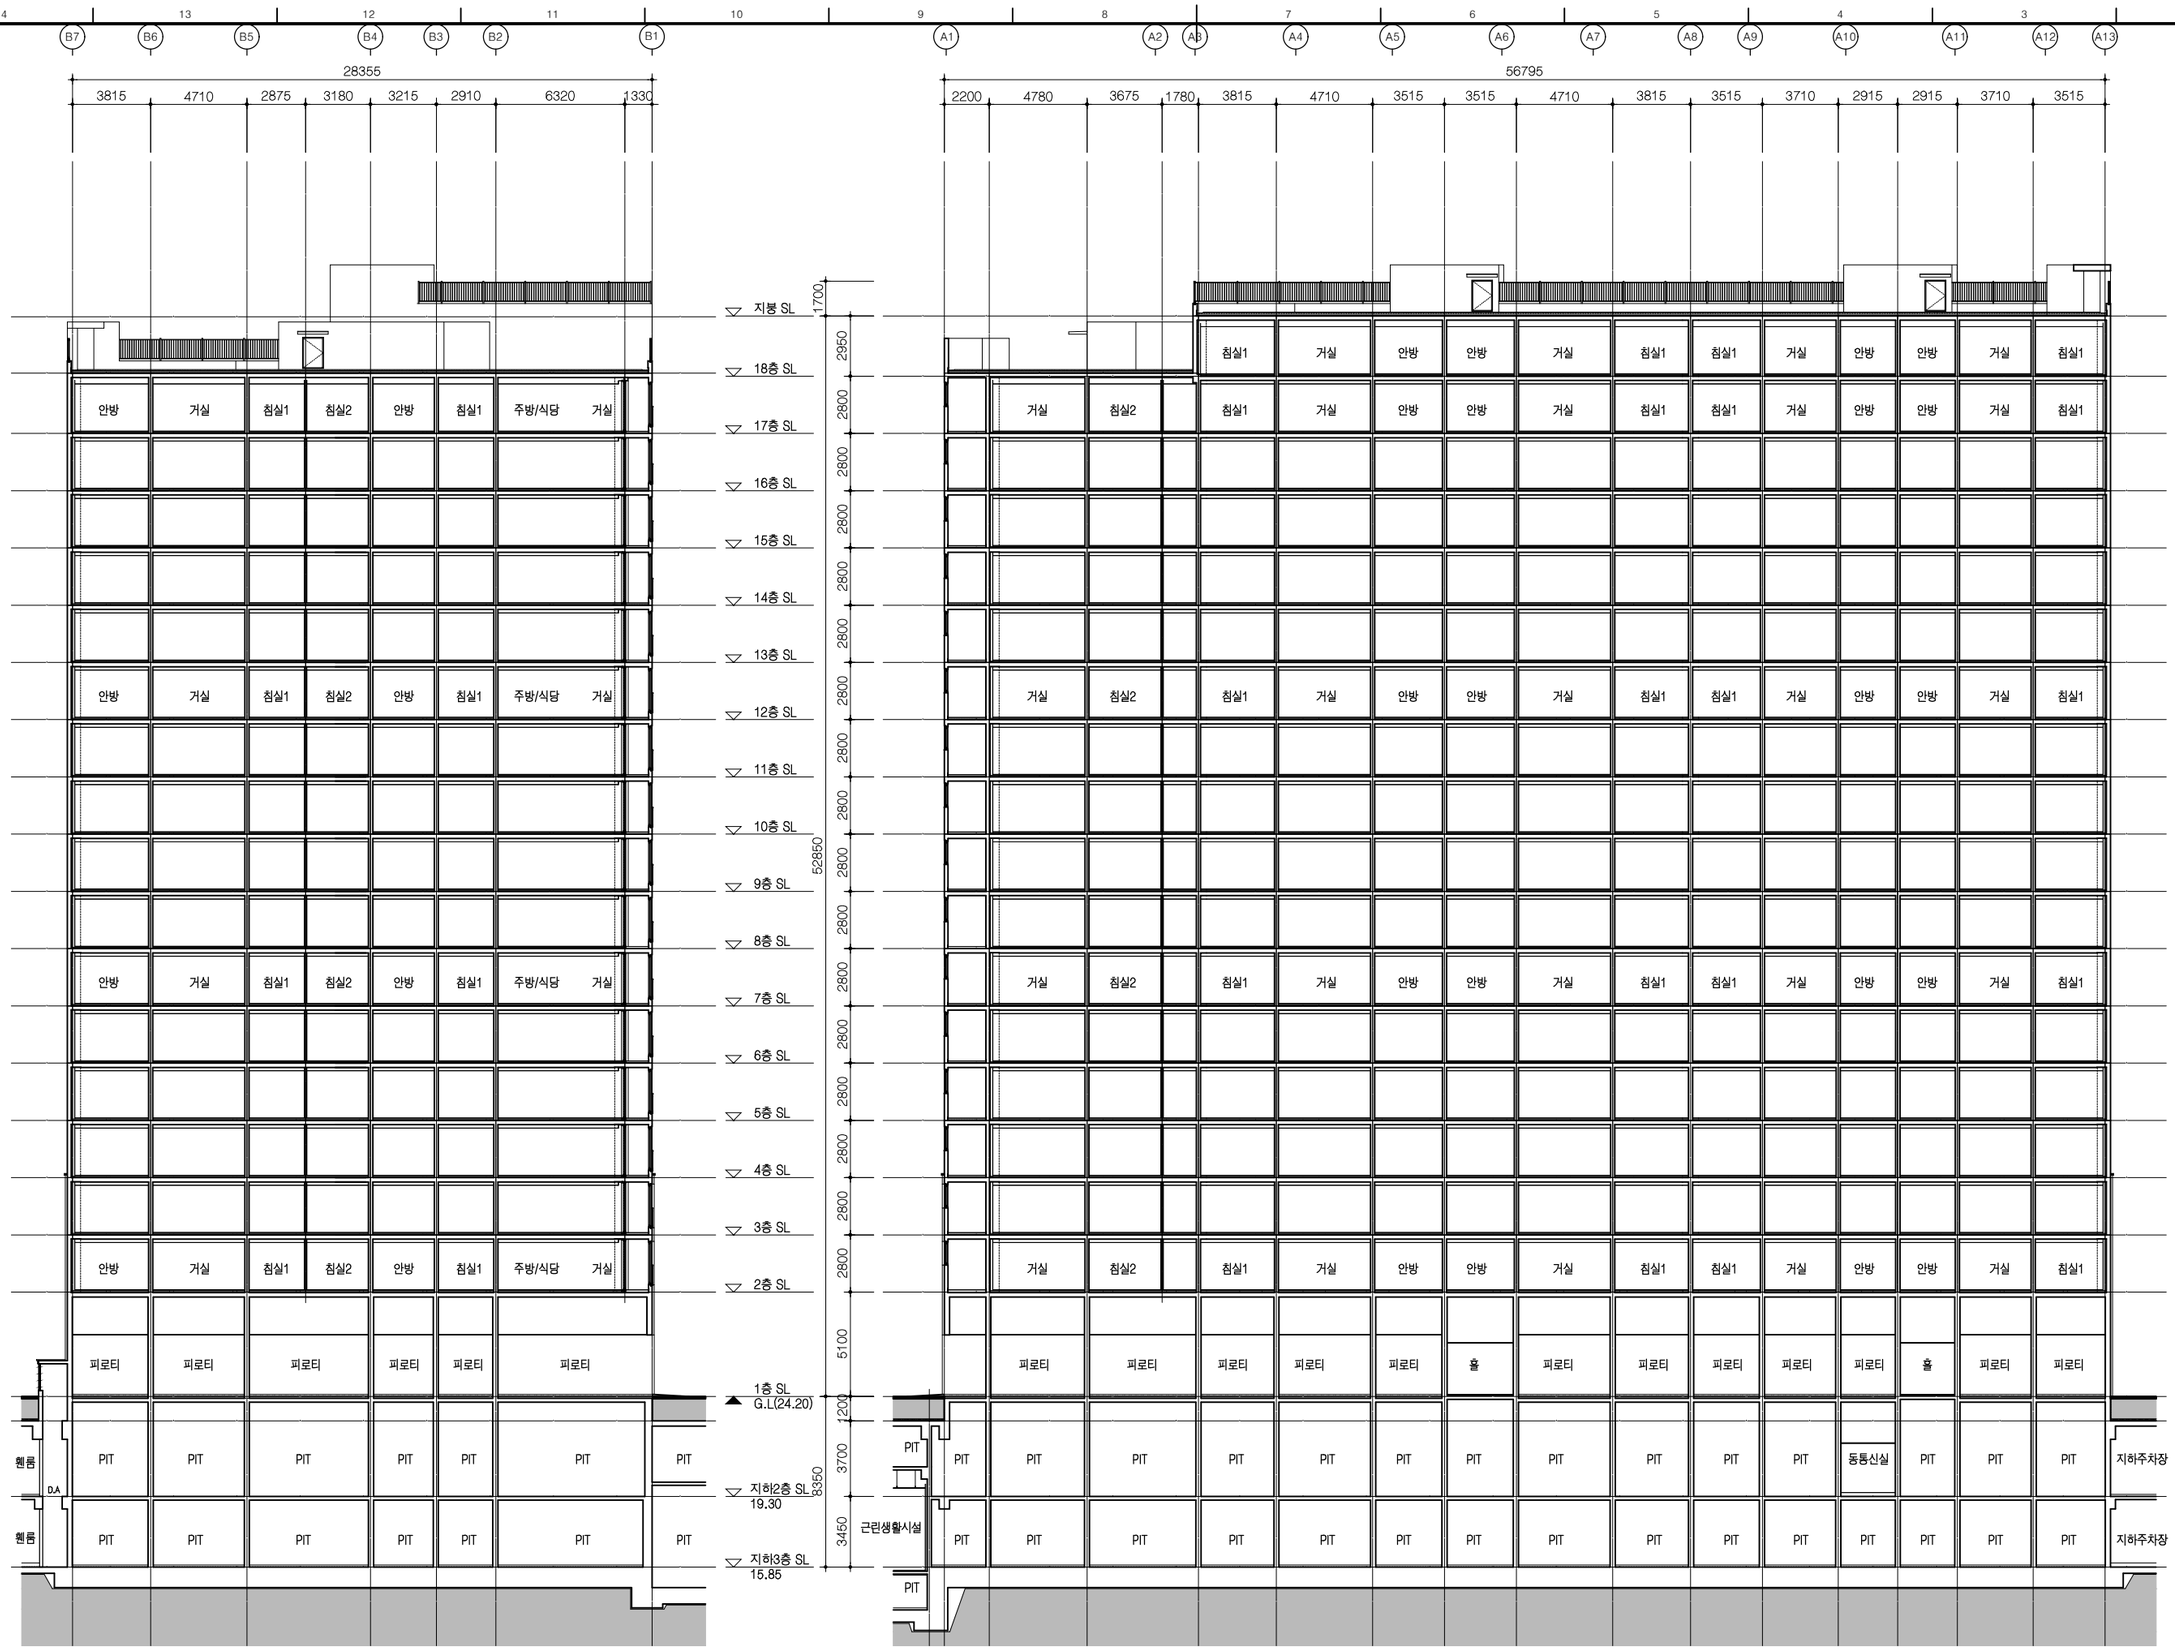

1 A 110동 종단면도

축척 = 1/150

2 A 110동 횡단면도

축척 = 1/150

사업번호 PROJECT NO.

사업명 PROJECT TITLE

수색4재정비촉진구역
주택재개발 정비사업

KEY PLAN

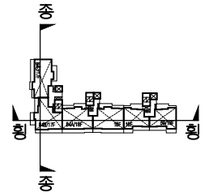

NOTE

수정번호 REV. NO.	일 자 DATE	내 용 DESCRIPTION	승 인 CHKD

설계 DESIGNED BY

검토 CHECKED BY
최 진 규

심사 SUMMITED BY
정 호 혁

승인 APPROVED BY
이 승 준

일자 DATE
2019.08

도면명 DRAWING TITLE
110동 종,횡단면도

축 척 SCALE
A1: 1/150
A3: 1/300

도면번호 DRAWING NO.
A-441

일련번호 SHEET NO.

REV. NO.

HAUD
(주)하우드한지니어링
종합건축사사무소
Architects, Planners & Engineers
TEL. 82 2 1 4G 4400, SEOUL, KOREA

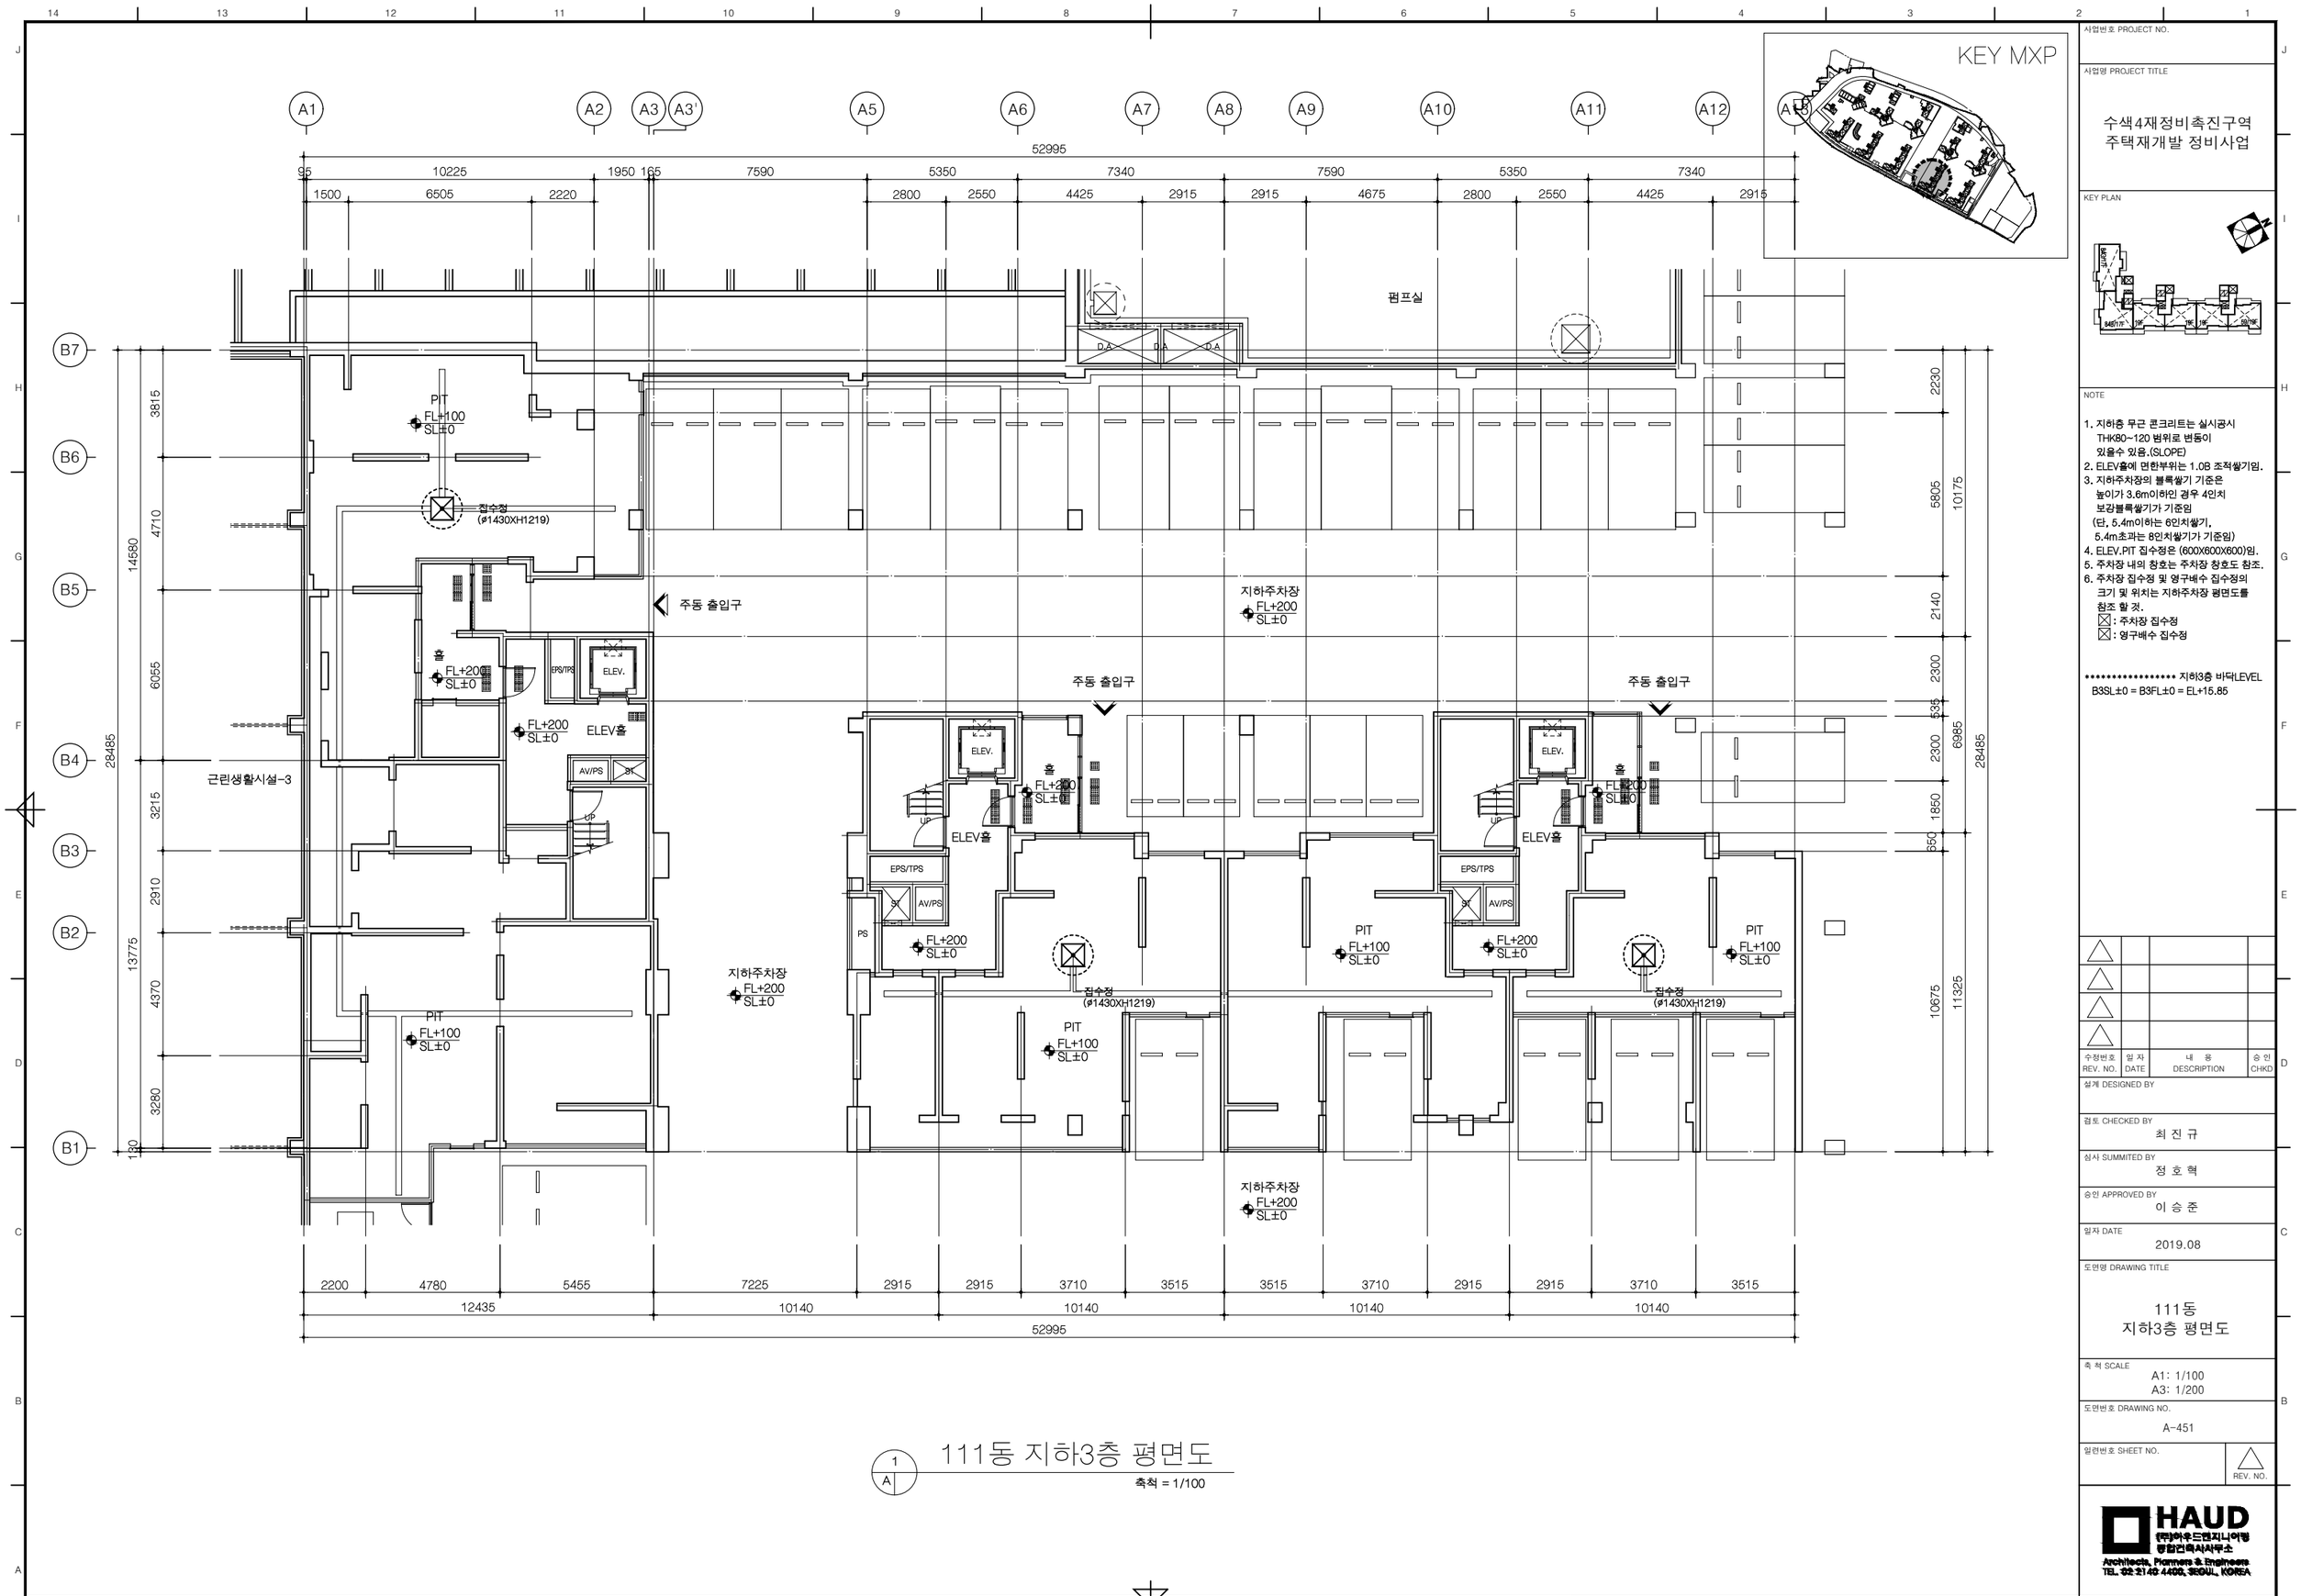

1 A 111동 지하3층 평면도

축척 = 1/100

KEY MXP

사업번호 PROJECT NO.

사업명 PROJECT TITLE

수색4재정비촉진구역
주택재개발 정비사업

KEY PLAN

NOTE

1. 지하층 무근 콘크리트는 실시공시 THK80~120 범위로 변동이 있을수 있음.(SLOPE)
2. ELEV홀에 면한부위는 1.0B 조적쌓기임.
3. 지하주차장의 블록쌓기 기준은 높이가 3.6m이하인 경우 4인치 보강블록쌓기가 기준임 (단, 5.4m이하는 6인치쌓기, 5.4m초과는 8인치쌓기가 기준임)
4. ELEV.PIT 집수정은 (600X600X600)임.
5. 주차장 내의 창호는 주차장 창호도 참조.
6. 주차장 집수정 및 영구배수 집수정의 크기 및 위치는 지하주차장 평면도를 참조 할 것.
   ☒ : 주차장 집수정
   ☒ : 영구배수 집수정

********** 지하3층 바닥LEVEL
B3SL±0 = B3FL±0 = EL+15.85

수정번호 REV. NO.	일 자 DATE	내 용 DESCRIPTION	승 인 CHKD
△			
△			
△			
△			

설계 DESIGNED BY

검토 CHECKED BY
최 진 규

심사 SUMMITED BY
정 호 혁

승인 APPROVED BY
이 승 준

일자 DATE
2019.08

도면명 DRAWING TITLE
111동
지하3층 평면도

축 척 SCALE
A1: 1/100
A3: 1/200

도면번호 DRAWING NO.
A-451

일련번호 SHEET NO. △ REV. NO.

HAUD
(주)하우드엔지니어링
종합건축사사무소
Architects, Planners & Engineers
TEL. 02 2140 4400, SEOUL, KOREA

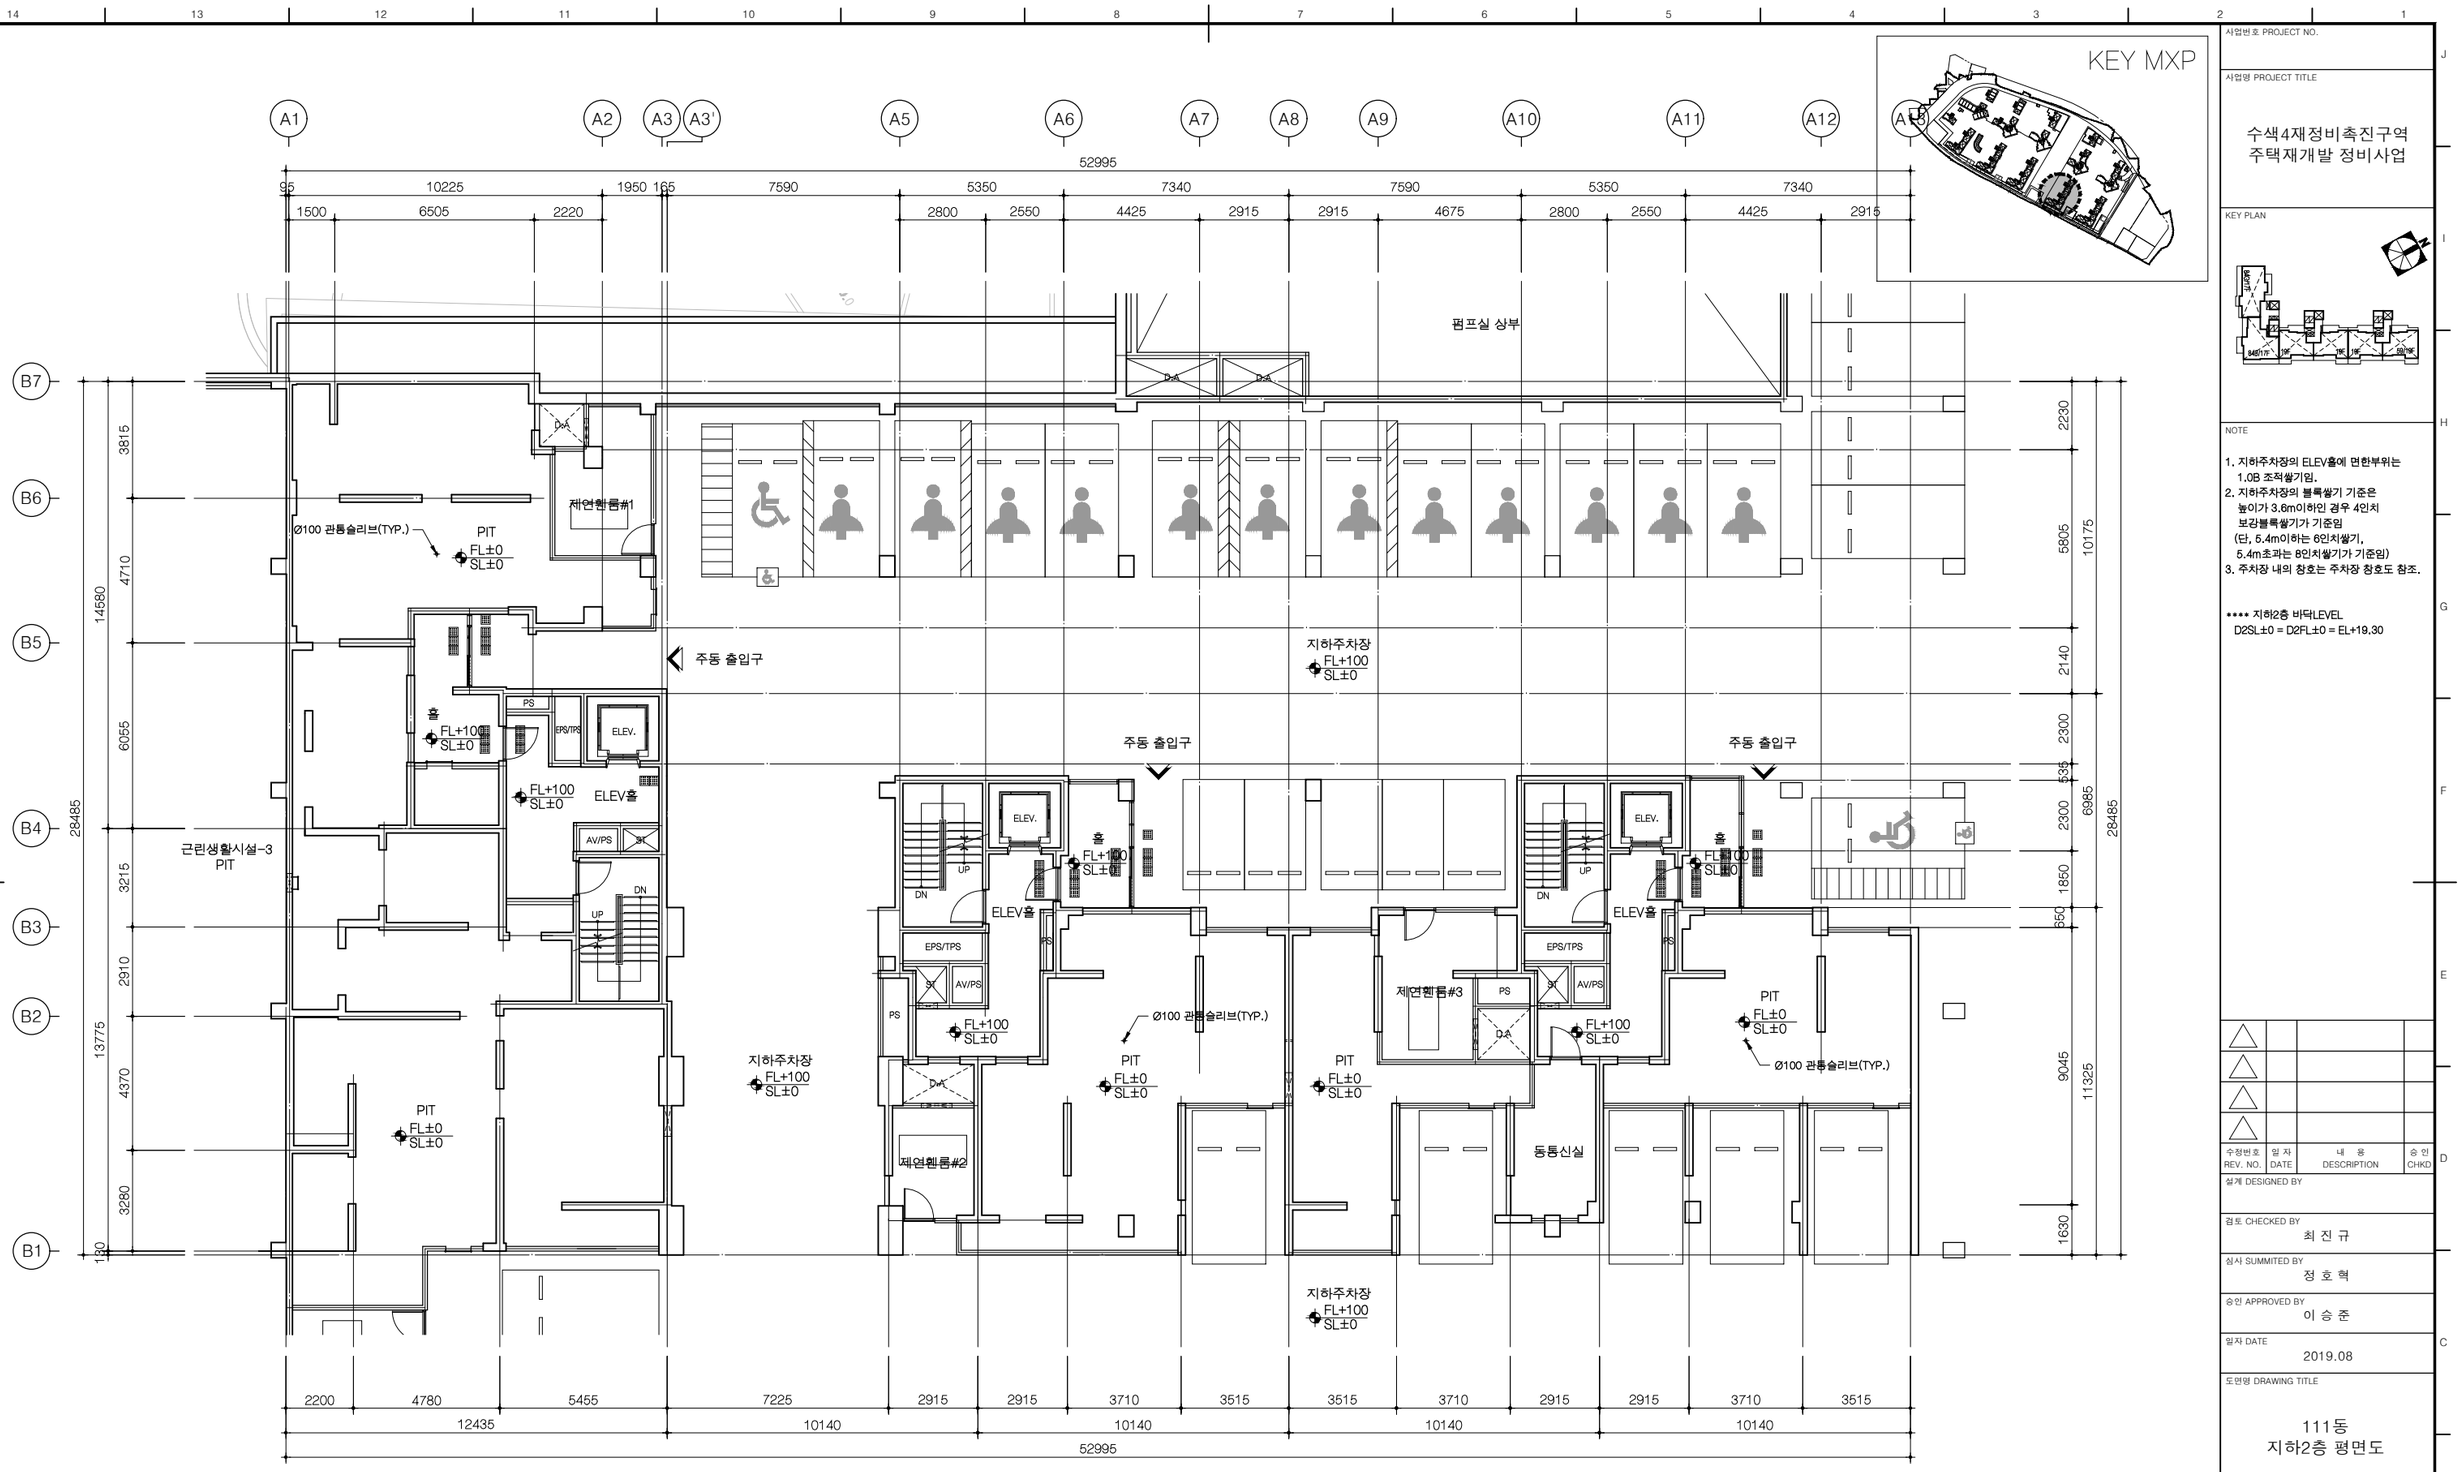

1 A 111동 지하2층 평면도

축척 = 1/100

KEY MXP

사업번호 PROJECT NO.

사업명 PROJECT TITLE

수색4재정비촉진구역
주택재개발 정비사업

KEY PLAN

NOTE

1. 지하주차장의 ELEV홀에 면한부위는 1.0B 조적쌓기임.
2. 지하주차장의 블록쌓기 기준은 높이가 3.6m이하인 경우 4인치 보강블록쌓기가 기준임 (단, 5.4m이하는 6인치쌓기, 5.4m초과는 8인치쌓기가 기준임)
3. 주차장 내의 창호는 주차장 창호도 참조.

**** 지하2층 바닥LEVEL
D2SL±0 = D2FL±0 = EL+19.30

수정번호 REV. NO.	일 자 DATE	내 용 DESCRIPTION	승 인 CHKD
△			
△			
△			
△			

설계 DESIGNED BY

검토 CHECKED BY
최 진 규

심사 SUMMITED BY
정 호 혁

승인 APPROVED BY
이 승 준

일자 DATE
2019.08

도면명 DRAWING TITLE
111동
지하2층 평면도

축 척 SCALE
A1: 1/100
A3: 1/200

도면번호 DRAWING NO.
A-452

일련번호 SHEET NO. △ REV. NO.

HAUD
(주)하우드엔지니어링
종합건축사사무소
Architects, Planners & Engineers
TEL. 02 2140 4400, SEOUL, KOREA

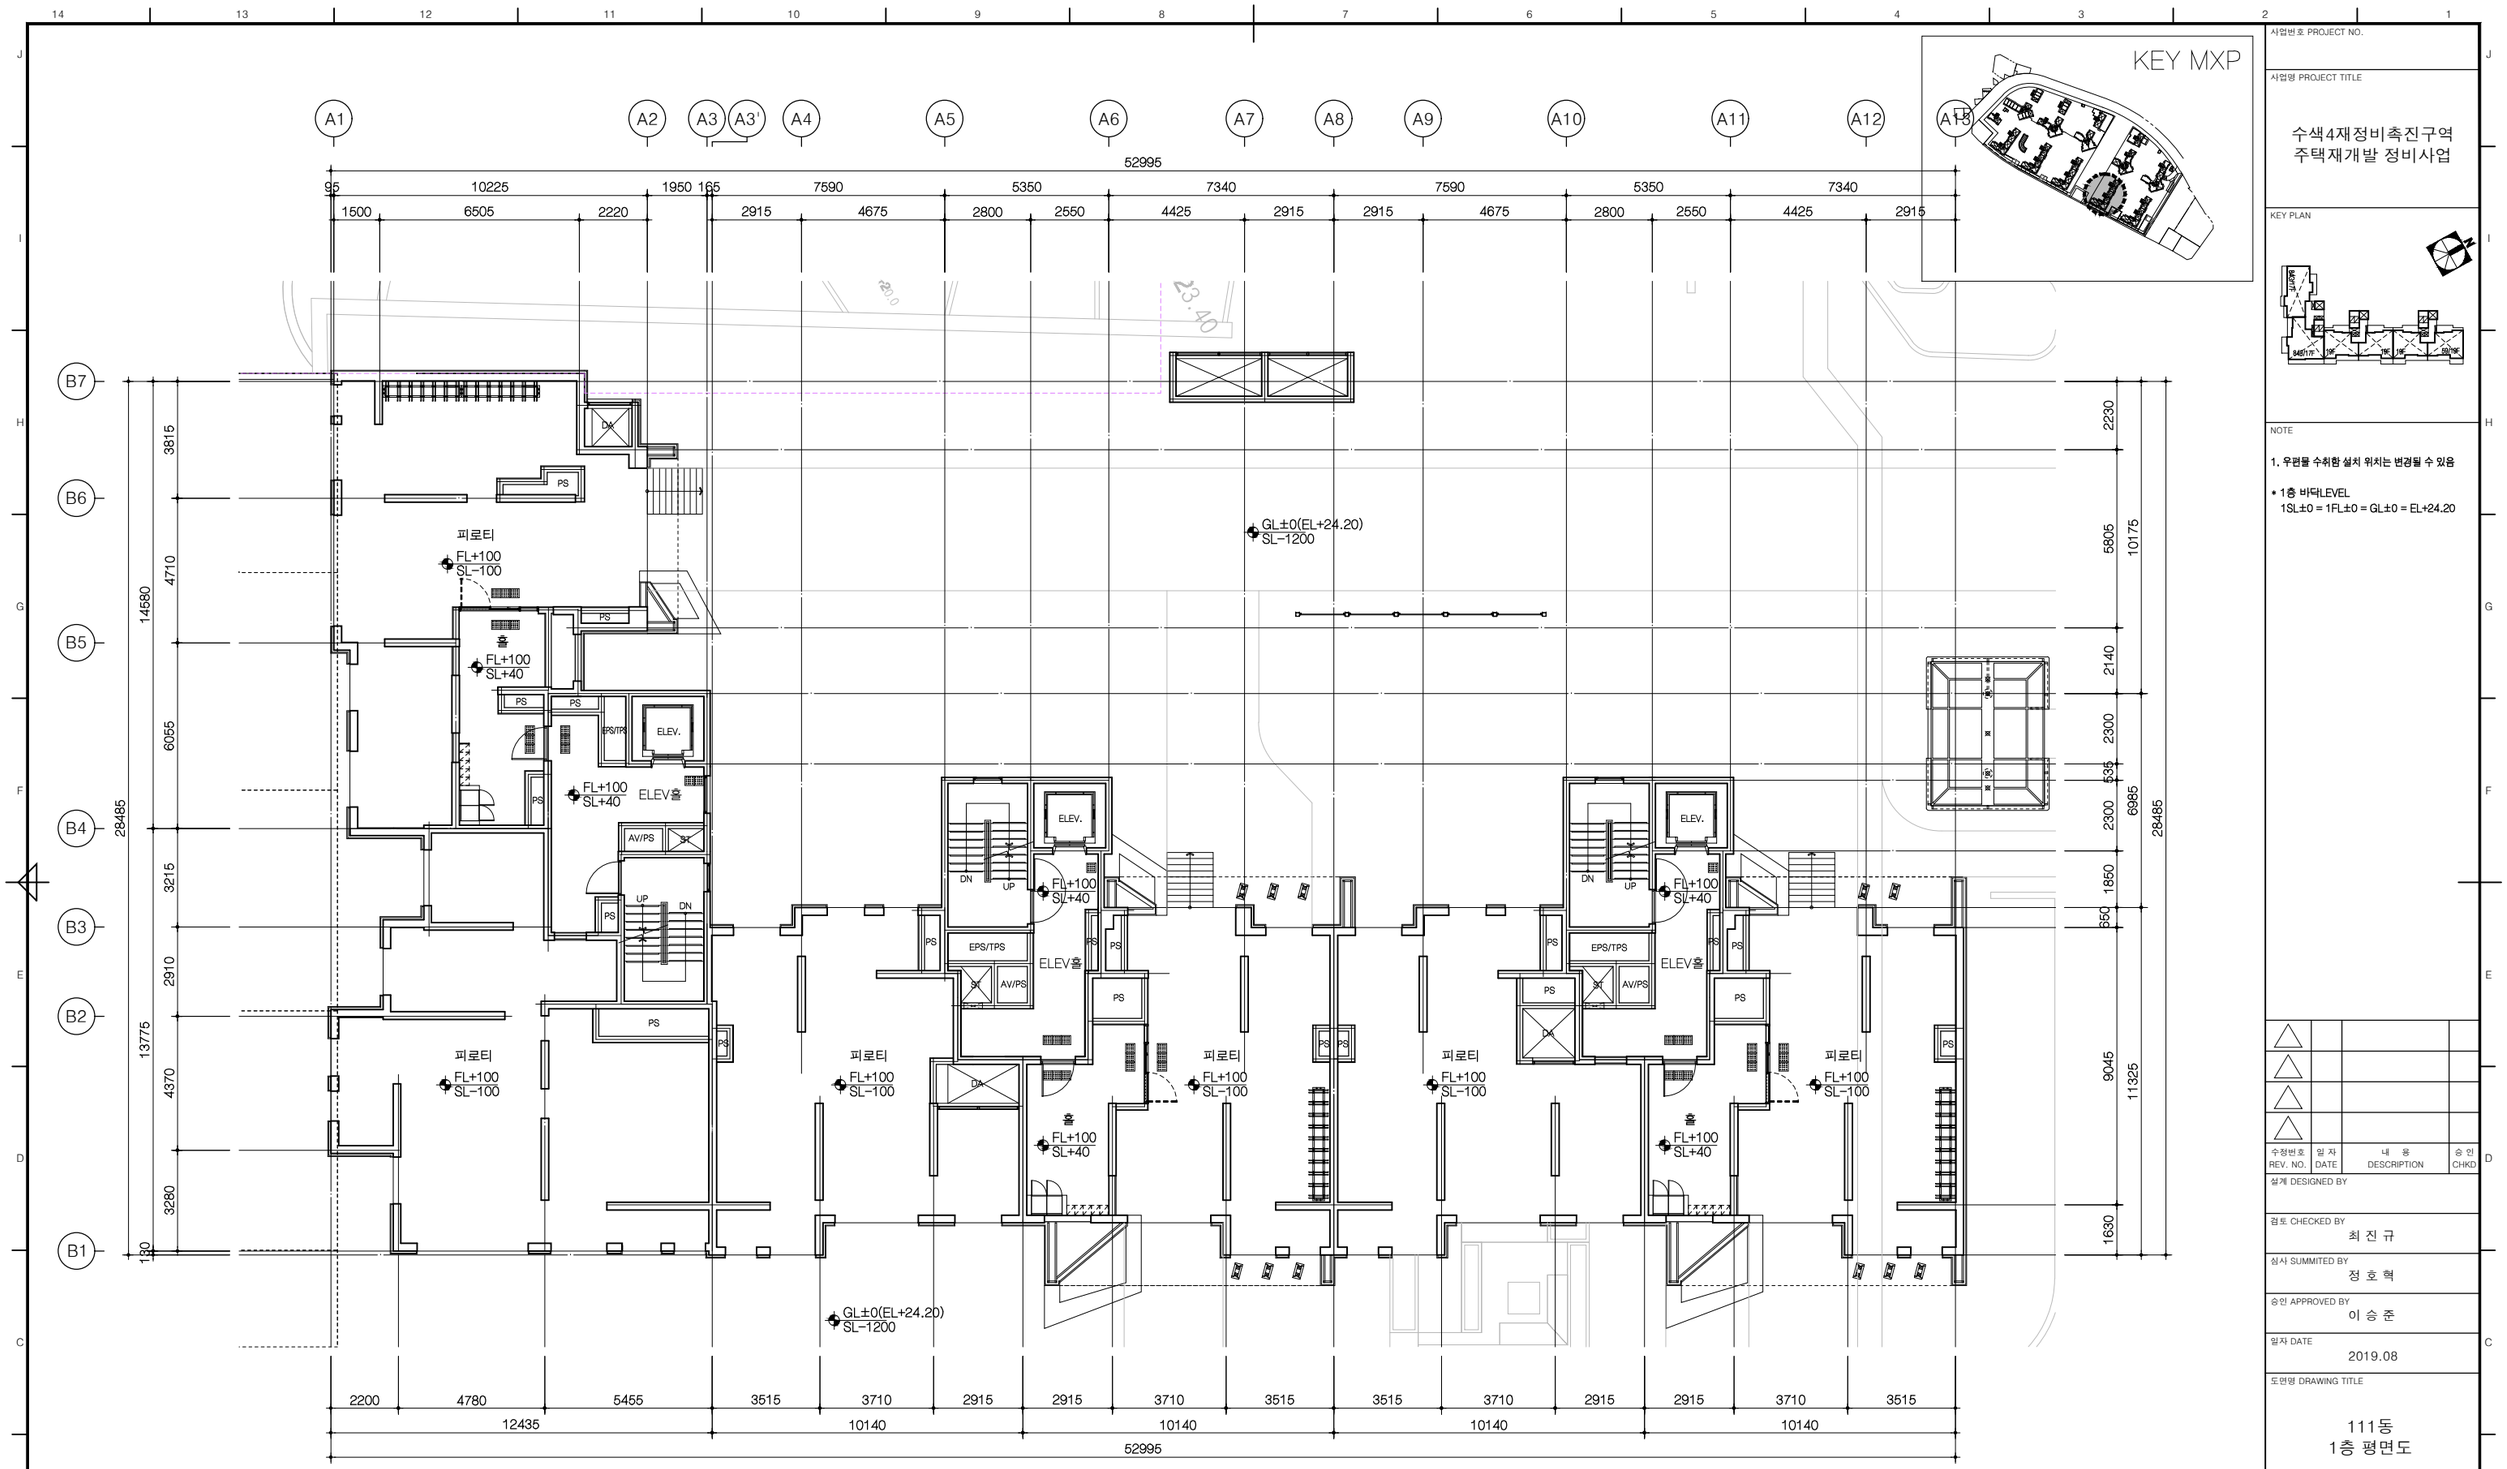

KEY MXP

111동 1층 평면도

축척 = 1/100

사업번호 PROJECT NO.

사업명 PROJECT TITLE

수색4재정비촉진구역
주택재개발 정비사업

KEY PLAN

NOTE

1. 우려물 수취함 설치 위치는 변경될 수 있음

• 1층 바닥LEVEL
1SL±0 = 1FL±0 = GL±0 = EL+24.20

수정번호 REV. NO.	일 자 DATE	내 용 DESCRIPTION	승 인 CHKD
△			
△			
△			
△			

설계 DESIGNED BY

검토 CHECKED BY
최 진 규

심사 SUMMITED BY
정 호 혁

승인 APPROVED BY
이 승 준

일자 DATE
2019.08

도면명 DRAWING TITLE
111동
1층 평면도

축 척 SCALE
A1: 1/100
A3: 1/200

도면번호 DRAWING NO.
A-453

일련번호 SHEET NO.

△ REV. NO.

HAUD
(주)하우드엔지니어링
종합건축사사무소
Architects, Planners & Engineers
TEL. 82 2 140 4400, SEOUL, KOREA

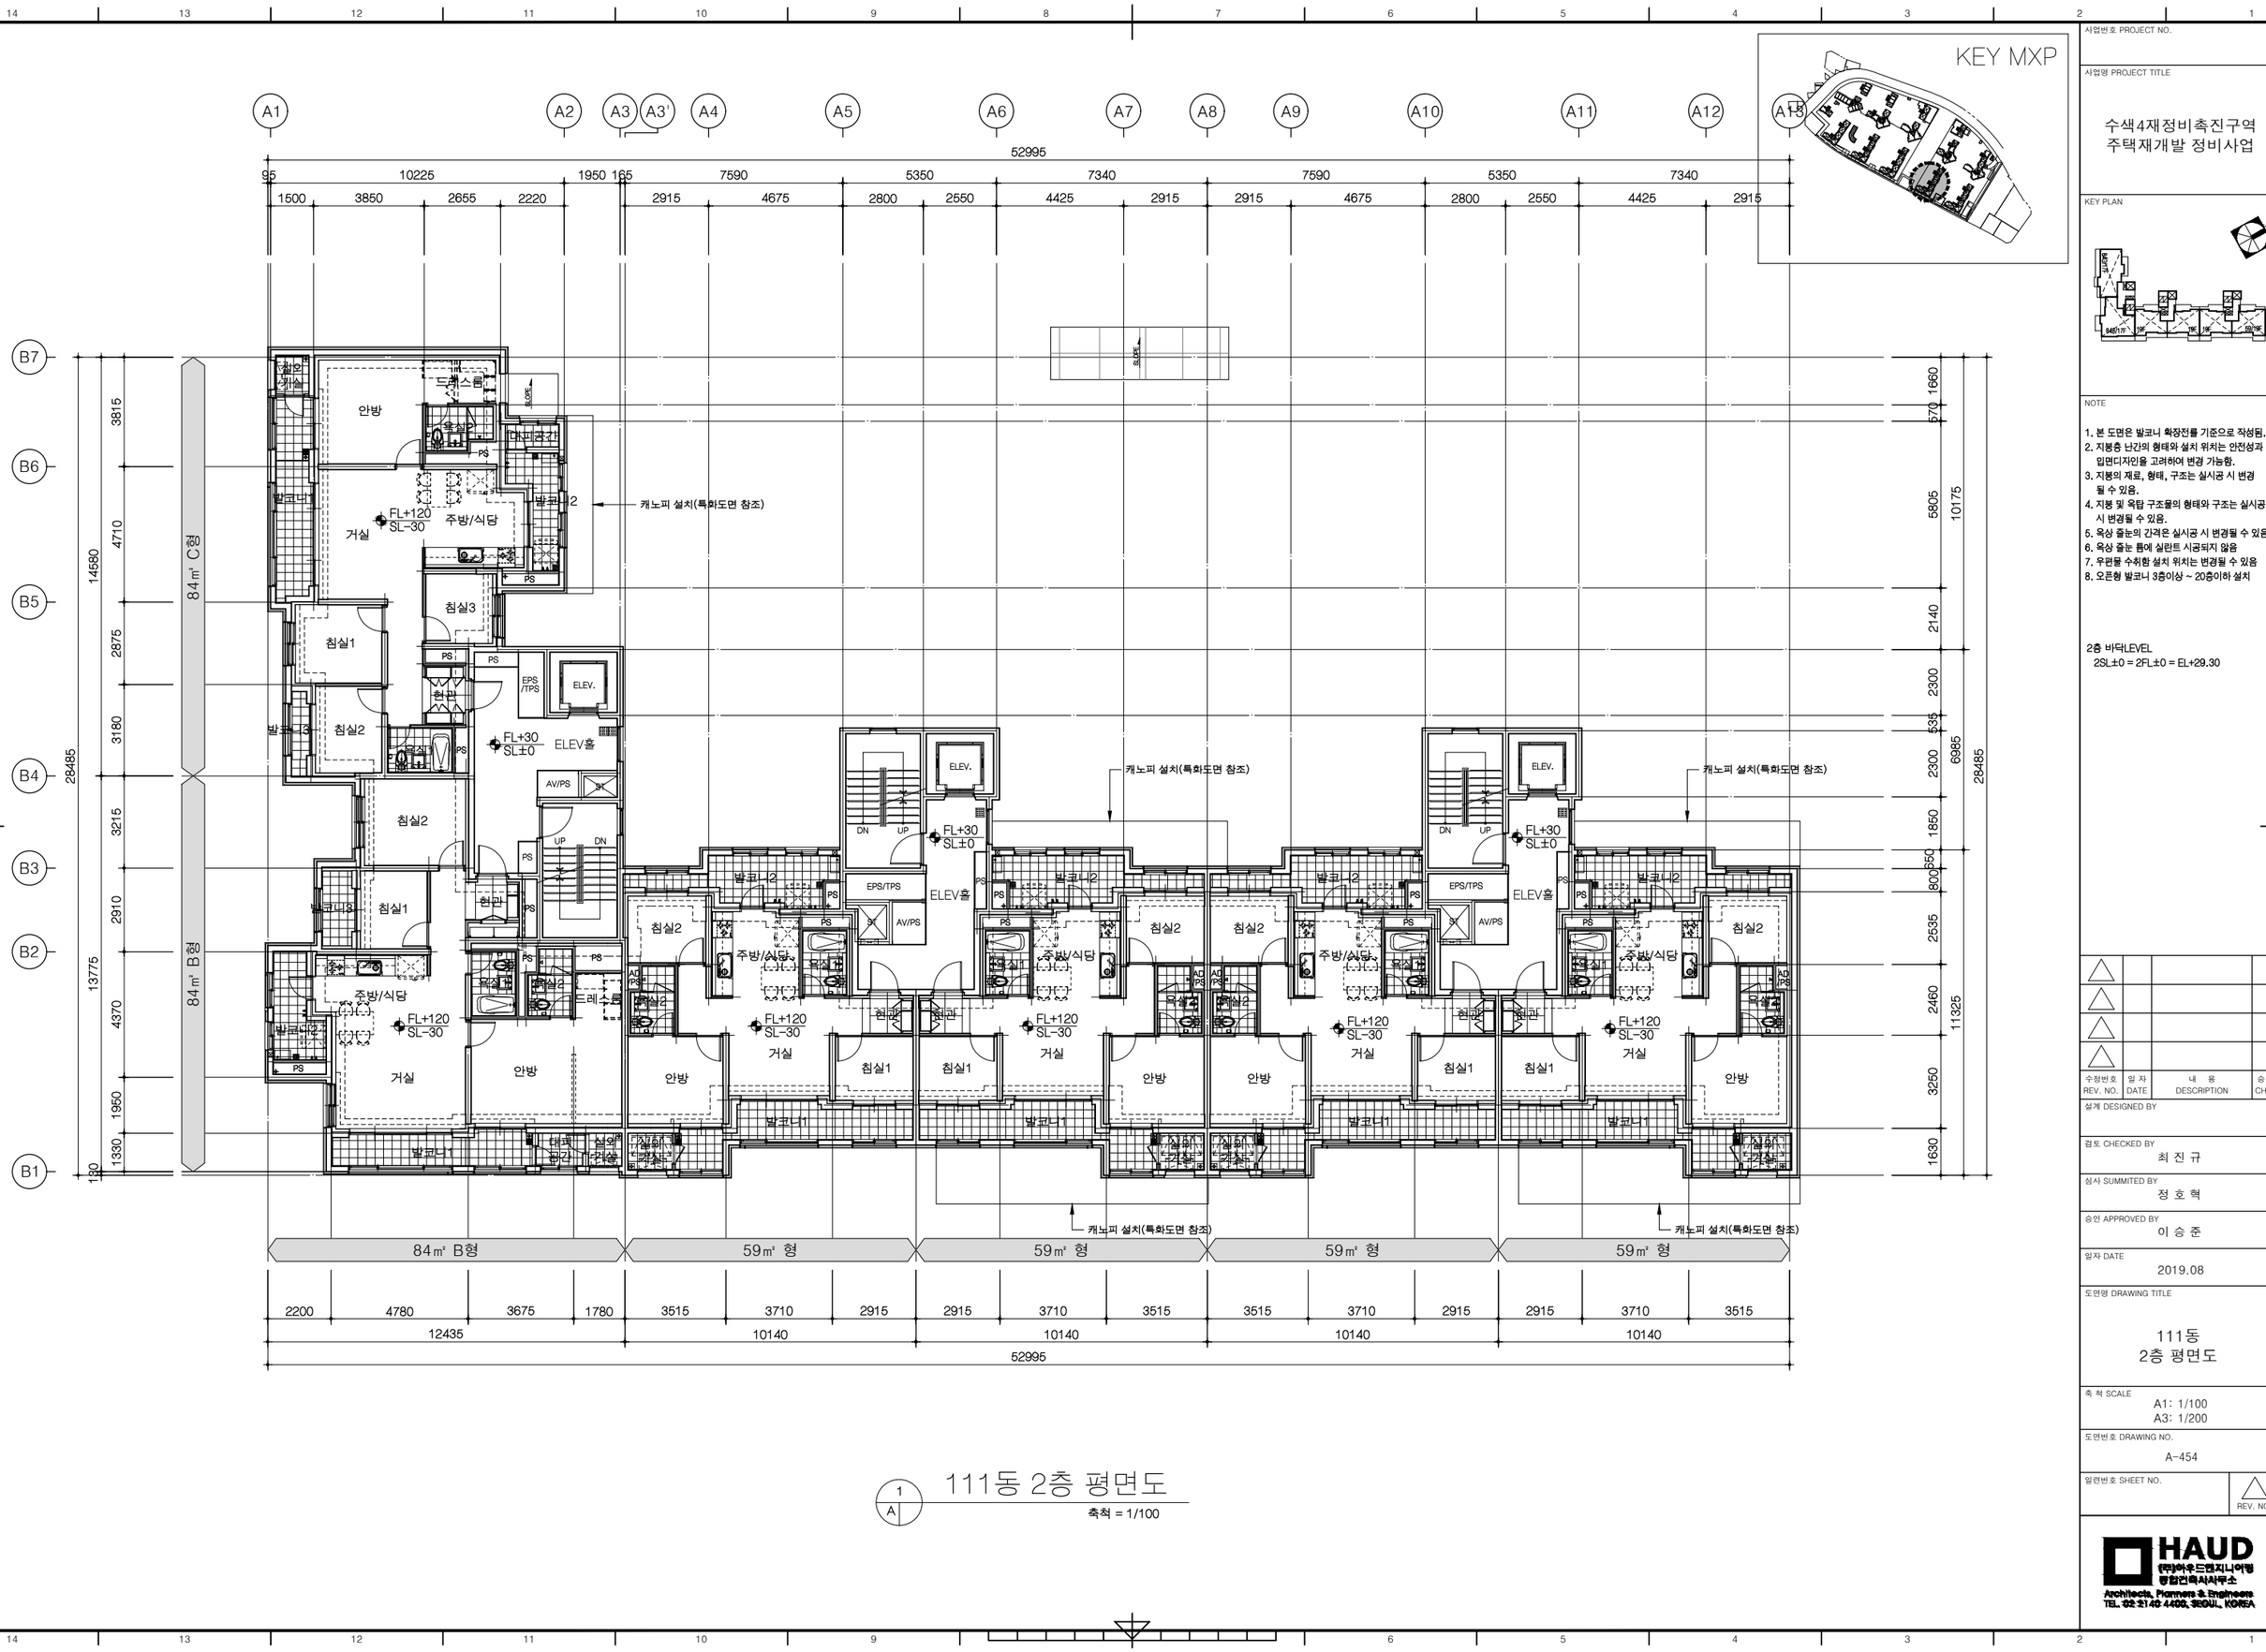

KEY MXP

1
A
111동 2층 평면도
축척 = 1/100

사업번호 PROJECT NO.

사업명 PROJECT TITLE

수색4재정비촉진구역
주택재개발 정비사업

KEY PLAN

NOTE

1. 본 도면은 발코니 확장전를 기준으로 작성됨.
2. 지붕층 난간의 형태와 설치 위치는 안전성과 입면디자인을 고려하여 변경 가능함.
3. 지붕의 재료, 형태, 구조는 실시공 시 변경 될 수 있음.
4. 지붕 및 옥탑 구조물의 형태와 구조는 실시공 시 변경될 수 있음.
5. 옥상 출눈의 간격은 실시공 시 변경될 수 있음.
6. 옥상 출눈 틈에 실란트 시공되지 않음
7. 우편물 수취함 설치 위치는 변경될 수 있음
8. 오픈형 발코니 3층이상 ~ 20층이하 설치

2층 바닥LEVEL
2SL±0 = 2FL±0 = EL+29.30

수정번호 REV. NO.	일 자 DATE	내 용 DESCRIPTION	승 인 CHKD
△			
△			
△			
△			

설계 DESIGNED BY

검토 CHECKED BY
최 진 규

심사 SUMMITED BY
정 호 혁

승인 APPROVED BY
이 승 준

일자 DATE
2019.08

도면명 DRAWING TITLE
111동
2층 평면도

축 척 SCALE
A1: 1/100
A3: 1/200

도면번호 DRAWING NO.
A-454

일련번호 SHEET NO.

△ REV. NO.

HAUD
㈜하우드엔지니어링
종합건축사사무소
Architects, Planners & Engineers
TEL. 02 2140 4400, SEOUL, KOREA

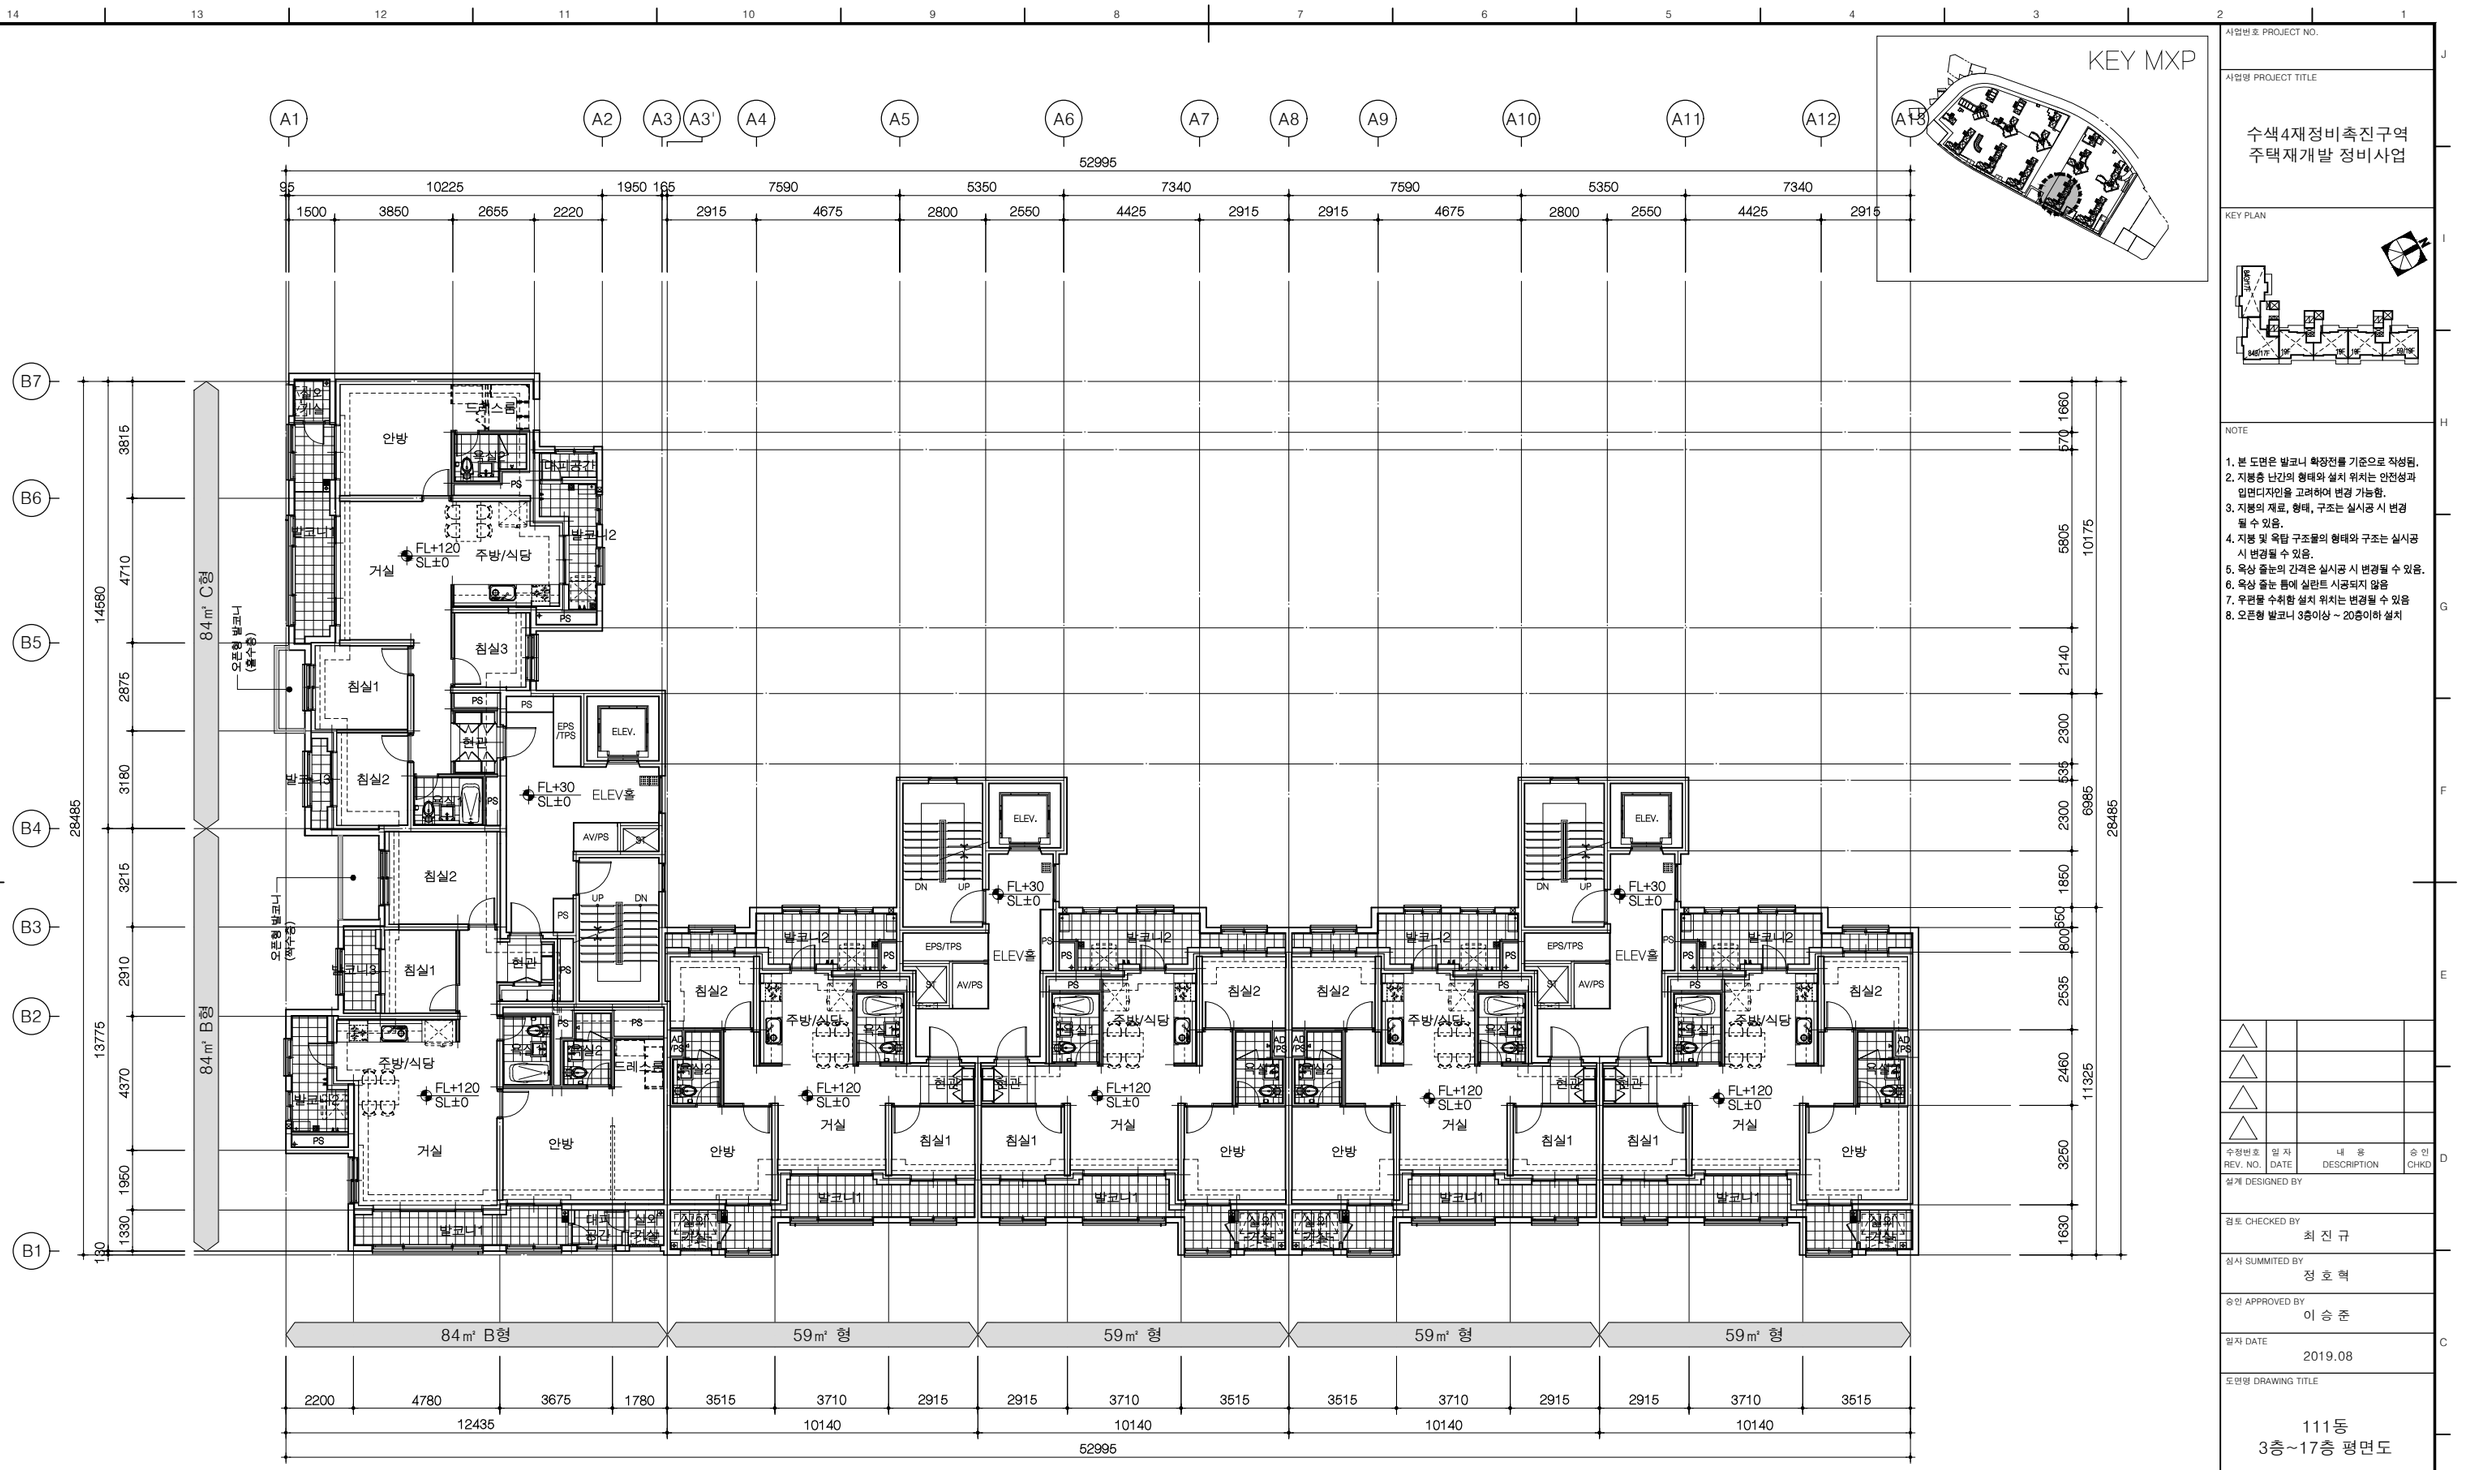

1 A 111동 3~17층 평면도

축척 = 1/100

KEY MXP

사업번호 PROJECT NO.

사업명 PROJECT TITLE

수색4재정비촉진구역
주택재개발 정비사업

KEY PLAN

NOTE

1. 본 도면은 발코니 확장전를 기준으로 작성됨.
2. 지붕층 난간의 형태와 설치 위치는 안전성과 입면디자인을 고려하여 변경 가능함.
3. 지붕의 재료, 형태, 구조는 실시공 시 변경 될 수 있음.
4. 지붕 및 옥탑 구조물의 형태와 구조는 실시공 시 변경될 수 있음.
5. 옥상 출눈의 간격은 실시공 시 변경될 수 있음.
6. 옥상 출눈 틈에 실란트 시공되지 않음
7. 우편물 수취함 설치 위치는 변경될 수 있음
8. 오픈형 발코니 3층이상 ~ 20층이하 설치

수정번호 REV. NO.	일 자 DATE	내 용 DESCRIPTION	승 인 CHKD
△			
△			
△			
△			

설계 DESIGNED BY

검토 CHECKED BY
최 진 규

심사 SUMMITED BY
정 호 혁

승인 APPROVED BY
이 승 준

일자 DATE
2019.08

도면명 DRAWING TITLE
111동
3층~17층 평면도

축 척 SCALE
A1: 1/100
A3: 1/200

도면번호 DRAWING NO.
A-455

일련번호 SHEET NO.

△ REV. NO.

HAUD
㈜하우드엔지니어링
종합건축사사무소
Architects, Planners & Engineers
TEL. 02 2140 4400, SEOUL, KOREA

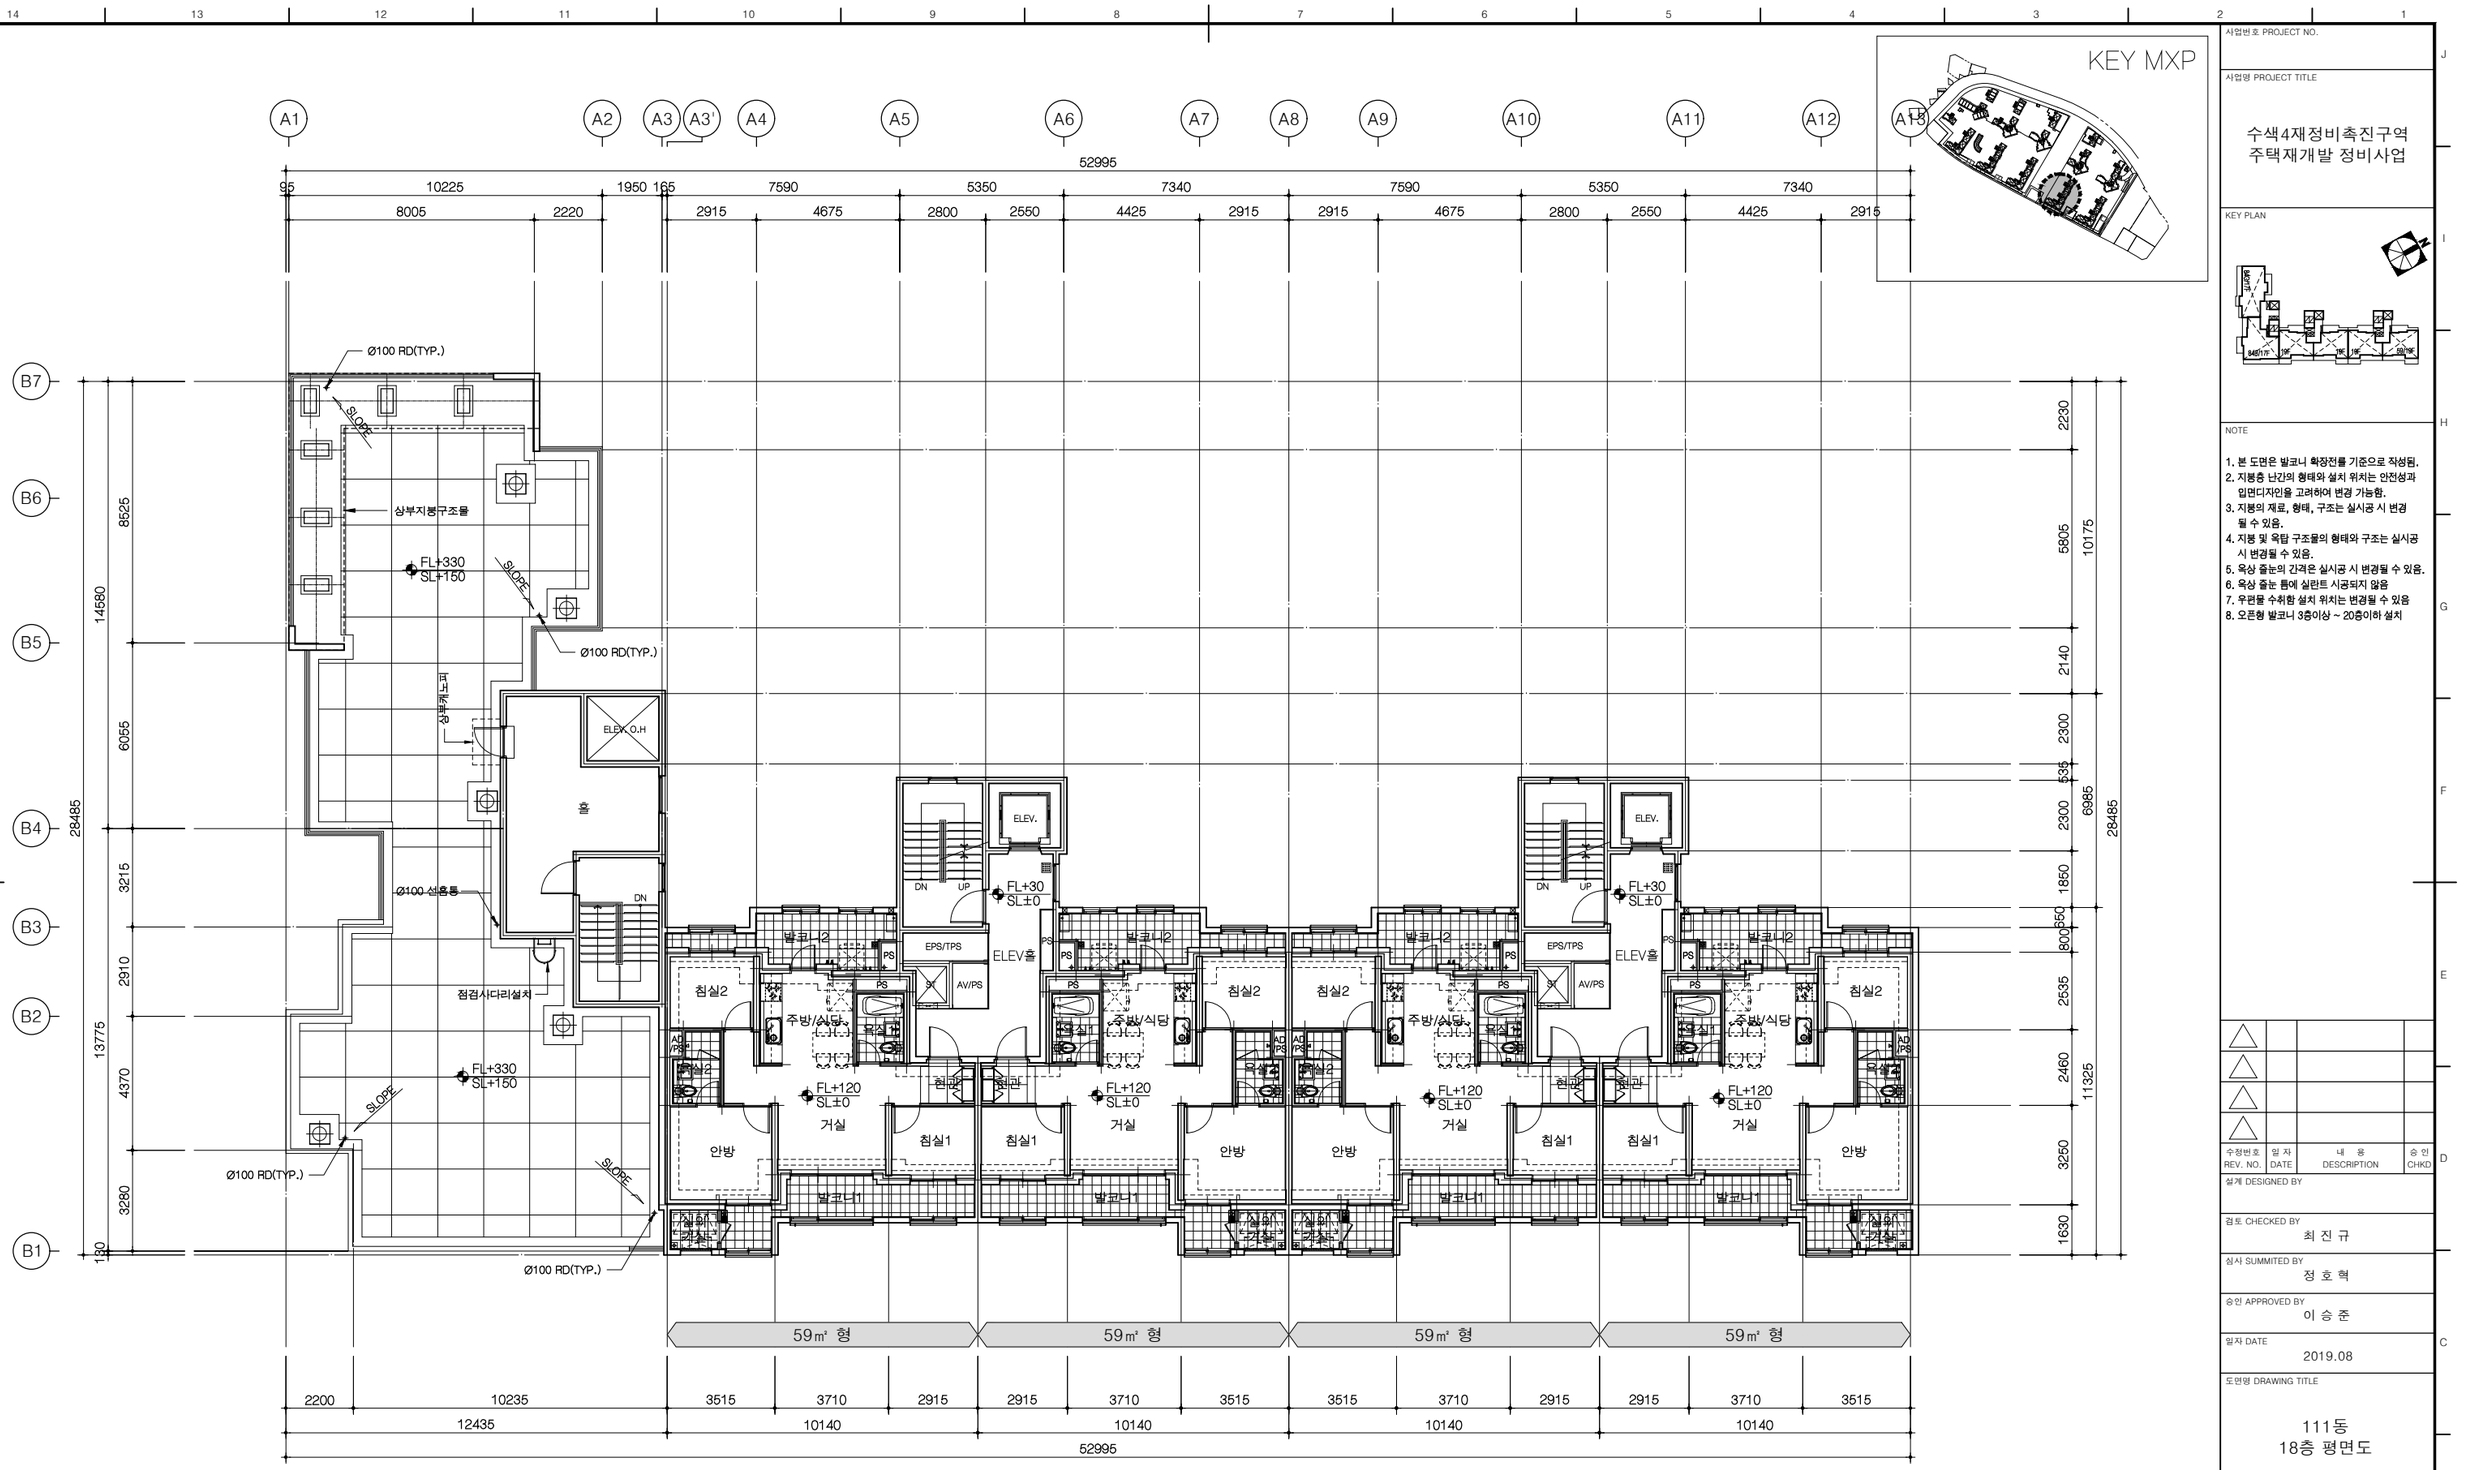

1 A 111동 18층 평면도

축척 = 1/100

사업번호 PROJECT NO.

사업명 PROJECT TITLE

수색4재정비촉진구역
주택재개발 정비사업

KEY PLAN

NOTE

1. 본 도면은 발코니 확장전를 기준으로 작성됨.
2. 지붕층 난간의 형태와 설치 위치는 안전성과 입면디자인을 고려하여 변경 가능함.
3. 지붕의 재료, 형태, 구조는 실시공 시 변경 될 수 있음.
4. 지붕 및 옥탑 구조물의 형태와 구조는 실시공 시 변경될 수 있음.
5. 옥상 출눈의 간격은 실시공 시 변경될 수 있음.
6. 옥상 출눈 틈에 실란트 시공되지 않음
7. 우편물 수취함 설치 위치는 변경될 수 있음
8. 오픈형 발코니 3층이상 ~ 20층이하 설치

수정번호 REV. NO.	일 자 DATE	내 용 DESCRIPTION	승 인 CHKD
△			
△			
△			
△			

설계 DESIGNED BY

검토 CHECKED BY
최 진 규

심사 SUMMITED BY
정 호 혁

승인 APPROVED BY
이 승 준

일자 DATE
2019.08

도면명 DRAWING TITLE
111동
18층 평면도

축 척 SCALE
A1: 1/100
A3: 1/200

도면번호 DRAWING NO.
A-456

일련번호 SHEET NO. △ REV. NO.

HAUD
㈜하우드엔지니어링
종합건축사사무소
Architects, Planners & Engineers
TEL. 02 2140 4400, SEOUL, KOREA

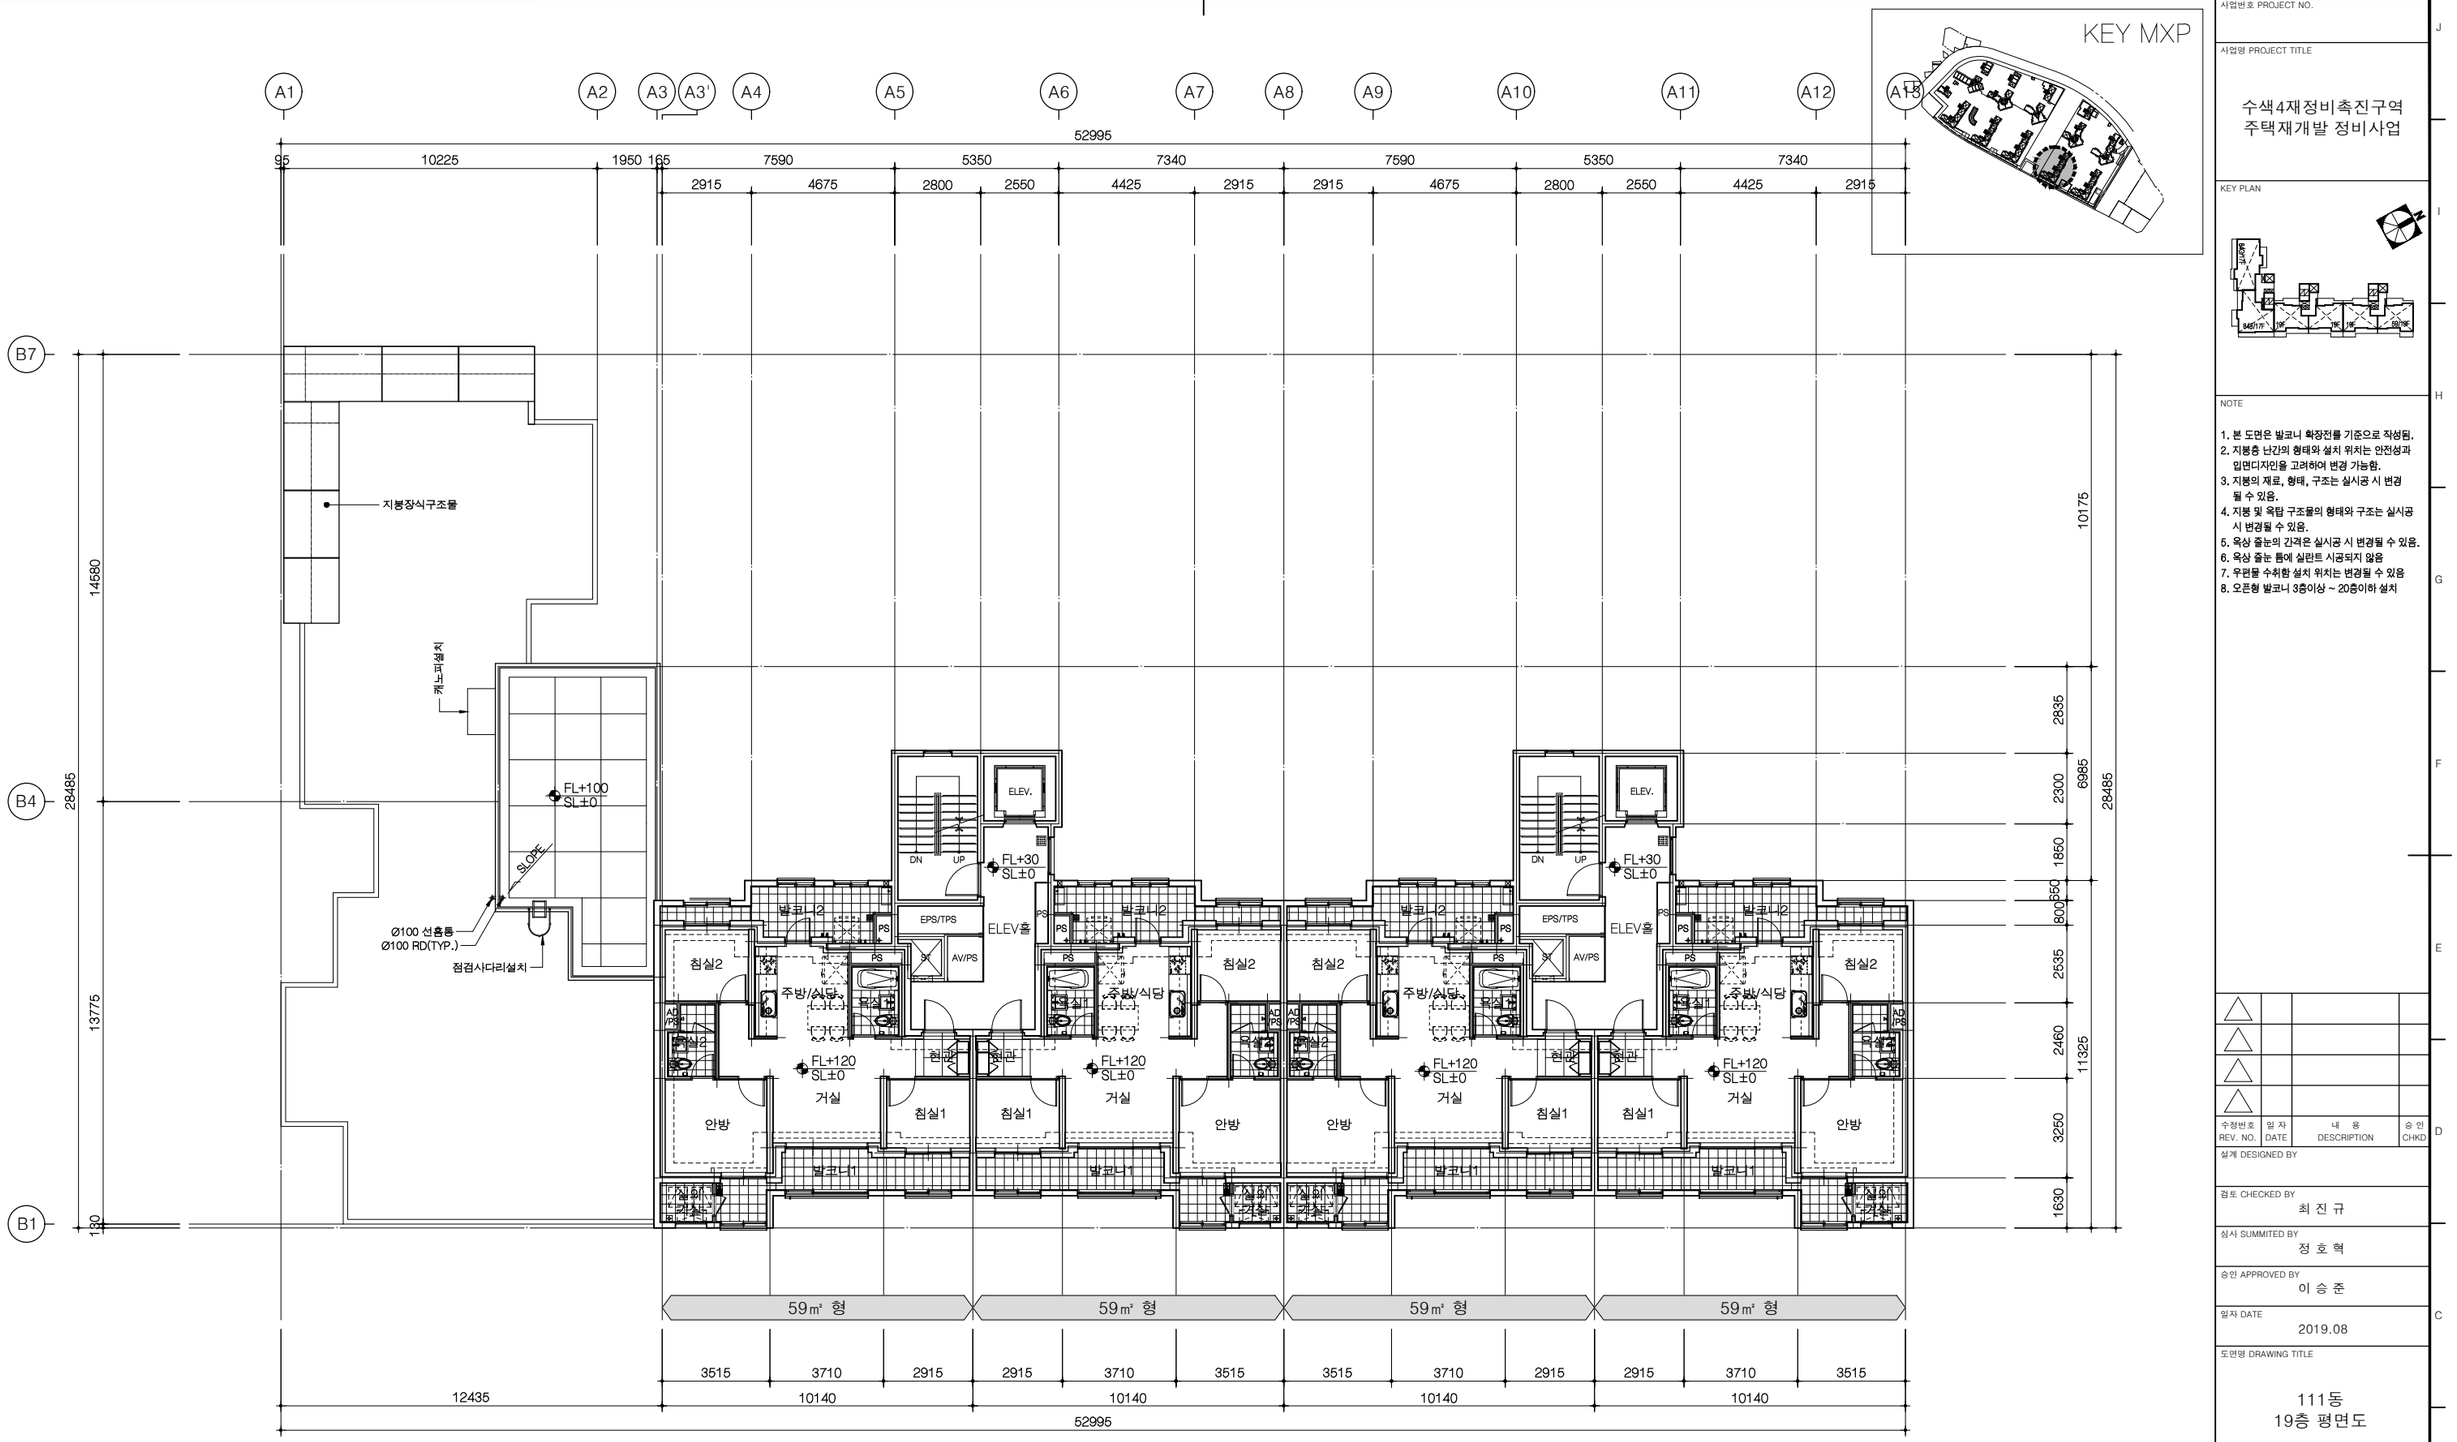

1 A 111동 19층 평면도

축척 = 1/100

KEY MXP

사업번호 PROJECT NO.

사업명 PROJECT TITLE

수색4재정비촉진구역
주택재개발 정비사업

KEY PLAN

NOTE

1. 본 도면은 발코니 확장전를 기준으로 작성됨.
2. 지붕층 난간의 형태와 설치 위치는 안전성과 입면디자인을 고려하여 변경 가능함.
3. 지붕의 재료, 형태, 구조는 실시공 시 변경 될 수 있음.
4. 지붕 및 옥탑 구조물의 형태와 구조는 실시공 시 변경될 수 있음.
5. 옥상 출눈의 간격은 실시공 시 변경될 수 있음.
6. 옥상 출눈 틈에 실란트 시공되지 않음
7. 우편물 수취함 설치 위치는 변경될 수 있음
8. 오픈형 발코니 3층이상 ~ 20층이하 설치

수정번호 REV. NO.	일 자 DATE	내 용 DESCRIPTION	승 인 CHKD
△			
△			
△			
△			

설계 DESIGNED BY

검토 CHECKED BY
최 진 규

심사 SUMMITED BY
정 호 혁

승인 APPROVED BY
이 승 준

일자 DATE
2019.08

도면명 DRAWING TITLE
111동
19층 평면도

축 척 SCALE
A1: 1/100
A3: 1/200

도면번호 DRAWING NO.
A-457

일련번호 SHEET NO.

△ REV. NO.

HAUD
㈜하우드엔지니어링
종합건축사사무소
Architects, Planners & Engineers
TEL. 02 2140 4466, SEOUL, KOREA

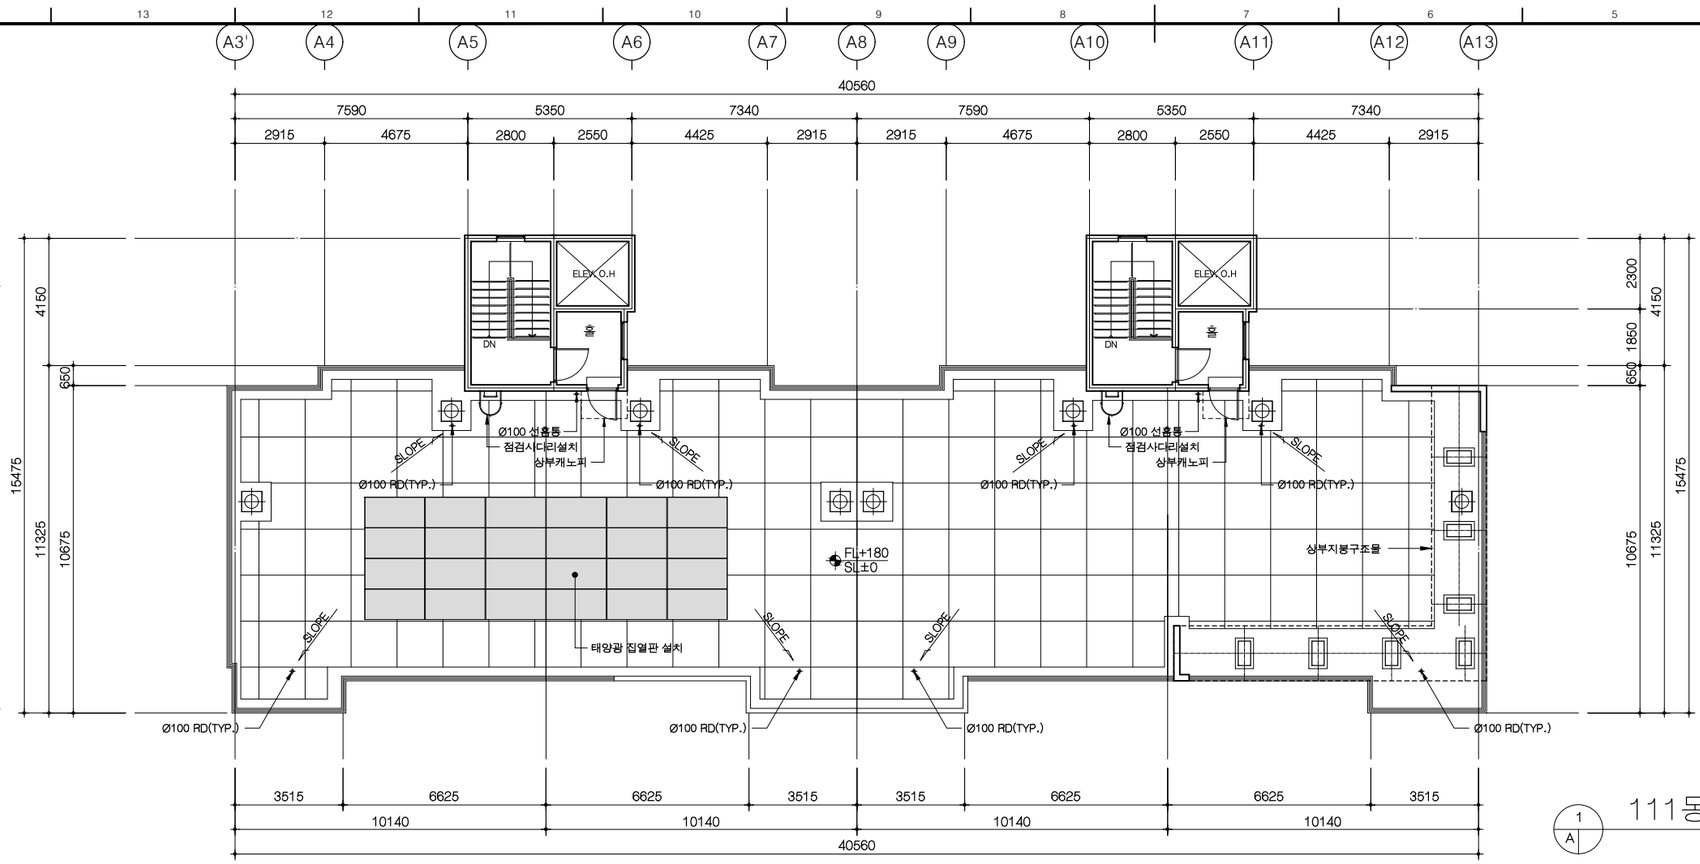

1 A 111동 지붕 평면도

축척 = 1/100

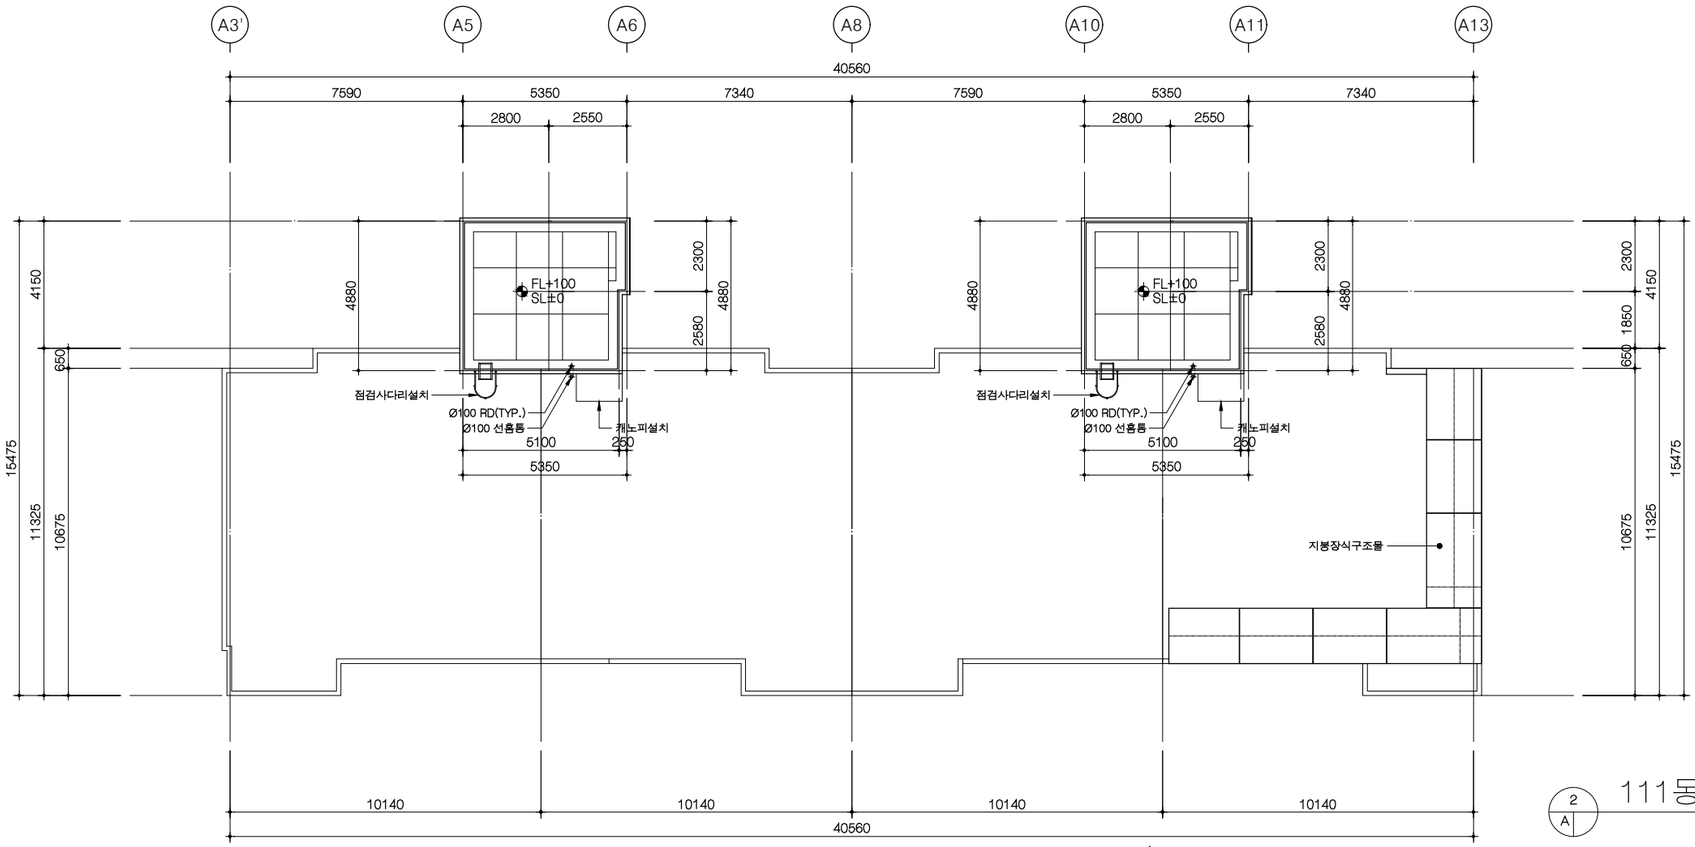

2 A 111동 옥탑지붕 평면도

축척 = 1/100

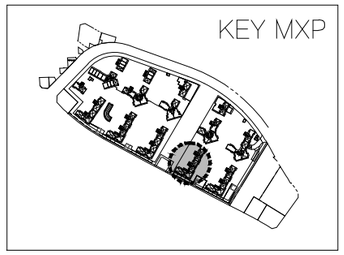

사업번호 PROJECT NO.

사업명 PROJECT TITLE

수색4재정비촉진구역
주택재개발 정비사업

KEY PLAN

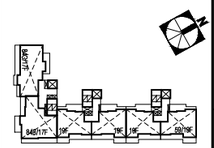

NOTE

1. 지붕바닥
   ① EXP. JOINT: 3000 X 3000
2. 본 평면도는 발코니확장전을 기준으로 작성됨
3. 재료마감은 실내,외 재료마감표 참조
4. 지붕 난간형태/설치위치는 안전성과 입면을 고려하여 실시공시 변경될 수 있음
5. 지붕재료 및 형태,구조는 실시공시 변경될수 있음
6. 지붕(옥탑지붕)의 배수드레인,청소용고리, 베기탑,점검사다리(점검구) 등의 설치위치/개소는 실시공시 변경될 수 있음
7. 옥상 상부구조물은 PC구조물 임.
8. 정화조 배기는 기계도서 참조

수정번호 REV. NO.	일 자 DATE	내 용 DESCRIPTION	승 인 CHKD
△			
△			
△			
△			

설계 DESIGNED BY

검토 CHECKED BY
최 진 규

심사 SUMMITED BY
정 호 혁

승인 APPROVED BY
이 승 준

일자 DATE
2019.08

도면명 DRAWING TITLE
111동
지붕 및 옥탑지붕 평면도

축 척 SCALE
A1: 1/100
A3: 1/200

도면번호 DRAWING NO.
A-458

일련번호 SHEET NO.

△ REV. NO.

HAUD
(주)하우드엔지니어링
종합건축사사무소
Architects, Planners & Engineers
TEL. 02 2140 4400, SEOUL, KOREA

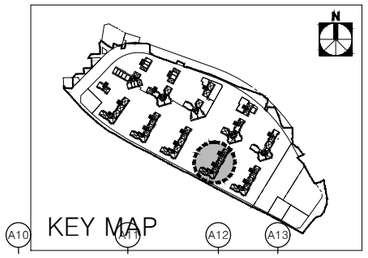

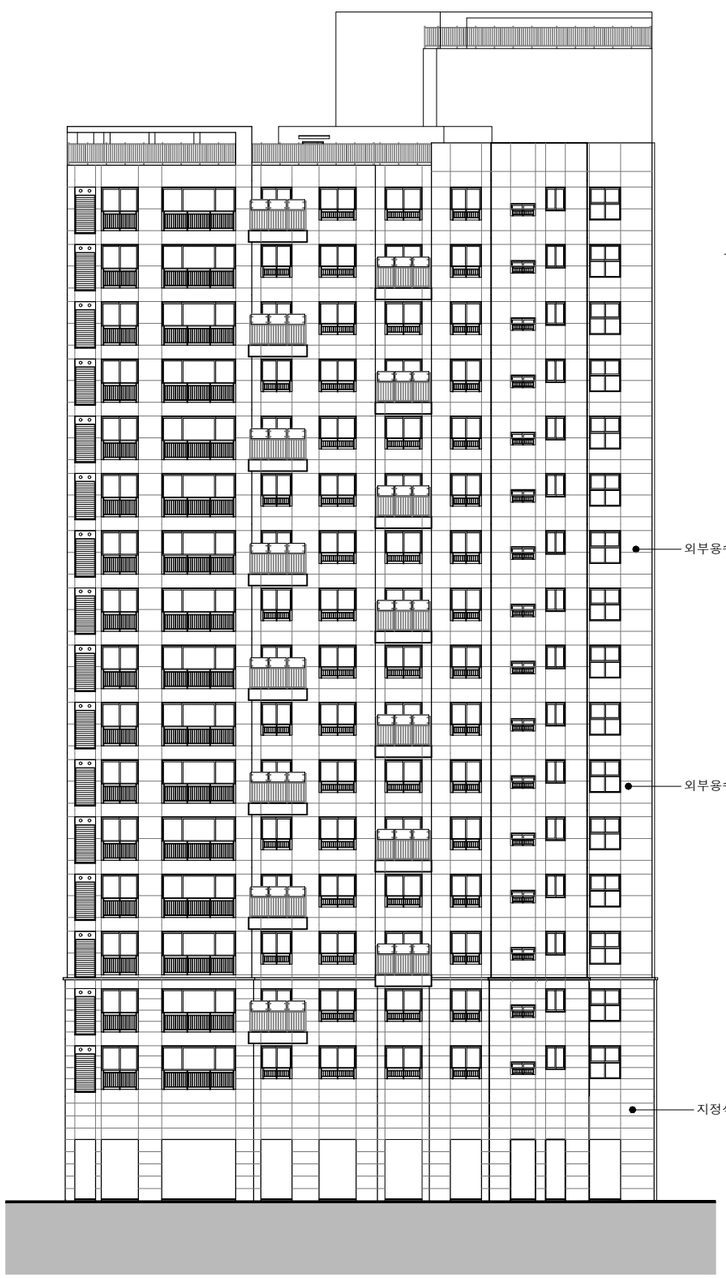

1 A 111동 정면도

축척 = 1/150

2 A 111동 우측면도

축척 = 1/150

사업번호 PROJECT NO.

사업명 PROJECT TITLE

수색4재정비촉진구역
주택재개발 정비사업

KEY PLAN

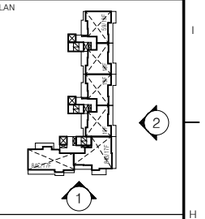

NOTE

1. 1층 바닥 LEVEL
   1SL±0 = 1FL±0 = GL±0 = EL+24.20
2. 지붕 난간의 형태 및 설치위치는 안전성과 입면디자인을 고려하여 변경가능함.
3. 지붕의 재료, 형태, 구조는 실시공시 변경될 수 있음.
4. 지붕 및 옥탑구조물의 형태와 구조는 실시공시 변경될 수 있음.
5. 외벽 및 측벽 문양은 실시공시 변경될 수 있음
6. 입면의 줄눈 및 마감선은 실시공시 변경될 수 있음.
7. 저층부 석재마감 및 입면 마감 색상, 재료에 대한 모든 기준은 특화도면을 우선 적용함.

수정번호 REV. NO.	일 자 DATE	내 용 DESCRIPTION	승 인 CHKD
△			
△			
△			
△			

설계 DESIGNED BY

검토 CHECKED BY
최 진 규

심사 SUMMITED BY
정 호 혁

승인 APPROVED BY
이 승 준

일자 DATE
2019.08

도면명 DRAWING TITLE
111동 정면도,우측면도

축 척 SCALE
A1: 1/150
A3: 1/300

도면번호 DRAWING NO.
A-459

일련번호 SHEET NO.

△ REV. NO.

HAUD
(주)하우드엔지니어링
종합건축사사무소
Architects, Planners & Engineers
TEL. 82 2140 4400, SEOUL, KOREA

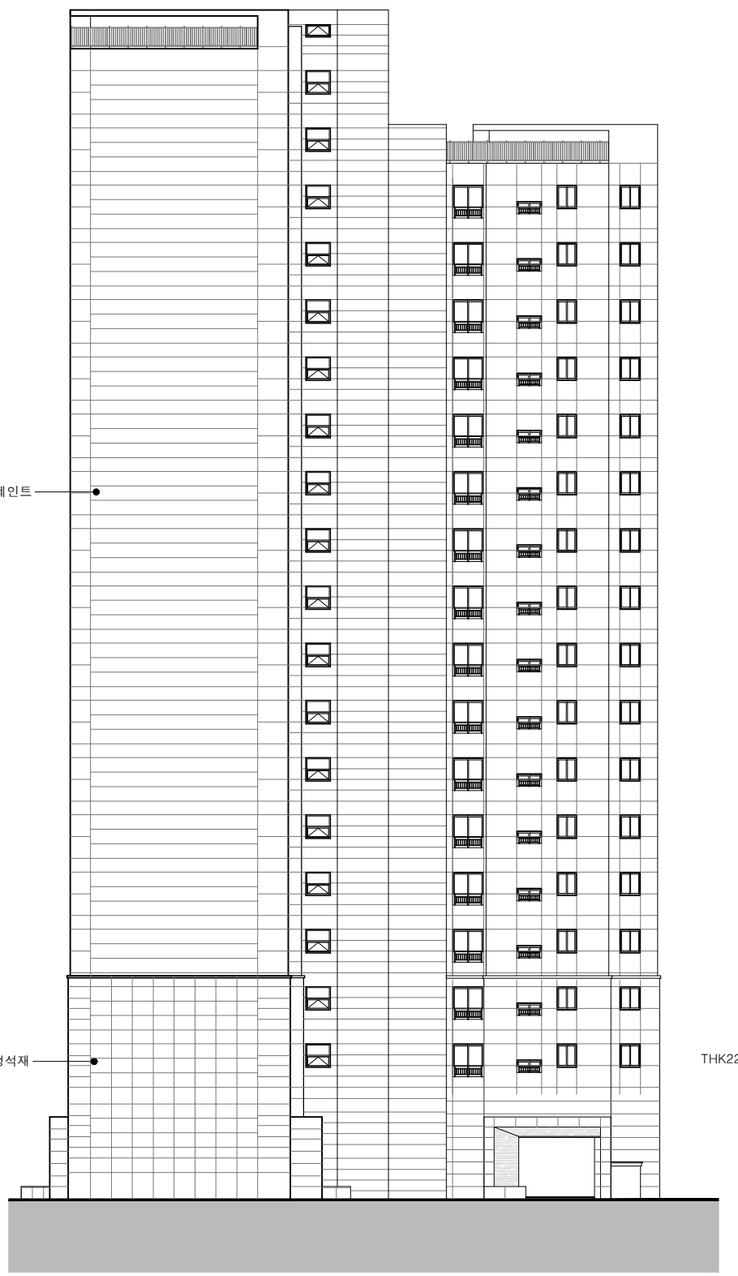

1 A 111동 배면도

축척 = 1/150

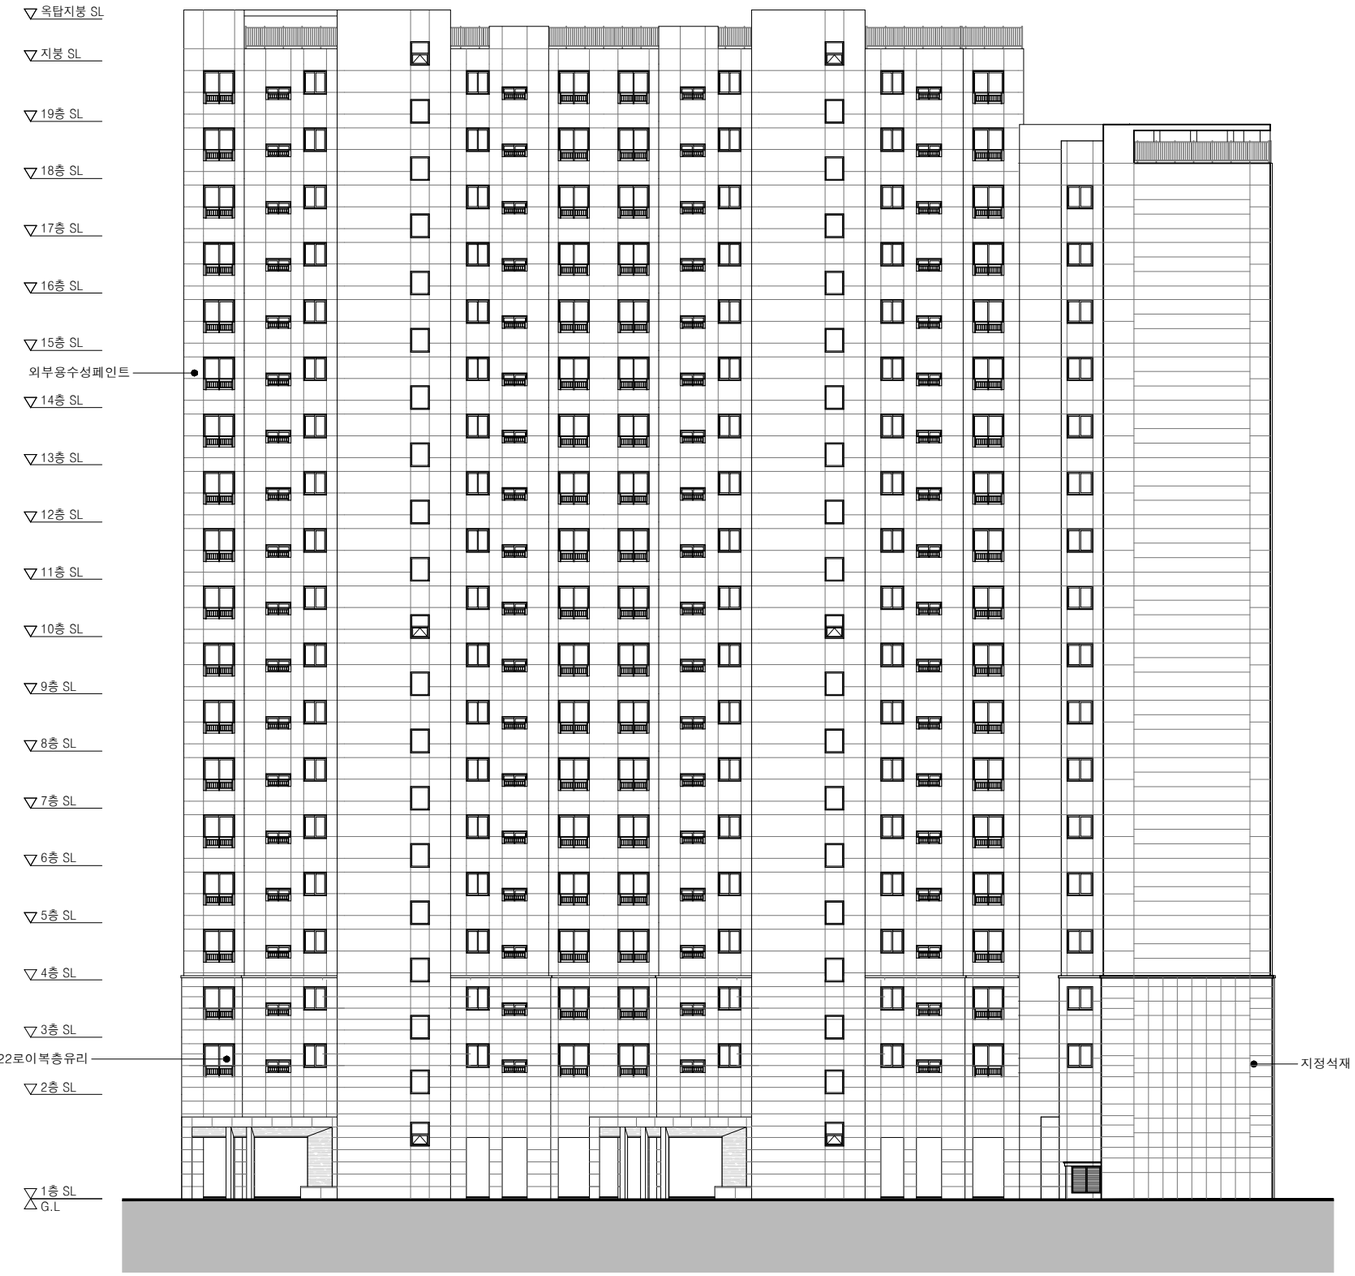

2 A 111동 좌측면도

축척 = 1/150

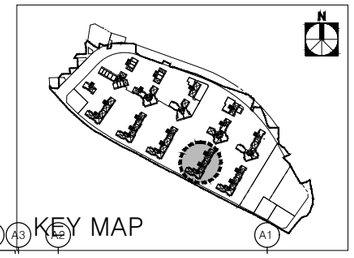

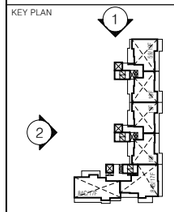

NOTE

1. 1층 바닥 LEVEL
   1SL±0 = 1FL±0 = GL±0 = EL+24.20
2. 지붕 난간의 형태 및 설치위치는 안전성과 입면디자인을 고려하여 변경가능함.
3. 지붕의 재료, 형태, 구조는 실시공시 변경될 수 있음.
4. 지붕 및 옥탑구조물의 형태와 구조는 실시공시 변경될 수 있음.
5. 외벽 및 측벽 문양은 실시공시 변경될 수 있음
6. 입면의 줄눈 및 마감선은 실시공시 변경될 수 있음.
7. 저층부 석재마감 및 입면 마감 색상, 재료에 대한 모든 기준은 특화도면을 우선 적용함.

수정번호 REV. NO.	일 자 DATE	내 용 DESCRIPTION	승 인 CHKD
△			
△			
△			
△			

사업번호 PROJECT NO.

사업명 PROJECT TITLE

수색4재정비촉진구역
주택재개발 정비사업

설계 DESIGNED BY

검토 CHECKED BY
최 진 규

심사 SUMMITED BY
정 호 혁

승인 APPROVED BY
이 승 준

일자 DATE
2019.08

도면명 DRAWING TITLE
111동 배면도,좌측면도

축 척 SCALE
A1: 1/150
A3: 1/300

도면번호 DRAWING NO.
A-460

일련번호 SHEET NO.

△ REV. NO.

HAUD
㈜하우드엔지니어링
종합건축사사무소
Architects, Planners & Engineers
TEL. 02 2140 4466, SEOUL, KOREA

1 A 111동 종단면도

축척 = 1/150

2 A 111동 횡단면도

축척 = 1/150

사업번호 PROJECT NO.

사업명 PROJECT TITLE

수색4재정비촉진구역
주택재개발 정비사업

KEY PLAN

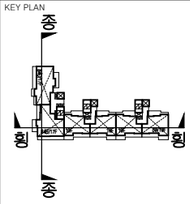

NOTE

수정번호 REV. NO.	일 자 DATE	내 용 DESCRIPTION	승 인 CHKD
△			
△			
△			
△			

설계 DESIGNED BY

검토 CHECKED BY
최 진 규

심사 SUMMITED BY
정 호 혁

승인 APPROVED BY
이 승 준

일자 DATE
2019.08

도면명 DRAWING TITLE
111동 종,횡단면도

축 척 SCALE
A1: 1/150
A3: 1/300

도면번호 DRAWING NO.
A-461

일련번호 SHEET NO. △ REV. NO.

HAUD
㈜하우드엔지니어링
종합건축사사무소
Architects, Planners & Engineers
TEL. 02 2149 4400, SEOUL, KOREA

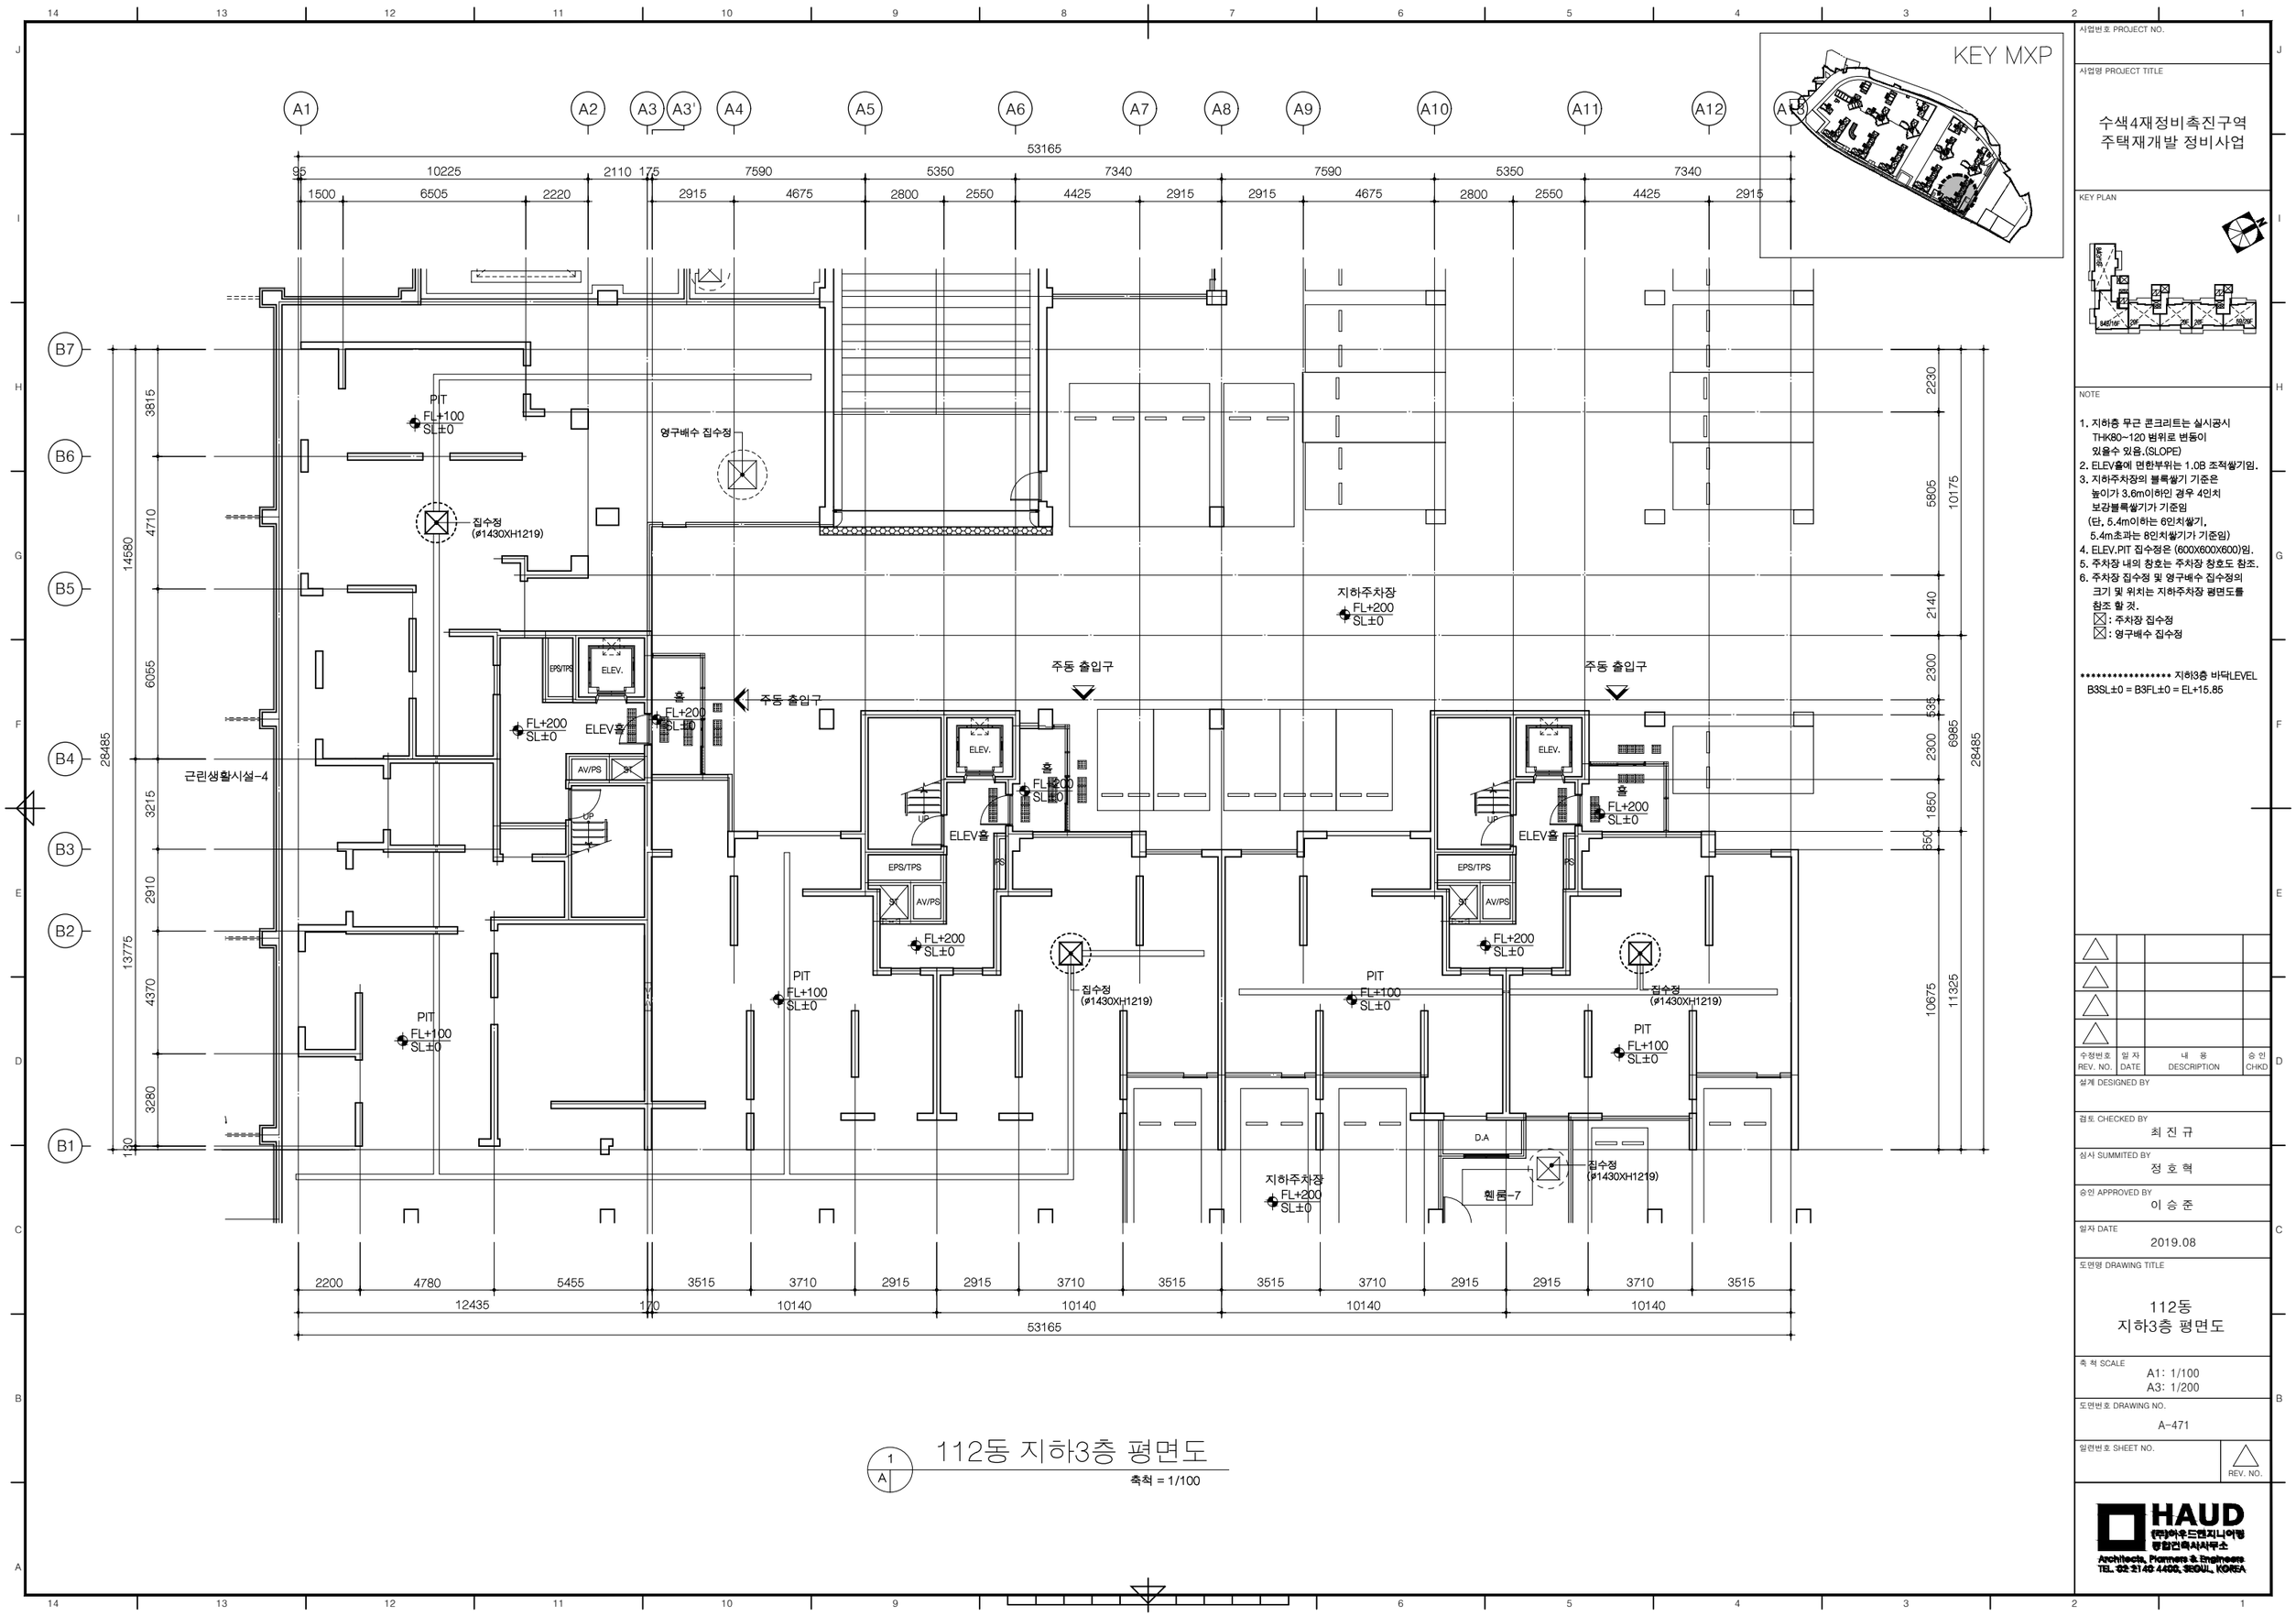

1 A 112동 지하3층 평면도

축척 = 1/100

KEY MXP

사업번호 PROJECT NO.

사업명 PROJECT TITLE

수색4재정비촉진구역
주택재개발 정비사업

KEY PLAN

NOTE

1. 지하층 무근 콘크리트는 실시공시 THK80~120 범위로 변동이 있을수 있음.(SLOPE)
2. ELEV홀에 면한부위는 1.0B 조적쌓기임.
3. 지하주차장의 블록쌓기 기준은 높이가 3.6m이하인 경우 4인치 보강블록쌓기가 기준임 (단, 5.4m이하는 6인치쌓기, 5.4m초과는 8인치쌓기가 기준임)
4. ELEV.PIT 집수정은 (600X600X600)임.
5. 주차장 내의 창호는 주차장 창호도 참조.
6. 주차장 집수정 및 영구배수 집수정의 크기 및 위치는 지하주차장 평면도를 참조 할 것.
   ☒ : 주차장 집수정
   ☒ : 영구배수 집수정

********** 지하3층 바닥LEVEL
B3SL±0 = B3FL±0 = EL+15.85

수정번호 REV. NO.	일 자 DATE	내 용 DESCRIPTION	승 인 CHKD

설계 DESIGNED BY

검토 CHECKED BY 최 진 규

심사 SUMMITED BY 정 호 혁

승인 APPROVED BY 이 승 준

일자 DATE 2019.08

도면명 DRAWING TITLE

112동
지하3층 평면도

축 척 SCALE
A1: 1/100
A3: 1/200

도면번호 DRAWING NO. A-471

일련번호 SHEET NO. REV. NO.

HAUD
(주)하우드엔지니어링
종합건축사사무소
Architects, Planners & Engineers
TEL. 82 2 1 4G 4400, SEOUL, KOREA

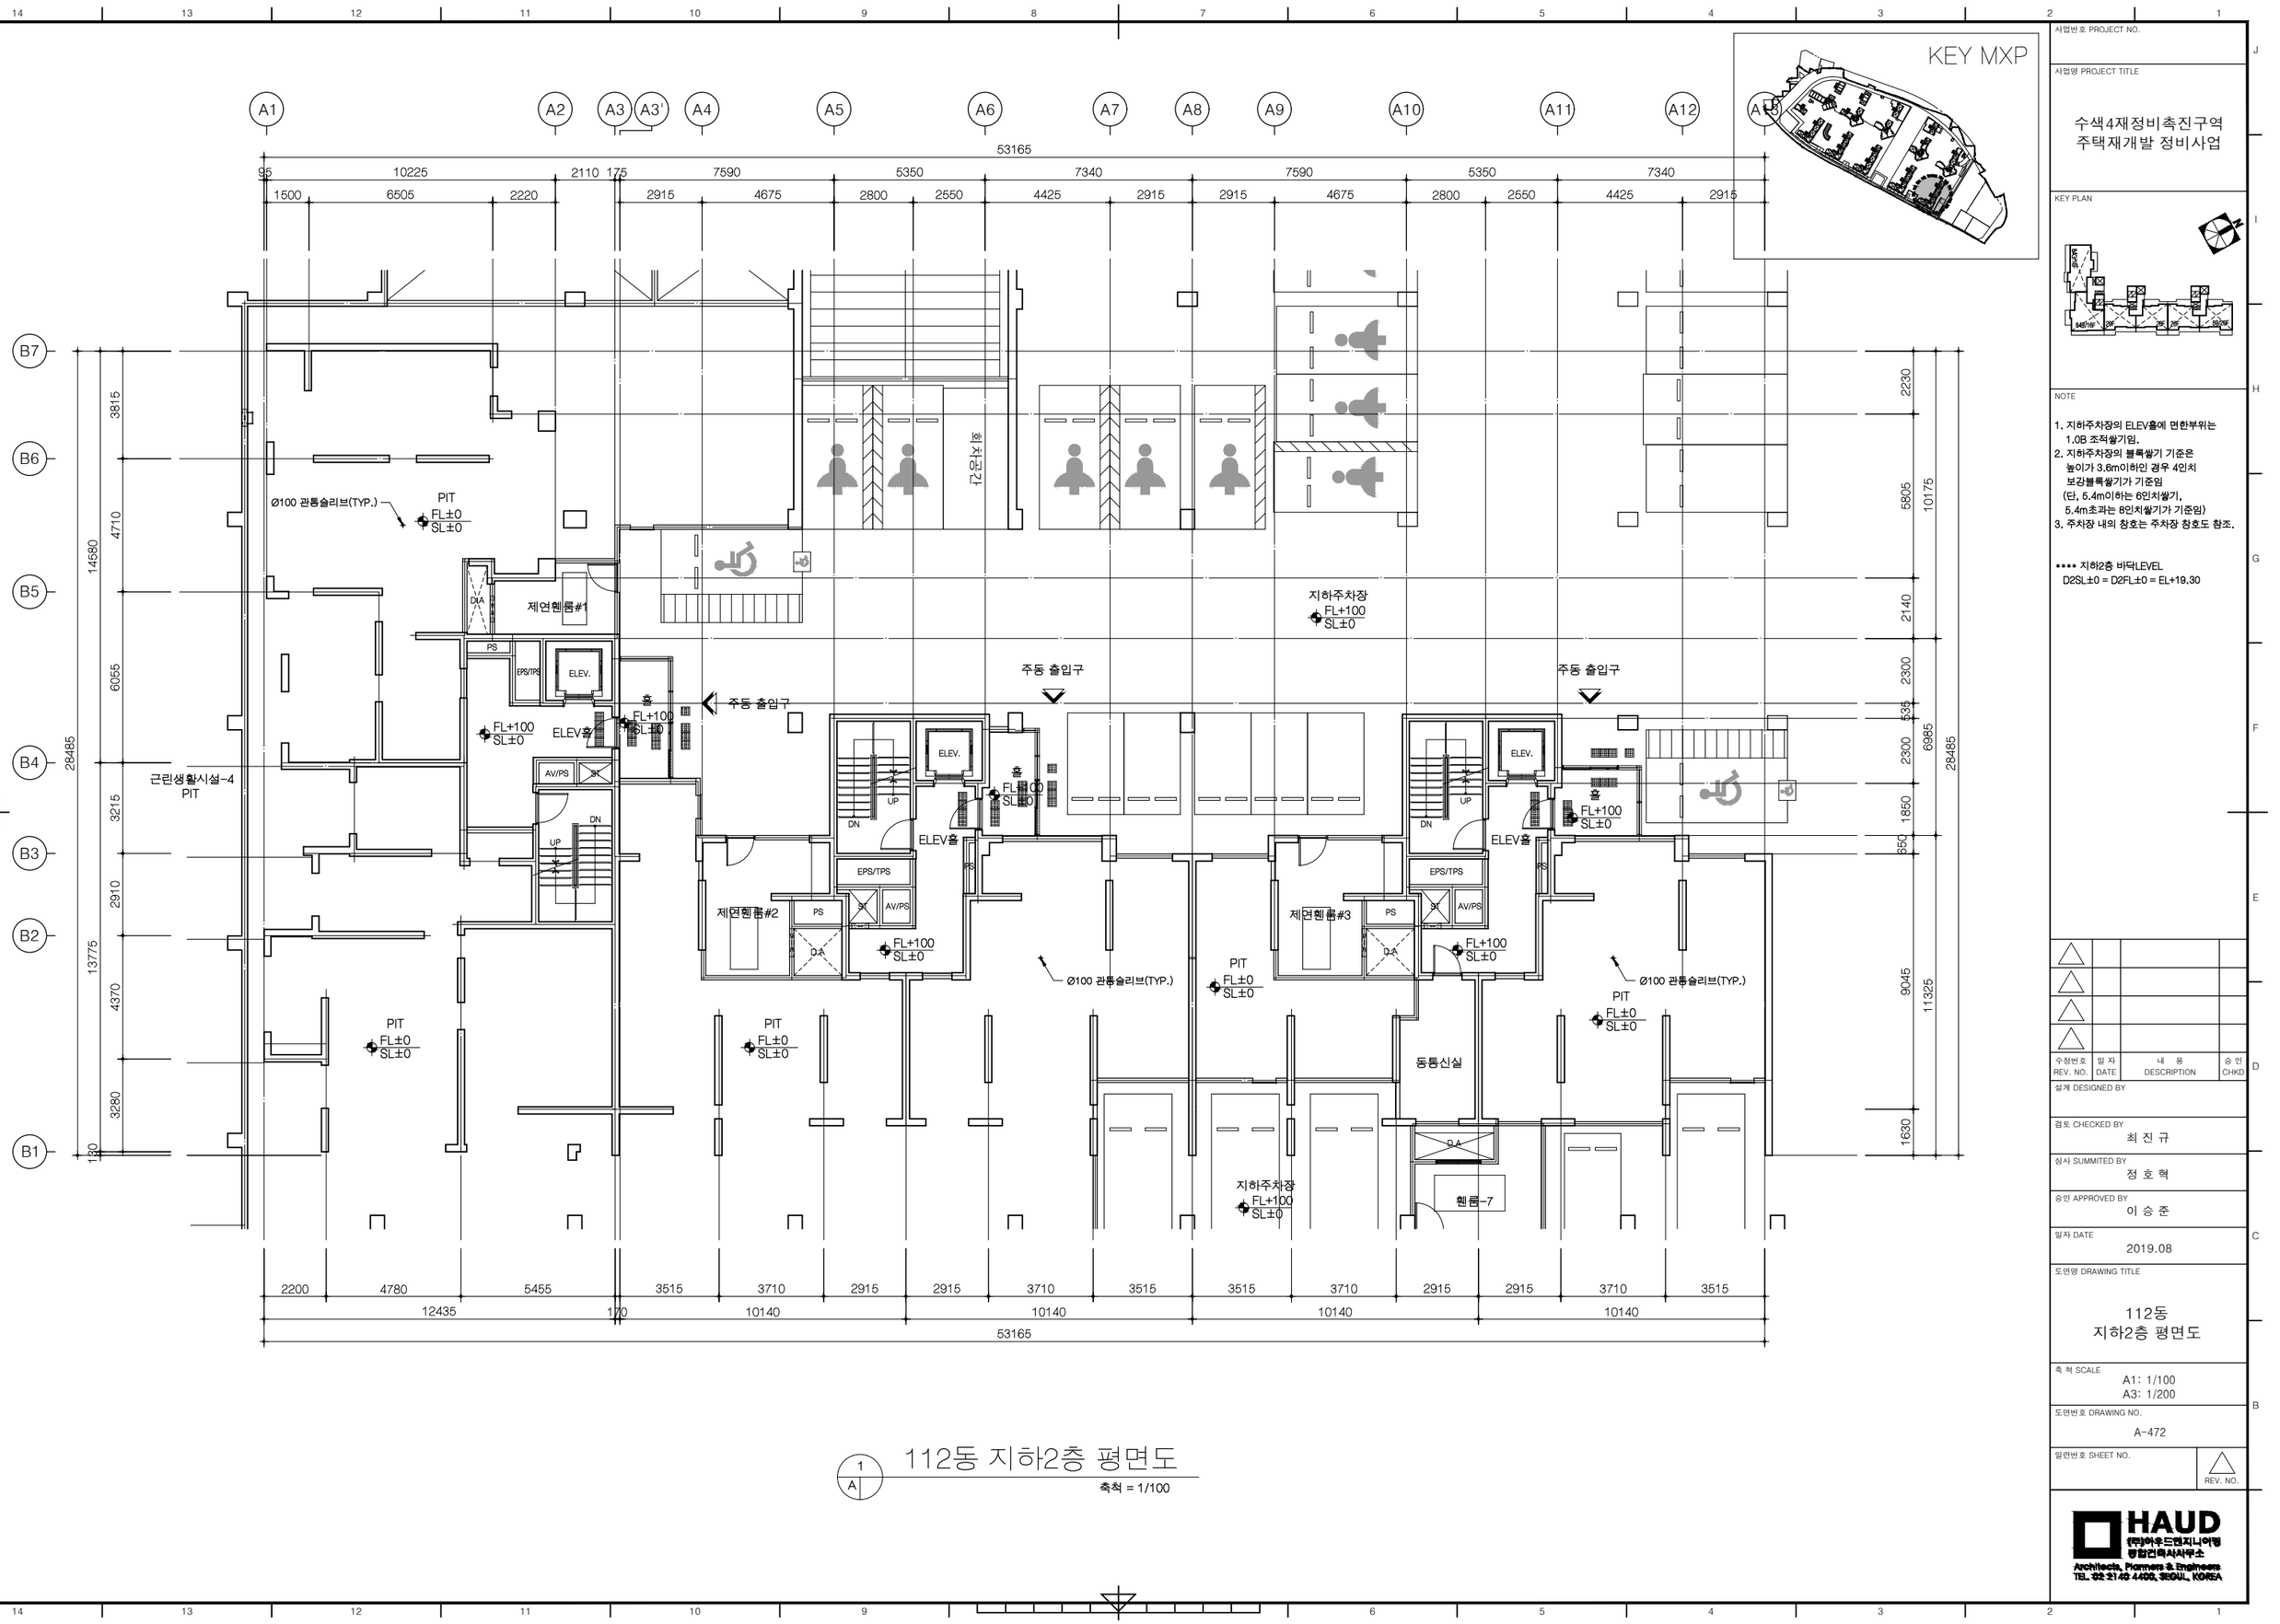

1 A 112동 지하2층 평면도

축척 = 1/100

KEY MXP

사업번호 PROJECT NO.

사업명 PROJECT TITLE

수색4재정비촉진구역
주택재개발 정비사업

KEY PLAN

NOTE

1. 지하주차장의 ELEV홀에 면한부위는 1.0B 조적쌓기임.
2. 지하주차장의 블록쌓기 기준은 높이가 3.6m이하인 경우 4인치 보강블록쌓기가 기준임 (단, 5.4m이하는 6인치쌓기, 5.4m초과는 8인치쌓기가 기준임)
3. 주차장 내의 창호는 주차장 창호도 참조.

**** 지하2층 바닥LEVEL
D2SL±0 = D2FL±0 = EL+19.30

수정번호 REV. NO.	일 자 DATE	내 용 DESCRIPTION	승 인 CHKD
△			
△			
△			
△			

설계 DESIGNED BY

검토 CHECKED BY
최 진 규

심사 SUMMITED BY
정 호 혁

승인 APPROVED BY
이 승 준

일자 DATE
2019.08

도면명 DRAWING TITLE
112동
지하2층 평면도

축 척 SCALE
A1: 1/100
A3: 1/200

도면번호 DRAWING NO.
A-472

일련번호 SHEET NO. △ REV. NO.

HAUD
(주)하우드엔지니어링 종합건축사사무소
Architects, Planners & Engineers
TEL. 02 2140 4400, SEOUL, KOREA

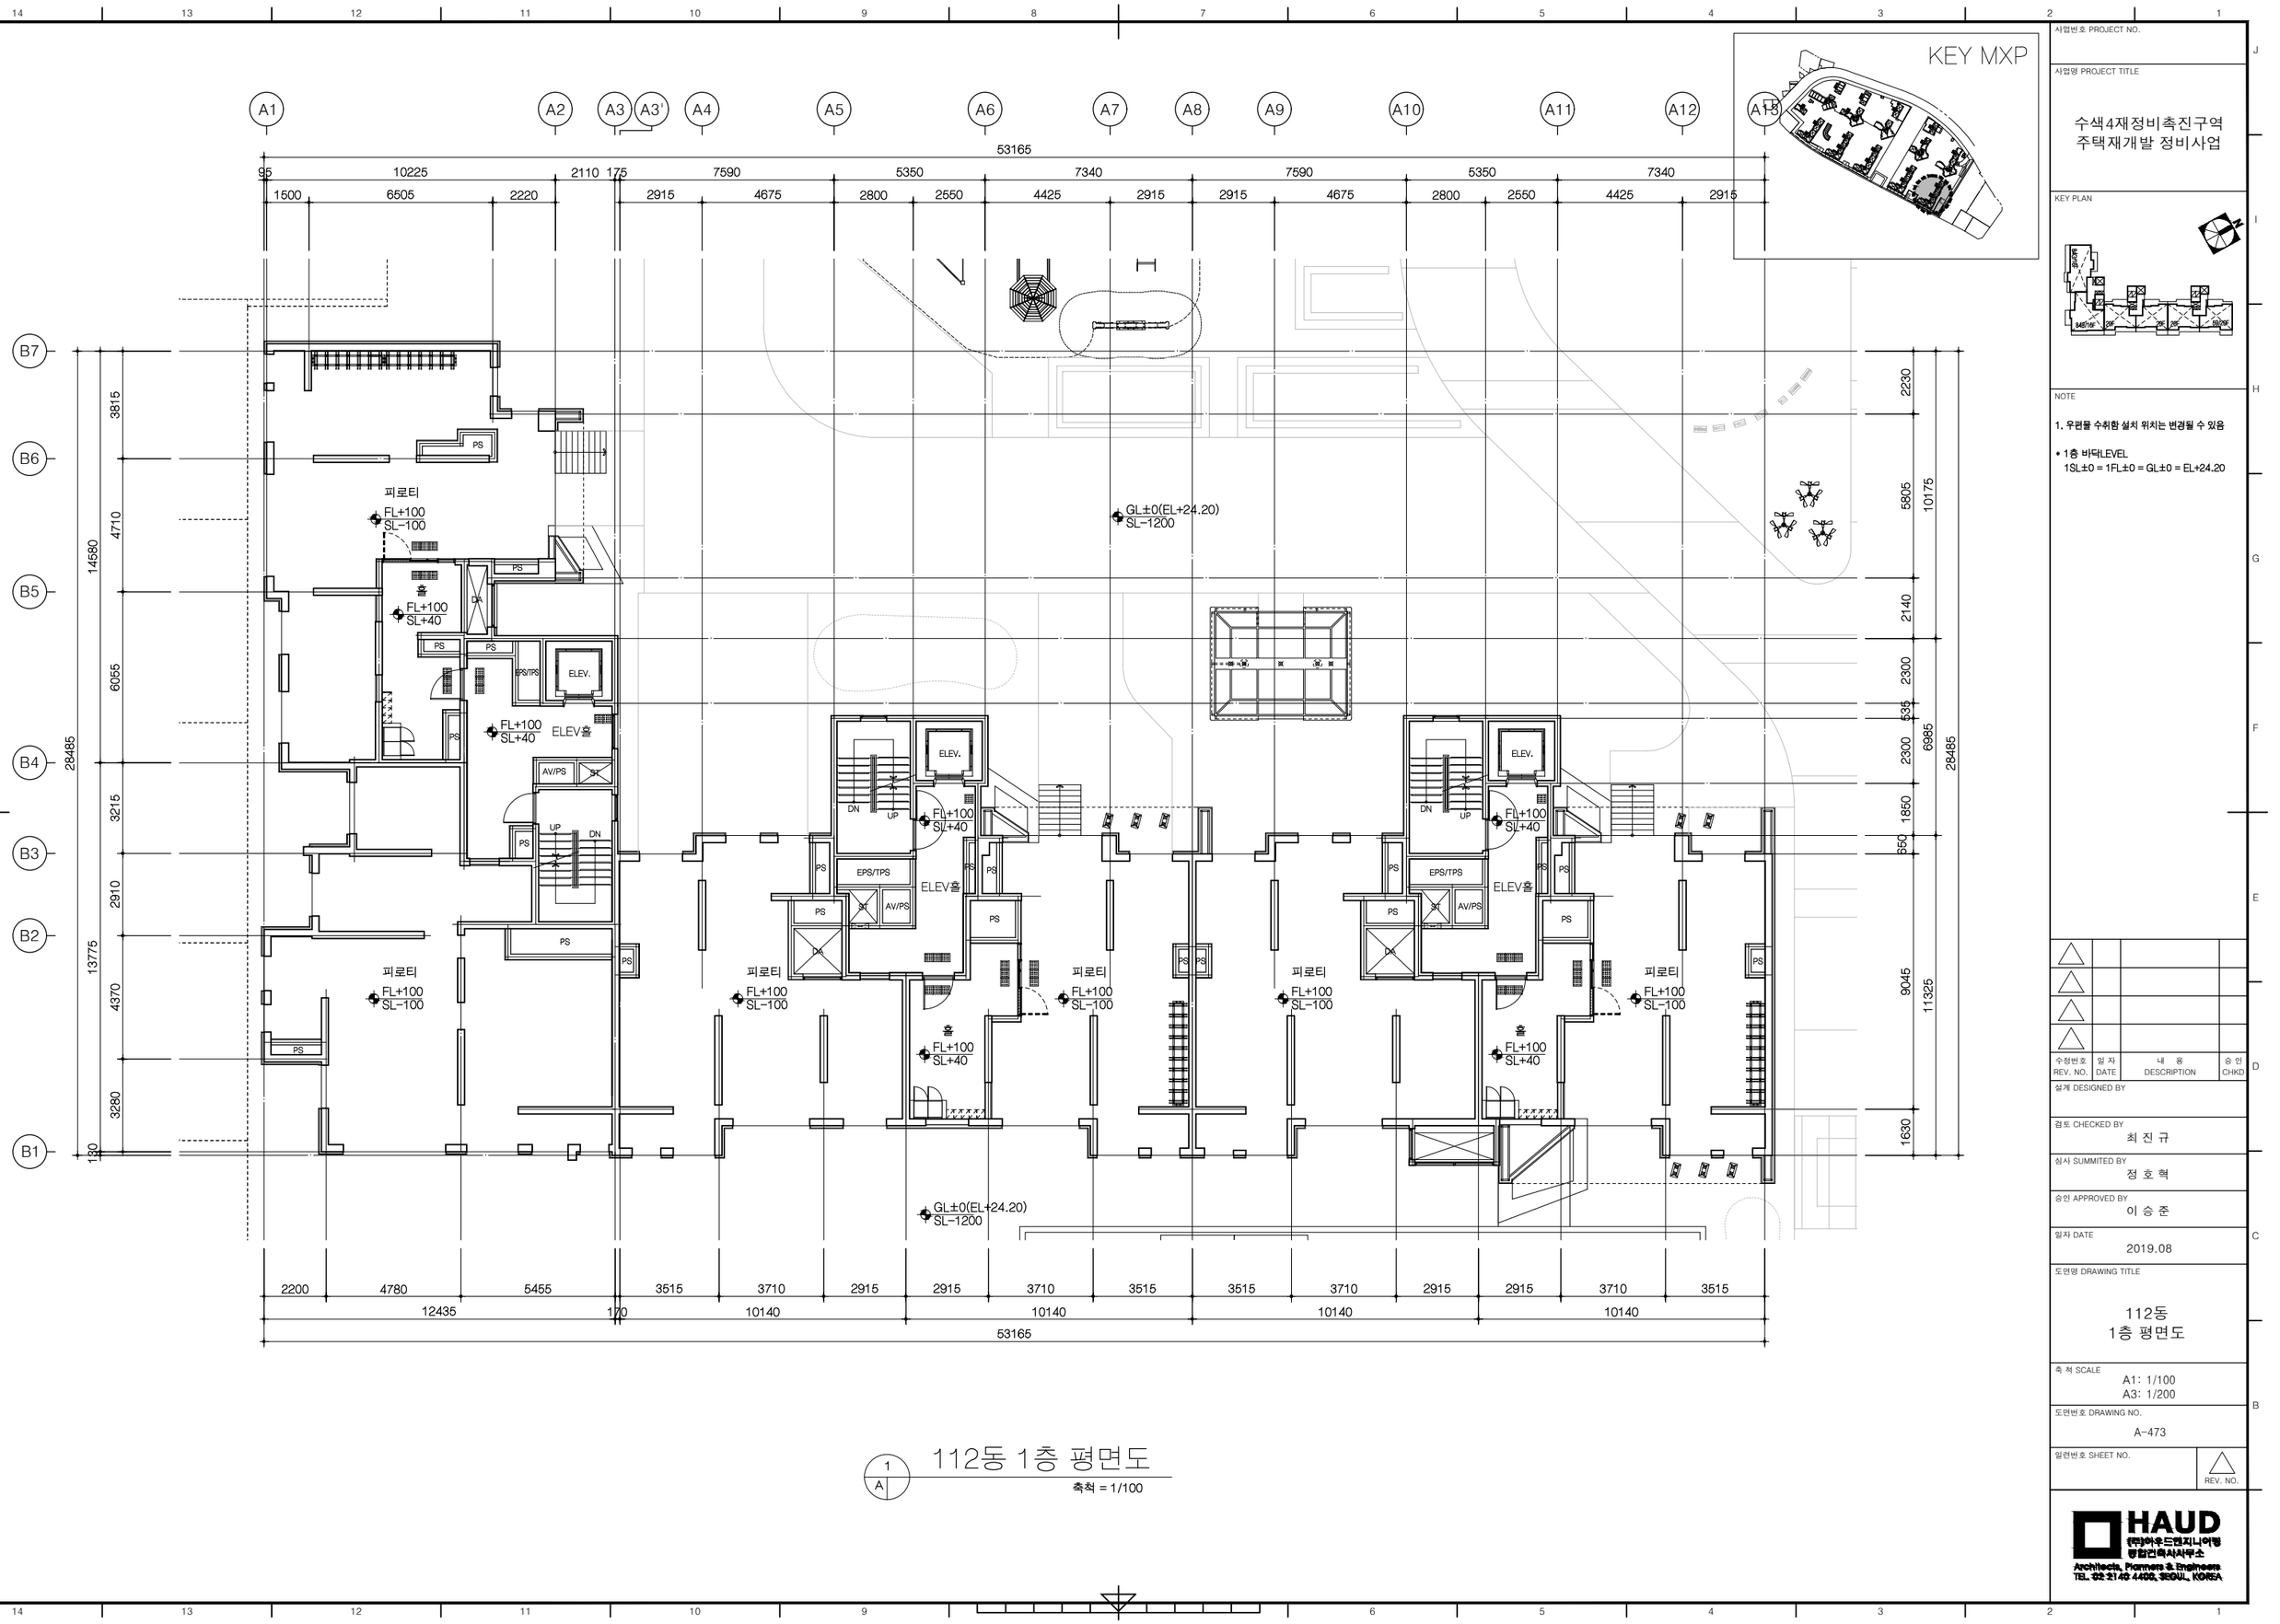

KEY MXP

112동 1층 평면도

축척 = 1/100

사업번호 PROJECT NO.

사업명 PROJECT TITLE

수색4재정비촉진구역
주택재개발 정비사업

KEY PLAN

NOTE

1. 우려물 수취함 설치 위치는 변경될 수 있음

• 1층 바닥LEVEL
1SL±0 = 1FL±0 = GL±0 = EL+24.20

수정번호 REV. NO.	일 자 DATE	내 용 DESCRIPTION	승 인 CHKD

설계 DESIGNED BY

검토 CHECKED BY
최 진 규

심사 SUMMITED BY
정 호 혁

승인 APPROVED BY
이 승 준

일자 DATE
2019.08

도면명 DRAWING TITLE
112동
1층 평면도

축 척 SCALE
A1: 1/100
A3: 1/200

도면번호 DRAWING NO.
A-473

일련번호 SHEET NO.

REV. NO.

HAUD
(주)하우드엔지니어링
종합건축사사무소
Architects, Planners & Engineers
TEL. 02 2140 4400, SEOUL, KOREA

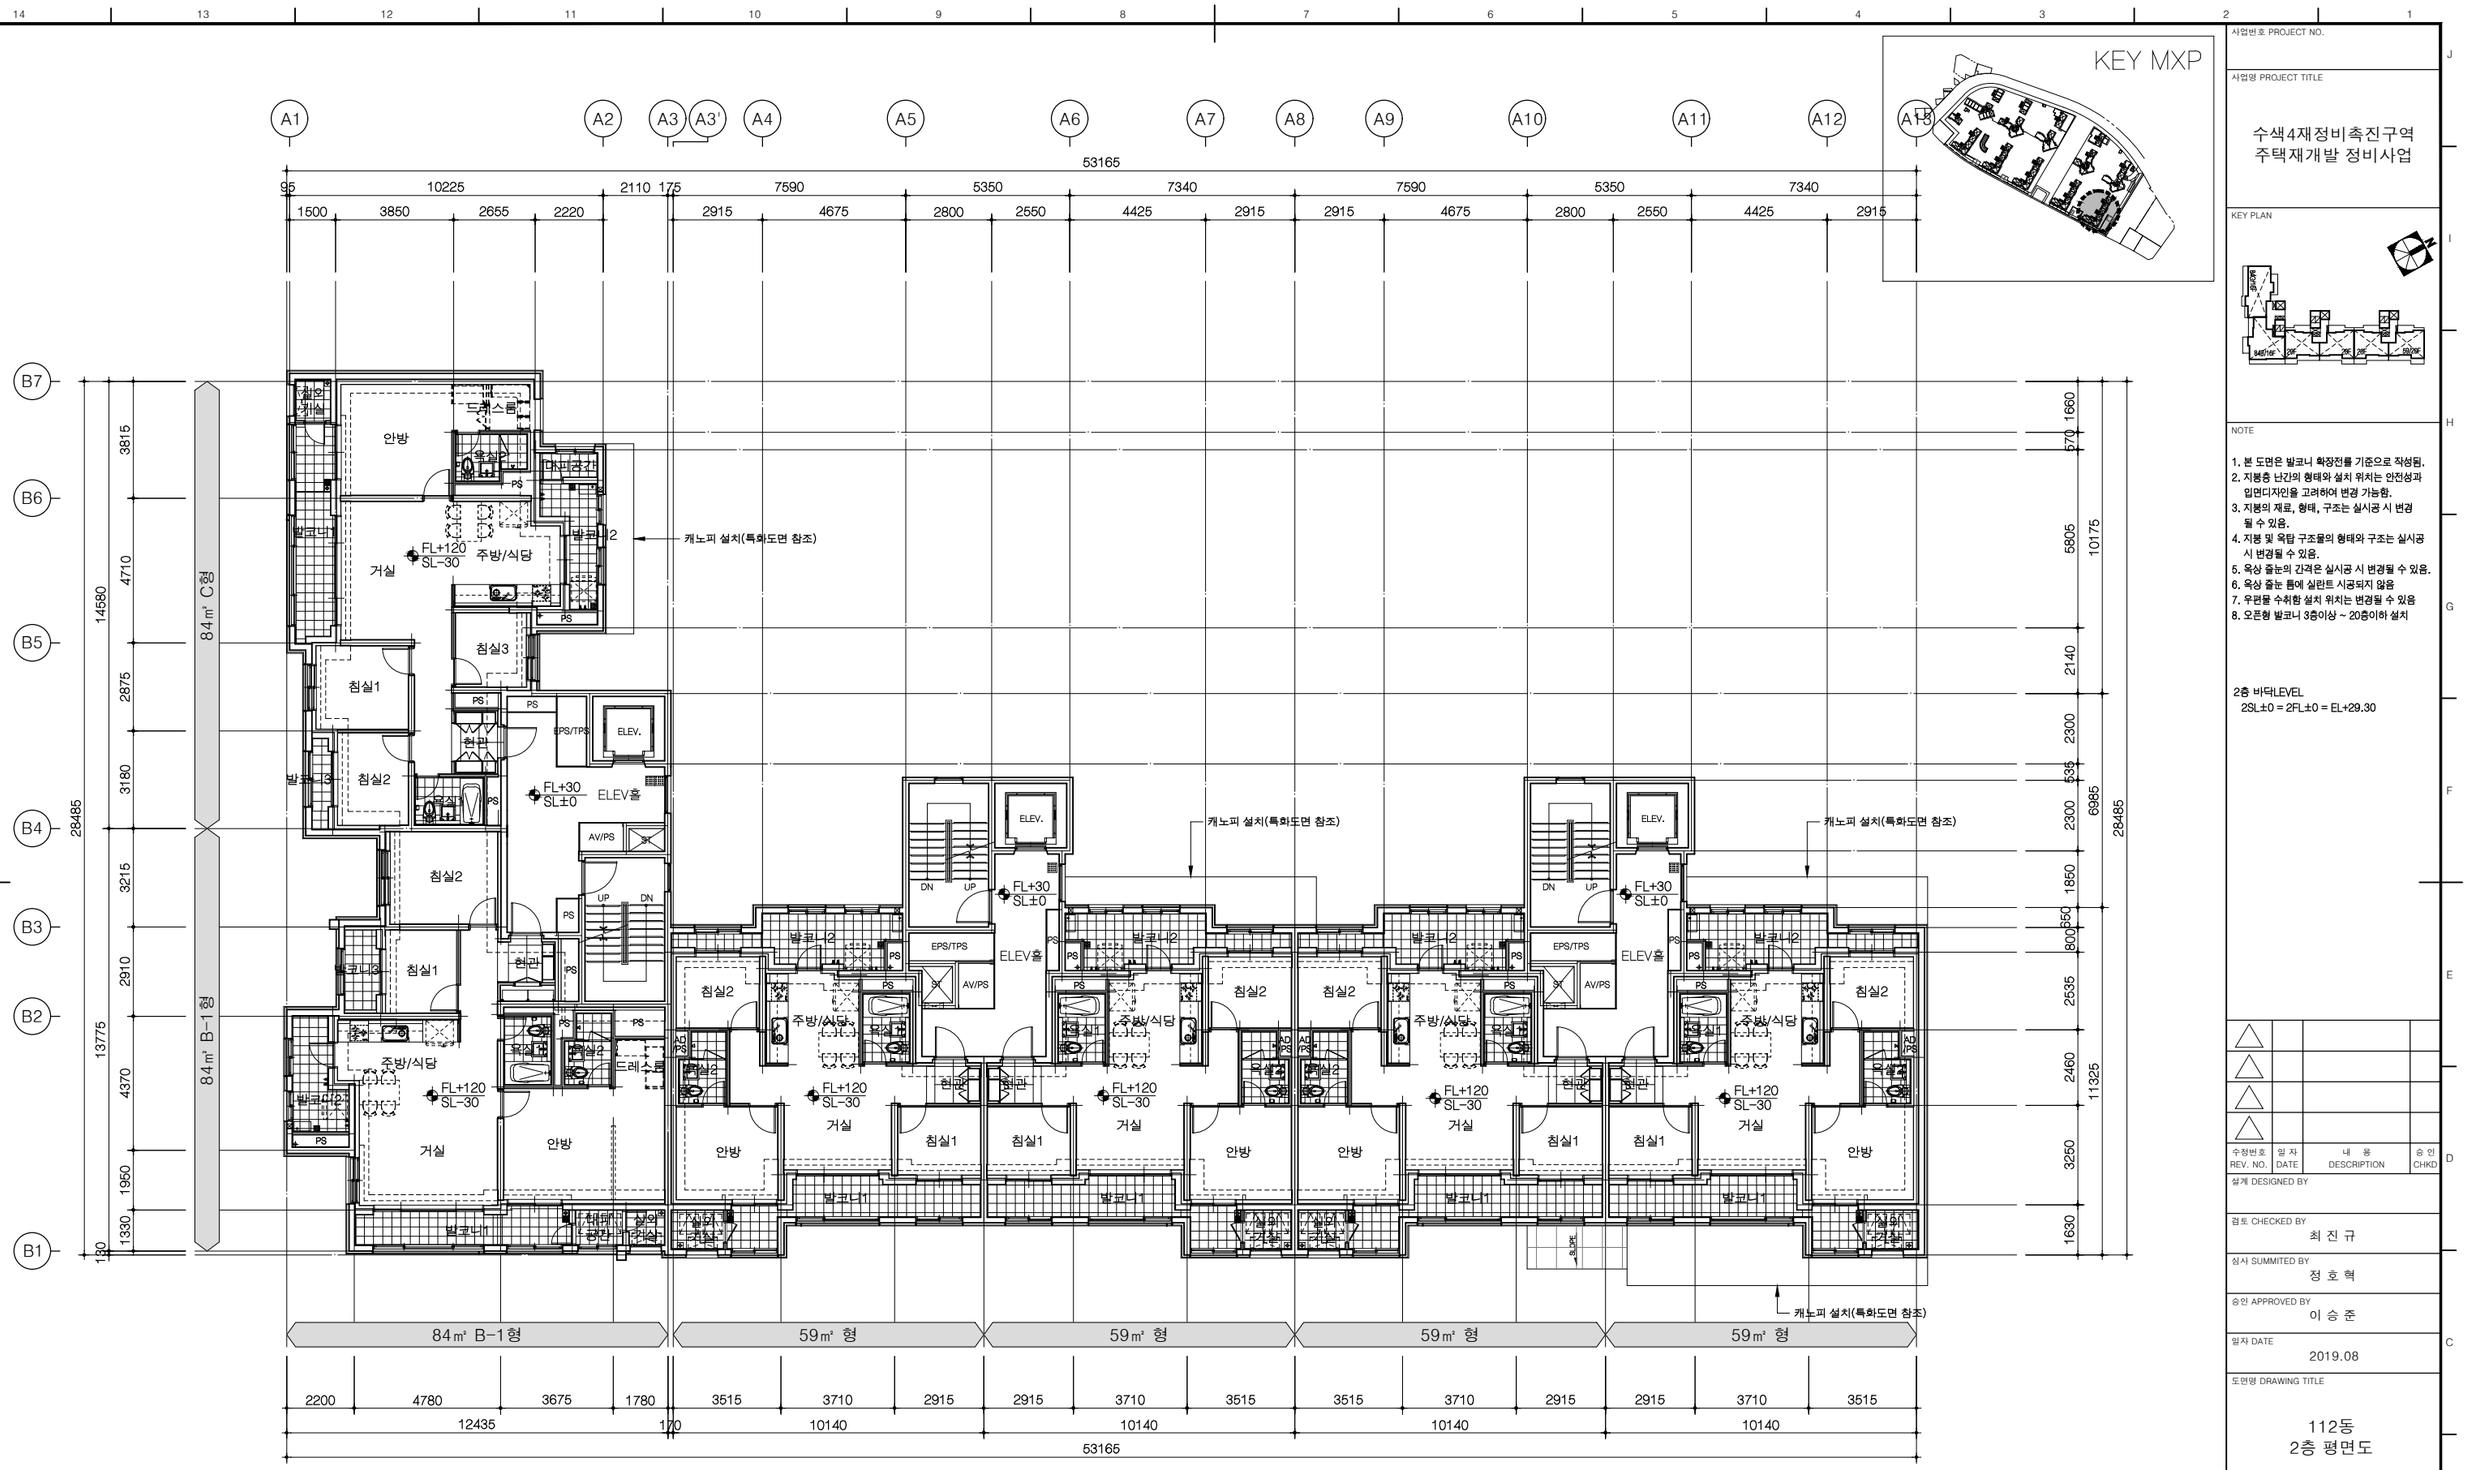

KEY MXP

1 A 112동 2층 평면도

축척 = 1/100

사업번호 PROJECT NO.

사업명 PROJECT TITLE

수색4재정비촉진구역
주택재개발 정비사업

KEY PLAN

NOTE

1. 본 도면은 발코니 확장전를 기준으로 작성됨.
2. 지붕층 난간의 형태와 설치 위치는 안전성과 입면디자인을 고려하여 변경 가능함.
3. 지붕의 재료, 형태, 구조는 실시공 시 변경 될 수 있음.
4. 지붕 및 옥탑 구조물의 형태와 구조는 실시공 시 변경될 수 있음.
5. 옥상 출눈의 간격은 실시공 시 변경될 수 있음.
6. 옥상 출눈 틈에 실란트 시공되지 않음
7. 우편물 수취함 설치 위치는 변경될 수 있음
8. 오픈형 발코니 3층이상 ~ 20층이하 설치

2층 바닥LEVEL
2SL±0 = 2FL±0 = EL+29.30

수정번호 REV. NO.	일 자 DATE	내 용 DESCRIPTION	승 인 CHKD
△			
△			
△			
△			

설계 DESIGNED BY

검토 CHECKED BY
최 진 규

심사 SUMMITED BY
정 호 혁

승인 APPROVED BY
이 승 준

일자 DATE
2019.08

도면명 DRAWING TITLE
112동
2층 평면도

축 척 SCALE
A1: 1/100
A3: 1/200

도면번호 DRAWING NO.
A-474

일련번호 SHEET NO.

△ REV. NO.

HAUD
(주)하우드엔지니어링
종합건축사사무소
Architects, Planners & Engineers
TEL. 02 2140 4400, SEOUL, KOREA

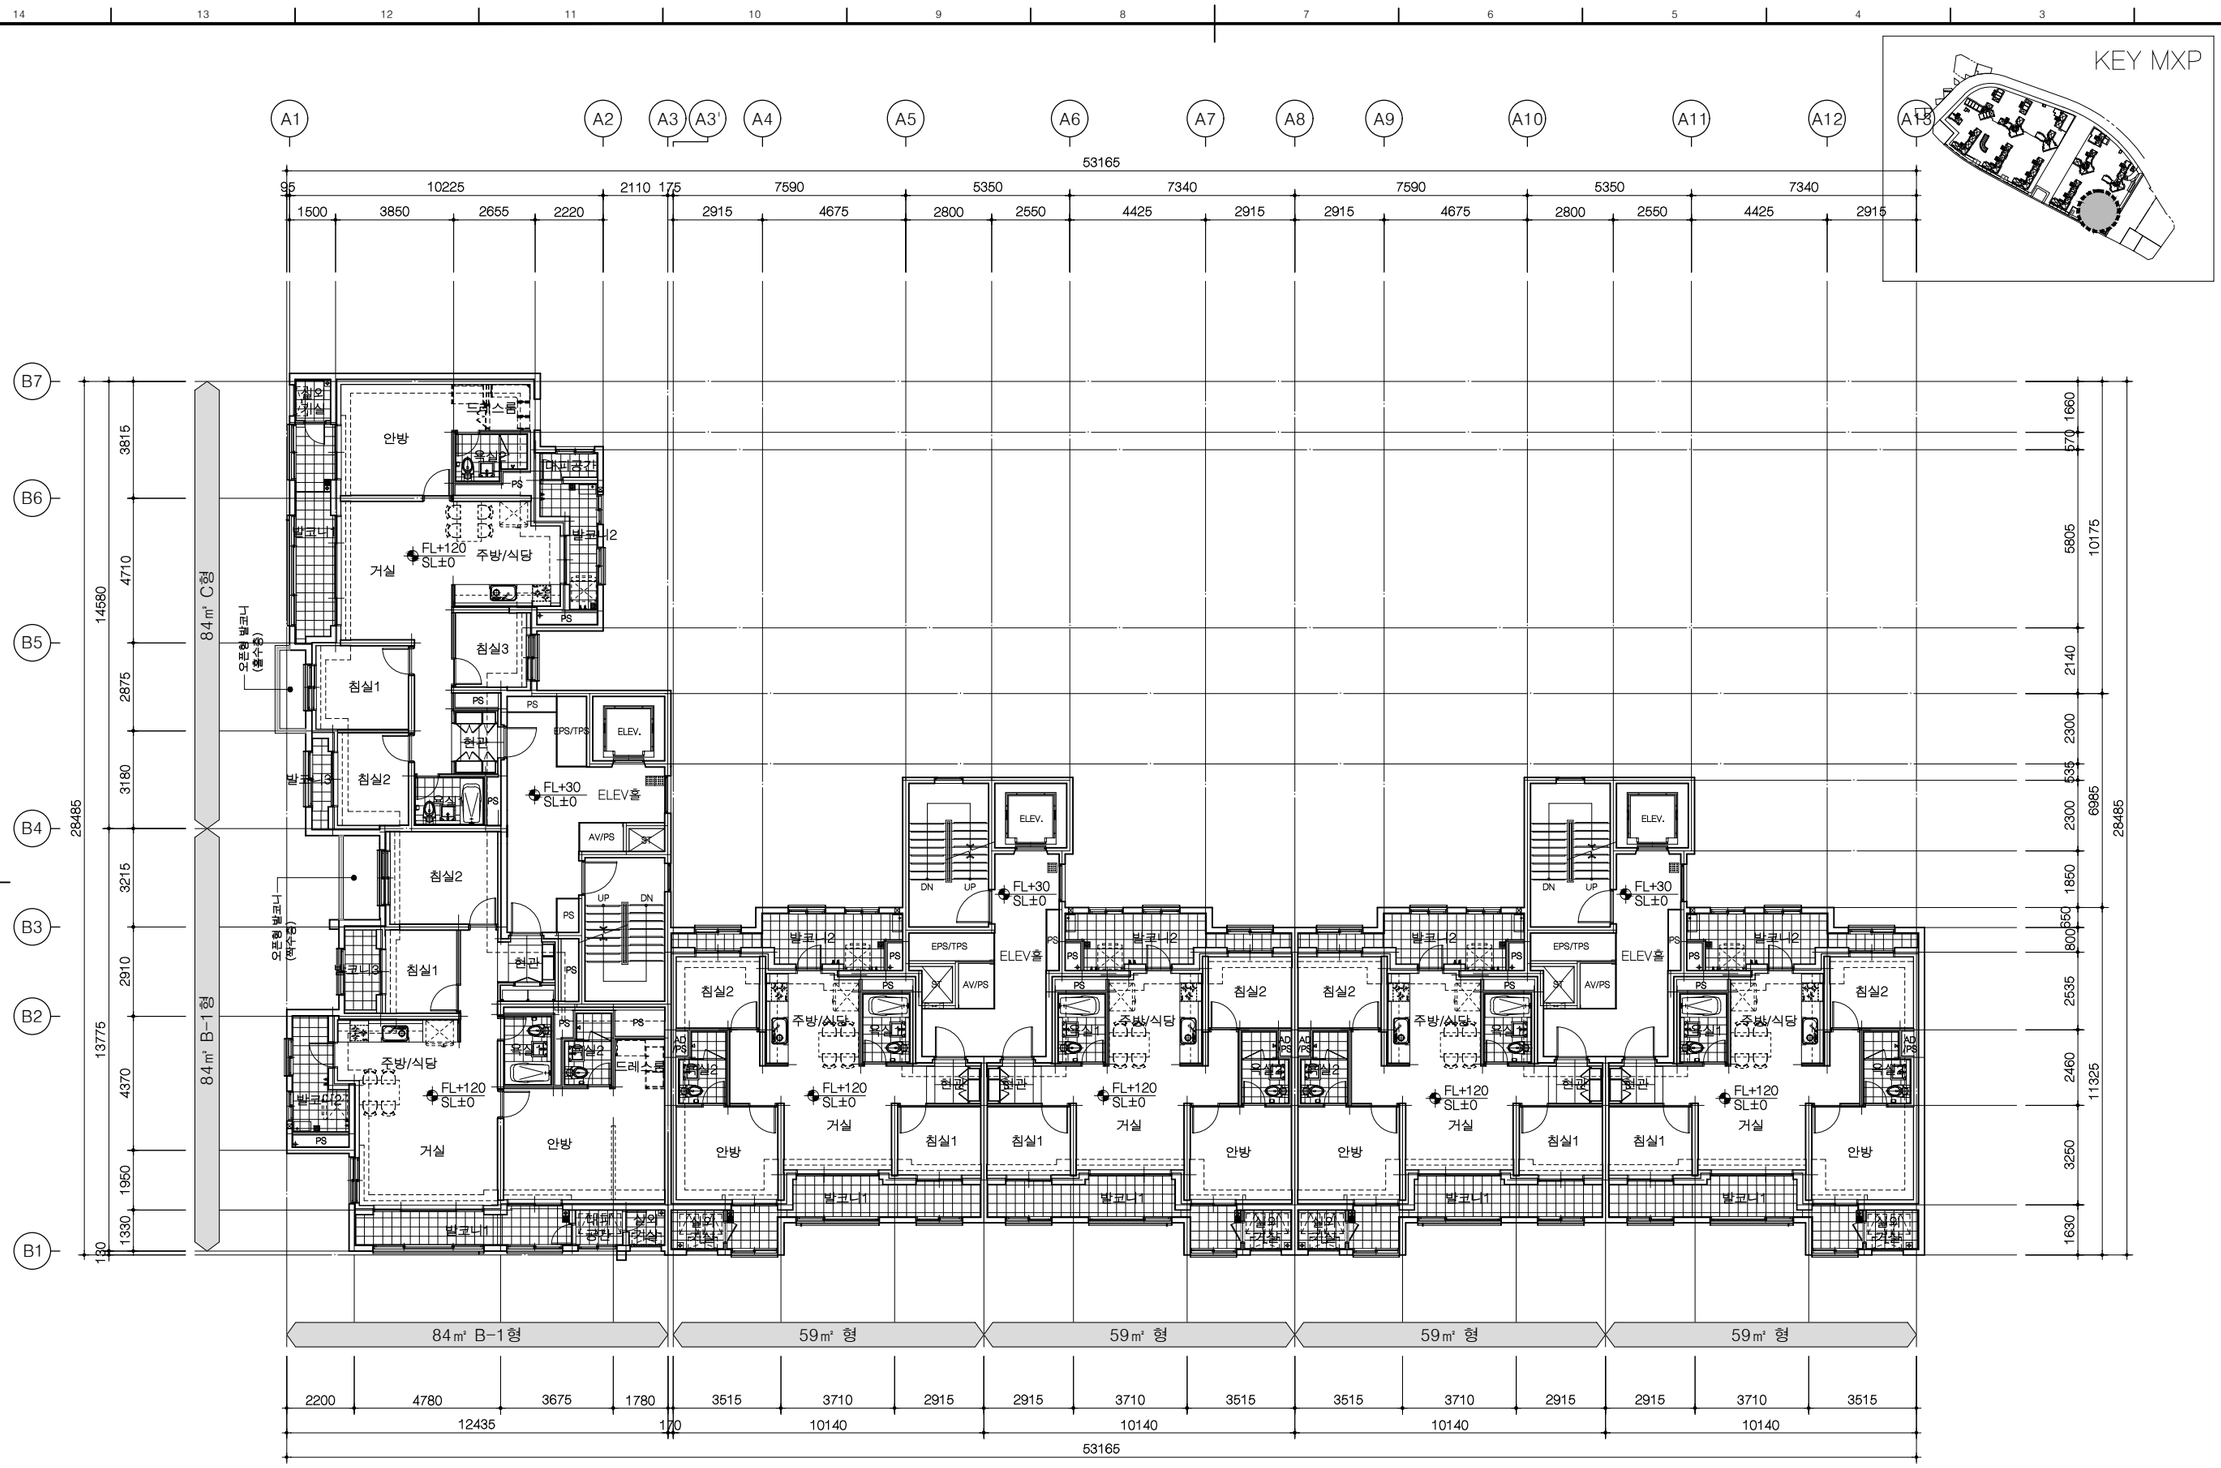

1 A 112동 3~16층 평면도

축척 = 1/100

사업번호 PROJECT NO.

사업명 PROJECT TITLE

수색4재정비촉진구역
주택재개발 정비사업

KEY PLAN

NOTE

1. 본 도면은 발코니 확장전를 기준으로 작성됨.
2. 지붕층 난간의 형태와 설치 위치는 안전성과 입면디자인을 고려하여 변경 가능함.
3. 지붕의 재료, 형태, 구조는 실시공 시 변경 될 수 있음.
4. 지붕 및 옥탑 구조물의 형태와 구조는 실시공 시 변경될 수 있음.
5. 옥상 출눈의 간격은 실시공 시 변경될 수 있음.
6. 옥상 출눈 틈에 실란트 시공되지 않음
7. 우편물 수취함 설치 위치는 변경될 수 있음
8. 오픈형 발코니 3층이상 ~ 20층이하 설치

수정번호 REV. NO.	일 자 DATE	내 용 DESCRIPTION	승 인 CHKD
△			
△			
△			
△			

설계 DESIGNED BY

검토 CHECKED BY
최 진 규

심사 SUMMITED BY
정 호 혁

승인 APPROVED BY
이 승 준

일자 DATE
2019.08

도면명 DRAWING TITLE
112동
3층~16층 평면도

축 척 SCALE
A1: 1/100
A3: 1/200

도면번호 DRAWING NO.
A-475

일련번호 SHEET NO. △ REV. NO.

HAUD
㈜하우드엔지니어링
종합건축사사무소
Architects, Planners & Engineers
TEL. 02 2140 4400, SEOUL, KOREA

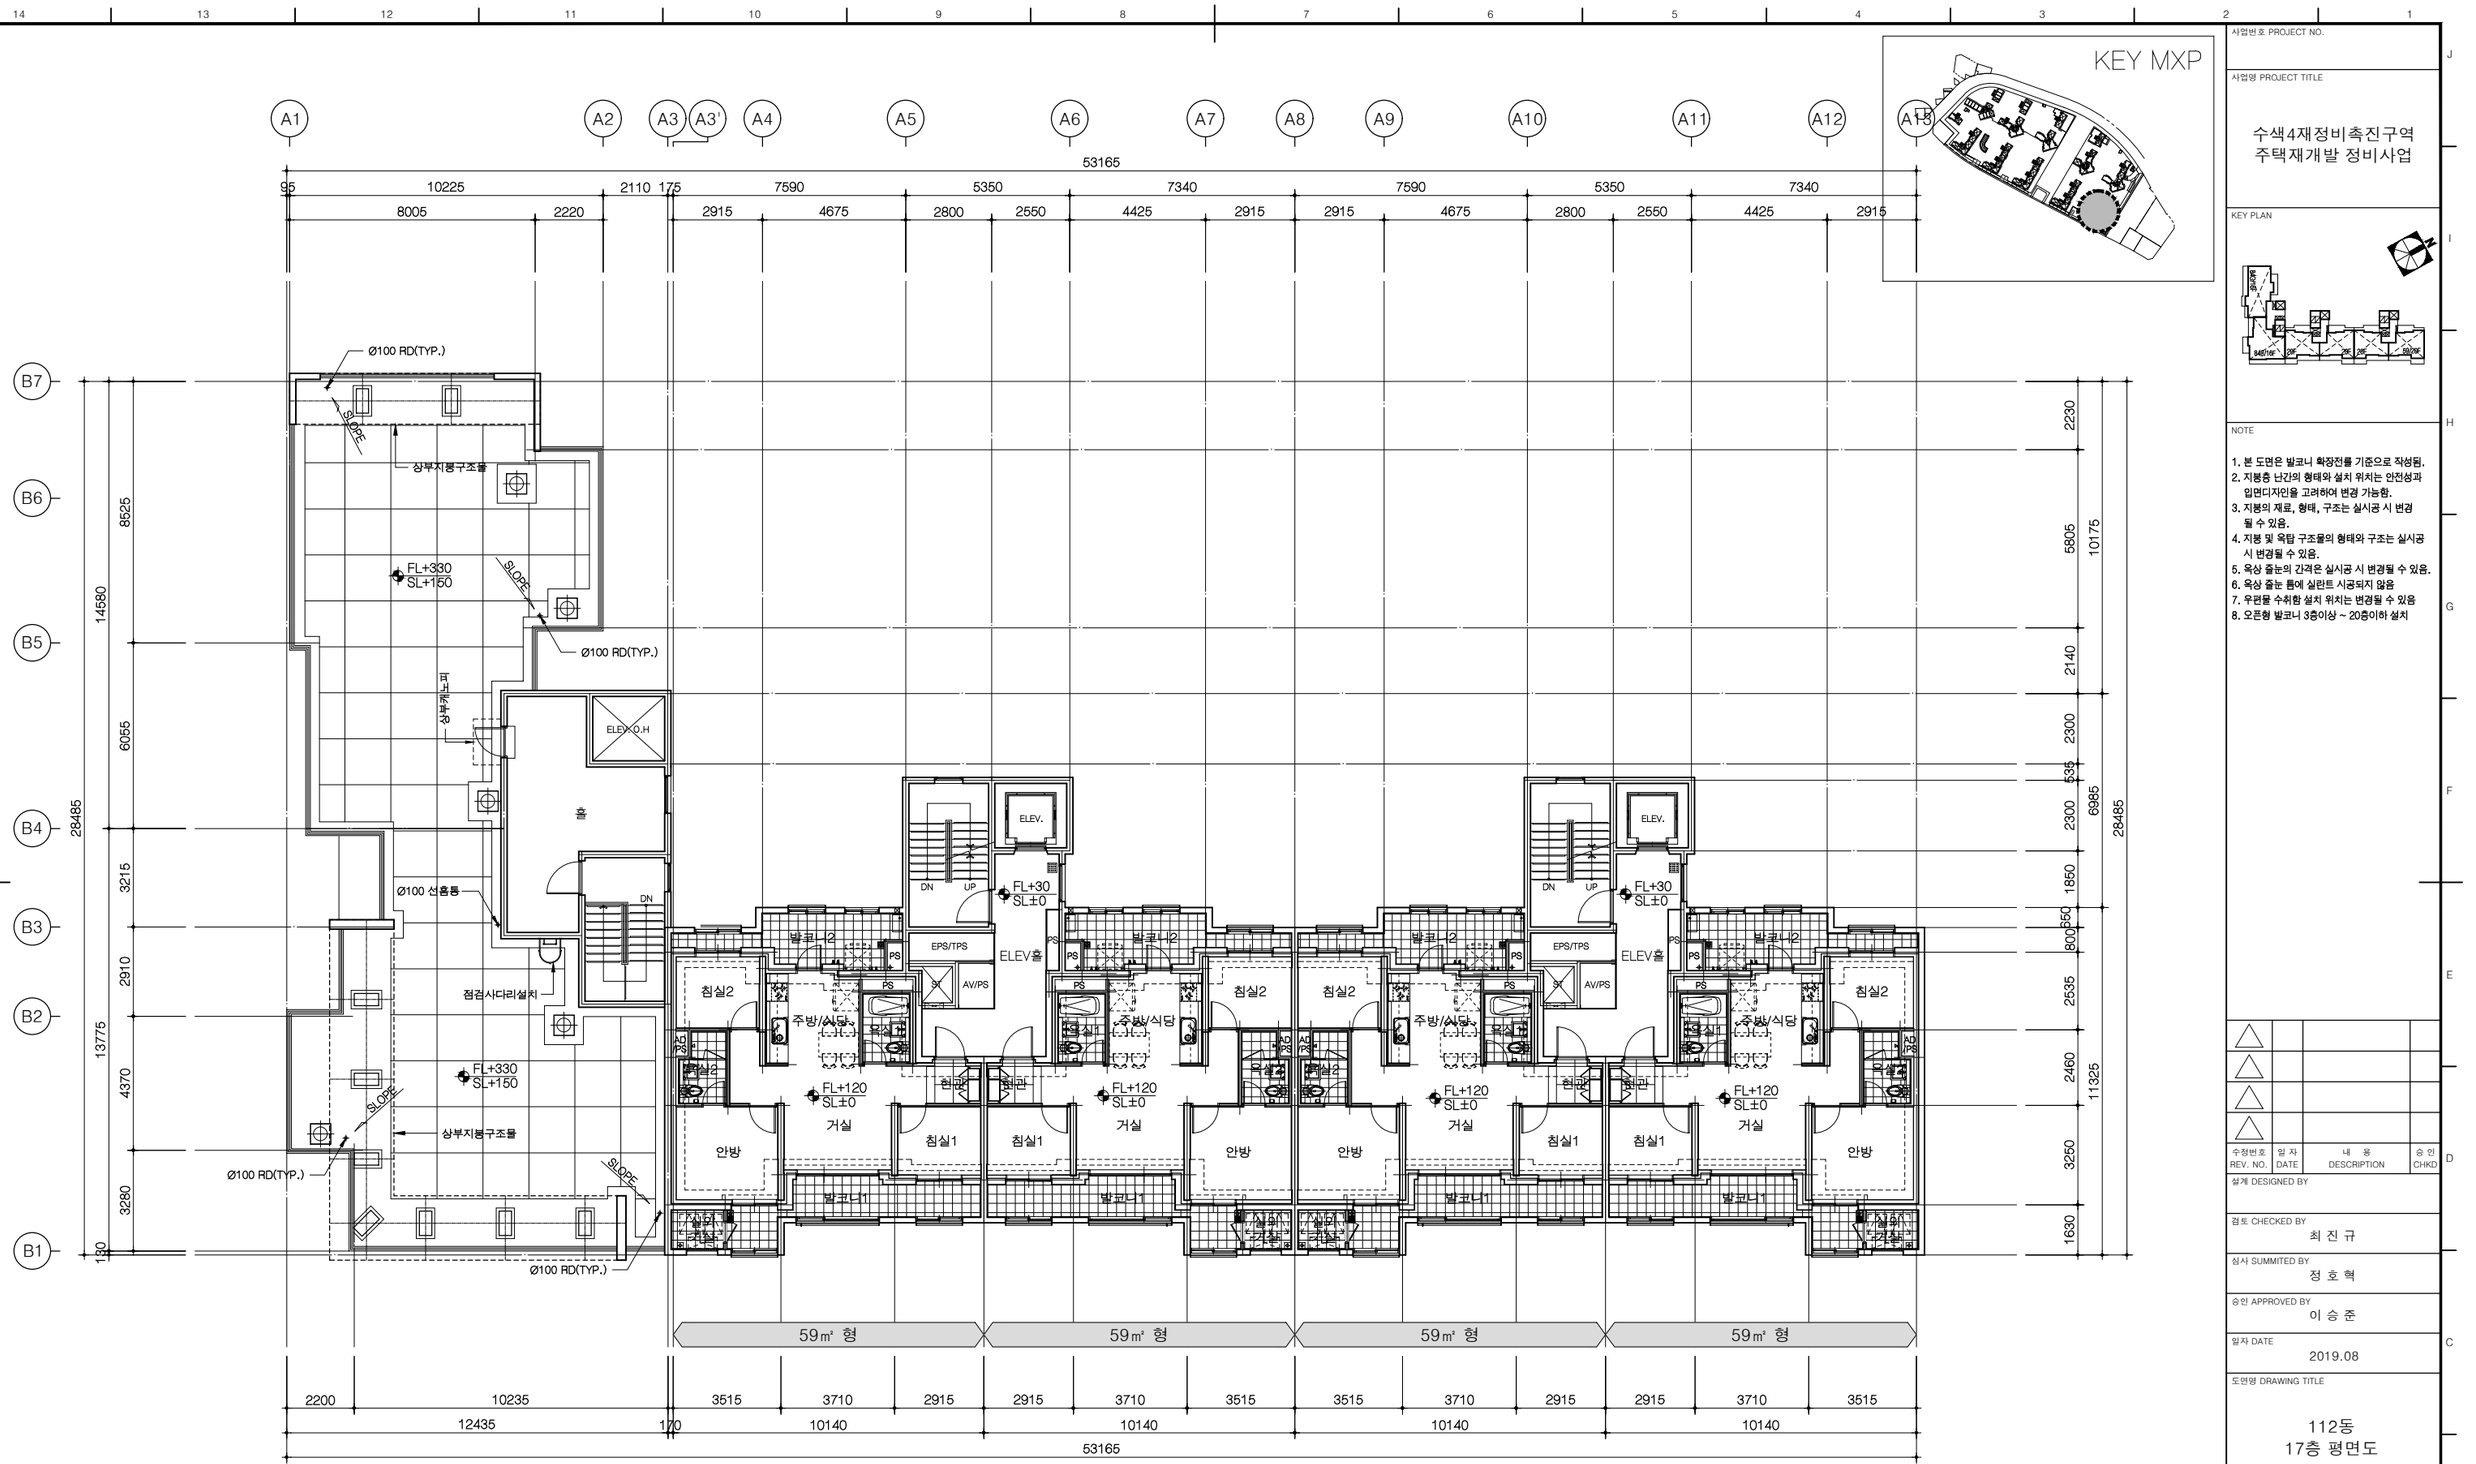

1 A 112동 17층 평면도

축척 = 1/100

KEY MXP

사업번호 PROJECT NO.

사업명 PROJECT TITLE

수색4재정비촉진구역
주택재개발 정비사업

KEY PLAN

NOTE

1. 본 도면은 발코니 확장전를 기준으로 작성됨.
2. 지붕층 난간의 형태와 설치 위치는 안전성과 입면디자인을 고려하여 변경 가능함.
3. 지붕의 재료, 형태, 구조는 실시공 시 변경 될 수 있음.
4. 지붕 및 옥탑 구조물의 형태와 구조는 실시공 시 변경될 수 있음.
5. 옥상 출눈의 간격은 실시공 시 변경될 수 있음.
6. 옥상 출눈 틈에 실란트 시공되지 않음
7. 우편물 수취함 설치 위치는 변경될 수 있음
8. 오픈형 발코니 3층이상 ~ 20층이하 설치

수정번호 REV. NO.	일 자 DATE	내 용 DESCRIPTION	승 인 CHKD
△			
△			
△			
△			

설계 DESIGNED BY

검토 CHECKED BY
최 진 규

심사 SUMMITED BY
정 호 혁

승인 APPROVED BY
이 승 준

일자 DATE
2019.08

도면명 DRAWING TITLE
112동
17층 평면도

축 척 SCALE
A1: 1/100
A3: 1/200

도면번호 DRAWING NO.
A-476

일련번호 SHEET NO.

△ REV. NO.

HAUD
㈜하우드엔지니어링
종합건축사사무소
Architects, Planners & Engineers
TEL. 02 2140 4400, SEOUL, KOREA

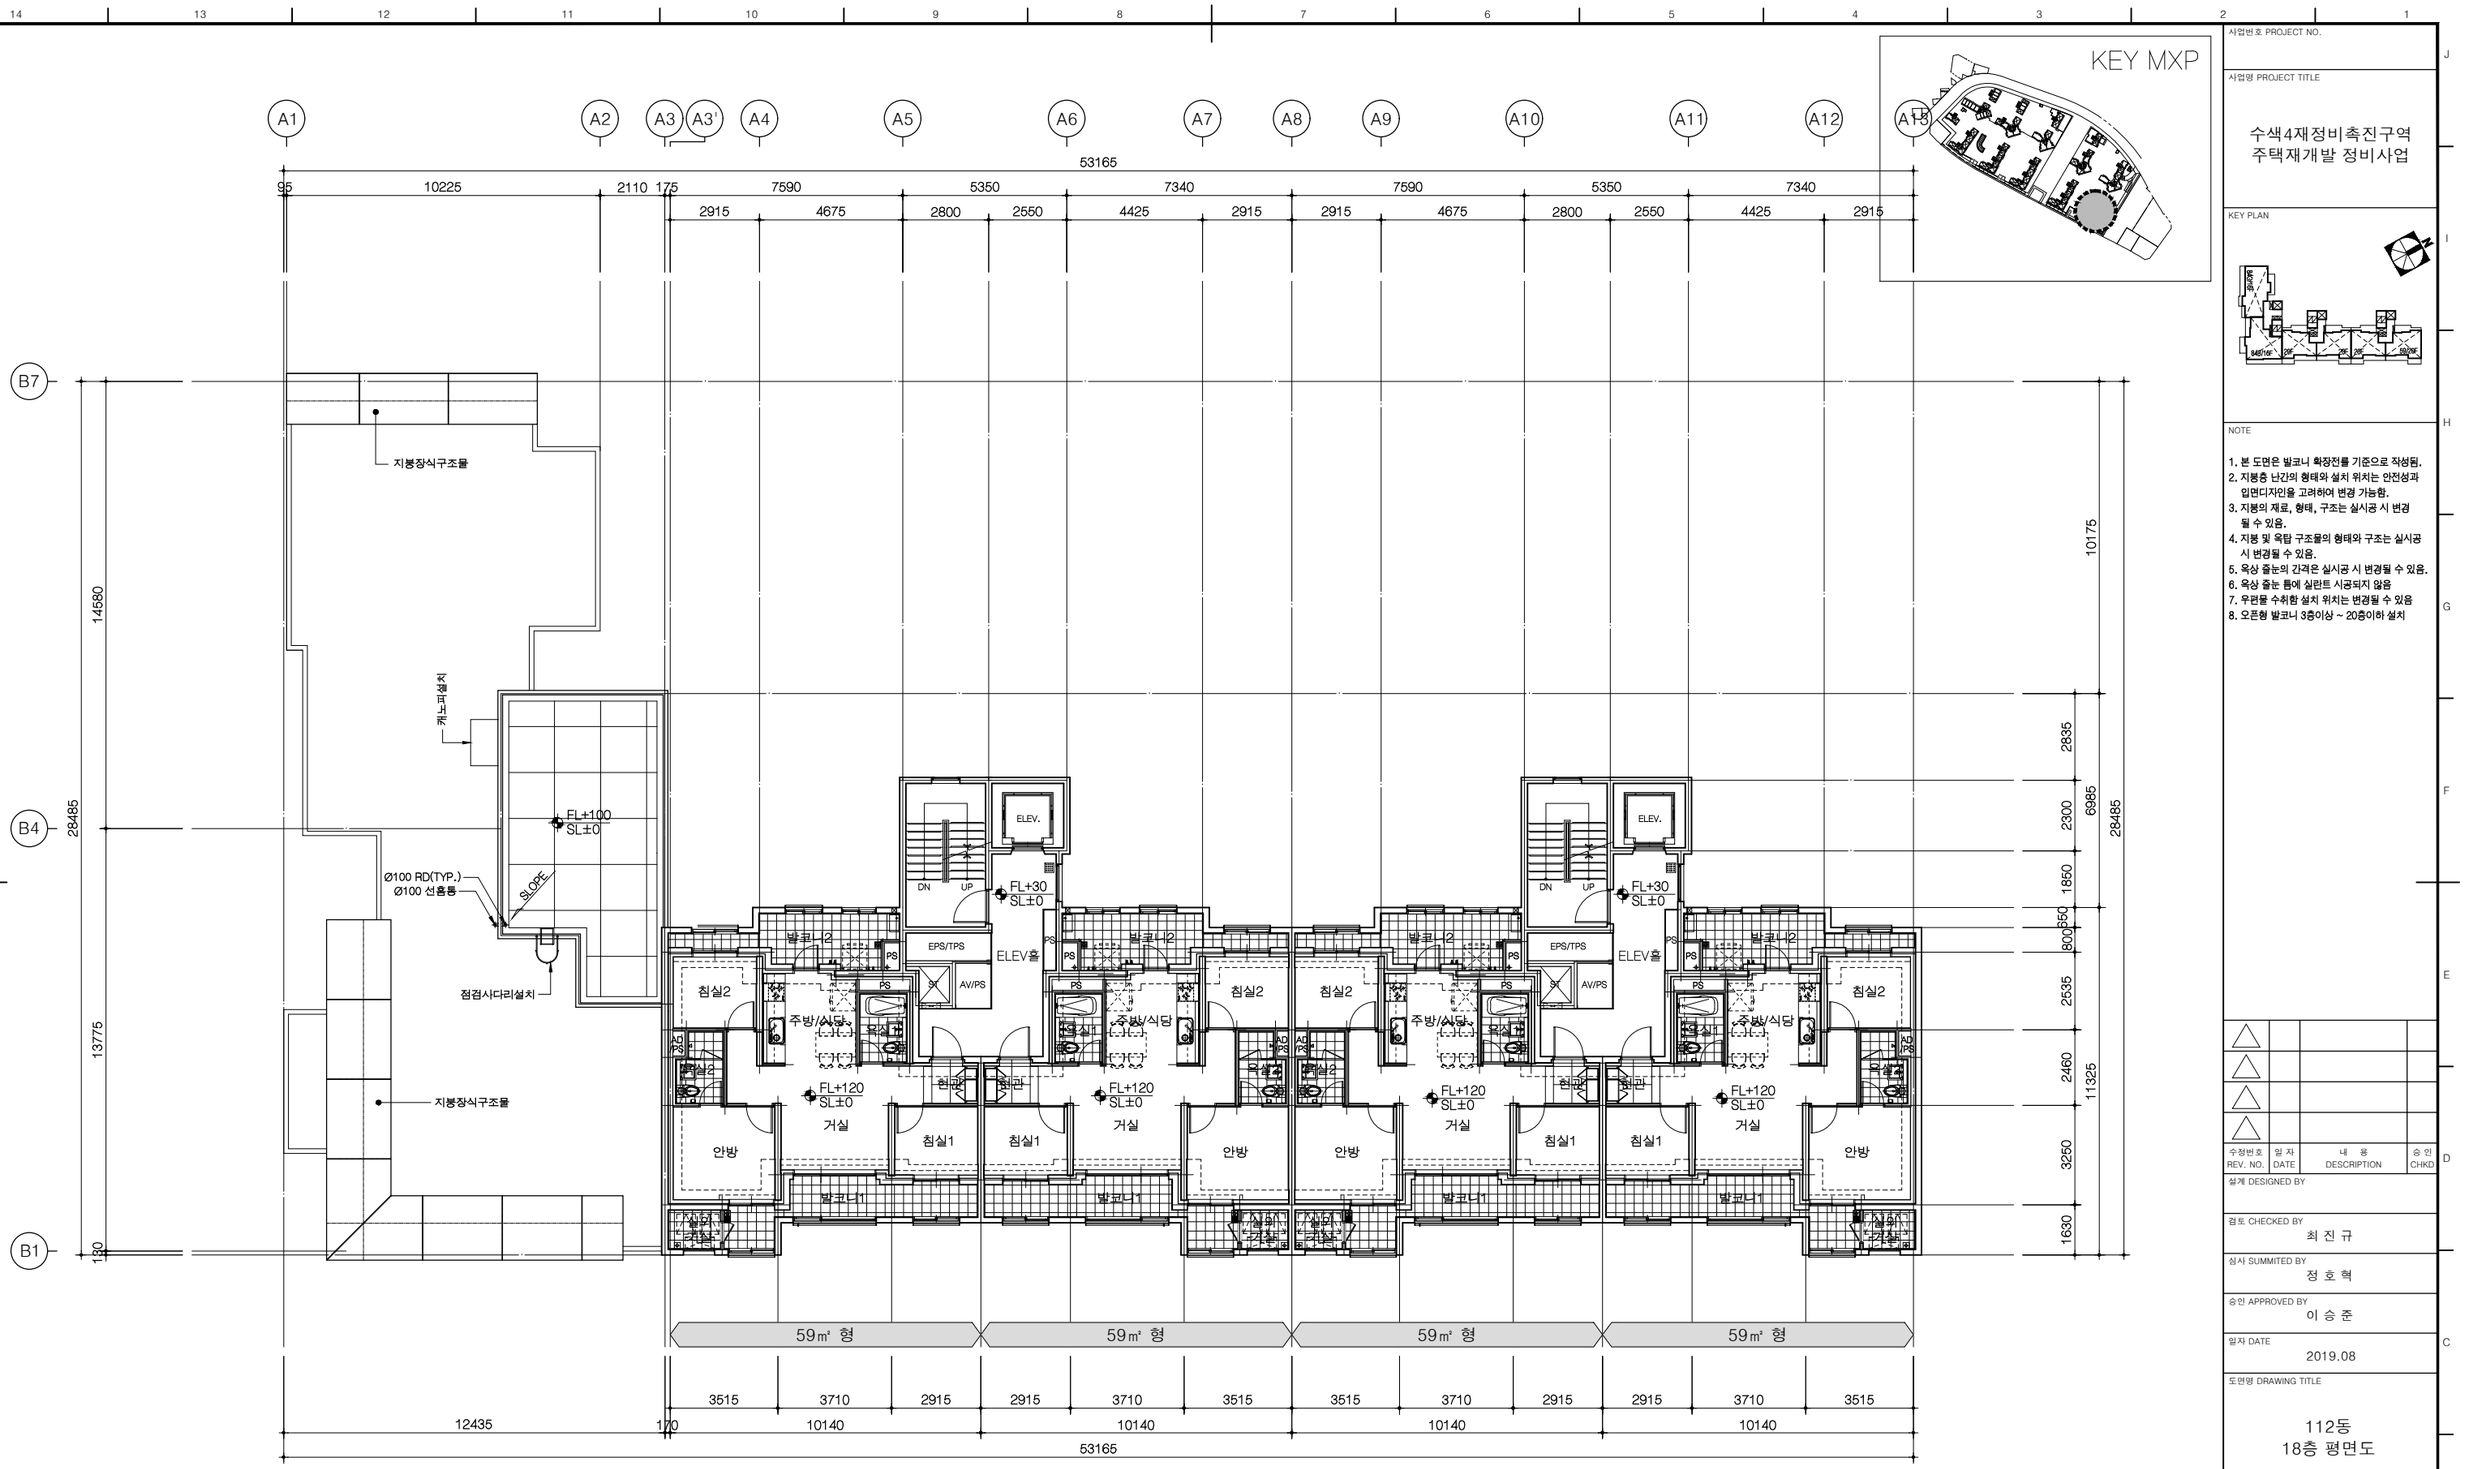

112동 18층 평면도

1/A

축척 = 1/100

KEY MXP

사업번호 PROJECT NO.

사업명 PROJECT TITLE

수색4재정비촉진구역
주택재개발 정비사업

KEY PLAN

NOTE

1. 본 도면은 발코니 확장전를 기준으로 작성됨.
2. 지붕층 난간의 형태와 설치 위치는 안전성과 입면디자인을 고려하여 변경 가능함.
3. 지붕의 재료, 형태, 구조는 실시공 시 변경 될 수 있음.
4. 지붕 및 옥탑 구조물의 형태와 구조는 실시공 시 변경될 수 있음.
5. 옥상 출눈의 간격은 실시공 시 변경될 수 있음.
6. 옥상 출눈 틈에 실란트 시공되지 않음
7. 우편물 수취함 설치 위치는 변경될 수 있음
8. 오픈형 발코니 3층이상 ~ 20층이하 설치

수정번호 REV. NO.	일 자 DATE	내 용 DESCRIPTION	승 인 CHKD
△			
△			
△			
△			

설계 DESIGNED BY

검토 CHECKED BY
최 진 규

심사 SUMMITED BY
정 호 혁

승인 APPROVED BY
이 승 준

일자 DATE
2019.08

도면명 DRAWING TITLE
112동
18층 평면도

축 척 SCALE
A1: 1/100
A3: 1/200

도면번호 DRAWING NO.
A-477

일련번호 SHEET NO.

△ REV. NO.

HAUD
㈜하우드엔지니어링
종합건축사사무소
Architects, Planners & Engineers
TEL. 02 2140 4466, SEOUL, KOREA

1 A — 112동 19~20층 평면도

축척 = 1/100

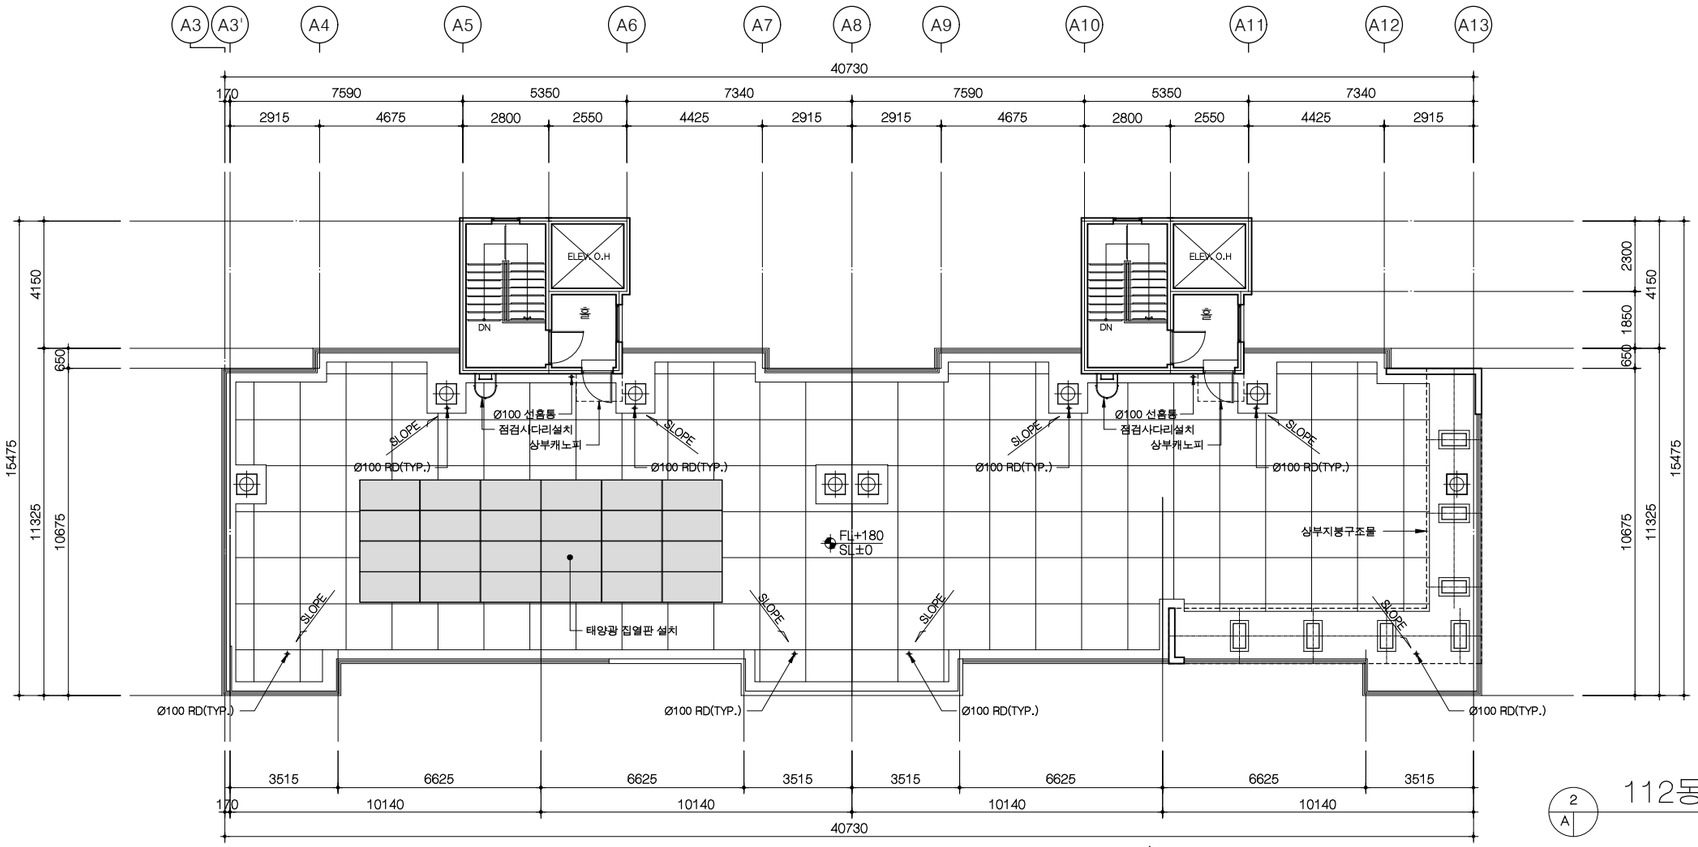

2 A — 112동 지붕 평면도

축척 = 1/100

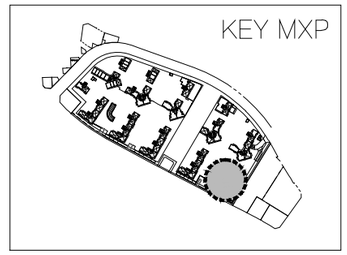

사업번호 PROJECT NO.

사업명 PROJECT TITLE

수색4재정비촉진구역
주택재개발 정비사업

KEY PLAN

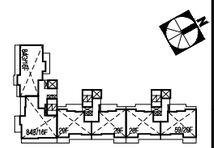

NOTE

1. 본 도면은 발코니 확장전를 기준으로 작성됨.
2. 지붕층 난간의 형태와 설치 위치는 안전성과 입면디자인을 고려하여 변경 가능함.
3. 지붕의 재료, 형태, 구조는 실시공 시 변경 될 수 있음.
4. 지붕 및 옥탑 구조물의 형태와 구조는 실시공 시 변경될 수 있음.
5. 옥상 출눈의 간격은 실시공 시 변경될 수 있음.
6. 옥상 출눈 틈에 실란트 시공되지 않음
7. 우편물 수취함 설치 위치는 변경될 수 있음
8. 오픈형 발코니 3층이상 ~ 20층이하 설치

수정번호 REV. NO.	일 자 DATE	내 용 DESCRIPTION	승 인 CHKD
△			
△			
△			
△			

설계 DESIGNED BY

검토 CHECKED BY
최 진 규

심사 SUMMITED BY
정 호 혁

승인 APPROVED BY
이 승 준

일자 DATE
2019.08

도면명 DRAWING TITLE
112동
19~20층 및 지붕 평면도

축 척 SCALE
A1: 1/100
A3: 1/200

도면번호 DRAWING NO.
A-478

일련번호 SHEET NO.

REV. NO. △

HAUD
㈜하우드엔지니어링
종합건축사사무소
Architects, Planners & Engineers
TEL. 02 2140 4466, SEOUL, KOREA

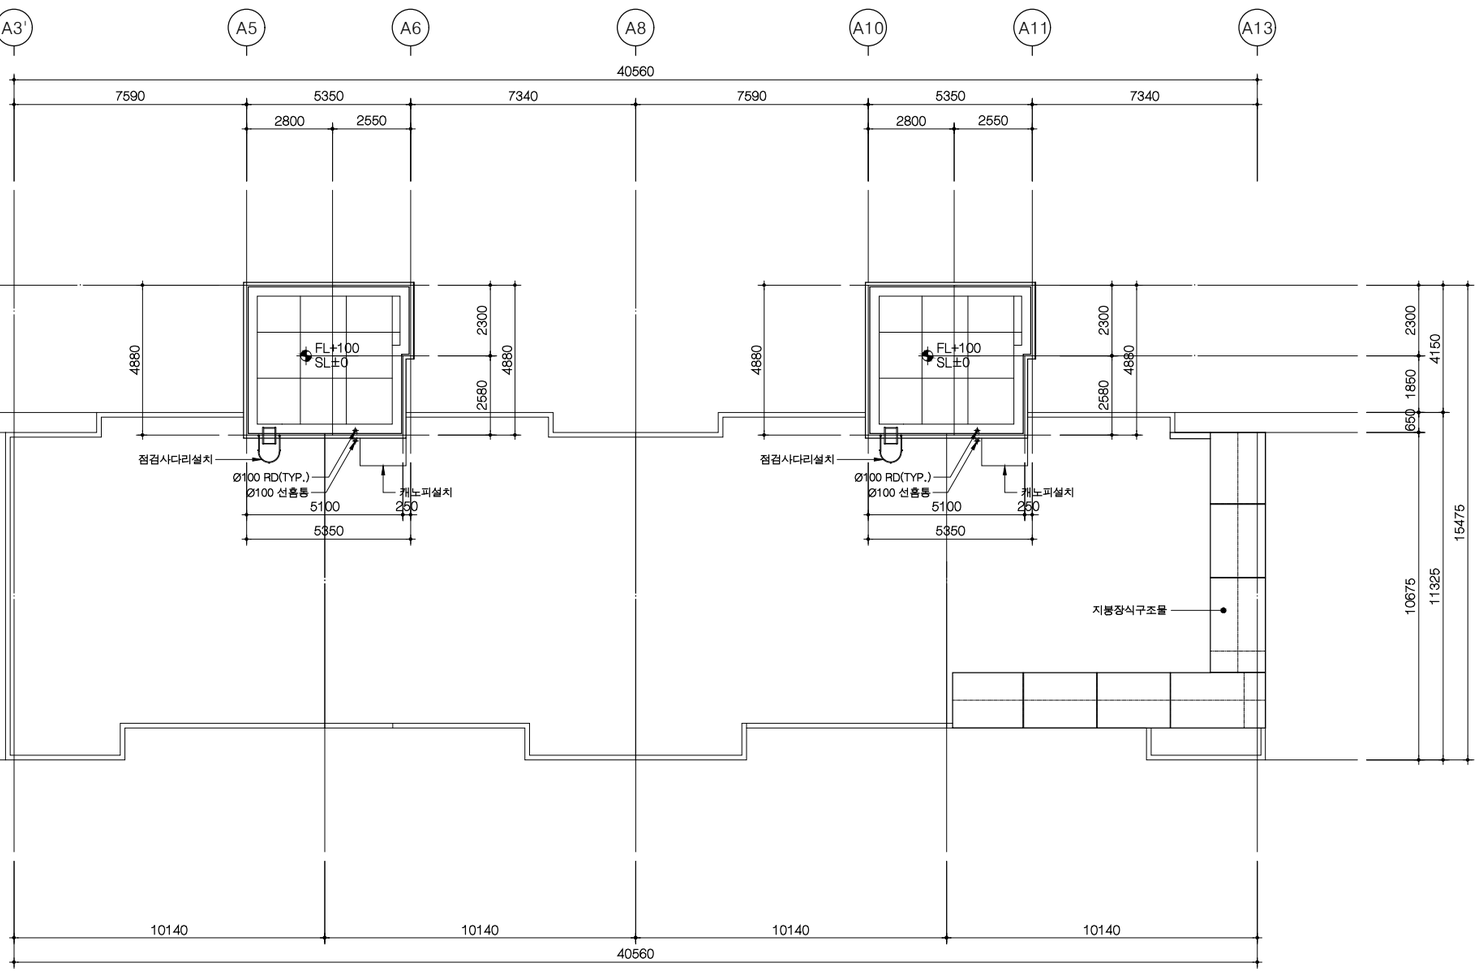

112동 옥탑지붕 평면도

축척 = 1/100

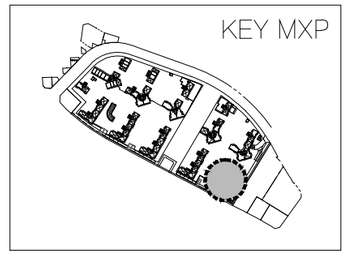

사업번호 PROJECT NO.

사업명 PROJECT TITLE

수색4재정비촉진구역
주택재개발 정비사업

KEY PLAN

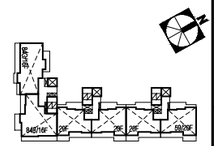

NOTE

1. 지붕바닥
   ① EXP. JOINT: 3000 X 3000
2. 본 평면도는 발코니확장전을 기준으로 작성됨
3. 재료마감은 실내,외 재료마감표 참조
4. 지붕 난간형태/설치위치는 안전성과 입면을 고려하여 실시공시 변경될 수 있음
5. 지붕재료 및 형태,구조는 실시공시 변경될수 있음
6. 지붕(옥탑지붕)의 배수드레인,환소음고리, 베기탑,점검사다리(점검구) 등의 설치위치/개소는 실시공시 변경될 수 있음
7. 옥상 상부구조물은 PC구조물 임.
8. 정화조 배기는 기계도서 참조

수정번호 REV. NO.	일 자 DATE	내 용 DESCRIPTION	승 인 CHKD
△			
△			
△			
△			

설계 DESIGNED BY

검토 CHECKED BY
최 진 규

심사 SUMMITED BY
정 호 혁

승인 APPROVED BY
이 승 준

일자 DATE
2019.08

도면명 DRAWING TITLE
112동
옥탑지붕 평면도

축 척 SCALE
A1: 1/100
A3: 1/200

도면번호 DRAWING NO.
A-479

일련번호 SHEET NO.

REV. NO. △

HAUD
㈜하우드엔지니어링
종합건축사사무소
Architects, Planners & Engineers
TEL. 02 2140 4400, SEOUL, KOREA

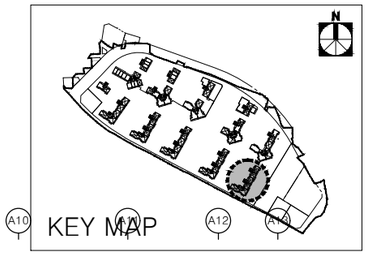

옥탑지붕 SL
지붕 SL
20층 SL
19층 SL
18층 SL
17층 SL
16층 SL
15층 SL
14층 SL
13층 SL
12층 SL
11층 SL
10층 SL
9층 SL
8층 SL
7층 SL
6층 SL
5층 SL
4층 SL
3층 SL
2층 SL
1층 SL
G.L

THK22로이복층유리
외부용수성페인트
지정석재

1 A 112동 정면도
축척 = 1/150

2 A 112동 우측면도
축척 = 1/150

사업번호 PROJECT NO.

사업명 PROJECT TITLE

수색4재정비촉진구역
주택재개발 정비사업

KEY PLAN

NOTE

1. 1층 바닥 LEVEL
   1SL±0 = 1FL±0 = GL±0 = EL+24.20
2. 지붕 난간의 형태 및 설치위치는 안전성과 입면디자인을 고려하여 변경가능함.
3. 지붕의 재료, 형태, 구조는 실시공시 변경될 수 있음.
4. 지붕 및 옥탑구조물의 형태와 구조는 실시공시 변경될 수 있음.
5. 외벽 및 측벽 문양은 실시공시 변경될 수 있음
6. 입면의 줄눈 및 마감선은 실시공시 변경될 수 있음.
7. 저층부 석재마감 및 입면 마감 색상, 재료에 대한 모든 기준은 특화도면을 우선 적용함.

수정번호 REV. NO.	일 자 DATE	내 용 DESCRIPTION	승 인 CHKD

설계 DESIGNED BY

검토 CHECKED BY
최 진 규

심사 SUMMITED BY
정 호 혁

승인 APPROVED BY
이 승 준

일자 DATE
2019.08

도면명 DRAWING TITLE
112동 정면도,우측면도

축척 SCALE
A1: 1/150
A3: 1/300

도면번호 DRAWING NO.
A-480

일련번호 SHEET NO.

REV. NO.

HAUD
(주)하우드엔지니어링
종합건축사사무소
Architects, Planners & Engineers
TEL. 02 2140 4400, SEOUL, KOREA

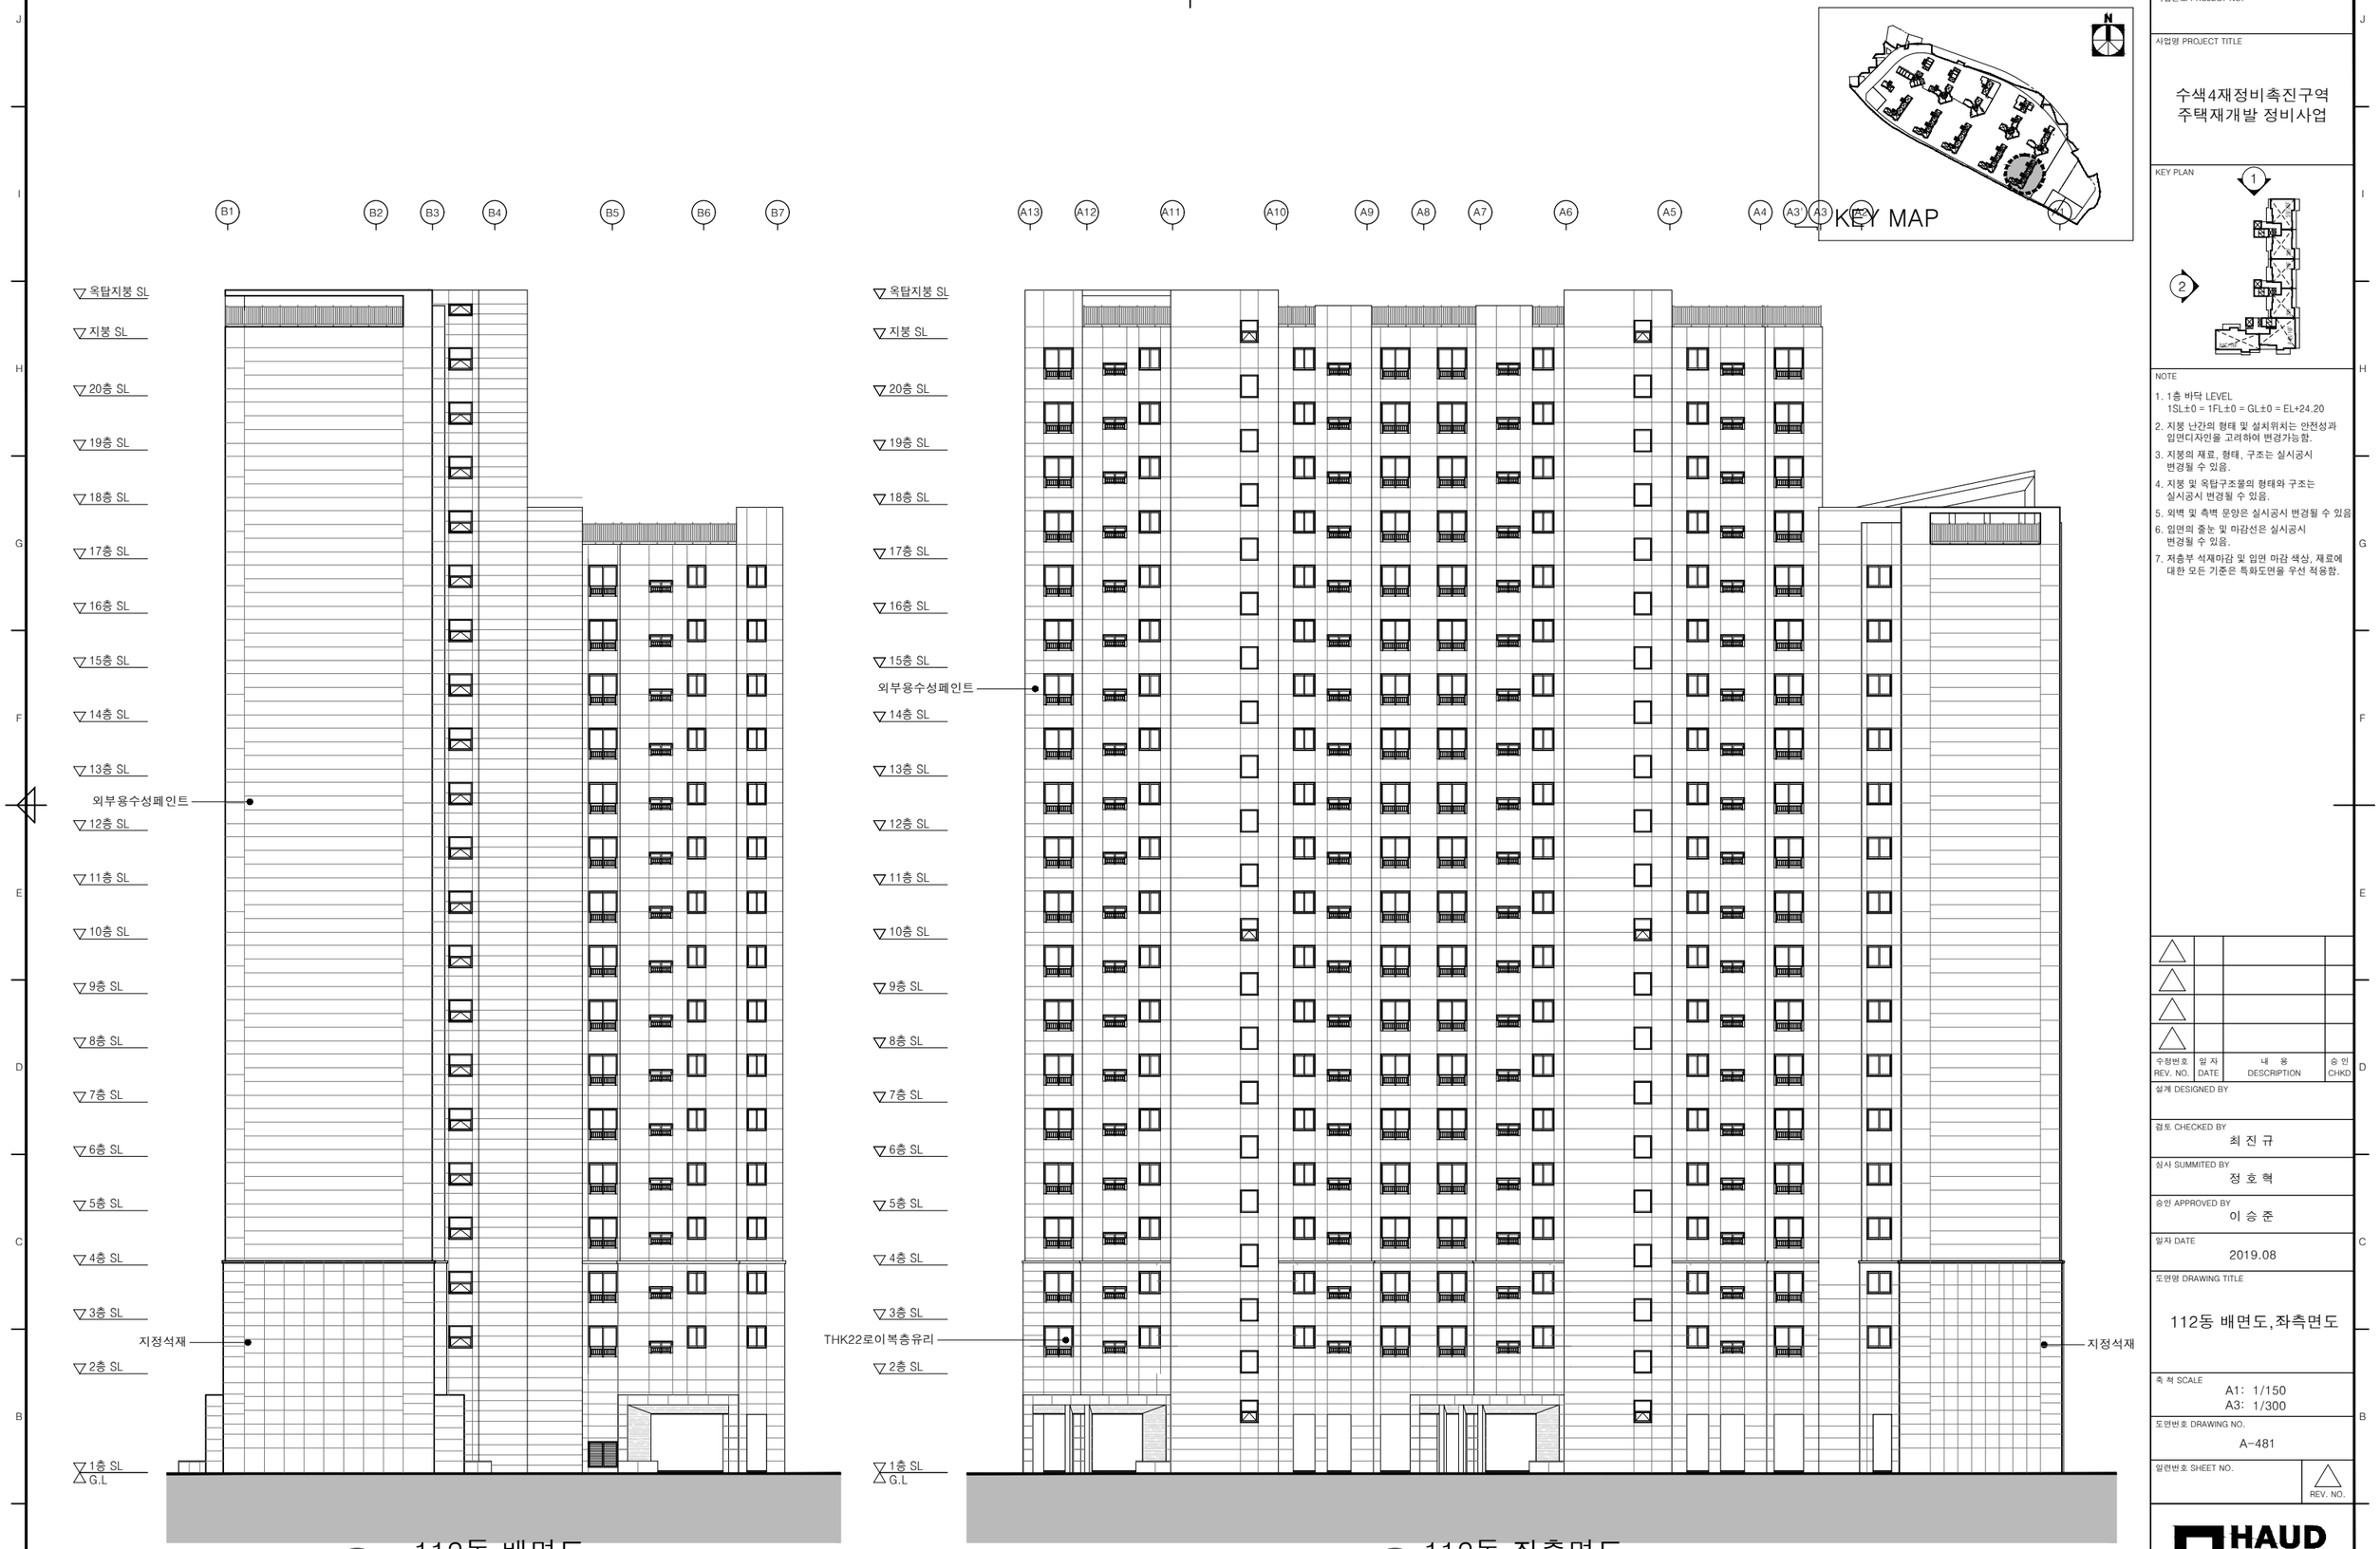

1 A 112동 배면도

축척 = 1/150

2 A 112동 좌측면도

축척 = 1/150

사업번호 PROJECT NO.

사업명 PROJECT TITLE

수색4재정비촉진구역
주택재개발 정비사업

KEY PLAN

NOTE

1. 1층 바닥 LEVEL
   1SL±0 = 1FL±0 = GL±0 = EL+24.20
2. 지붕 난간의 형태 및 설치위치는 안전성과 입면디자인을 고려하여 변경가능함.
3. 지붕의 재료, 형태, 구조는 실시공시 변경될 수 있음.
4. 지붕 및 옥탑구조물의 형태와 구조는 실시공시 변경될 수 있음.
5. 외벽 및 측벽 문양은 실시공시 변경될 수 있음
6. 입면의 줄눈 및 마감선은 실시공시 변경될 수 있음.
7. 저층부 석재마감 및 입면 마감 색상, 재료에 대한 모든 기준은 특화도면을 우선 적용함.

수정번호 REV. NO.	일 자 DATE	내 용 DESCRIPTION	승 인 CHKD
△			
△			
△			
△			

설계 DESIGNED BY

검토 CHECKED BY
최 진 규

심사 SUMMITED BY
정 호 혁

승인 APPROVED BY
이 승 준

일자 DATE
2019.08

도면명 DRAWING TITLE
112동 배면도,좌측면도

축 척 SCALE
A1: 1/150
A3: 1/300

도면번호 DRAWING NO.
A-481

일련번호 SHEET NO.

△ REV. NO.

HAUD
㈜하우드엔지니어링
종합건축사사무소
Architects, Planners & Engineers
TEL. 82 2 140 4400, SEOUL, KOREA

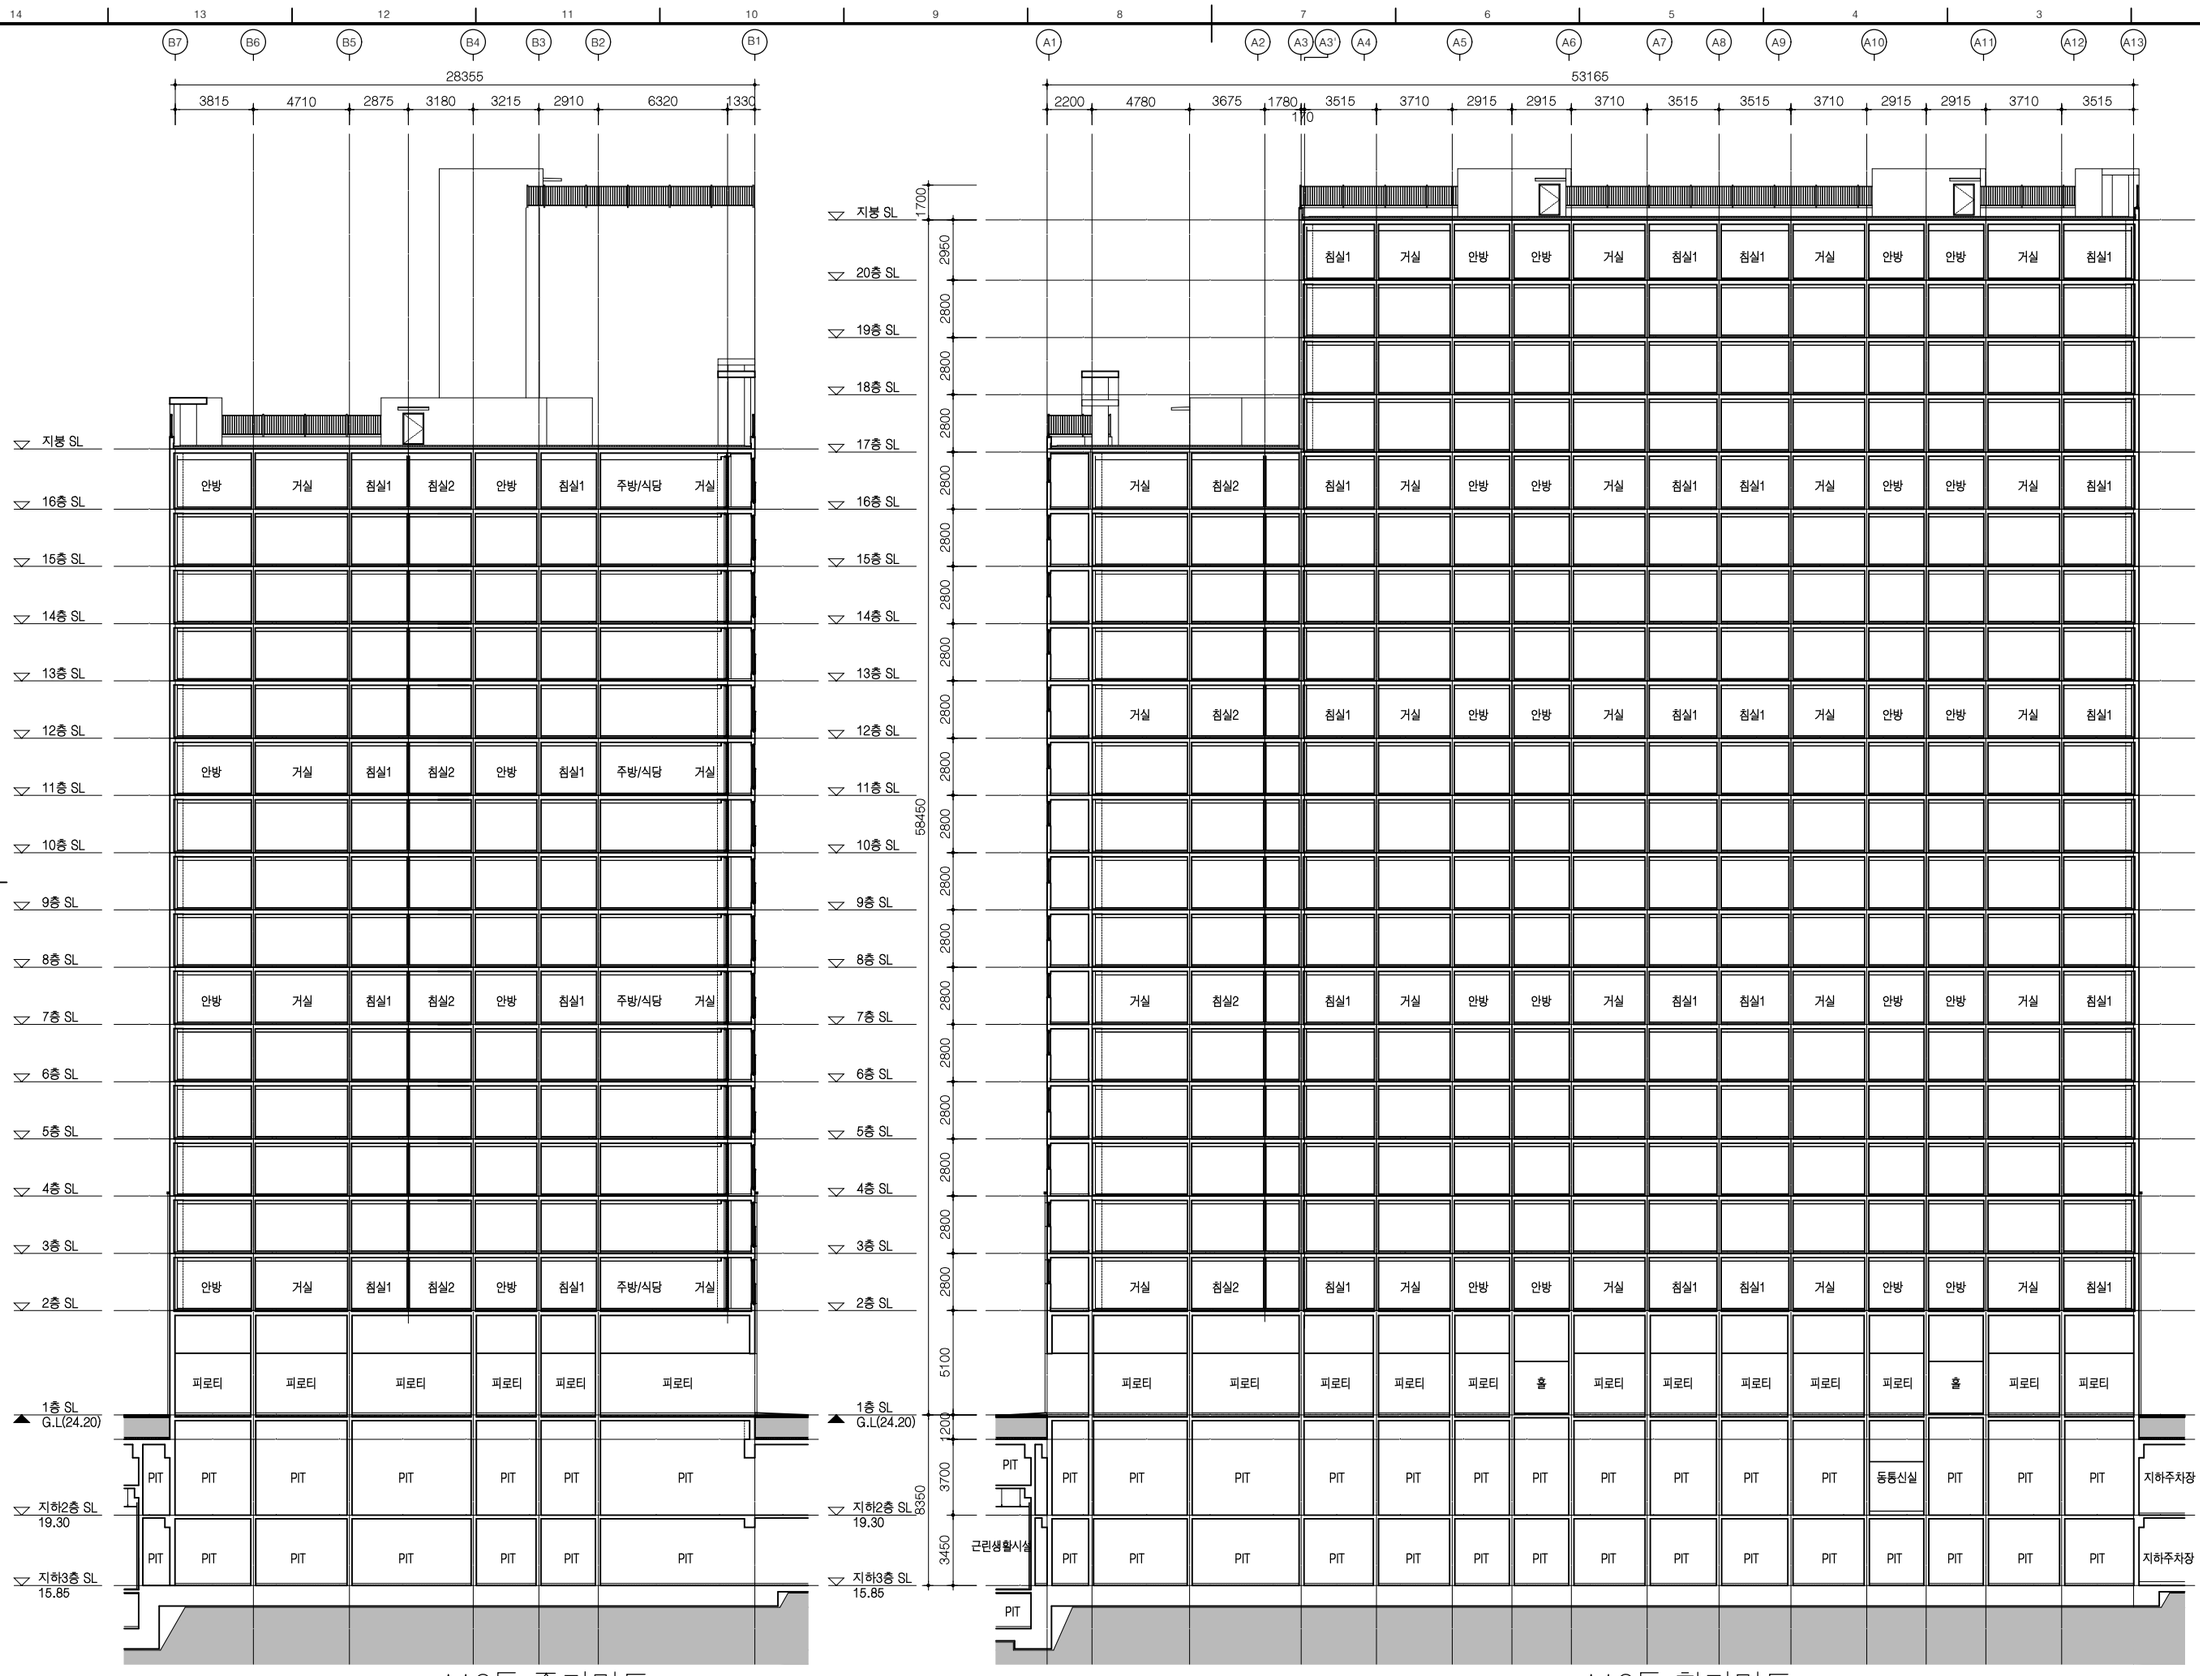

1 A 112동 종단면도

축척 = 1/150

2 A 112동 횡단면도

축척 = 1/150

사업번호 PROJECT NO.

사업명 PROJECT TITLE

수색4재정비촉진구역
주택재개발 정비사업

KEY PLAN

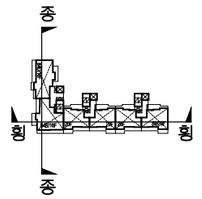

NOTE

수정번호 REV. NO.	일 자 DATE	내 용 DESCRIPTION	승 인 CHKD
△			
△			
△			
△			

설계 DESIGNED BY

검토 CHECKED BY
최 진 규

심사 SUMMITED BY
정 호 혁

승인 APPROVED BY
이 승 준

일자 DATE
2019.08

도면명 DRAWING TITLE
112동 종,횡단면도

축 척 SCALE
A1: 1/150
A3: 1/300

도면번호 DRAWING NO.
A-482

일련번호 SHEET NO.

△ REV. NO.

HAUD
(주)하우드엔지니어링
종합건축사사무소
Architects, Planners & Engineers
TEL. 02 2140 4400, SEOUL, KOREA

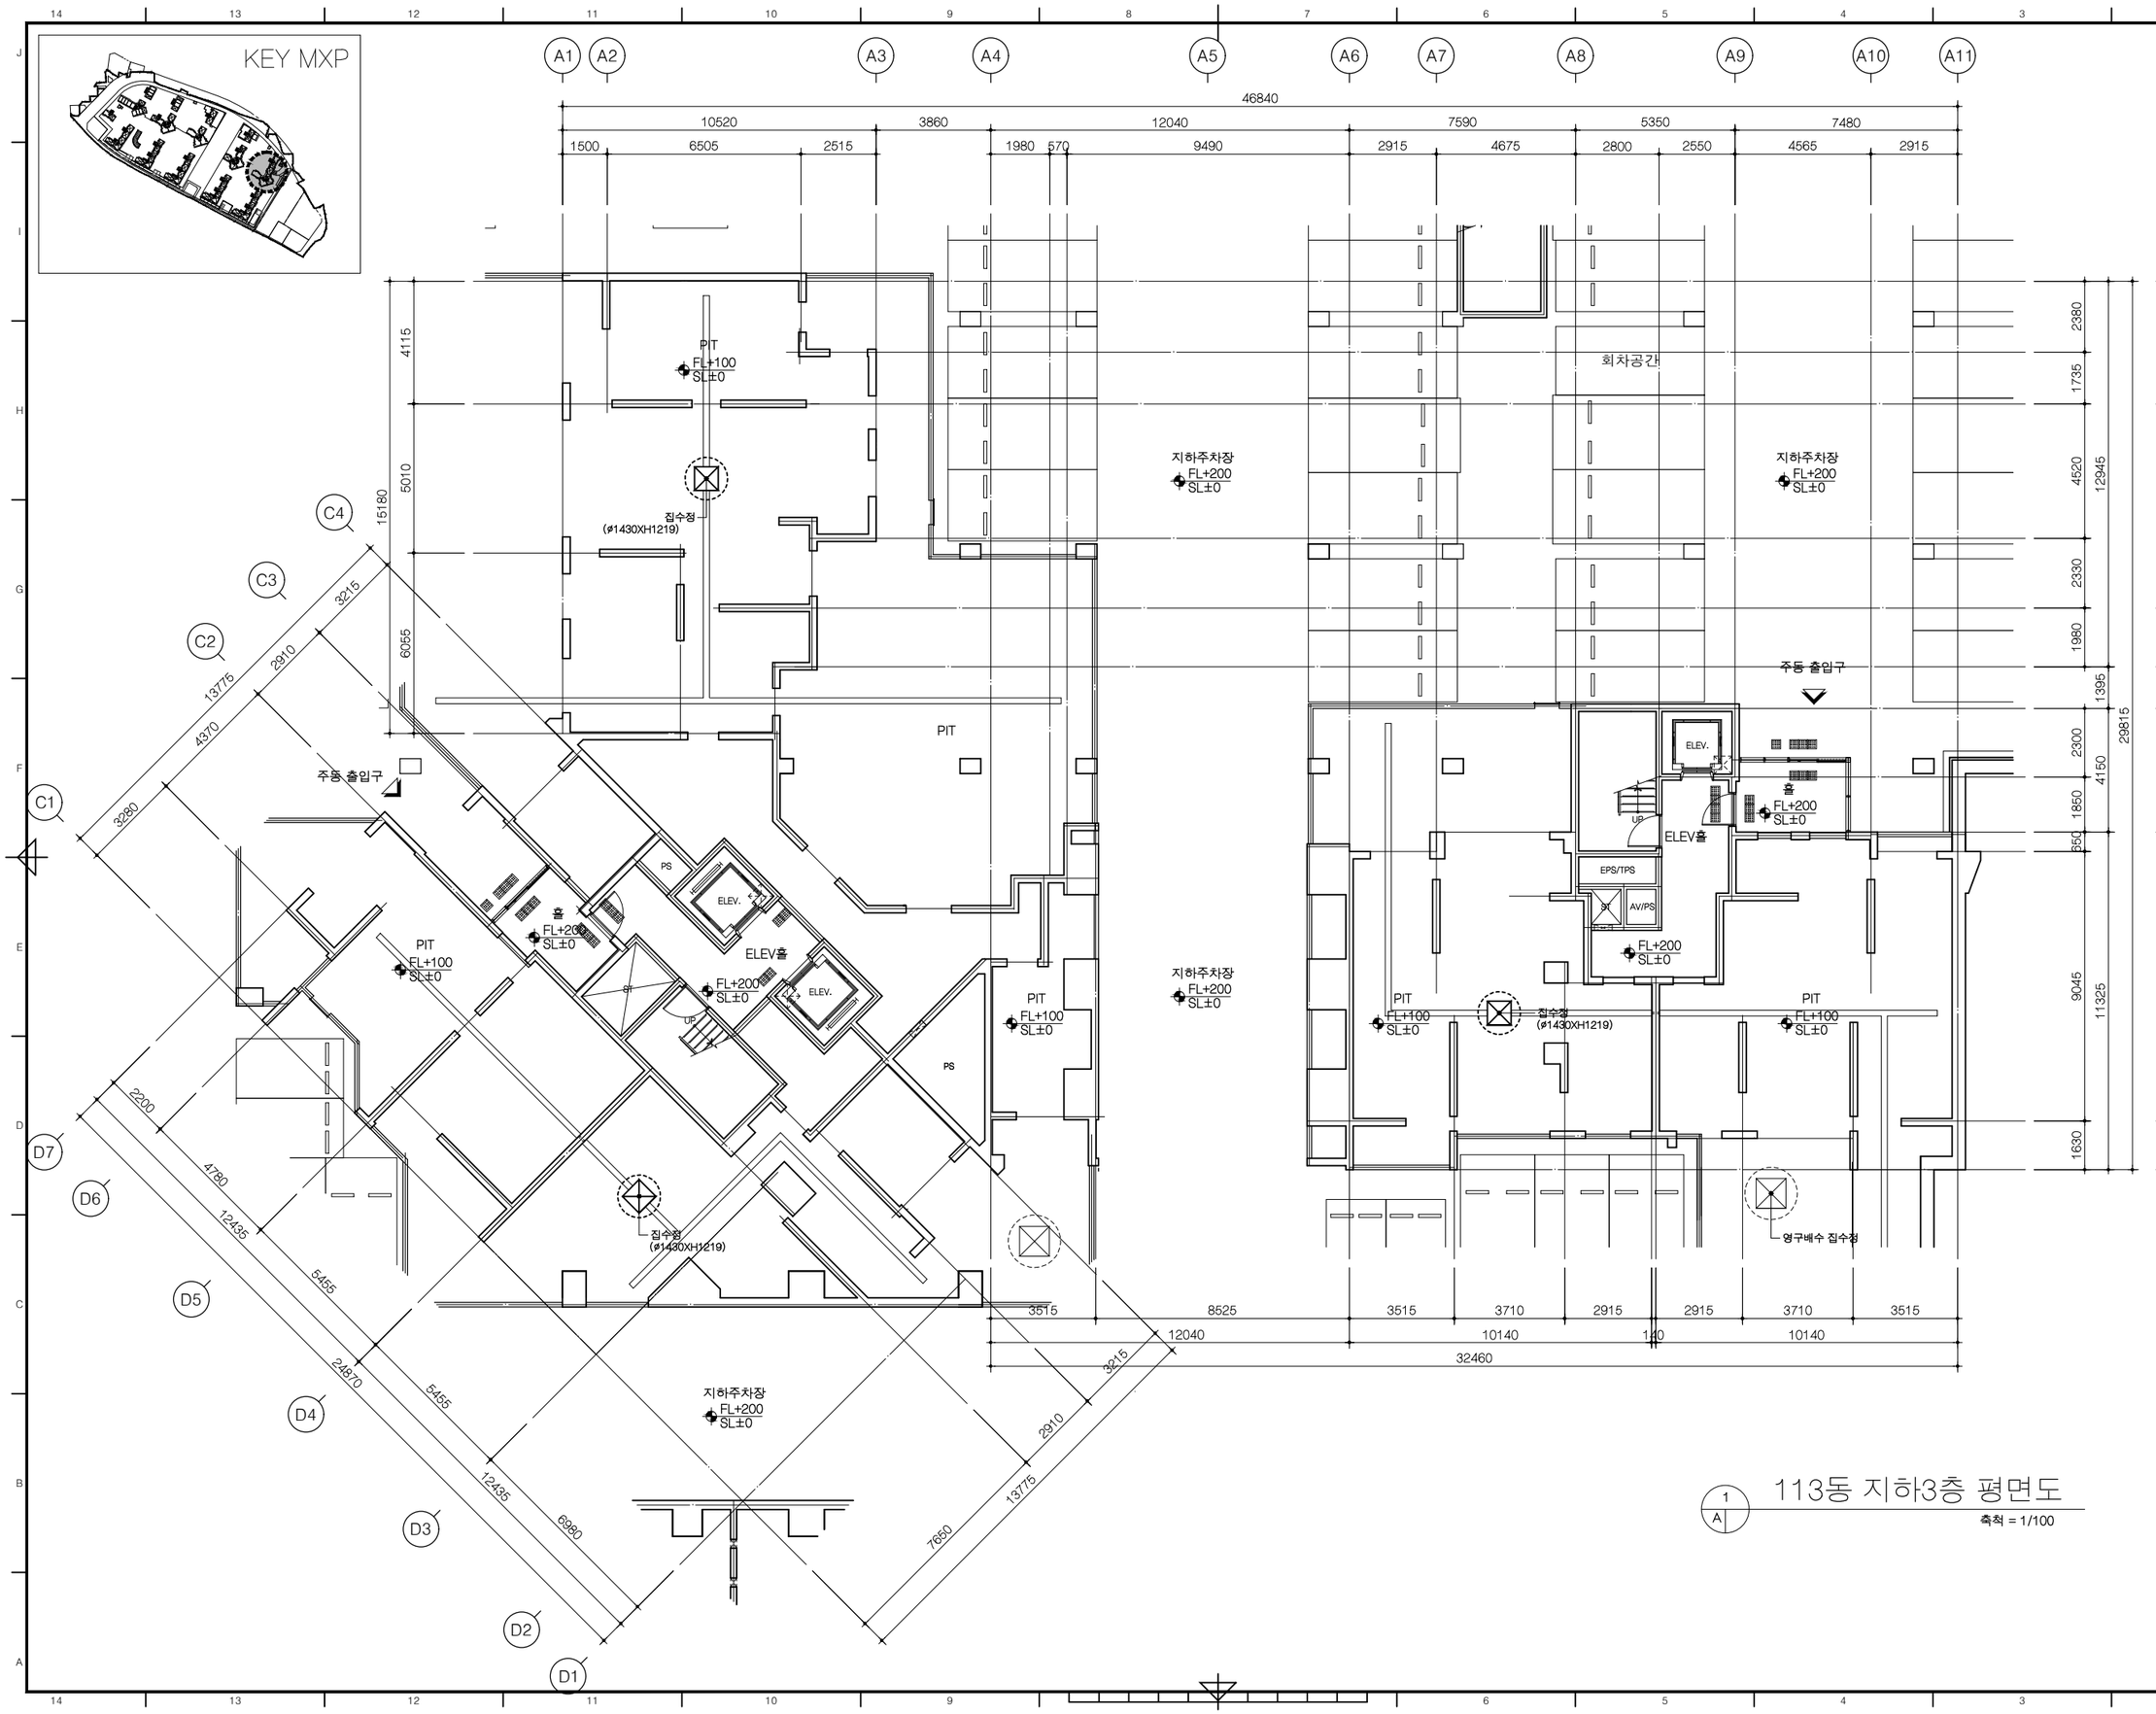

1 A 113동 지하3층 평면도

축척 = 1/100

사업번호 PROJECT NO.

사업명 PROJECT TITLE

수색4재정비촉진구역
주택재개발 정비사업

KEY PLAN

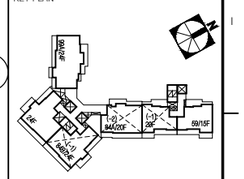

NOTE

1. 지하층 무근 콘크리트는 실시공시 THK80~120 범위로 변동이 있을수 있음.(SLOPE)
2. ELEV홀에 면한부위는 1.0B 조적쌓기임.
3. 지하주차장의 블록쌓기 기준은 높이가 3.6m이하인 경우 4인치 보강블록쌓기가 기준임 (단, 5.4m이하는 6인치쌓기, 5.4m초과는 8인치쌓기가 기준임)
4. ELEV.PIT 집수정은 (600X600X600)임.
5. 주차장 내의 창호는 주차장 창호도 참조.
6. 주차장 집수정 및 영구배수 집수정의 크기 및 위치는 지하주차장 평면도를 참조 할 것.

▨ : 주차장 집수정
▨ : 영구배수 집수정

•••••••••••••••• 지하3층 바닥LEVEL
B3SL±0 = B3FL±0 = EL+15.85

수정번호 REV. NO.	일 자 DATE	내 용 DESCRIPTION	승 인 CHKD

설계 DESIGNED BY

검토 CHECKED BY
최 진 규

심사 SUMMITED BY
정 호 혁

승인 APPROVED BY
이 승 준

일자 DATE
2019.08

도면명 DRAWING TITLE

113동
지하3층 평면도

축 척 SCALE
A1: 1/100
A3: 1/200

도면번호 DRAWING NO.
A-491

일련번호 SHEET NO.

REV. NO.

HAUD
(주)하우드엔지니어링
종합건축사사무소
Architects, Planners & Engineers
TEL. 02 2140 4400, SEOUL, KOREA

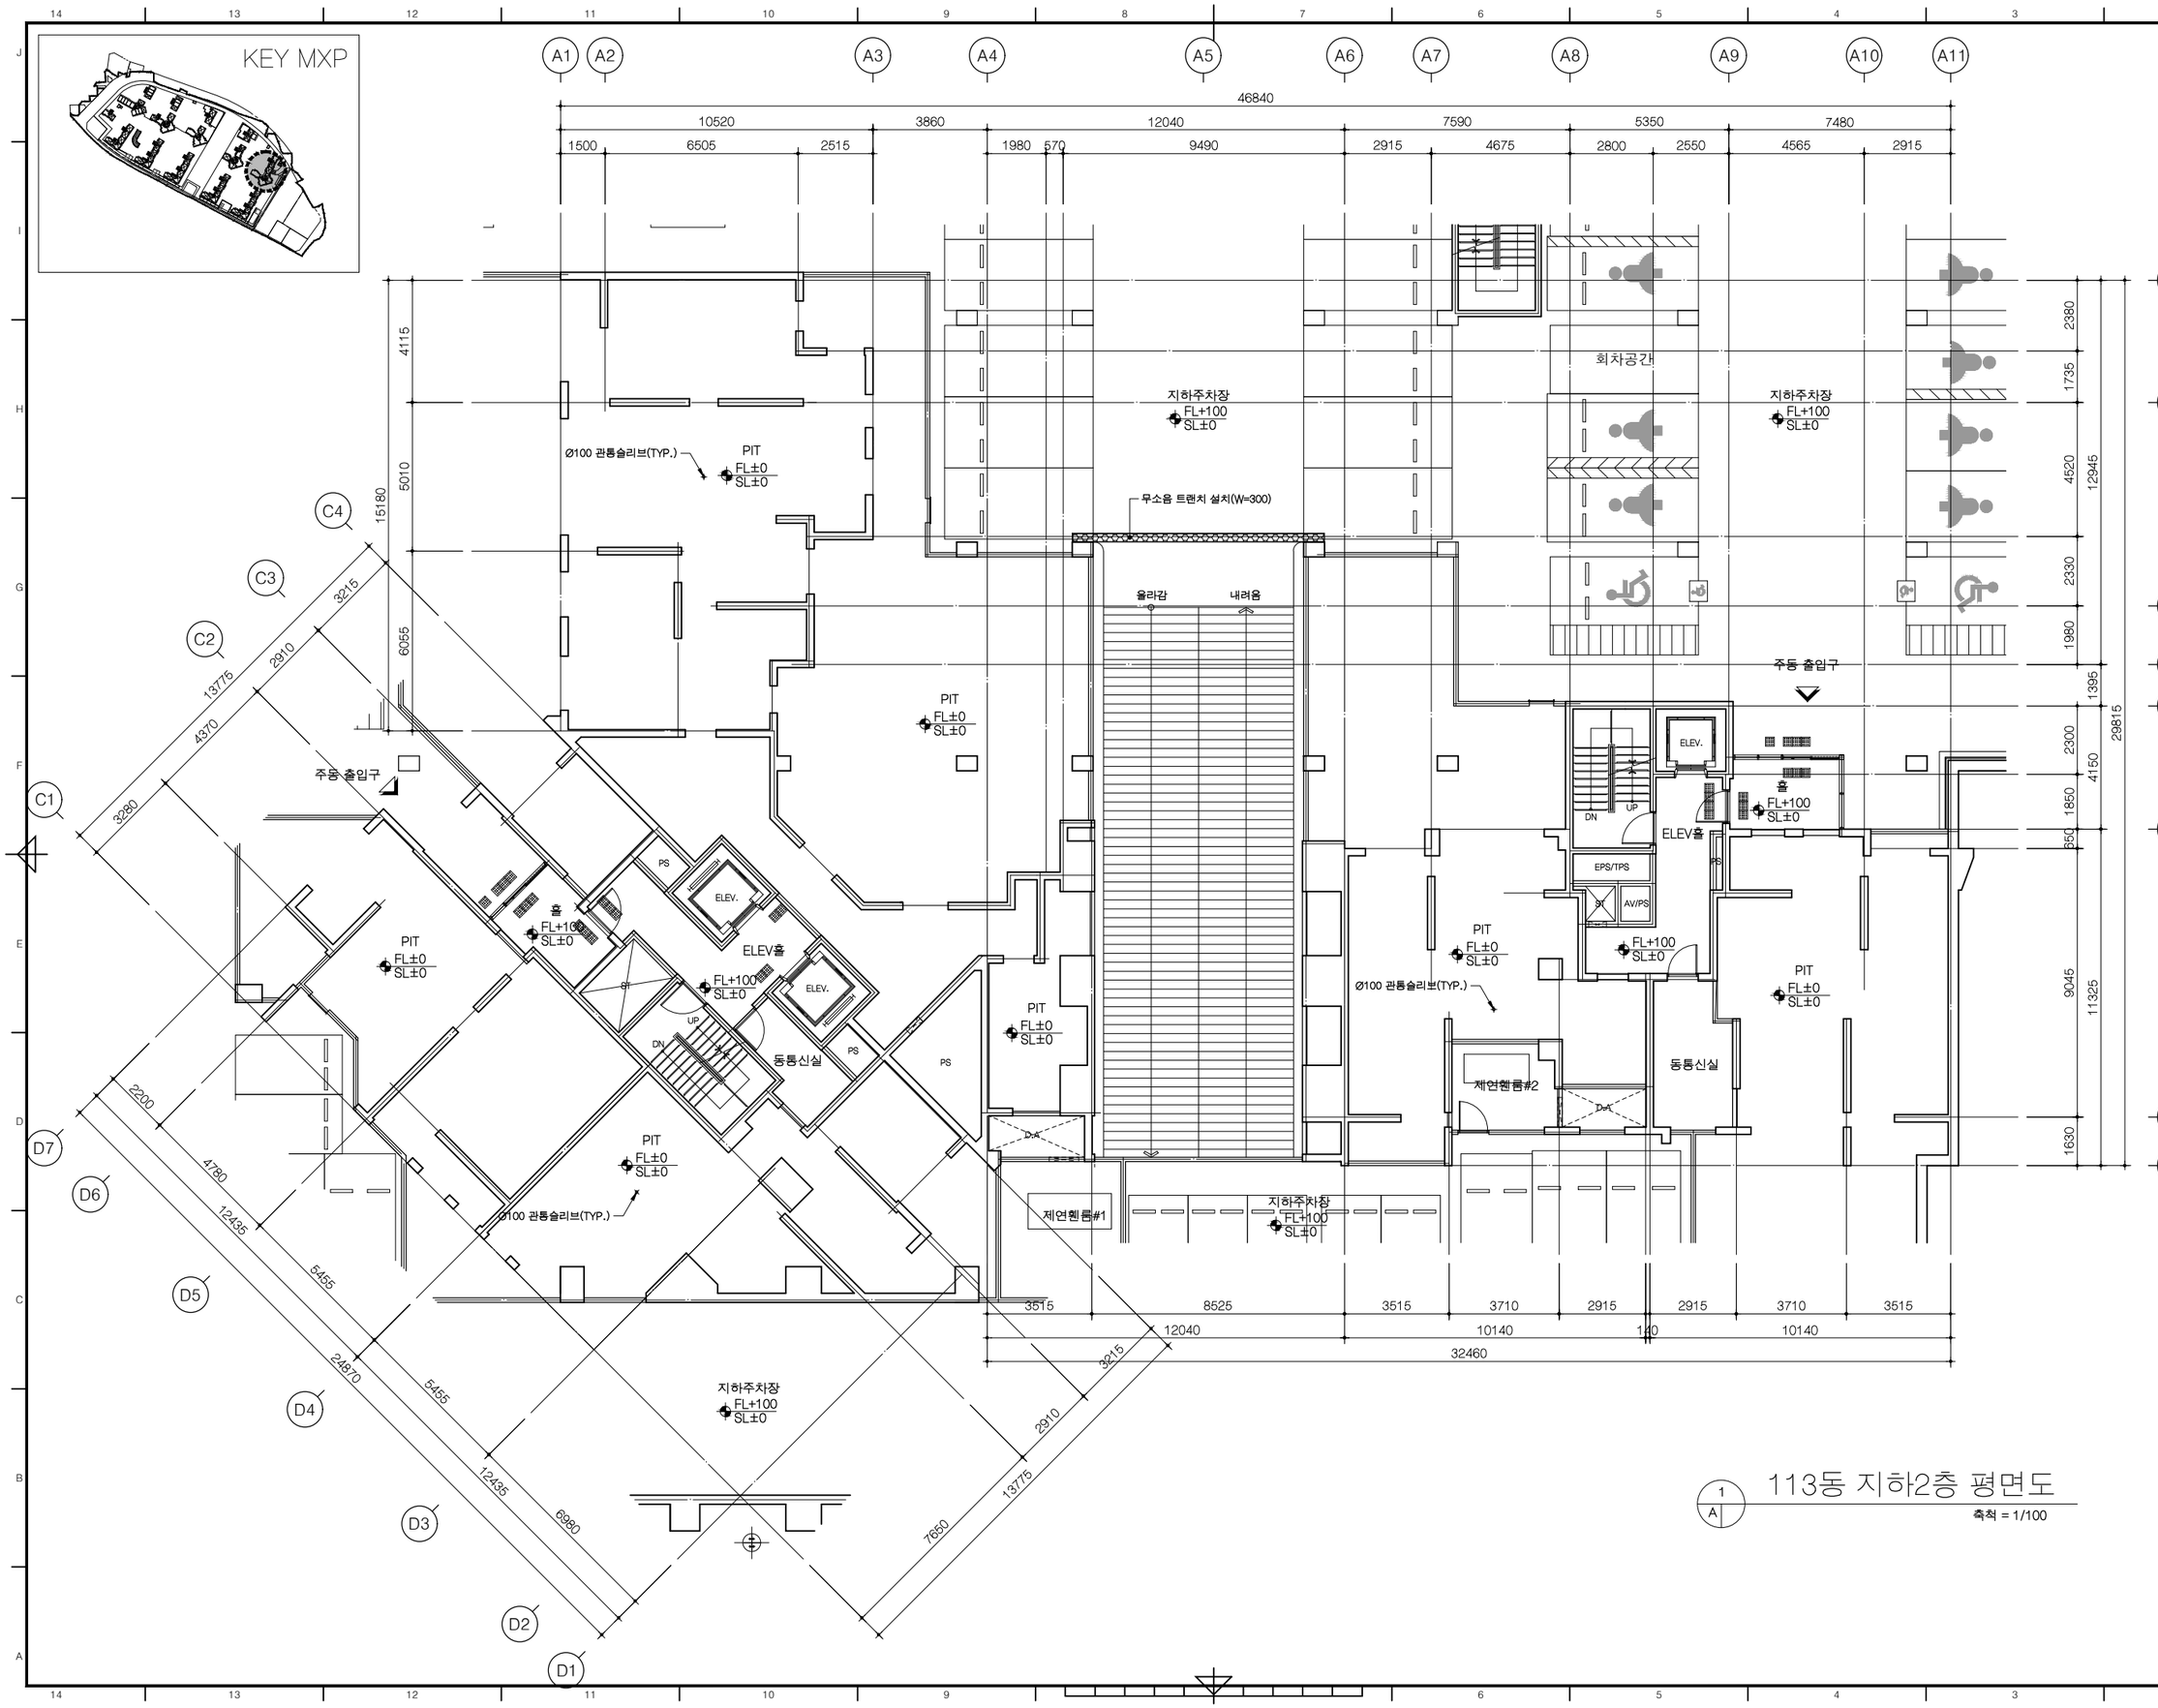

1 A 113동 지하2층 평면도

축척 = 1/100

사업번호 PROJECT NO.

사업명 PROJECT TITLE

수색4재정비촉진구역
주택재개발 정비사업

KEY PLAN

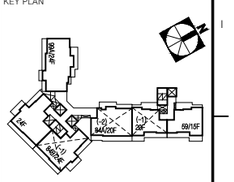

NOTE

1. 지하주차장의 ELEV홀에 면한부위는 1.0B 조적쌓기임.
2. 지하주차장의 블록쌓기 기준은 높이가 3.6m이하인 경우 4인치 보강블록쌓기가 기준임 (단, 5.4m이하는 6인치쌓기, 5.4m초과는 8인치쌓기가 기준임)
3. 주차장 내의 창호는 주차장 창호도 참조.

**** 지하2층 바닥LEVEL
D2SL±0 = D2FL±0 = EL+19.30

수정번호 REV. NO.	일 자 DATE	내 용 DESCRIPTION	승 인 CHKD

설계 DESIGNED BY

검토 CHECKED BY
최 진 규

심사 SUMMITED BY
정 호 혁

승인 APPROVED BY
이 승 준

일자 DATE
2019.08

도면명 DRAWING TITLE

113동
지하2층 평면도

축 척 SCALE
A1: 1/100
A3: 1/200

도면번호 DRAWING NO.
A-492

일련번호 SHEET NO.

REV. NO.

HAUD
(주)하우드엔지니어링
종합건축사사무소
Architects, Planners & Engineers
TEL. 02 2140 4400, SEOUL, KOREA

113동 1층 평면도

축척 = 1/100

사업번호 PROJECT NO.

사업명 PROJECT TITLE

수색4재정비촉진구역
주택재개발 정비사업

KEY PLAN

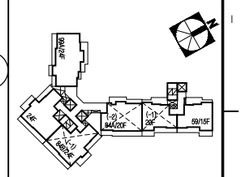

NOTE

1. 본 도면은 발코니 확장전를 기준으로 작성됨.
2. 지붕층 난간의 형태와 설치 위치는 안전성과 입면디자인을 고려하여 변경 가능함.
3. 지붕의 재료, 형태, 구조는 실시공 시 변경 될 수 있음.
4. 지붕 및 옥탑 구조물의 형태와 구조는 실시공 시 변경될 수 있음.
5. 옥상 출눈의 간격은 실시공 시 변경될 수 있음.
6. 옥상 출눈 틈에 실란트 시공되지 않음
7. 우편물 수취함 설치 위치는 변경될 수 있음

• 1층 바닥LEVEL
1SL±0 = 1FL±0 = GL±0 = EL+24.80
GL-600 = EL+24.20(토목도면 참조)

수정번호 REV. NO.	일 자 DATE	내 용 DESCRIPTION	승 인 CHKD
△			
△			
△			
△			

설계 DESIGNED BY

검토 CHECKED BY
최 진 규

심사 SUMMITED BY
정 호 혁

승인 APPROVED BY
이 승 준

일자 DATE
2019.08

도면명 DRAWING TITLE
113동
1층 평면도

축 척 SCALE
A1: 1/100
A3: 1/200

도면번호 DRAWING NO.
A-493

일련번호 SHEET NO.

REV. NO.

HAUD
(주)하우드엔지니어링
종합건축사사무소
Architects, Planners & Engineers
TEL. 02 2149 4400, SEOUL, KOREA

113동 2층 평면도

축척 = 1/100

사업번호 PROJECT NO.

사업명 PROJECT TITLE

수색4재정비촉진구역
주택재개발 정비사업

KEY PLAN

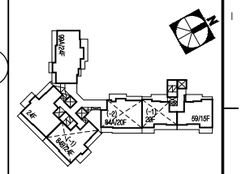

NOTE

1. 본 도면은 발코니 확장전를 기준으로 작성됨.
2. 지붕층 난간의 형태와 설치 위치는 안전성과 입면디자인을 고려하여 변경 가능함.
3. 지붕의 재료, 형태, 구조는 실시공 시 변경 될 수 있음.
4. 지붕 및 옥탑 구조물의 형태와 구조는 실시공 시 변경될 수 있음.
5. 옥상 줄눈의 간격은 실시공 시 변경될 수 있음.
6. 옥상 줄눈 틈에 실란트 시공되지 않음
7. 우편물 수취함 설치 위치는 변경될 수 있음
8. 오픈형 발코니 3층이상 ~ 20층이하 설치

2층 바닥LEVEL
2SL±0 = 2FL±0 = EL+28.00

수정번호 REV. NO.	일 자 DATE	내 용 DESCRIPTION	승 인 CHKD

설계 DESIGNED BY

검토 CHECKED BY
최 진 규

심사 SUMMITED BY
정 호 혁

승인 APPROVED BY
이 승 준

일자 DATE
2019.08

도면명 DRAWING TITLE
113동
2층 평면도

축 척 SCALE
A1: 1/100
A3: 1/200

도면번호 DRAWING NO.
A-494

일련번호 SHEET NO.

REV. NO.

HAUD
(주)하우드엔지니어링
종합건축사사무소
Architects, Planners & Engineers
TEL. 02 2149 4400, SEOUL, KOREA

1 A 113동 3층 평면도

축척 = 1/100

사업번호 PROJECT NO.

사업명 PROJECT TITLE

수색4재정비촉진구역
주택재개발 정비사업

KEY PLAN

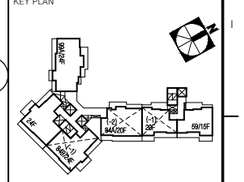

NOTE

1. 본 도면은 발코니 확장전를 기준으로 작성됨.
2. 지붕층 난간의 형태와 설치 위치는 안전성과 입면디자인을 고려하여 변경 가능함.
3. 지붕의 재료, 형태, 구조는 실시공 시 변경 될 수 있음.
4. 지붕 및 옥탑 구조물의 형태와 구조는 실시공 시 변경될 수 있음.
5. 옥상 출눈의 간격은 실시공 시 변경될 수 있음.
6. 옥상 출눈 틈에 실란트 시공되지 않음
7. 우편물 수취함 설치 위치는 변경될 수 있음
8. 오픈형 발코니 3층이상 ~ 20층이하 설치

수정번호 REV. NO.	일 자 DATE	내 용 DESCRIPTION	승 인 CHKD

설계 DESIGNED BY

검토 CHECKED BY
최 진 규

심사 SUMMITED BY
정 호 혁

승인 APPROVED BY
이 승 준

일자 DATE
2019.08

도면명 DRAWING TITLE
113동
3층 평면도

축 척 SCALE
A1: 1/100
A3: 1/200

도면번호 DRAWING NO.
A-495

일련번호 SHEET NO.

REV. NO.

HAUD
(주)하우드랜지니어링
종합건축사사무소
Architects, Planners & Engineers
TEL. 82 2) 49 4409, SEOUL, KOREA

1 A 113동 4~15층 평면도

축척 = 1/100

사업번호 PROJECT NO.

사업명 PROJECT TITLE

수색4재정비촉진구역
주택재개발 정비사업

KEY PLAN

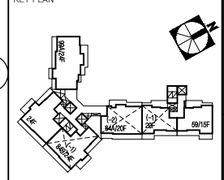

NOTE

1. 본 도면은 발코니 확장전를 기준으로 작성됨.
2. 지붕층 난간의 형태와 설치 위치는 안전성과 입면디자인을 고려하여 변경 가능함.
3. 지붕의 재료, 형태, 구조는 실시공 시 변경 될 수 있음.
4. 지붕 및 옥탑 구조물의 형태와 구조는 실시공 시 변경될 수 있음.
5. 옥상 출눈의 간격은 실시공 시 변경될 수 있음.
6. 옥상 출눈 틈에 실란트 시공되지 않음
7. 우편물 수취함 설치 위치는 변경될 수 있음
8. 오픈형 발코니 3층이상 ~ 20층이하 설치

수정번호 REV. NO.	일 자 DATE	내 용 DESCRIPTION	승 인 CHKD
△			
△			
△			
△			

설계 DESIGNED BY

검토 CHECKED BY
최 진 규

심사 SUMMITED BY
정 호 혁

승인 APPROVED BY
이 승 준

일자 DATE
2019.08

도면명 DRAWING TITLE
113동
4~15층 평면도

축 척 SCALE
A1: 1/100
A3: 1/200

도면번호 DRAWING NO.
A-496

일련번호 SHEET NO.

REV. NO. △

HAUD
(주)하우드엔지니어링
종합건축사사무소
Architects, Planners & Engineers
TEL. 02 3143 4400, SEOUL, KOREA

사업번호 PROJECT NO.

사업명 PROJECT TITLE

수색4재정비촉진구역
주택재개발 정비사업

KEY PLAN

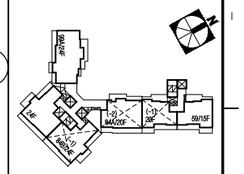

NOTE

1. 본 도면은 발코니 확장전를 기준으로 작성됨.
2. 지붕층 난간의 형태와 설치 위치는 안전성과 입면디자인을 고려하여 변경 가능함.
3. 지붕의 재료, 형태, 구조는 실시공 시 변경 될 수 있음.
4. 지붕 및 옥탑 구조물의 형태와 구조는 실시공 시 변경될 수 있음.
5. 옥상 출눈의 간격은 실시공 시 변경될 수 있음.
6. 옥상 출눈 틈에 실란트 시공되지 않음
7. 우편물 수취함 설치 위치는 변경될 수 있음
8. 오픈형 발코니 3층이상 ~ 20층이하 설치

수정번호 REV. NO.	일 자 DATE	내 용 DESCRIPTION	승 인 CHKD

설계 DESIGNED BY

검토 CHECKED BY
최 진 규

심사 SUMMITED BY
정 호 혁

승인 APPROVED BY
이 승 준

일자 DATE
2019.08

도면명 DRAWING TITLE
113동
16층 평면도

축 척 SCALE
A1: 1/100
A3: 1/200

도면번호 DRAWING NO.
A-497

일련번호 SHEET NO.

REV. NO.

HAUD
(주)하우드엔지니어링
종합건축사사무소
Architects, Planners & Engineers
TEL. 02 2149 4400, SEOUL, KOREA

1 / A 113동 16층 평면도
축척 = 1/100

1 / A 113동 17층 평면도

축척 = 1/100

사업번호 PROJECT NO.

사업명 PROJECT TITLE

수색4재정비촉진구역
주택재개발 정비사업

KEY PLAN

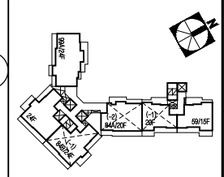

NOTE

1. 본 도면은 발코니 확장전를 기준으로 작성됨.
2. 지붕층 난간의 형태와 설치 위치는 안전성과 입면디자인을 고려하여 변경 가능함.
3. 지붕의 재료, 형태, 구조는 실시공 시 변경 될 수 있음.
4. 지붕 및 옥탑 구조물의 형태와 구조는 실시공 시 변경될 수 있음.
5. 옥상 출눈의 간격은 실시공 시 변경될 수 있음.
6. 옥상 출눈 틈에 실란트 시공되지 않음
7. 우편물 수취함 설치 위치는 변경될 수 있음
8. 오픈형 발코니 3층이상 ~ 20층이하 설치

수정번호 REV. NO.	일자 DATE	내 용 DESCRIPTION	승인 CHKD

설계 DESIGNED BY

검토 CHECKED BY
최 진 규

심사 SUMMITED BY
정 호 혁

승인 APPROVED BY
이 승 준

일자 DATE
2019.08

도면명 DRAWING TITLE
113동
17층 평면도

축 척 SCALE
A1: 1/100
A3: 1/200

도면번호 DRAWING NO.
A-498

일련번호 SHEET NO.

REV. NO.

HAUD
(주)하우드엔지니어링
종합건축사사무소
Architects, Planners & Engineers
TEL. 02 2149 4400, SEOUL, KOREA

1 A 113동 18~20층 평면도

축척 = 1/100

사업번호 PROJECT NO.

사업명 PROJECT TITLE

수색4재정비촉진구역
주택재개발 정비사업

KEY PLAN

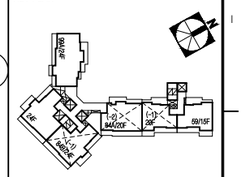

NOTE

1. 본 도면은 발코니 확장전를 기준으로 작성됨.
2. 지붕층 난간의 형태와 설치 위치는 안전성과 입면디자인을 고려하여 변경 가능함.
3. 지붕의 재료, 형태, 구조는 실시공 시 변경 될 수 있음.
4. 지붕 및 옥탑 구조물의 형태와 구조는 실시공 시 변경될 수 있음.
5. 옥상 출눈의 간격은 실시공 시 변경될 수 있음.
6. 옥상 출눈 틈에 실란트 시공되지 않음
7. 우편물 수취함 설치 위치는 변경될 수 있음
8. 오픈형 발코니 3층이상 ~ 20층이하 설치

수정번호 REV. NO.	일 자 DATE	내 용 DESCRIPTION	승 인 CHKD
1			
2			
3			
4			

설계 DESIGNED BY

검토 CHECKED BY
최 진 규

심사 SUMMITED BY
정 호 혁

승인 APPROVED BY
이 승 준

일자 DATE
2019.08

도면명 DRAWING TITLE
113동
18~20층 평면도

축 척 SCALE
A1: 1/100
A3: 1/200

도면번호 DRAWING NO.
A-499

일련번호 SHEET NO.

REV. NO.

HAUD
(주)하우드엔지니어링
종합건축사사무소
Architects, Planners & Engineers
TEL. 02 2149 4400, SEOUL, KOREA

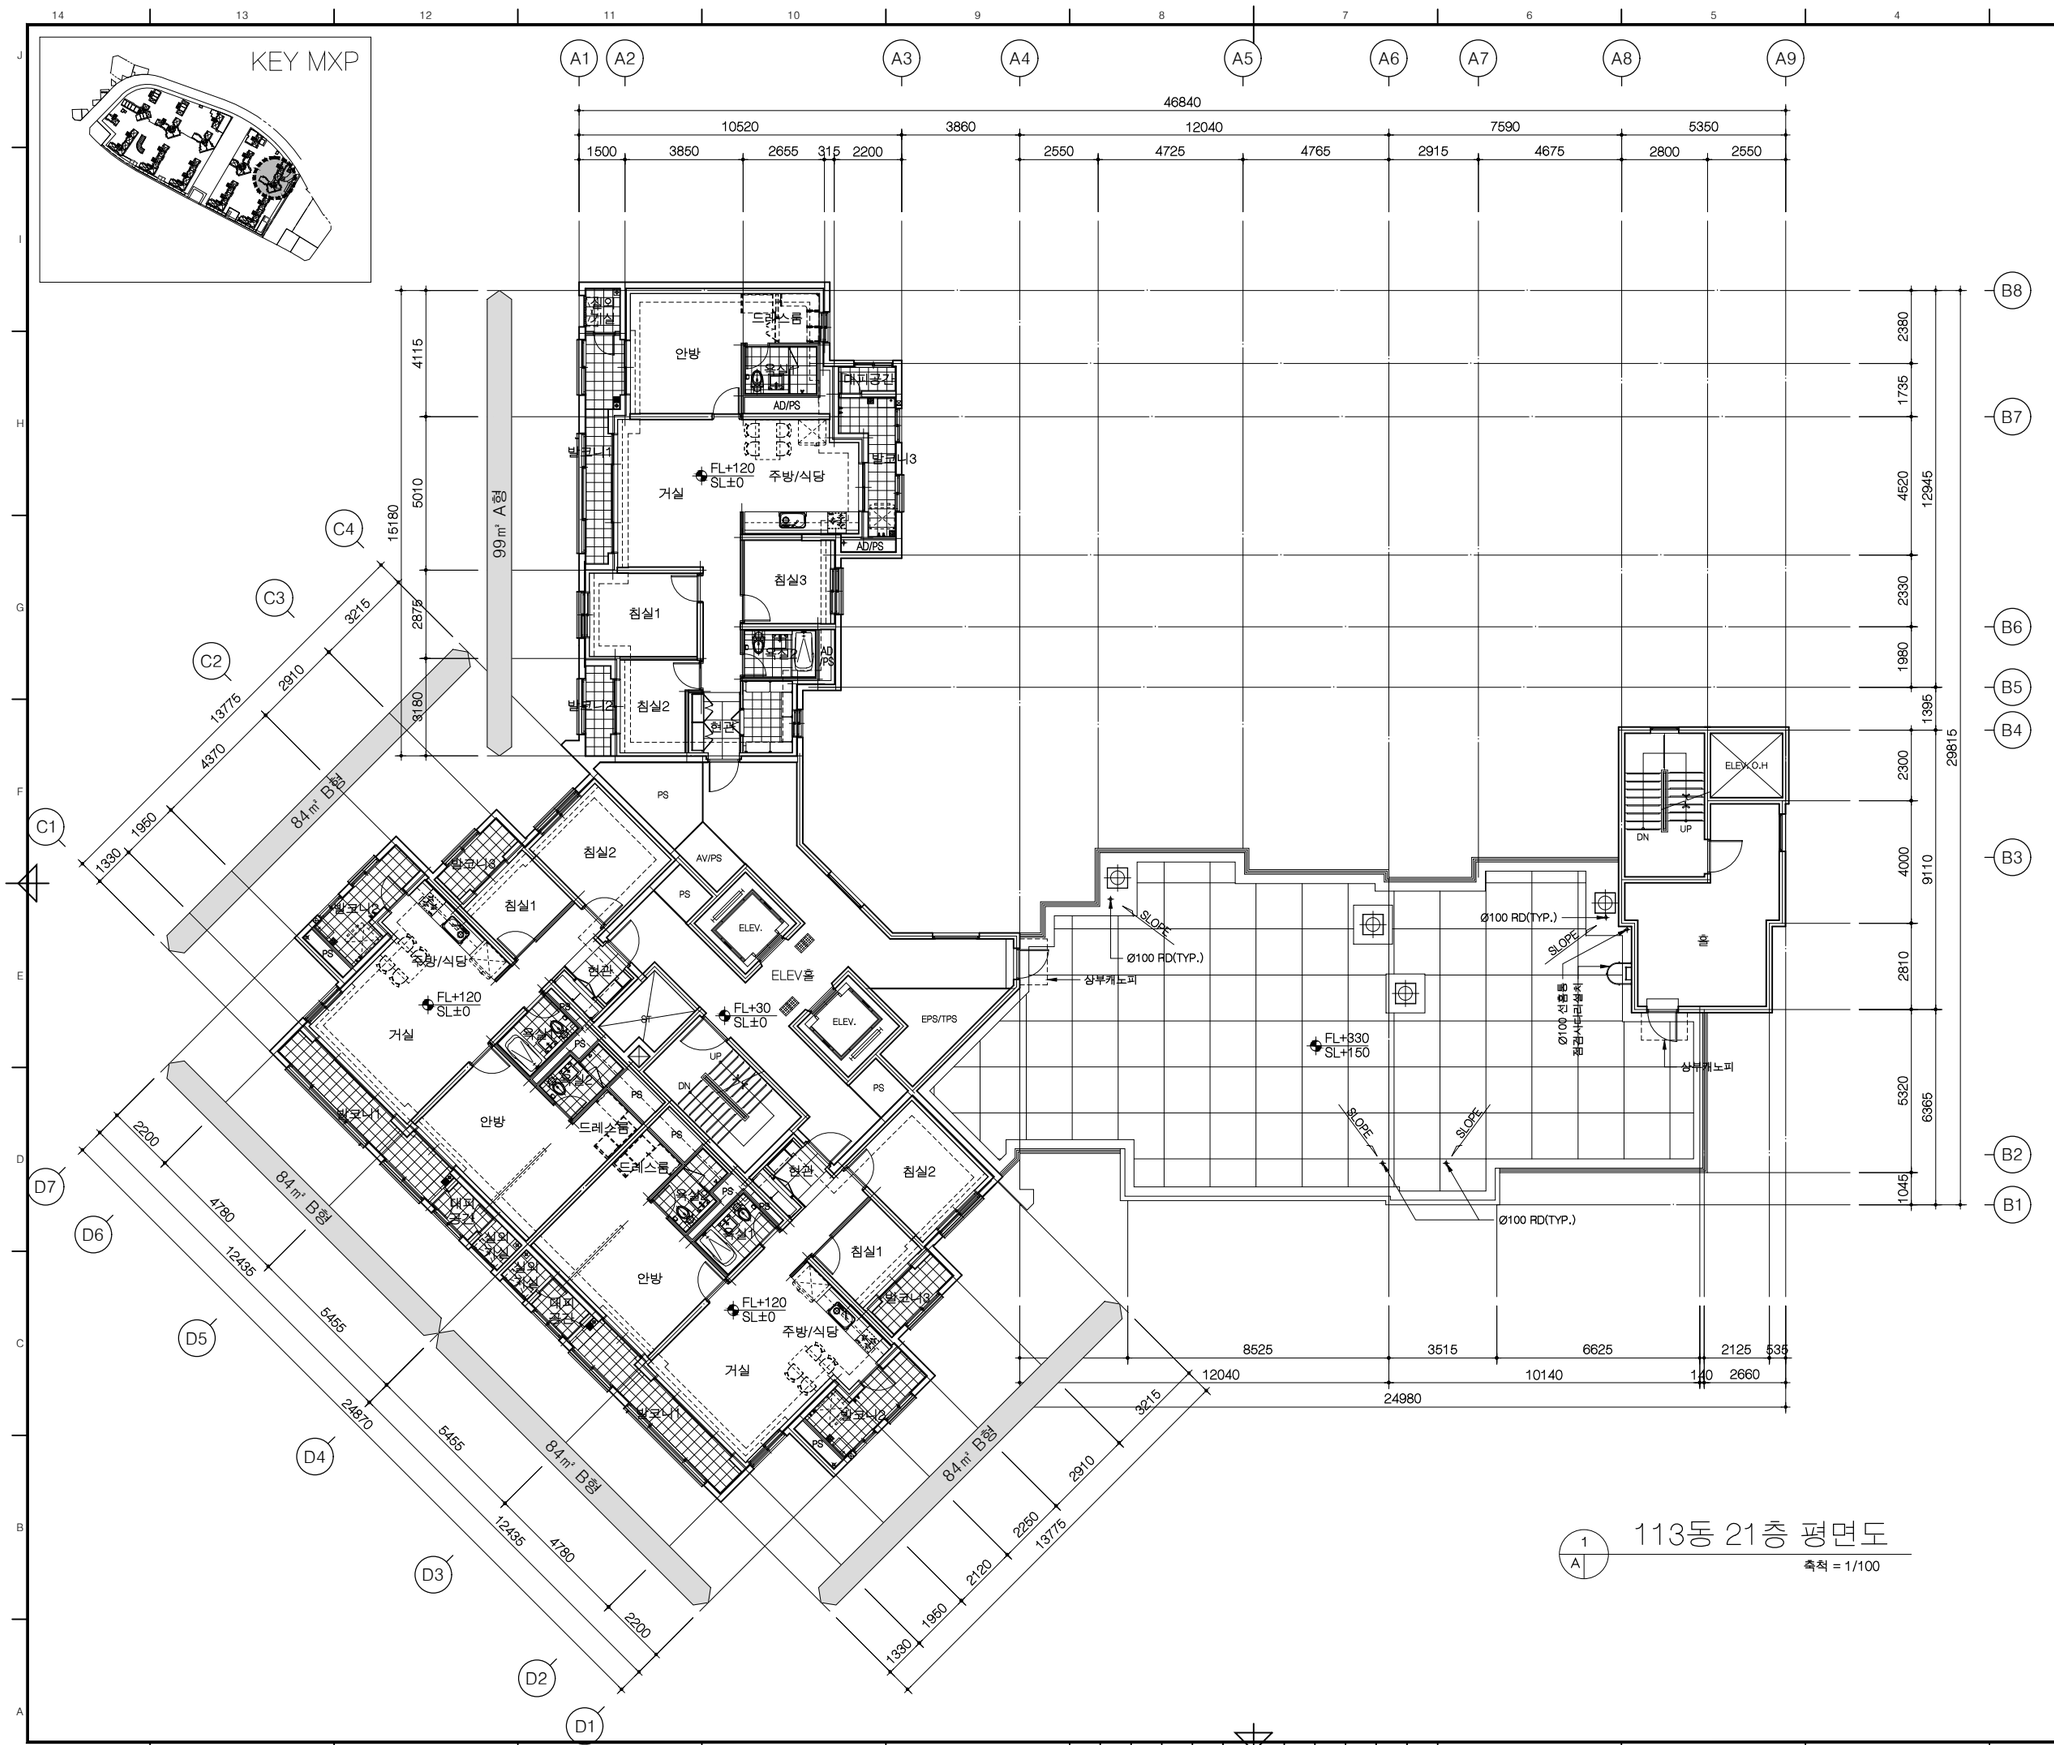

1 A 113동 21층 평면도

축척 = 1/100

사업번호 PROJECT NO.

사업명 PROJECT TITLE

수색4재정비촉진구역
주택재개발 정비사업

KEY PLAN

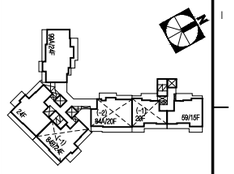

NOTE

1. 본 도면은 발코니 확장전를 기준으로 작성됨.
2. 지붕층 난간의 형태와 설치 위치는 안전성과 입면디자인을 고려하여 변경 가능함.
3. 지붕의 재료, 형태, 구조는 실시공 시 변경 될 수 있음.
4. 지붕 및 옥탑 구조물의 형태와 구조는 실시공 시 변경될 수 있음.
5. 옥상 출눈의 간격은 실시공 시 변경될 수 있음.
6. 옥상 출눈 틈에 실란트 시공되지 않음
7. 우편물 수취함 설치 위치는 변경될 수 있음
8. 오픈형 발코니 3층이상 ~ 20층이하 설치

수정번호 REV. NO.	일 자 DATE	내 용 DESCRIPTION	승 인 CHKD

설계 DESIGNED BY

검토 CHECKED BY
최 진 규

심사 SUMMITED BY
정 호 혁

승인 APPROVED BY
이 승 준

일자 DATE
2019.08

도면명 DRAWING TITLE

113동
21층 평면도

축 척 SCALE
A1: 1/100
A3: 1/200

도면번호 DRAWING NO.
A-500

일련번호 SHEET NO.

REV. NO.

HAUD
(주)하우드엔지니어링
종합건축사사무소
Architects, Planners & Engineers
TEL. 02 2140 4400, SEOUL, KOREA

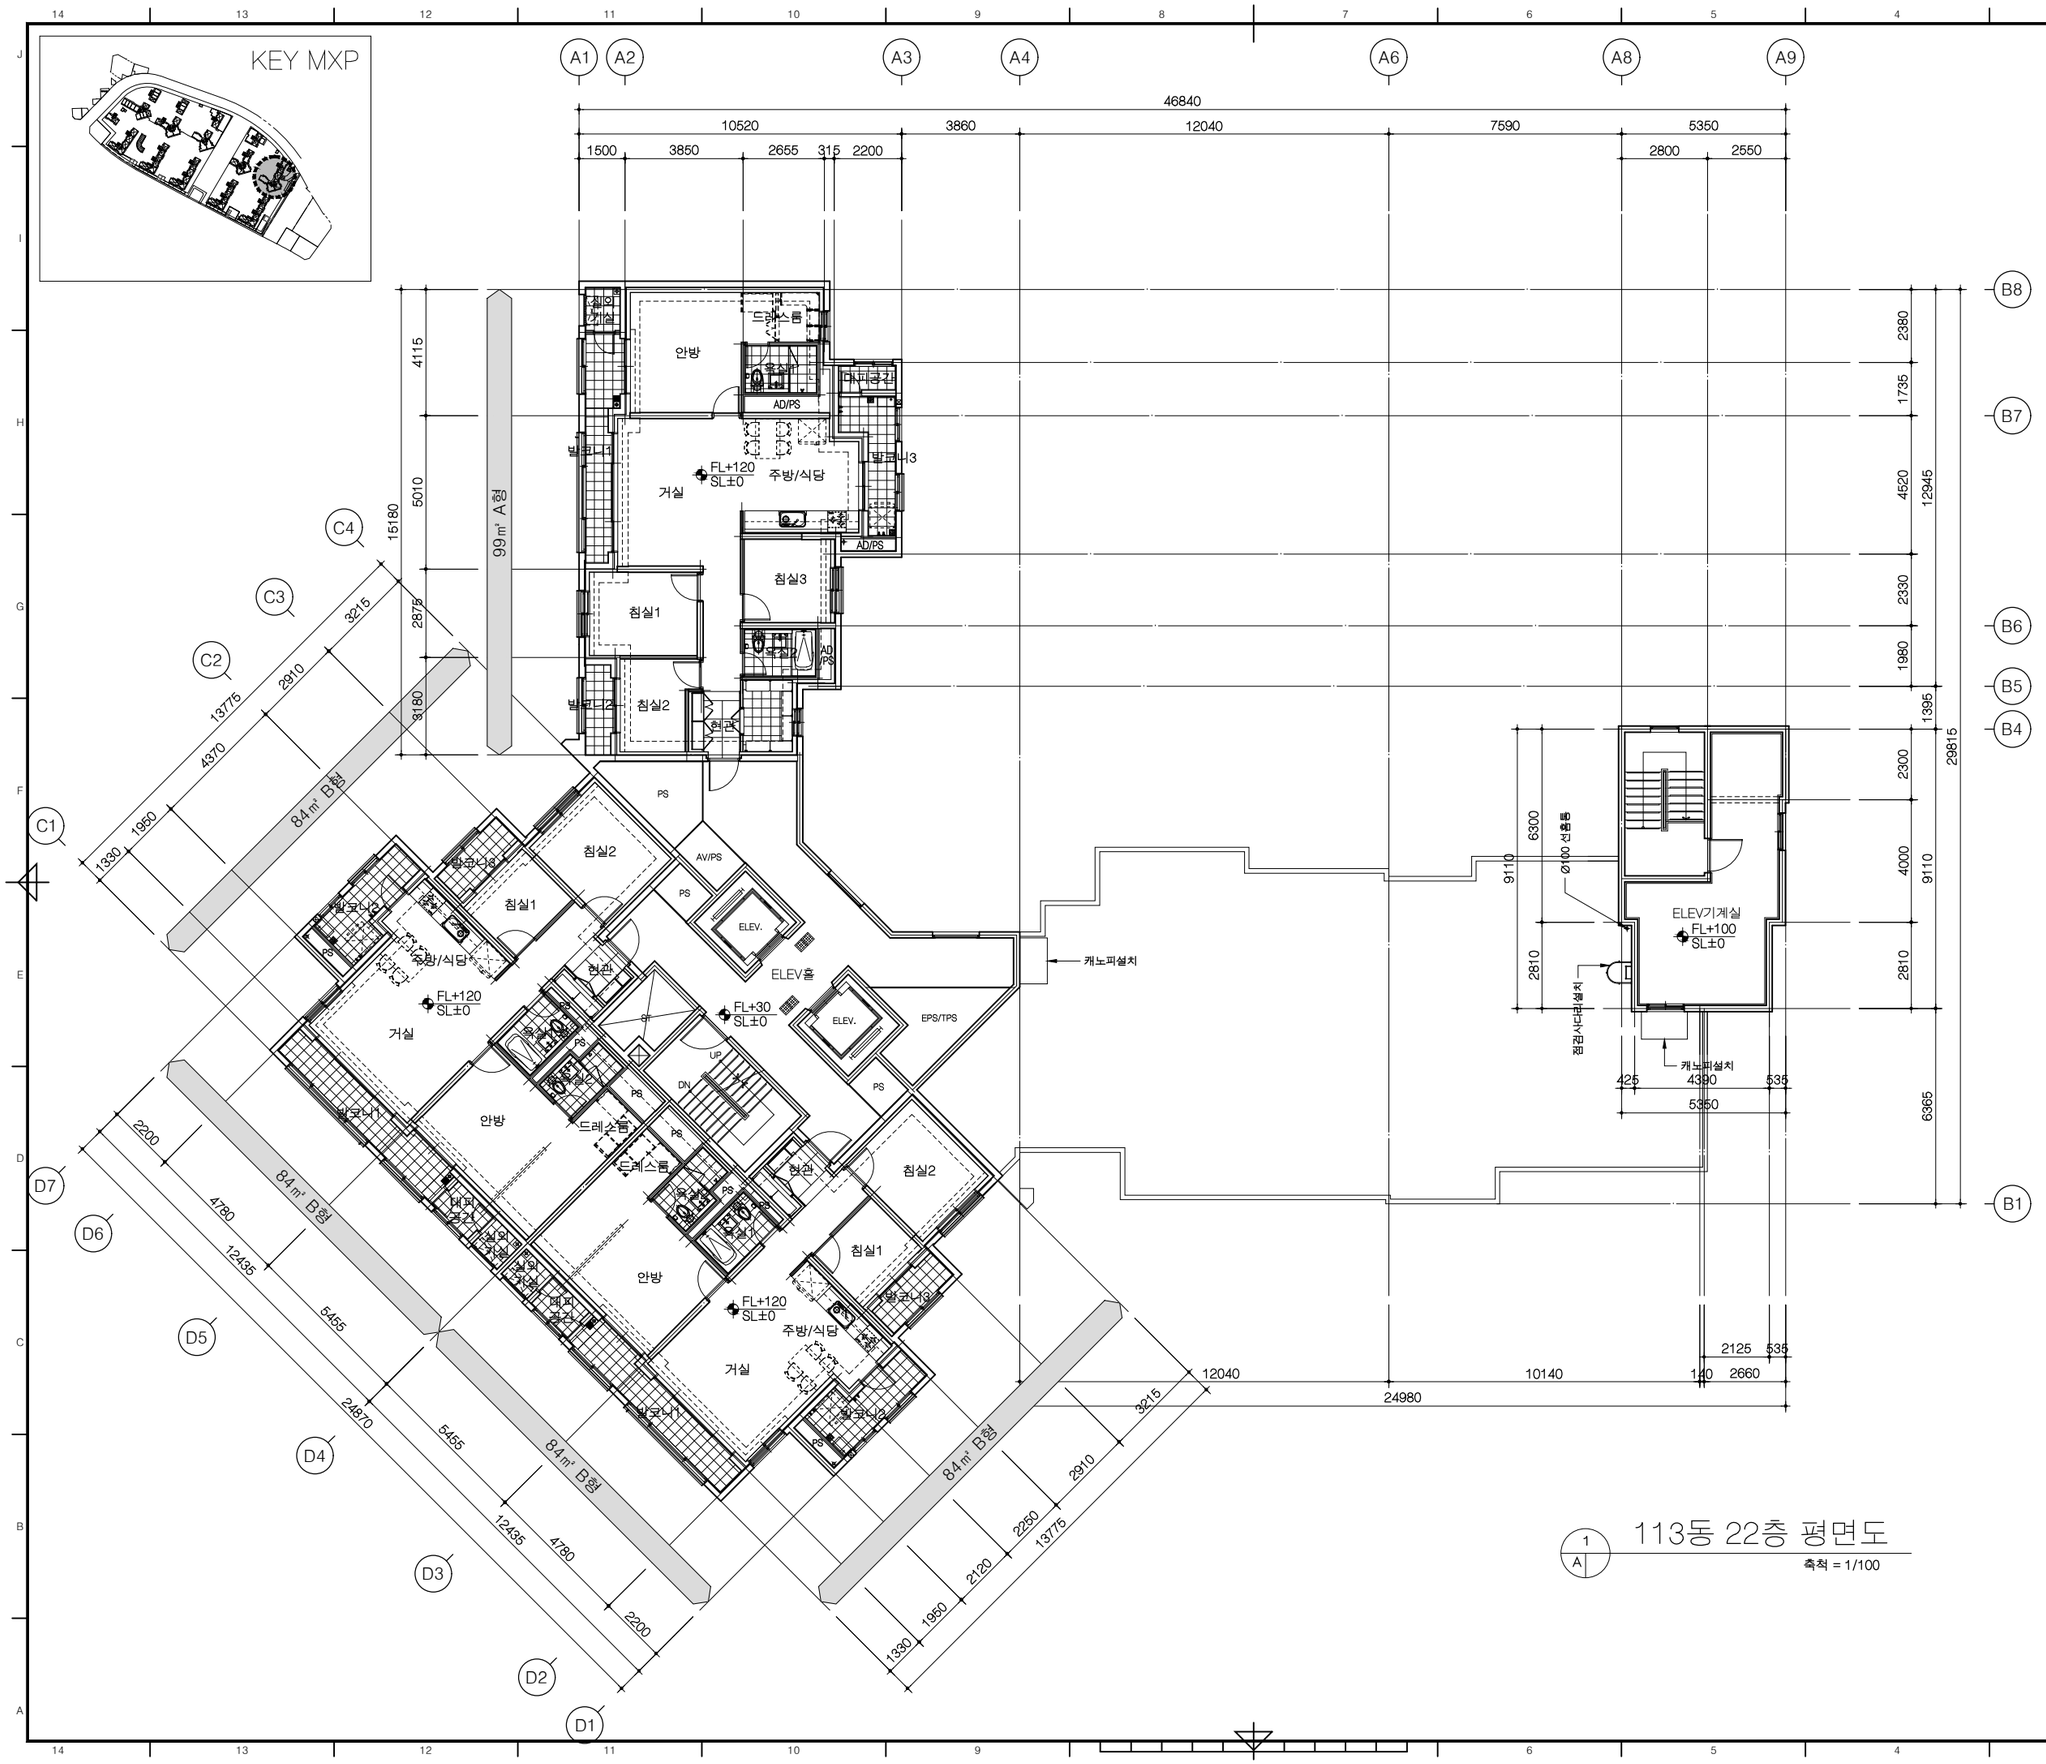

1 A 113동 22층 평면도

축척 = 1/100

사업번호 PROJECT NO.

사업명 PROJECT TITLE

수색4재정비촉진구역
주택재개발 정비사업

KEY PLAN

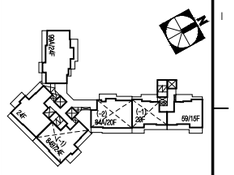

NOTE

1. 본 도면은 발코니 확장전를 기준으로 작성됨.
2. 지붕층 난간의 형태와 설치 위치는 안전성과 입면디자인을 고려하여 변경 가능함.
3. 지붕의 재료, 형태, 구조는 실시공 시 변경 될 수 있음.
4. 지붕 및 옥탑 구조물의 형태와 구조는 실시공 시 변경될 수 있음.
5. 옥상 출눈의 간격은 실시공 시 변경될 수 있음.
6. 옥상 출눈 틈에 실란트 시공되지 않음
7. 우편물 수취함 설치 위치는 변경될 수 있음
8. 오픈형 발코니 3층이상 ~ 20층이하 설치

수정번호 REV. NO.	일자 DATE	내 용 DESCRIPTION	승인 CHKD

설계 DESIGNED BY

검토 CHECKED BY
최 진 규

심사 SUMMITED BY
정 호 혁

승인 APPROVED BY
이 승 준

일자 DATE
2019.08

도면명 DRAWING TITLE

113동
22층 평면도

축 척 SCALE
A1: 1/100
A3: 1/200

도면번호 DRAWING NO.
A-501

일련번호 SHEET NO.

REV. NO.

HAUD
(주)하우드엔지니어링
종합건축사사무소
Architects, Planners & Engineers
TEL. 02 2149 4400, SEOUL, KOREA

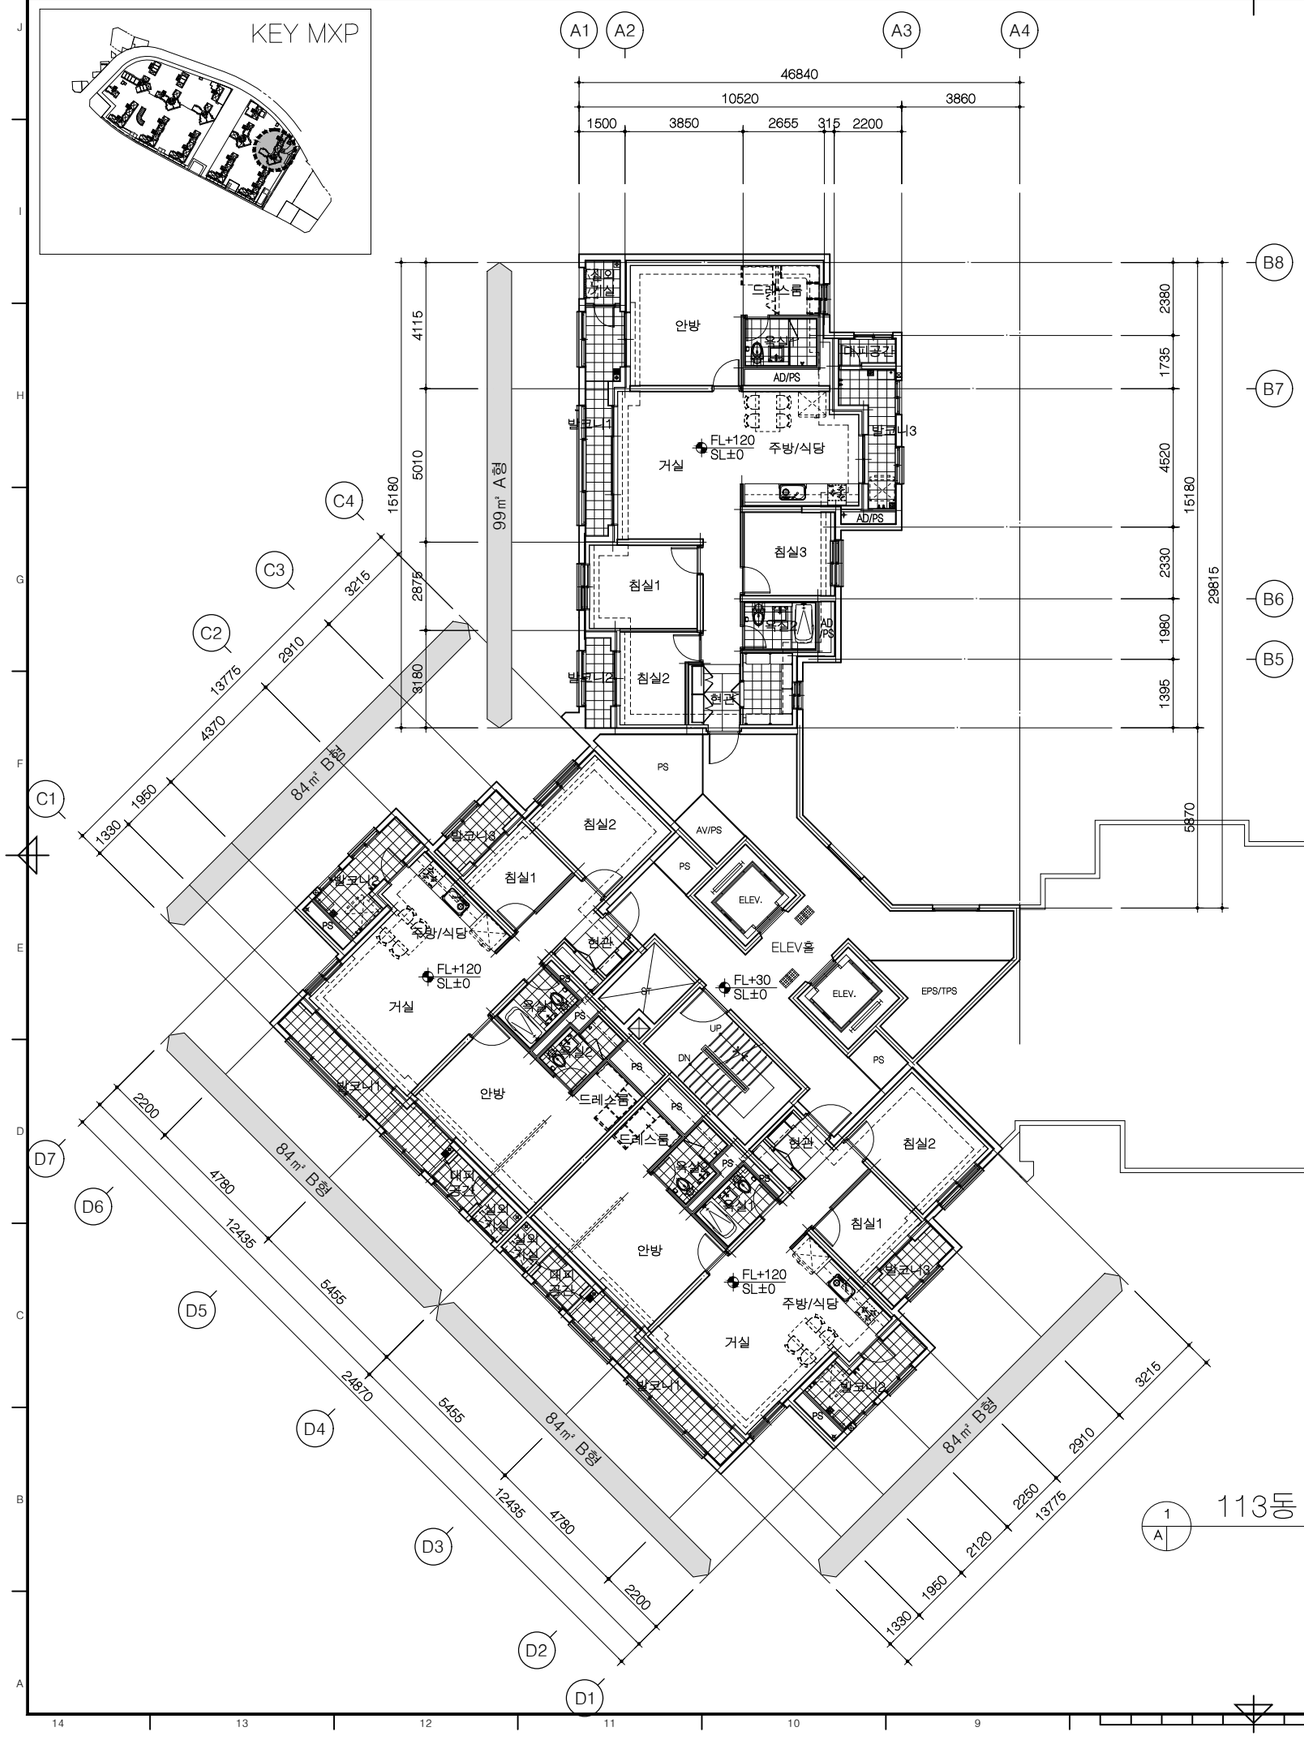

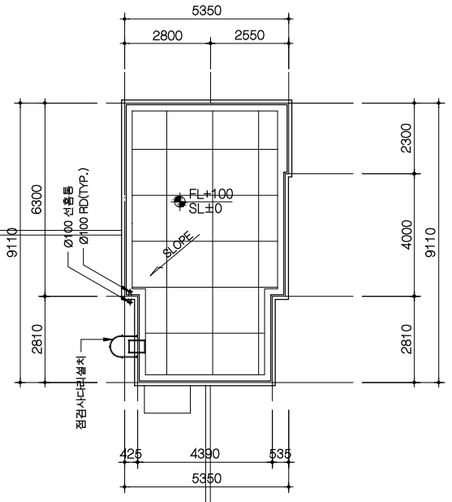

1 A 113동 23층 평면도

축척 = 1/100

사업번호 PROJECT NO.

사업명 PROJECT TITLE

수색4재정비촉진구역
주택재개발 정비사업

KEY PLAN

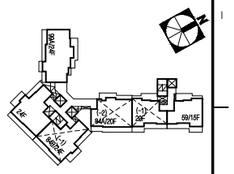

NOTE

1. 본 도면은 발코니 확장전를 기준으로 작성됨.
2. 지붕층 난간의 형태와 설치 위치는 안전성과 입면디자인을 고려하여 변경 가능함.
3. 지붕의 재료, 형태, 구조는 실시공 시 변경 될 수 있음.
4. 지붕 및 옥탑 구조물의 형태와 구조는 실시공 시 변경될 수 있음.
5. 옥상 출눈의 간격은 실시공 시 변경될 수 있음.
6. 옥상 출눈 틈에 실란트 시공되지 않음
7. 우편물 수취함 설치 위치는 변경될 수 있음
8. 오픈형 발코니 3층이상 ~ 20층이하 설치

수정번호 REV. NO.	일 자 DATE	내 용 DESCRIPTION	승 인 CHKD
△			
△			
△			
△			

설계 DESIGNED BY

검토 CHECKED BY
최 진 규

심사 SUMMITED BY
정 호 혁

승인 APPROVED BY
이 승 준

일자 DATE
2019.08

도면명 DRAWING TITLE

113동
23층 평면도

축 척 SCALE
A1: 1/100
A3: 1/200

도면번호 DRAWING NO.
A-502

일련번호 SHEET NO. △ REV. NO.

HAUD
(주)하우드엔지니어링
종합건축사사무소
Architects, Planners & Engineers
TEL. 02 2149 4400, SEOUL, KOREA

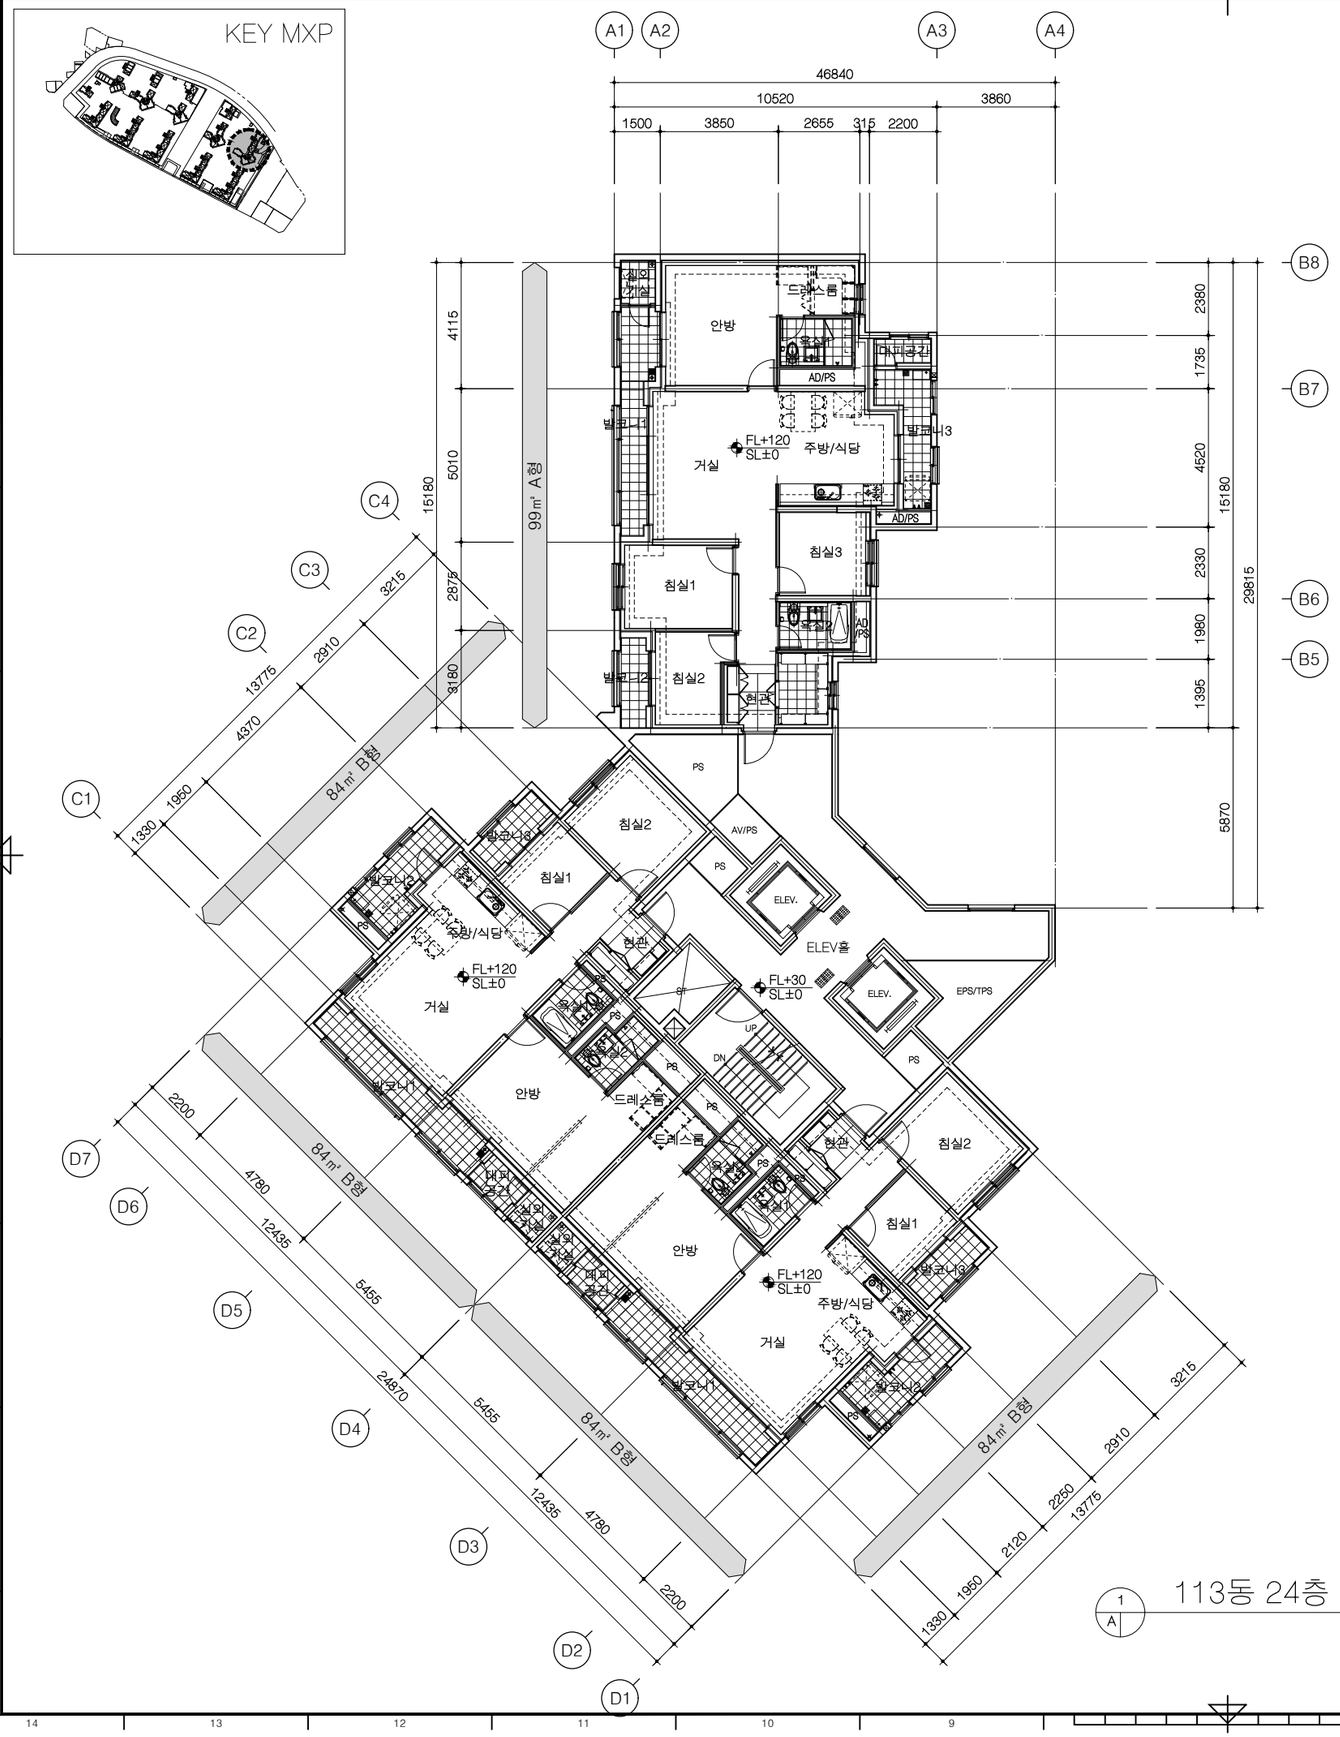

1 A 113동 24층 평면도

축척 = 1/100

사업번호 PROJECT NO.

사업명 PROJECT TITLE

수색4재정비촉진구역
주택재개발 정비사업

KEY PLAN

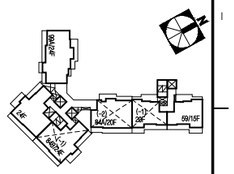

NOTE

1. 본 도면은 발코니 확장전를 기준으로 작성됨.
2. 지붕층 난간의 형태와 설치 위치는 안전성과 입면디자인을 고려하여 변경 가능함.
3. 지붕의 재료, 형태, 구조는 실시공 시 변경 될 수 있음.
4. 지붕 및 옥탑 구조물의 형태와 구조는 실시공 시 변경될 수 있음.
5. 옥상 출눈의 간격은 실시공 시 변경될 수 있음.
6. 옥상 출눈 틈에 실란트 시공되지 않음
7. 우편물 수취함 설치 위치는 변경될 수 있음
8. 오픈형 발코니 3층이상 ~ 20층이하 설치

수정번호 REV. NO.	일 자 DATE	내 용 DESCRIPTION	승 인 CHKD

설계 DESIGNED BY

검토 CHECKED BY
최 진 규

심사 SUMMITED BY
정 호 혁

승인 APPROVED BY
이 승 준

일자 DATE
2019.08

도면명 DRAWING TITLE

113동
24층 평면도

축 척 SCALE
A1: 1/100
A3: 1/200

도면번호 DRAWING NO.
A-503

일련번호 SHEET NO.

REV. NO.

HAUD
(주)하우드엔지니어링
종합건축사사무소
Architects, Planners & Engineers
TEL. 02 2140 4400, SEOUL, KOREA

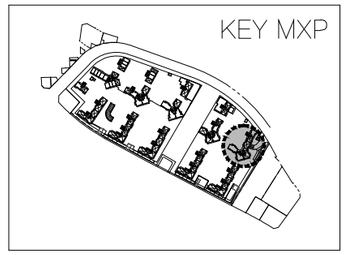

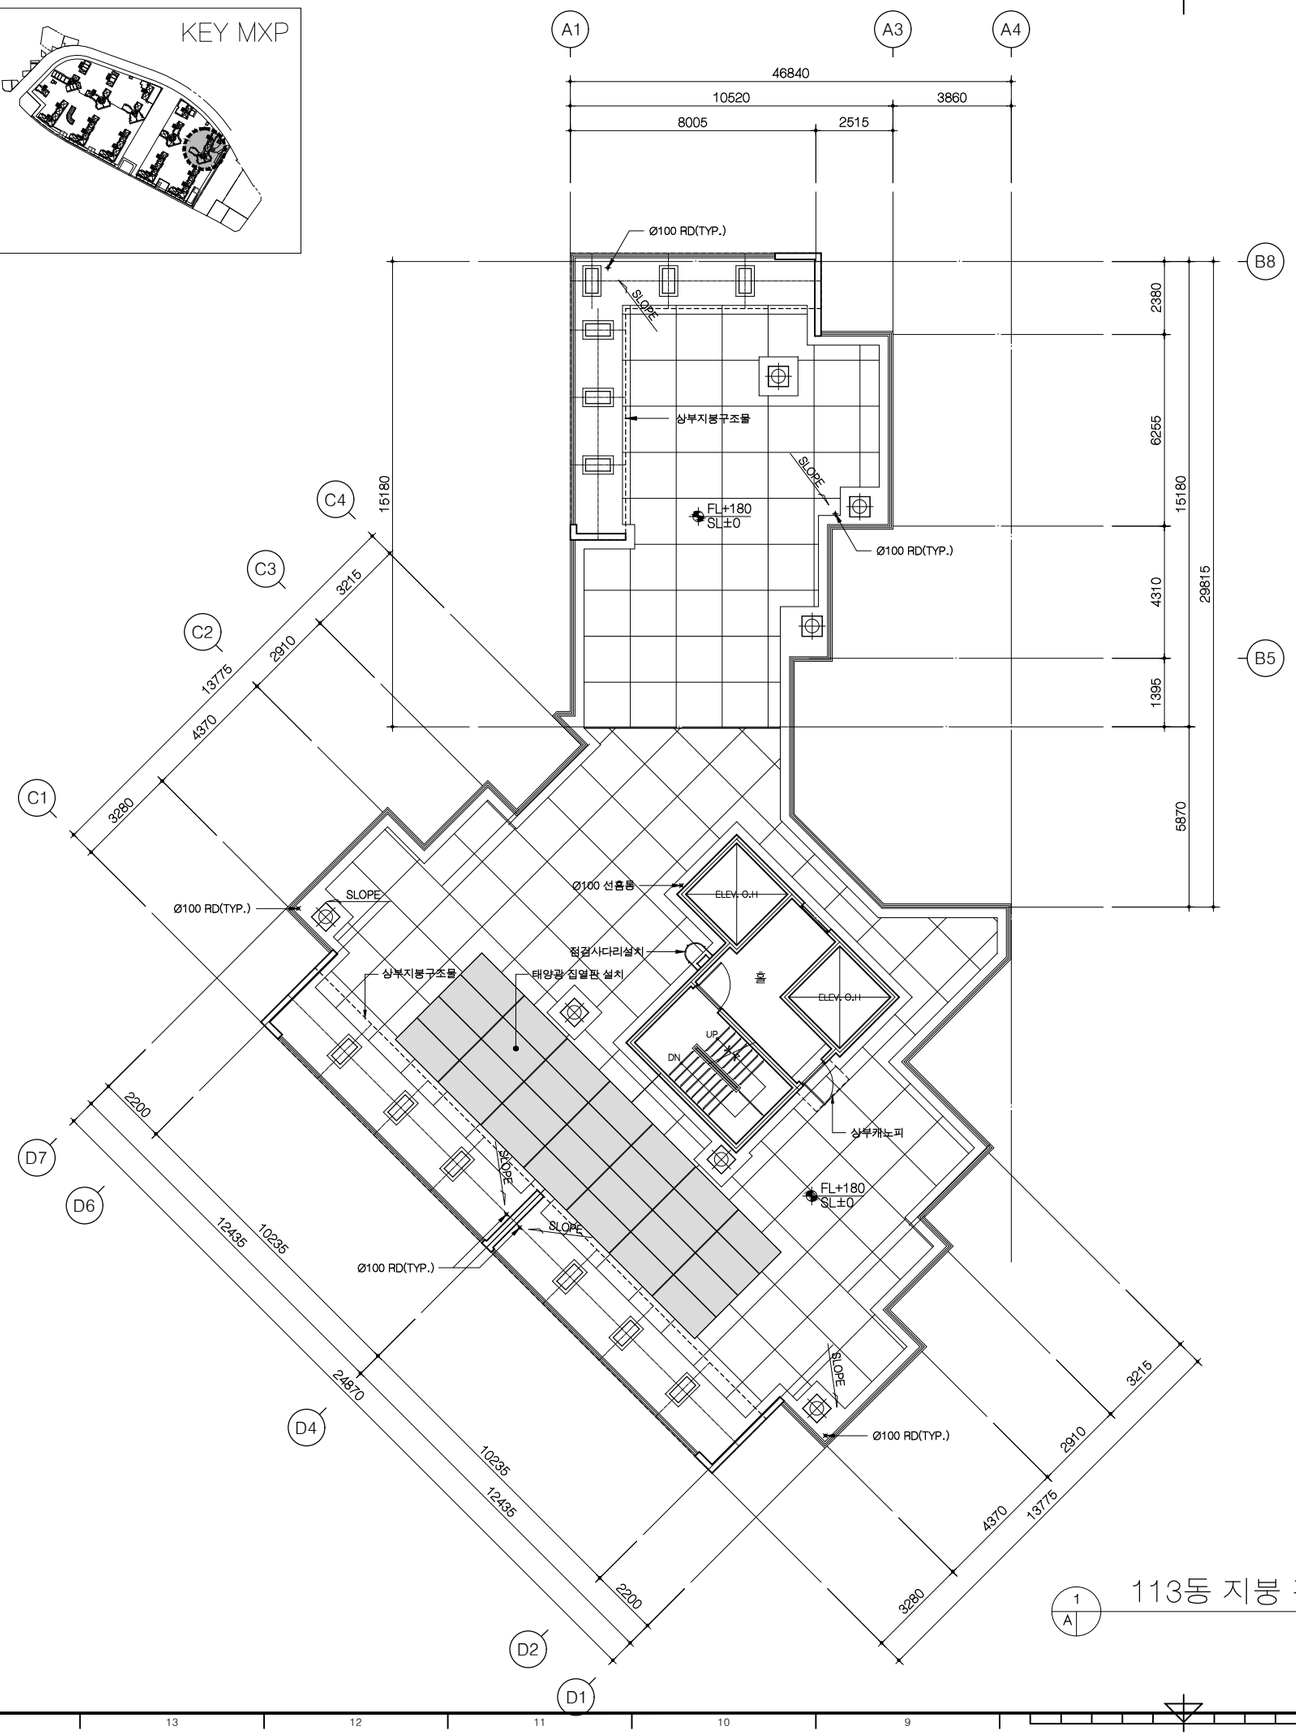

1 A 113동 지붕 평면도

축척 = 1/100

사업번호 PROJECT NO.

사업명 PROJECT TITLE

수색4재정비촉진구역
주택재개발 정비사업

KEY PLAN

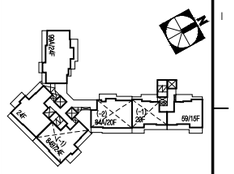

NOTE

1. 지붕바닥
   ① EXP. JOINT: 3000 X 3000
2. 본 평면도는 발코니확장전을 기준으로 작성됨
3. 재료마감은 실내,외 재료마감표 참조
4. 지붕 난간형태/설치위치는 안전성과 입면을 고려하여 실시공시 변경될 수 있음
5. 지붕재료 및 형태,구조는 실시공시 변경될수 있음
6. 지붕(옥탑지붕)의 배수드레인,청소용고리, 베기탑,점검사다리(점검구) 등의 설치위치/개소는 실시공시 변경될 수 있음
7. 옥상 상부구조물은 PC구조물 임.
8. 정화조 배기는 기계도서 참조

수정번호 REV. NO.	일 자 DATE	내 용 DESCRIPTION	승 인 CHKD

설계 DESIGNED BY

검토 CHECKED BY
최 진 규

심사 SUMMITED BY
정 호 혁

승인 APPROVED BY
이 승 준

일자 DATE
2019.08

도면명 DRAWING TITLE
113동
지붕 평면도

축 척 SCALE
A1: 1/100
A3: 1/200

도면번호 DRAWING NO.
A-504

일련번호 SHEET NO.

REV. NO.

HAUD
(주)하우드엔지니어링
종합건축사사무소
Architects, Planners & Engineers
TEL. 02 2149 4400, SEOUL, KOREA

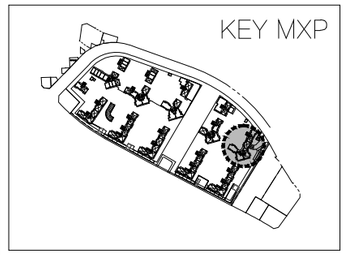

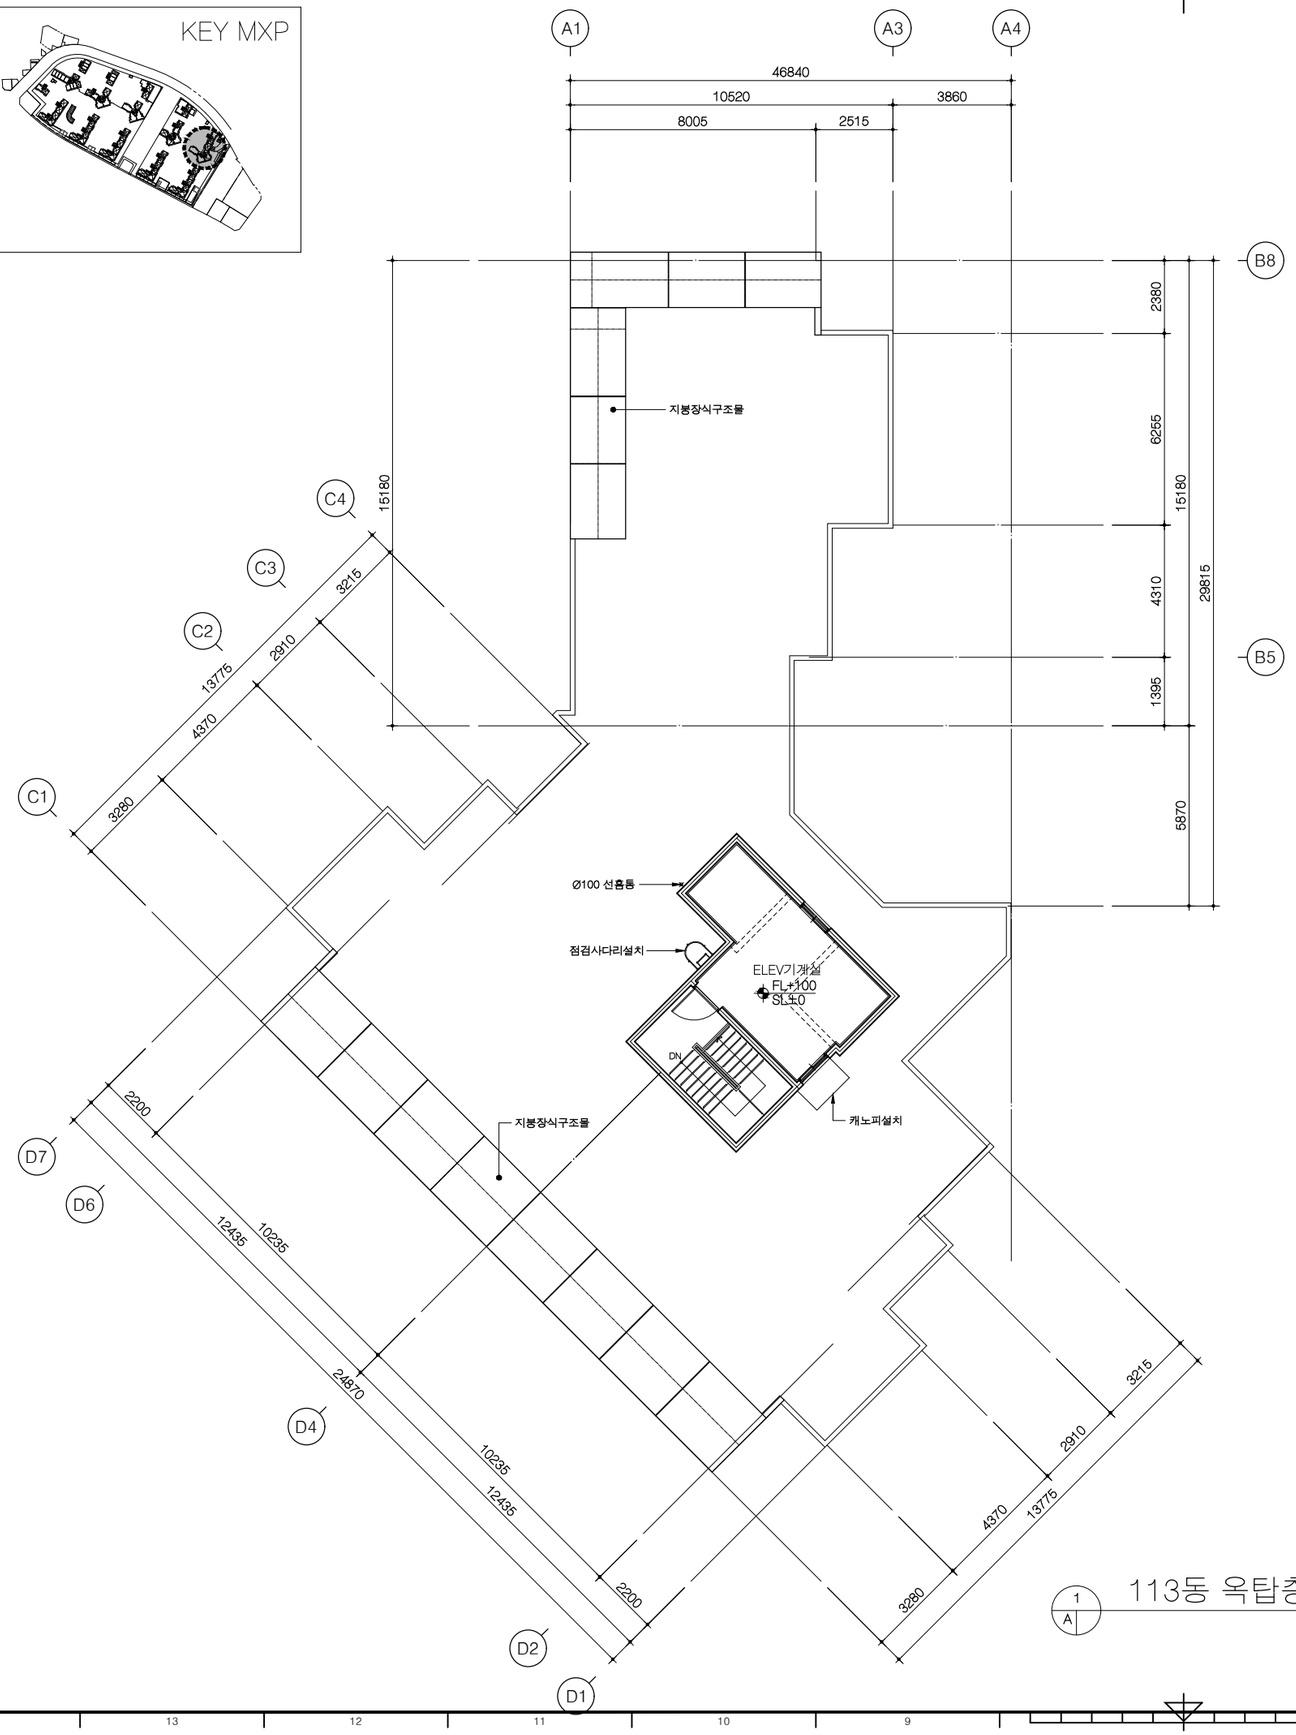

113동 옥탑층 평면도

축척 = 1/100

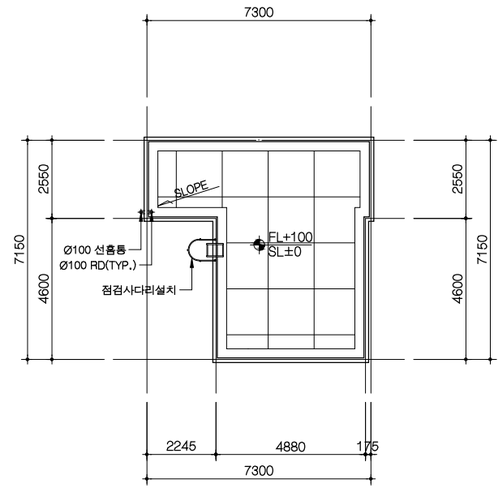

113동 옥탑지붕 평면도

축척 = 1/100

사업번호 PROJECT NO.

사업명 PROJECT TITLE

수색4재정비촉진구역
주택재개발 정비사업

KEY PLAN

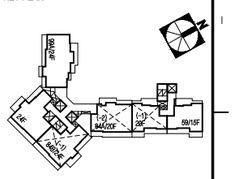

NOTE

1. 지붕바닥
   ① EXP. JOINT: 3000 X 3000
2. 본 평면도는 발코니확장전을 기준으로 작성됨
3. 재료마감은 실내,외 재료마감표 참조
4. 지붕 난간형태/설치위치는 안전성과 입면을 고려하여 실시공시 변경될 수 있음
5. 지붕재료 및 형태,구조는 실시공시 변경될수 있음
6. 지붕(옥탑지붕)의 배수드레인,청소용고리, 베기탑,점검사다리(점검구) 등의 설치위치/개소는 실시공시 변경될 수 있음
7. 옥상 상부구조물은 PC구조물 임.
8. 정화조 배기는 기계도서 참조

수정번호 REV. NO.	일 자 DATE	내 용 DESCRIPTION	승 인 CHKD

설계 DESIGNED BY

검토 CHECKED BY
최 진 규

심사 SUMMITED BY
정 호 혁

승인 APPROVED BY
이 승 준

일자 DATE
2019.08

도면명 DRAWING TITLE

113동
옥탑층 및 옥탑지붕 평면도

축 척 SCALE
A1: 1/100
A3: 1/200

도면번호 DRAWING NO.
A-505

일련번호 SHEET NO.

REV. NO.

HAUD
(주)하우드엔지니어링
종합건축사사무소
Architects, Planners & Engineers
TEL. 02 2140 4400, SEOUL, KOREA

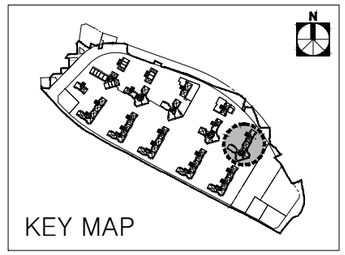

1 A 113동 정면도
축척 = 1/150

2 A 113동 우측면도
축척 = 1/150

사업번호 PROJECT NO.

사업명 PROJECT TITLE

수색4재정비촉진구역
주택재개발 정비사업

KEY PLAN

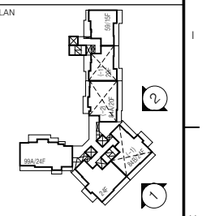

NOTE

1. 1층 바닥 LEVEL
   1SL±0 = 1FL±0 = GL±0 = EL+24.80
2. 지붕 난간의 형태 및 설치위치는 안전성과 입면디자인을 고려하여 변경가능함.
3. 지붕의 재료, 형태, 구조는 실시공시 변경될 수 있음.
4. 지붕 및 옥탑구조물의 형태와 구조는 실시공시 변경될 수 있음.
5. 외벽 및 측벽 문양은 실시공시 변경될 수 있음
6. 입면의 줄눈 및 마감선은 실시공시 변경될 수 있음.
7. 저층부 석재마감 및 입면 마감 색상, 재료에 대한 모든 기준은 특화도면을 우선 적용함.

수정번호 REV. NO.	일 자 DATE	내 용 DESCRIPTION	승 인 CHKD
△			
△			
△			
△			

설계 DESIGNED BY

검토 CHECKED BY
최 진 규

심사 SUMMITED BY
정 호 혁

승인 APPROVED BY
이 승 준

일자 DATE
2019.08

도면명 DRAWING TITLE
113동 정면도,우측면도

축척 SCALE
A1: 1/150
A3: 1/300

도면번호 DRAWING NO.
A-506

일련번호 SHEET NO.

REV. NO.

HAUD
(주)하우드엔지니어링
종합건축사사무소
Architects, Planners & Engineers
TEL. 02 2140 4400, SEOUL, KOREA

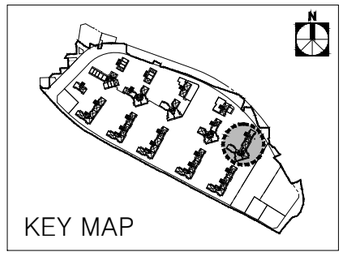

1 A 113동 배면도
축척 = 1/150

2 A 113동 좌측면도
축척 = 1/150

사업번호 PROJECT NO.

사업명 PROJECT TITLE

수색4재정비촉진구역
주택재개발 정비사업

KEY PLAN

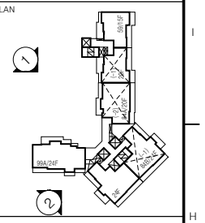

NOTE

1. 1층 바닥 LEVEL
   1SL±0 = 1FL±0 = GL±0 = EL+24.80
2. 지붕 난간의 형태 및 설치위치는 안전성과 입면디자인을 고려하여 변경가능함.
3. 지붕의 재료, 형태, 구조는 실시공시 변경될 수 있음.
4. 지붕 및 옥탑구조물의 형태와 구조는 실시공시 변경될 수 있음.
5. 외벽 및 측벽 문양은 실시공시 변경될 수 있음
6. 입면의 줄눈 및 마감선은 실시공시 변경될 수 있음.
7. 저층부 석재마감 및 입면 마감 색상, 재료에 대한 모든 기준은 특화도면을 우선 적용함.

수정번호 REV. NO.	일 자 DATE	내 용 DESCRIPTION	승 인 CHKD
△			
△			
△			
△			

설계 DESIGNED BY

검토 CHECKED BY
최 진 규

심사 SUMMITED BY
정 호 혁

승인 APPROVED BY
이 승 준

일자 DATE
2019.08

도면명 DRAWING TITLE
113동 배면도,좌측면도

축 척 SCALE
A1: 1/150
A3: 1/300

도면번호 DRAWING NO.
A-507

일련번호 SHEET NO. △ REV. NO.

HAUD
(주)하우드엔지니어링
종합건축사사무소
Architects, Planners & Engineers
TEL. 82 2140 4400, SEOUL, KOREA

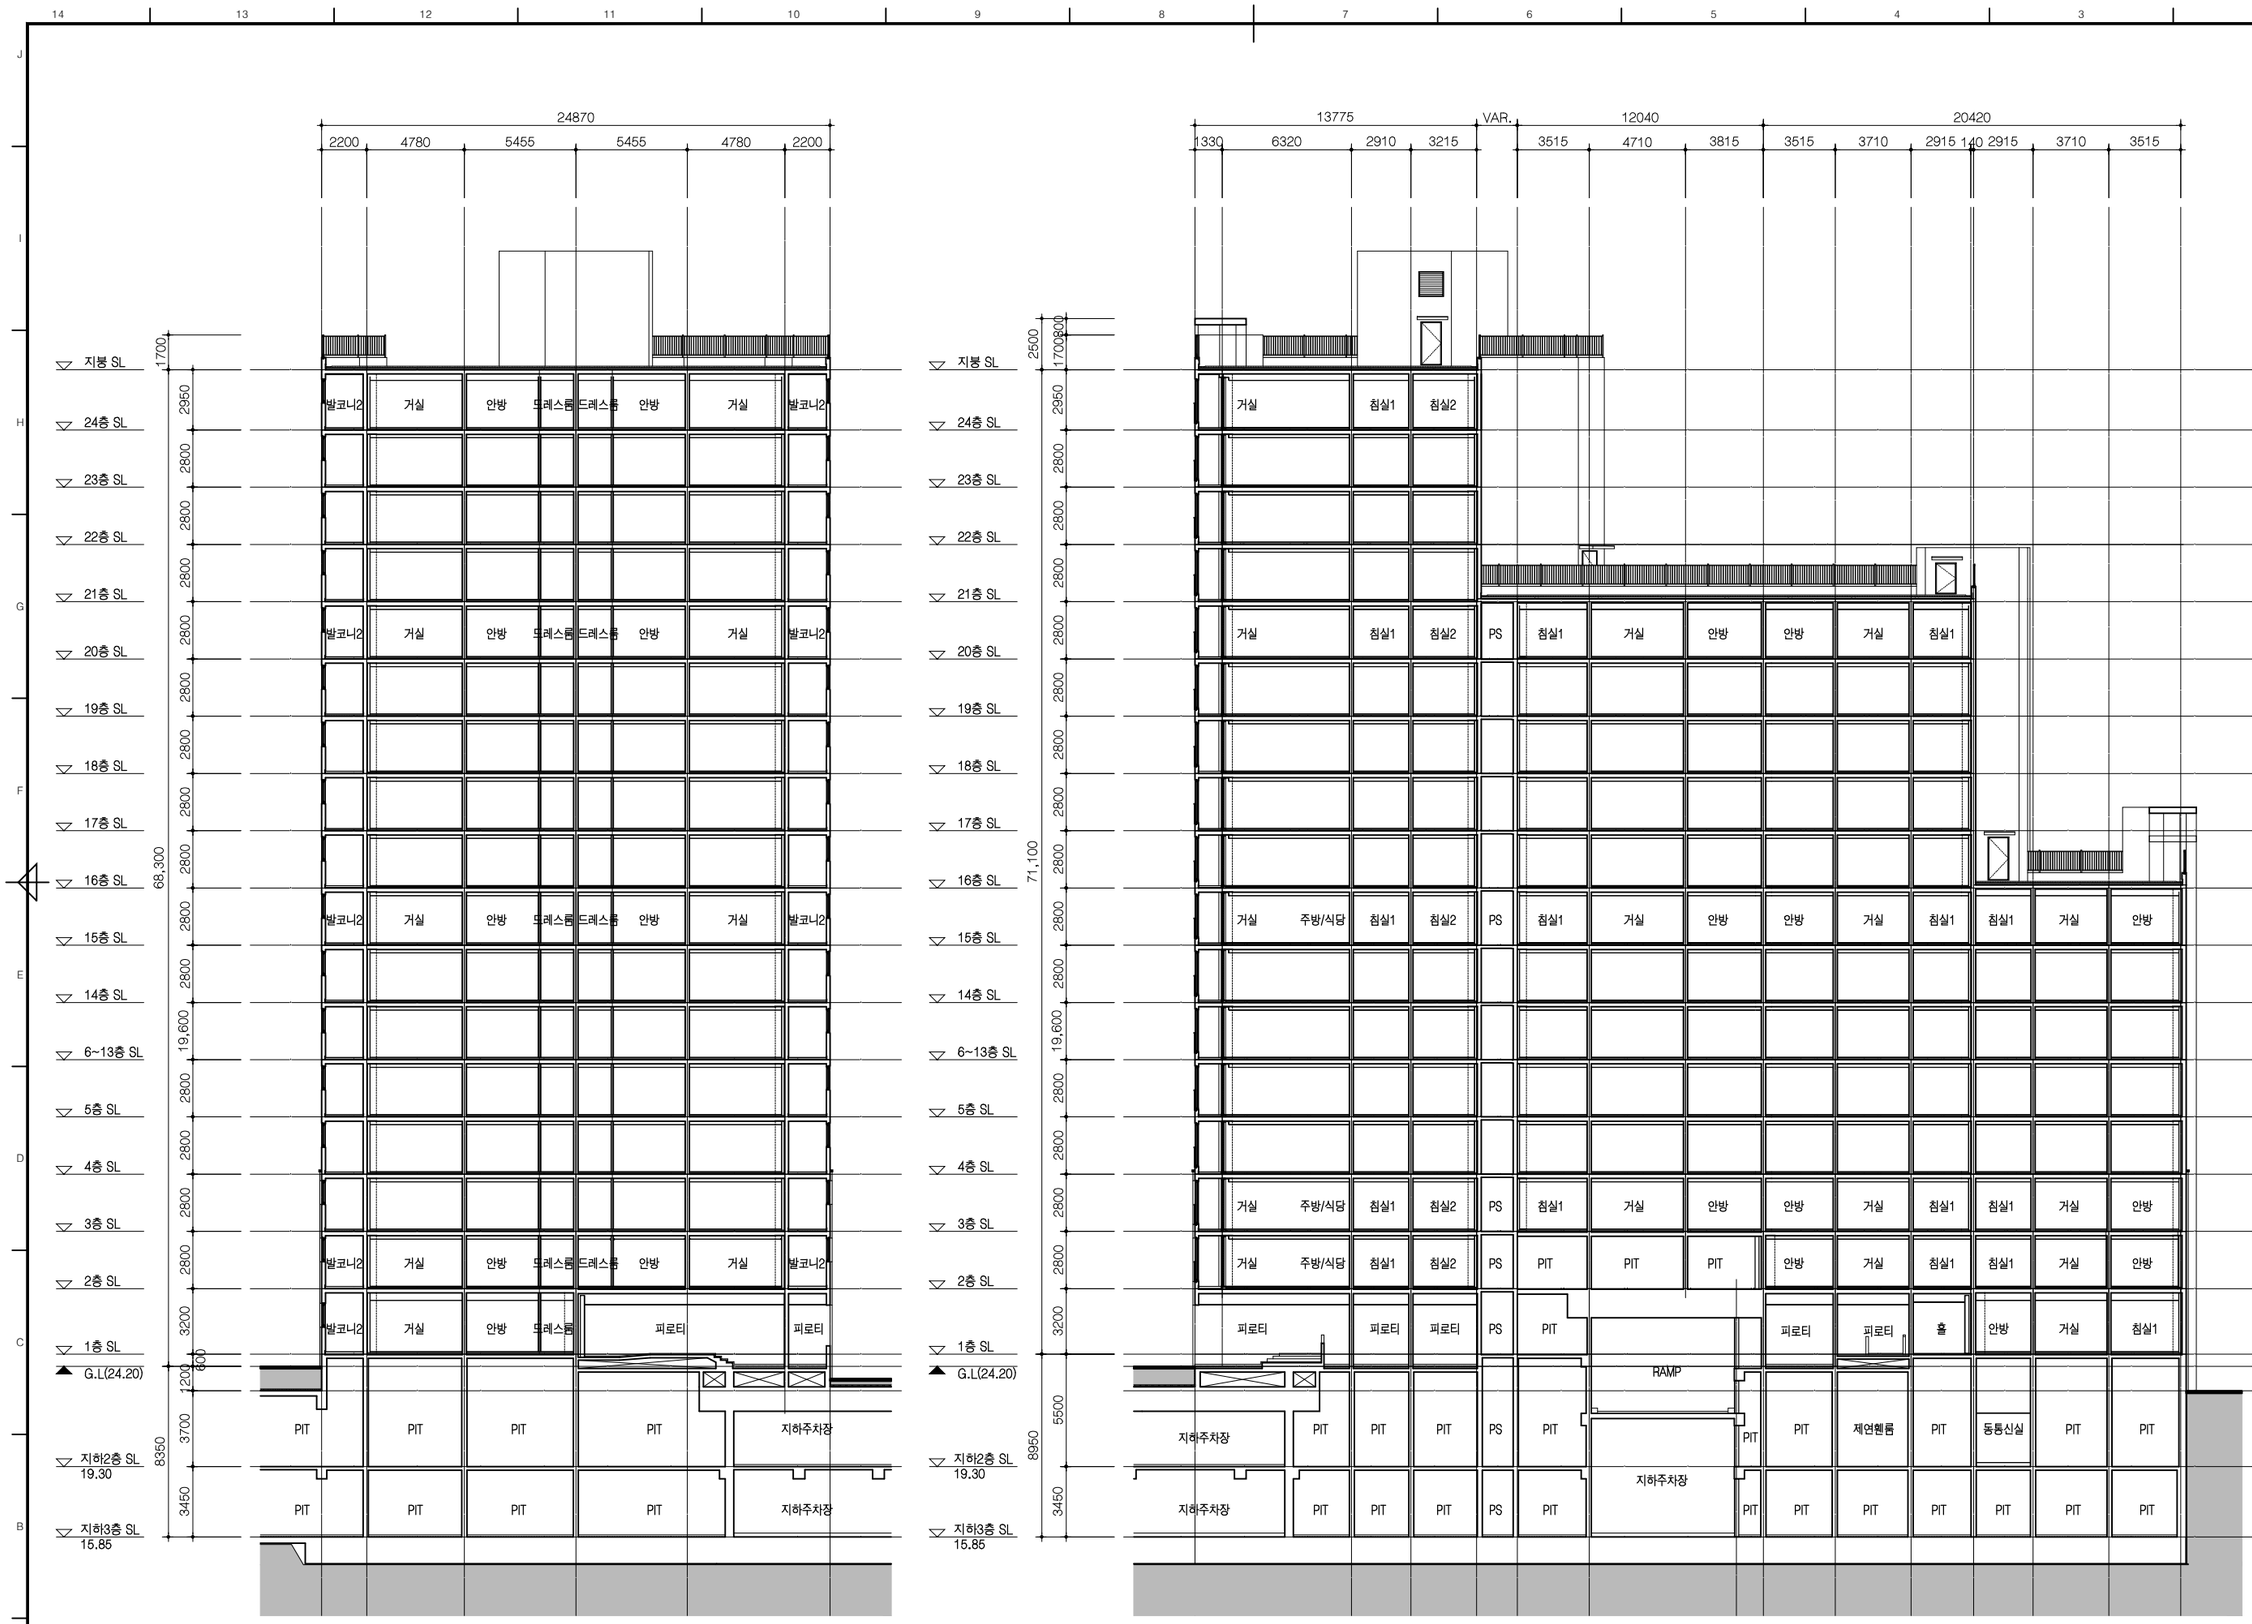

1 A 113동 종단면도

축척 = 1/150

2 A 113동 횡단면도

축척 = 1/150

사업번호 PROJECT NO.

사업명 PROJECT TITLE

수색4재정비촉진구역
주택재개발 정비사업

KEY PLAN

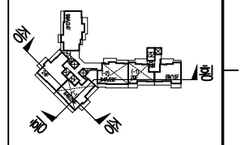

NOTE

수정번호 REV. NO.	일 자 DATE	내 용 DESCRIPTION	승 인 CHKD
1			
2			
3			
4			

설계 DESIGNED BY

검토 CHECKED BY
최 진 규

심사 SUMMITED BY
정 호 혁

승인 APPROVED BY
이 승 준

일자 DATE
2019.08

도면명 DRAWING TITLE
113동 종,횡단면도

축 척 SCALE
A1: 1/150
A3: 1/300

도면번호 DRAWING NO.
A-508

일련번호 SHEET NO.

REV. NO.

HAUD
㈜하우드엔지니어링
종합건축사사무소
Architects, Planners & Engineers
TEL. 02 2140 4400, SEOUL, KOREA

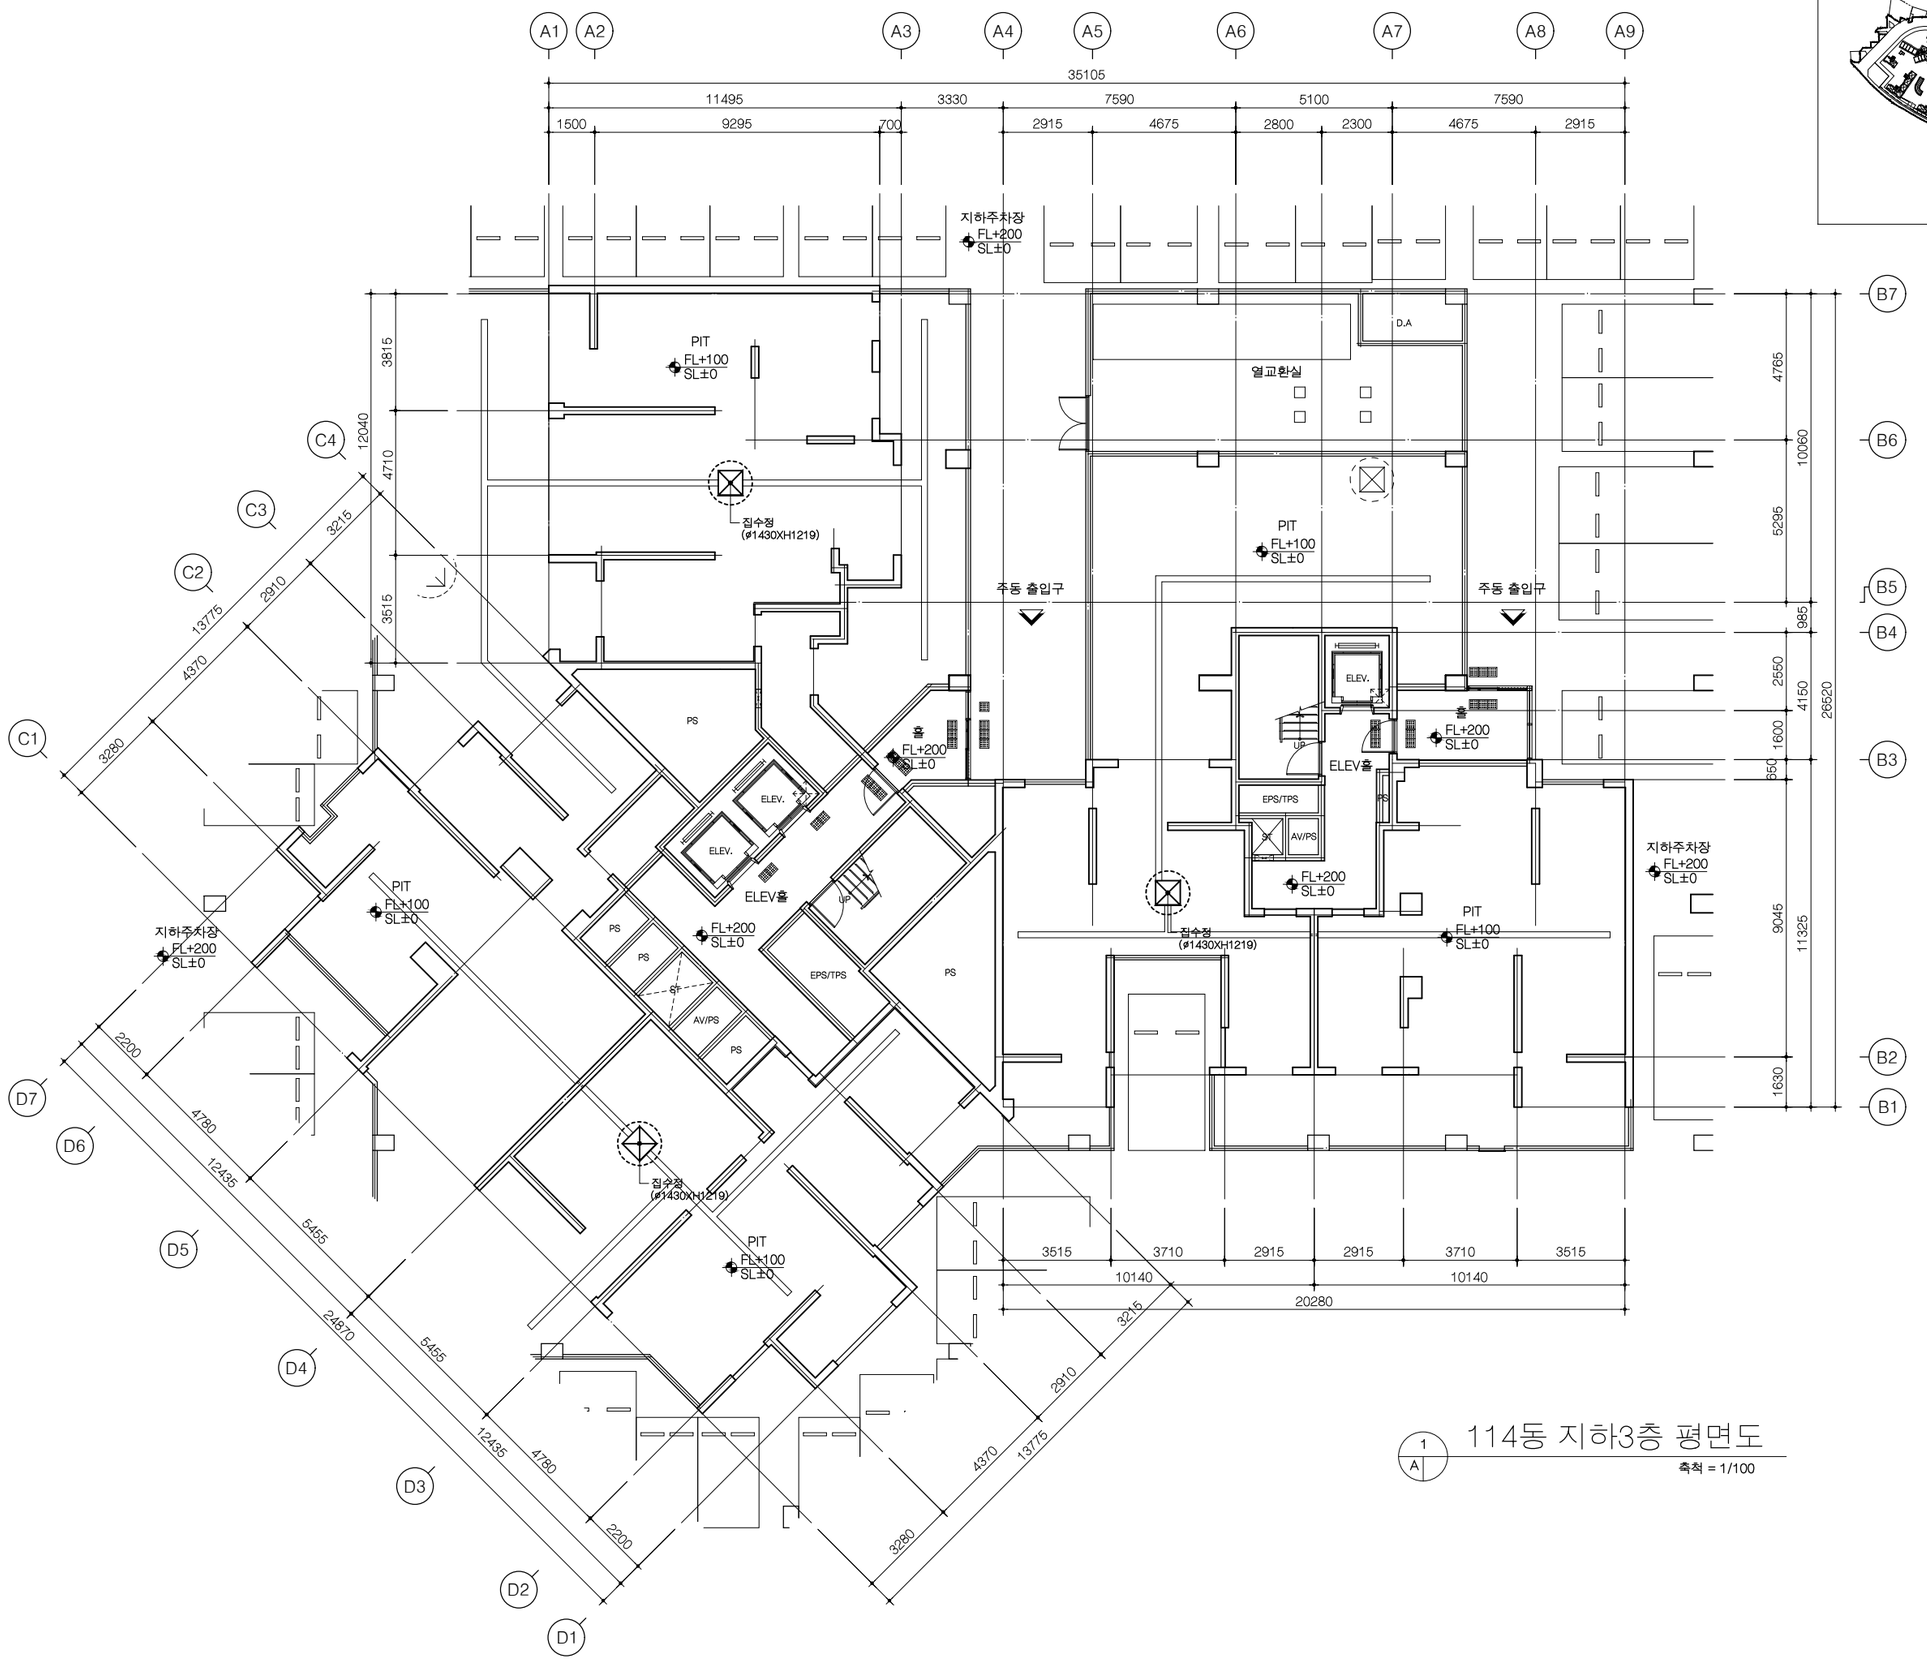

1 A 114동 지하3층 평면도

축척 = 1/100

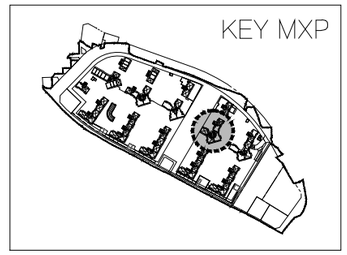

사업번호 PROJECT NO.

사업명 PROJECT TITLE

수색4재정비촉진구역
주택재개발 정비사업

KEY PLAN

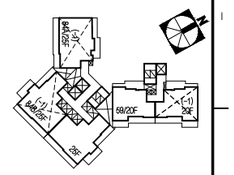

NOTE

1. 지하층 무근 콘크리트는 실시공시 THK80~120 범위로 변동이 있을수 있음.(SLOPE)
2. ELEV홀에 면한부위는 1.0B 조적쌓기임.
3. 지하주차장의 블록쌓기 기준은 높이가 3.6m이하인 경우 4인치 보강블록쌓기가 기준임 (단, 5.4m이하는 6인치쌓기, 5.4m초과는 8인치쌓기가 기준임)
4. ELEV.PIT 집수정은 (600X600X600)임.
5. 주차장 내의 창호는 주차장 창호도 참조.
6. 주차장 집수정 및 영구배수 집수정의 크기 및 위치는 지하주차장 평면도를 참조 할 것.
   ☒ : 주차장 집수정
   ☒ : 영구배수 집수정

********** 지하3층 바닥LEVEL
B3SL±0 = B3FL±0 = EL+15.85

수정번호 REV. NO.	일 자 DATE	내 용 DESCRIPTION	승 인 CHKD
△			
△			
△			
△			

설계 DESIGNED BY

검토 CHECKED BY
최 진 규

심사 SUMMITED BY
정 호 혁

승인 APPROVED BY
이 승 준

일자 DATE
2019.08

도면명 DRAWING TITLE
114동
지하3층 평면도

축 척 SCALE
A1: 1/100
A3: 1/200

도면번호 DRAWING NO.
A-511

일련번호 SHEET NO.

△ REV. NO.

HAUD
㈜하우드엔지니어링
종합건축사사무소
Architects, Planners & Engineers
TEL. 02 2140 4400, SEOUL, KOREA

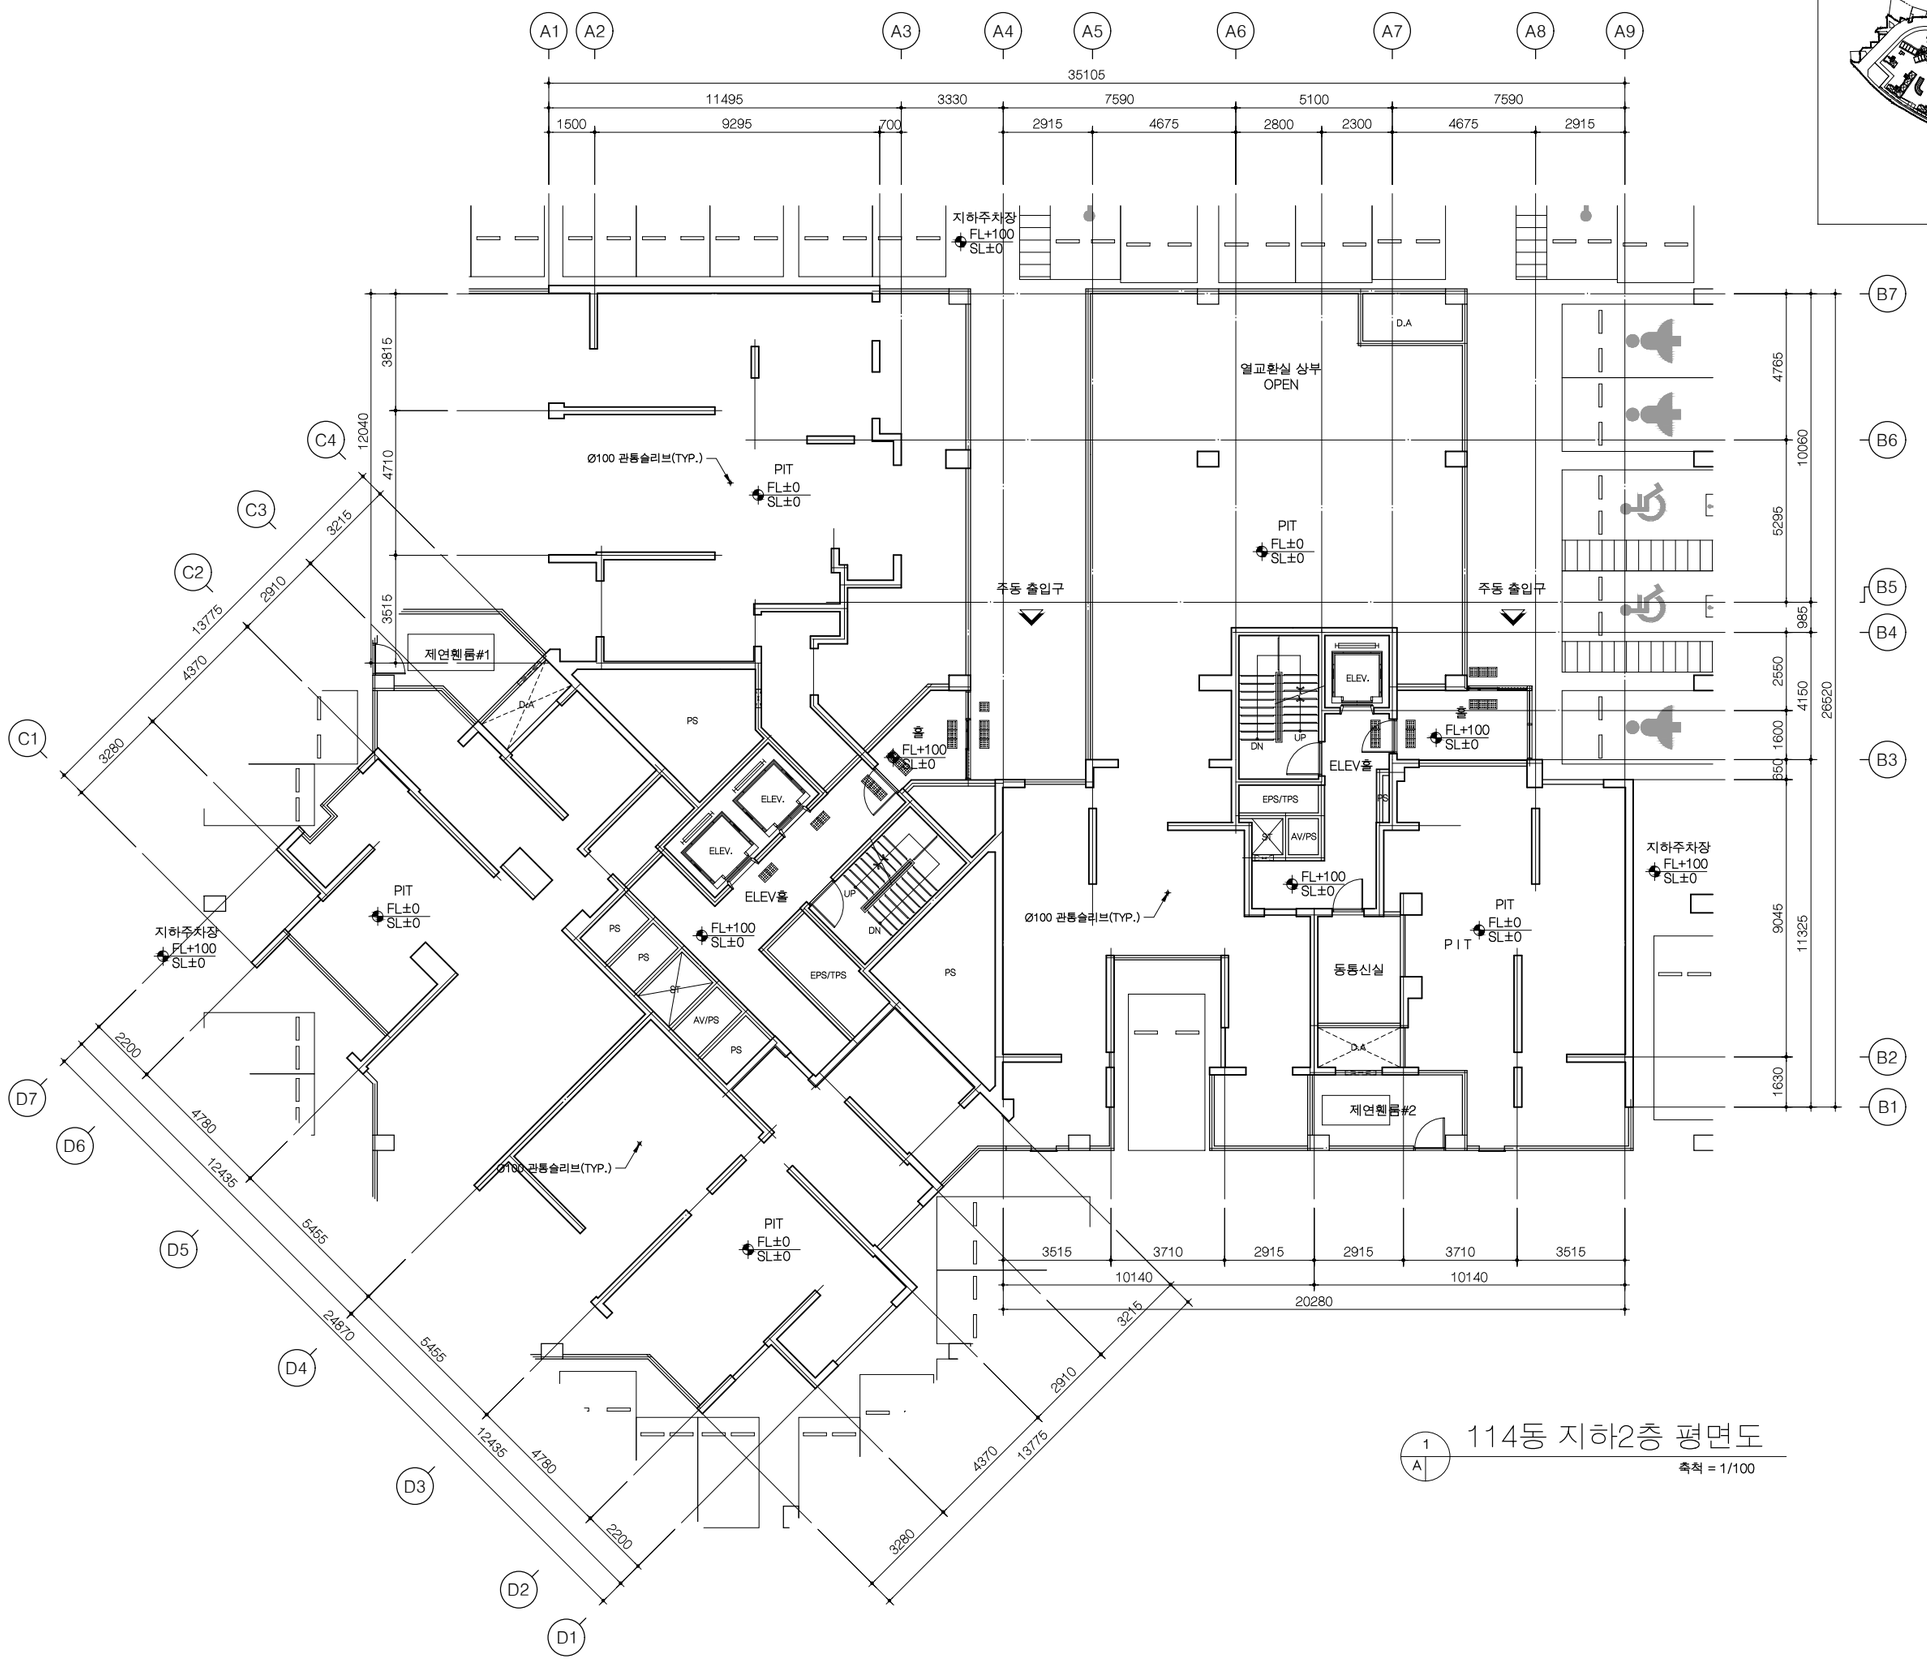

1 A 114동 지하2층 평면도

축척 = 1/100

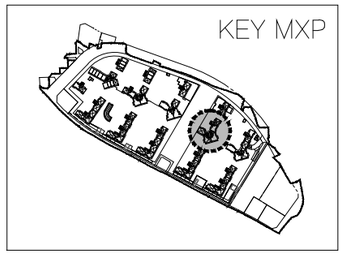

사업번호 PROJECT NO.

사업명 PROJECT TITLE

수색4재정비촉진구역
주택재개발 정비사업

KEY PLAN

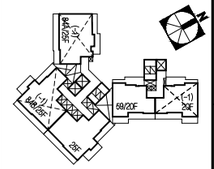

NOTE

1. 지하주차장의 ELEV홀에 면한부위는 1.0B 조적쌓기임.
2. 지하주차장의 블록쌓기 기준은 높이가 3.6m이하인 경우 4인치 보강블록쌓기가 기준임 (단, 5.4m이하는 6인치쌓기, 5.4m초과는 8인치쌓기가 기준임)
3. 주차장 내의 창호는 주차장 창호도 참조.

**** 지하2층 바닥LEVEL
D2SL±0 = D2FL±0 = EL+19.30

수정번호 REV. NO.	일 자 DATE	내 용 DESCRIPTION	승 인 CHKD
△			
△			
△			
△			

설계 DESIGNED BY

검토 CHECKED BY
최 진 규

심사 SUMMITED BY
정 호 혁

승인 APPROVED BY
이 승 준

일자 DATE
2019.08

도면명 DRAWING TITLE
114동
지하2층 평면도

축 척 SCALE
A1: 1/100
A3: 1/200

도면번호 DRAWING NO.
A-512

일련번호 SHEET NO.

△ REV. NO.

HAUD
㈜하우드엔지니어링
종합건축사사무소
Architects, Planners & Engineers
TEL. 02 2140 4400, SEOUL, KOREA

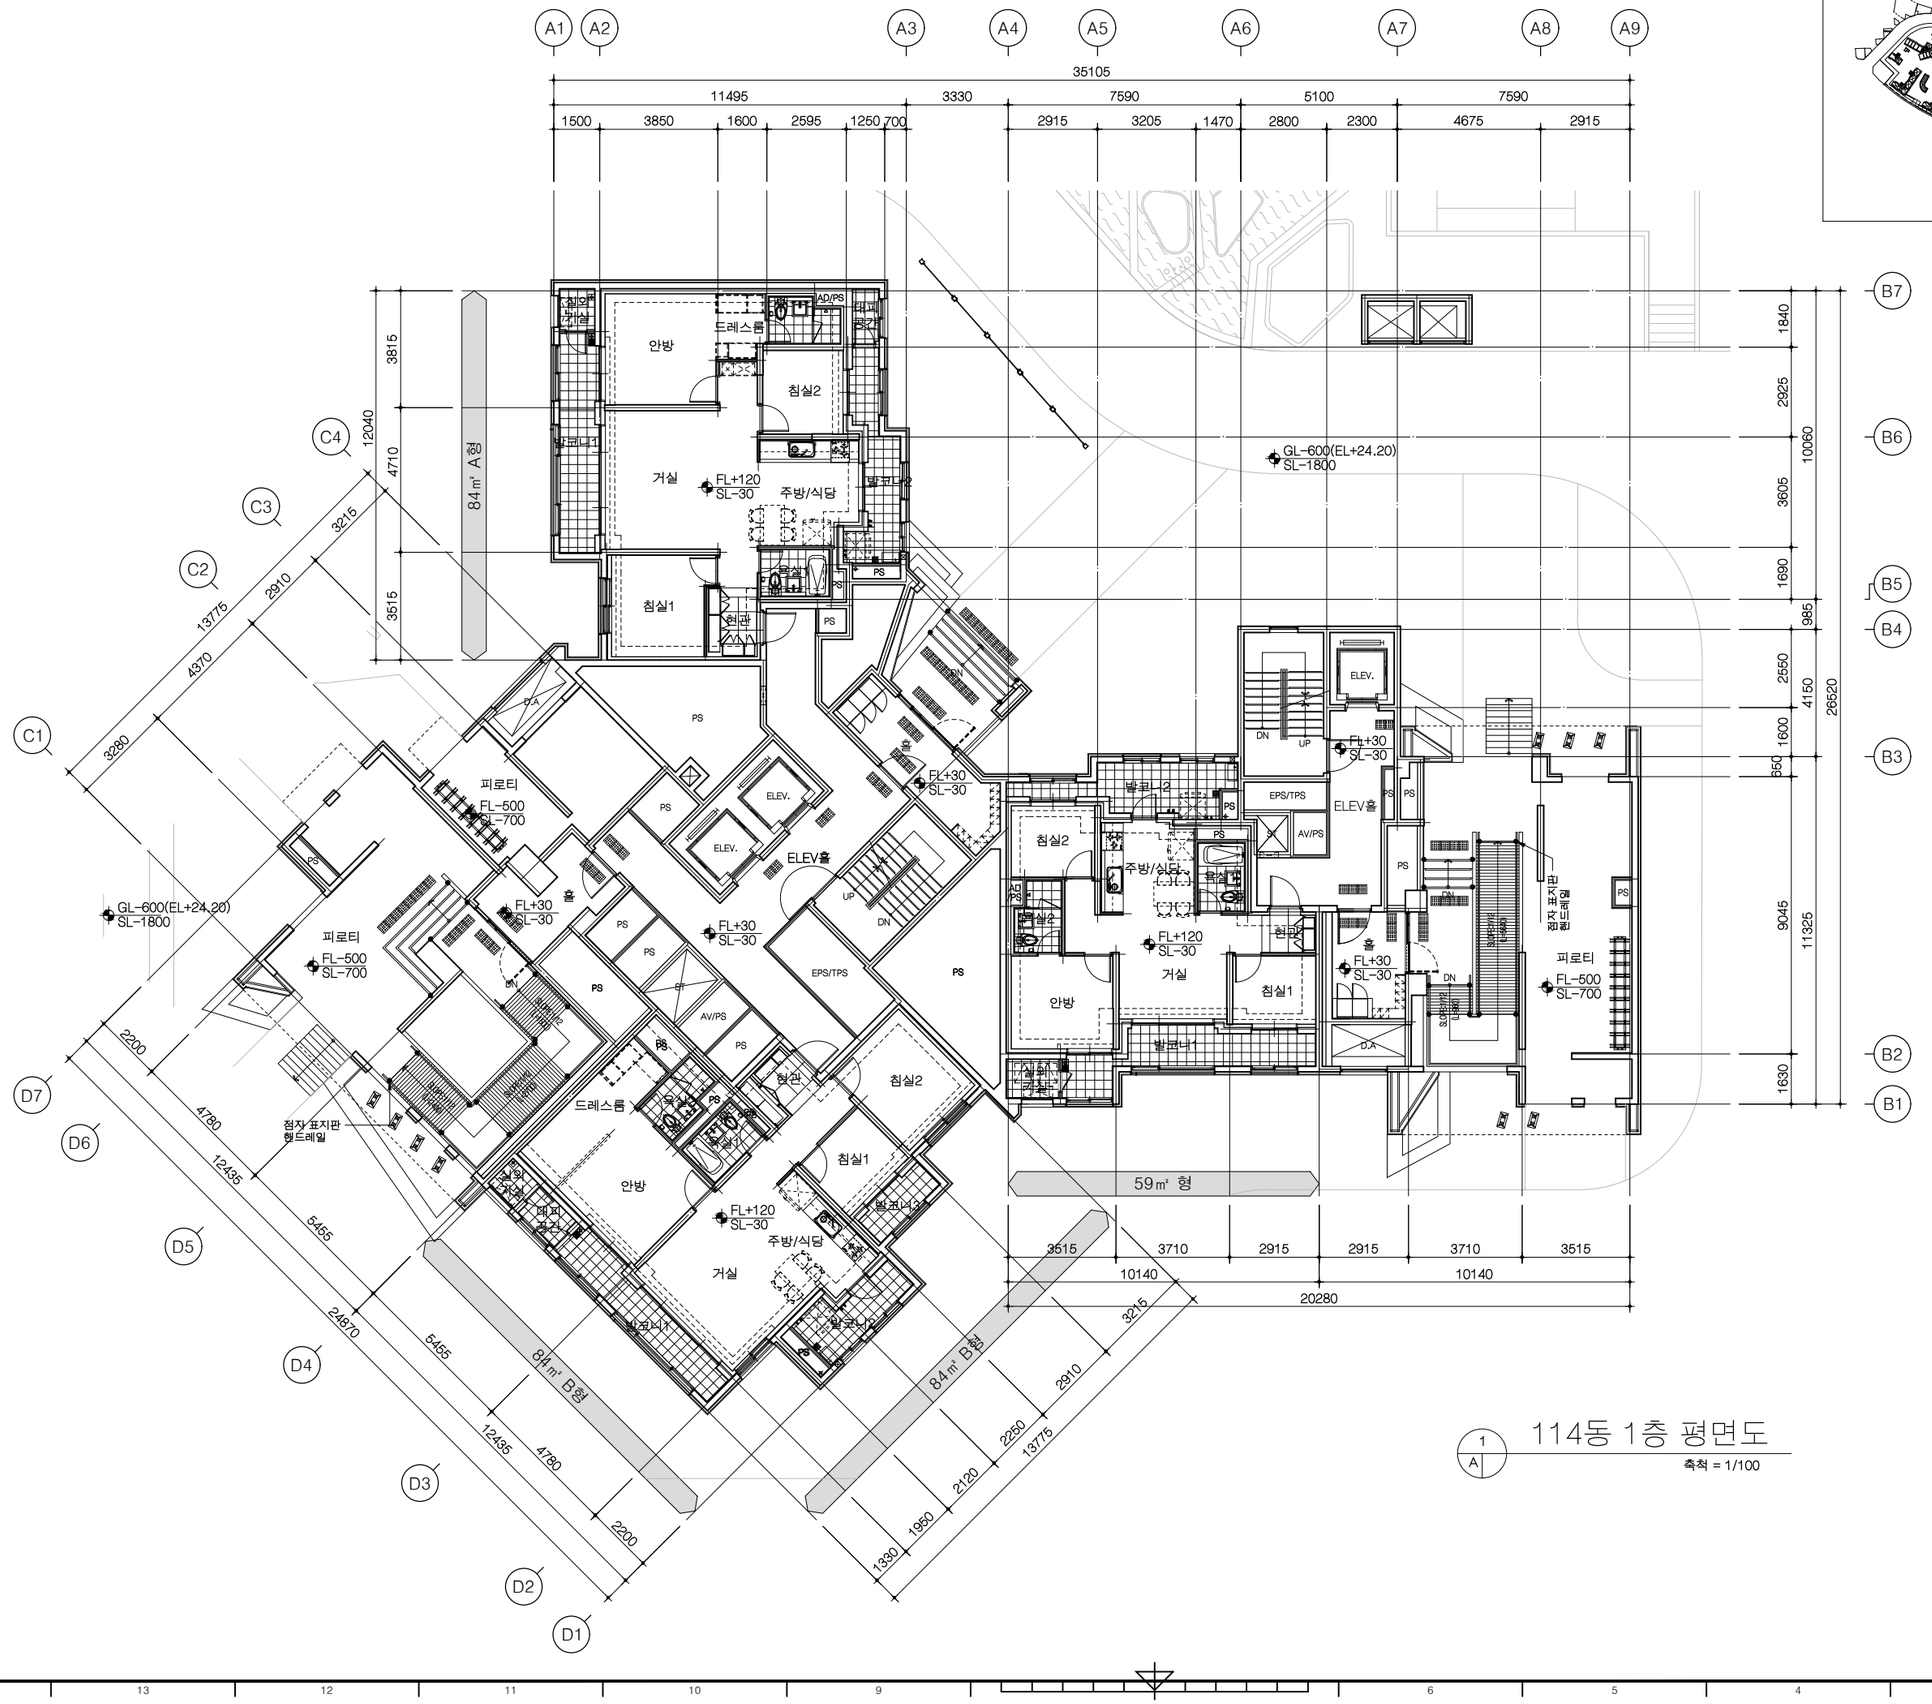

사업번호 PROJECT NO.

사업명 PROJECT TITLE

수색4재정비촉진구역
주택재개발 정비사업

수정번호 REV. NO.	일자 DATE	내 용 DESCRIPTION	승인 CHKD
△			
△			
△			
△			

설계 DESIGNED BY

검토 CHECKED BY
최 진 규

심사 SUMMITED BY
정 호 혁

승인 APPROVED BY
이 승 준

일자 DATE
2019.08

도면명 DRAWING TITLE
114동
1층 평면도

축 척 SCALE
A1: 1/100
A3: 1/200

도면번호 DRAWING NO.
A-513

일련번호 SHEET NO.

REV. NO. △

HAUD
(주)하우드엔지니어링
종합건축사사무소
Architects, Planners & Engineers
TEL. 02 2149 4400, SEOUL, KOREA

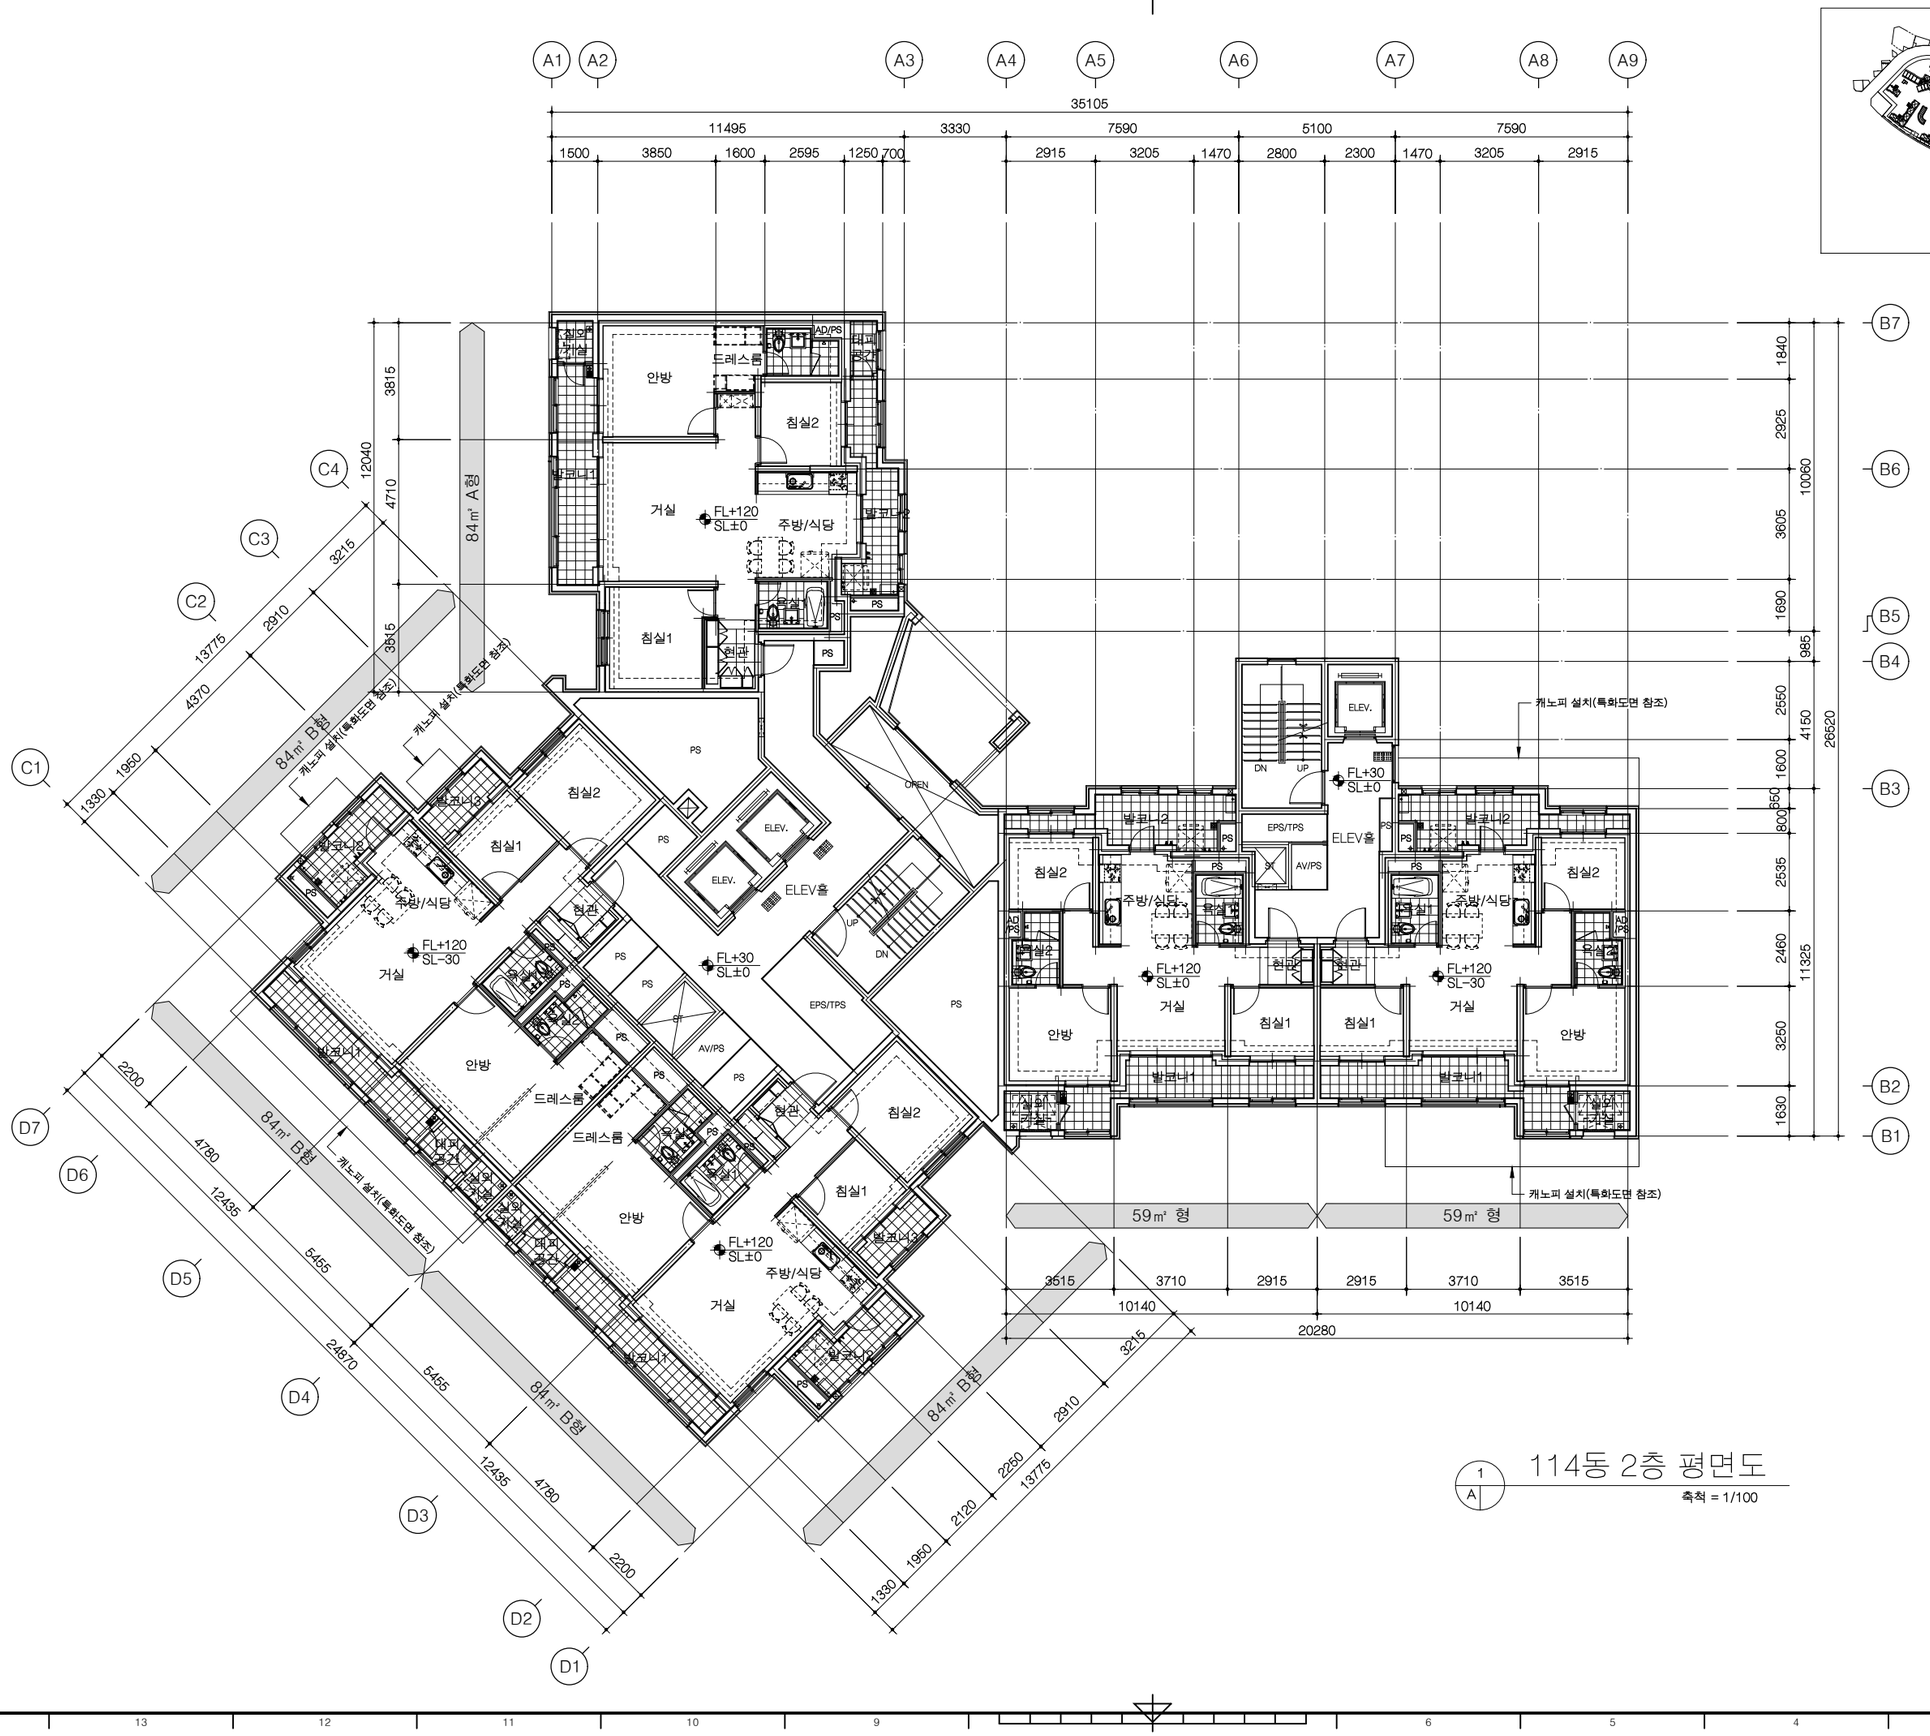

114동 2층 평면도

축척 = 1/100

KEY MXP

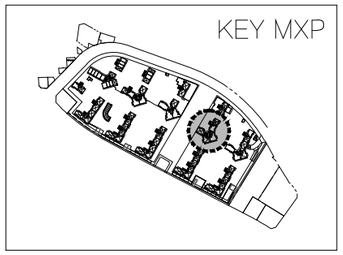

사업번호 PROJECT NO.

사업명 PROJECT TITLE

수색4재정비촉진구역
주택재개발 정비사업

KEY PLAN

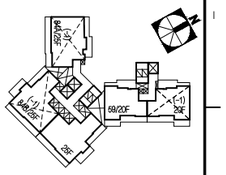

NOTE

1. 본 도면은 발코니 확장전를 기준으로 작성됨.
2. 지붕층 난간의 형태와 설치 위치는 안전성과 입면디자인을 고려하여 변경 가능함.
3. 지붕의 재료, 형태, 구조는 실시공 시 변경 될 수 있음.
4. 지붕 및 옥탑 구조물의 형태와 구조는 실시공 시 변경될 수 있음.
5. 옥상 출눈의 간격은 실시공 시 변경될 수 있음.
6. 옥상 출눈 틈에 실란트 시공되지 않음
7. 우편물 수취함 설치 위치는 변경될 수 있음
8. 오픈형 발코니 3층이상 ~ 20층이하 설치

2층 바닥LEVEL
2SL±0 = 2FL±0 = EL+28.00

수정번호 REV. NO.	일자 DATE	내 용 DESCRIPTION	승인 CHKD

설계 DESIGNED BY

검토 CHECKED BY
최 진 규

심사 SUMMITED BY
정 호 혁

승인 APPROVED BY
이 승 준

일자 DATE
2019.08

도면명 DRAWING TITLE
114동
2층 평면도

축 척 SCALE
A1: 1/100
A3: 1/200

도면번호 DRAWING NO.
A-514

일련번호 SHEET NO.

REV. NO.

HAUD
(주)하우드엔지니어링
종합건축사사무소
Architects, Planners & Engineers
TEL. 02 2149 4400, SEOUL, KOREA

1 A 114동 3층~20층 평면도

축척 = 1/100

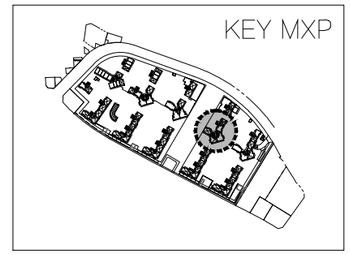

사업번호 PROJECT NO.

사업명 PROJECT TITLE

수색4재정비촉진구역
주택재개발 정비사업

KEY PLAN

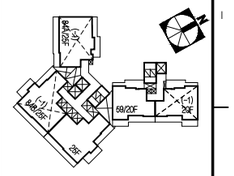

NOTE

1. 본 도면은 발코니 확장전를 기준으로 작성됨.
2. 지붕층 난간의 형태와 설치 위치는 안전성과 입면디자인을 고려하여 변경 가능함.
3. 지붕의 재료, 형태, 구조는 실시공 시 변경 될 수 있음.
4. 지붕 및 옥탑 구조물의 형태와 구조는 실시공 시 변경될 수 있음.
5. 옥상 출눈의 간격은 실시공 시 변경될 수 있음.
6. 옥상 출눈 틈에 실란트 시공되지 않음
7. 우편물 수취함 설치 위치는 변경될 수 있음
8. 오픈형 발코니 3층이상 ~ 20층이하 설치

수정번호 REV. NO.	일 자 DATE	내 용 DESCRIPTION	승 인 CHKD
1			
2			
3			
4			

설계 DESIGNED BY

검토 CHECKED BY
최 진 규

심사 SUMMITED BY
정 호 혁

승인 APPROVED BY
이 승 준

일자 DATE
2019.08

도면명 DRAWING TITLE

114동
3~20층 평면도

축 척 SCALE
A1: 1/100
A3: 1/200

도면번호 DRAWING NO.
A-515

일련번호 SHEET NO.

REV. NO.

HAUD
(주)하우드건지니어링
종합건축사사무소
Architects, Planners & Engineers
TEL. 02 3143 4400, SEOUL, KOREA

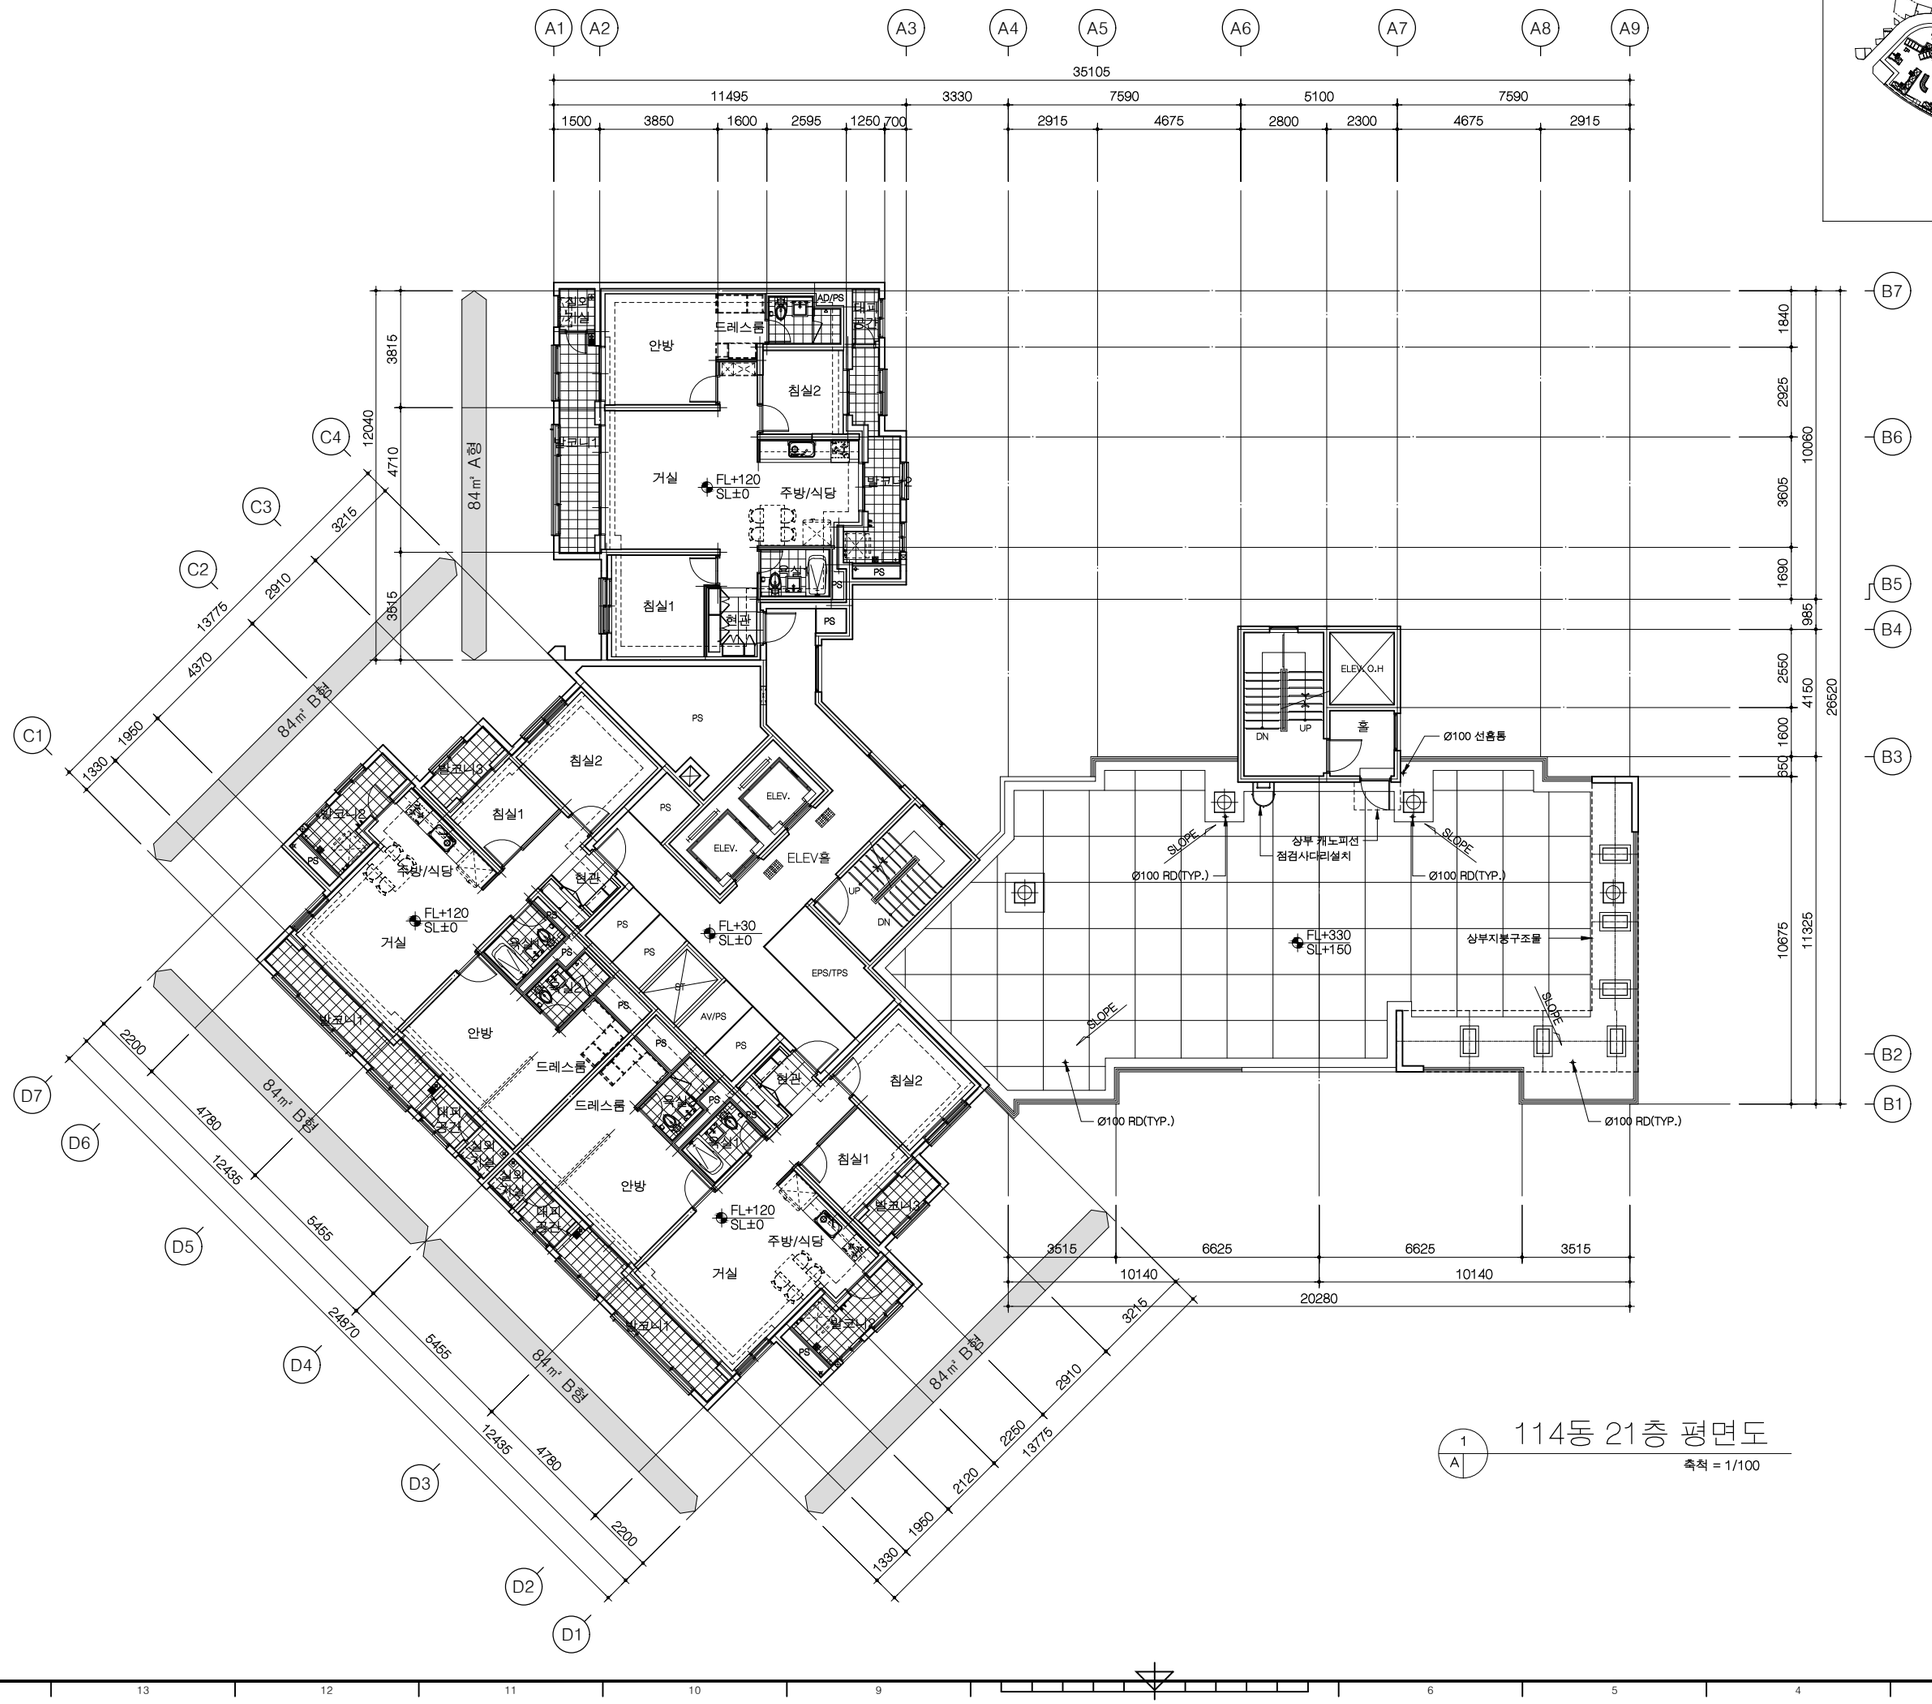

1 A 114동 21층 평면도

축척 = 1/100

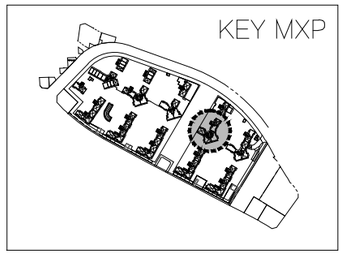

사업번호 PROJECT NO.

사업명 PROJECT TITLE

수색4재정비촉진구역
주택재개발 정비사업

KEY PLAN

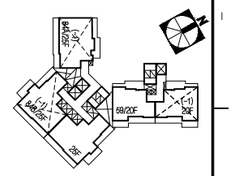

NOTE

1. 본 도면은 발코니 확장전를 기준으로 작성됨.
2. 지붕층 난간의 형태와 설치 위치는 안전성과 입면디자인을 고려하여 변경 가능함.
3. 지붕의 재료, 형태, 구조는 실시공 시 변경 될 수 있음.
4. 지붕 및 옥탑 구조물의 형태와 구조는 실시공 시 변경될 수 있음.
5. 옥상 출눈의 간격은 실시공 시 변경될 수 있음.
6. 옥상 출눈 틈에 실란트 시공되지 않음
7. 우편물 수취함 설치 위치는 변경될 수 있음
8. 오픈형 발코니 3층이상 ~ 20층이하 설치

수정번호 REV. NO.	일 자 DATE	내 용 DESCRIPTION	승 인 CHKD

설계 DESIGNED BY

검토 CHECKED BY
최 진 규

심사 SUMMITED BY
정 호 혁

승인 APPROVED BY
이 승 준

일자 DATE
2019.08

도면명 DRAWING TITLE

114동
21층 평면도

축 척 SCALE
A1: 1/100
A3: 1/200

도면번호 DRAWING NO.
A-516

일련번호 SHEET NO.

REV. NO.

HAUD
(주)하우드엔지니어링
종합건축사사무소
Architects, Planners & Engineers
TEL. 02 2149 4400, SEOUL, KOREA

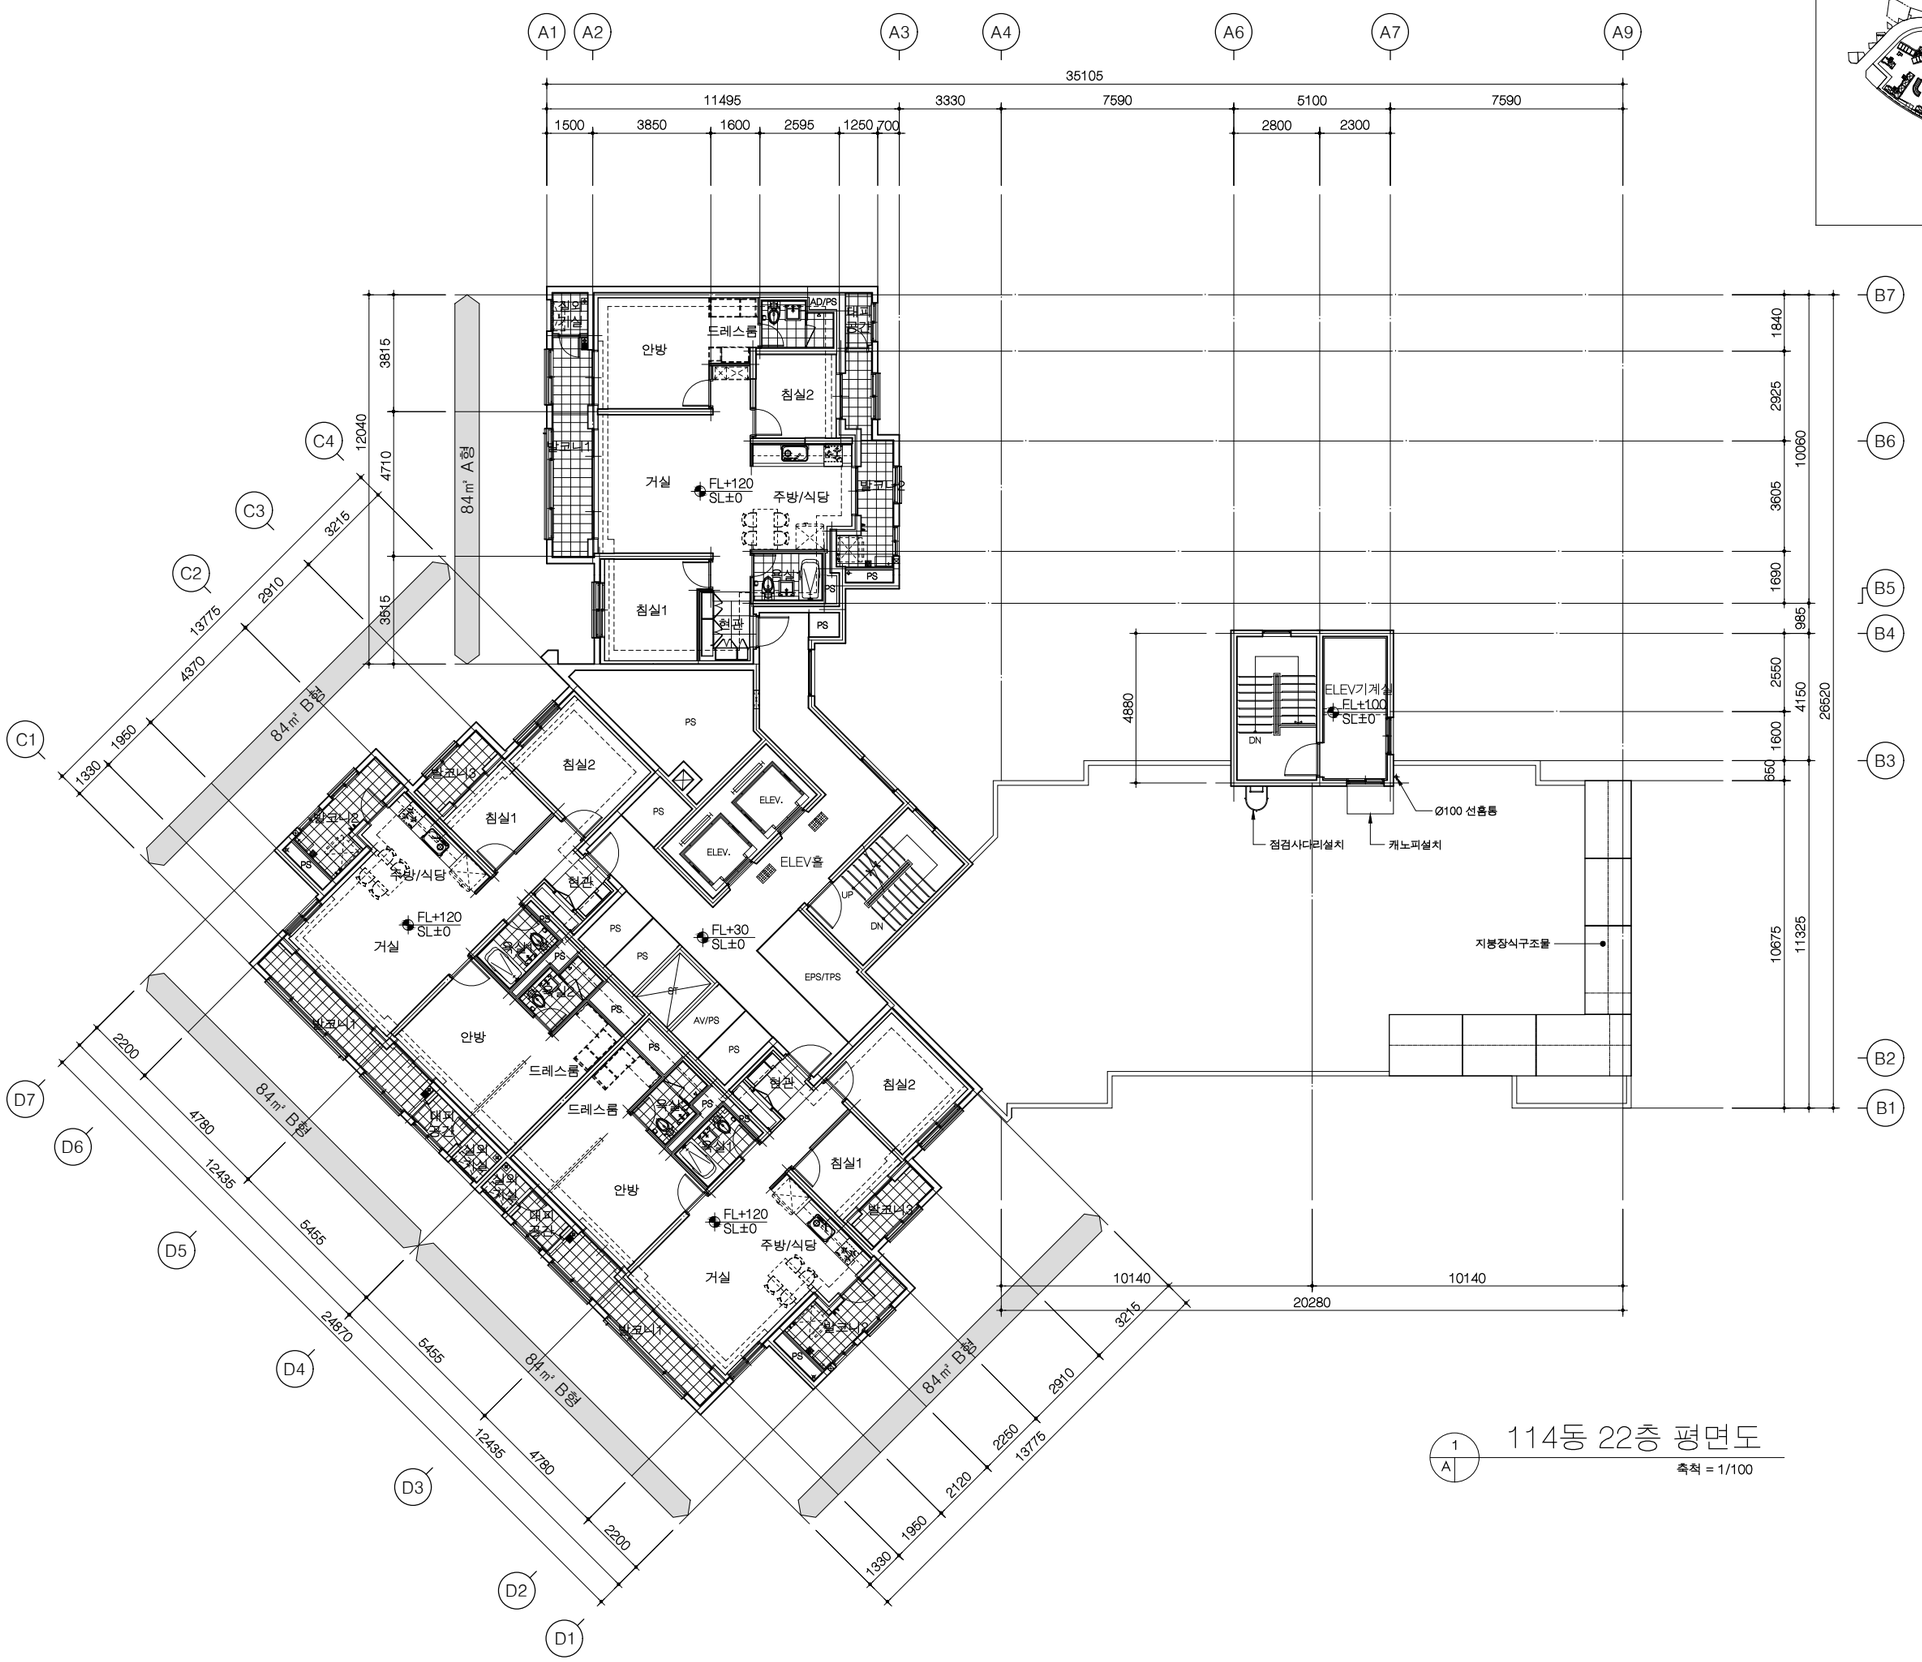

114동 22층 평면도

1/A

축척 = 1/100

KEY MXP

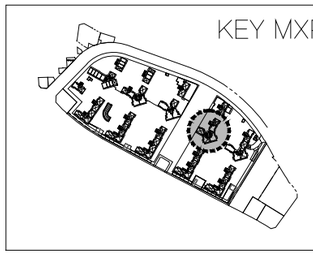

사업번호 PROJECT NO.

사업명 PROJECT TITLE

수색4재정비촉진구역
주택재개발 정비사업

KEY PLAN

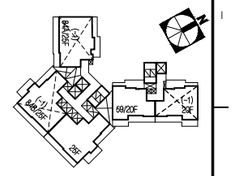

NOTE

1. 본 도면은 발코니 확장전를 기준으로 작성됨.
2. 지붕층 난간의 형태와 설치 위치는 안전성과 입면디자인을 고려하여 변경 가능함.
3. 지붕의 재료, 형태, 구조는 실시공 시 변경 될 수 있음.
4. 지붕 및 옥탑 구조물의 형태와 구조는 실시공 시 변경될 수 있음.
5. 옥상 출눈의 간격은 실시공 시 변경될 수 있음.
6. 옥상 출눈 틈에 실란트 시공되지 않음
7. 우편물 수취함 설치 위치는 변경될 수 있음
8. 오픈형 발코니 3층이상 ~ 20층이하 설치

수정번호 REV. NO.	일 자 DATE	내 용 DESCRIPTION	승 인 CHKD

설계 DESIGNED BY

검토 CHECKED BY
최 진 규

심사 SUMMITED BY
정 호 혁

승인 APPROVED BY
이 승 준

일자 DATE
2019.08

도면명 DRAWING TITLE

114동
22층 평면도

축 척 SCALE
A1: 1/100
A3: 1/200

도면번호 DRAWING NO.
A-517

일련번호 SHEET NO.

REV. NO.

HAUD
(주)하우드엔지니어링
종합건축사사무소
Architects, Planners & Engineers
TEL. 82 2140 4400, SEOUL, KOREA

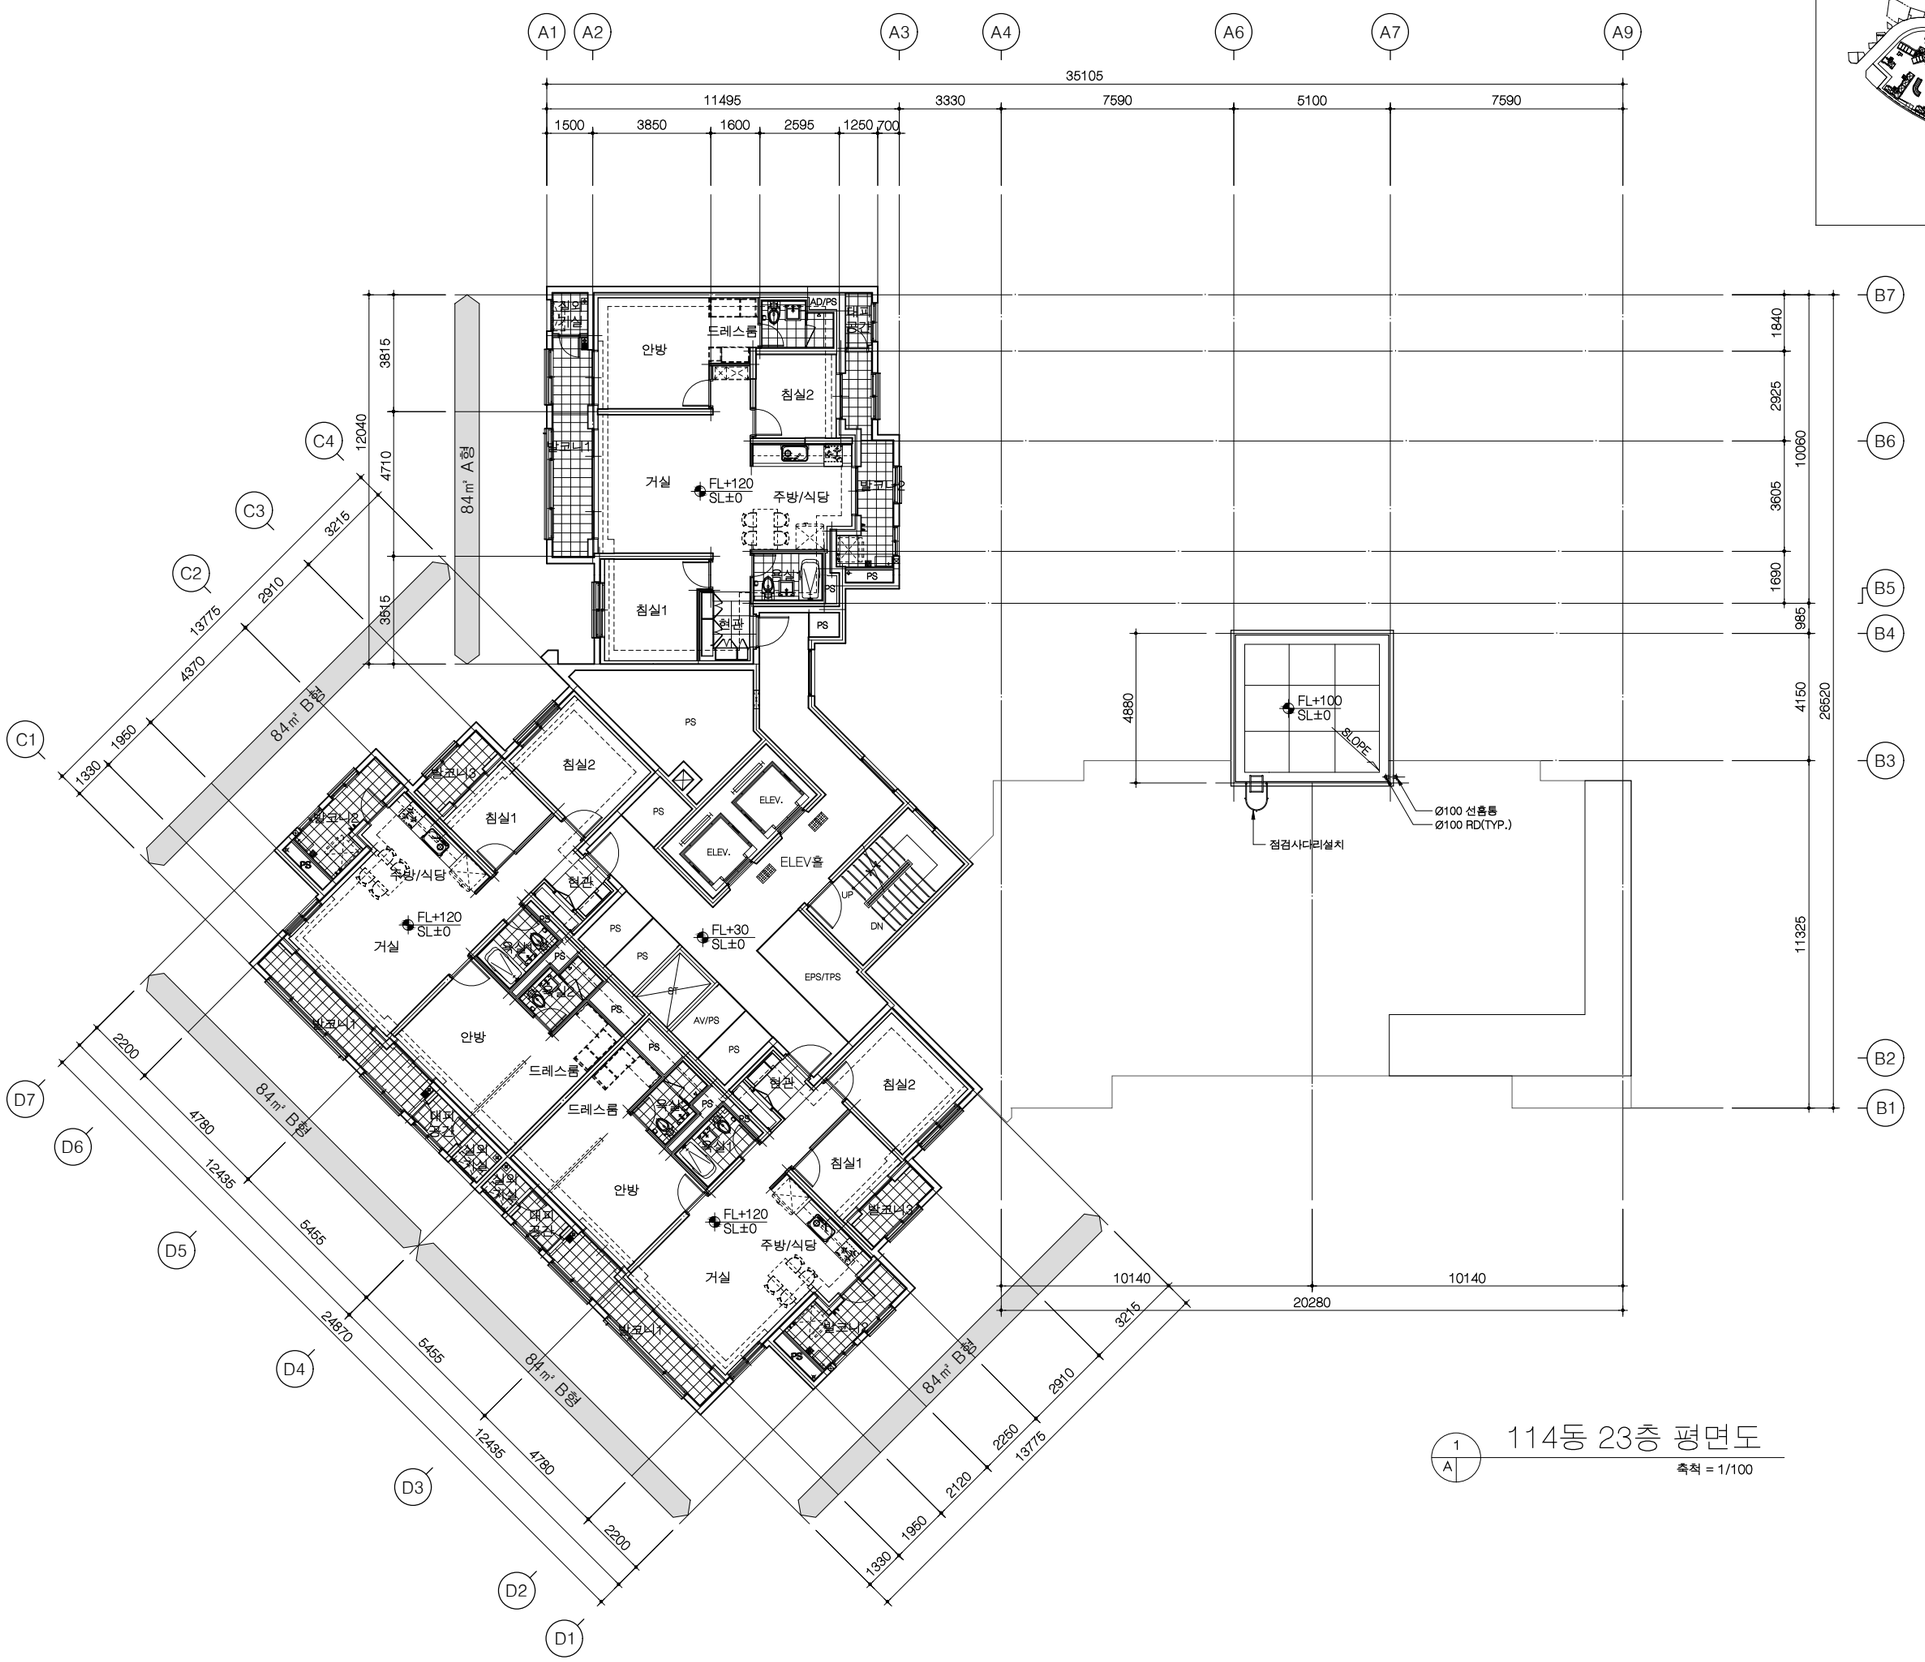

1 A 114동 23층 평면도

축척 = 1/100

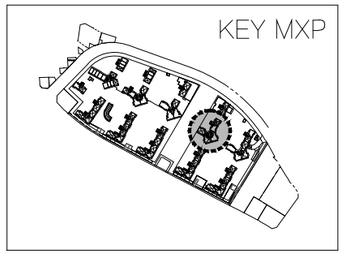

사업번호 PROJECT NO.

사업명 PROJECT TITLE

수색4재정비촉진구역
주택재개발 정비사업

KEY PLAN

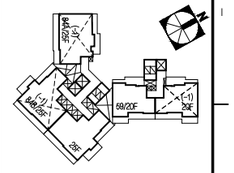

NOTE

1. 본 도면은 발코니 확장전를 기준으로 작성됨.
2. 지붕층 난간의 형태와 설치 위치는 안전성과 입면디자인을 고려하여 변경 가능함.
3. 지붕의 재료, 형태, 구조는 실시공 시 변경 될 수 있음.
4. 지붕 및 옥탑 구조물의 형태와 구조는 실시공 시 변경될 수 있음.
5. 옥상 출눈의 간격은 실시공 시 변경될 수 있음.
6. 옥상 출눈 틈에 실란트 시공되지 않음
7. 우편물 수취함 설치 위치는 변경될 수 있음
8. 오픈형 발코니 3층이상 ~ 20층이하 설치

수정번호 REV. NO.	일 자 DATE	내 용 DESCRIPTION	승 인 CHKD

설계 DESIGNED BY

검토 CHECKED BY
최 진 규

심사 SUMMITED BY
정 호 혁

승인 APPROVED BY
이 승 준

일자 DATE
2019.08

도면명 DRAWING TITLE

114동
23층 평면도

축 척 SCALE
A1: 1/100
A3: 1/200

도면번호 DRAWING NO.
A-518

일련번호 SHEET NO.

REV. NO.

HAUD
㈜하우드엔지니어링
종합건축사사무소
Architects, Planners & Engineers
TEL. 82 2 140 4400, SEOUL, KOREA

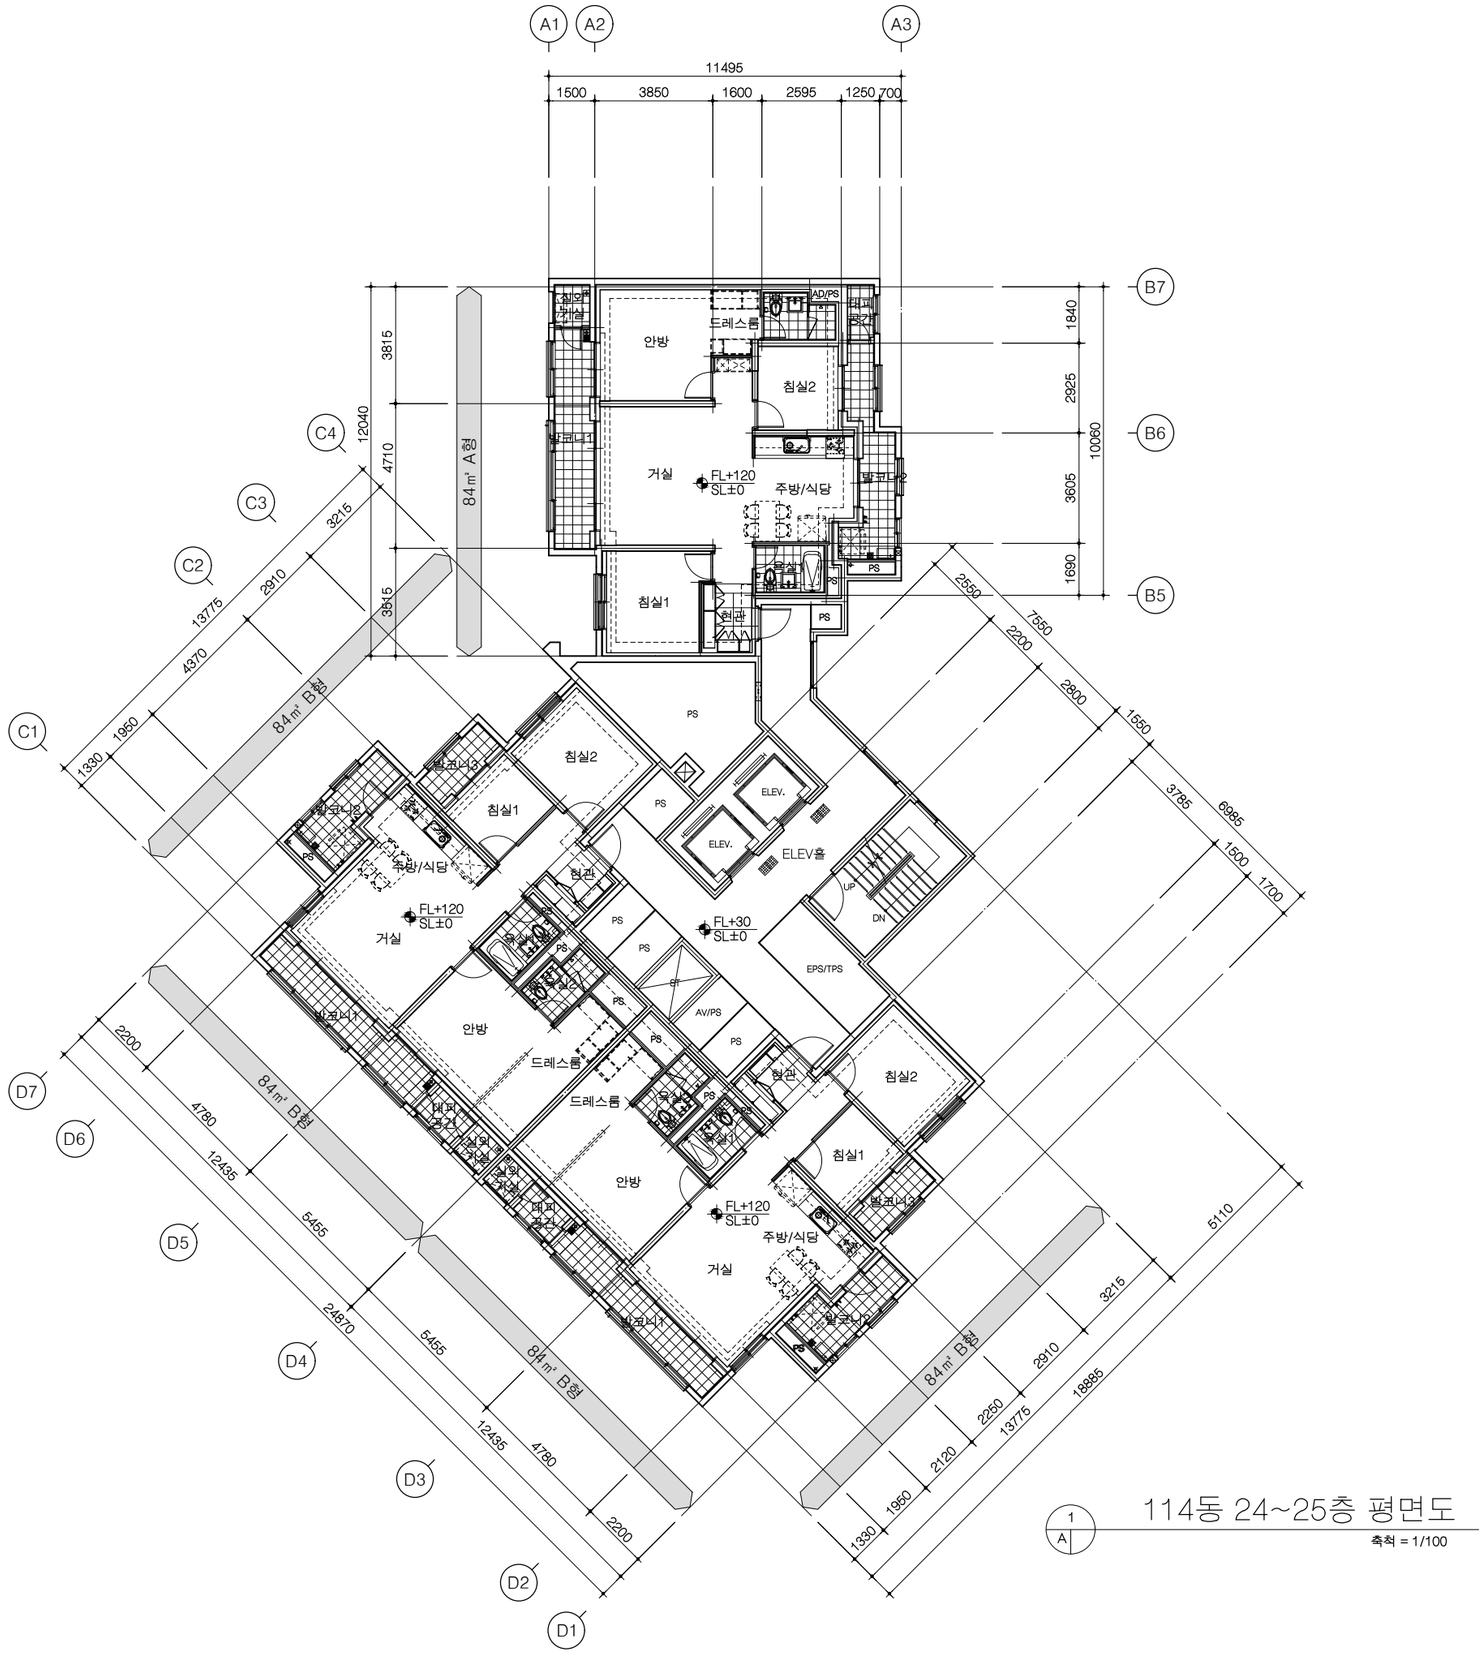

1 A 114동 24~25층 평면도

축척 = 1/100

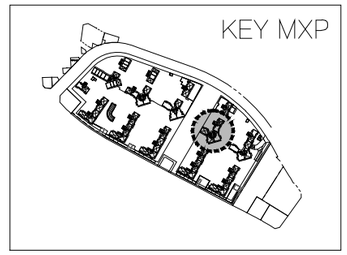

사업번호 PROJECT NO.

사업명 PROJECT TITLE

수색4재정비촉진구역
주택재개발 정비사업

KEY PLAN

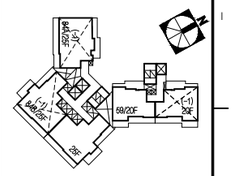

NOTE

1. 본 도면은 발코니 확장전를 기준으로 작성됨.
2. 지붕층 난간의 형태와 설치 위치는 안전성과 입면디자인을 고려하여 변경 가능함.
3. 지붕의 재료, 형태, 구조는 실시공 시 변경 될 수 있음.
4. 지붕 및 옥탑 구조물의 형태와 구조는 실시공 시 변경될 수 있음.
5. 옥상 출눈의 간격은 실시공 시 변경될 수 있음.
6. 옥상 출눈 틈에 실란트 시공되지 않음
7. 우편물 수취함 설치 위치는 변경될 수 있음
8. 오픈형 발코니 3층이상 ~ 20층이하 설치

수정번호 REV. NO.	일 자 DATE	내 용 DESCRIPTION	승 인 CHKD
△			
△			
△			
△			

설계 DESIGNED BY

검토 CHECKED BY
최 진 규

심사 SUMMITED BY
정 호 혁

승인 APPROVED BY
이 승 준

일자 DATE
2019.08

도면명 DRAWING TITLE
114동
24~25층 평면도

축 척 SCALE
A1: 1/100
A3: 1/200

도면번호 DRAWING NO.
A-519

일련번호 SHEET NO.

△ REV. NO.

HAUD
(주)하우드엔지니어링
종합건축사사무소
Architects, Planners & Engineers
TEL. 02 2149 4400, SEOUL, KOREA

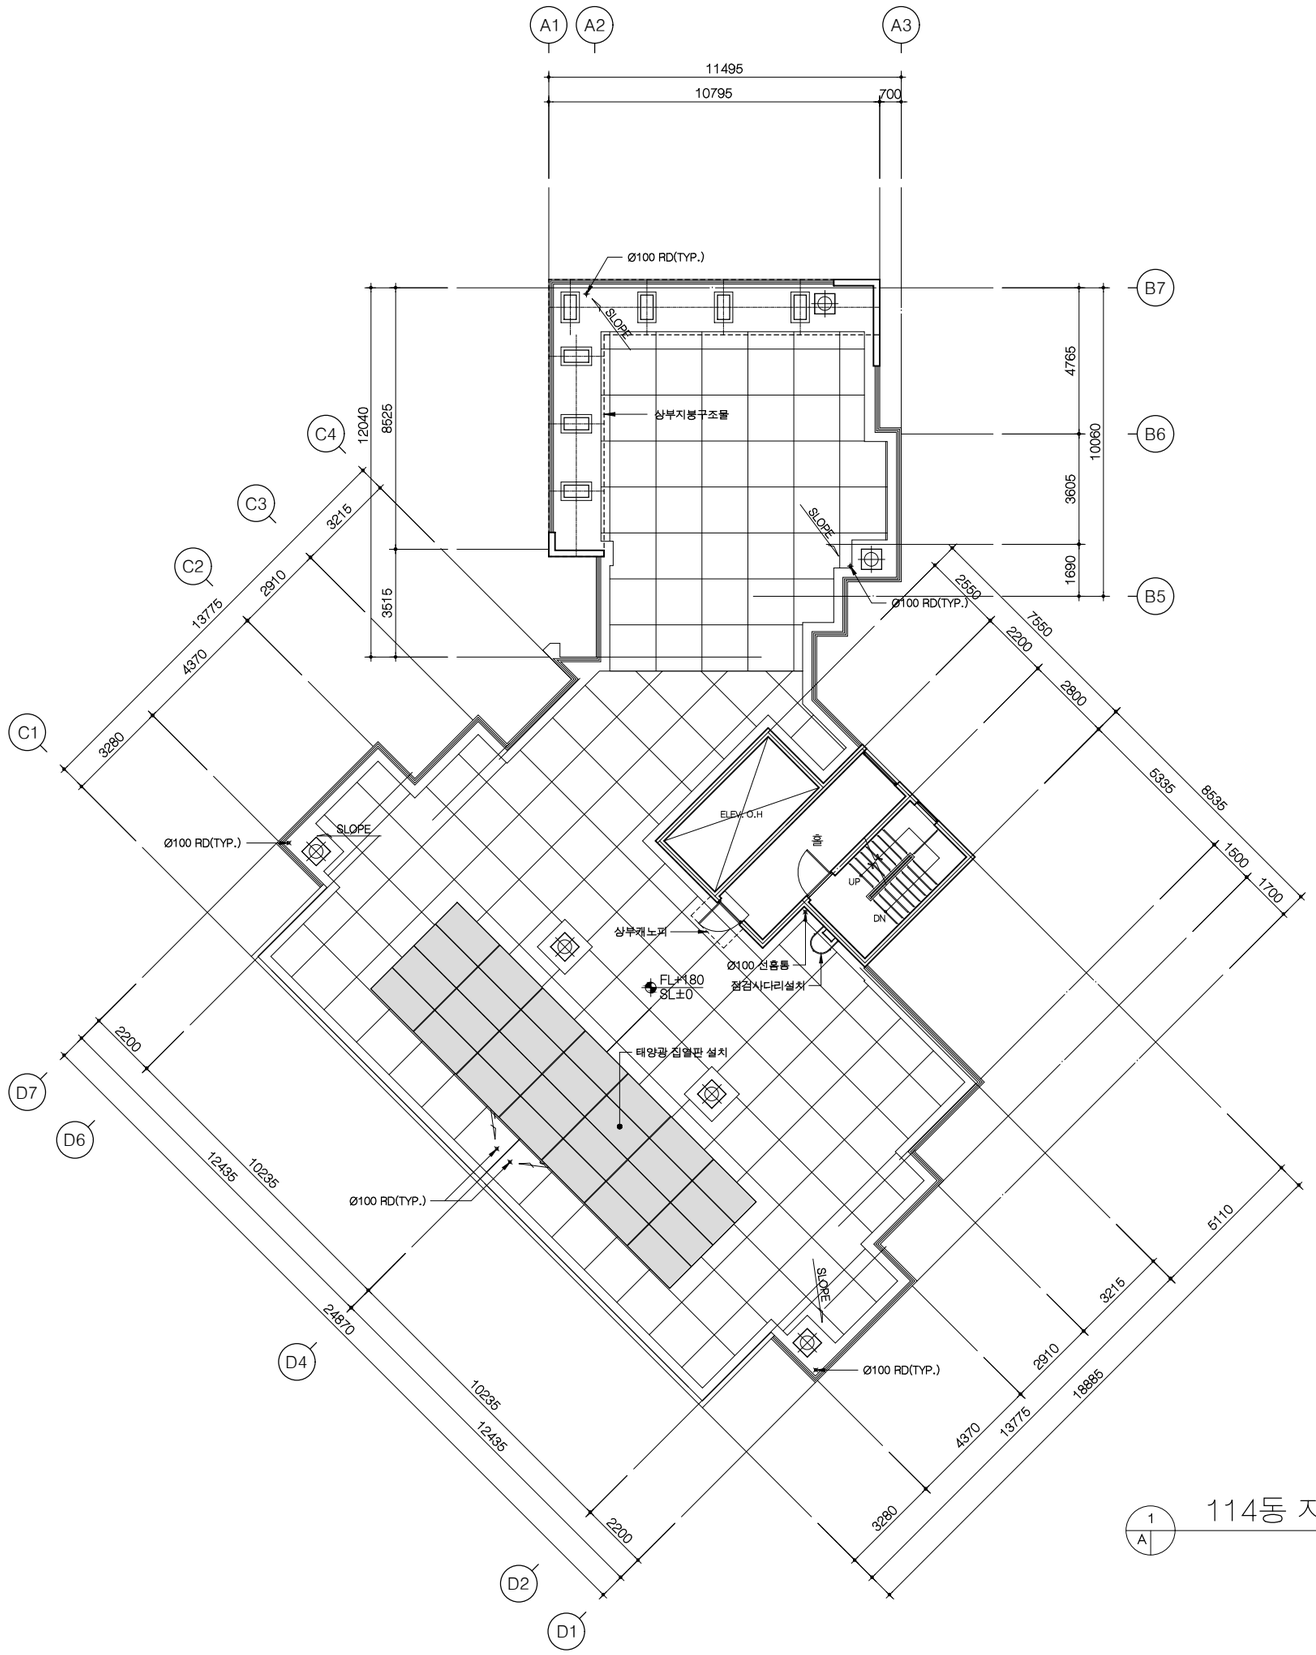

1 A 114동 지붕 평면도

축척 = 1/100

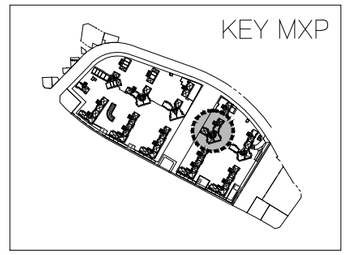

사업번호 PROJECT NO.

사업명 PROJECT TITLE

수색4재정비촉진구역
주택재개발 정비사업

KEY PLAN

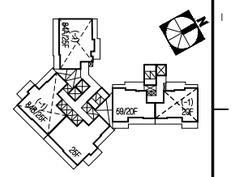

NOTE

1. 지붕바닥
   ① EXP. JOINT: 3000 X 3000
2. 본 평면도는 발코니확장전을 기준으로 작성됨
3. 재료마감은 실내,외 재료마감표 참조
4. 지붕 난간형태/설치위치는 안전성과 입면을 고려하여 실시공시 변경될 수 있음
5. 지붕재료 및 형태,구조는 실시공시 변경될수 있음
6. 지붕(옥탑지붕)의 배수드레인,환소용고리, 베기탑,점검사다리(점검구) 등의 설치위치/개소는 실시공시 변경될 수 있음
7. 옥상 상부구조물은 PC구조물 임.
8. 정화조 배기는 기계도서 참조

수정번호 REV. NO.	일 자 DATE	내 용 DESCRIPTION	승 인 CHKD

설계 DESIGNED BY

검토 CHECKED BY
최 진 규

심사 SUMMITED BY
정 호 혁

승인 APPROVED BY
이 승 준

일자 DATE
2019.08

도면명 DRAWING TITLE
114동
지붕 평면도

축 척 SCALE
A1: 1/100
A3: 1/200

도면번호 DRAWING NO.
A-520

일련번호 SHEET NO.

REV. NO.

HAUD
㈜하우드엔지니어링
종합건축사사무소
Architects, Planners & Engineers
TEL. 02 2140 4400, SEOUL, KOREA

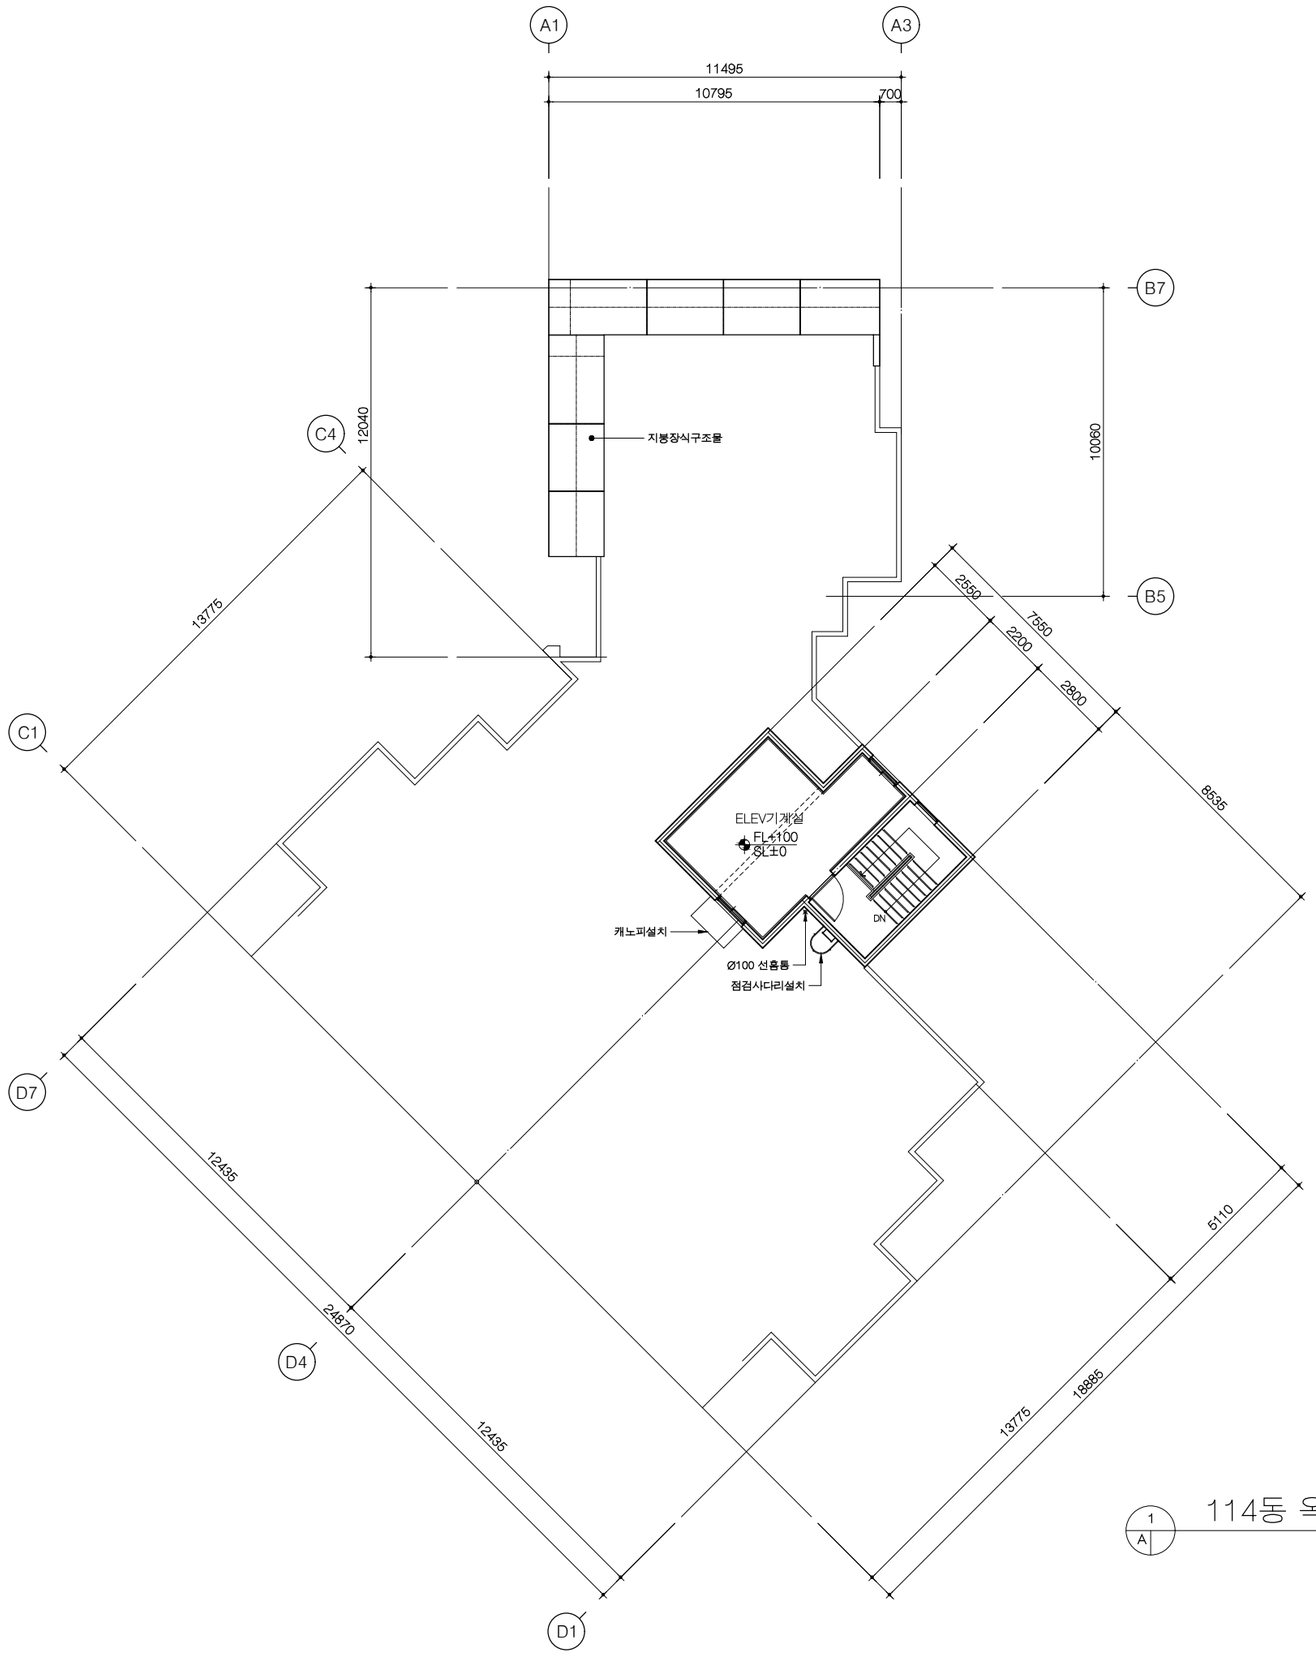

1 A 114동 옥탑 평면도

축척 = 1/100

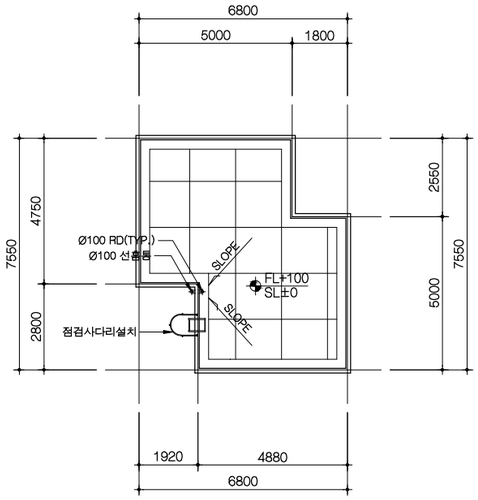

2 A 114동 옥탑지붕 평면도

축척 = 1/100

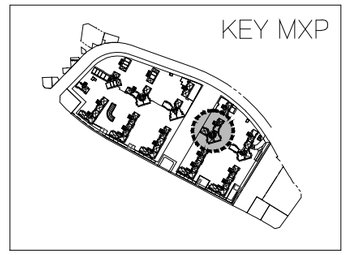

사업번호 PROJECT NO.

사업명 PROJECT TITLE

수색4재정비촉진구역
주택재개발 정비사업

KEY PLAN

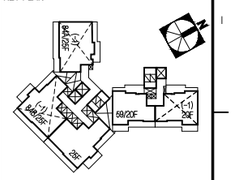

NOTE

1. 지붕바닥
   ① EXP. JOINT: 3000 X 3000
2. 본 평면도는 발코니확장전을 기준으로 작성됨
3. 재료마감은 실내,외 재료마감표 참조
4. 지붕 난간형태/설치위치는 안전성과 입면을 고려하여 실시공시 변경될 수 있음
5. 지붕재료 및 형태,구조는 실시공시 변경될수 있음
6. 지붕(옥탑지붕)의 배수드레인,청소용고리, 베기탑,점검사다리(점검구) 등의 설치위치/개소는 실시공시 변경될 수 있음
7. 옥상 상부구조물은 PC구조물 임.
8. 정화조 배기는 기계도서 참조

수정번호 REV. NO.	일 자 DATE	내 용 DESCRIPTION	승 인 CHKD
△			
△			
△			
△			

설계 DESIGNED BY

검토 CHECKED BY
최 진 규

심사 SUMMITED BY
정 호 혁

승인 APPROVED BY
이 승 준

일자 DATE
2019.08

도면명 DRAWING TITLE
114동
옥탑층 및 옥탑지붕 평면도

축 척 SCALE
A1: 1/100
A3: 1/200

도면번호 DRAWING NO.
A-521

일련번호 SHEET NO.

REV. NO.

HAUD
(주)하우드엔지니어링
종합건축사사무소
Architects, Planners & Engineers
TEL. 02 2143 4400, SEOUL, KOREA

1 A 114동 정면도

축척 = 1/150

2 A 114동 우측면도

축척 = 1/150

사업번호 PROJECT NO.

사업명 PROJECT TITLE

수색4재정비촉진구역
주택재개발 정비사업

KEY PLAN

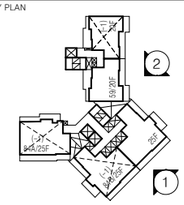

NOTE

1. 1층 바닥 LEVEL
   1SL±0 = 1FL±0 = GL±0 = EL+24.80
2. 지붕 난간의 형태 및 설치위치는 안전성과 입면디자인을 고려하여 변경가능함.
3. 지붕의 재료, 형태, 구조는 실시공시 변경될 수 있음.
4. 지붕 및 옥탑구조물의 형태와 구조는 실시공시 변경될 수 있음.
5. 외벽 및 측벽 문양은 실시공시 변경될 수 있음
6. 입면의 줄눈 및 마감선은 실시공시 변경될 수 있음.
7. 저층부 석재마감 및 입면 마감 색상, 재료에 대한 모든 기준은 특화도면을 우선 적용함.

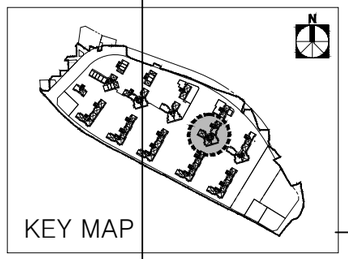

수정번호 REV. NO.	일 자 DATE	내 용 DESCRIPTION	승 인 CHKD
△			
△			
△			
△			

설계 DESIGNED BY

검토 CHECKED BY
최 진 규

심사 SUMMITED BY
정 호 혁

승인 APPROVED BY
이 승 준

일자 DATE
2019.08

도면명 DRAWING TITLE
114동 정면도,우측면도

축 척 SCALE
A1: 1/150
A3: 1/300

도면번호 DRAWING NO.
A-522

일련번호 SHEET NO.

△ REV. NO.

HAUD
㈜하우드엔지니어링
종합건축사사무소
Architects, Planners & Engineers
TEL. 82 2149 4400, SEOUL, KOREA

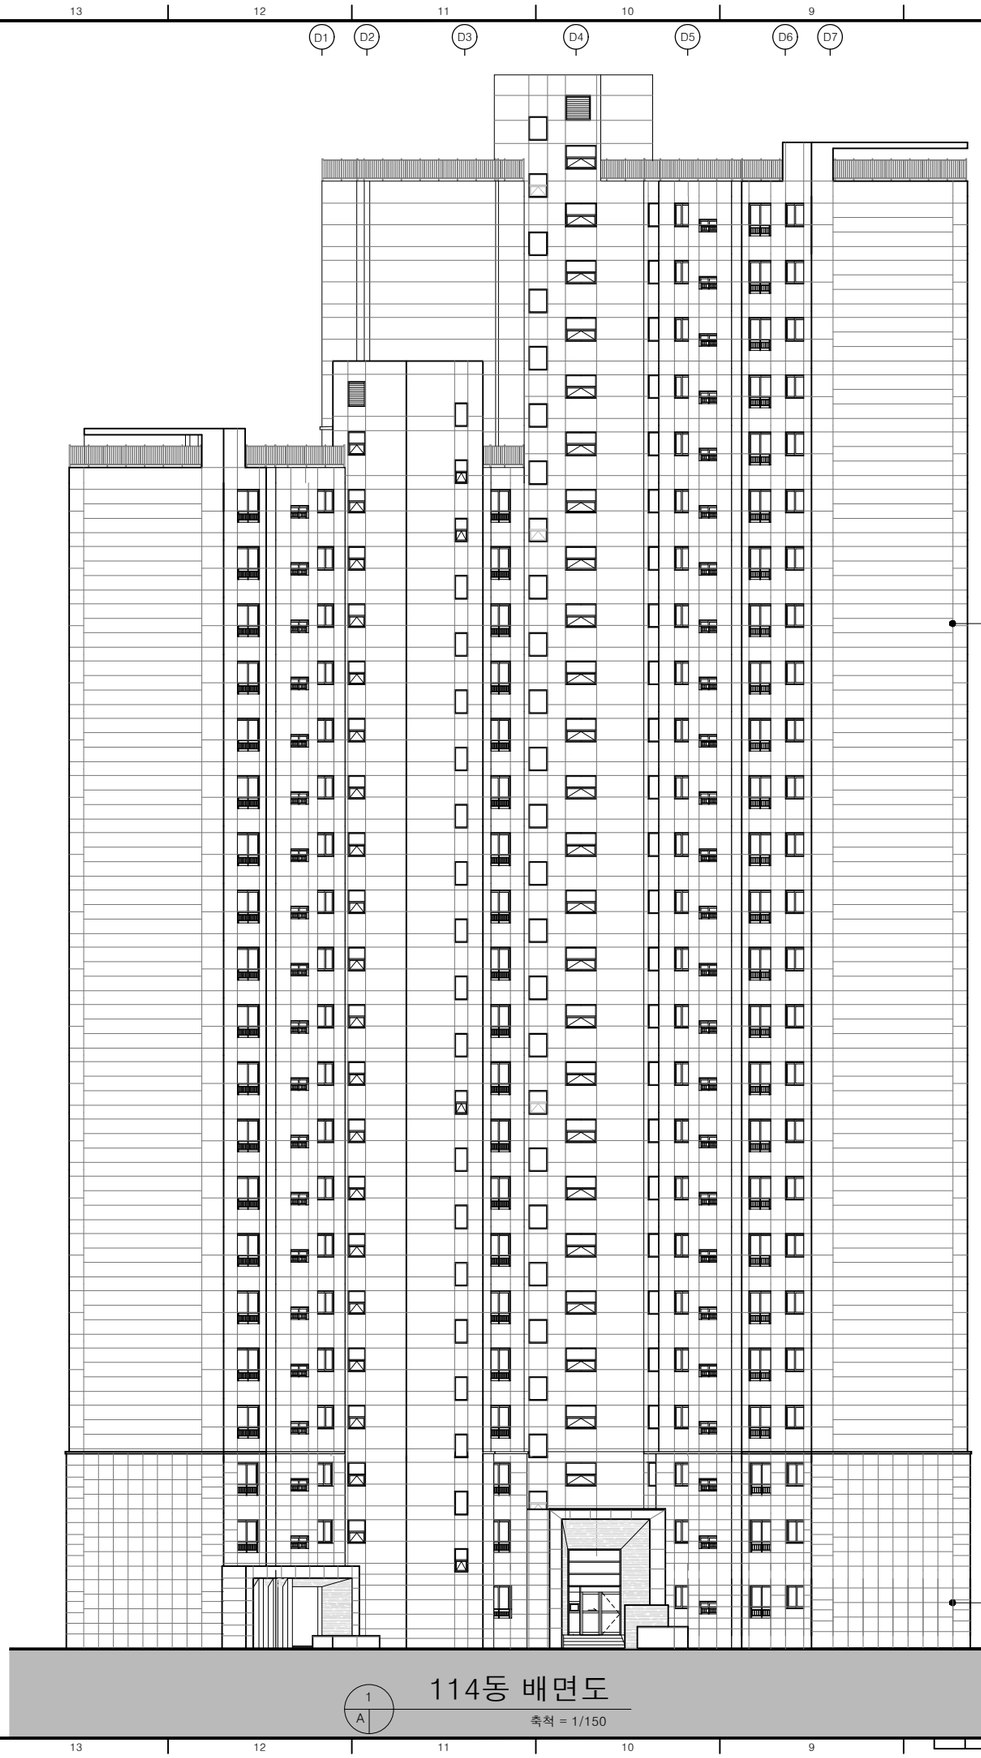

1 A 114동 배면도

축척 = 1/150

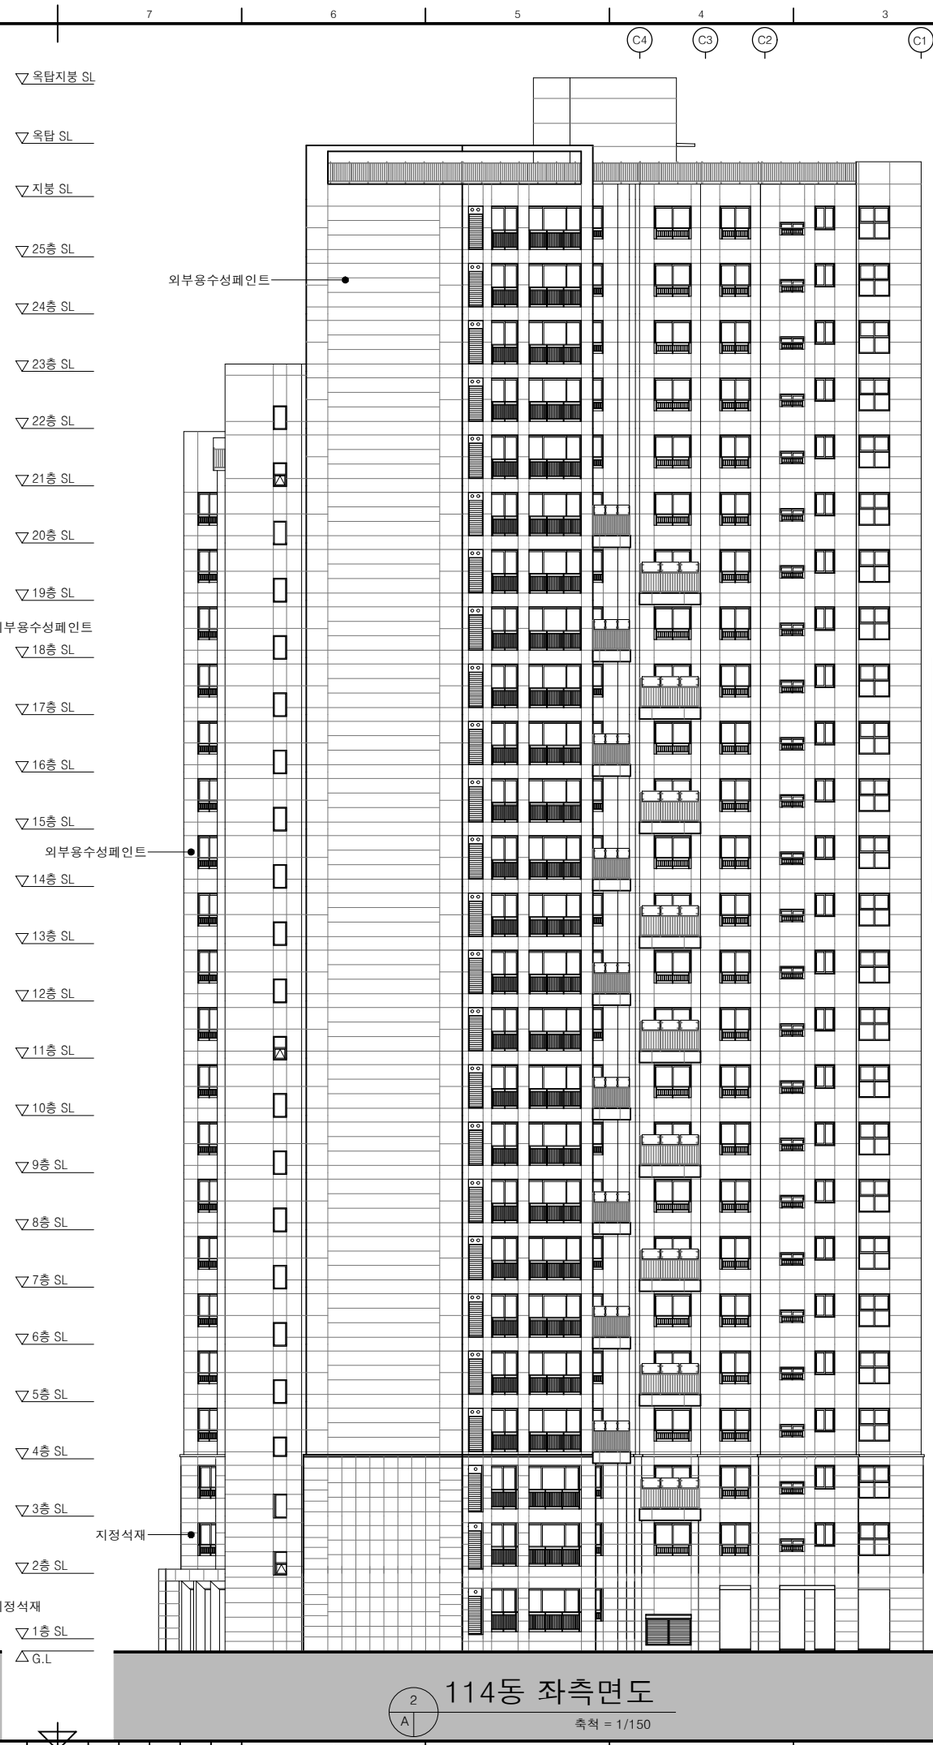

2 A 114동 좌측면도

축척 = 1/150

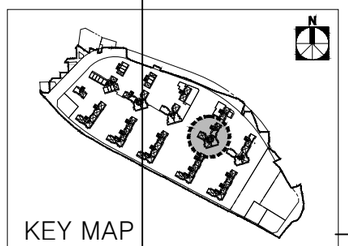

KEY MAP

사업번호 PROJECT NO.

사업명 PROJECT TITLE

수색4재정비촉진구역
주택재개발 정비사업

KEY PLAN

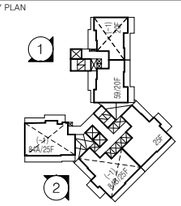

NOTE

1. 1층 바닥 LEVEL
   1SL±0 = 1FL±0 = GL±0 = EL+24.80
2. 지붕 난간의 형태 및 설치위치는 안전성과 입면디자인을 고려하여 변경가능함.
3. 지붕의 재료, 형태, 구조는 실시공시 변경될 수 있음.
4. 지붕 및 옥탑구조물의 형태와 구조는 실시공시 변경될 수 있음.
5. 외벽 및 측벽 문양은 실시공시 변경될 수 있음
6. 입면의 줄눈 및 마감선은 실시공시 변경될 수 있음.
7. 저층부 석재마감 및 입면 마감 색상, 재료에 대한 모든 기준은 특화도면을 우선 적용함.

수정번호 REV. NO.	일 자 DATE	내 용 DESCRIPTION	승 인 CHKD
△			
△			
△			
△			

설계 DESIGNED BY

검토 CHECKED BY
최 진 규

심사 SUMMITED BY
정 호 혁

승인 APPROVED BY
이 승 준

일자 DATE
2019.08

도면명 DRAWING TITLE
114동 배면도,좌측면도

축 척 SCALE
A1: 1/150
A3: 1/300

도면번호 DRAWING NO.
A-523

얼럿번호 SHEET NO.

△ REV. NO.

HAUD
㈜하우드엔지니어링
종합건축사사무소
Architects, Planners & Engineers
TEL. 82 2 140 4400, SEOUL, KOREA

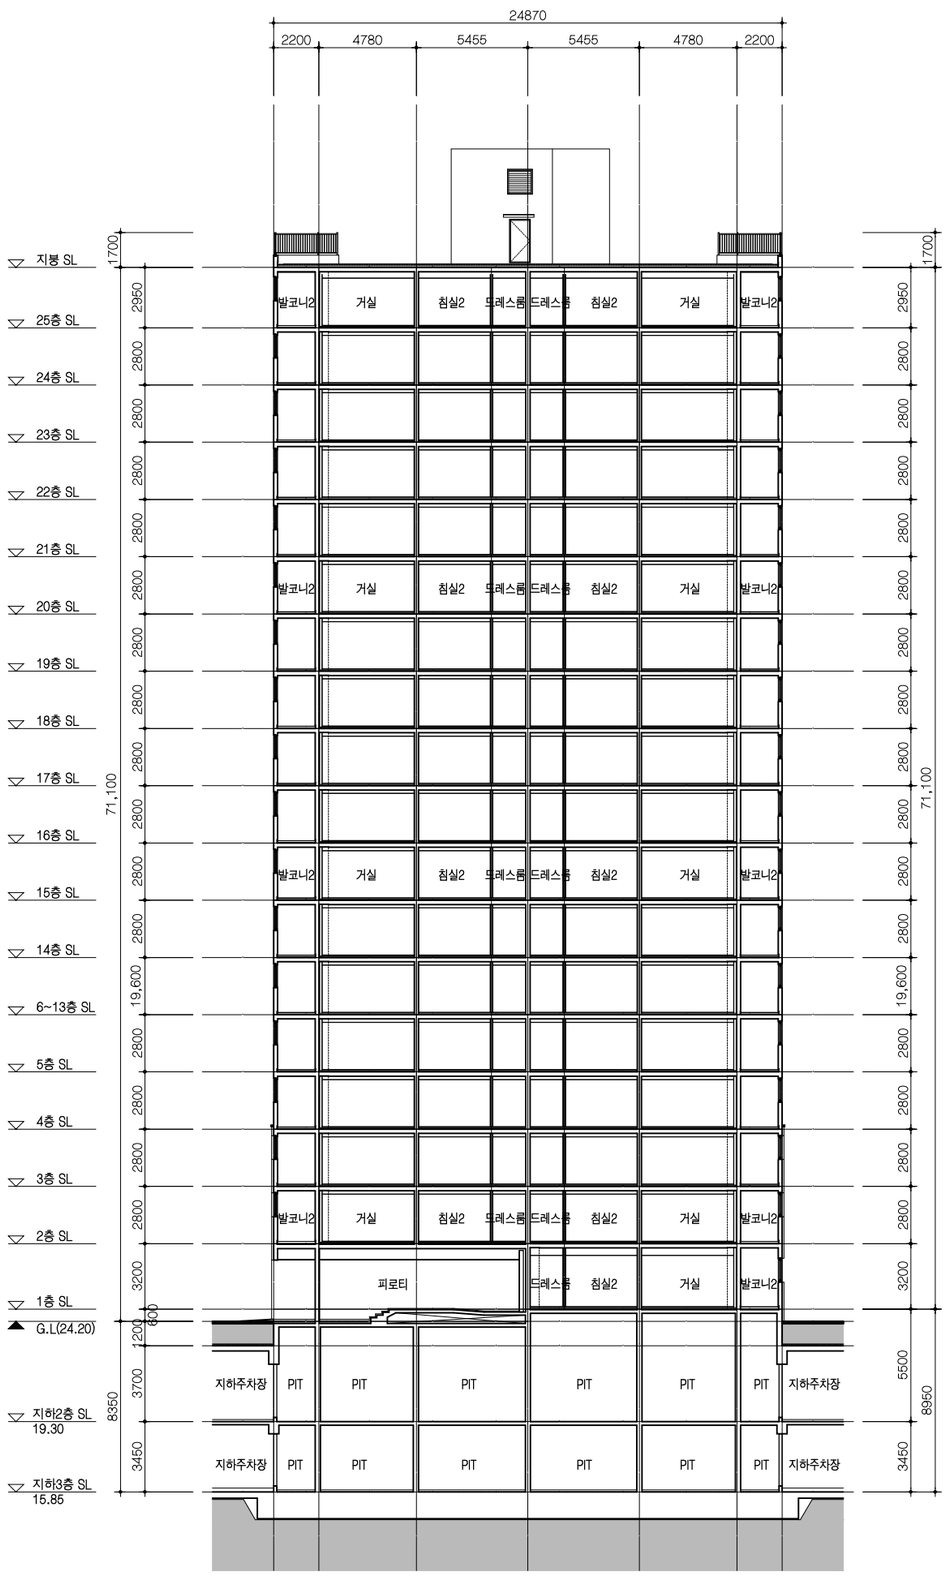

1 A 114동 종단면도

축척 = 1/150

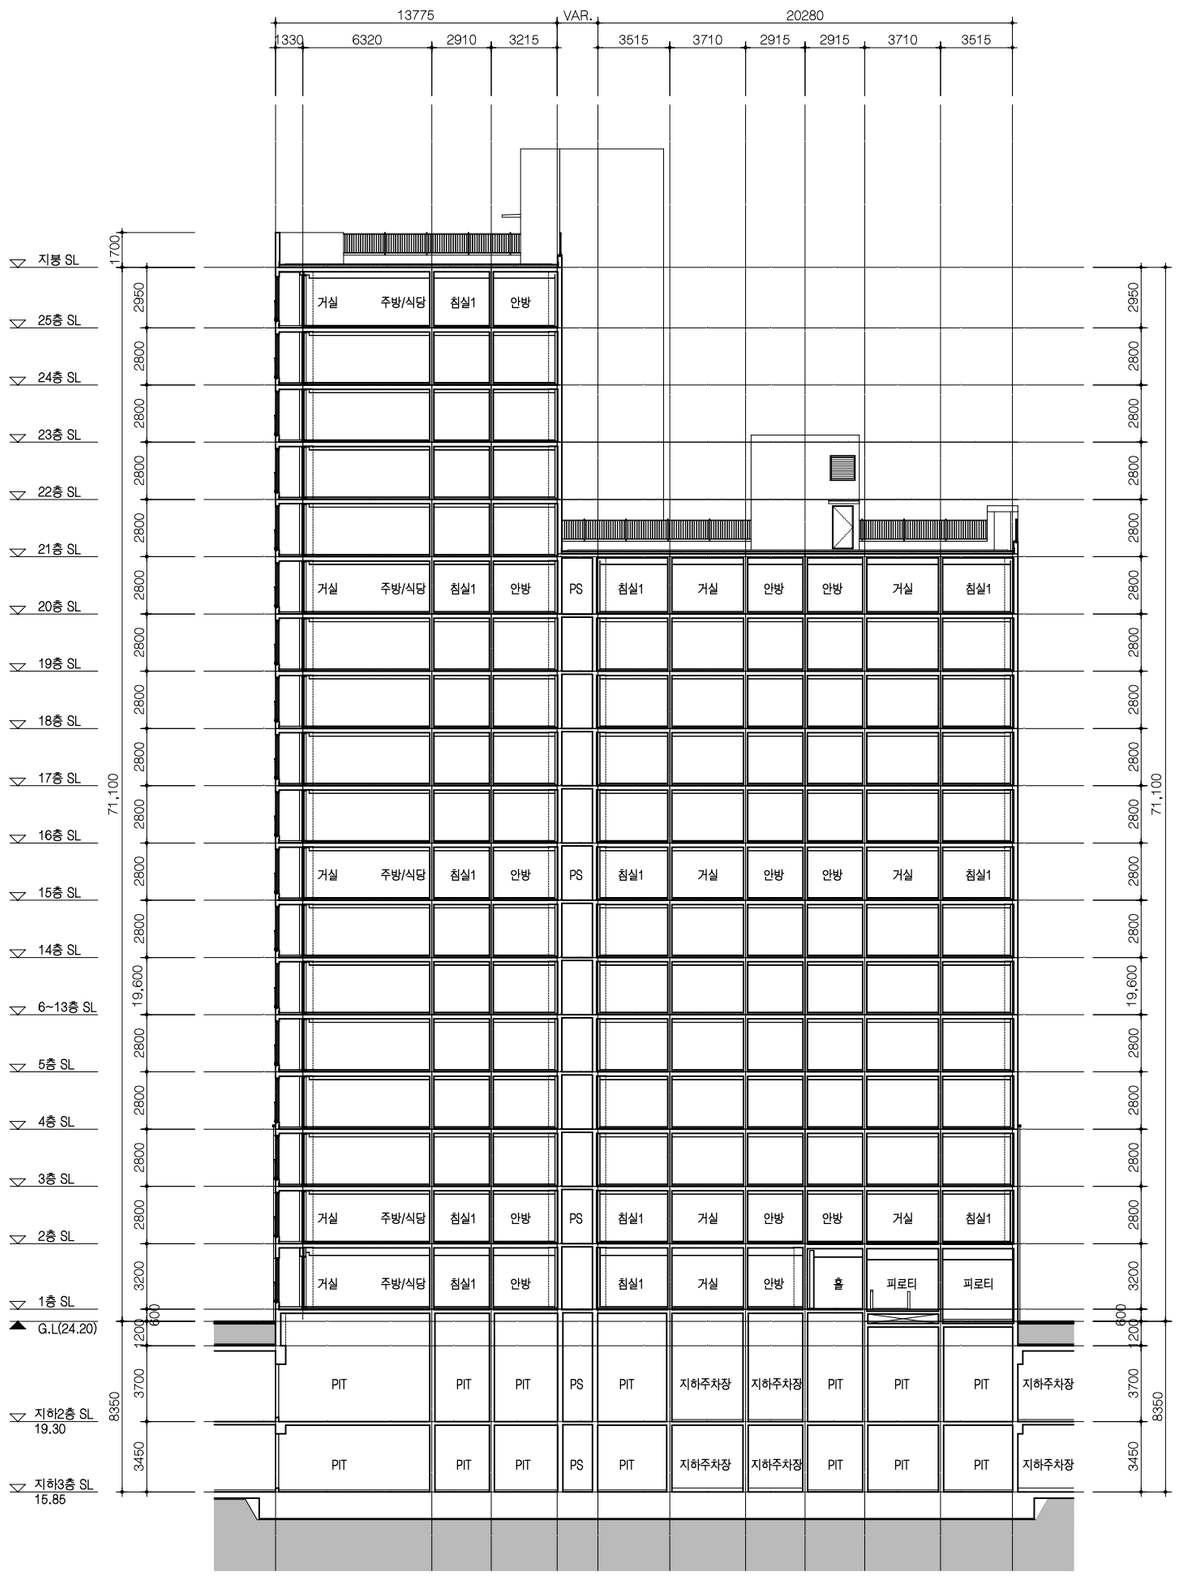

2 A 114동 횡단면도

축척 = 1/150

사업번호 PROJECT NO.

사업명 PROJECT TITLE

수색4재정비촉진구역
주택재개발 정비사업

KEY PLAN

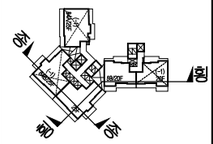

NOTE

수정번호 REV. NO.	일 자 DATE	내 용 DESCRIPTION	승 인 CHKD
△			
△			
△			
△			

설계 DESIGNED BY

검토 CHECKED BY
최 진 규

심사 SUMMITED BY
정 호 혁

승인 APPROVED BY
이 승 준

일자 DATE
2019.08

도면명 DRAWING TITLE
114동 종,횡단면도

축 척 SCALE
A1: 1/150
A3: 1/300

도면번호 DRAWING NO.
A-524

일련번호 SHEET NO. △ REV. NO.

HAUD
㈜하우드엔지니어링
종합건축사사무소
Architects, Planners & Engineers
TEL. 02 2143 4466, SEOUL, KOREA

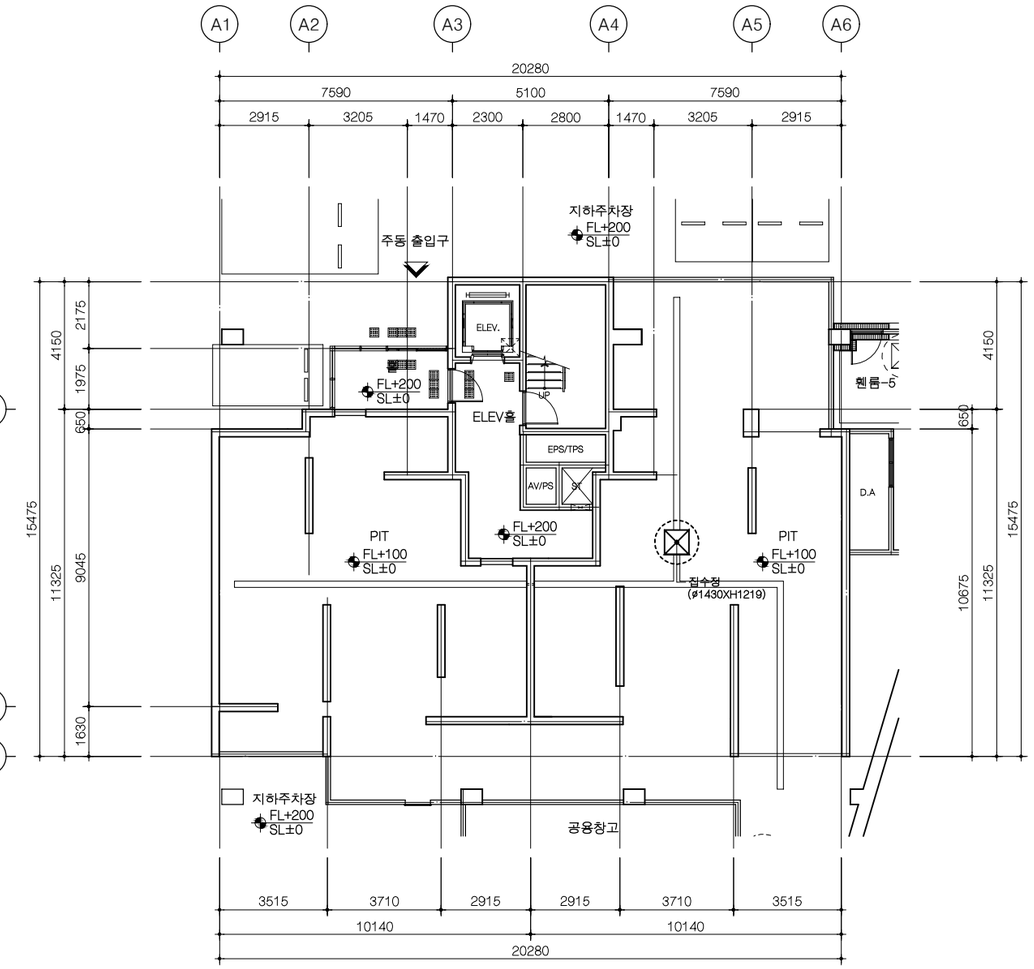

1 A 115동 지하3층 평면도

축척 = 1/100

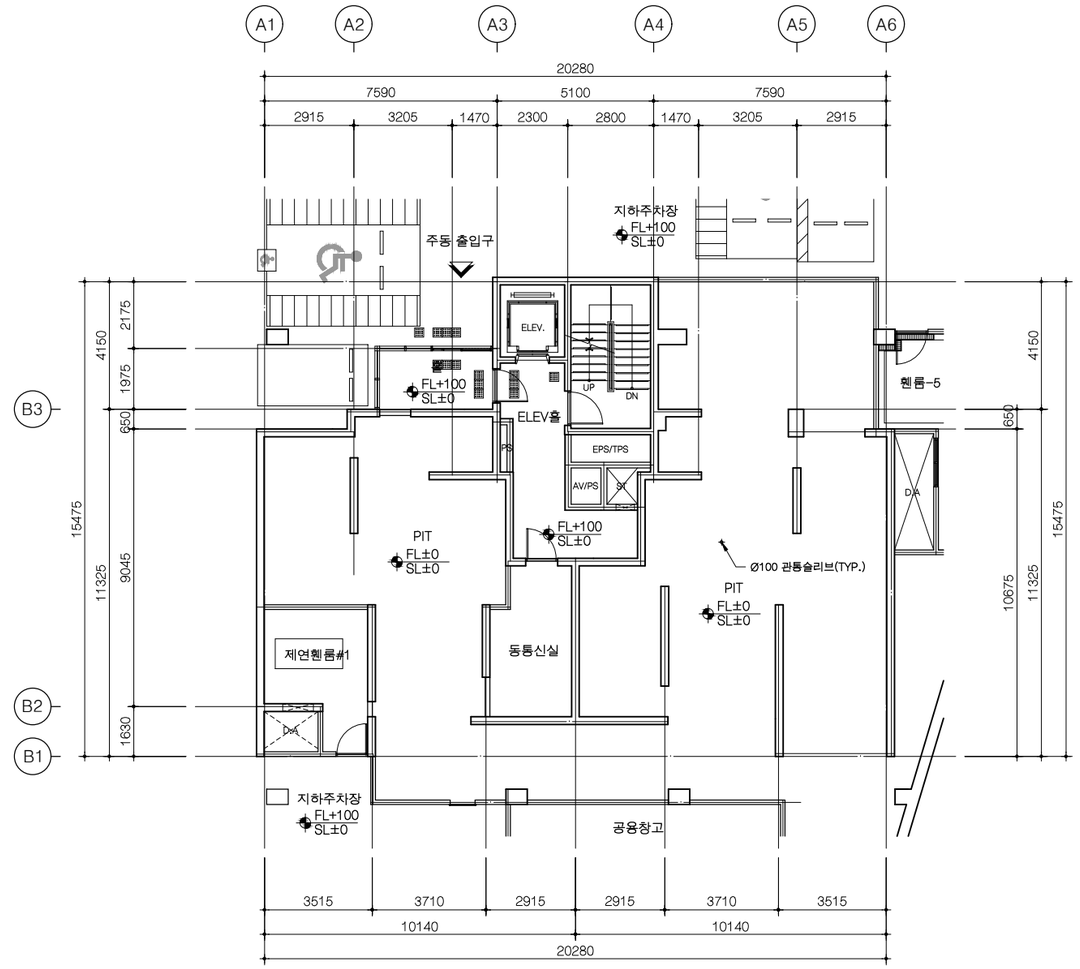

2 A 115동 지하2층 평면도

축척 = 1/100

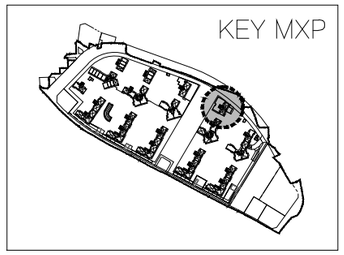

사업번호 PROJECT NO.

사업명 PROJECT TITLE

수색4재정비촉진구역
주택재개발 정비사업

KEY PLAN

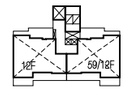

NOTE

1. 지하층 무근 콘크리트는 실시공시 THK80~120 범위로 변동이 있을수 있음.(SLOPE)
2. ELEV홀에 면한부위는 1.0B 조적쌓기임.
3. 지하주차장의 블록쌓기 기준은 높이가 3.6m이하인 경우 4인치 보강블록쌓기가 기준임 (단, 5.4m이하는 6인치쌓기, 5.4m초과는 8인치쌓기가 기준임)
4. ELEV.PIT 집수정은 (600X600X600)임.
5. 주차장 내의 창호는 주차장 창호도 참조.
6. 주차장 집수정 및 영구배수 집수정의 크기 및 위치는 지하주차장 평면도를 참조 할 것.
   ⊠: 주차장 집수정(ø1430XH1219)
   ⊠: 영구배수 집수정(ø1760XH1524)
   ⊗: 아파트 집수정(ø1430XH1219)

********** 지하3층 바닥LEVEL
B3SL±0 = B3FL±0 = EL+15.85
**** 지하2층 바닥LEVEL
B2SL±0 = B2FL±0 = EL+19.30

수정번호 REV. NO.	일 자 DATE	내 용 DESCRIPTION	승 인 CHKD
△			
△			
△			
△			

설계 DESIGNED BY

검토 CHECKED BY
최 진 규

심사 SUMMITED BY
정 호 혁

승인 APPROVED BY
이 승 준

일자 DATE
2019.08

도면명 DRAWING TITLE
115동
지하3층 및 지하2층 평면도

축 척 SCALE
A1: 1/100
A3: 1/200

도면번호 DRAWING NO.
A-531

일련번호 SHEET NO.

△ REV. NO.

HAUD
㈜하우드엔지니어링
종합건축사사무소
Architects, Planners & Engineers
TEL. 02 2140 4400, SEOUL, KOREA

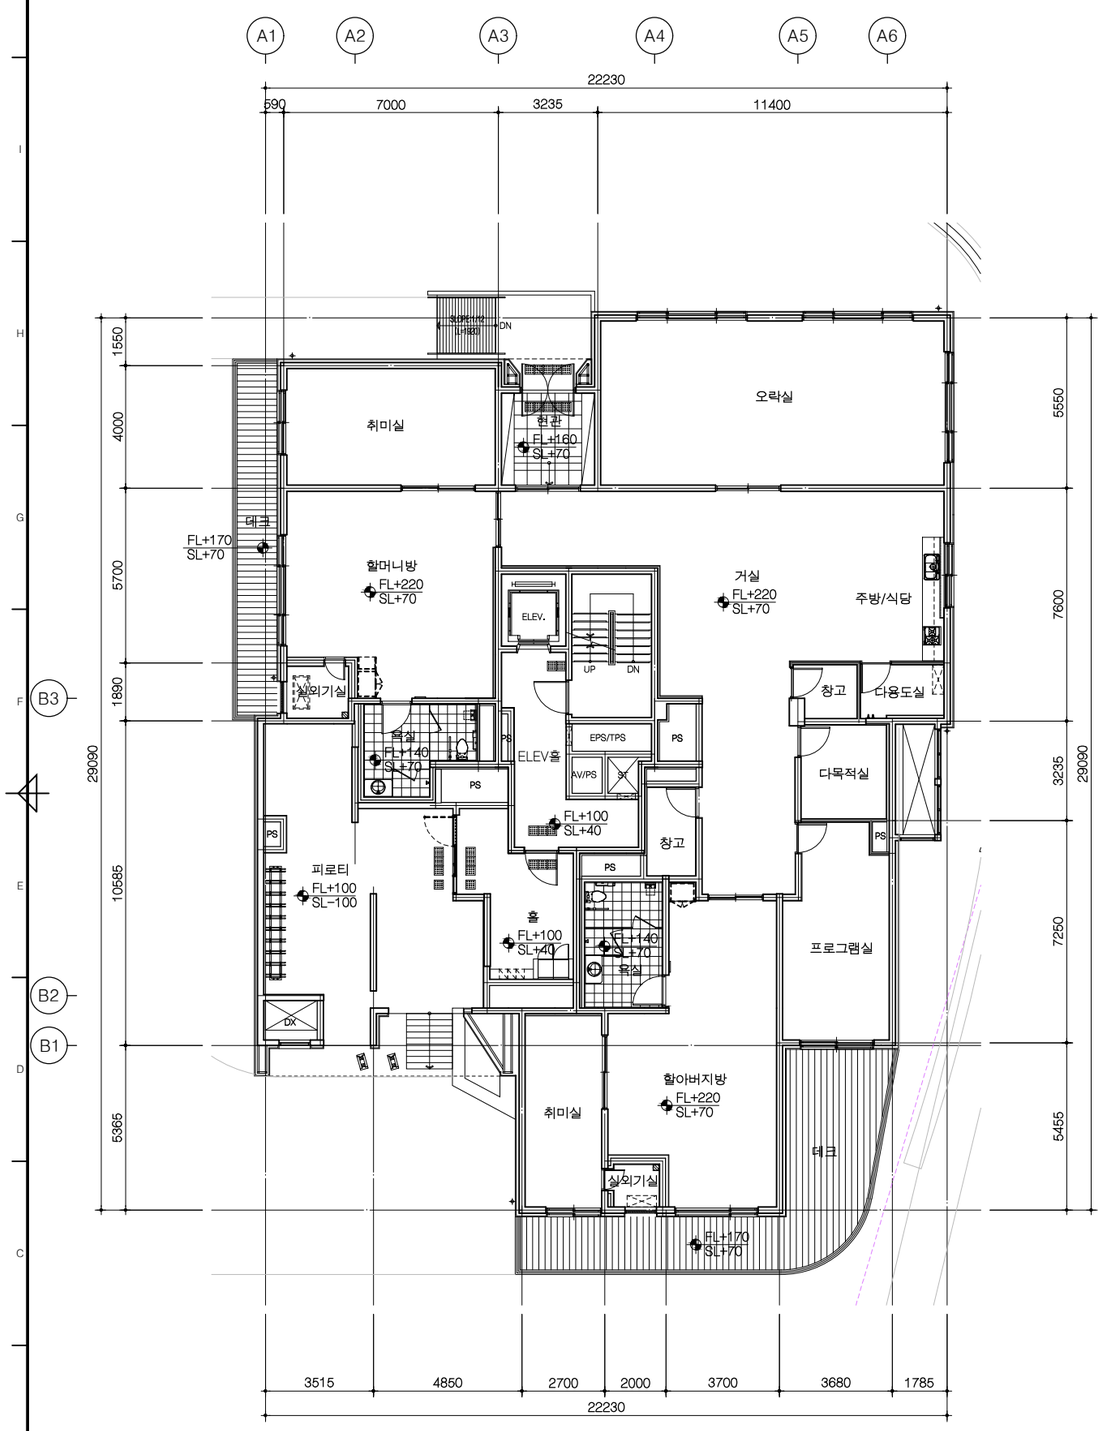

1 A 115동 1층 평면도(경로당)

축척 = 1/100

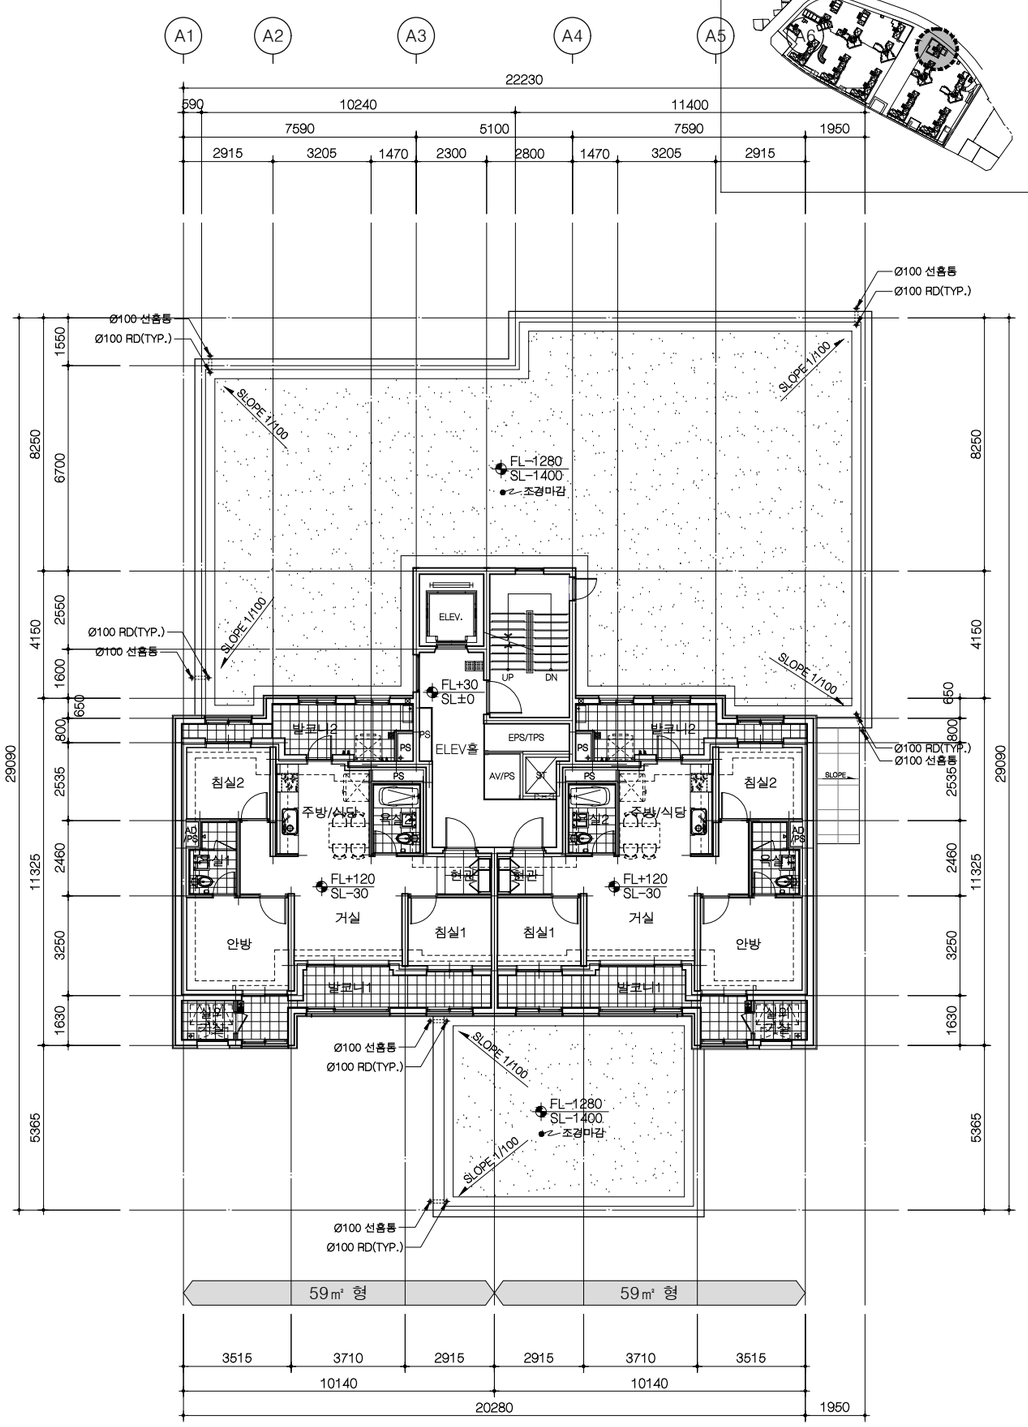

2 A 115동 2층 평면도

축척 = 1/100

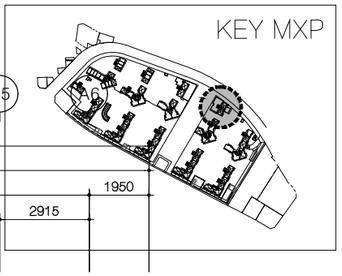

사업번호 PROJECT NO.

사업명 PROJECT TITLE

수색4재정비촉진구역
주택재개발 정비사업

KEY PLAN

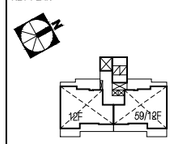

NOTE

1. 우려물 수취함 설치 위치는 변경될 수 있음

• 1층 바닥LEVEL
1SL±0 = 1FL±0 = GL±0 = EL+24.20
2층 바닥LEVEL
2SL±0 = 2FL±0 = EL+29.30

수정번호 REV. NO.	일 자 DATE	내 용 DESCRIPTION	승 인 CHKD
△			
△			
△			
△			

설계 DESIGNED BY

검토 CHECKED BY
최 진 규

심사 SUMMITED BY
정 호 혁

승인 APPROVED BY
이 승 준

일자 DATE
2019.08

도면명 DRAWING TITLE
115동
1층 및 2층 평면도

축 척 SCALE
A1: 1/100
A3: 1/200

도면번호 DRAWING NO.
A-532

일련번호 SHEET NO. △ REV. NO.

HAUD
(주)하우드엔지니어링
종합건축사사무소
Architects, Planners & Engineers
TEL. 02 2140 4400, SEOUL, KOREA

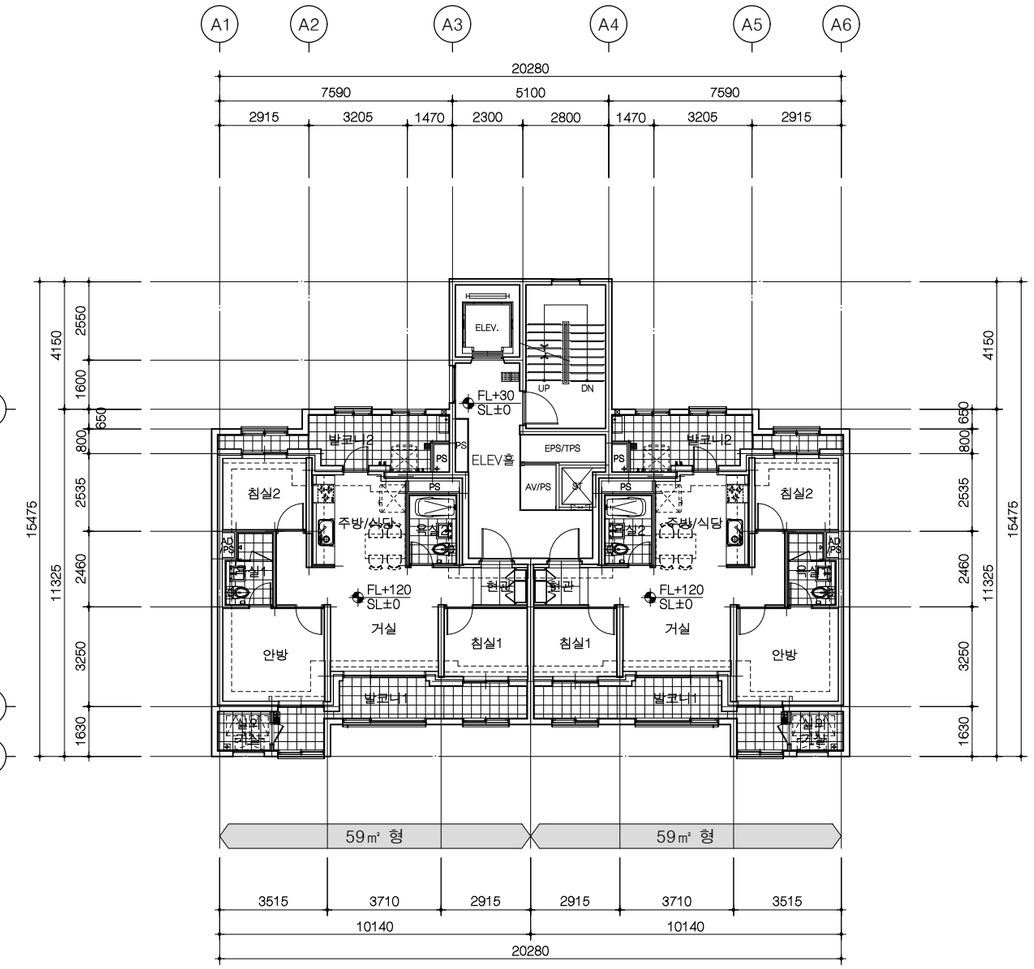

1 A 115동 3~12층 평면도

축척 = 1/100

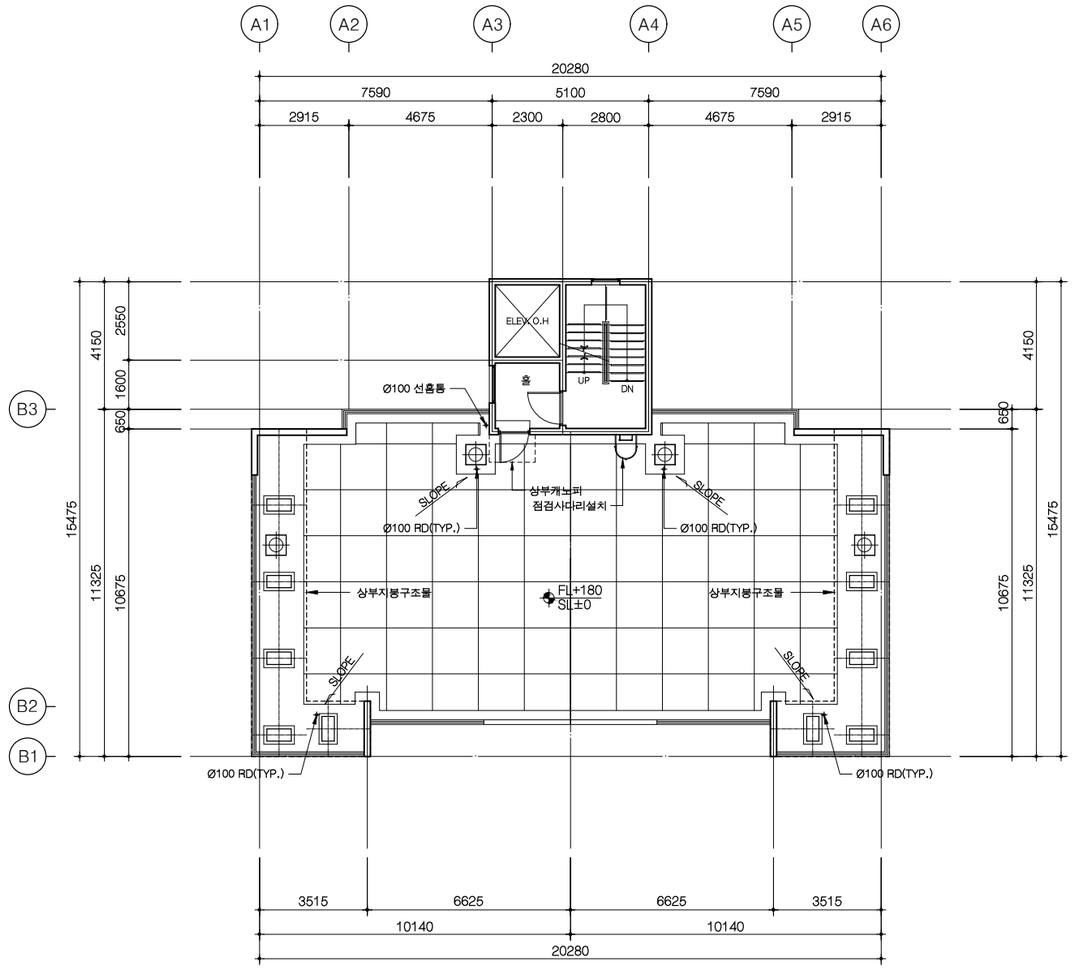

2 A 115동 지붕 평면도

축척 = 1/100

KEY MXP

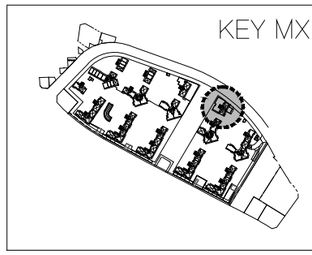

사업번호 PROJECT NO.

사업명 PROJECT TITLE

수색4재정비촉진구역
주택재개발 정비사업

KEY PLAN

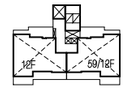

NOTE

1. 본 도면은 발코니 확장전를 기준으로 작성됨.
2. 지붕층 난간의 형태와 설치 위치는 안전성과 입면디자인을 고려하여 변경 가능함.
3. 지붕의 재료, 형태, 구조는 실시공 시 변경 될 수 있음.
4. 지붕 및 옥탑 구조물의 형태와 구조는 실시공 시 변경될 수 있음.
5. 옥상 출눈의 간격은 실시공 시 변경될 수 있음.
6. 옥상 출눈 틈에 실란트 시공되지 않음
7. 우편물 수취함 설치 위치는 변경될 수 있음

수정번호 REV. NO.	일 자 DATE	내 용 DESCRIPTION	승 인 CHKD
△			
△			
△			
△			

설계 DESIGNED BY

검토 CHECKED BY
최 진 규

심사 SUMMITED BY
정 호 혁

승인 APPROVED BY
이 승 준

일자 DATE
2019.08

도면명 DRAWING TITLE
115동
3~12층 및 지붕 평면도

축 척 SCALE
A1: 1/100
A3: 1/200

도면번호 DRAWING NO.
A-533

일련번호 SHEET NO.

△ REV. NO.

HAUD
(주)하우드엔지니어링
종합건축사사무소
Architects, Planners & Engineers
TEL. 02 2140 4400, SEOUL, KOREA

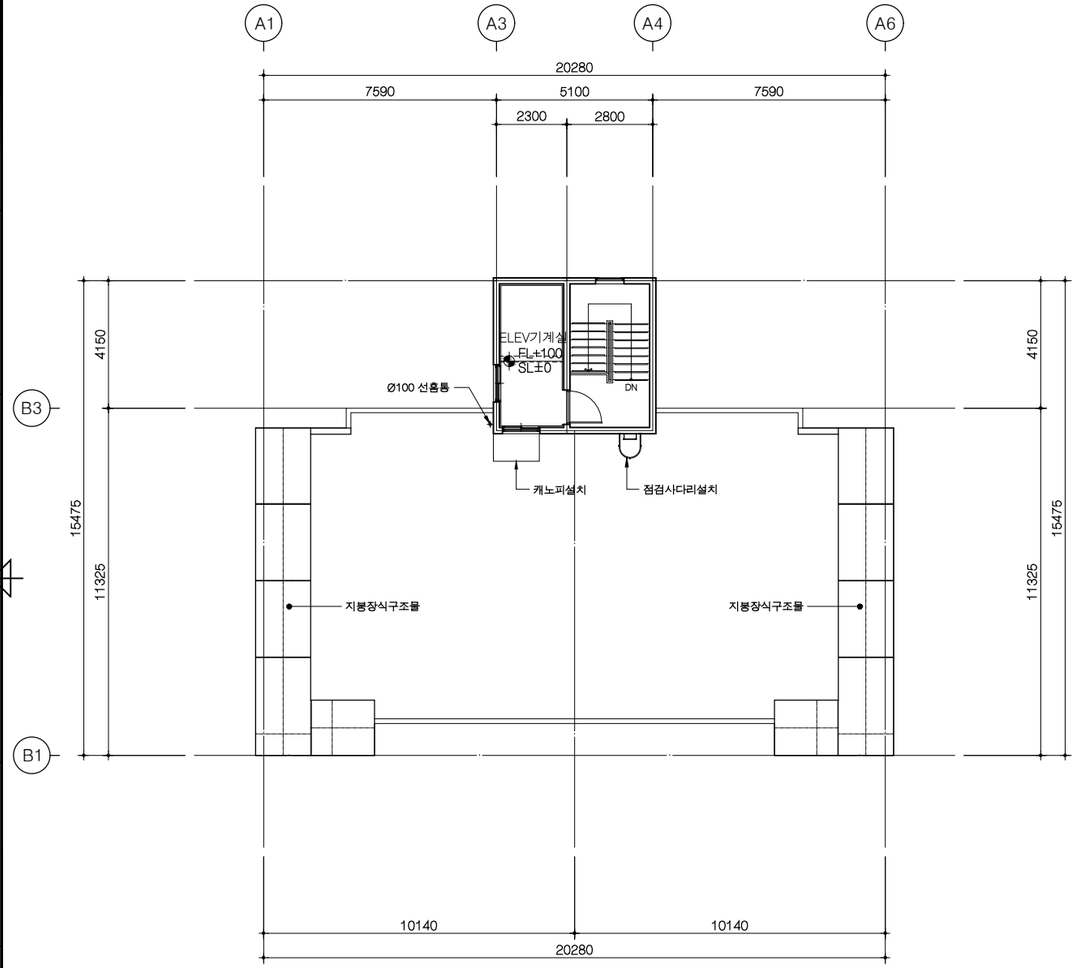

1 A 115동 옥탑층 평면도

축척 = 1/100

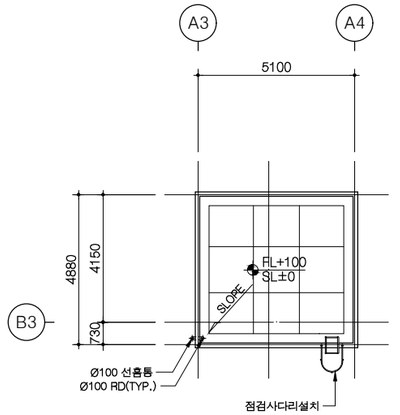

2 A 115동 옥탑지붕 평면도

축척 = 1/100

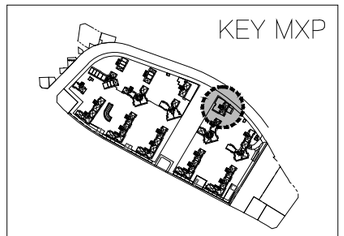

사업번호 PROJECT NO.

사업명 PROJECT TITLE

수색4재정비촉진구역
주택재개발 정비사업

KEY PLAN

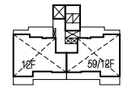

NOTE

1. 지붕바닥
   ① EXP. JOINT: 3000 X 3000
2. 본 평면도는 발코니확장전을 기준으로 작성됨
3. 재료마감은 실내,외 재료마감표 참조
4. 지붕 난간형태/설치위치는 안전성과 입면을 고려하여 실시공시 변경될 수 있음
5. 지붕재료 및 형태,구조는 실시공시 변경될수 있음
6. 지붕(옥탑지붕)의 배수드레인,청소용고리, 베기탑,점검사다리(점검구) 등의 설치위치/개소는 실시공시 변경될 수 있음
7. 옥상 상부구조물은 PC구조물 임.
8. 정화조 배기는 기계도서 참조

수정번호 REV. NO.	일 자 DATE	내 용 DESCRIPTION	승 인 CHKD
△			
△			
△			
△			

설계 DESIGNED BY

검토 CHECKED BY
최 진 규

심사 SUMMITED BY
정 호 혁

승인 APPROVED BY
이 승 준

일자 DATE
2019.08

도면명 DRAWING TITLE
115동
옥탑층 및 옥탑지붕 평면도

축 척 SCALE
A1: 1/100
A3: 1/200

도면번호 DRAWING NO.
A-534

일련번호 SHEET NO.

△ REV. NO.

HAUD
㈜하우드랜지니어링
종합건축사사무소
Architects, Planners & Engineers
TEL. 02 2140 4400, SEOUL, KOREA

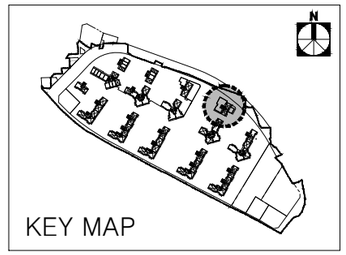

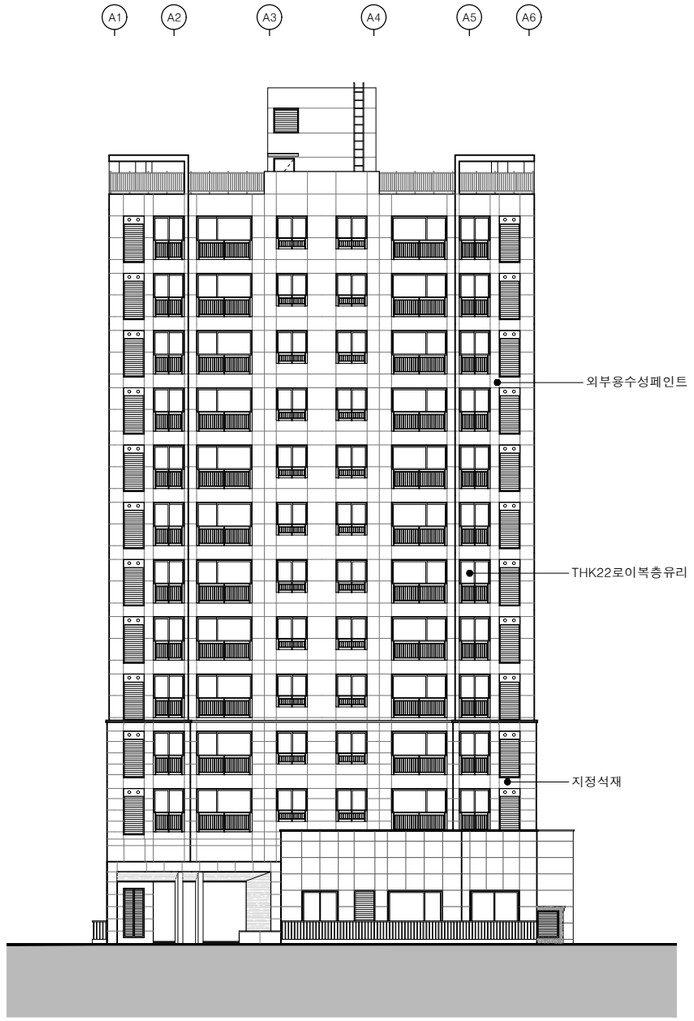

1 A 115동 정면도

축척 = 1/150

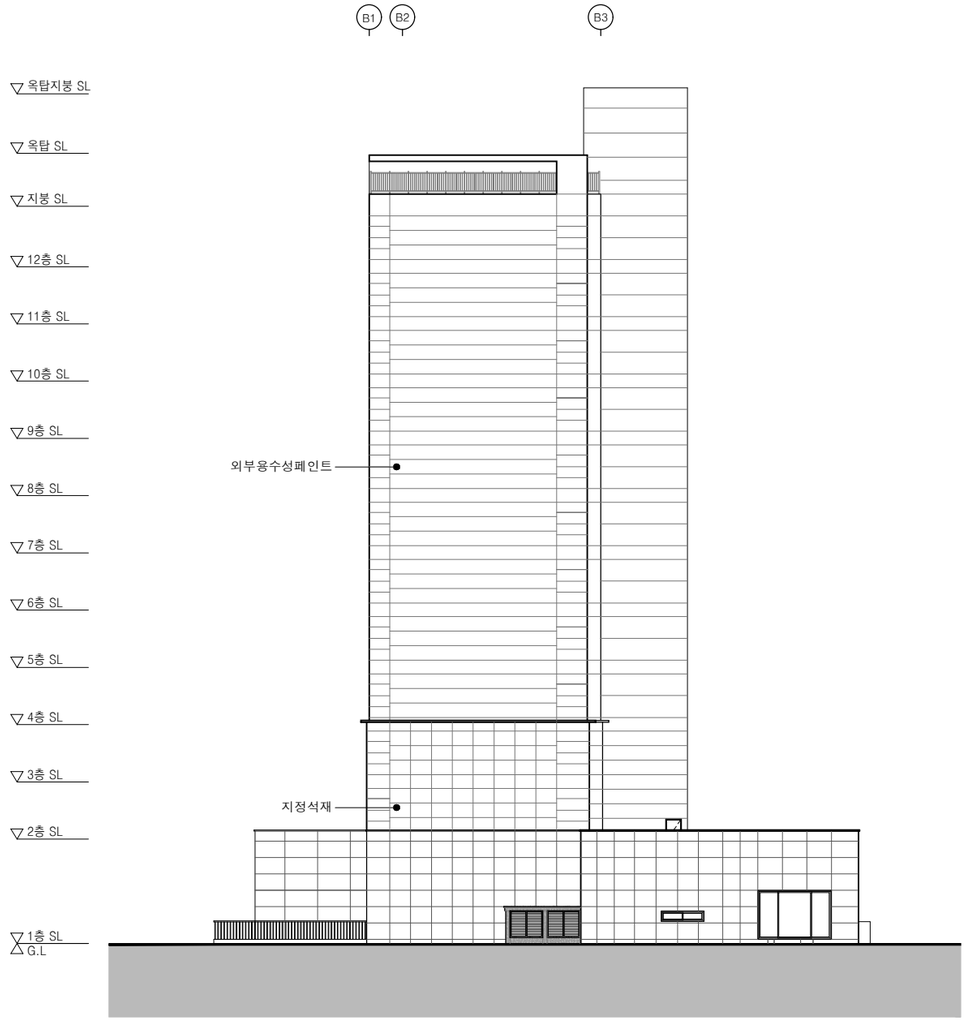

2 A 115동 우측면도

축척 = 1/150

사업번호 PROJECT NO.

사업명 PROJECT TITLE

수색4재정비촉진구역
주택재개발 정비사업

KEY PLAN

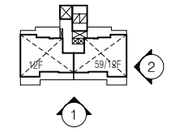

NOTE

1. 1층 바닥 LEVEL
   1SL±0 = 1FL±0 = GL±0 = EL+24.20
2. 지붕 난간의 형태 및 설치위치는 안전성과 입면디자인을 고려하여 변경가능함.
3. 지붕의 재료, 형태, 구조는 실시공시 변경될 수 있음.
4. 지붕 및 옥탑구조물의 형태와 구조는 실시공시 변경될 수 있음.
5. 외벽 및 측벽 문양은 실시공시 변경될 수 있음
6. 입면의 줄눈 및 마감선은 실시공시 변경될 수 있음.
7. 저층부 석재마감 및 입면 마감 색상, 재료에 대한 모든 기준은 특화도면을 우선 적용함.

수정번호 REV. NO.	일 자 DATE	내 용 DESCRIPTION	승 인 CHKD
△			
△			
△			
△			

설계 DESIGNED BY

검토 CHECKED BY
최 진 규

심사 SUMMITED BY
정 호 혁

승인 APPROVED BY
이 승 준

일자 DATE
2019.08

도면명 DRAWING TITLE
115동 정면도,우측면도

축 척 SCALE
A1: 1/150
A3: 1/300

도면번호 DRAWING NO.
A-535

얼럿번호 SHEET NO.

REV. NO. △

HAUD
㈜하우드엔지니어링
종합건축사사무소
Architects, Planners & Engineers
TEL. 02 2140 4400, SEOUL, KOREA

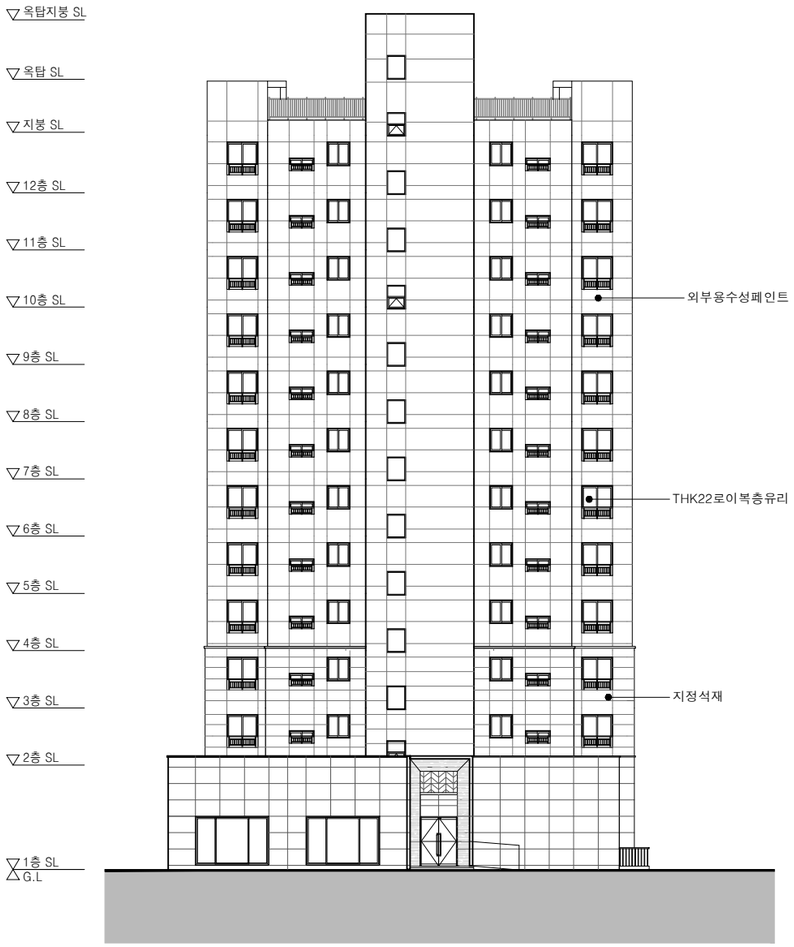

1 A 115동 배면도

축척 = 1/150

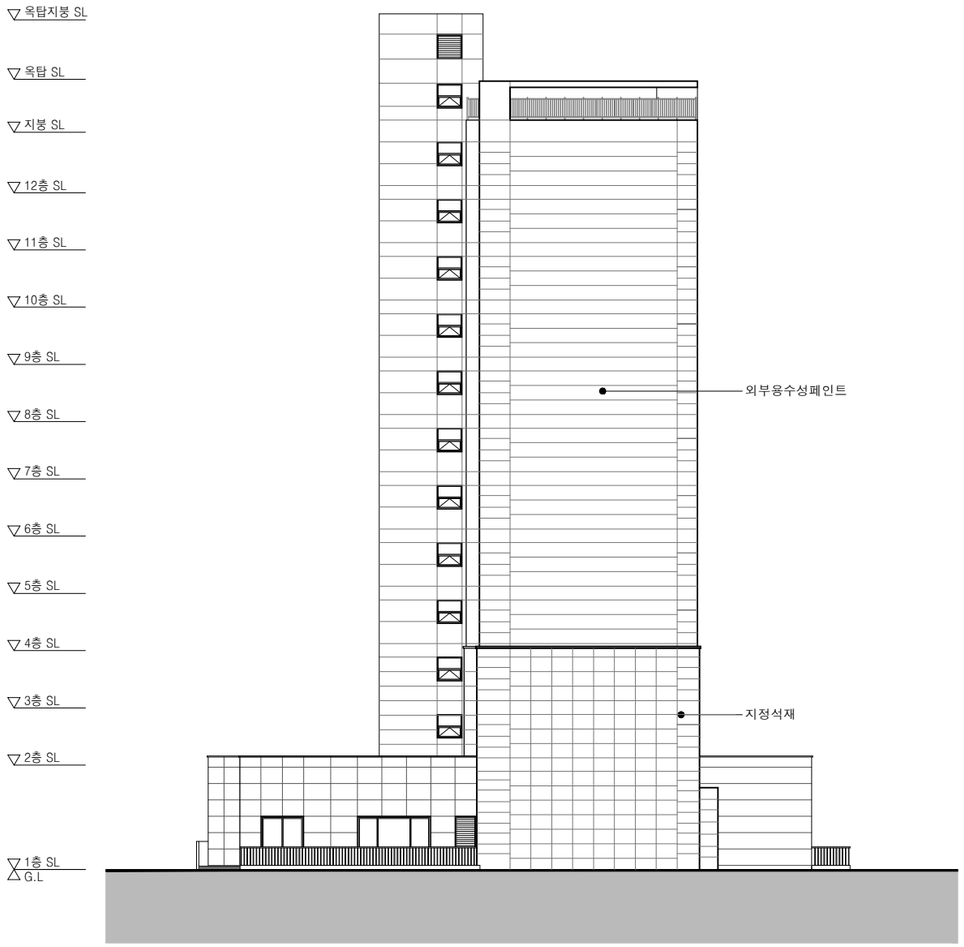

2 A 115동 좌측면도

축척 = 1/150

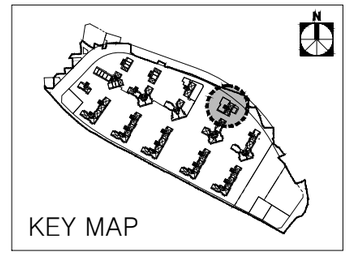

사업번호 PROJECT NO.

사업명 PROJECT TITLE

수색4재정비촉진구역
주택재개발 정비사업

KEY PLAN

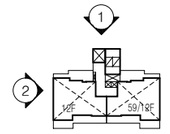

NOTE

1. 1층 바닥 LEVEL
   1SL±0 = 1FL±0 = GL±0 = EL+24.20
2. 지붕 난간의 형태 및 설치위치는 안전성과 입면디자인을 고려하여 변경가능함.
3. 지붕의 재료, 형태, 구조는 실시공시 변경될 수 있음.
4. 지붕 및 옥탑구조물의 형태와 구조는 실시공시 변경될 수 있음.
5. 외벽 및 측벽 문양은 실시공시 변경될 수 있음
6. 입면의 줄눈 및 마감선은 실시공시 변경될 수 있음.
7. 저층부 석재마감 및 입면 마감 색상, 재료에 대한 모든 기준은 특화도면을 우선 적용함.

수정번호 REV. NO.	일 자 DATE	내 용 DESCRIPTION	승 인 CHKD
△			
△			
△			
△			

설계 DESIGNED BY

검토 CHECKED BY
최 진 규

심사 SUMMITED BY
정 호 혁

승인 APPROVED BY
이 승 준

일자 DATE
2019.08

도면명 DRAWING TITLE
115동 배면도,좌측면도

축 척 SCALE
A1: 1/150
A3: 1/300

도면번호 DRAWING NO.
A-536

일련번호 SHEET NO.

REV. NO.

HAUD
㈜하우드엔지니어링
종합건축사사무소
Architects, Planners & Engineers
TEL. 02 2142 4400, SEOUL, KOREA

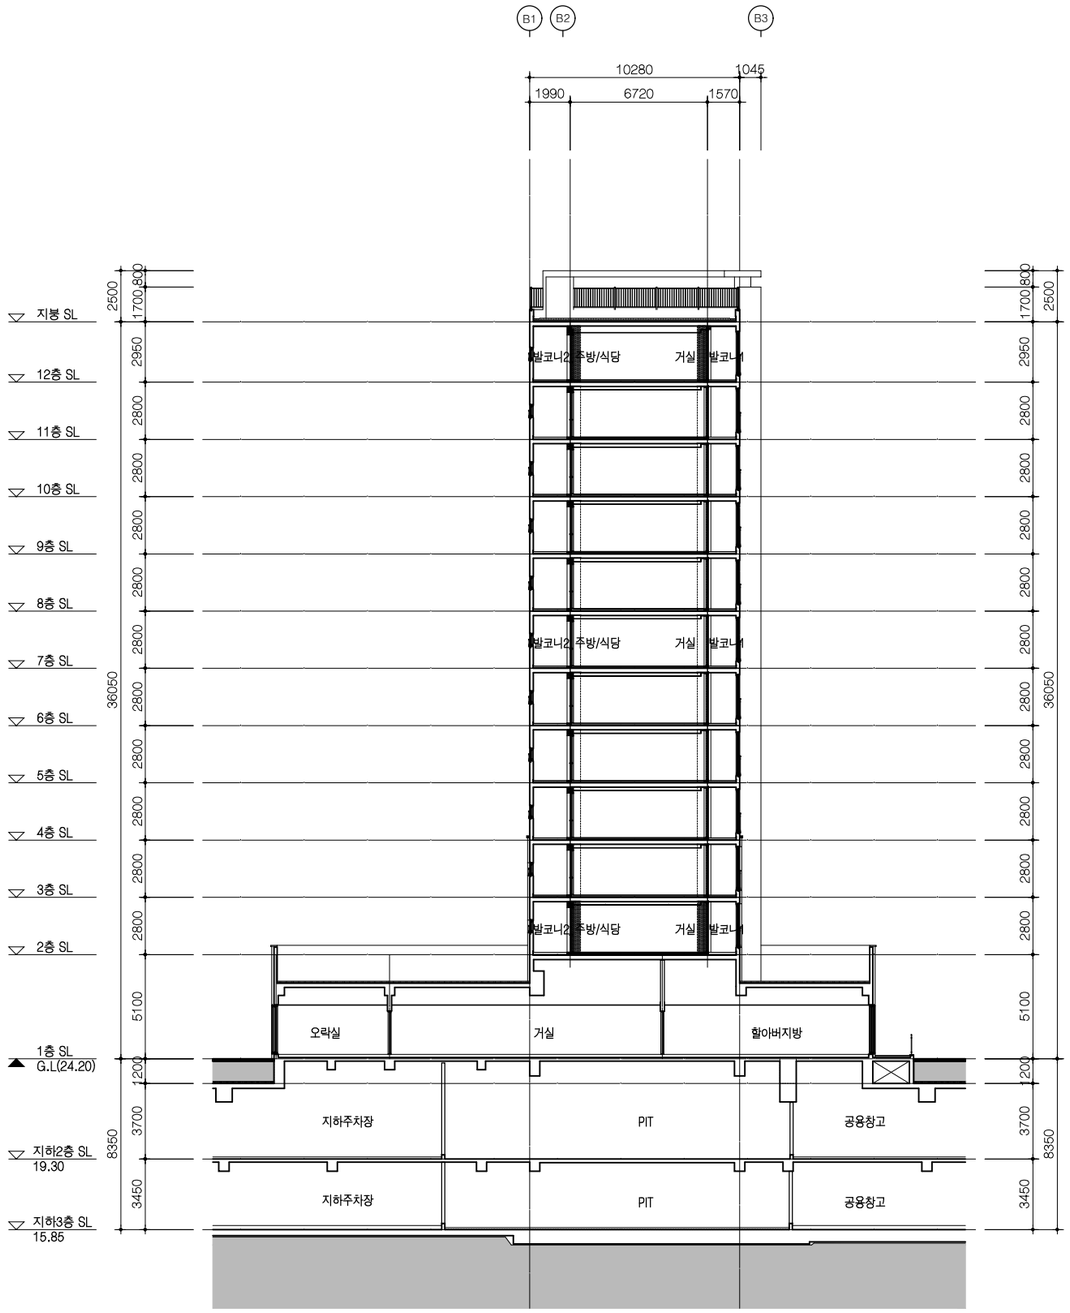

1 A 115동 종단면도

축척 = 1/150

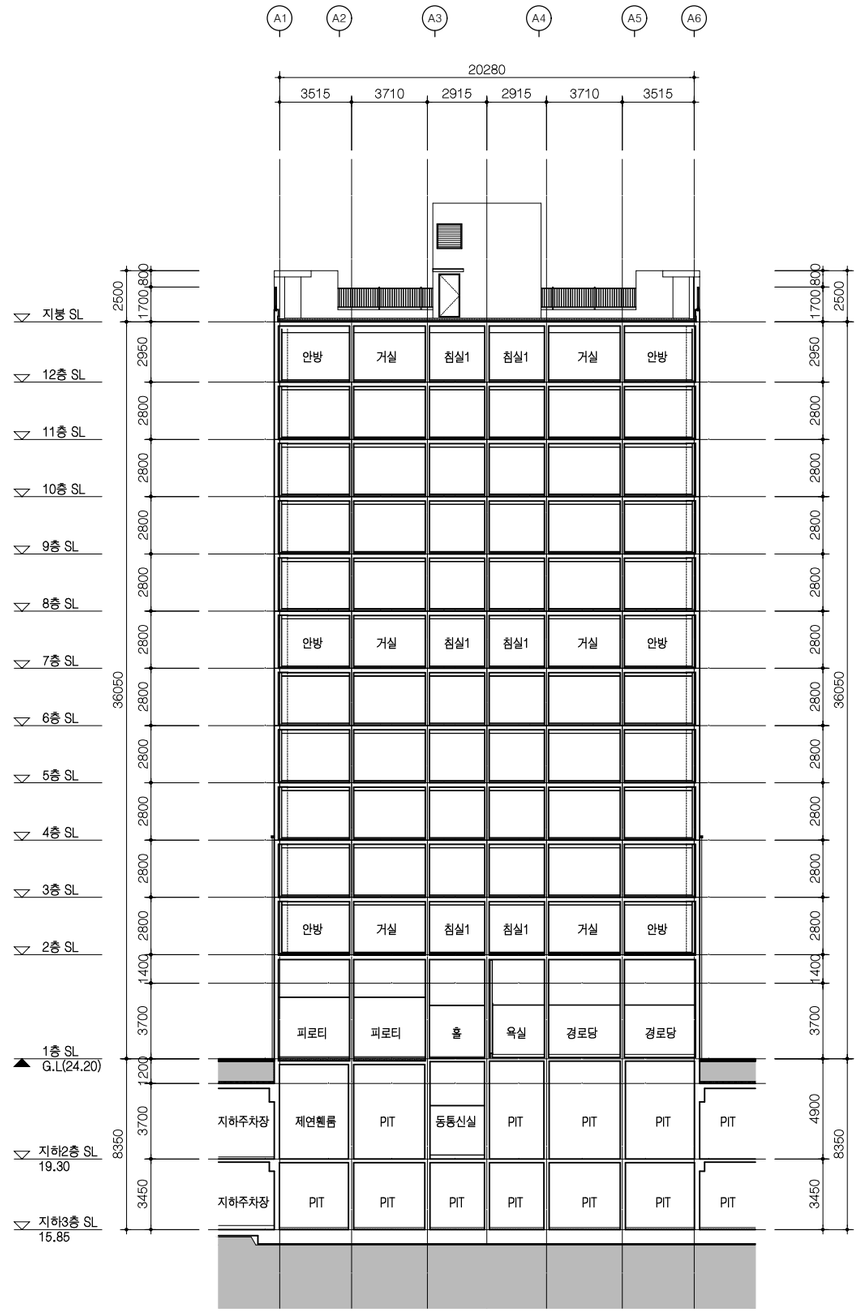

2 A 115동 횡단면도

축척 = 1/150

사업번호 PROJECT NO.

사업명 PROJECT TITLE

수색4재정비촉진구역
주택재개발 정비사업

KEY PLAN

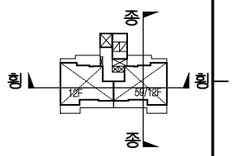

NOTE

수정번호 REV. NO.	일 자 DATE	내 용 DESCRIPTION	승 인 CHKD
△			
△			
△			
△			

설계 DESIGNED BY

검토 CHECKED BY
최 진 규

심사 SUMMITED BY
정 호 혁

승인 APPROVED BY
이 승 준

일자 DATE
2019.08

도면명 DRAWING TITLE
115동 종,횡단면도

축 척 SCALE
A1: 1/150
A3: 1/300

도면번호 DRAWING NO.
A-537

일련번호 SHEET NO.

REV. NO. △

HAUD
㈜하우드엔지니어링
종합건축사사무소
Architects, Planners & Engineers
TEL. 02 2149 4400, SEOUL, KOREA